

การประกอบเลขที่ ASSEMBLY NO. **0525 A**

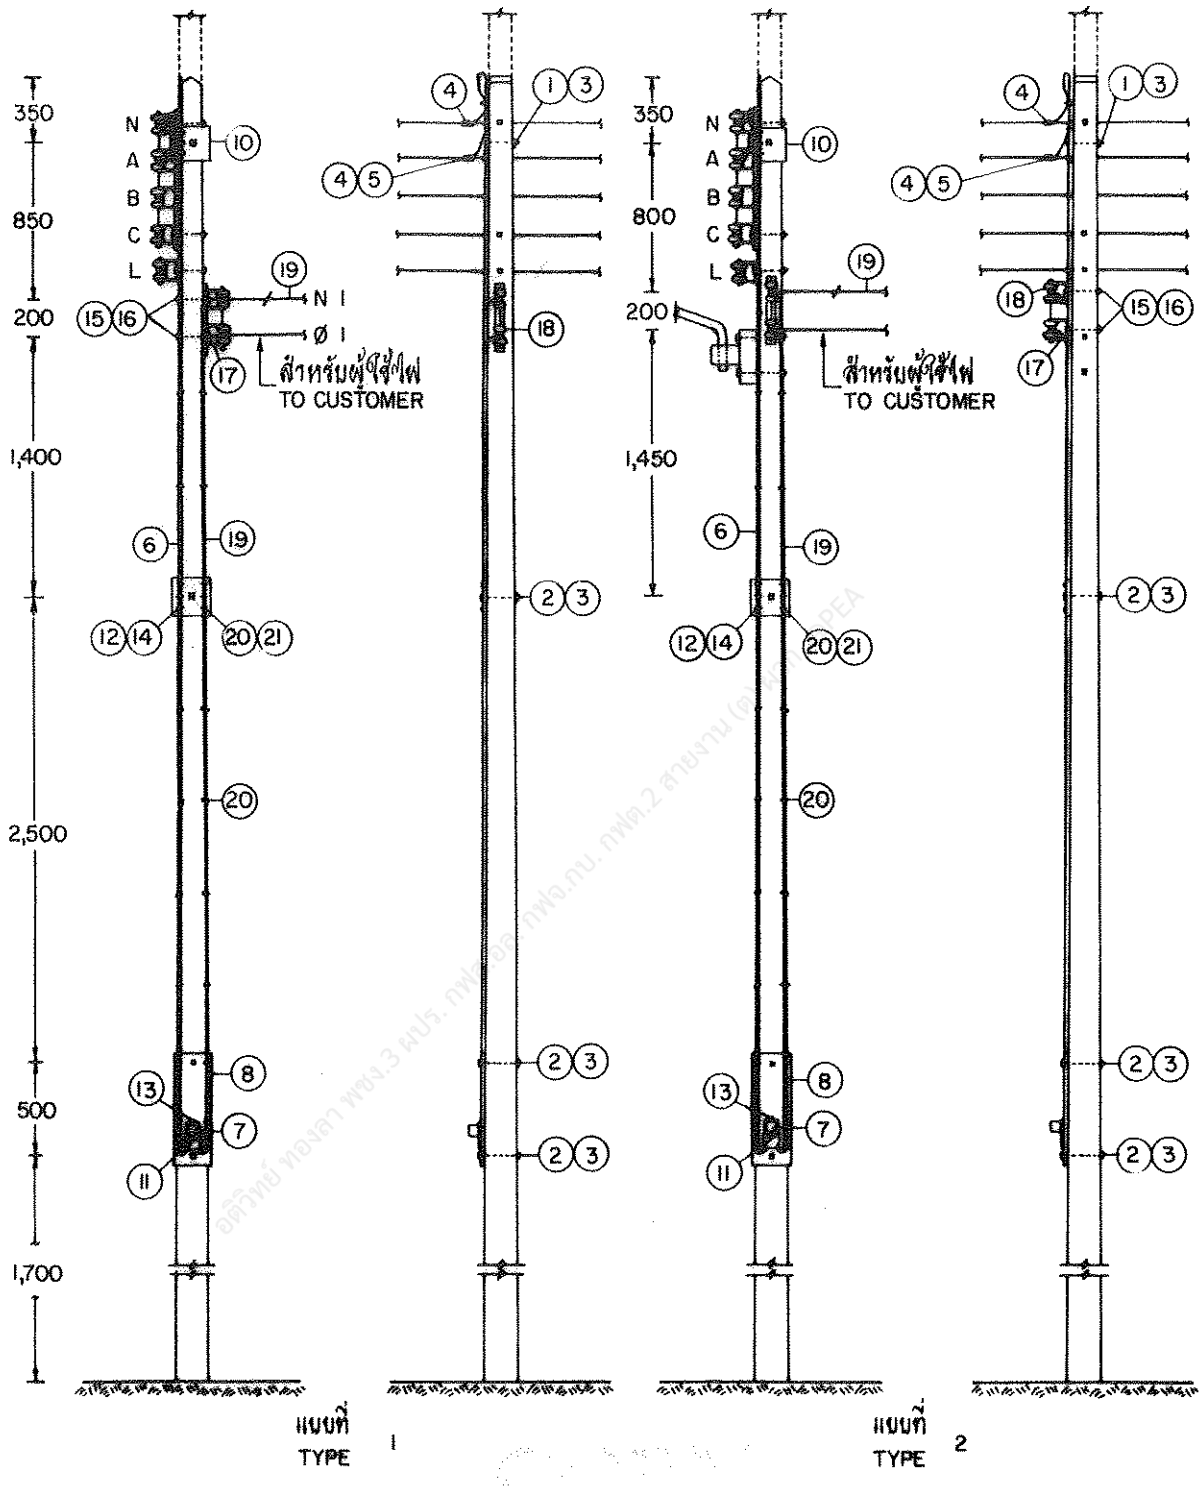

หน่วยวิศวกรรมไฟฟ้าและเครื่องกล ฝ่ายวิศวกรรม ผู้เขียน ผู้ตรวจ วิศวกร หัวหน้าแผนก ผู้อำนวยการกอง ผู้อำนวยการฝ่าย ของผู้ว่าการฝ่ายเทคนิค	การไฟฟ้าส่วนภูมิภาค ตู้ว่าการ 10 มิถุนายน 2538 การติดตั้งมิเตอร์ 1 เฟส 220 โวลต์ ขนาด 3-15 แอมป์ บนเสาคอนกรีต 9 ม. (สายเข้ามิเตอร์ทองแดง) 1 จำนวน 1 เครื่อง 3-15 A, 1-Ø, 220 V METER INSTALLATION ON 9 m CONCRETE POLE (Cu SERVICE ENTRANCE CABLE) 1 UNIT	ใช้แทนแบบ ถูกแทนโดยแบบ เขียนแล้วเสร็จวันที่ 30 ม.ย. 37 แก้แบบวันที่ 12 พ.ค. 41 มิติเป็น มิลลิเมตร มาตราส่วน 1 : 40 แบบเลขที่ SA4-015/37033 แผ่นที่ 1 ของจำนวน 6 แผ่น

การประกอบเลขที่ ASSEMBLY NO. **0525 A**

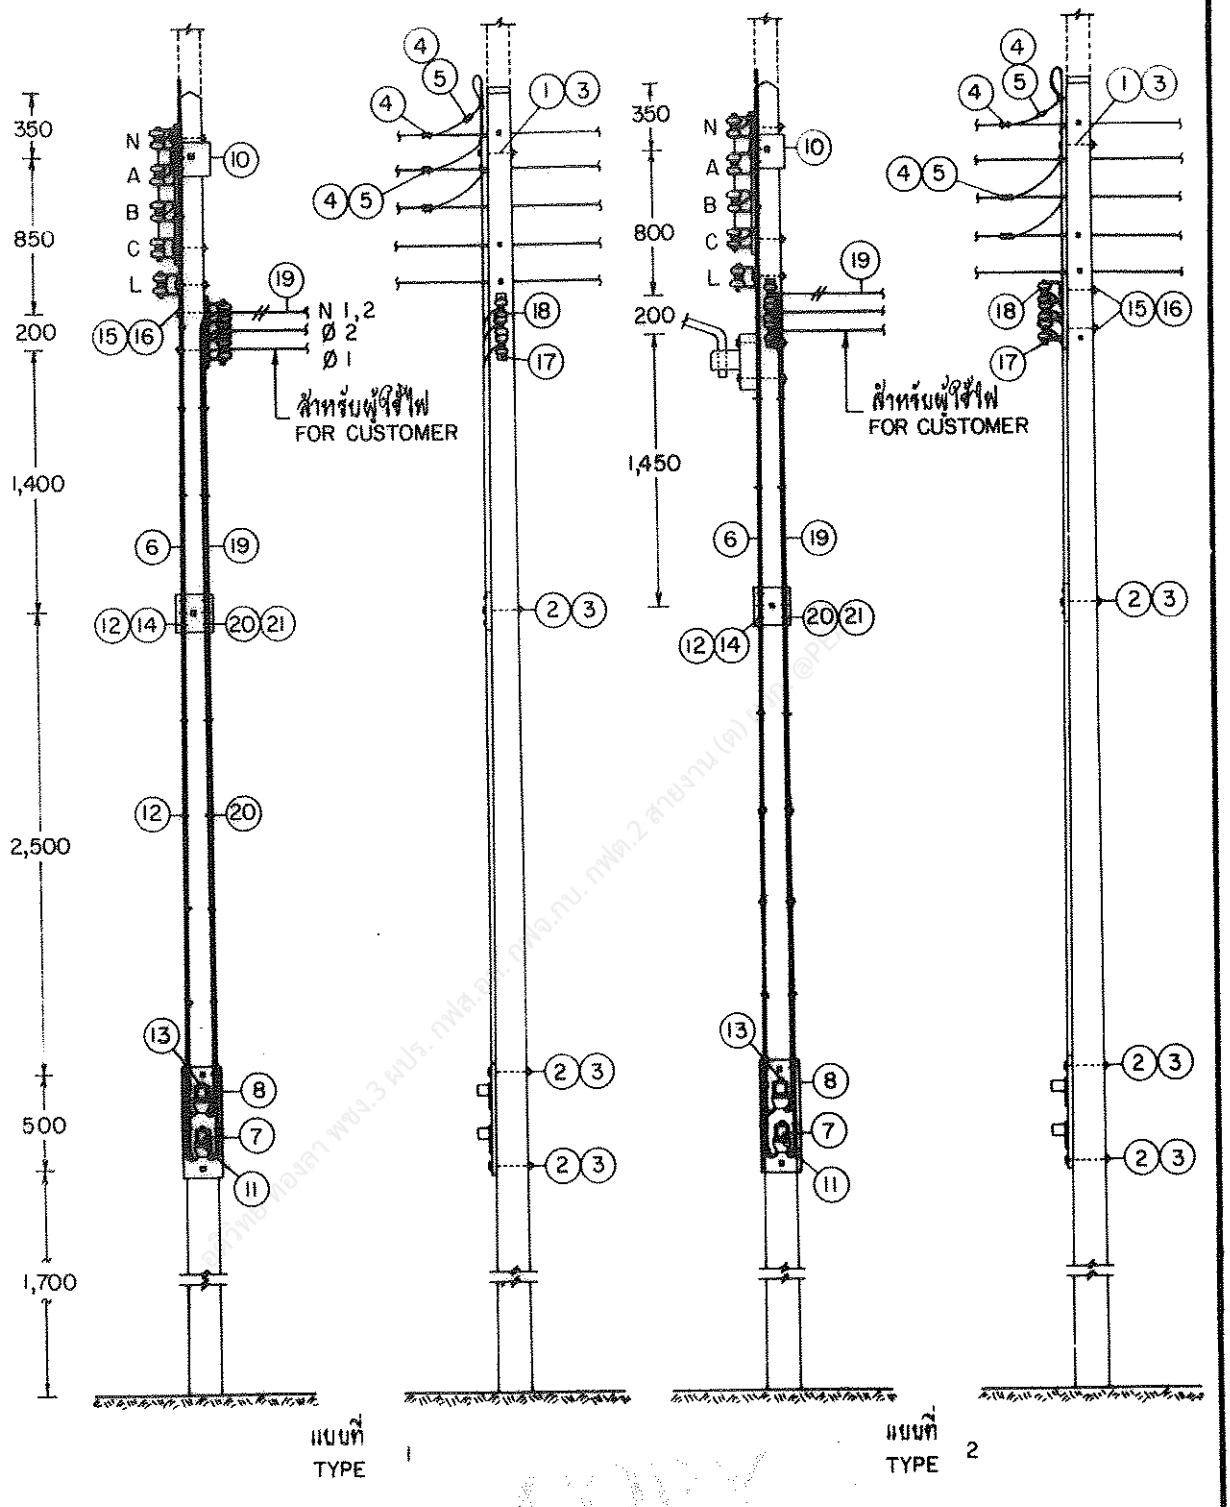


แบบที่ TYPE 1

แบบที่ TYPE 2


กองวิศวกรรมไฟฟ้าและเครื่องกล ฝ่ายวิศวกรรม	การไฟฟ้าส่วนภูมิภาค	ใช้แทนแบบ ถูกแทนโดยแบบ
ผู้เรียน ผู้สำรวจ วิศวกร หัวหน้าแผนก ผู้อำนวยการกอง ผู้อำนวยการฝ่าย	ผู้ว่าการ 10 มิถุนายน 2538 การติดตั้งมิเตอร์ 1 เฟส 220 โวลต์ ขนาด 3-15 แอมป์ บนเสาคอนกรีต 9 ม. (สายเข้ามิเตอร์ทองแดง) 2. จำนวน 2 เครื่อง	เขียนเต็มจำนวนที่ 30 พ.ย. 37 แก้แบบจำนวนที่ 12 พ.ค. 41 มิติเป็น มิลลิเมตร มาตราส่วน 1 : 40
รองผู้ว่าการฝ่ายเทคนิค	3-15 A, 1-Ø, 220 V METER INSTALLATION ON 9 m CONCRETE POLE (Cu SERVICE ENTRANCE CABLE) 2. 2 UNITS	แบบเลขที่ SA4-015/37033 แผ่นที่ 2 รวมจำนวน 6 แผ่น

การประกอบเลขที่
ASSEMBLY NO. **0525 A**

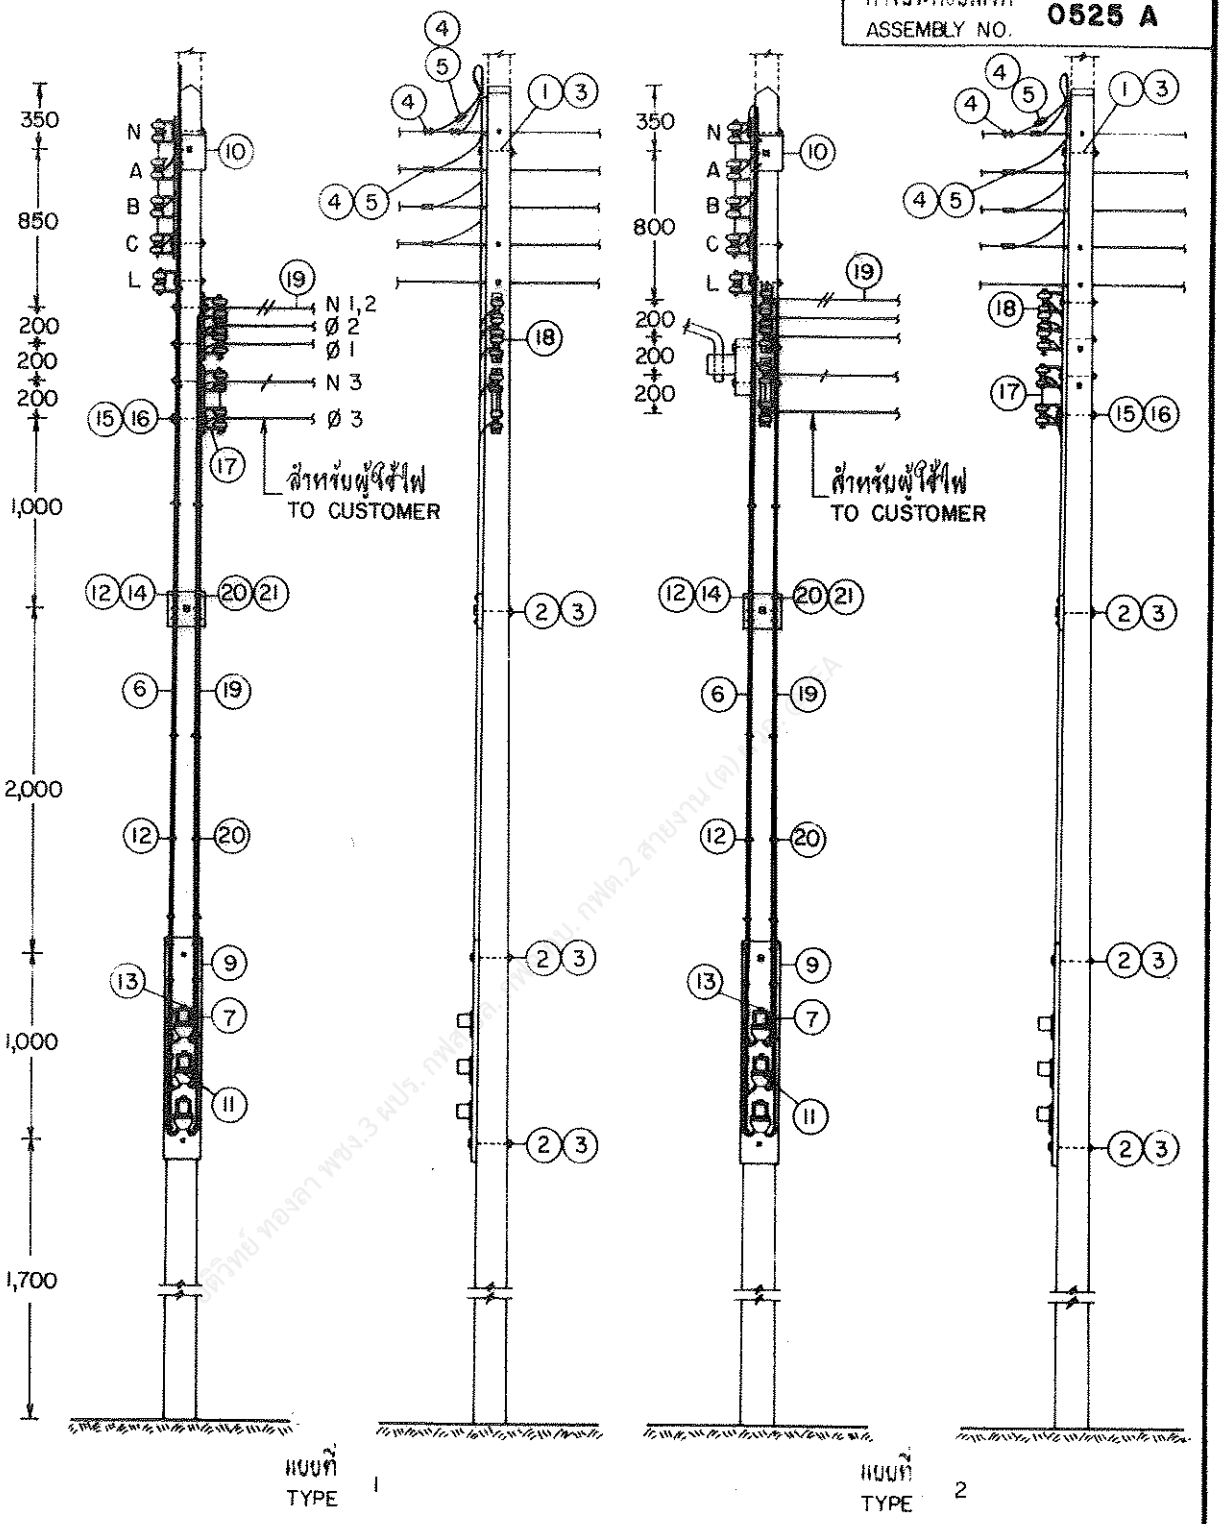

กองวิศวกรรมไฟฟ้าและเครื่องกล ฝ่ายวิศวกรรม	การไฟฟ้าส่วนภูมิภาค	ใช้แทนแบบ ถูกแทนที่โดยแบบ
ผู้เขียน ผู้ตรวจ ผู้ตรวจ หัวหน้าแผนก ผู้อำนวยการกลุ่ม ผู้อำนวยการฝ่าย	ผู้ว่าการ 10 มิถุนายน 2538 การติดตั้งมิเตอร์ 1 เฟส 220 โวลต์ ขนาด 3-15 แอมป์ บนเสาคอนกรีต 9 ม. (สายเข้ามิเตอร์ทองแดง) 3. จำนวน 3 เครื่อง	เขียนเสร็จวันที่ 30 พ.ย. 37 แก้แบบวันที่ 12 พ.ค. 41 มิลลิเมตร มาตราส่วน 1 : 40
รองผู้ว่าการฝ่ายเทคนิค	3-15 A, 1-Ø, 220 V METER INSTALLATION ON 9 m CONCRETE POLE (Cu SERVICE ENTRANCE CABLE) 3. 3 UNITS	แบบเลขที่ SA4-015/37033 แผ่นที่ 3 ของจำนวน 6 แผ่น

การประกอบเลขที่ ASSEMBLY NO. **0525 A**

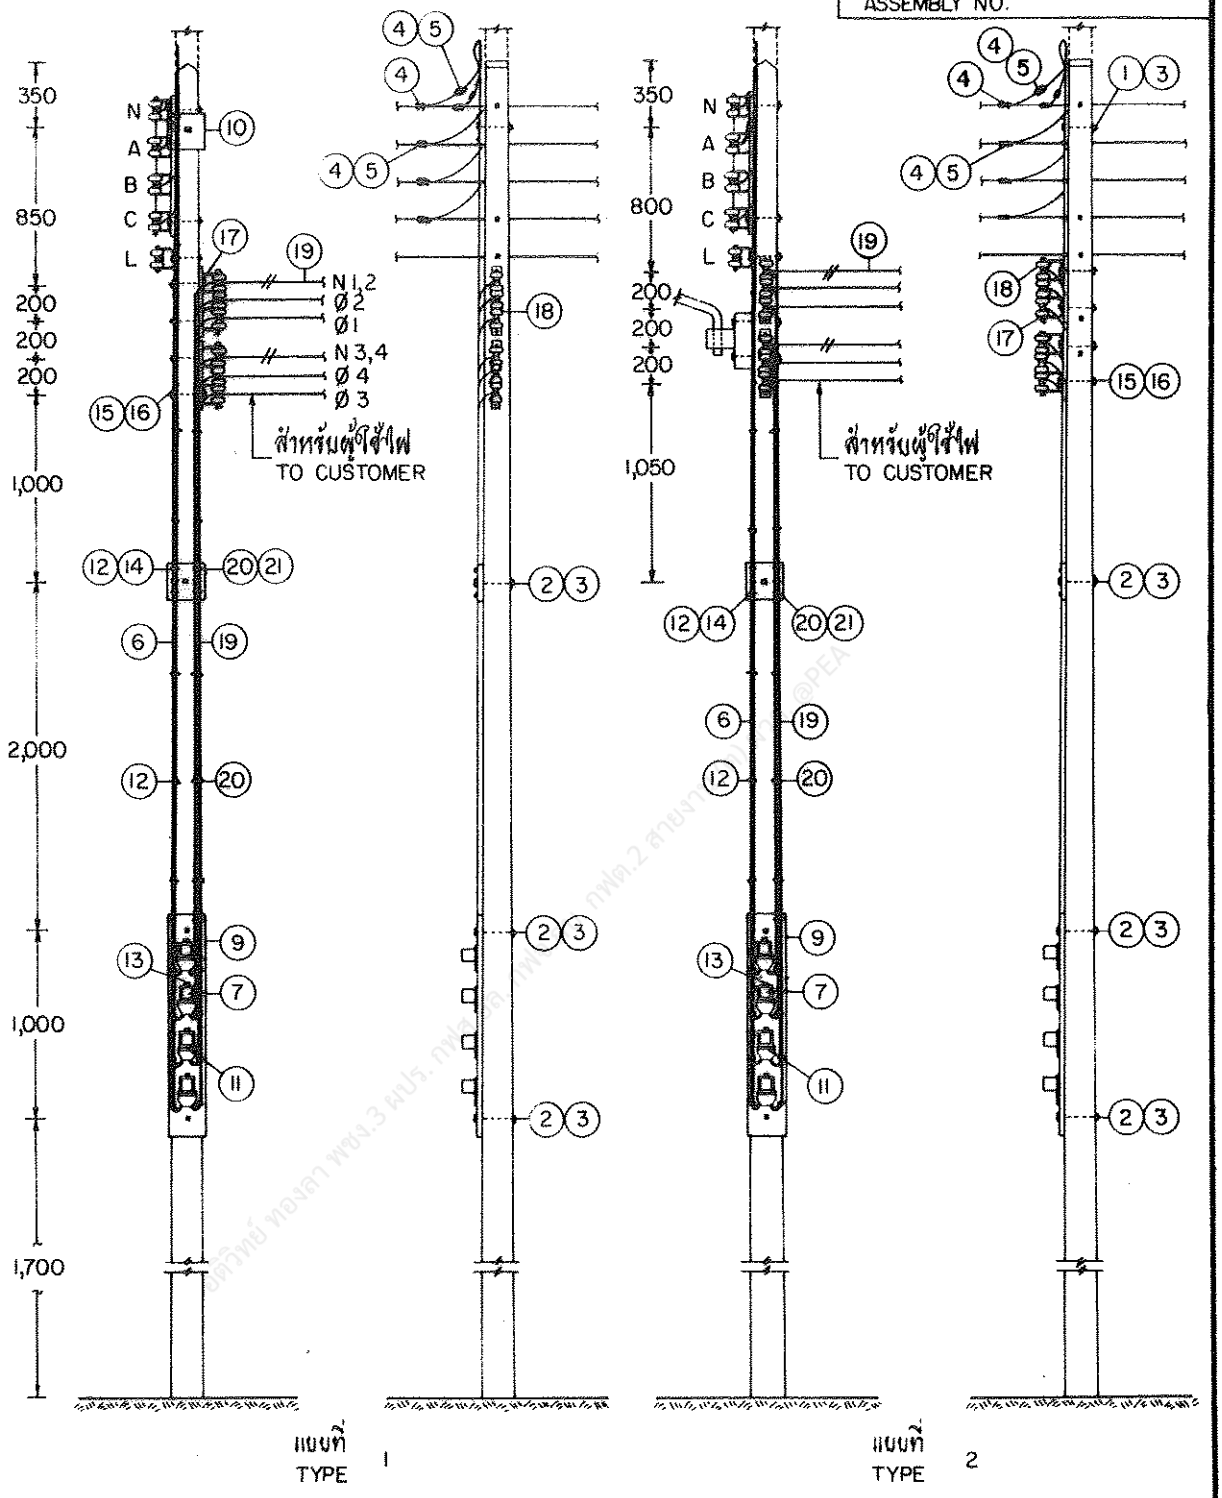

แบบที่ 1 TYPE 1

แบบที่ 2 TYPE 2

กองวิศวกรรมไฟฟ้าและเครื่องกล ฝ่ายวิศวกรรม ผู้เขียน ผู้สำรวจ วิศวกร หัวหน้าแผนก ผู้อำนวยการกอง ผู้อำนวยการฝ่าย รองผู้ว่าการฝ่ายเทคนิค	**การไฟฟ้าส่วนภูมิภาค** ผู้ว่าการ 13 มี.ค. 2538 การติดตั้งมิเตอร์ 1 เฟส 220 โวลต์ ขนาด 3-15 แอมป์ บนเสาคอนกรีต 9 ม. (สายเข้ามิเตอร์ทองแดง) 4. จำนวน 4 เครื่อง 3-15 A, 1-Ø, 220 V METER INSTALLATION ON 9 m CONCRETE POLE (Cu SERVICE ENTRANCE CABLE) 4. 4 UNITS	ใช้แทนแบบ ถูกแทนโดยแบบ เขียนเสร็จวันที่ 30 พ.ย. 37 แก้แบบวันที่ 12 พ.ค. 41 มิติเป็น มิลลิเมตร มาตราส่วน 1 : 40 แบบเลขที่ SA4-015/37033 แผ่นที่ 4 รวมจำนวน 6 แผ่น

การประกอบเลขที่ ASSEMBLY NO. **0525 A**

บัญชีวัสดุในส่วนที่ กฟภ. สงทุน
BILL OF MATERIAL FOR PEA.

ลำดับที่ ITEM	รายละเอียด DESCRIPTION	จำนวน REQ'D 1	2	3	4	วัสดุเลขที่ MAT. NO.
1	สลักเกลียว M 16 X 200 มม. BOLT, MACHINE, M 16 X 200 mm	1	1	1	1	01110202
	สลักเกลียว M 16 X 250 มม. สำหรับเสาคอนกรีต 12 ม. BOLT, MACHINE, M 16 X 250 mm, FOR 12 m CONCRETE POLE	1	1	1	1	01110203
2	สลักเกลียว M 16 X 250 มม. BOLT, MACHINE, M 16 X 250 mm	3	3	3	3	01110203
	สลักเกลียว M 16 X 300 มม. สำหรับเสาคอนกรีต 12 ม. BOLT, MACHINE, M 16 X 300 mm, FOR 12 m CONCRETE POLE	3	3	3	3	01110204
3	แหวนสี่เหลี่ยมแบน 52X52X4.5 มม. รู Ø 18 มม. มอก. 258 WASHER, SQUARE, FLAT, 52X52X4.5 mm, HOLE Ø 18 mm TIS 258	8	8	8	8	01180100
4	คอนเนคเตอร์ชนิดบีบ แบบ H ขนาดตามต้องการ CONNECTOR, COMRRESSION, H TYPE; SIZE AS REQUIRED	2	4	6	8	02320002-6
5	PVC เทป กว้าง 19 มม. (ใช้ความยาว 2 ม. ต่อ 1 จุด (มอก. 386) PVC TAPE, 19 mm WIDE (2 m LONG PER POINT) TIS 386	ม. m	ม. m	ม. m	ม. m	02180001 or 02180002
6 *	สายทองแดงหุ้มฉนวนเข้ามิเตอร์แรงต่ำ 600 V, 2X6 ต.มม. หรือ 2X10 ต.มม. CABLE, FOR SERVICE ENTRANCE, Cu, 600 V, 2X6 mm^2, OR 2X10 mm^2	6.5 ม. m	13 ม. m	19 ม. m	25 ม. m	02080500 or 02080501
7	วัตต์อาวร์มิเตอร์ 1 เฟส 2 สาย 220 โวลต์ ใช้กายนอก METER, WATTHOUR, SINGLE-PHASE, 2-WIRE 220 V, WEATHER PROOF	1	2	3	4	06000000-1 or 06000009
8	แป้นไม้รองเข้มิเตอร์ไสเกลี้ยง ขนาด 60X20X2 ซม. METER PLATE, HARD WOOD, SURFACE FINISHED, 60X20X2 cm	1	1	—	—	——
9	แป้นไม้รองเข้มิเตอร์ไสเกลี้ยง ขนาด 120X20X2 ซม. METER PLATE, HARD WOOD, SURFACE FINISHED, 120X20X2 cm	—	—	1	1	——
10	แป้นไม้สำหรับยึดสายเข้า และออกจากมิเตอร์ ไสเกลี้ยง ขนาด 20X20X2 ซม. CABLE PLATE, HARD WOOD, SURFACE FINISHED, 20X20X2 cm	2	2	2	2	——
11	หมายเลขผู้ใช้ไฟ (ดูตัวอย่างข้างล่าง) NUMBER OF CUSTOMER	1	2	3	4	——
12	เข็มขัดรัดสาย (ทำด้วยสเตอะลูมิเนียมแบน 1X10 มม.) ช่วงระยะ 50 ซม. CABLE STRAP (MADE OF ARMOUR TAPE 1X10 mm) AT 50 cm INTERVALS	2 ม. m	3 ม. m	5 ม. m	5 ม. m	02200000
13	ตะปูเกลียวชุบโครเมียม ขนาด 15-20 มม. SCREW, CHROME PLATED, SIZE 15-20 mm	3	6	9	12	
14	ตะปูหัวกลมแบน ยาว 15-20 มม. Ø1 มม. มอก. 113 NAIL, ROUND, MILD STEEL WIRE 15-20 mm LONG Ø1 mm TIS 113	24	24	40	40	

* — สายทองแดง ขนาด 2X6 ต.มม. สำหรับมิเตอร์ขนาด 3-5 แอมป์
— สายทองแดง ขนาด 2X10 ต.มม. สำหรับมิเตอร์ขนาด 15 แอมป์

แผ่นอะลูมิเนียม ขนาด 15 X 100 มม. หนา 0.5 มม.

รู Ø 3.5 มม.

322/1 25271

ใช้ที่ตอกตัวเลข ขนาดความสูง 10 มม. ทอก แล้วทาด้วยสีดำ ตามรอยตัวอักษร

ตัวอย่างหมายเลขผู้ใช้ไฟ

กองวิศวกรรมไฟฟ้าและเครื่องกล ฝ่ายวิศวกรรม ผู้เขียน ... ผู้ตรวจ ... วิศวกร ... หัวหน้าแผนก ... ผู้อำนวยการกอง ... ผู้อำนวยการฝ่าย ...	**การไฟฟ้าส่วนภูมิภาค** ผู้ว่าการ ... 18 มิถุนายน 2538 การติดตั้งมิเตอร์ 1 เฟส 220 โวลต์ ขนาด 3-15 แอมป์ บนเสาคอนกรีต 9 ม. (สายเข้ามิเตอร์ทองแดง) 3-15 A, 1-Ø, 220 V METER INSTALLATION ON 9 m CONCRETE POLE (Cu SERVICE ENTRANCE CABLE)	ใช้แทนแบบ ... ถูกแทนโดยแบบ ... เขียนแต่ครั้งที่ 30 พ.ย. 37 แก้แบบครั้งที่ 12 พ.ค. 41 มิติเป็น ... หมายเหตุ ... แบบเลขที่ SA4-015/37033 แผ่นที่ 5 จำนวน 6 แผ่น
ของผู้ว่าการฝ่ายเทคนิค ...		

การประกอบเลขที่ ASSEMBLY NO. **0525 A**

บัญชีวัสดุในส่วนของผู้ใช้ไฟ
BILL OF MATERIAL FOR CUSTOMER

ลำดับที่ ITEM	รายละเอียด DESCRIPTION	จำนวน REQ'D 1	2	3	4	วัสดุเลขที่ MAT. NO.
15	สลักเกลียว M 16 X 200 มม. BOLT, MACHINE, M 16 X 200 mm	2	2	4	4	01110202
	สลักเกลียว M 16 X 250 มม. สำหรับเสาคอนกรีต 12 ม. BOLT, MACHINE, M 16 X 250 mm, FOR 12 m CONCRETE POLE	2	2	4	4	01110203
16	แหวนสี่เหลี่ยมแบน 52X52X4.5 มม. รู Ø 18 มม. มอก. 258 WASHER, SQUARE, FLAT, 52X52X4.5 mm, HOLE Ø 18 mm TIS 258	2	2	4	4	01180100
17	แร็ค 2 X 200 มม. แบบหลังงอ RACK, SECONDARY, MEDIUM PRESSED STEEL, 2X200 mm, EXTENDED RACK	1	1	2	2	03130002
18	ลูกรอกแรงต่ำ มอก. 227 แบบ ข (แบบ 53-2) INSULATOR, SPOOL TYPE, L.T. TIS 227 TYPE B (CLASS 53-2)	2	3	5	6	03030000
19	สายอะลูมิเนียม หรือสายทองแดงหุ้มฉนวน PVC 750 โวลต์ 70°ซ. CABLE, AI OR Cu, PVC-INSULATED, 750 V, 70°C					02070100 or 02070101
20	เข็มขัดรัดสาย (ทำด้วยลวดอะลูมิเนียม 1X10 มม.) ช่วงระยะ 50 ซม. CABLE STRAP (MADE OF ARMOUR TAPE 1X10 mm) AT 50 cm INTERVALS	3 ม. m	3 ม. m	6 ม. m	6 ม. m	02200000
21	ตะปูหัวกลมแบน ยาว 15-20 มม. Ø1 มม. มอก. 113 NAIL, ROUND MILD STEEL WIRE 15-20 mm LONG Ø 1 mm TIS 113	24	24	40	40	

ข้อแนะนำในการติดตั้งแร็คแรงต่ำรับสายหลังมิเตอร์

ในกรณีที่ติดตั้งมิเตอร์ใหม่ จำนวน 3 หรือ 4 เครื่อง ในคราวเดียวกัน สามารถพิจารณาใช้แร็ค 4X200 มม. (วัสดุเลขที่ 03130002) แทนแร็ค 2X200 มม. วัสดุลำดับที่ 17 ได้ โดยลดจำนวนสลักเกลียว วัสดุลำดับที่ 15 คงเหลือ 2 ชุด และลดจำนวนแหวนสี่เหลี่ยม วัสดุลำดับที่ 16 คงเหลือ 2 อัน

ข้อแนะนำในการจัดทำเข็มขัดรัดสายด้วยลวดอะลูมิเนียมแบน 1X10 มม.

— ถ้าเป็นสายเข้า หรือ ออกจากมิเตอร์ จำนวน 1-2 เครื่อง ใช้ลวดอะลูมิเนียมแบน 1X10 มม. ยาว 15 ซม. ต่อหนึ่งชุด
— ถ้าเป็นสายเข้า หรือ ออกจากมิเตอร์ จำนวน 3-4 เครื่อง ——"—— ยาว 20 ซม. ——"——

หมายเหตุ

1 แบบนี้เหมาะสมสำหรับก่อสร้างในเขตเมือง หรือย่านชุมชน
2 การเข้าปลายสายอะลูมิเนียมหุ้ม PVC สีฟ้า และสายทองแดงหุ้มฉนวน ดูแบบเลขที่ SAI-015/21006 และ SAI-015/21005 (การประกอบเลขที่ 9529 และ 0520)
3 การติดตั้งมิเตอร์บนแป้นรองรับมิเตอร์ ดูแบบเลขที่ SA4-015/37030 (การประกอบเลขที่ 0524 A)

NOTES

1 THIS CONSTRUCTION DRAWING IS SUITABLE FOR URBAN AREA.
2 SKY BLUE PVC INSULATED ALUMINIUM CONDUCTOR AND INSULATED COPPER CONDUCTOR DEADENDING SEE DWG. NO. SAI-015/21006 AND SAI-015/21005 (ASSEMBLY NO. 9529 AND 0520)
3 METER INSTALLATION ON METER PLATE SEE DWG. NO. SA4-015/37030 (ASSEMBLY NO. 0524

กองวิศวกรรมไฟฟ้าและเครื่องกล ฝ่ายวิศวกรรม	**การไฟฟ้าส่วนภูมิภาค**	ใช้แทนแบบ ถูกแทนโดยแบบ
ผู้เขียน ตรวจสอบ ผู้ตรวจ หัวหน้าแผนก ผู้อำนวยการกอง ผู้อำนวยการฝ่าย	ผู้ว่าการ 18 มิถุนายน 2538	เขียนแบบเสร็จวันที่ 30 พ.ย. 37 แก้แบบวันที่ 12 พ.ค. 41 มิติเป็น มาตราส่วน
รองผู้ว่าการฝ่ายเทคนิค	การติดตั้งมิเตอร์ 1 เฟส 220 โวลต์ ขนาด 3-15 แอมป์ บนเสาคอนกรีต 9 ม. (สายเข้ามิเตอร์ทองแดง) 3-15 A, 1-Ø, 220 V METER INSTALLATION ON 9 m CONCRETE POLE (Cu SERVICE ENTRANCE CABLE)	แบบเลขที่ SA4-015/37033 แผ่นที่ 6 ของจำนวน 6 แผ่น