

การประกอบเลขที่ ASSEMBLY NO. 5702

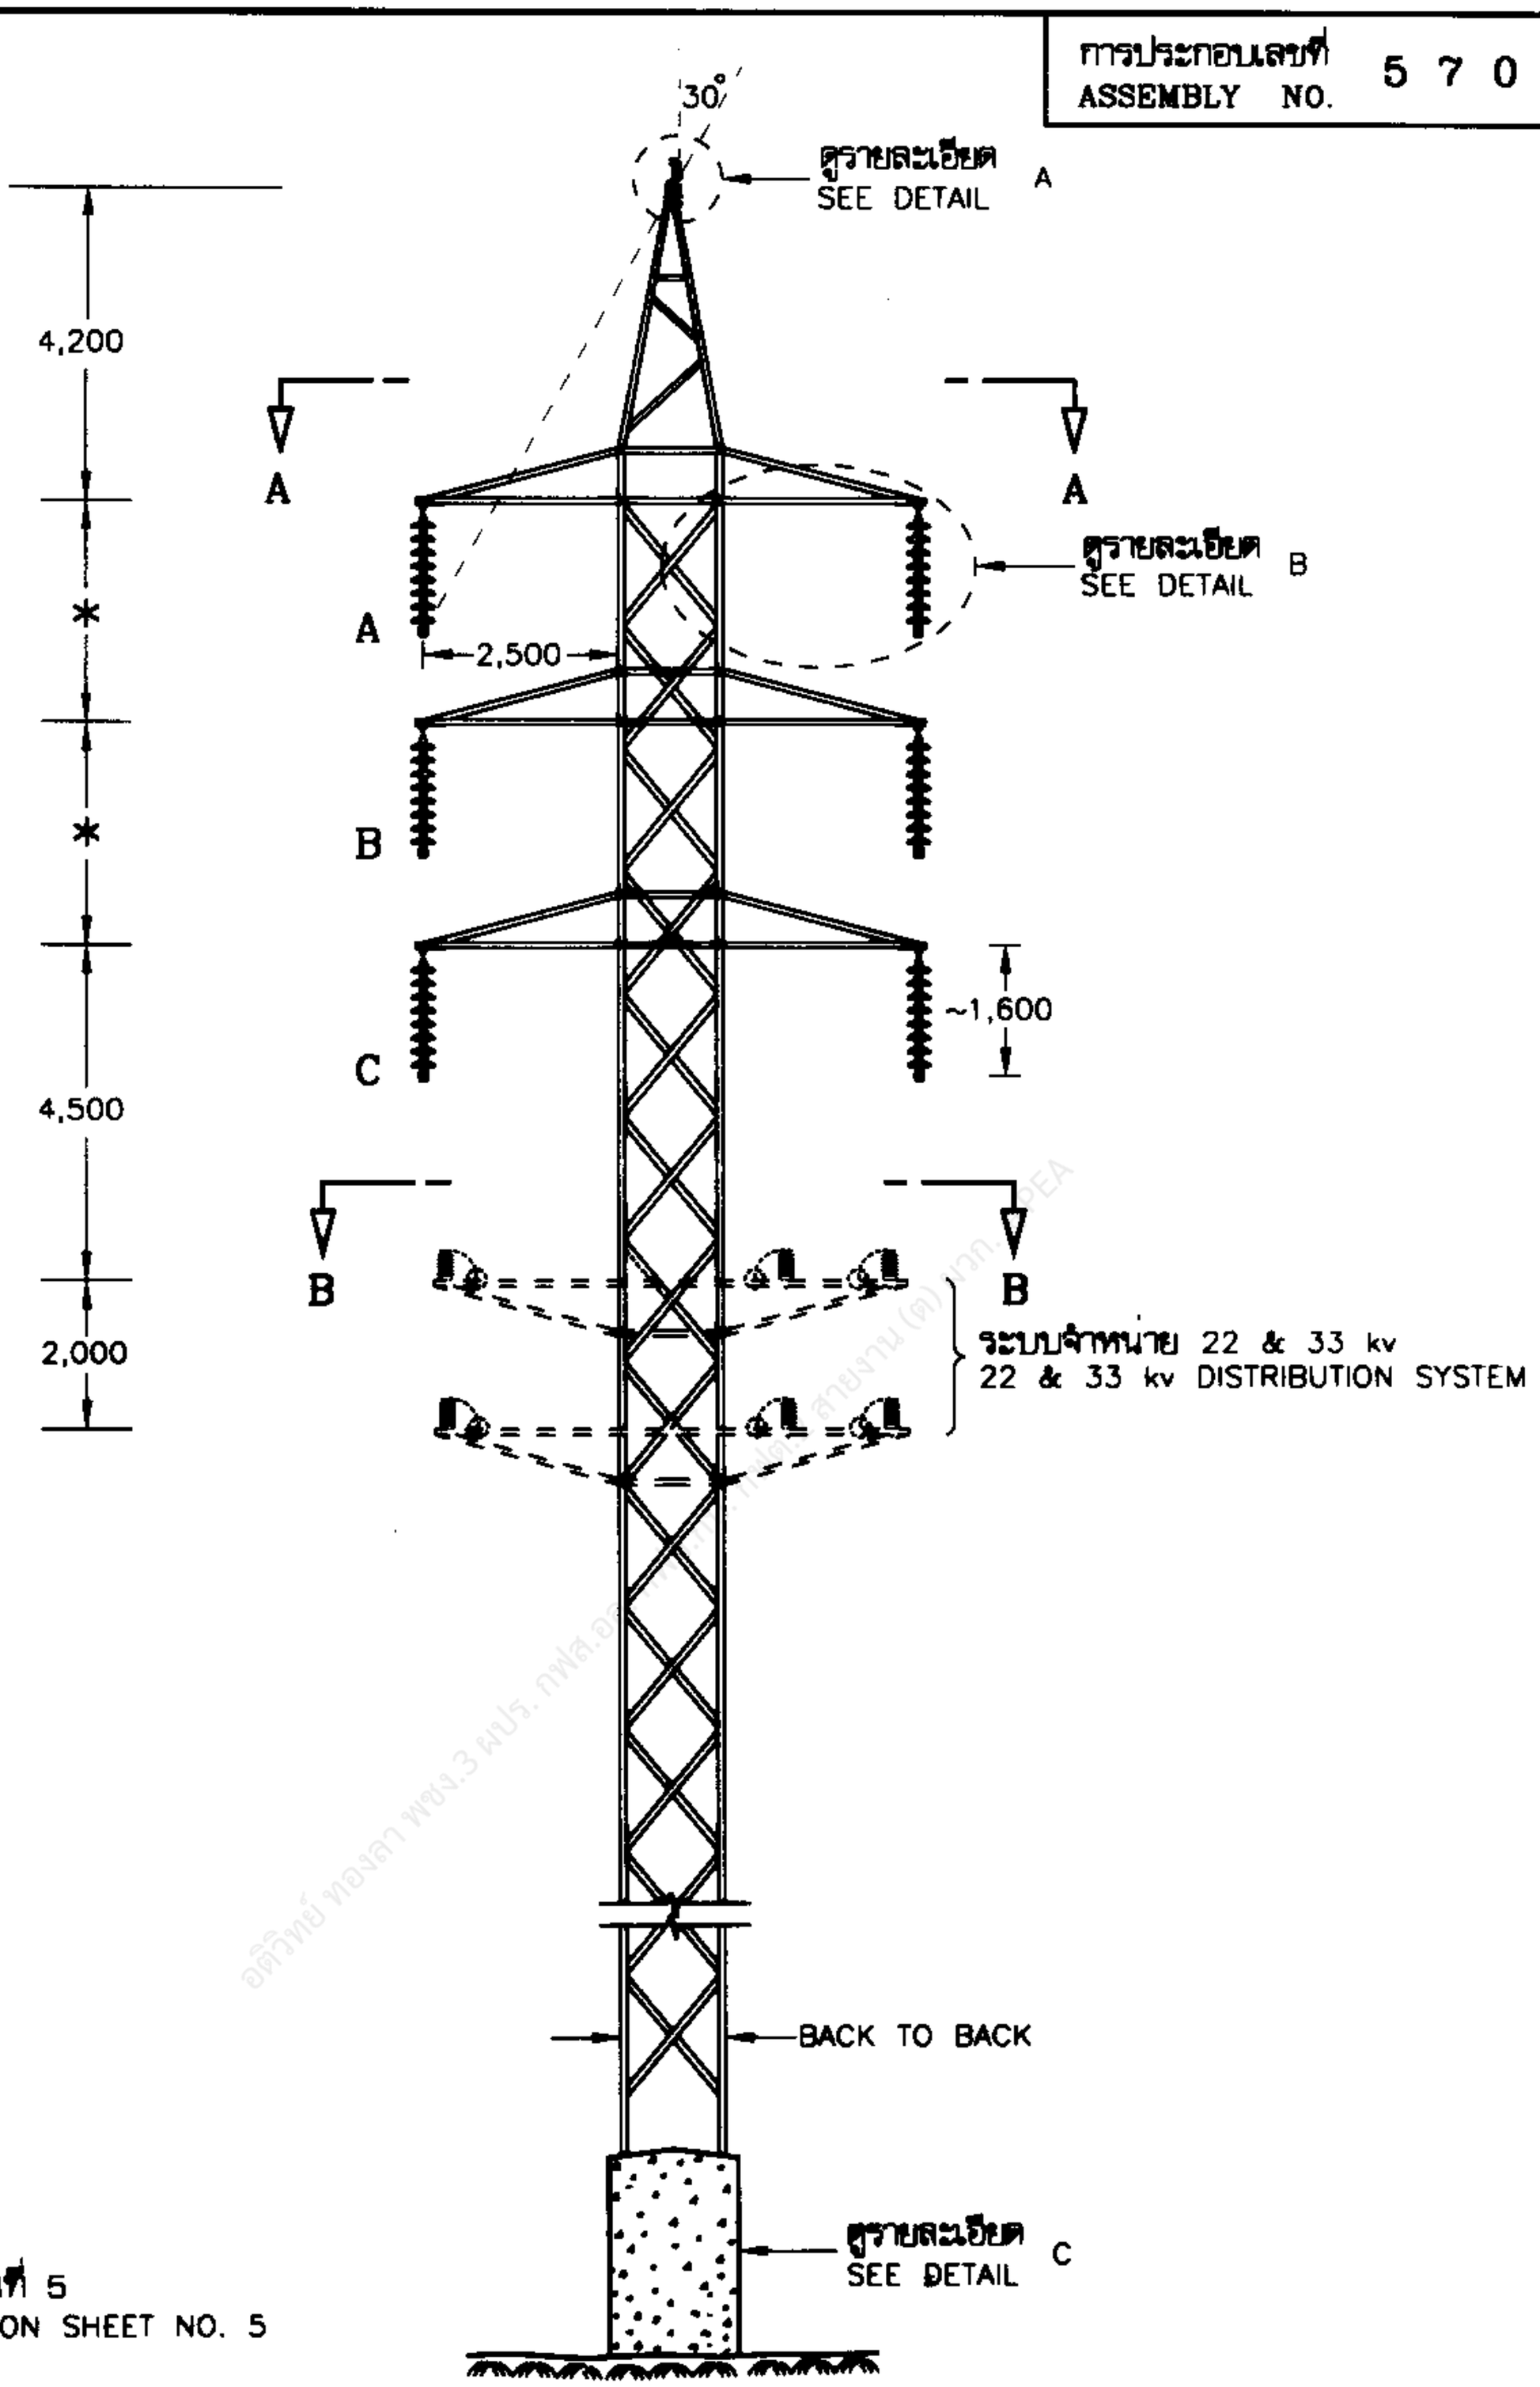


* ดูตาราง แผ่นที่ 5
SEE TABLE ON SHEET NO. 5

กองมาตรฐานระบบไฟฟ้า ฝ่ายมาตรฐานและความปลอดภัย	การไฟฟ้าส่วนภูมิภาค	ใช้แทนแบบ..... ถูกแทนโดยแบบ.....
ผู้เขียน สมชาย..... ผู้สำรวจ..... วิศวกร..... หัวหน้าแผนก..... ผู้อำนวยการกอง..... ผู้อำนวยการฝ่าย.....	ผู้ว่าการ..... 13 มิ.ย. 2545 โครงเหล็กทางตรง แบบที่ 1	เขียนเสร็จวันที่ 25 เมย. 45 แก้แบบวันที่..... มิติเป็น มิลลิเมตร มาตราส่วน 1 : 150
รองผู้ว่าการวางแผนและพัฒนาระบบไฟฟ้า 13 มิ.ย. 2545	STEEL TOWER, TANGENT STRUCTURE TYPE 1	แบบเลขที่ SA1-015/45006 แผ่นที่ 1 ของจำนวน 5 แผ่น

การประกอบเลขที่ ASSEMBLY NO. 5 7 0 2

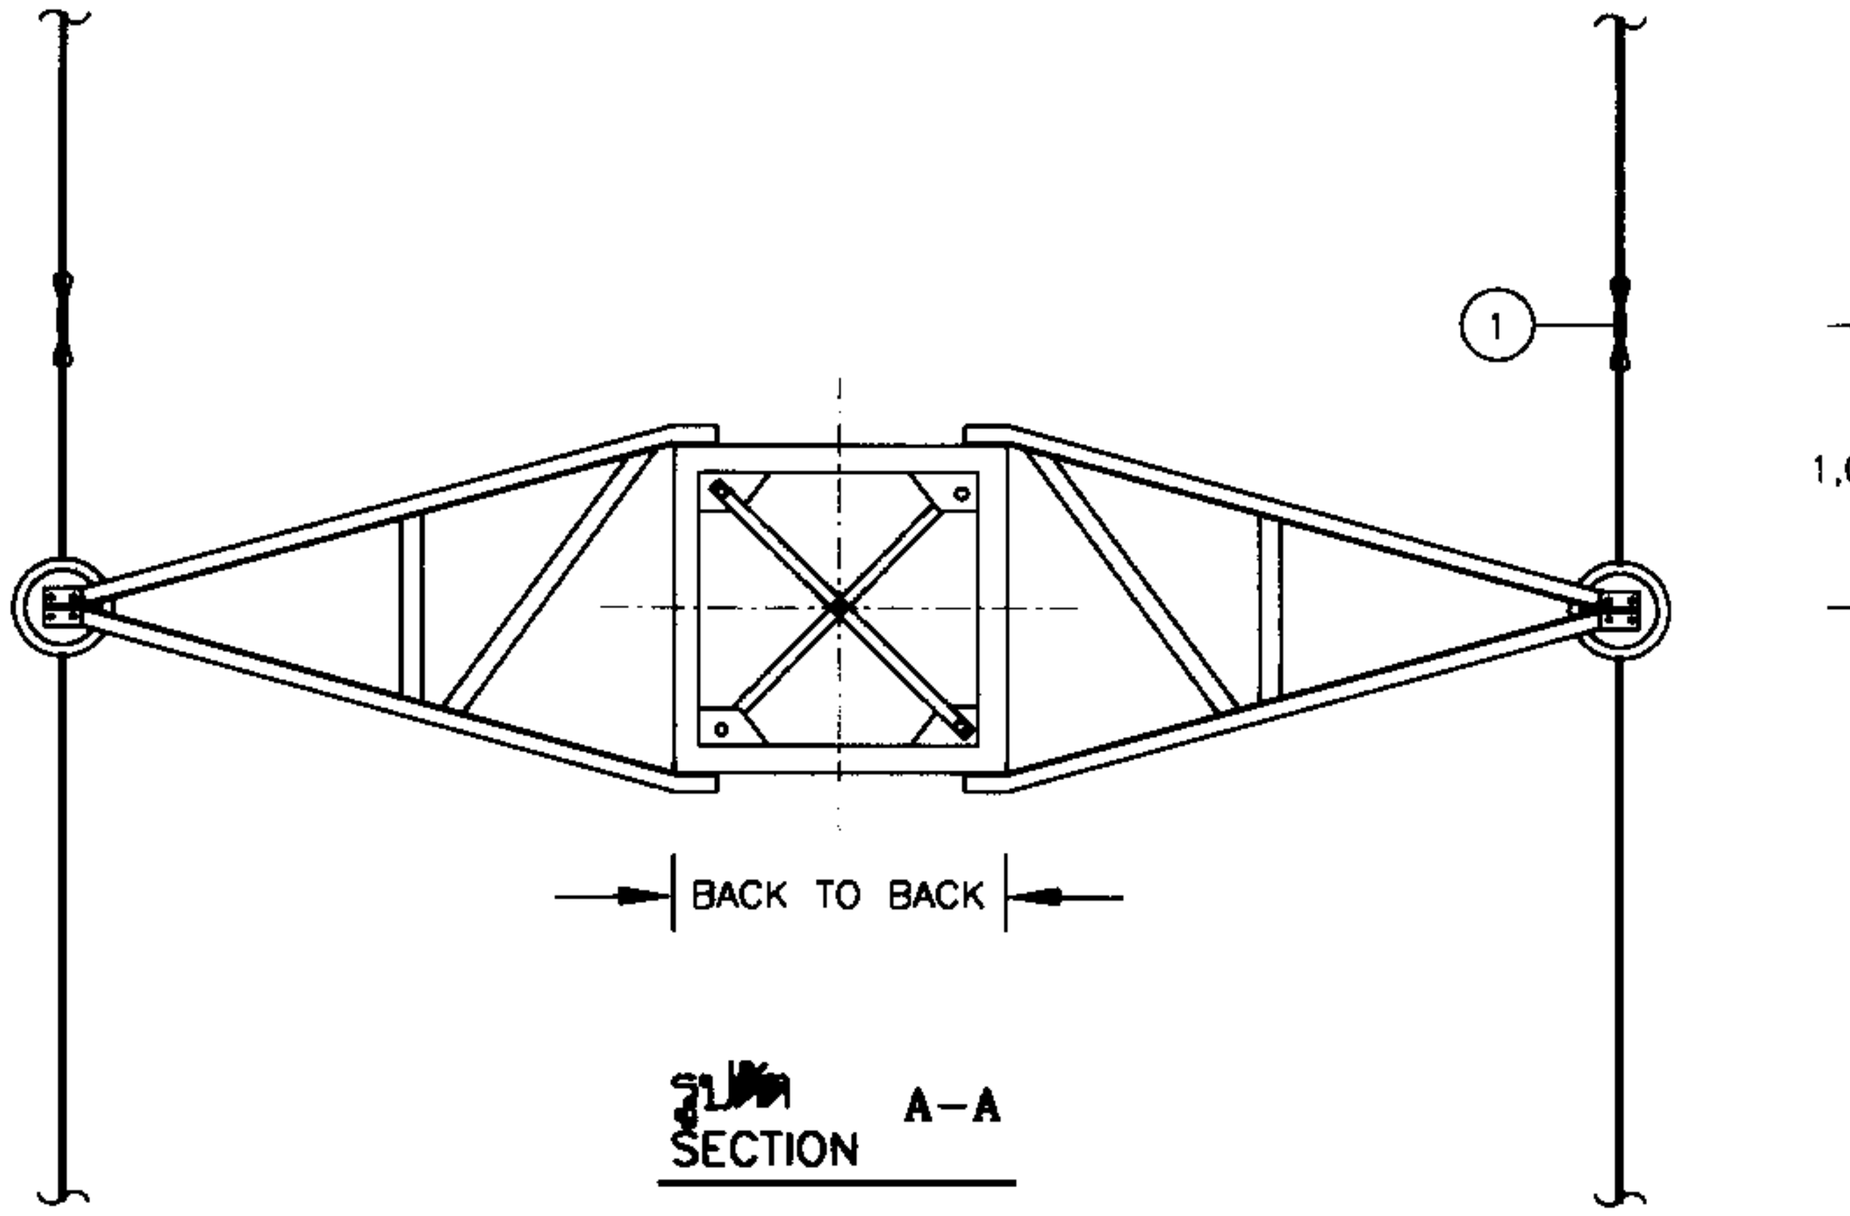

รูปตัด A–A
SECTION

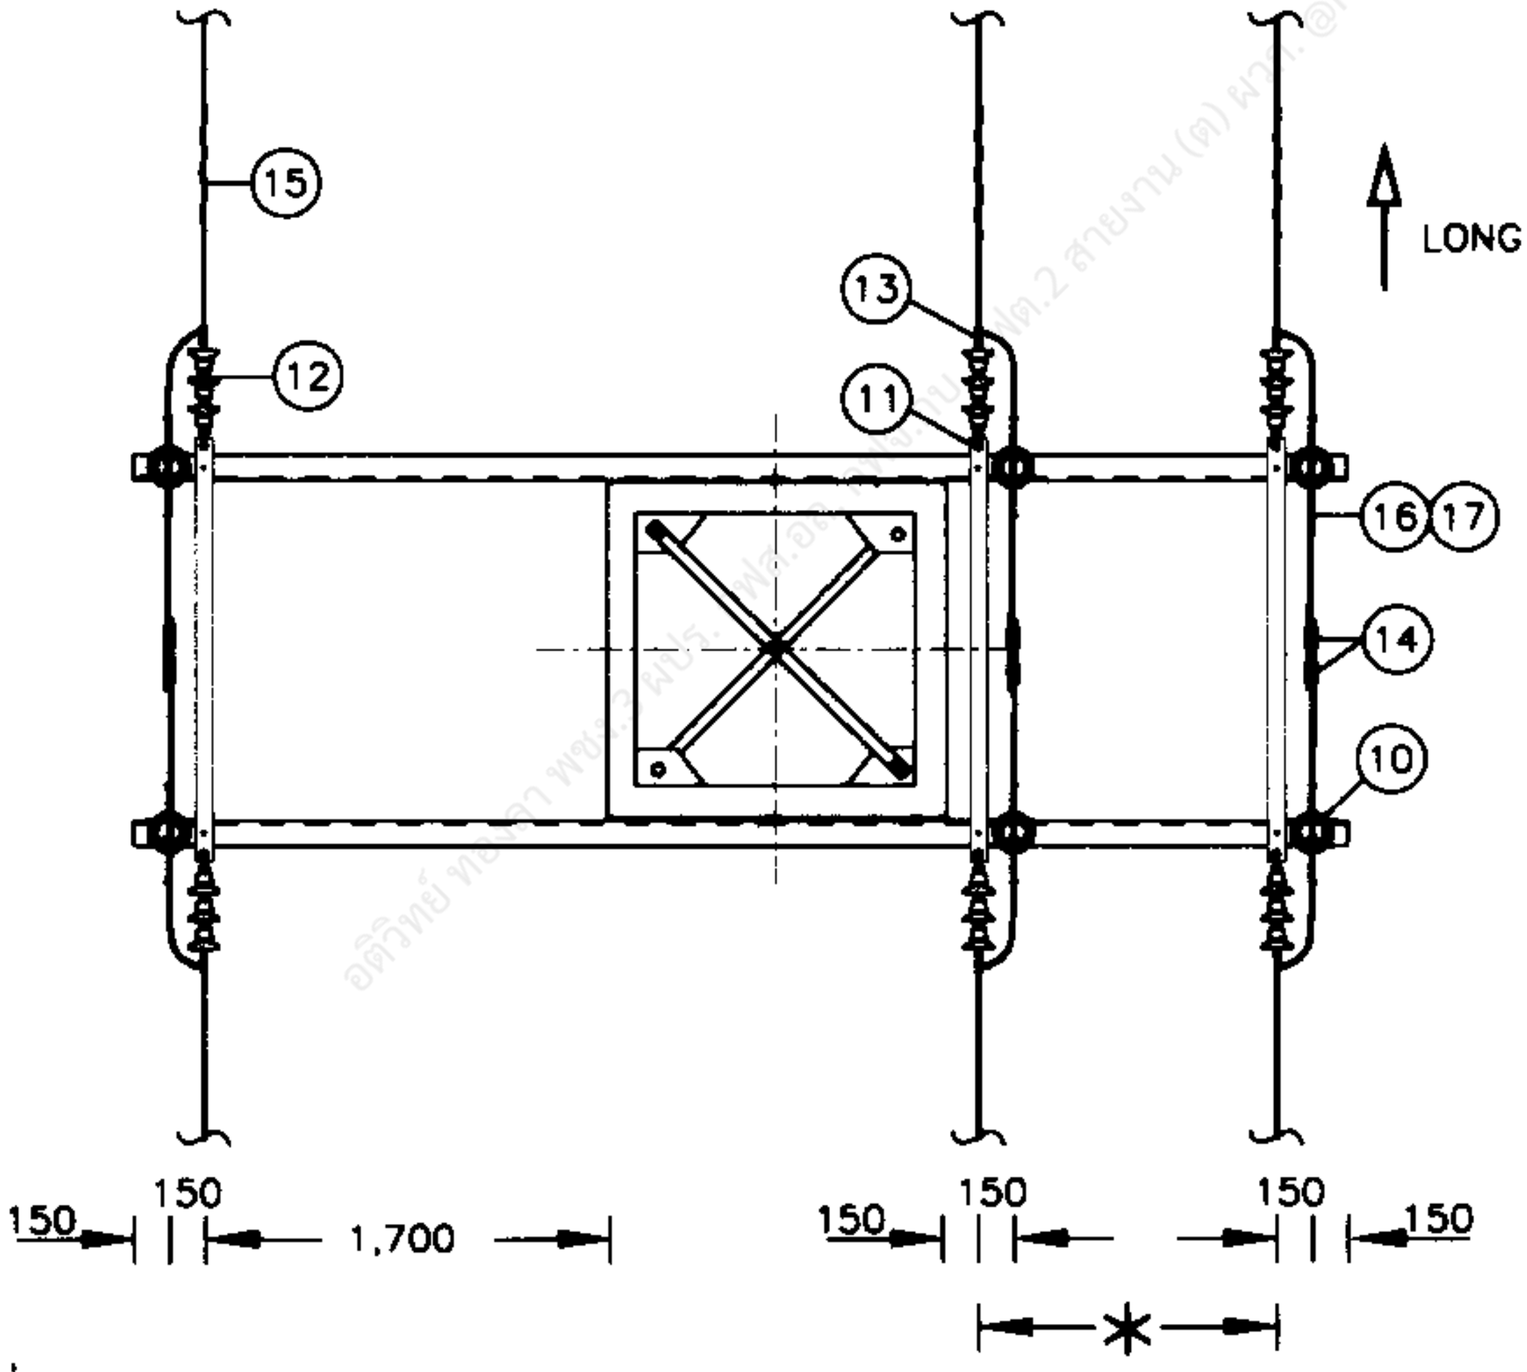


* ดูตาราง แผ่นที่ 5
SEE TABLE ON SHEET NO. 5


รูปตัด B–B
SECTION

กองมาตรฐานระบบไฟฟ้า ฝ่ายมาตรฐานและความปลอดภัย	การไฟฟ้าส่วนภูมิภาค	ใช้แทนแบบ ..... ถูกแทนโดยแบบ .....
ผู้เขียน สมชาย ..... ผู้สำรวจ ..... วิศวกร ..... หัวหน้าแผนก ..... ผู้อำนวยการกอง ..... ผู้อำนวยการฝ่าย	ผู้ว่าการ ..... 3 ก.ค. 2545 โครงเหล็กทางตรง แบบที่ 1	เขียนแล้วเสร็จวันที่ 25 เมษ. 45 แก้แบบวันที่ ..... มิติเป็น มิลลิเมตร มาตราส่วน 1 : 60
รองผู้ว่าการวางแผนและพัฒนาระบบไฟฟ้า	STEEL TOWER, TANGENT STRUCTURE TYPE 1	แบบเลขที่ SA1–015/45006 แผ่นที่ 2 ของจำนวน 5 แผ่น


การประกอบเลขที่ ASSEMBLY NO. 5 7 0 2

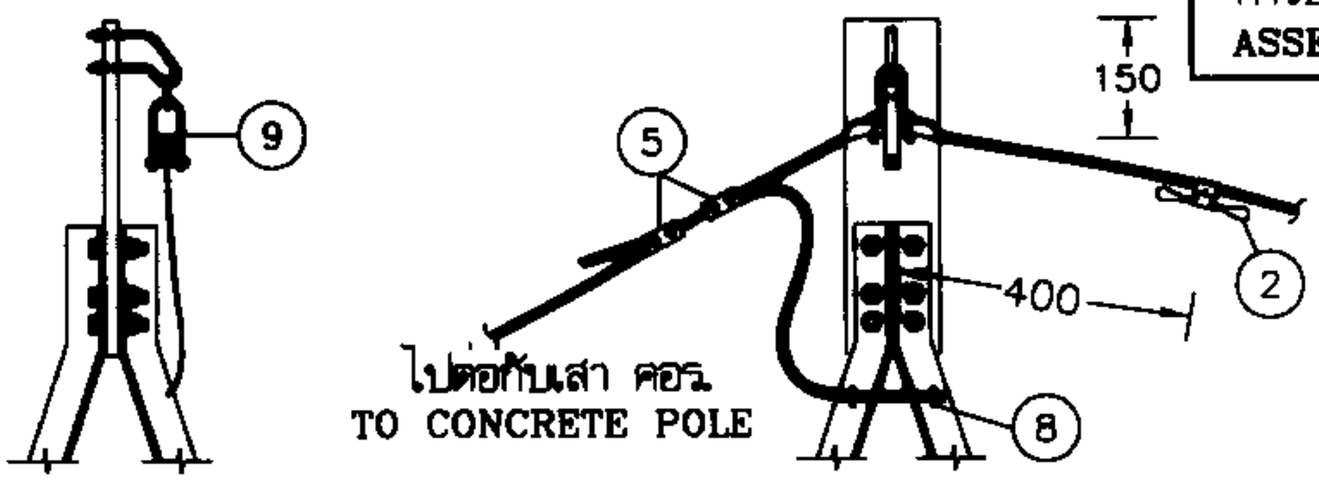

รายละเอียด A
DETAIL

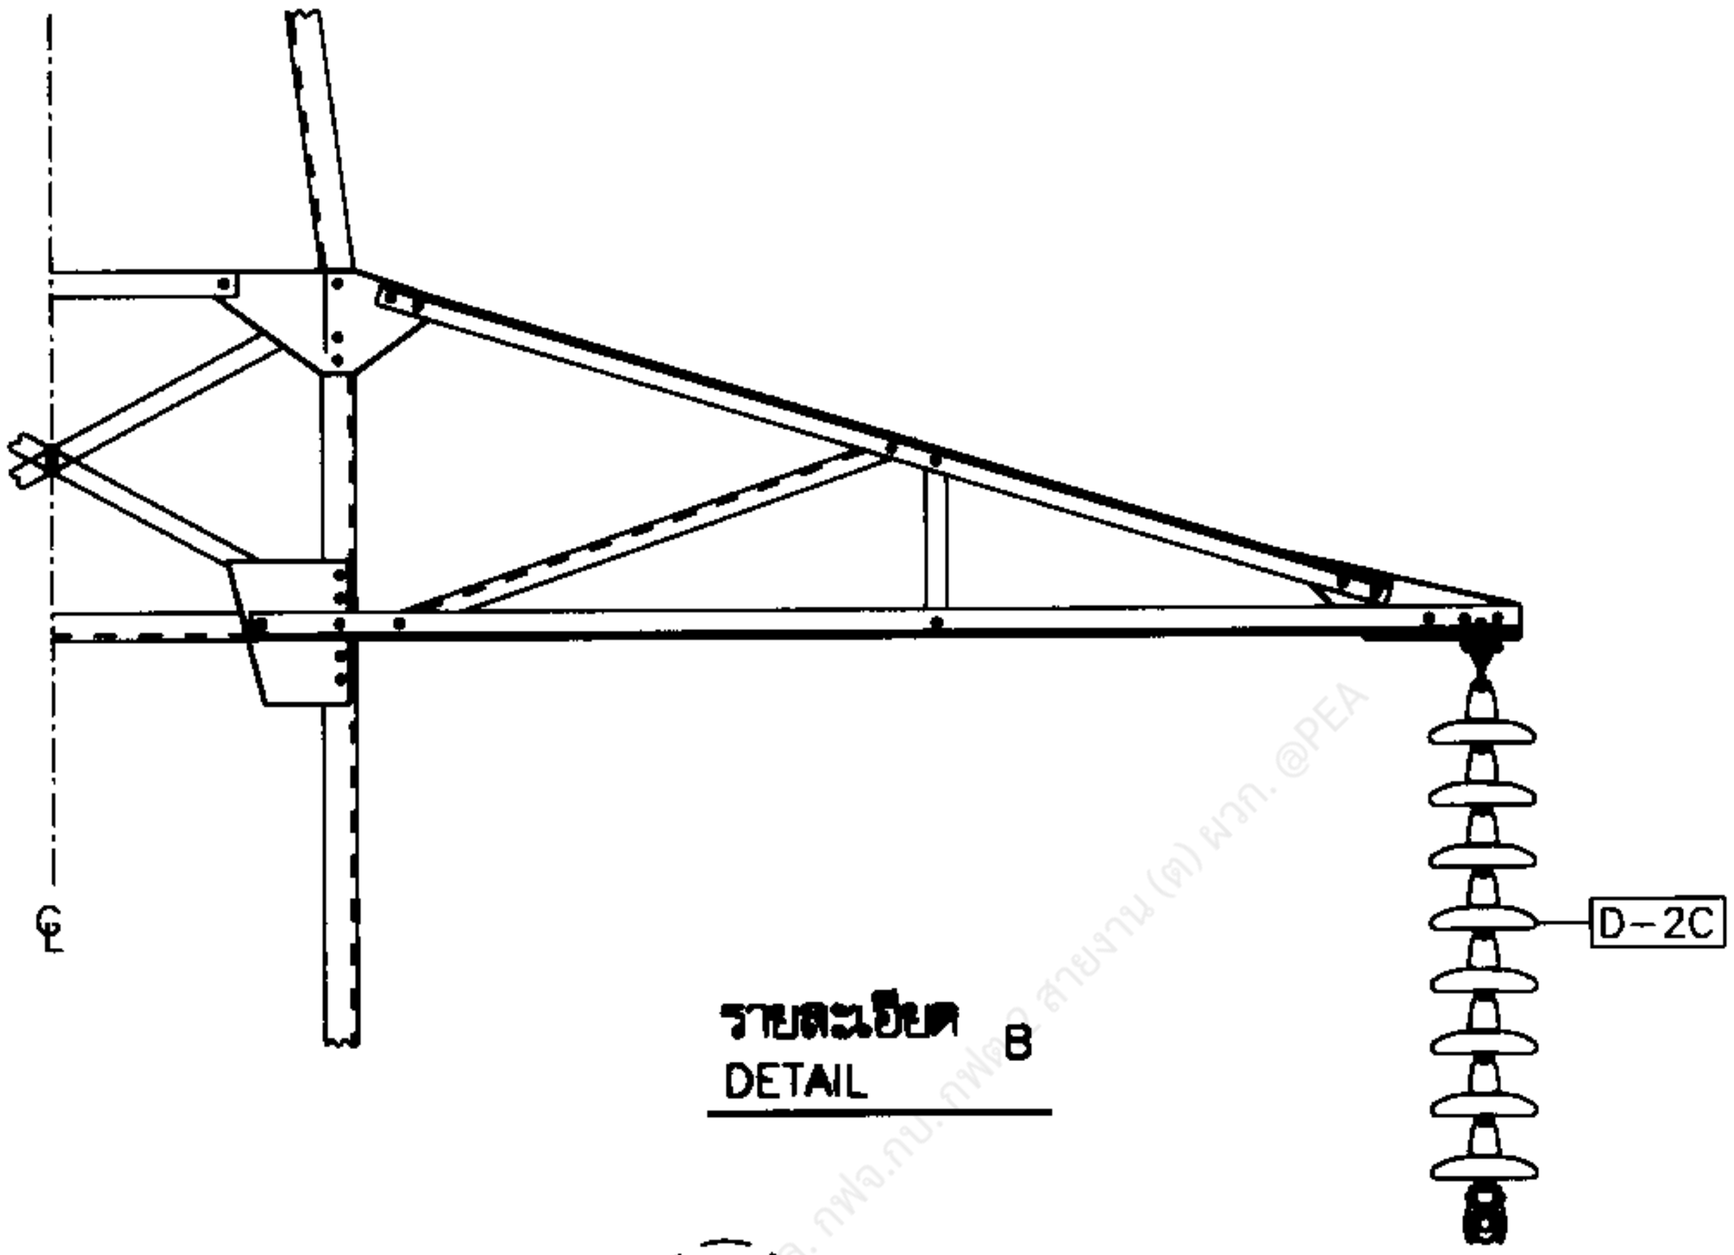

รายละเอียด B
DETAIL

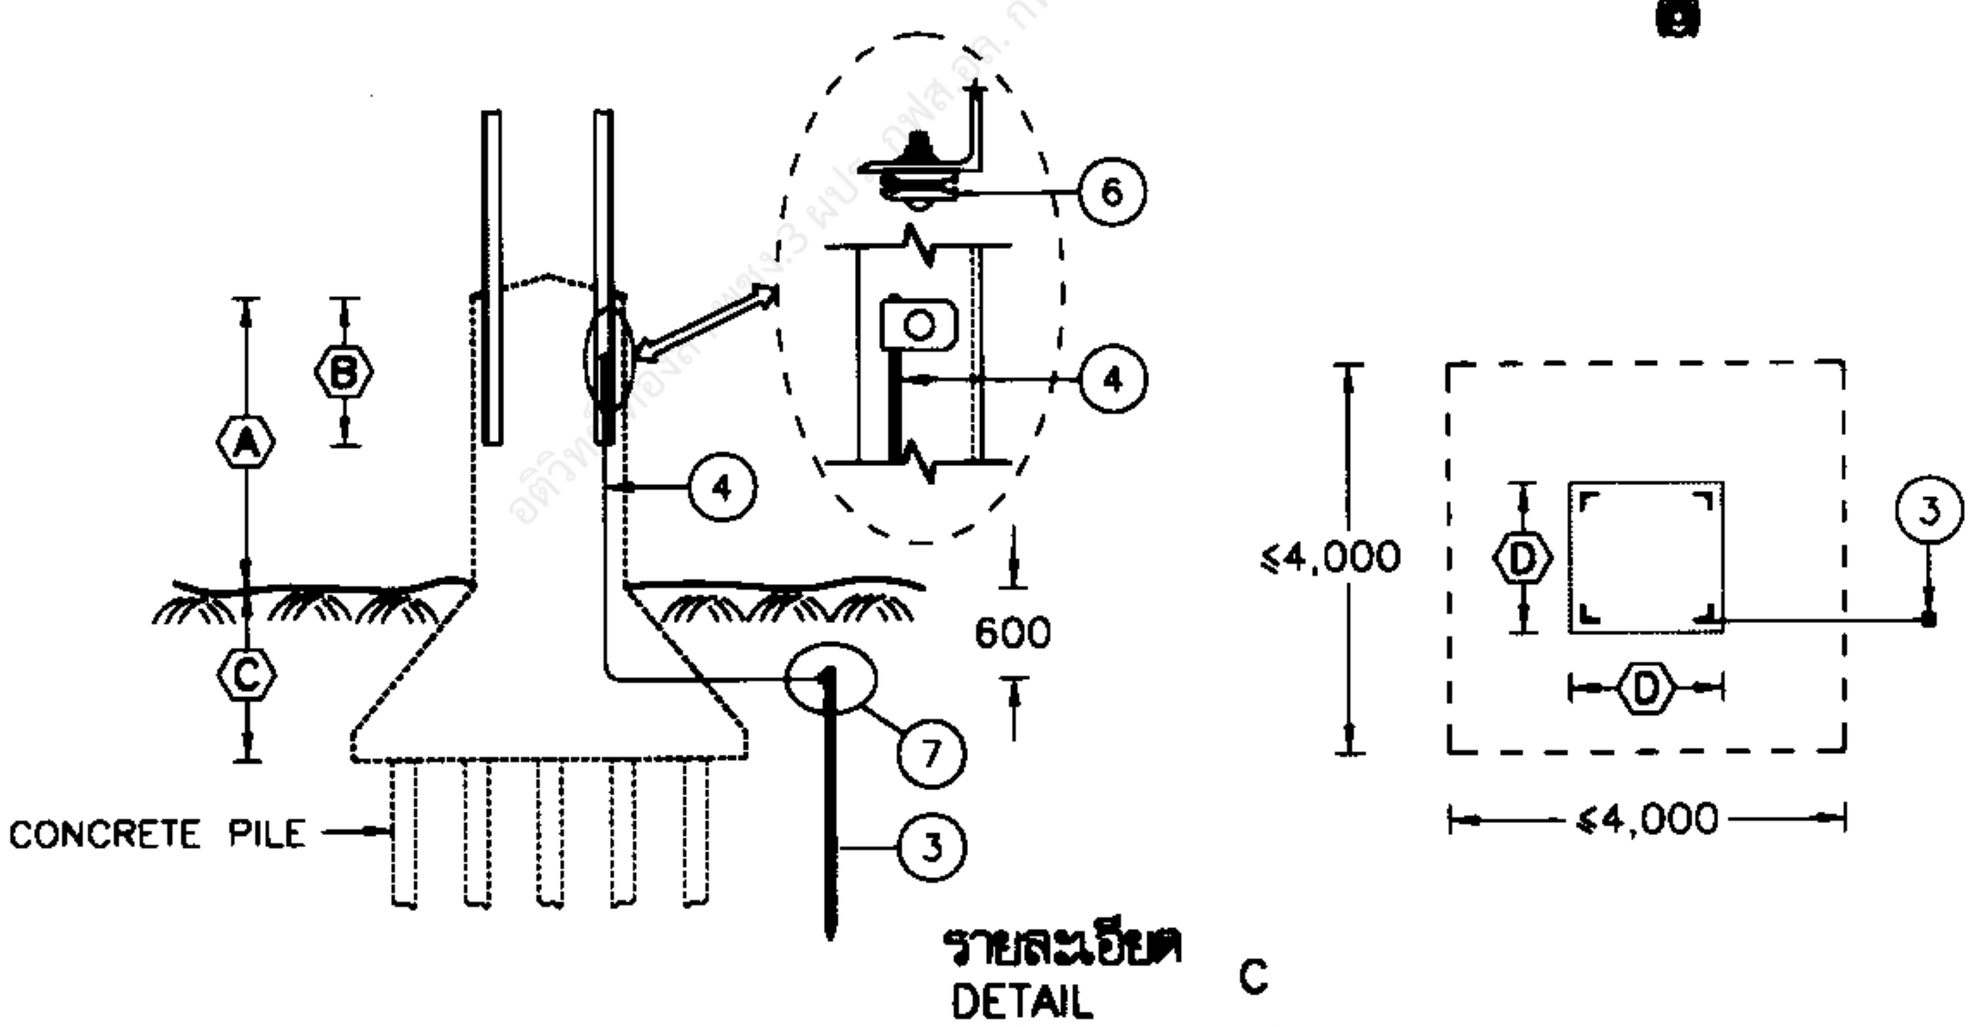

รายละเอียด C
DETAIL

กองมาตรฐานระบบไฟฟ้า ฝ่ายมาตรฐานและความปลอดภัย	การไฟฟ้าส่วนภูมิภาค	ใช้แทนแบบ ..... ถูกแทนโดยแบบ .....
ผู้เขียน สมชาย ..... ผู้สำรวจ ..... วิศวกร ..... หัวหน้าแผนก ..... ผู้อำนวยการกอง ..... ผู้อำนวยการฝ่าย	ผู้ว่าการ ..... 13 มิ.ย. 2545 โครงเหล็กทางตรง แบบที่ 1	เขียนเสร็จวันที่ 25 เมษ. 45 แก้แบบวันที่ ..... มิติเป็น มิลลิเมตร มาตราส่วน —
ของผู้ว่าการวางแผนและพัฒนาระบบไฟฟ้า	STEEL TOWER, TANGENT STRUCTURE TYPE 1	แบบเลขที่ SA1-015/45006 แผ่นที่ 3 ของจำนวน 5 แผ่น

การประกอบเลขที่ ASSEMBLY NO. 5702

บัญชีวัสดุ สำหรับระบบ 115 kV
BILL OF MATERIAL FOR 115 kV SYSTEM

ลำดับที่ ITEM	รายละเอียด DESCRIPTION	จำนวน REQ. D	วัสดุเลขที่ MAT. NO.
1	ไวบรชั่นแดมเปอร์ แบบดัมเบล สำหรับสายอะลูมิเนียมแกนเหล็ก ขนาด 380/50 ตร.มม. VIBRATION DAMPER, DUMBBELL; FOR 380/50 mm^2 ACSR	6	02200107
2	ไวบรชั่นแดมเปอร์ แบบดัมเบล สำหรับสายลวดเหล็กตีเกลียว ขนาด 50 ตร.มม. VIBRATION DAMPER, DUMBBELL; FOR 50 mm^2 STEEL STRANDED WIRE	1	02200100
3	หลักดินทำด้วยเหล็กเคลือบทองแดง ø 16 มม. ยาว 3 ม. จำนวนตามต้องการ ROD, GROUND, COPPER COVERED STEEL, 16 mm DIA., 3 m LONG, QUANTITIES AS REQUIRED		01220007
4	สายทองแดงเปลือย 95 ตร.มม. มอก. 64 ความยาวตามต้องการ CONDUCTOR, CU, BARE, 95 mm^2, TIS 64; QUANTITIES AS REQUIRED	ม. m	02000007
5	แคล้มป์สลัก 3 ตัว สำหรับลวดเหล็กตีเกลียว 50 ตร.มม. CLAMP, TRIPLE BOLTS; FOR 50 mm^2 STEEL STRANDED WIRE	2	01230004
6	แคล้มป์สายดินแบบร่องเดี่ยว สำหรับสายทองแดง 95 ตร.มม. CLAMP, GROUND, SINGLE GROOVE; FOR 95 mm^2 Cu CONDUCTOR	1	01230009
7	การต่อหลักดินแบบเชื่อมด้วยความร้อน ชนิดและจำนวนตามต้องการ GROUNDING, THERMO WELDING, QUANTITIES AS REQUIRED		–
8	ยูแคล้มป์ สลักเดี่ยว M 8 CLAMP, SINGLE U-BOLT, M 8	2	01230000
9	การวัดด้วยแคล้มป์ สำหรับเหล็กฉากรับสายล่อฟ้า GROUND WIRE SUPPORT AND CLAMP FOR BAYONET	1	01230203
	บัญชีวัสดุ สำหรับระบบ 22 & 33 kV **BILL OF MATERIAL FOR 22 & 33 kV SYSTEM**		
10	ลูกถ้วยไลน์โพสท์ไทพ์แบบ 57-2 หรือแบบ 57-3 มอก. 1077 INSULATOR, LINE POST TYPE, CLASS 57-2 OR 57-3, TIS 1077	12	03010001 or 03010103
11	ข้อต่อแบบ เคลวิส-อาย CLEVIS, EYE	12	03140000
12	ลูกถ้วยแขวน มอก. 354 แบบ ง (แบบ 52-4) INSULATOR, SUSPENSION TYPE, TIS 354, TYPE D (CLASS 52-4)	36	03020002
13	สเตรนแคล้มป์สำหรับสายอะลูมิเนียมแกนเหล็ก ขนาด 185/30 ตร.มม. CLAMP, STRAIN; FOR 185/30 mm^2 ACSR	12	03110004
14	พีจี คอนเนคเตอร์ 3 สลัก สำหรับสายอะลูมิเนียมแกนเหล็ก ขนาด 185/30 ตร.มม. CONNECTOR, PARALLEL GROOVE, TRIPLE BOLT; FOR 185/30 mm^2 ACSR	12	02300103
15	ไวบรชั่น แดมเปอร์ แบบสไปแรล สำหรับสายอะลูมิเนียมแกนเหล็กขนาด 185/30 ตร.มม. VIBRATION DAMPER, SPIRAL; FOR 185/30 mm^2 ACSR	6 หรือ or 12	02200103
16	ลวดอะลูมิเนียมกลม 4.0 มม. ความยาวตามต้องการ TIE, WIRE, AL, ø 4.0 mm; LENGTH AS REQUIRED	ม. m	02200002
17	ลวดอะลูมิเนียมแบน 1x10 มม. ความยาวตามต้องการ TAPE, ARMOUR, AL, 1x10 mm; LENGTH AS REQUIRED	ม. m	02200000
	รายละเอียด **DESCRIPTION**		
	การประกอบลูกถ้วยแขวน D-2C SUSPENSION, INSULATOR ASSEMBLY, D-2C	6	

กองมาตรฐานระบบไฟฟ้า ฝ่ายมาตรฐานและความปลอดภัย	การไฟฟ้าส่วนภูมิภาค	ใช้แทนแบบ..... ถูกแทนโดยแบบ..... เขียนเสร็จวันที่ 25 เมย. 45 แก้แบบวันที่ ..... มิติเป็น — มาตราส่วน —
ผู้เขียน สมชาย..... ผู้สำรวจ..... วิศวกร..... หัวหน้าแผนก..... ผู้อำนวยการกอง..... ผู้อำนวยการฝ่าย.....	ผู้ว่าการ.....	
รองผู้ว่าการวางแผนและพัฒนาระบบไฟฟ้า.....	โครงเหล็กทางตรง แบบที่ 1 — 13 มิ ย. 2545	
	STEEL TOWER, TANGENT STRUCTURE TYPE 1	แบบเลขที่ SA1-015/45006 แผ่นที่ 4 ของจำนวน 5 แผ่น

กฟภ. @PEA

การประกอบเลขที่ ASSEMBLY NO.	5 7 0 2

หมายเหตุ

1. โครงสร้างของโครงเหล็ก (Ⓐ,Ⓑ,Ⓒ,Ⓓ, และขนาด BACK TO BACK) ผู้รับจ้างเป็นผู้ออกแบบและต้องส่งรายการคำนวณให้ กฟภ. พิจารณาอนุมัติก่อนดำเนินการก่อสร้าง
2. แนะนำให้ใช้โครงเหล็ก แบบนี้ที่ระยะห่างเสาไม่เกิน 350 เมตร และมีมุมเบี่ยงเบน ไม่เกิน 1°
3. จำนวนวงจรของระบบจำหน่าย 22 & 33 kV ใต้ไลน์ 115 kV ไม่เกิน 2 วงจร
4. การประกอบไวเบรชั่นแดมเปอร์ แบบสไปแรล ดูแบบเลขที่ SA1-015/22019 (การประกอบเลขที่ 9557)
5. รายละเอียดเพิ่มเติม ดูแบบเลขที่ SA1-015/45005 (การประกอบเลขที่ 5701)

NOTES

1. THE STRUCTURE OF STEEL TOWER (Ⓐ,Ⓑ,Ⓒ,Ⓓ AND BACK TO BACK) SHALL BE DESIGNED BY THE CONTRACTOR AND SUBMITED CALCULATION SHEET TO PEA FOR APPROVAL BEFORE CONSTRUCTION .
2. SPAN OF STEEL TOWER IS RECOMMENDED TO BE NO MORE THAN 350 METERS AND LINE DEFLECTION ANGLE TO BE NO MORE THAN 1° DEGREE .
3. THE NUMBER OF 22 & 33 kV DISTRIBUTION LINE UNDER 115 kV SYSTEM NO MORE THAN TWO(2) CIRCUITS.
4. SPIRAL VIBRATION DAMPER ASSEMBLY, SEE DWG. NO. SA1-015/22019 (ASSEMBLY NO. 9557)
5. FOR MORE DETAILS SEE DWG. NO. SA1-015/45005 (ASSEMBLY NO. 5701) .

✳ ระยะห่างเฟส (A กับ B และ B กับ C) ดูตามตารางข้างล่างนี้
PHASE SPACING (A TO B AND B TO C) IS SHOWN IN TABLE BELOW .

ระยะห่างเสา SPAN LENGTH (ม) (m)		200-250	251-300	301-350
ระยะห่างเฟส PHASE SPACING (ม) (m)	ระบบ 115 kV 115 kV SYSTEM	2.7	3.0	3.2
	ระบบ 22&33 kV 22&33 kV SYSTEM	1.5	1.7	1.9

กองมาตรฐานระบบไฟฟ้า ฝ่ายมาตรฐานและความปลอดภัย	การไฟฟ้าส่วนภูมิภาค	ใช้แทนแบบ..... ถูกแทนโดยแบบ..... เขียนเสร็จวันที่ 25 เม.ย. 45 แก้แบบวันที่ ..... มีดเป็น ..... มาตราส่วน .....
ผู้เขียน สมชาย..... ผู้สำรวจ..... วิศวกร..... หัวหน้าแผนก..... ผู้อำนวยการกอง..... ผู้อำนวยการฝ่าย.....	ผู้ว่าการ.....	
ของผู้ว่าการวางแผนและพัฒนาระบบไฟฟ้า	โครงเหล็กทางตรง แบบที่ 1 — 13 มี.ค. 2545 STEEL TOWER, TANGENT STRUCTURE TYPE 1	แบบเลขที่ SA1-015/45006 แผ่นที่ 5 ของจำนวน 5 แผ่น