


การประกอบเลขที่ ASSEMBLY NO. 3502

ตำแหน่ง

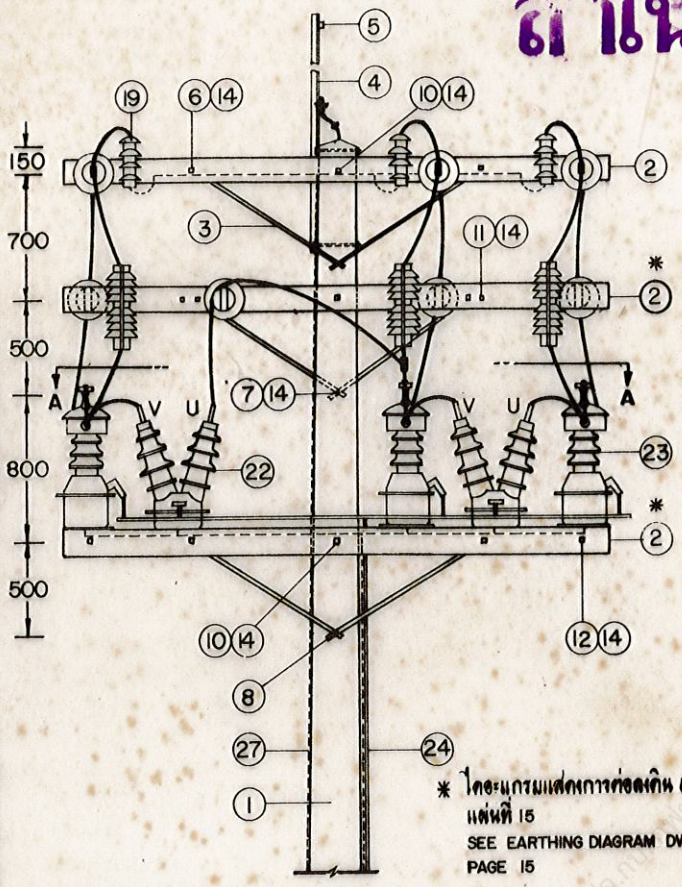


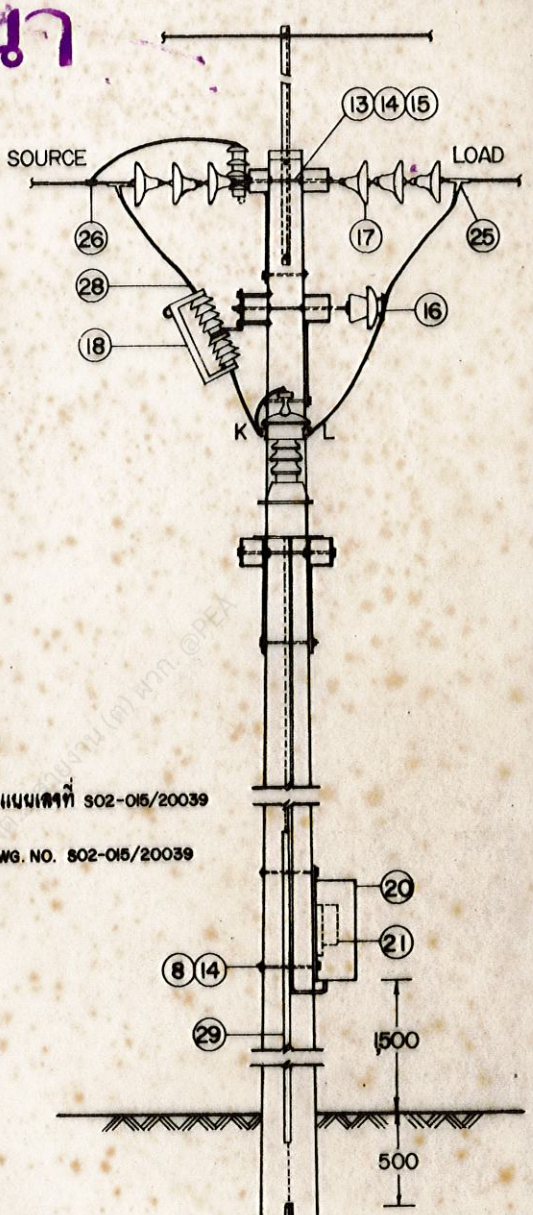

* โดยะแกรมแสดงการต่อลงดิน แบบเลขที่ S02-015/20039 แผ่นที่ 15
SEE EARTHING DIAGRAM DWG. NO. S02-015/20039 PAGE 15

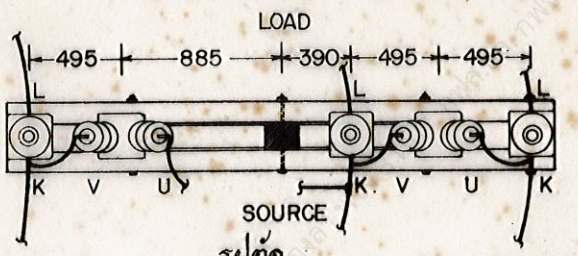

รูปตัด A–A
SECTION

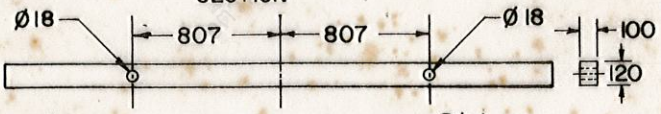

* (2) ไม้คอนสายเจาะรูพิเศษ สำหรับเหล็กประกับไม้คอน
CROSSARM, WOOD, SPECIAL DRILLING FOR BRACE





สำหรับสายเป็นกลางแรงต่ำของพี.ที. ซี.ที. เปลือกของ พี.ที. ซี.ที. และตู้มิเตอร์
FOR P.T, C.T SECONDARY P.T, C.T CASE AND METER CABINET

กองวิศวกรรม	การไฟฟ้าส่วนภูมิภาค	ใช้แทนแบบ S02-015/16068
ผู้เขียน	ผู้ว่าการ ..... 8 ธ.ค. 18	ถูกแทนโดยแบบ .....
สถาปนิก	การติดตั้งพี.ที.และซี.ที.สำหรับมิเตอร์แรงสูง 3 เฟส 4 สาย ระบบ 33 kV ก ครอพเอาต์ฟิวส์ดัดเอาต์แบบ หนึ่ง อินซูเลเตอร์	เขียนเสร็จวันที่ 27 พ.ค. 18
วิศวกร		แก้แบบวันที่ .....
หัวหน้าแผนก		มิติเป็น ..... ม.ม.
ผู้อำนวยการกอง		มาตราส่วน 1:40
รองผู้ว่าการฝ่ายเทคนิค	P.T. & C.T. INSTALLATION FOR 3-PHASE 4-WIRE H.T. METER 33 kV SYSTEM A DROP OUT FUSE CUTOUT SINGLE INSULATOR TYPE	แบบเลขที่ S02-015/18033
		แผ่นที่ 1 จำนวน 4 แผ่น


การประกอบเลขที่ ASSEMBLY NO. 3502

สำเนา

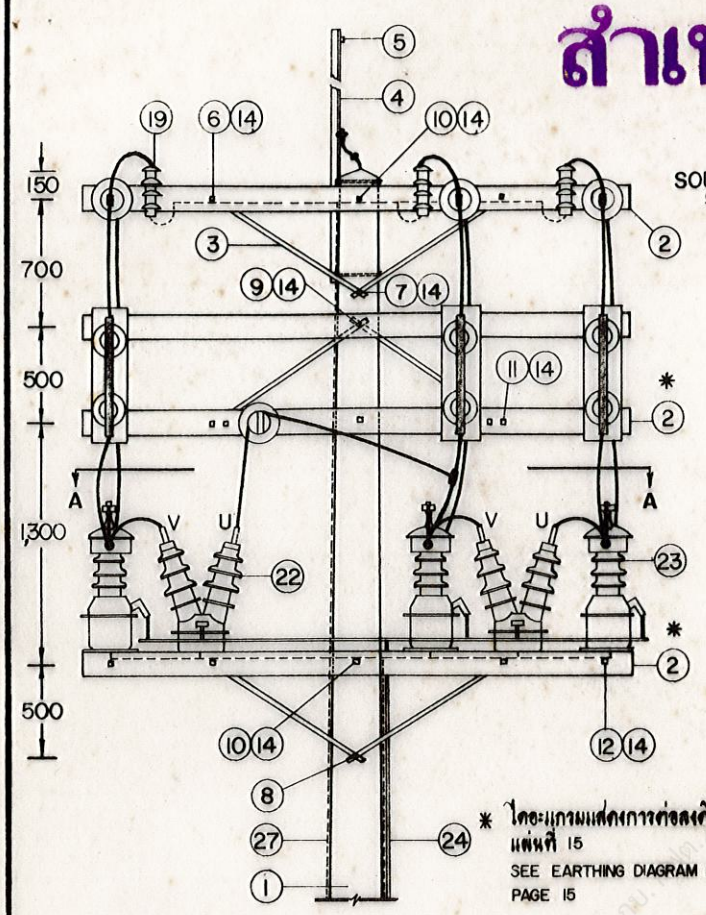


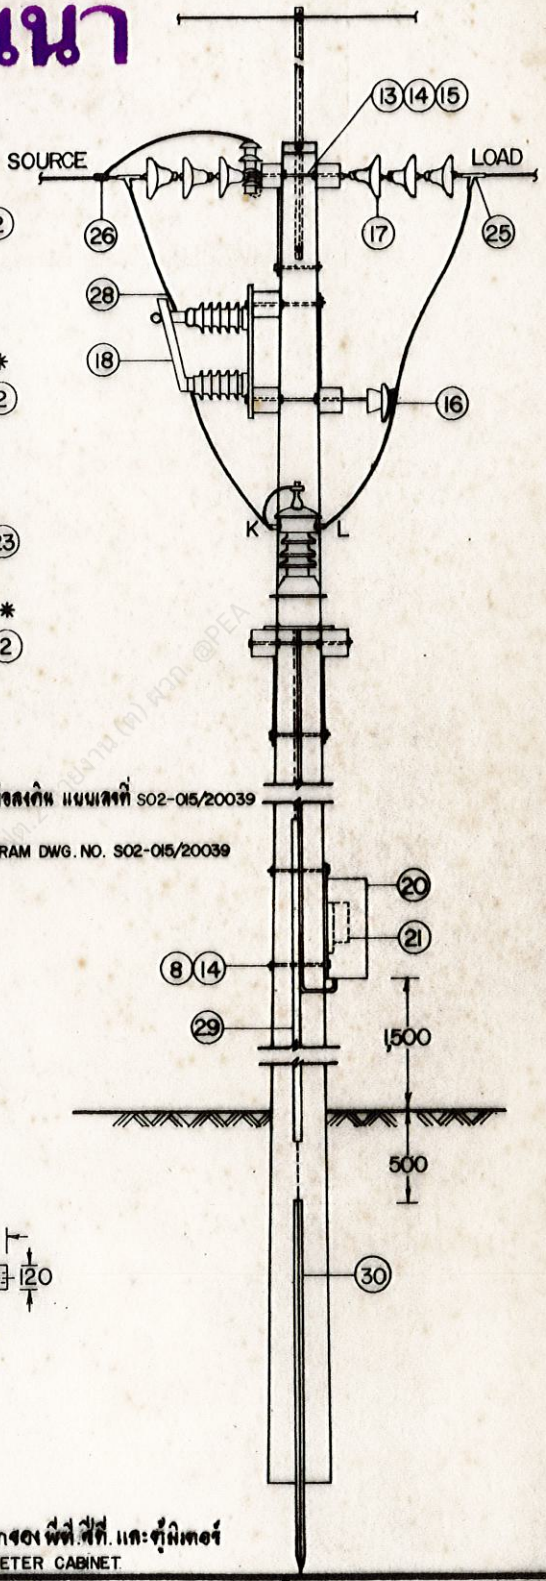


* ไดอะแกรมแสดงการต่อลงดิน แบบเลขที่ S02-015/20039 แผ่นที่ 15
SEE EARTHING DIAGRAM DWG. NO. S02-015/20039 PAGE 15

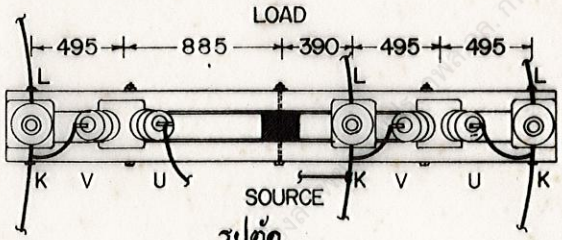

รูปตัด A — A
SECTION

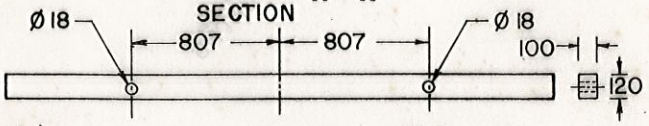

* (2) ไม้คอนสายเจาะรูพิเศษ สำหรับเหล็กประกับไม้คอน
CROSSARM, WOOD, SPECIAL DRILLING FOR BRACE

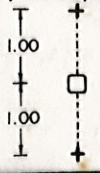

สำหรับล่อฟ้าแรงสูง
FOR H.T. LIGHTNING ARRESTER

สำหรับสายเส้นกลางแรงต่ำของหม้อ P.T. ซีที. เปลือกของ พีที. ซีที. และตู้มิเตอร์
FOR P.T., C.T SECONDARY P.T., C.T CASE AND METER CABINET

กองวิศวกรรม	การไฟฟ้าส่วนภูมิภาค	ใช้แทนแบบ S02-015/16068
ผู้เขียน	ผู้ว่าการ	ถูกแทนโดยแบบ
สถาปนิก	การติดตั้งพีทีและซีทีสำหรับมิเตอร์แรงสูง 3 เฟส 4 สาย ระบบ 33 kV ชนิดครอบเอาต์ฟิวส์ดัดเอาต์แบบ สอง อินซูเลเตอร์	เขียนเสร็จวันที่ 27 พ.ค. 18
วิศวกร		แก้แบบวันที่
หัวหน้าแผนก	P.T. & C.T. INSTALLATION FOR 3-PHASE 4-WIRE H.T. METER 33 kV SYSTEM B DROP OUT FUSE CUTOUT TWO INSULATORS TYPE	มิติเป็น N.N.
ผู้อำนวยการกอง		มาตราส่วน 1 : 40
รองผู้ว่าการฝ่ายเทคนิค		แบบเลขที่ S02-015/18033
		แผ่นที่ 2 ของจำนวน 4 แผ่น

การประกอบเลขที่ ASSEMBLY NO. 3502

บัญชีวัสดุ
BILL OF MATERIAL

ลำดับที่ ITEM	รายละเอียด DESCRIPTION	จำนวน REQ'D ก/A	จำนวน REQ'D ข/B	วัสดุเลขที่ MAT. NO.
1	เสาคอนกรีต 12 เมตร POLE, CONCRETE 12 m LONG	1	1	00010004
2	ไม้คอนสายแรงสูง 100 X 120 X 3000 มม. CROSSARM, WOOD, H.T. 100 X 120 X 3000 mm	6	7	00100003
3	เหล็กประกับไม้คอน 40 X 6 X 1000 มม. BRACE, FLAT, FOR CROSSARM 40 X 6 X 1000 mm	8	8	01200002
4	เหล็กฉากรับสายล่อฟ้า 60 X 60 X 6 มม. ยาว 3000 มม. OVERHEAD GROUND WIRE BAYONET 60 X 60 X 6 mm 3000 mm LONG	1	1	01010006
5	กราวด์ วายร์ แคล้มป์ เจ 1152 GROUND WIRE CLAMP J 1152	1	1	01230205
6	สลักเกลียว M 16 X 130 มม. BOLT, MACHINE, M 16 X 130 mm	8	8	01110200
7	สลักเกลียว M 16 X 200 มม. BOLT, MACHINE, M 16 X 200 mm	2	1	01110202
8	สลักเกลียว M 16 X 250 มม. BOLT, MACHINE, M 16 X 250 mm	5	5	01110203
9	สลักเกลียว M 16 X 300 มม. BOLT, MACHINE, M 16 X 300 mm	-	1	01110204
10	สลักเกลียว M 16 X 400 มม. BOLT, MACHINE, M 16 X 400 mm	3	3	01110206
11	สลักเกลียวตลอด M 16 X 400 มม. BOLT, DOUBLE ARMING, M 16 X 400 mm	2	2	01120000
12	สลักเกลียวตลอด M 16 X 450 มม. BOLT, DOUBLE ARMING, M 16 X 450 mm	2	2	01120001
13	สลักเกลียวห่วงกลม M 16 X 400 มม. BOLT, DOUBLE ARMING, ROUND EYE, M 16 X 400 mm	3	3	01130000
14	แหวนสี่เหลี่ยมแผน 52 X 52 X 4.5 มม. รู Ø 18 มม. มอก. 258 WASHER, SQUARE, FLAT 52 X 52 X 4.5 mm HOLE Ø 18 mm TIS 258	50	50	01180100
15	นัทรูปห่วง M 16 DIN 582 NUT, EYE, M 16 DIN 582	3	3	01180001
16	ลูกถ้วยก้านตรง 33 kV มอก.279 แบบ ค (แบบ 56-3) พร้อมก้าน INSULATOR, PIN TYPE, 33 kV TIS 279 TYPE C (CLASS 56-3) COMP. WITH PIN	4	4	03000002 03100001
17	ลูกถ้วยแขวน มอก. 354 แบบ ง (แบบ 52-4) INSULATOR, SUSPENSION TYPE, TIS 354 TYPE D (CLASS 52-4)	18	18	03020002
18 A	ครอพเอาท์ ฟิวส์คัตเอาท์หนึ่งอินซูเลเตอร์ 33 kV 100 หรือ 200 แอมป์ CUT-OUT, FUSE, OPEN TYPE, SINGLE INSULATOR, DROP OUT, 33 kV, 100 OR 200 A	3	-	04010100 or 04010101
18 B	ครอพเอาท์ ฟิวส์คัตเอาท์สองอินซูเลเตอร์ 33 kV 100 หรือ 200 แอมป์ CUT-OUT, FUSE, OPEN TYPE, TWO INSULATORS, DROP OUT, 33 kV, 100 OR 200 A	-	3	04019911 or 04019912
19	ล่อฟ้า 30 kV 5 กิโลแอมป์ LIGHTNING ARRESTER, 30 kV, 5 kA	3	3	04000100

สำเนา

กองวิศวกรรม	การไฟฟ้าส่วนภูมิภาค	ใช้แทนแบบ S02-015/16068
ผู้เขียน	ผู้ว่าการ	ถูกแทนโดยแบบ .....
สถาปนิก	การติดตั้งพีทีและซีที สำหรับมิเตอร์แรงสูง 3 เฟส 4 สาย ระบบ 33 kV	เขียนเสร็จวันที่ 27 พ.ค. 18
วิศวกร	ค บัญชีวัสดุ	แก้แบบวันที่ .....
หัวหน้าแผนก	P.T. & C.T. INSTALLATION FOR 3-PHASE 4-WIRE H.T. METER 33 kV SYSTEM C BILL OF MATERIAL	มิติเป็น .....
ผู้อำนวยการกอง		มาตราส่วน .....
รองผู้ว่าการฝ่ายเทคนิค		แบบเลขที่ S02-015/18033
		แผ่นที่ 3 รวมจำนวน 4 แผ่น

การประกอบเลขที่ ASSEMBLY NO. 3502

บัญชีวัสดุ
BILL OF MATERIAL

ลำดับที่ ITEM	รายละเอียด DESCRIPTION	จำนวน REQ'D ก/A	จำนวน REQ'D ข/B	วัสดุเลขที่ MAT. NO.
20	ตู้โลหะมิเตอร์แรงสูง พร้อมแป้นไม้ ALUMINIUM METER CASE FOR HIGH TENSION METER COMPLETE WITH METER PLATE	1	1	06100007
21	ดีมานด์มิเตอร์ ชนิดสะสม 3 เฟส 4 สาย 110/64 โวลต์ 5 แอมป์ DEMAND METER, CUMULATIVE, 3 - PHASE, 4 - WIRE 110/64 V 5 A	1	1	06000304
22	พี ที หนึ่งเฟสใช้นอกอาคาร 33000-110 โวลต์ พร้อมอุปกรณ์ติดตั้ง TRANSFORMER, POTENTIAL, 1Ø, OUTDOOR, 33000-110 V COMP. WITH MOUNTING ACCESS.	2	2	06020100
23	ซี ที ใช้นอกอาคาร 33 kV เรโชตามต้องการ พร้อมอุปกรณ์ติดตั้ง TRANSFORMER, CURRENT, OUTDOOR, 33 kV, RATIO AS REQ'D, COMP. WITH MOUNTING ACCESS.	3	3	06340100 - 06040106
24	คอนโทรลเคเบิล ขนาด 7 X 2.5 ต.มม. CONTROL CABLE, SIZE 7 X 2.5 mm^2	20 น. m	20 น. m	02080402
25	สเตรนแคล้มป์สำหรับสายอะลูมิเนียม และอะลูมิเนียมแกนเหล็ก ขนาดตามต้องการ CLAMP, STRAIN, FOR AI AND ACSR SIZE AS REQ'D	6	6	03110000 - 03110101
26	พี จี คอนเนคเตอร์ สำหรับสายอะลูมิเนียม ขนาดตามต้องการ CONNECTOR, PARALLEL GROOVE, FOR AI SIZE AS REQ'D	7	7	02300102 - 02300104
27	ลวดเหล็กตีเกลียว 50/7 ต.มม. มอก. 404 WIRE, STEEL STRANDED 50/7 mm^2 TIS 404	30 น. m	30 น. m	01100004
28	สายอะลูมิเนียมเปลือย 35-185 ต.มม. มอก. 85 CONDUCTOR 35-185 mm^2 TIS 85			02010001 - 02010007
29	ท่อ PVC แข็ง ขนาด Ø 20 X 2,500 - 4,000 มม. พร้อมอุปกรณ์ยึด CONDUIT, PVC RIGID, Ø 20 X 2,500 - 4,000 mm ; COMP. WITH FIXING ACCESS.	2	2	08040002 08040001
30	หลักดิน 60 X 60 X 5 มม. ยาว 2 ม. ROD, GROUND 60 X 60 X 5 mm 2 m LONG	2	2	01220002

หมายเหตุ: 1 การประกอบที่ยึดท่อเอสลอน และสายลงดิน ดูแบบเลขที่ S02-015/19128 และ S02-015/19166

2 ตู้อะลูมิเนียมมิเตอร์ เปลือกพี ที. ซี ที. และสายเป็นกลางของมิเตอร์ ต่อสายดินร่วมกัน

3 การต่อสายคอนโทรลเคเบิล ดูแบบเลขที่ S02-015/18031 (การประกอบเลขที่ 0507)

NOTES 1 S'LON PIPE FITTING AND GROUND LEAD ASSEMBLY SEE DWG. NO. S02-015/19128 AND S02-015/19166.

2 ALUMINIUM METER CASE, P.T. & C.T. CASE AND NEUTRAL SHALL BE GROUND AT ONE POINT.

3 THE CONNECTION DIAGRAM OF CONTROL CABLE, SEE DRAWING NUMBER S02-015/18031 (ASSEMBLY NO. 0507).

สำเนา

กองวิศวกรรม	การไฟฟ้าส่วนภูมิภาค	ใช้แทนแบบ S02-015/16068
ผู้เขียน	ผู้ว่าการ	ถูกแทนโดยแบบ .....
สถาปนิก		เสนอเสร็จวันที่ 27 พ.ย. 18
วิศวกร	การติดตั้งพีทีและซีทีสำหรับมิเตอร์แรงสูง 3 เฟส 4 สาย ระบบ 33 kV ก บัญชีวัสดุ	แก้แบบวันที่ .....
หัวหน้าแผนก		ลิขิตเป็น .....
ผู้อำนวยการกอง		มาตราส่วน .....
รองผู้ว่าการฝ่ายเทคนิค	P.T. & C.T. INSTALLATION FOR 3-PHASE 4-WIRE H.T. METER 33 kV SYSTEM C BILL OF MATERIAL	แบบเลขที่ S02-015/18033
		แผ่นที่ 4 รวมจำนวน 4 แผ่น