

การประกอบเลขที่ ASSEMBLY NO. 0403

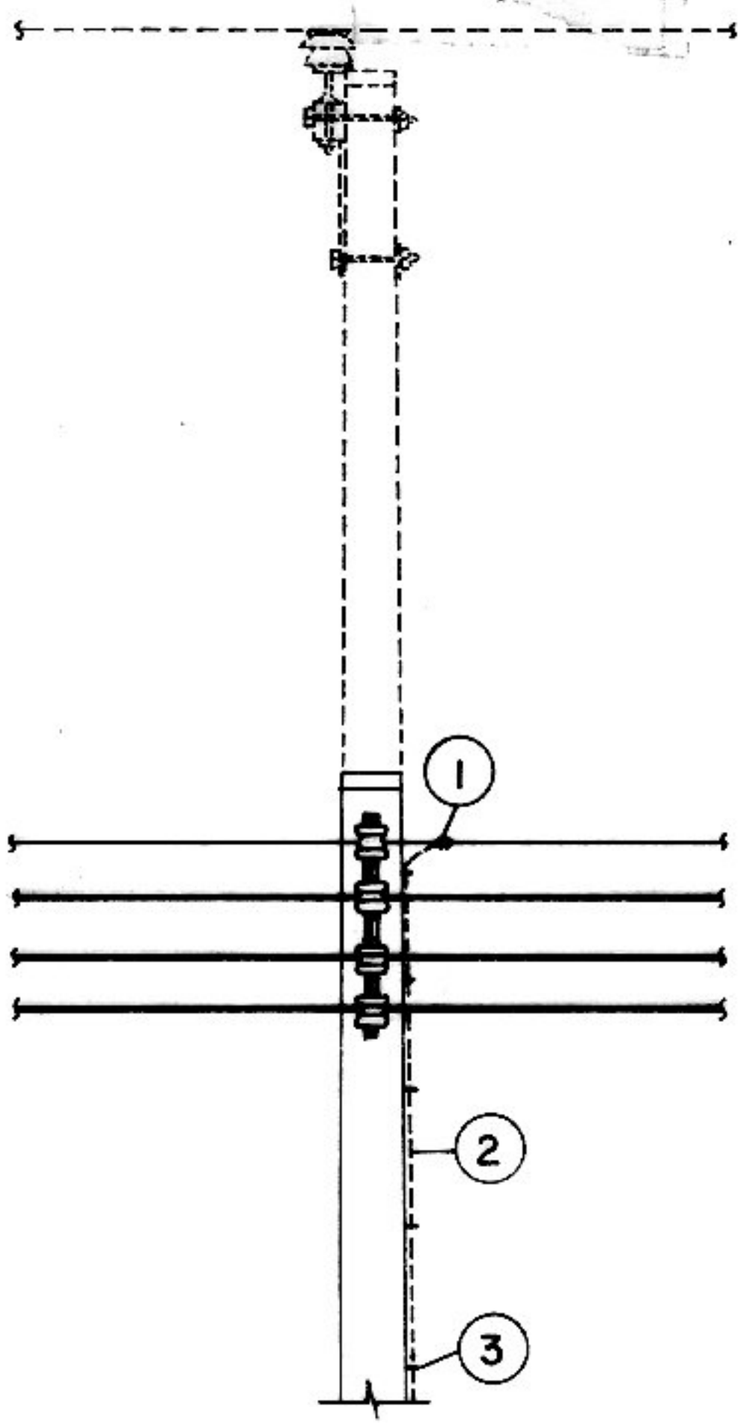

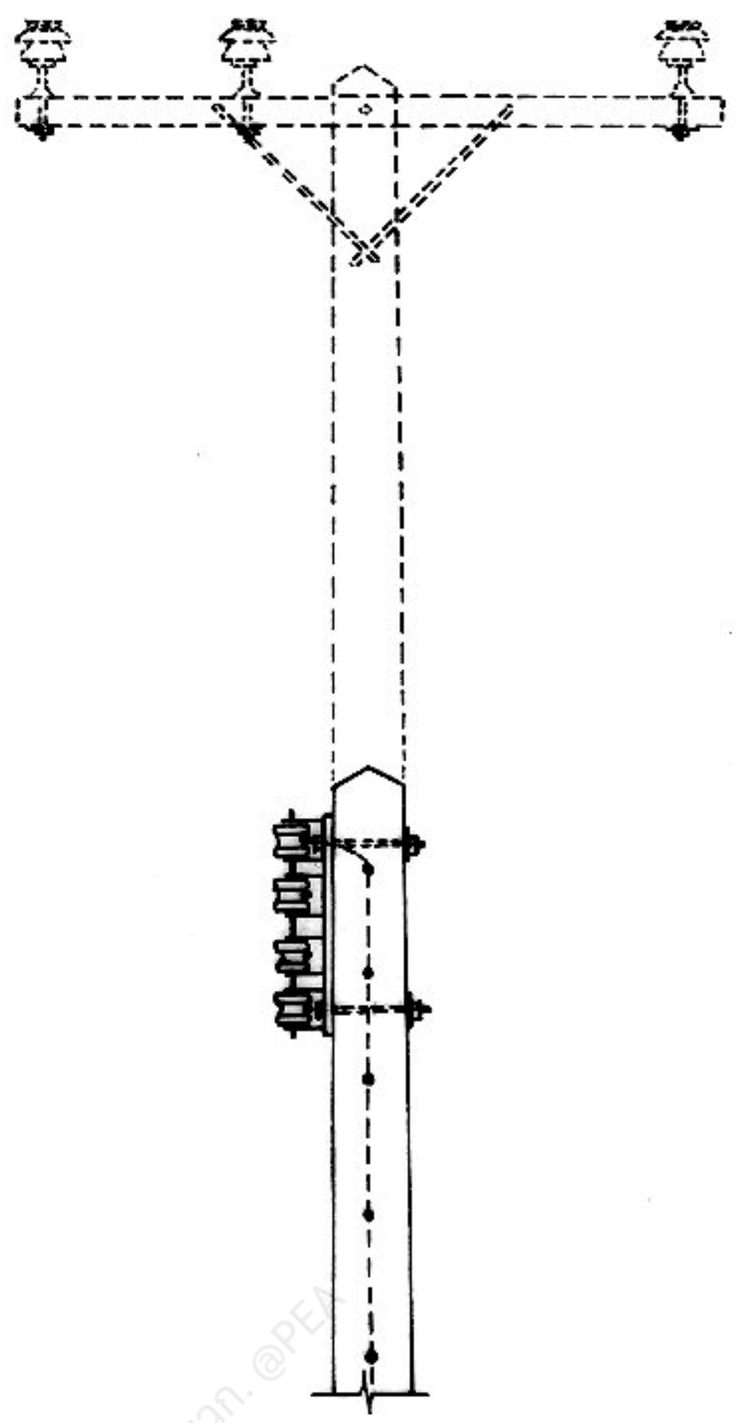

บัญชีวัสดุ
BILL OF MATERIAL

ลำดับที่ ITEM	รายละเอียด DESCRIPTION	จำนวน REQ'D	วัสดุเลขที่ MAT. NO.
1	คีจี. คอนเนคเตอร์ สลักคู่ สำหรับสายอลูมิเนียม 25-95 ต.มม. CONNECTOR, PARALLEL GROOVE, DOUBLE BOLT, AI 25-95 mm^2	1	02300102
2	ลวดเหล็กตีเกลียว 50/7 ต.มม. มอก. 404 WIRE, STEEL STRANDED 50/7 mm^2 TIS 404	20 ม. m	01100004
3	ลวดอะลูมิเนียมกลม และทมุดไม้ แบบเลขที่ S02-015/19166 TIE WIRE, ALUMINIUM AND WOOD PLUG DWG. NO. S02-015/19166	10-12	02200002
4	ท่อ PVC แข็ง ขนาด Ø 20 X 2,500 - 4,000 มม. พร้อมอุปกรณ์ยึด COUNDUIT, PVC RIGID, 20 X 2,500 - 4,000 mm, COMP. WITH FIXING ACCESS.	1	08040002 08040001
5	หลักดิน 60 X 60 X 5 มม. ยาว 2 ม. ROD, GROUND 60 X 60 X 5 mm, 2 m LONG	1	01220002

หมายเหตุ
1. ระยะห่างระหว่างจุดยึดสายลงดิน 500 มม.
2. การต่อลงดินดูแบบเลขที่ S02-015/20039 (การประกอบเลขที่ 8456)

NOTES
1. GROUND LEAD CLAMPS AT 500 mm INTERVALS.
2. EARTHING SEE DRAWING NO. S02-015/20039 (ASSEMBLY NO. 8456).

กองวิศวกรรมไฟฟ้าและเครื่องกล
ฝ่ายวิศวกรรม

ผู้เขียน
ผู้สำรวจ
วิศวกร
หัวหน้าแผนก
หัวหน้ากอง
ผู้อำนวยการฝ่าย

รองผู้ว่าการฝ่ายเทคนิค

การไฟฟ้าส่วนภูมิภาค

ผู้ว่าการ

การต่อสายเป็นกลางแรงต่ำลงดิน
สำหรับหม้อแปลงและสายระบบจำหน่าย

SECONDARY NEUTRAL EARTHING
FOR TRANSFORMER AND DISTRIBUTION LINE

ใช้แทนแบบ
ถูกแทนโดยแบบ
เขียนแล้วเมื่อวันที่ 26 พ.ค. 20
แก้แบบวันที่
มิติเป็น
มาตราส่วน 1 : 50

แบบเลขที่ S02-015/20066
แผ่นที่ 1 ของจำนวน 1 แผ่น