การประกอบเลขที่ ASSEMBLY NO. 5357

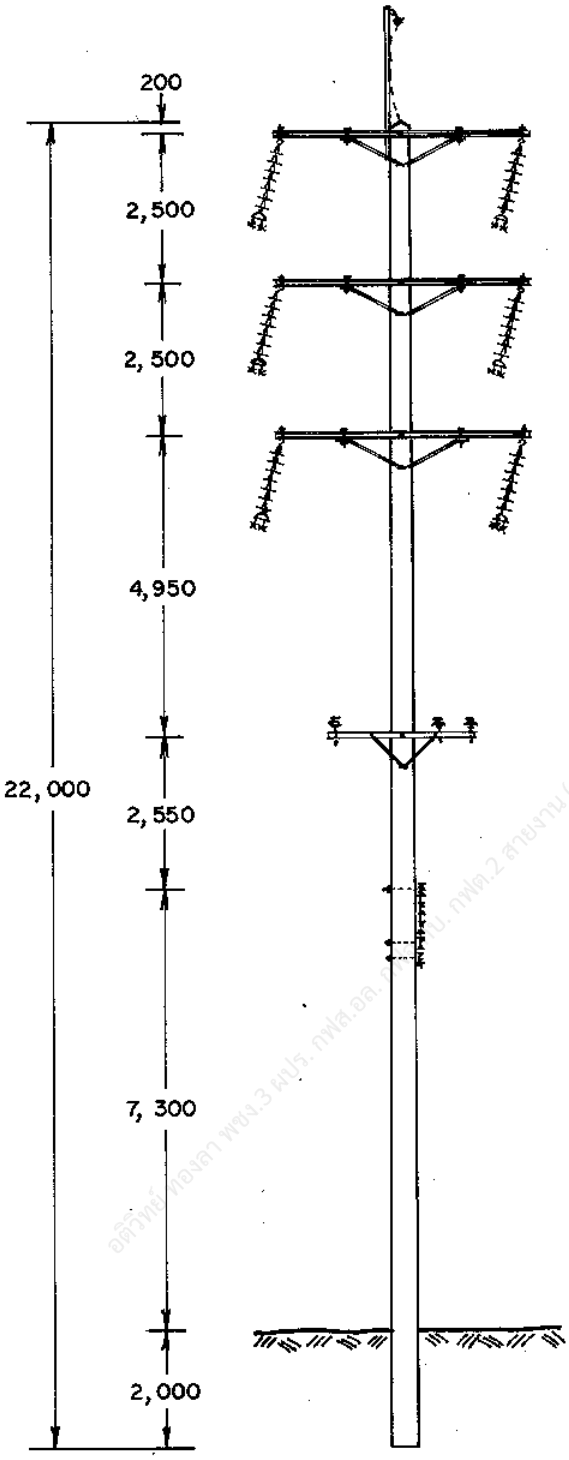

อดิวิทย์ ทองลา พชง.3 ผปร. กฟส.อล. กฟน. กฟต.2 สายงาน (ต) ผวก. @PEA

| | | |
|---|---|---|
| กองวิศวกรรมไฟฟ้าและเครื่องก<br>ฝ่ายวิศวกรรม | การไฟฟ้าส่วนภูมิภาค | ใช้แทนแบบ<br>ถูกแทนโดยแบบ |
| ผู้เขียน<br>ผู้ตรวจ<br>วิศวกร<br>หัวหน้าแผนก<br>ผู้อำนวยการกอง<br>ผู้อำนวยการฝ่าย | ผู้ว่าการ 5 มี.ค. 2531 | เขียนเสร็จวันที่ 15 ธ.ค. 2536<br>แก้แบบวันที่ |
| | 115kV วงจรคู่ สายไฟฟ้าคู่<br>เสาต้นทางตรง ก่อนเสาต้นเข้าปลายสาย<br>แบบ DD-TG-2 | มิติเป็น มิลลิเมตร<br>มาตราส่วน 1 : 125 |
| รองผู้ว่าการฝ่ายเทคนิค | 115kV DOUBLE CIRCUIT DOUBLE CONDUCTOR<br>TANGENT STRUCTURE ADJACENT TO DEADEND POLE<br>TYPE DD-TG-2 | แบบเลขที่ SAI-015/36003<br>แผ่นที่ 1 ของจำนวน 3 แผ่น |

การประกอบเลขที่ 5357
ASSEMBLY NO. 5357

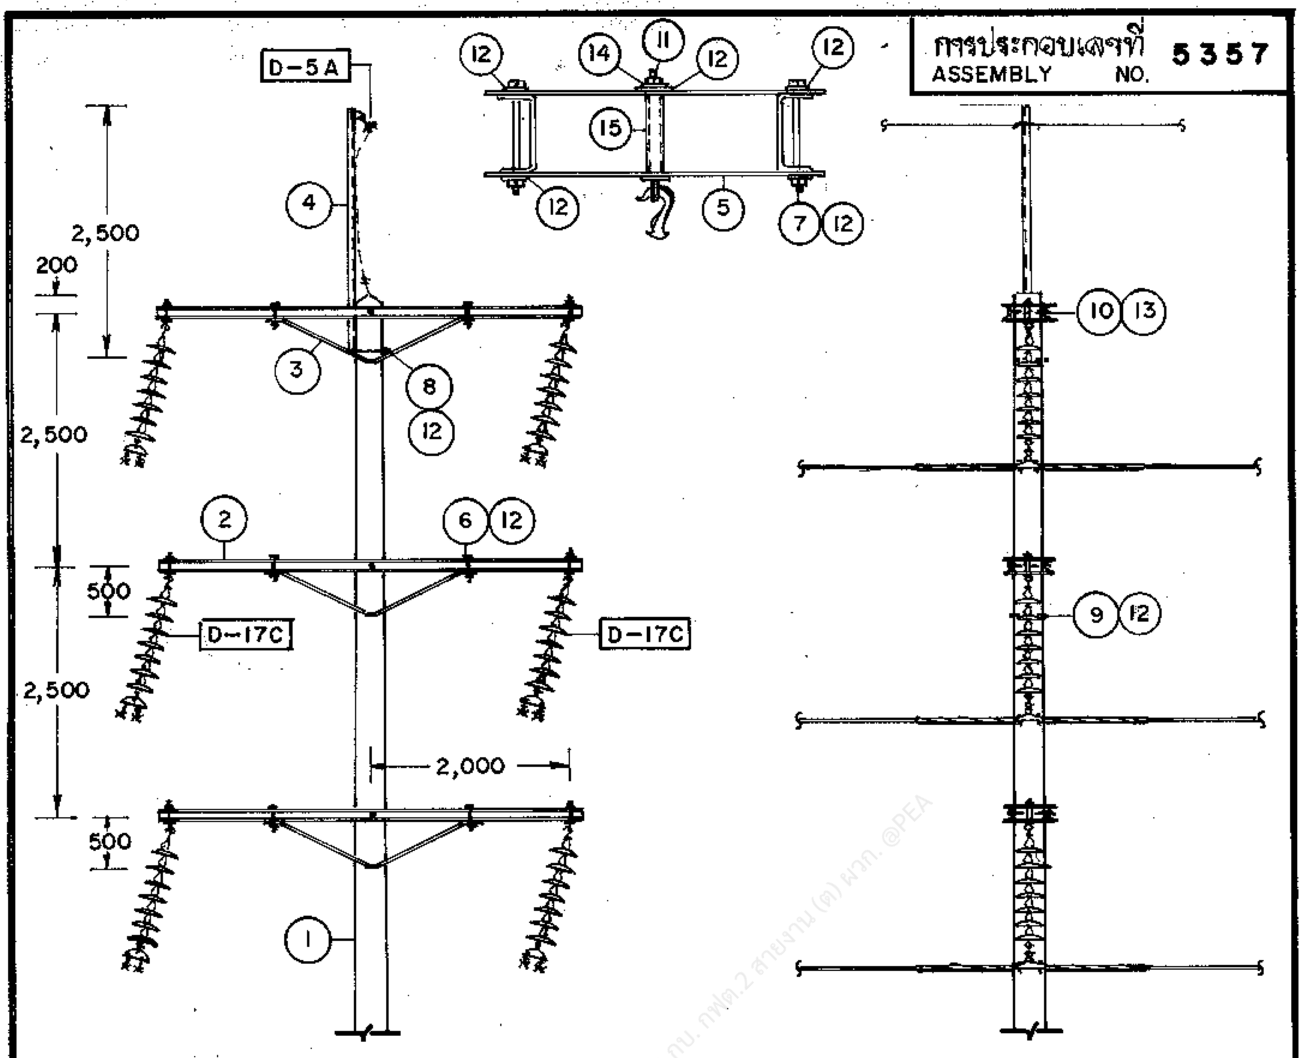

**SD-TG-2**

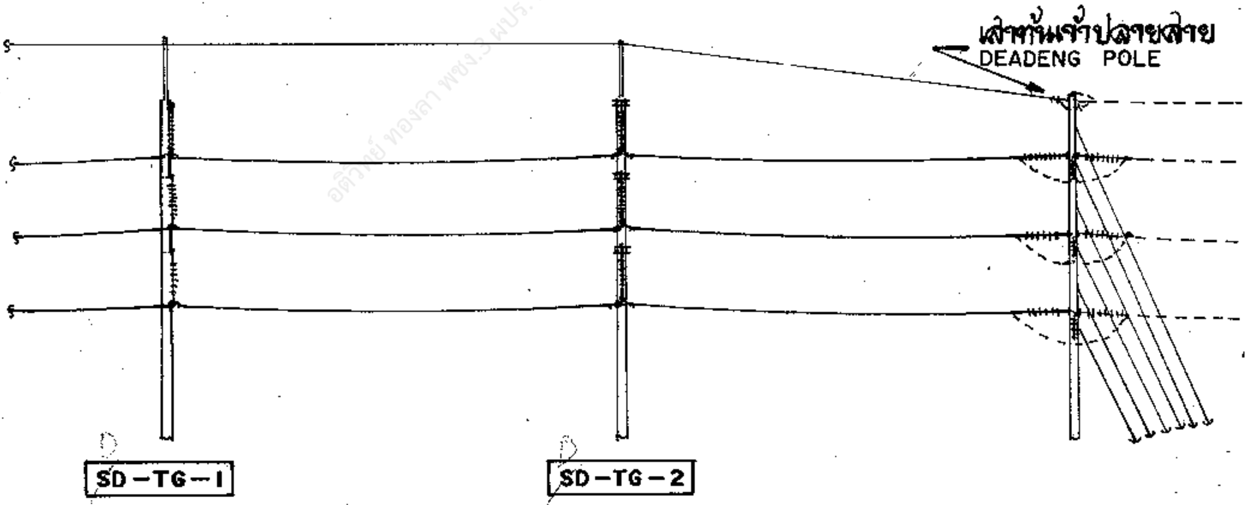

| | | |
|---|---|---|
| กองวิศวกรรมไฟฟ้าและเครื่องกล<br>ฝ่ายวิศวกรรม | การไฟฟ้าส่วนภูมิภาค | ใช้แทนแบบ<br>ถูกแทนโดยแบบ |
| ผู้เขียน<br>ผู้ตรวจ<br>วิศวกร<br>หัวหน้าแผนก<br>ผู้อำนวยการกอง<br>ผู้อำนวยการฝ่าย | ผู้ว่าการ<br>5 ส.ค. 2537 | เขียนเสร็จวันที่ 15 ต.ค. 2536 |
| | 115 kV วงจรคู่ สายไฟฟ้าคู่<br>เสาต้นทางตรง ก่อนเสาต้นเข้าปลายสาย<br>แบบ DD-TG-2 | แก้แบบวันที่<br>มิติเป็น มิลลิเมตร<br>มาตราส่วน 1 : 75 |
| รองผู้ว่าการฝ่ายเทคนิค | 115 kV DOUBLE CIRCUIT DOUBLE CONDUCTOR<br>TANGENT STRUCTURE ADJACENT TO DEADEND POLE<br>TYPE DD-TG-2 | แบบเลขที่ SAI-015/36003<br>แผ่นที่ 2 ของจำนวน 3 แผ่น |

อดิศักดิ์ ทองลา พชง.3 ผปร. กพส. [illegible] กบ. กฟต.2 สายงาน (ต) ผวก. @PEA

การประกอบเลขที่
ASSEMBLY NO. **5357**

## บัญชีวัสดุ
## BILL OF MATERIAL

| ลำดับที่<br>ITEM | รายละเอียด<br>DESCRIPTION | จำนวน<br>REQ'D | รหัสวัสดุเลขที่<br>MAT. NO. |
|---|---|---|---|
| 1 | เสาคอนกรีต 22 ม.<br>POLE, CONCRETE 22 m LONG | 1 | 00010011<br>(0041) |
| 2 | คอนสายแบบเหล็กรูปรางน้ำ ขนาด 100X50X5 มม. ยาว 4.20 ม. มอก. 116<br>CROSSARM, STEEL, CHANNEL 100X50X5 mm 4.20 m LONG TIS 116 | 6 | |
| 3 | เหล็กฉากรับคอนสาย ขนาด 50X50X6 มม. ช่วงกว้าง 1,800 มม. ดรอพ 450 มม.<br>BRACE, ANGLE STEEL, 50X50X6 mm, 1,800 mm WIDE, 450 mm DROP | 6 | 01200007<br>(0119) |
| 4 | เหล็กฉากรับสายล่อฟ้าทางตรง ยาว 2.50 ม.<br>OVERHEAD GROUND WIRE BAYONET, 2.50 m LONG | 1 | 01010004<br>(0135) |
| 5 | เหล็กแผ่น ขนาด 6X100X450 มม.<br>PLATE, STEEL, 6X100X450 mm | 12 | 01030002<br>(0143) |
| 6 | สลักเกลียว M 16X130 มม.<br>BOLT, MACHINE, M 16X130 mm | 12 | 01110200<br>(0220) |
| 7 | สลักเกลียว M 16X170 มม.<br>BOLT, MACHINE, M 16X170 mm | 12 | 01110201<br>(0221) |
| 8 | สลักเกลียว M 16X300 มม.<br>BOLT, MACHINE, M 16X300 mm | 2 | 01110204<br>(0224) |
| 9 | สลักเกลียว M 16X350 มม.<br>BOLT, MACHINE, M 16X350 mm | 3 | 01110205<br>(0225) |
| 10 | สลักเกลียว M 20X350 มม.<br>BOLT, MACHINE, M 20X350 mm | 3 | 01110300 |
| 11 | สลักห่วงโอแวล M 16X150 มม.<br>BOLT, OVAL EYE, M 16X150 mm | 6 | 01150000<br>(0257) |
| 12 | แหวนสี่เหลี่ยมแบน 52X52X4.5 มม. รู ø 18 มม. มอก. 258<br>WASHER, SQUARE, FLAT 52X52X4.5 mm, HOLE ø 18 mm, TIS 258 | 53 | 01180100<br>(0355) |
| 13 | แหวนสี่เหลี่ยมแบน 62X62X6 มม. รู ø 22 มม. มอก. 258<br>WASHER, SQUARE, FLAT 62X62X6 mm, HOLE ø 22 mm, TIS 258 | 6 | 01180101<br>(0356) |
| 14 | แหวนสปริง M 16 มอก. 259<br>WASHER, LOCK, M 16, TIS 259 | 6 | 01180301<br>(0365) |
| 15 | ท่อเหล็ก ชื่อขนาด 20 มม. หนา 2.65 มม. ยาว 100 มม. มอก. 277 ประเภท 2<br>PIPE, IRON, DIA. 20 mm I.D., 2.65 mm THICKNESS, 100 mm LONG, TIS 277, TYPE 2 | 6 | 01050000<br>(0905) |
| | | | |

| | | | |
|---|---|---|---|
| D-17C | การประกอบลูกถ้วยแขวน<br>SUSPENSION INSULATOR ASSEMBLY | 6 | |
| D-5A | การต่อสายล่อฟ้า<br>OVERHEAD GROUND WIRE CONNECTION | 1 | |
| D-10A | ฐานรากเสา<br>POLE FOUNDATION | 1 | |

กองวิศวกรรมไฟฟ้าและเครื่องกล
ฝ่ายวิศวกรรม

ผู้เขียน
ผู้สำรวจ
วิศวกร
หัวหน้าแผนก
ผู้อำนวยการกอง
ผู้อำนวยการฝ่าย

รองผู้ว่าการฝ่ายเทคนิค

**การไฟฟ้าส่วนภูมิภาค**

5 มี.ค. 2537

ผู้ว่าการ

115 kV วงจรคู่ สายไฟฟ้าคู่
เสาต้นทางตรง ก่อนเสาต้นเข้าปลายสาย
แบบ DD-TG-2

115 kV DOUBLE CIRCUIT DOUBLE CONDUCTOR
TANGENT STRUCTURE ADJACENT TO DEADEND POLE
TYPE DD-TG-2

ใช้แทนแบบ
ถูกแทนโดยแบบ
เขียนเสร็จวันที่ 15 ธค. 2536
แก้แบบวันที่
ผิดเป็น
มาตราส่วน

แบบเลขที่ SAI-015/36003
แผ่นที่ 3 ของจำนวน 3 แผ่น