
การประกอบเลขที่ 0543
ASSEMBLY NO.

กิโลวัตต์-ชั่วโมงมิเตอร์
kWh-METER

มิเตอร์ T.O.U.
T.O.U. METER

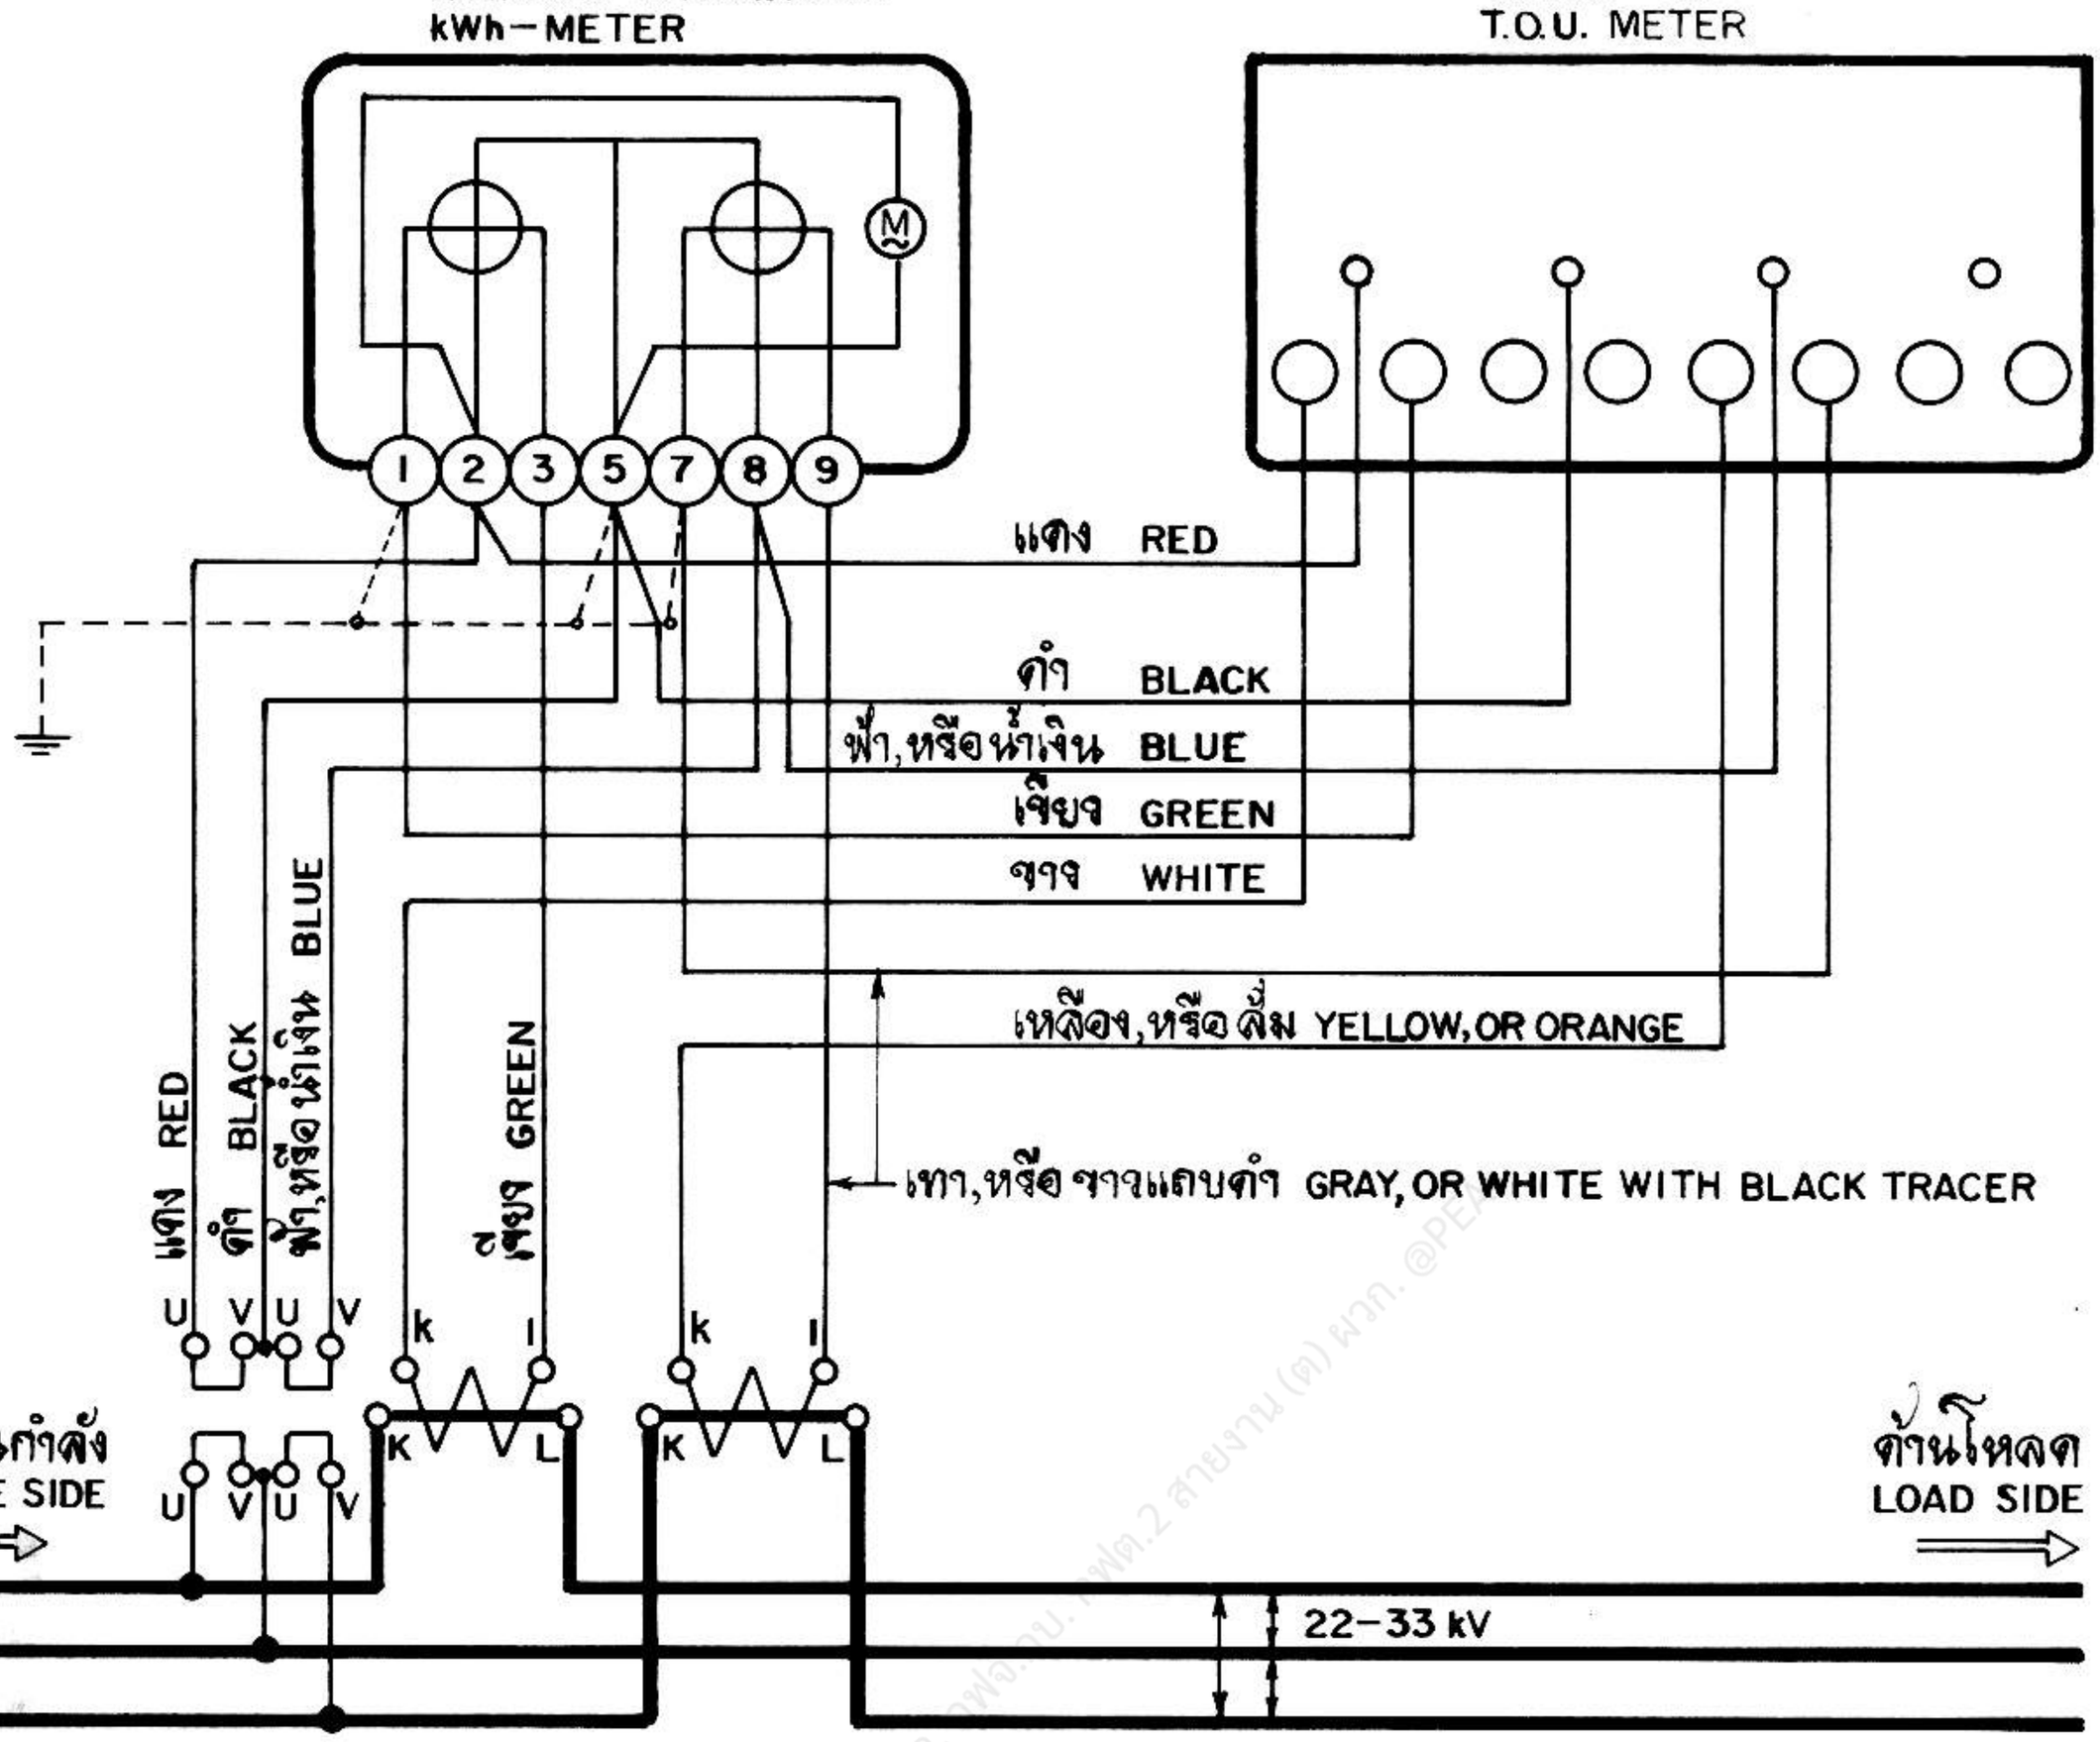

หมายเหตุ

1. การต่อสายตามแผนผังนี้ ใช้ในกรณีที่ต่อร่วมกับมิเตอร์ T.O.U.(ผลิตภัณฑ์ของ โพลีมิเตอร์)
2. ใช้สายคอนโทรลเคเบิล ขนาด 7X2.5 ต.มม.
3. การติดตั้ง ให้ดำเนินตามรายละเอียดเช่นเดียวกับแบบเลขที่ SAI-015/28020 และเลขที่ SAI-015/28021 (การประกอบเลขที่ 2506 และเลขที่ 3505) โดยติดตั้งมิเตอร์ T.O.U. แทนการติดตั้ง กิโลวาร์-ชั่วโมงมิเตอร์
4. รายละเอียดตู้มิเตอร์ T.O.U. ตู้แบบเลขที่ SAI-015/32045 (การประกอบเลขที่ 0544)

NOTES

1. THIS CONNECTION DIAGRAM IS ONLY FOR COMBINATION WITH **T.O.U.** METER (BY POLY METERS).
2. USE CONTROL CABLE SIZE **7X2.5** mm^2.
3. **T.O.U.** METER INSTALLATION, INSTEAD OF kVarh METER, SEE DETAIL AS DWGS. NO. SAI-015/28020 AND NO. SAI-015/28021 (ASSEMBLY NO. **2506** AND NO. **3505**).
4. DETAIL OF **T.O.U.** METER CABINET, SEE DWG. NO. SAI-015/32045 (ASSEMBLY NO. **0544**).

กองวิศวกรรมไฟฟ้าและเครื่องกล ฝ่ายวิศวกรรม	การไฟฟ้าส่วนภูมิภาค	ใช้แทนแบบ ---------- ถูกแทนโดยแบบ ---------- เขียนเสร็จวันที่ 14 ธ.ค. 32 แก้แบบวันที่ 5 ก.ย. 34 มิติเป็น — มาตราส่วน —
ผู้เขียน ผมกอ. ผู้สำรวจ วิศวกร หัวหน้าแผนก ผู้อำนวยการกอง ผู้อำนวยการฝ่าย	ผู้จ่าการ 27 ธ.ค. 32	
รองผู้จ่าการฝ่ายเทคนิค	แผนผัง การต่อมิเตอร์แรงสูง 3 เฟส 3 สาย กรณีติดตั้งกิโลวัตต์ ชั่วโมงมิเตอร์ ร่วมกับมิเตอร์ T.O.U. ระบบ 22-33 kV INSTALLATION OF 3-Ø, 3-W, METER WITH P.T. AND C.T. kWh AND **T.O.U.** METERS COMBINATION 22-33 kV SYSTEM	แบบเลขที่ SAI-015/32044 แผ่นที่ 1 ของสำนวน 1 แผ่น