การประกอบเลขที่
ASSEMBLY NO. **5429**

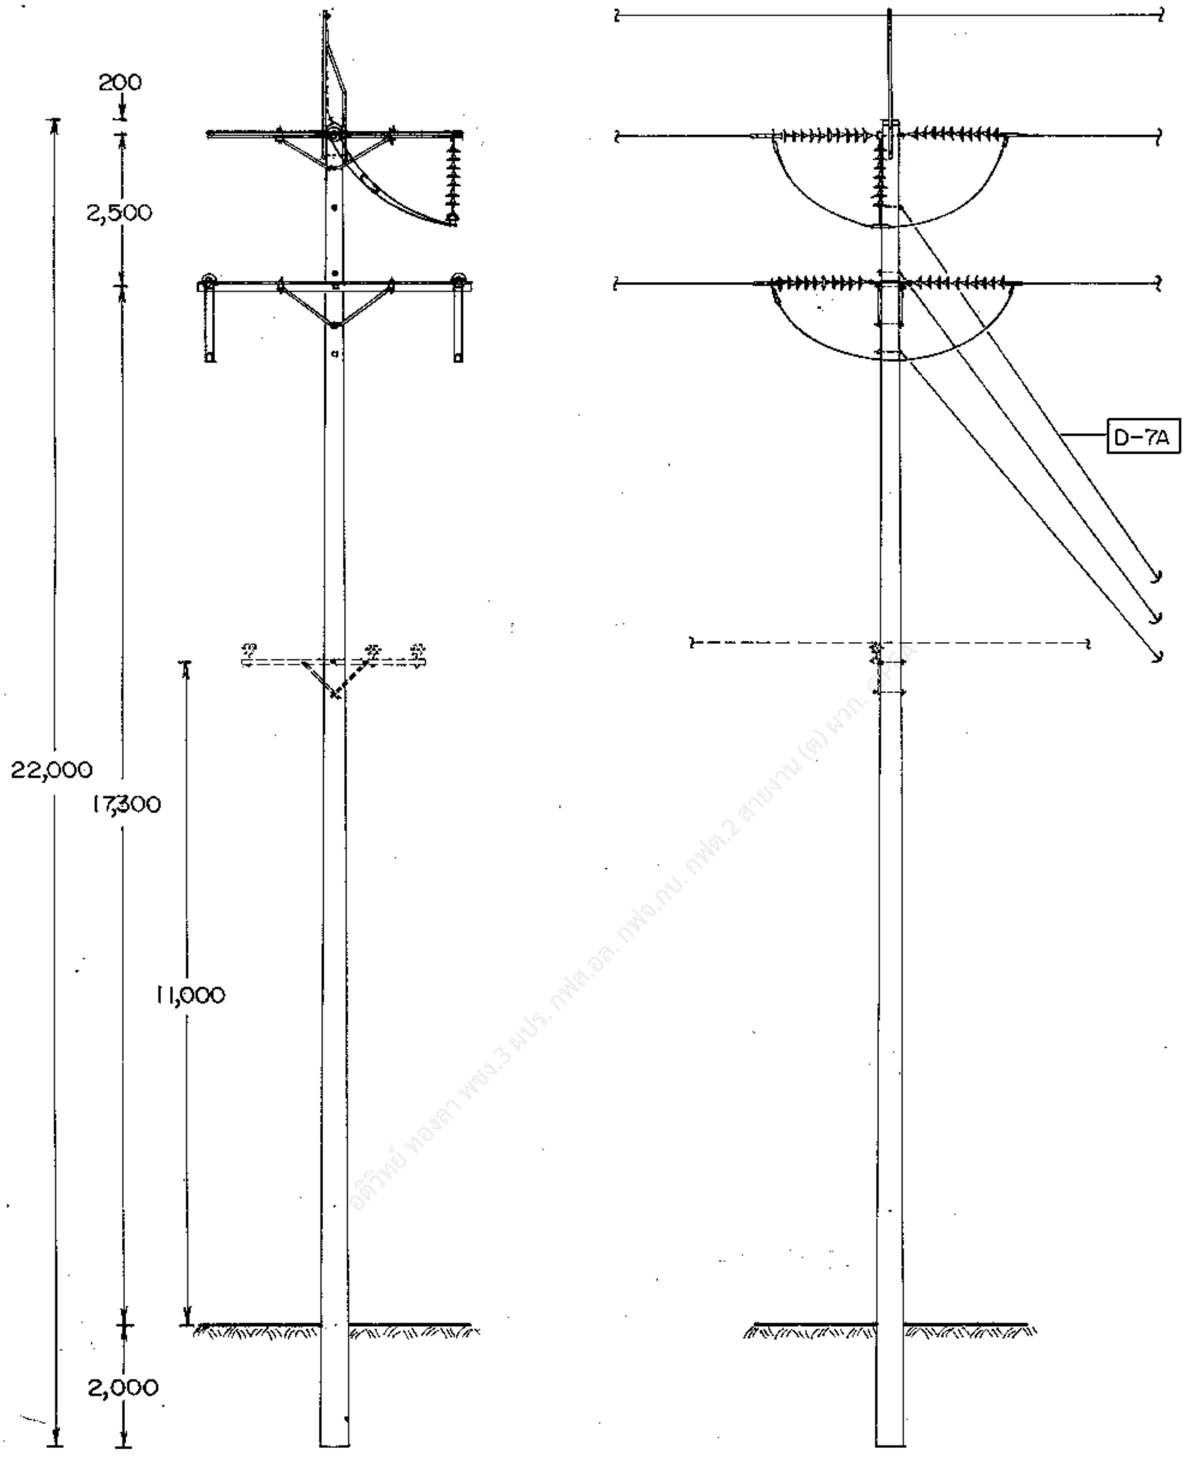

อดิวิทย์ ทองลา พชง.3 ผปร. กฟส.อล. กฟจ.กบ. กฟต.2 สายงาน (ต) ผวก. @PEA

กองวิศวกรรมไฟฟ้าและเครื่องกล
ฝ่ายวิศวกรรม

ผู้เขียน
ผู้ตรวจ
วิศวกร
หัวหน้าแผนก
ผู้อำนวยการกอง
ผู้อำนวยการฝ่าย

รองผู้ว่าการฝ่ายเทคนิค

การไฟฟ้าส่วนภูมิภาค

ผู้ว่าการ

115 kV วงจรเดี่ยว สายไฟฟ้าคู่
เสาสำหรับยกระดับความสูงการพาดสาย
แบบ SD-IH-1

115 kV SINGLE CIRCUIT DOUBLE CONDUCTOR
INCREASING HEIGHT OF CONDUCTOR STRINGING STRUCTURE
TYPE SD-IH-1

ใช้แทนแบบ
ถูกแทนโดยแบบ
เขียนเสร็จวันที่ 14 ก.พ. 31
แก้แบบวันที่
มิติเป็น มิลลิเมตร
มาตราส่วน 1:125

แบบเลขที่ SAI-015/31069
แผ่นที่ 1 ของจำนวน 4 แผ่น

การประกอบเลขที่ ASSEMBLY NO.	5429

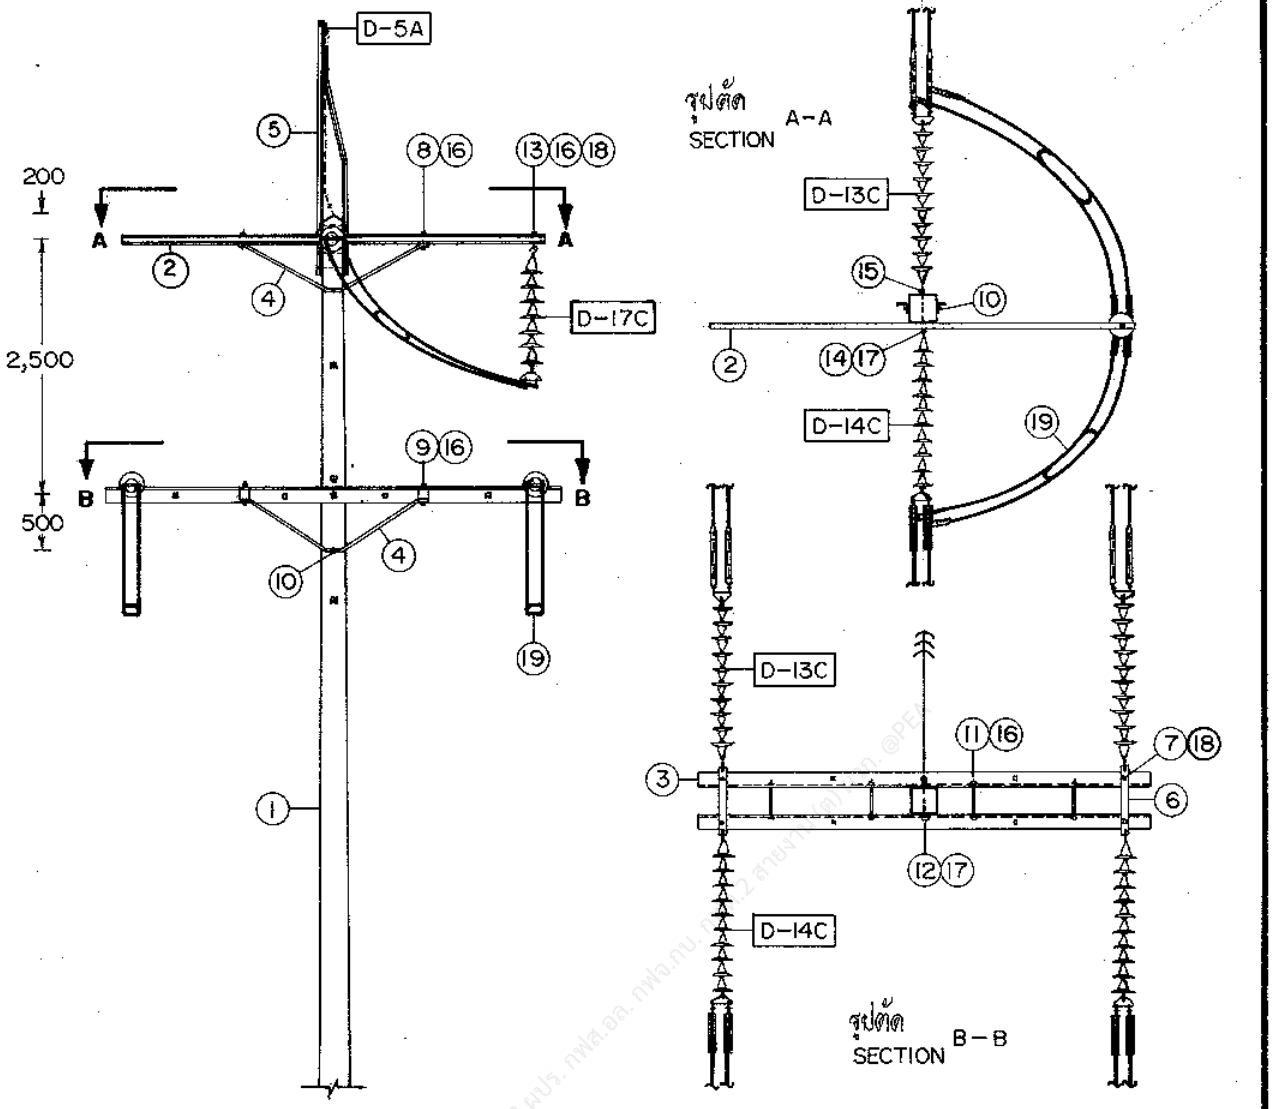

D-5A
5
8 16
13 16 18
200
A
A
2
4
D-17C
2,500
9 16
B
B
500
10
4
19
1
รูปตัด SECTION A-A
D-13C
15
10
2
14 17
D-14C
19
D-13C
11 16
7 18
3
6
12 17
D-14C
รูปตัด SECTION B-B

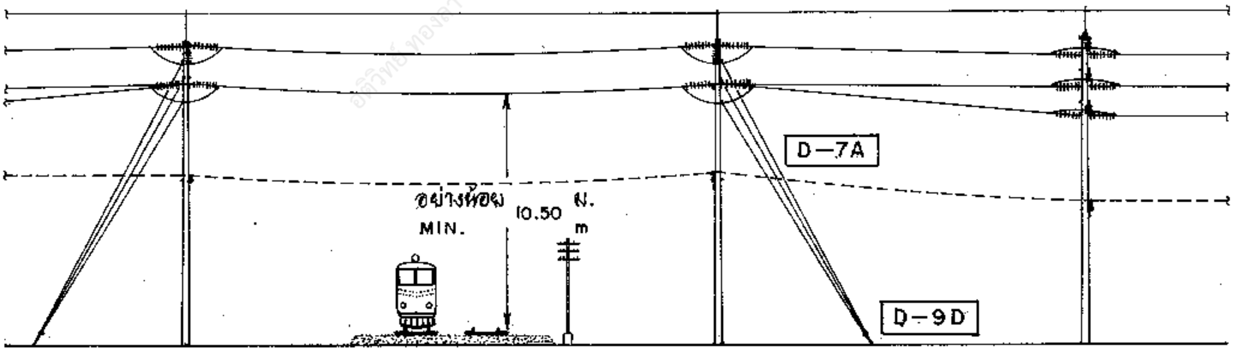

D-7A
อย่างน้อย MIN. 10.50 ม. m
D-9D
SD-IH-I
SD-IH-I
SD-DD-I

ลักษณะการใช้งาน
(APPLICATION)

กองวิศวกรรมไฟฟ้าและเครื่องกล ฝ่ายวิศวกรรม	การไฟฟ้าส่วนภูมิภาค	ใช้แทนแบบ ถูกแทนโดยแบบ
ผู้เขียน ผู้ตรวจ วิศวกร หัวหน้าแผนก ผู้อำนวยการกอง ผู้อำนวยการฝ่าย	ผู้ว่าการ	เขียนเสร็จวันที่ 14 กย. 31 แก้แบบ วันที่
	115 kV วงจรเดี่ยว สายไฟฟ้าคู่ เสาสำหรับยกระดับความสูงการพาดสาย แบบ SD-IH-I	มิติเป็น มิลลิเมตร มาตราส่วน 1:75
รองผู้ว่าการฝ่ายเทคนิค	115 kV SINGLE CIRCUIT DOUBLE CONDUCTOR INCREASING HEIGHT OF CONDUCTOR STRINGING STRUCTURE TYPE SD-IH-I	แบบเลขที่ SAI-015/31069 แผ่นที่ 2 ของจำนวน 4 แผ่น

การประกอบเลขที่ ASSEMBLY NO.	5429

บัญชีวัสดุ
BILL OF MATERIAL

ลำดับที่ ITEM	รายละเอียด DESCRIPTION	จำนวน REQ' D	วัสดุเลขที่ MAT. NO.
1	เสาคอนกรีต 22 ม. POLE, CONCRETE 22 m LONG	1	00010011 (0041)
2	คอนสายแบบเหล็กรูปรางน้ำ ขนาด 100X50X5 มม. ยาว 4.20 ม. มอก. 116 CROSSARM, STEEL, CHANNEL 100X50X5 mm 4.20 m LONG TIS 116	1	
3	คอนสายแบบเหล็กฉาก ขนาด 150X100X12 มม. ยาว 4.50 ม. CROSSARM, STEEL ANGLE, 150X100X12 mm, 4.50 m LONG	2	00120002 (6001)
4	เหล็กฉากรับคอนสาย 50X50X6 มม. ช่วงกว้าง 1,800 มม. ดรอพ 450 มม. BRACE, ANGLE STEEL 50X50X6 mm, 1,800 mm WIDE, 450 mm DROP	3	01200007 (0119)
5	**เหล็กฉากรับสายล่อฟ้า ทางโค้ง** OVERHEAD GROUND WIRE CORNER BAYONET	1	01010005 (0136)
6	แผ่นเหล็กยึดสองปลาย ขนาด 12X100X760 มม. PLATE, STEEL, DOUBLE ARMING, 12X100X760 mm	2	01030102 (6006)
7	สลักเกลียว M 16X75 มม. พร้อมแหวนกลม 2 อัน BOLT, MACHINE, M 16X75 mm, COMPLETE WITH 2 ROUND WASHERS	4	01110400 (0236)
8	สลักเกลียว M 16X130 มม. BOLT, MACHINE, M 16X130 mm	2	01110200 (0220)
9	สลักเกลียว M 16X170 มม. BOLT, MACHINE, M 16X170 mm	4	01110201 (0221)
10	สลักเกลียว M 16X350 มม. BOLT, MACHINE, M 16X350 mm	5	01110205 (0225)
11	สลักเกลียวตลอด M 16X400 มม. BOLT, DOUBLE ARMING, M 16X400 mm	4	01120000 (0243)
12	สลักเกลียว M 20X400 มม. BOLT, MACHINE, M 20X400 mm	1	01110301 (0233)
13	สลักห่วงโอแวล M 16X150 มม. BOLT, OVAL EYE, M 16X150 mm	1	01150000 (0257)
14	สลักห่วงโอแวล M 20X350 มม. BOLT, OVAL EYE, M 20X350 mm	1	01150100 (0260)
15	อายเล็ท สำหรับสลักเกลียว M 20 EYELET FOR BOLT, M 20	1	01180002 (0346)
16	แหวนสี่เหลี่ยมแบน 52X52X4.5 มม. รู Ø 18 มม. มอก. 258 WASHER, SQUARE, FLAT 52X52X4.5 mm, HOLE Ø 18 mm, TIS 258	25	01180100 (0355)
17	แหวนสี่เหลี่ยมแบน 62X62X6 มม. รู Ø 22 มม. มอก. 258 WASHER, SQUARE, FLAT 62X62X6 mm, HOLE Ø 22 mm, TIS 258	4	01180101 (0356)
18	แหวนสปริง M 16 มอก. 259 WASHER, LOCK, M 16, TIS 259	5	01180301 (0365)
19	ปรีฟอร์มแยกสาย SPACER, HELICAL ROD, PREFORMED	4	02240000 (0918)

กองวิศวกรรมไฟฟ้าและเครื่องกล ฝ่ายวิศวกรรม	**การไฟฟ้าส่วนภูมิภาค**	ใช้แทนแบบ ถูกแทนโดยแบบ เขียนแล้วเสร็จวันที่ 14 ก.พ. 31
ผู้เขียน ผู้สำรวจ วิศวกร หัวหน้าแผนก ผู้อำนวยการกอง ผู้อำนวยการฝ่าย	ผู้ว่าการ 115 kV วงจรเดี่ยว สายไฟฟ้าคู่ เสาสำหรับยกระดับความสูงการพาดสาย แบบ SD-IH-1	แก้แบบวันที่ มิติเป็น —— มาตราส่วน ——
รองผู้ว่าการฝ่ายเทคนิค	115 kV SINGLE CIRCUIT DOUBLE CONDUCTOR INCREASING HEIGHT OF CONDUCTOR STRINGING STRUCTURE TYPE SD-IH-1	แบบเลขที่ SAI-015/31069 แผ่นที่ 3 ของจำนวน 4 แผ่น

การประกอบเลขที่
ASSEMBLY NO. **5429**

	รายละเอียด DETAIL		
D-13C	การประกอบลูกถ้วยแขวน SUSPENSION INSULATOR ASSEMBLY	3	
D-14C	การประกอบลูกถ้วยแขวน SUSPENSION INSULATOR ASSEMBLY	3	
D-17C	การประกอบลูกถ้วยแขวน SUSPENSION INSULATOR ASSEMBLY	1	
D-5A	การต่อสายล่อฟ้า OVERHEAD GROUND WIRE CONNECTION	1	
D-7A	การประกอบสายยึดโยงลวดเหล็กตีเกลียว 95 ต.มม. STEEL STRANDED WIRE 95 mm^2 GUY ASSEMBLY	3	
D-9D	สมอบกคอนกรีต CONCRETE ANCHOR	1	
D-10A	ฐานรากเสา POLE FOUNDATION	1	

อดิวิทย์ ทองลา พชง.3 ผปร. กฟส.อล. กฟจ.กบ. กฟต.2 สายงาน (ต) ผวก. @PEA

กองวิศวกรรมไฟฟ้าและเครื่องกล
ฝ่ายวิศวกรรม

ผู้เขียน
ผู้สำรวจ
วิศวกร
หัวหน้าแผนก
ผู้อำนวยการกอง
ผู้อำนวยการฝ่าย
รองผู้ว่าการฝ่ายเทคนิค

การไฟฟ้าส่วนภูมิภาค

ผู้ว่าการ

115 kV วงจรเดี่ยว สายไฟฟ้าคู่
เสาสำหรับยกระดับความสูงการพาดสาย
แบบ SD-IH-1

115 kV SINGLE CIRCUIT DOUBLE CONDUCTOR
INCREASING HEIGHT OF CONDUCTOR STRINGING STRUCTURE
TYPE SD-IH-1

ใช้แทนแบบ
ถูกแทนที่โดยแบบ
เขียนเสร็จวันที่ 14 กย. 31
แก้แบบวันที่
มิติเป็น —
มาตราส่วน —
แบบเลขที่ SAI-015/31069
แผ่นที่ 4 ของจำนวน 4 แผ่น