การประกอบเลขที่
ASSEMBLY NO. **3804**

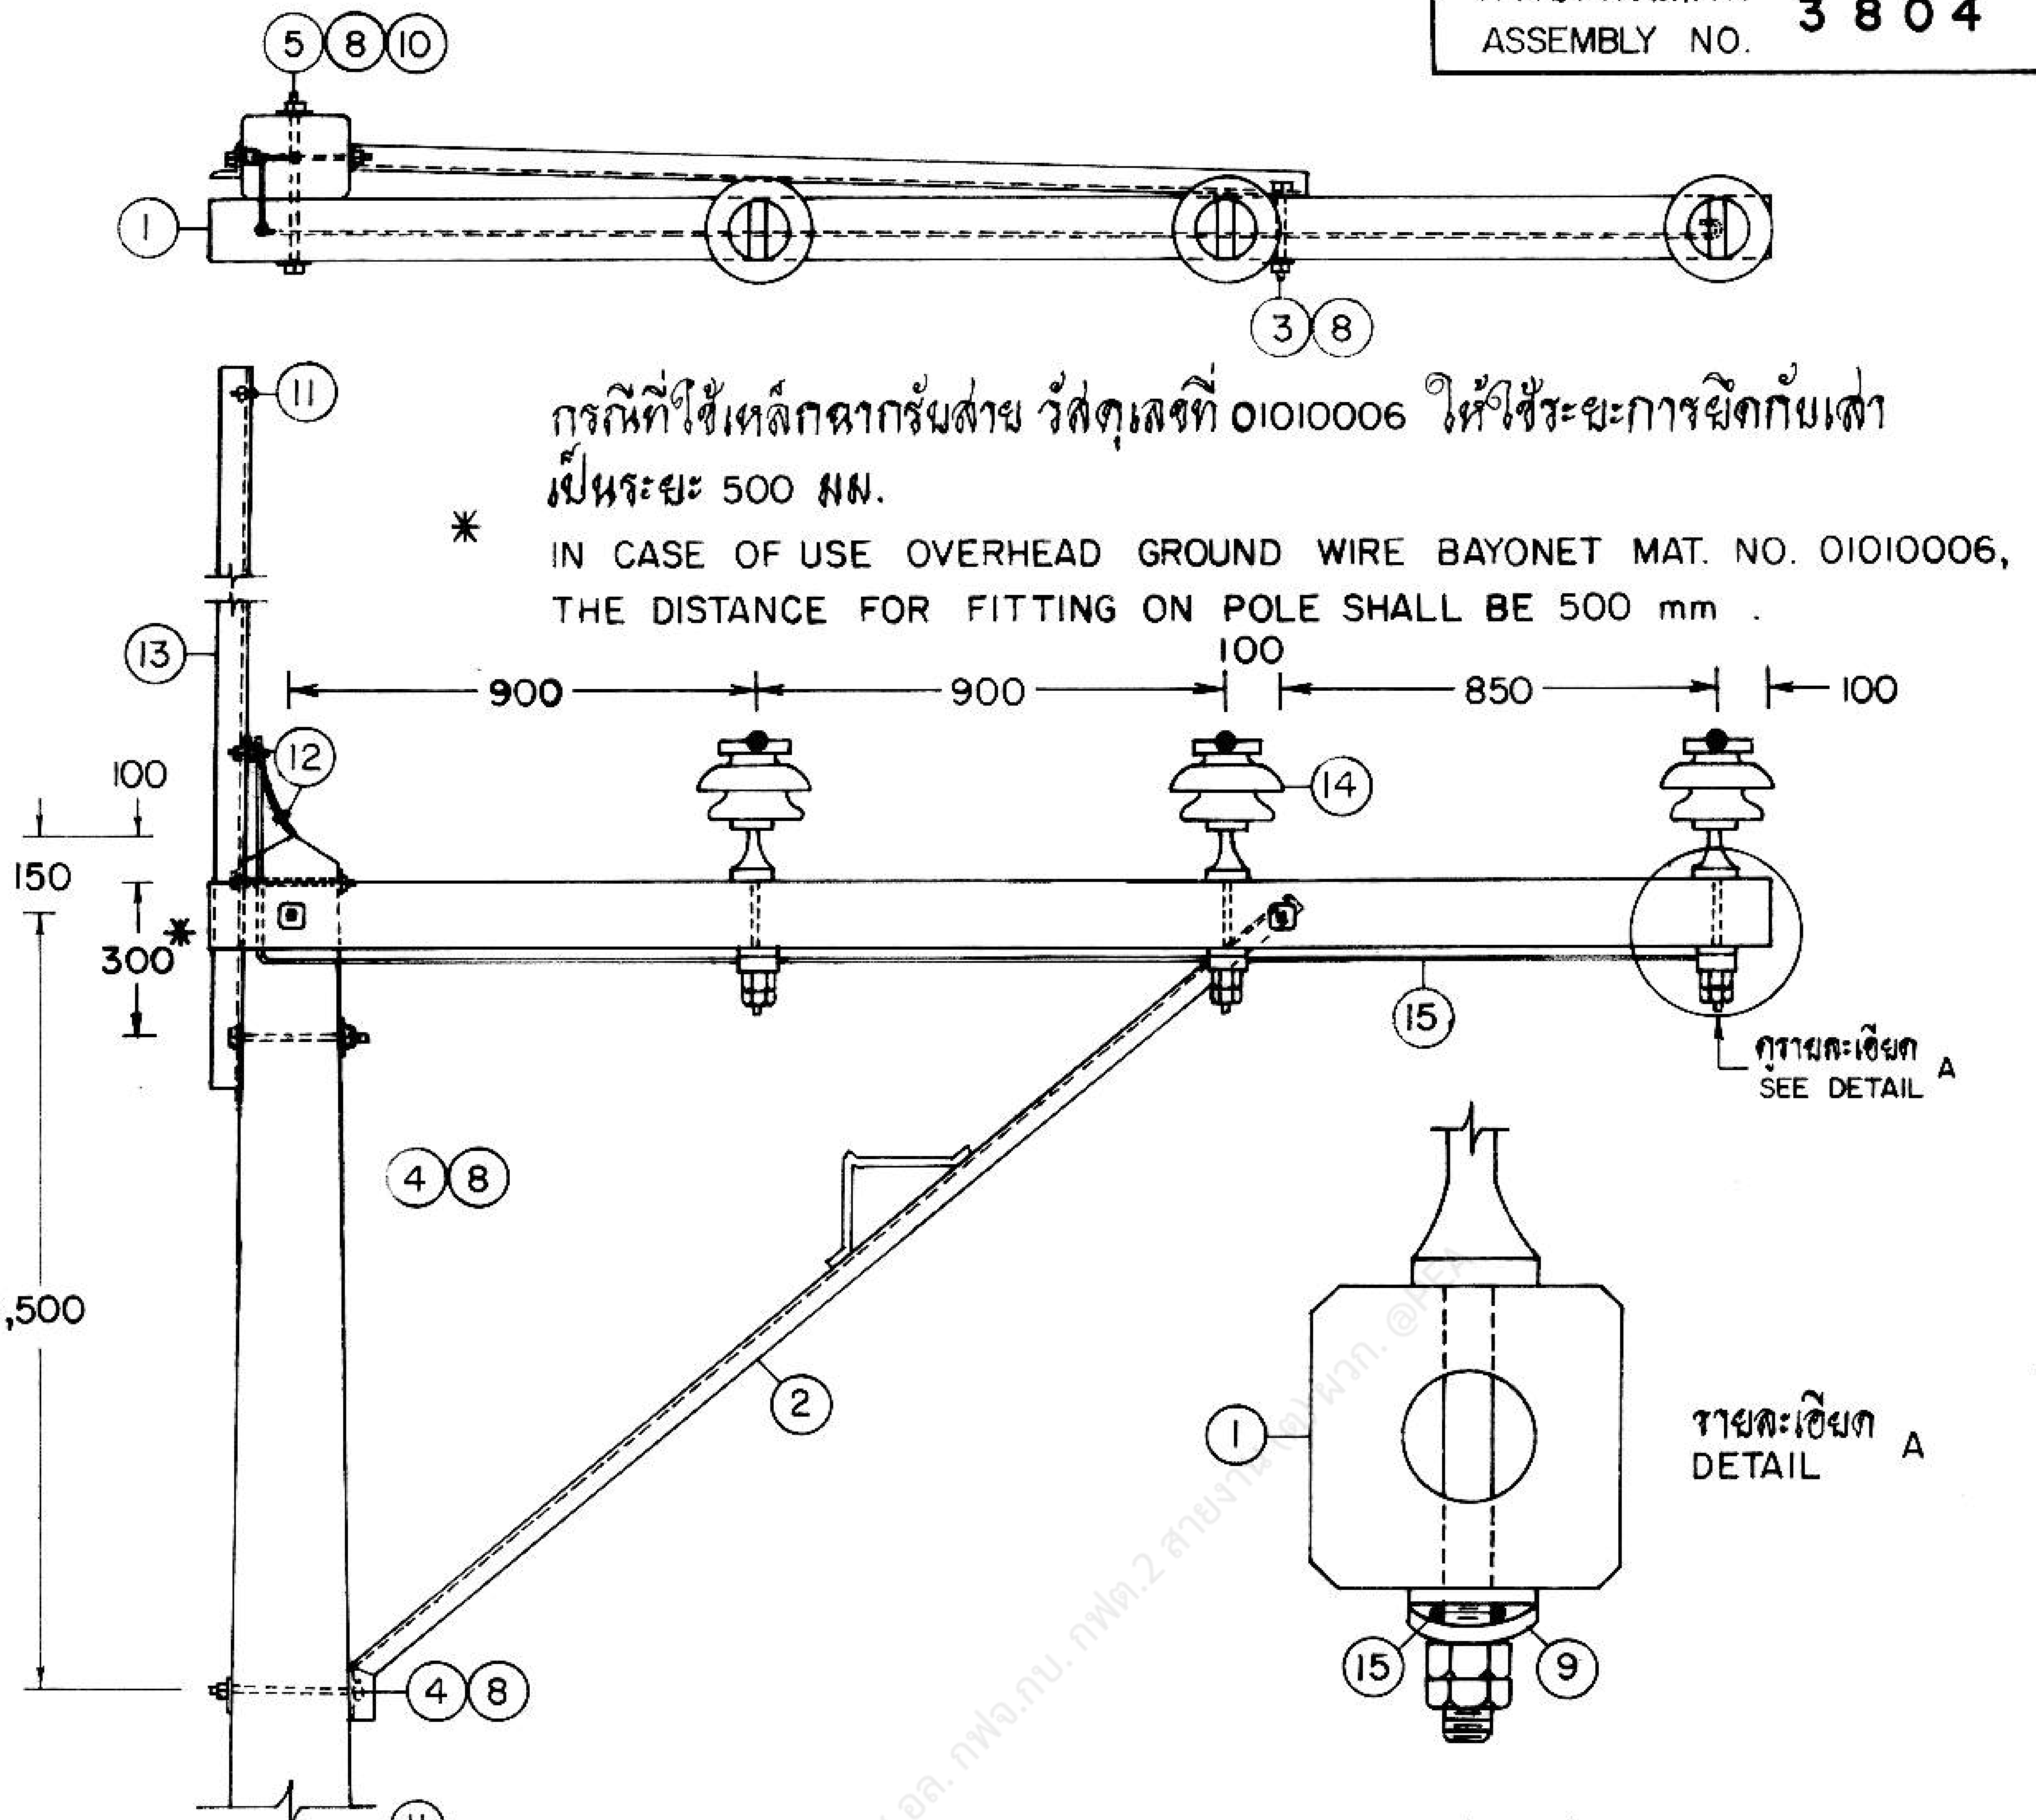
5
8
10
1
3
8
11
13
12
100
150
300*
1,500
900
900
100
850
100
14
15
4
8
2
4
8
ดูรายละเอียด A
SEE DETAIL A
1
15
9
รายละเอียด A
DETAIL A

* กรณีที่ใช้เหล็กฉากรับสาย วัสดุเลขที่ 01010006 ให้ใช้ระยะการยึดกับเสา เป็นระยะ 500 มม.
IN CASE OF USE OVERHEAD GROUND WIRE BAYONET MAT. NO. 01010006, THE DISTANCE FOR FITTING ON POLE SHALL BE 500 mm .

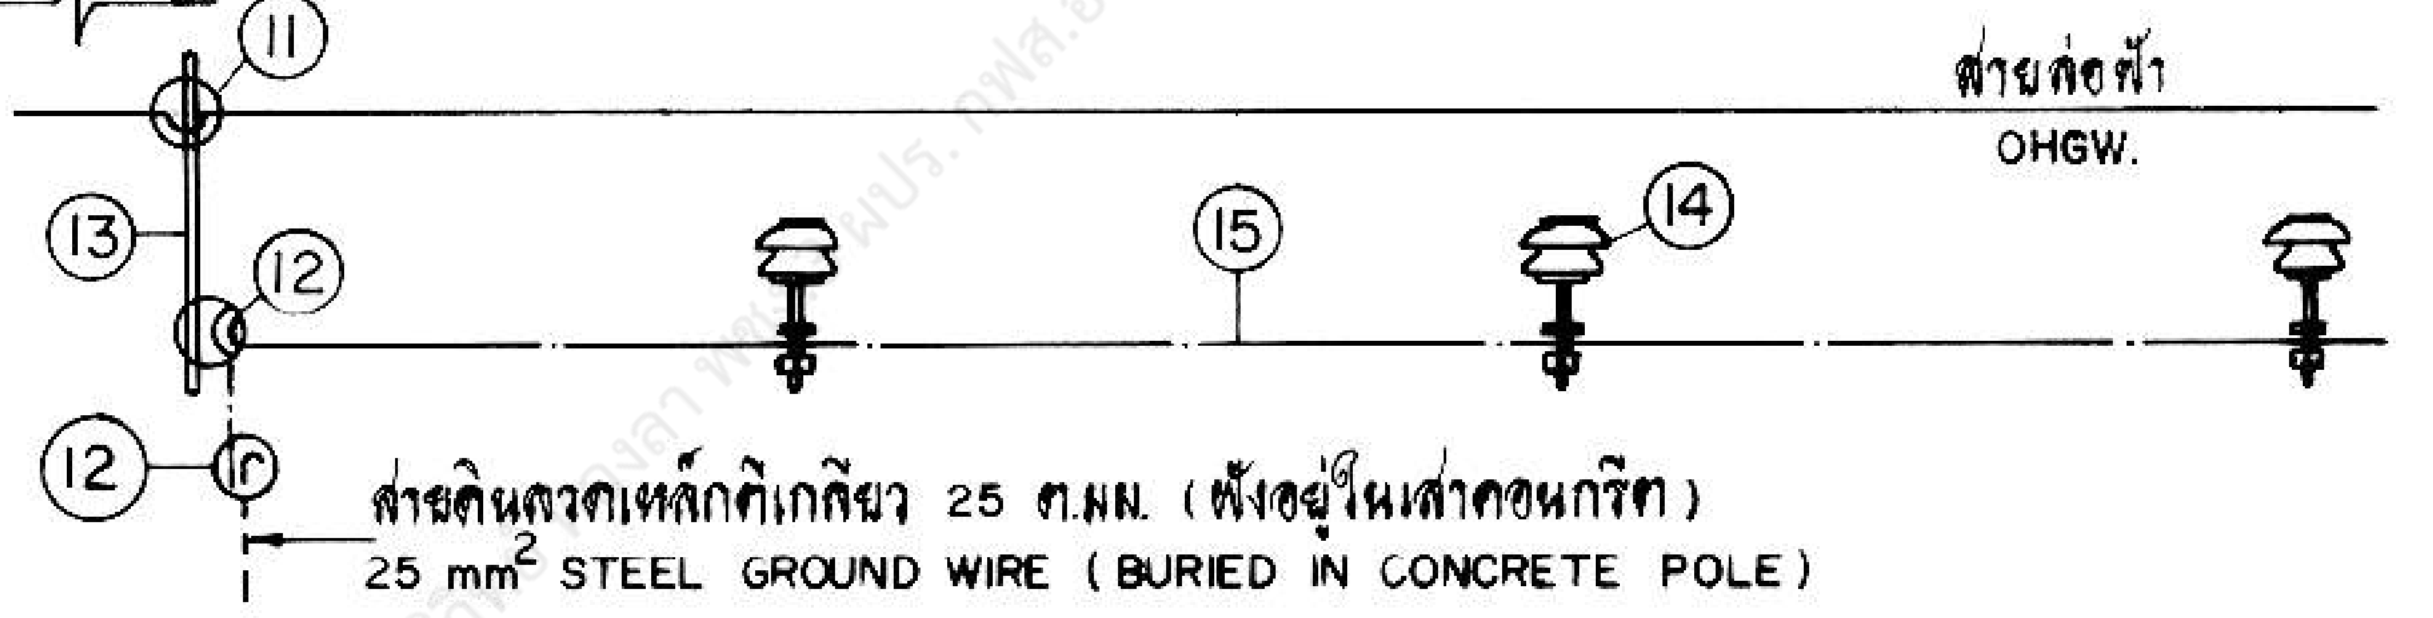
11
สายล่อฟ้า
OHGW.
13
12
15
14
12
สายดินลวดเหล็กตีเกลียว 25 ต.มม. (ฝังอยู่ในเสาคอนกรีต)
25 mm² STEEL GROUND WIRE (BURIED IN CONCRETE POLE)

ไดอะแกรมแสดงการต่อลงดิน
EARTHING DIAGRAM

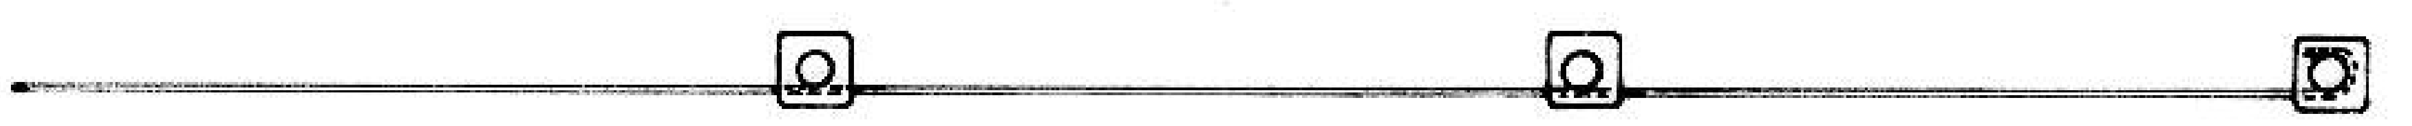

การโค้งตัดสายดินลวดเหล็กเส้นเดี่ยว Ø 4 มม. ต่อระหว่างก้านลูกถ้วย ประกอบที่คอน คอร. สปัน
THE ARRANGEMENT OF Ø 4 mm GALVANIZED STEEL WIRE BOND BETWEEN INSULATOR PINS

กองวิศวกรรมไฟฟ้าและเครื่องกล ฝ่ายวิศวกรรม	การไฟฟ้าส่วนภูมิภาค	ใช้แทนแบบ ถูกแทนโดยแบบ
ผู้เขียน ผู้ตรวจ วิศวกร หัวหน้าแผนก ธีรวัฒน์ หัวหน้ากอง ผู้อำนวยการฝ่าย	ผู้ว่าการ 24 / เม.ย. 21	เขียนเสร็จวันที่ 23 มี.ค. 21 แก้แบบวันที่ 1 มิ.ย. 21 2 ส.ค. 39 มิติเป็น มม. มาตราส่วน 1 : 25
	การประกอบคอน คอร. สปัน แบบก้างแขน กับเสาคอนกรีต ระบบ 33 kV ก สำหรับทางตรง 0°-5°	
รองผู้ว่าการฝ่ายเทคนิค	SPUN PRESTRESSED CONCRETE ALLEY ARM ASSEMBLY 33 kV SYSTEM A TANGENT STRUCTURE 0°-5°	แบบเลขที่ SAI-015/21022 แผ่นที่ 1 ของจำนวน 3 แผ่น

การประกอบเลขที่
ASSEMBLY NO. **3804**

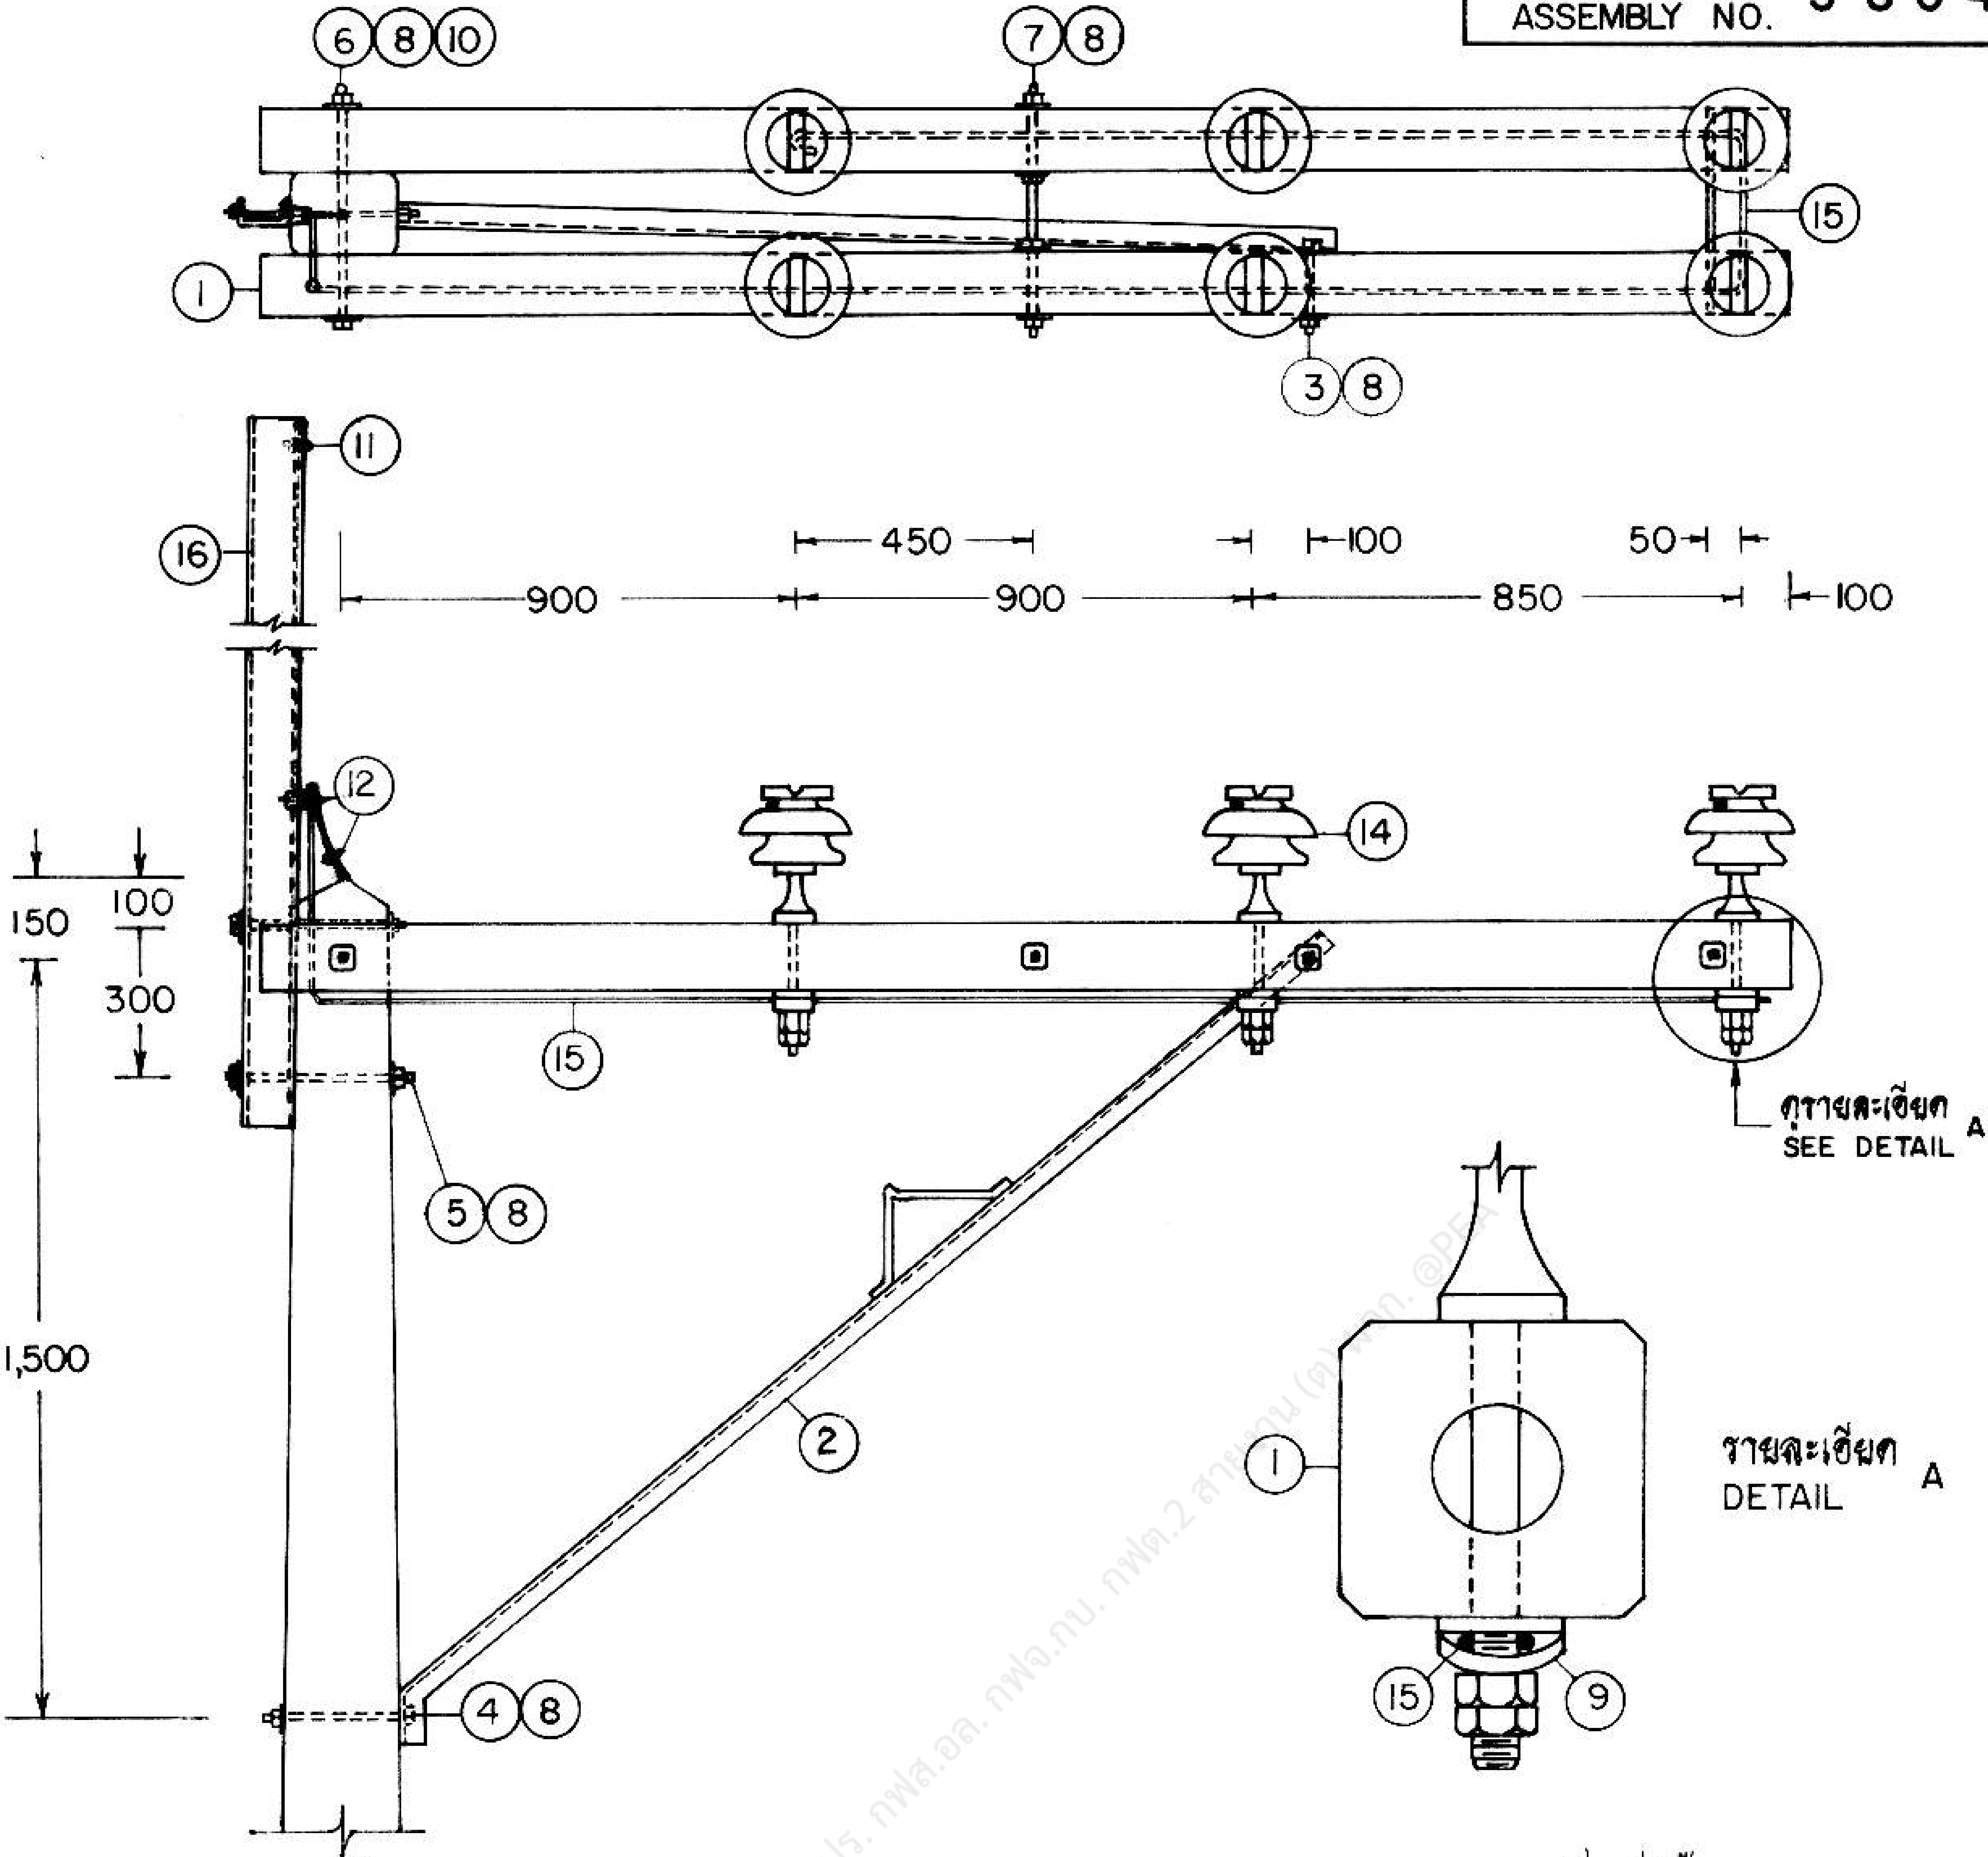

⑥⑧⑩
⑦⑧
①
⑮
③⑧
⑪
⑯
450
100
50
900
900
850
100
⑫
⑭
150
100
300
1,500
⑮
⑤⑧
②
④⑧
ดูรายละเอียด A
SEE DETAIL A
①
⑮
⑨
รายละเอียด A
DETAIL A

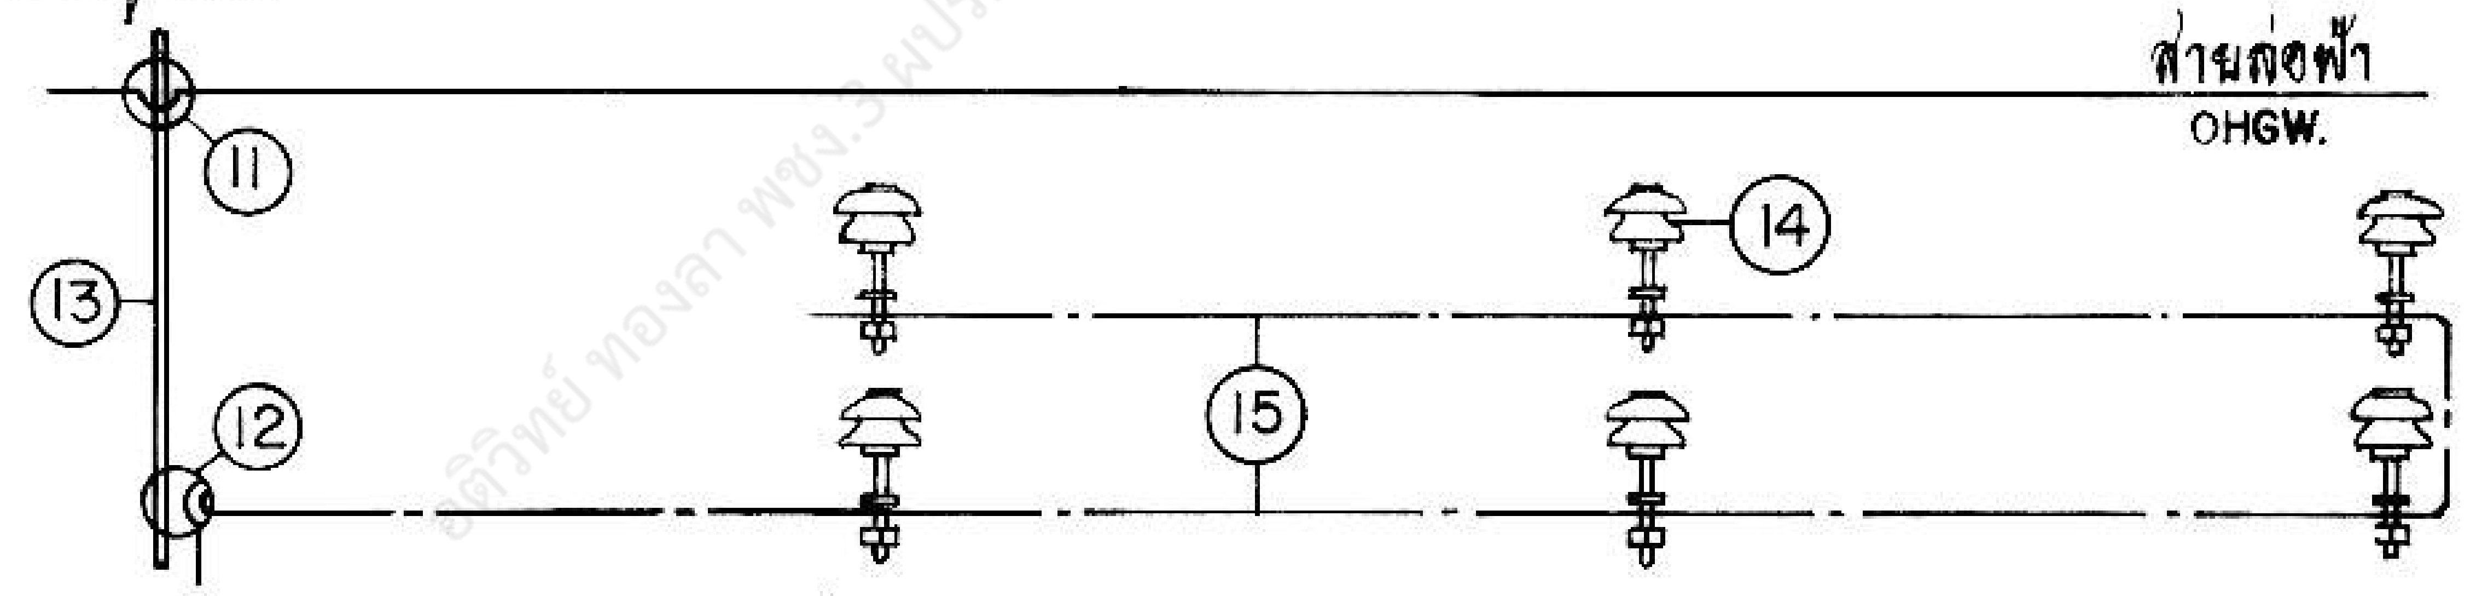

สายล่อฟ้า
OHGW.
⑪
⑬
⑭
⑮
⑫
⑫

ไดอะแกรมแสดงการต่อลงดิน
EARTHING DIAGRAM

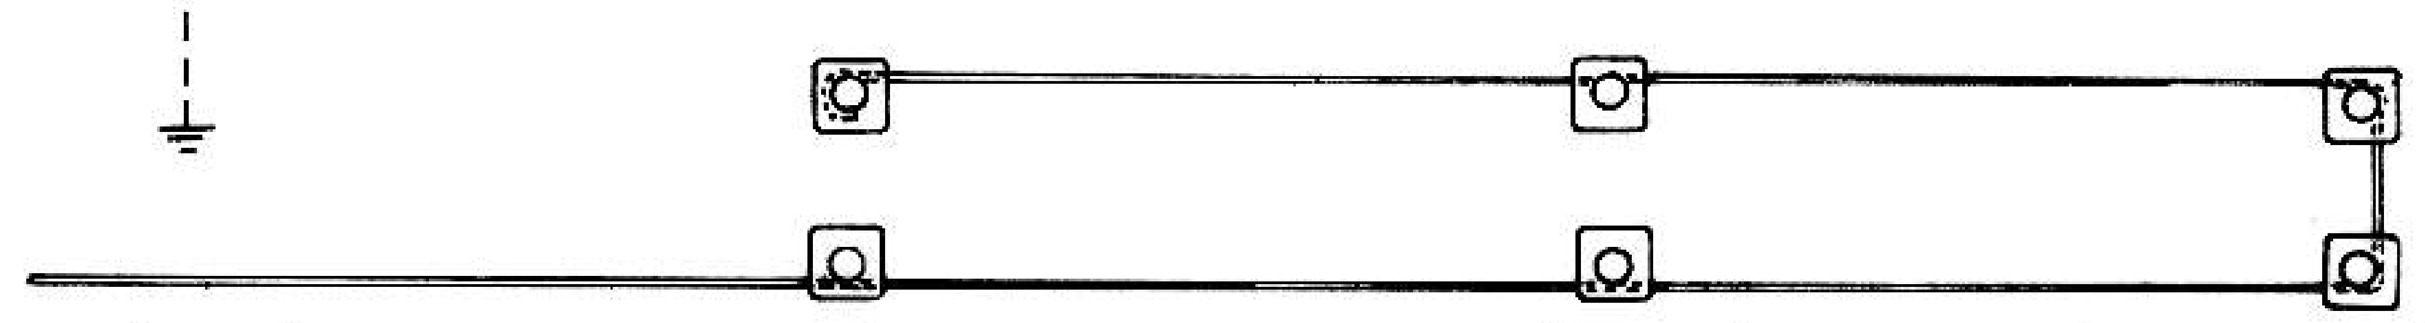

การโค้งดัดสายดินลวดเหล็กเส้นเดี่ยว ø 4 มม. ต่อระหว่างก้านลูกถ้วย ประกอบที่คอน คอร. สปัน
THE ARRANGEMENT OF ø 4 mm GALVANIZED STEEL WIRE BOND BETWEEN INSULATOR PINS

อดิวิทย์ ทองลา พชง.3 ผปร. กฟส.อล. กฟจ.กบ. กฟต.2 สายงาน (ต) กฟภ. @PEA

กองวิศวกรรมไฟฟ้าและเครื่องกล
ฝ่ายวิศวกรรม

ผู้เขียน
ผู้สำรวจ
วิศวกร
หัวหน้าแผนก
หัวหน้ากอง
ผู้อำนวยการฝ่าย
รองผู้ว่าการฝ่ายเทคนิค

การไฟฟ้าส่วนภูมิภาค

ผู้ว่าการ 24 เม.ย. 21.

การประกอบคอน คอร. สปัน แบบทางแคบ กับเสาคอนกรีต
ระบบ 33 kV
ข สำหรับทางโค้ง 5°-30°

SPUN PRESTRESSED CONCRETE ALLEY ARM ASSEMBLY
33 kV SYSTEM
B SMALL ANGLE STRUCTURE 5°-30°

ใช้แทนแบบ
ถูกแทนโดยแบบ
เขียนเสร็จวันที่ 23 มี.ค. 21
แก้แบบวันที่ 1 มิ.ย. 21
มิติเป็น มม. 2 ส.ค. 39
มาตราส่วน 1 : 25

แบบเลขที่ SAI-015/21022
แผ่นที่ 2 ของจำนวน 3 แผ่น

การประกอบเลขที่
ASSEMBLY NO. **3804**

บัญชีวัสดุ
BILL OF MATERIAL

ลำดับที่ ITEM	รายละเอียด DESCRIPTION	จำนวน REQ'D		วัสดุเลขที่ MAT. NO.
		ก/A	ข/B	
1	คอน คอร. สปัน ขนาด 120 X 120 X 3,000 มม. CROSSARM, SPUN, PRESTRESSED CONCRETE 120 X 120 X 3,000 mm	1	2	00110002
2	เหล็กประกับไม้คอน แบบท้าวแขน 50 X 50 X 5 มม. ยาว 2,350 มม. BRACE, ALLEY ARM, 50 X 50 X 5 mm 2,350 mm LONG	1	1	01200005
3	สลักเกลียว M 16 X 170 มม. BOLT, MACHINE, M 16 X 170 mm	1	1	01110201
4	สลักเกลียว M 16 X 250 มม. BOLT, MACHINE, M 16 X 250 mm	3	1	01110203
5	สลักเกลียว M 16 X 350 มม. BOLT, MACHINE, M 16 X 350 mm	1	2	01110205
6	สลักเกลียว M 16 X 450 มม. BOLT, MACHINE, M 16 X 450 mm	–	1	01110207
7	สลักเกลียวตลอด M 16 X 450 มม. BOLT, DOUBLE ARMING M 16 X 450 mm	–	2	01120001
8	แหวนสี่เหลี่ยมแบน ขนาด 52X52X4.5 มม. รู Ø 18 มม. มอก.258 WASHER, SQUARE, FLAT 52X52X4.5 mm HOLE Ø 18 mm TIS 258	6	14	01180100
9	แหวนสี่เหลี่ยมโค้ง ขนาด 60 X 60 X 5 มม. รู Ø 22 มม. WASHER, SQUARE, CURVED 60 X 60 X 5 mm HOLE Ø 22 mm	3	6	01180201
10	แหวนสปริง M 16 มอก. 259 WASHER, LOCK M 16 TIS 259	1	1	01180301
11	กราวด์วายร์แคล้มป์ แบบ J 1152 GROUND WIRE CLAMP J 1152	1	1	01230205
12	ยูแคล้มป์ สลักเดี่ยว M 8 (ไวร์ โร้ป คลิ๊พ) CLAMP, SINGLE U-BOLT M 8 (WIRE ROPE CLIP)	2	2	01230000
13	เหล็กฉากรับสายล่อฟ้า 65 X 65 X 6 มม. ยาว 2,250 มม. OVERHEAD GROUND WIRE BAYONET 65 X 65 X 6 mm 2,250 mm LONG	1	–	01010003
14	ลูกถ้วยก้านตรง 33 kV แบบ ค (แบบ 56-3) มอก. 279 พร้อมก้าน INSULATOR, PIN TYPE, 33 kV, TYPE C (CLASS 56-3) TIS 279 COMP. WITH PIN	3	6	03000002 03100001
15	ลวดเหล็กกลม เส้นผ่าศูนย์กลาง 4 มม. เส้นเดี่ยว (มอก. 71) น้ำหนักประมาณ 0.1 กก./ม. WIRE, STEEL, SOLID, DIAMETER 4 mm (TIS 71) WEIGHT 0.1 kg/m	3.5 ม. m	5.5 ม. m	01100000
16	เหล็กรูปรางน้ำ ขนาด 100 X 50 X 5 มม. ยาว 2,250 มม. STEEL, CHANNEL, 100 X 50 X 5 mm, 2,250 mm LONG	–	1	01000100

กฟต.2 สายงาน (ต) ผวก. @PEA

กองวิศวกรรมไฟฟ้าและเครื่องกล ฝ่ายวิศวกรรม	การไฟฟ้าส่วนภูมิภาค	ใช้แทนแบบ ถูกแทนโดยแบบ เขียนเสร็จวันที่ 23 มี.ค. 21 แก้แบบวันที่ 1 มิ.ย. 21 2 สิ.ค. 39 มิติเป็น มาตราส่วน
ผู้เขียน ผู้สำรวจ วิศวกร หัวหน้าแผนก ชัยรัตน์ หัวหน้ากอง ผู้อำนวยการฝ่าย	ผู้ว่าการ 24 เม.ย. 21 การประกอบคอน คอร. สปัน แบบท้าวแขน กับเสาคอนกรีต ระบบ 33 kV	
รองผู้ว่าการฝ่ายเทคนิค	SPUN PRESTRESSED CONCRETE ALLEY ARM ASSEMBLY 33 kV SYSTEM	แบบเลขที่ SAI-015/21022 แผ่นที่ 3 ของจำนวน 3 แผ่น