
# ก) โครงสร้างสายส่ง 115 kV วงจรเดี่ยว
# A) 115 kV SINGLE CIRCUIT STRUCTURE CONSTRUCTION

การประกอบเลขที่ ASSEMBLY NO. **5 I 5 9**

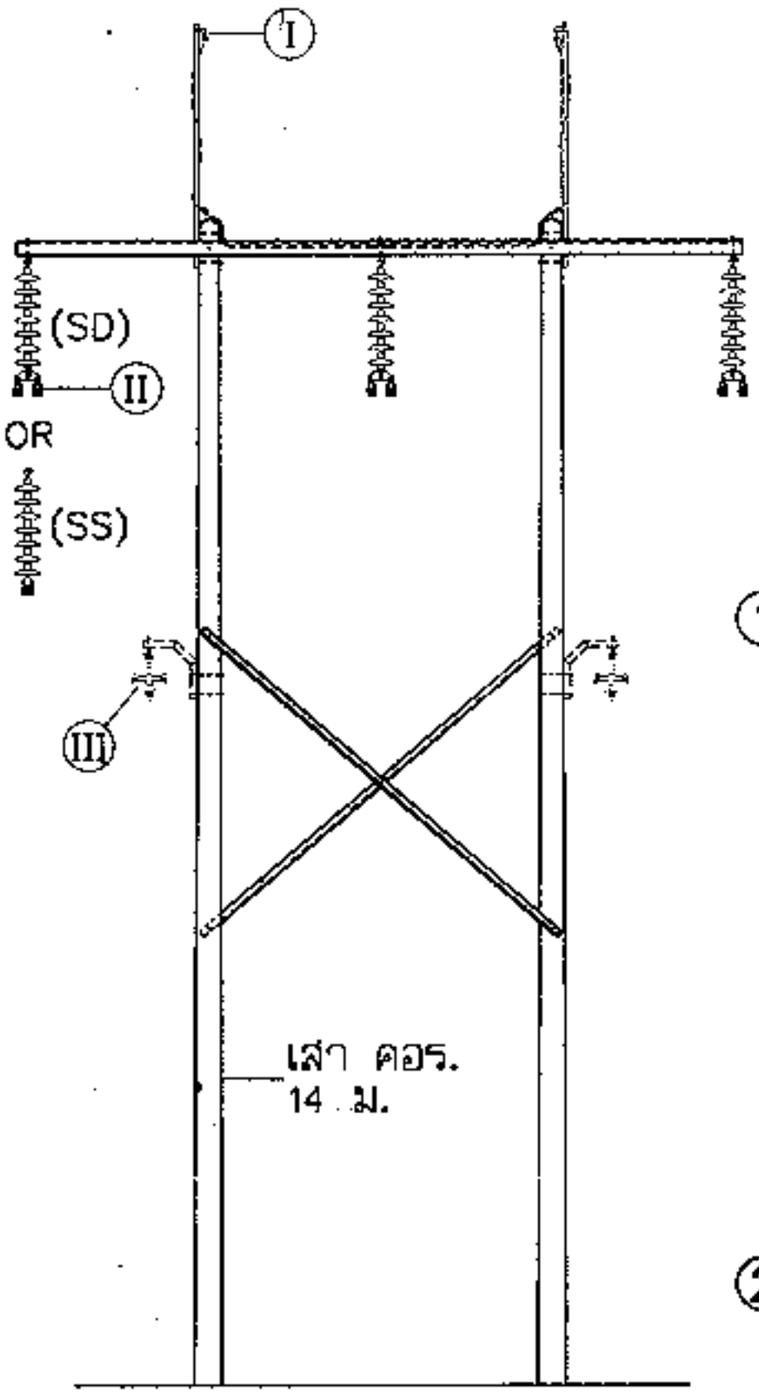



| ที่ ITEM | วงจรระบบ SYSTEM CIRCUIT | ขนาดสายสูงสุด (ต.มม.) MAX.COND.SIZE ($mm^2$) | จำนวน (เส้น) QUANTITY (WIRE) |
|---|---|---|---|
| I | สายล่อฟ้า OHGW. | 35 | 2 |
| II | สายเปลือย 115 kV 115 kV BARE CONDUCTOR | 400 | 3(SS), 6(SD) |
| III | เคเบิลอากาศ AERIAL CABLE | 185 | 3 or 6 |

## ① โครงสร้างทางตรง TANGENT STRUCTURE (0° – 2°)

| วงจรระบบ SYSTEM CIRCUIT | | ระยะช่วงเสาสูงสุด (ม.) MAX. SPAN (m) | หมายเหตุ NOTE |
|---|---|---|---|
| วงจร 115 kV 115 kV CIRCUIT | (I+II) | 40 | – |
| วงจร 22, 33 kV 22, 33 kV CIRCUIT | (III) | | |

## ② โครงสร้างทางโค้ง SLACK SPAN ANGLE STRUCTURE

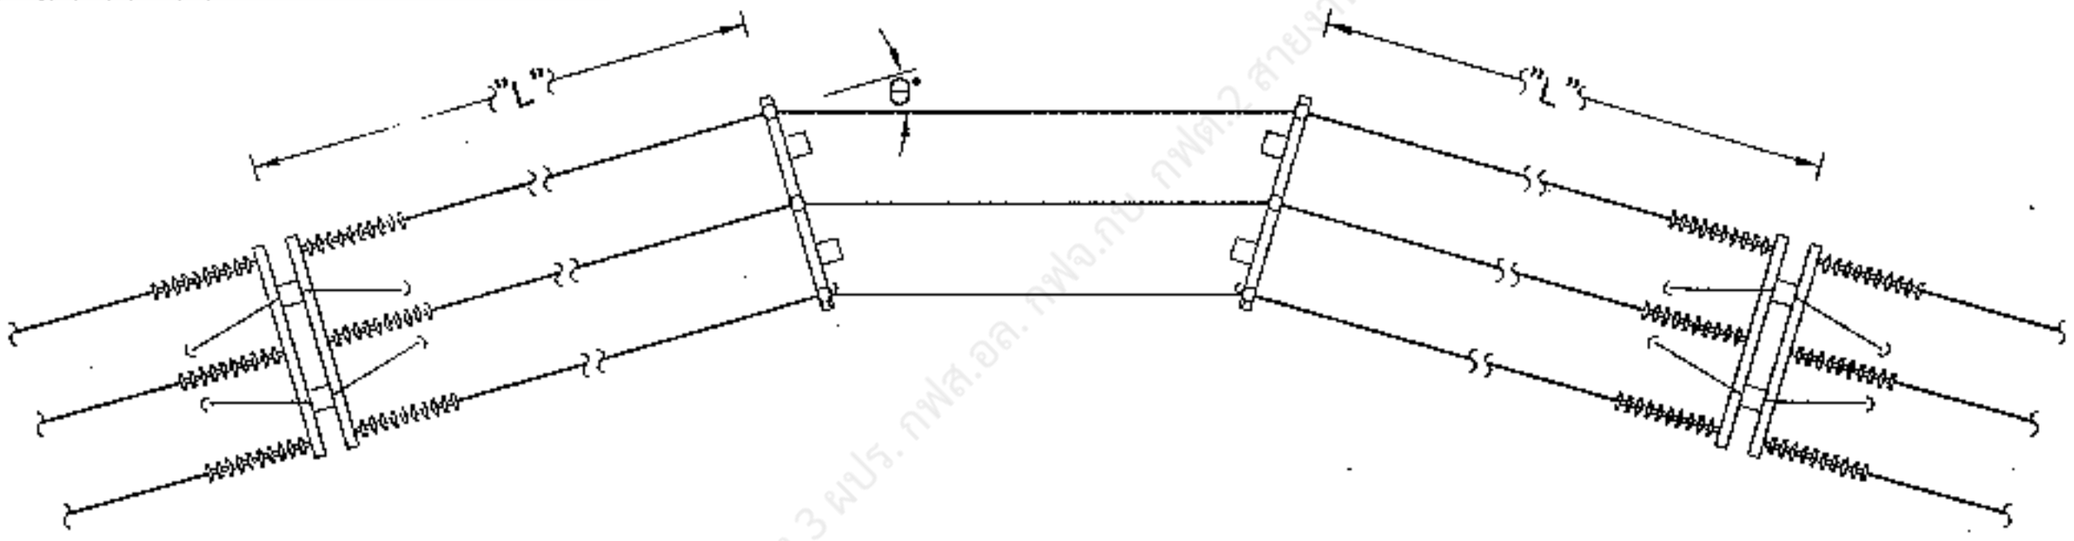



| มุมเบี่ยงเบนระหว่างเสา LINE DEFLECTION ANGLE (θ°) | "L" ช่วงเสาสูงสุด (ม.) MAX. SPAN (m) | ระยะหย่อนยานของสายไม่น้อยกว่า (ม.) MINIMUM SAG (m) | | |
|---|---|---|---|---|
| | | I | II | III |
| 2° – 5° | 35 | 0.50 | 1.50 | 1.00 |
| 5° – 10° | 30 | 0.50 | 1.50 | 1.00 |
| 10° – 15° | 25 | 0.50 | 1.20 | 0.80 |
| 15° – 30° | 20 | 0.50 | 1.20 | 0.80 |


| | | |
|---|---|---|
| กองวิศวกรรมไฟฟ้าและเครื่องกล ฝ่ายวิศวกรรม | การไฟฟ้าส่วนภูมิภาค | ใช้แทนแบบ ..... ถูกแทนโดยแบบ ..... |
| ผู้เขียน ..... ผู้สำรวจ ..... วิศวกร ..... หัวหน้าแผนก ..... ผู้อำนวยการกอง ..... ผู้อำนวยการฝ่าย ..... | ผู้ว่าการ ..... 23 ธ.ค. 2541 | เขียนเสร็จวันที่ 14 ต.ค. 2541 แก้แบบวันที่ ..... มิติเป็น ..... มาตราส่วน ..... |
| รองผู้ว่าการเทคนิคและบริการ ..... | ระยะห่างระหว่างช่วงเสาสำหรับโครงสร้างสายส่ง 115 kV กรณีก่อสร้างบนเขา<br>SPAN LENGTHS FOR 115 kV STRUCTURE CONSTRUCTION IN CASE OF CONSTRUCTION ON THE MOUNTAIN | แบบเลขที่ SA1-015/41019 แผ่นที่ 1 ของจำนวน 2 แผ่น |

23 ธ.ค. 2541


การประกอบเลขที่ ASSEMBLY NO. **5 I 5 9**

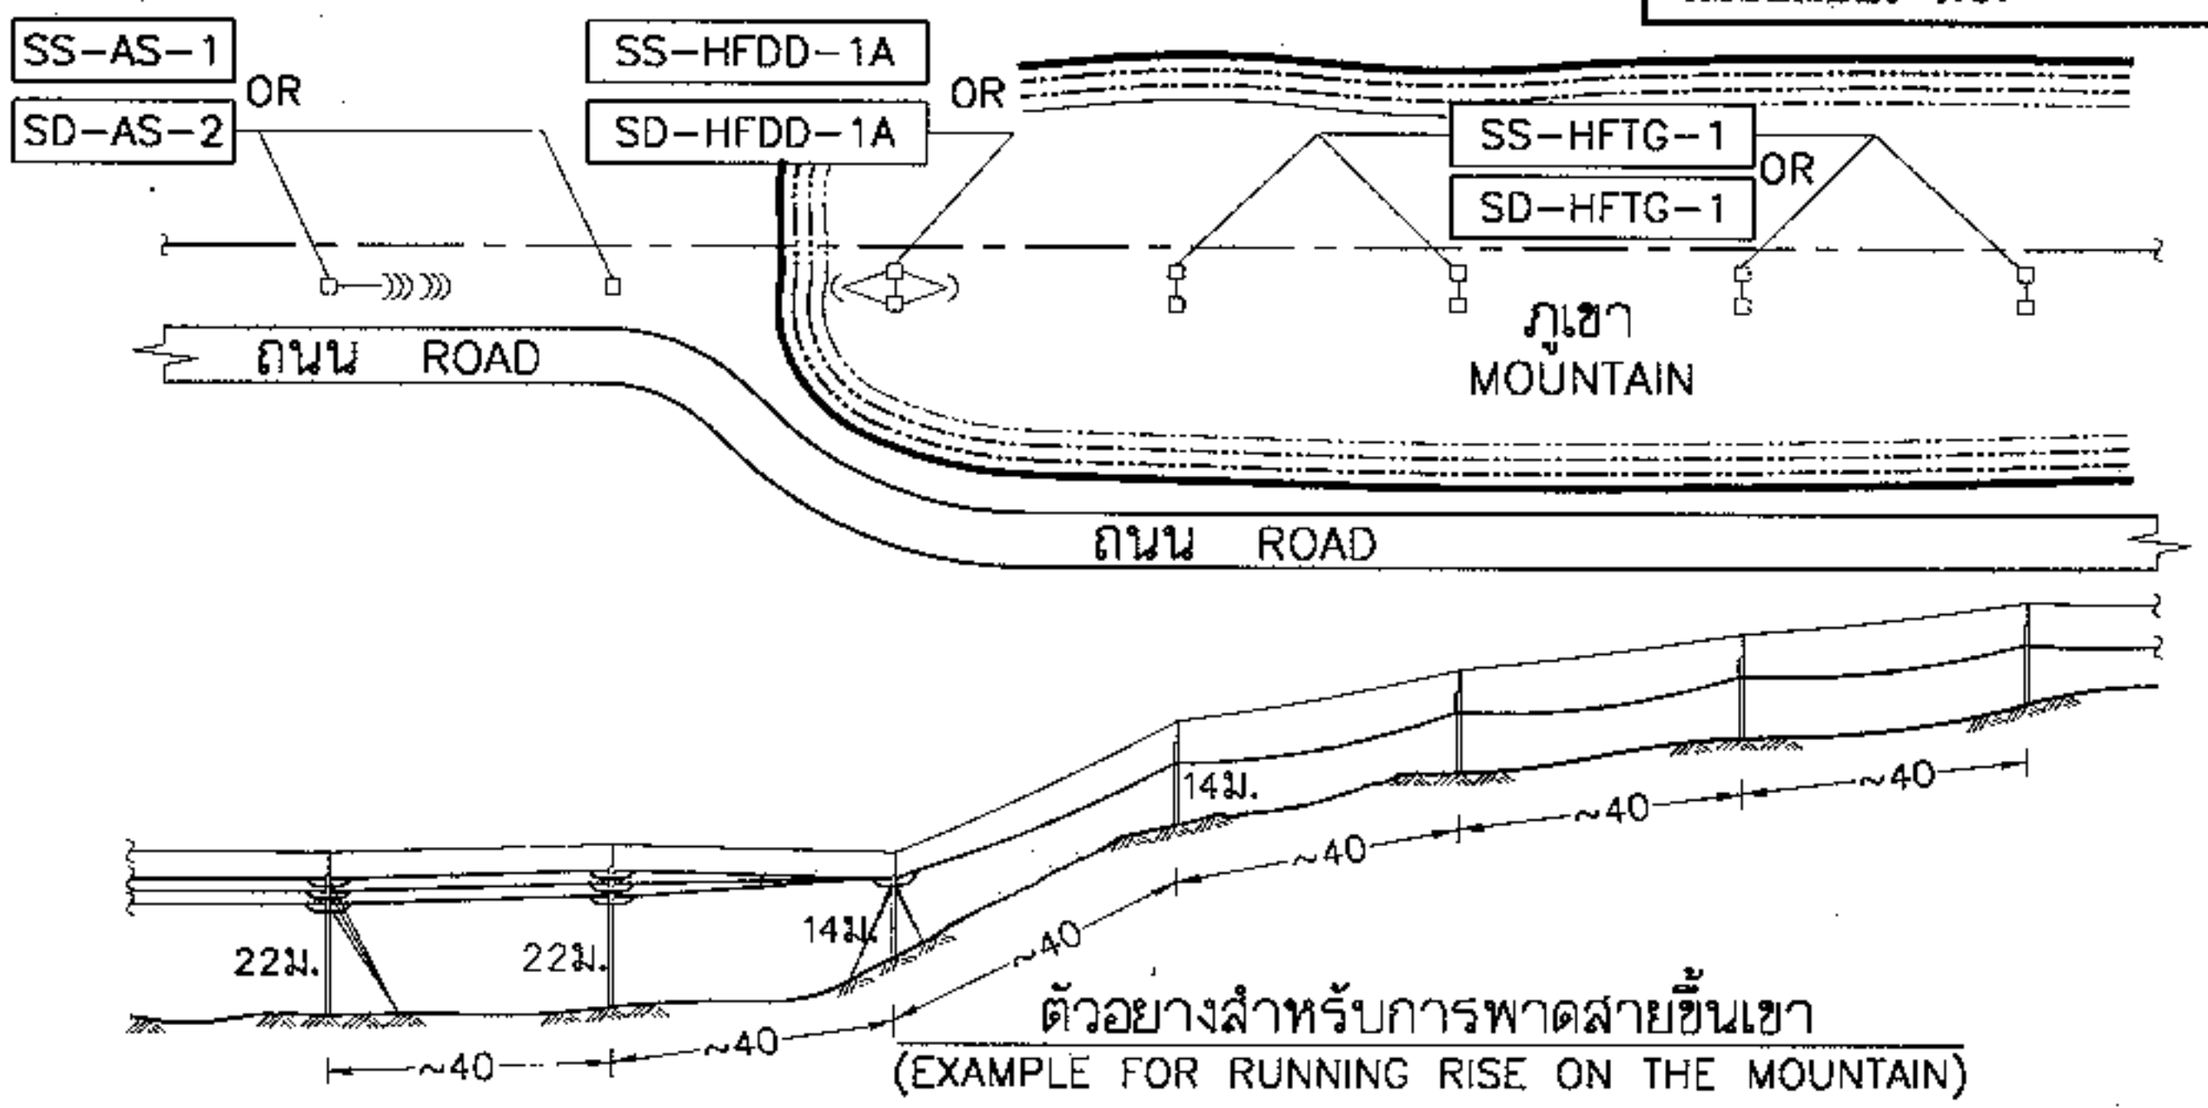


ตัวอย่างสำหรับการพาดสายขึ้นเขา
(EXAMPLE FOR RUNNING RISE ON THE MOUNTAIN)

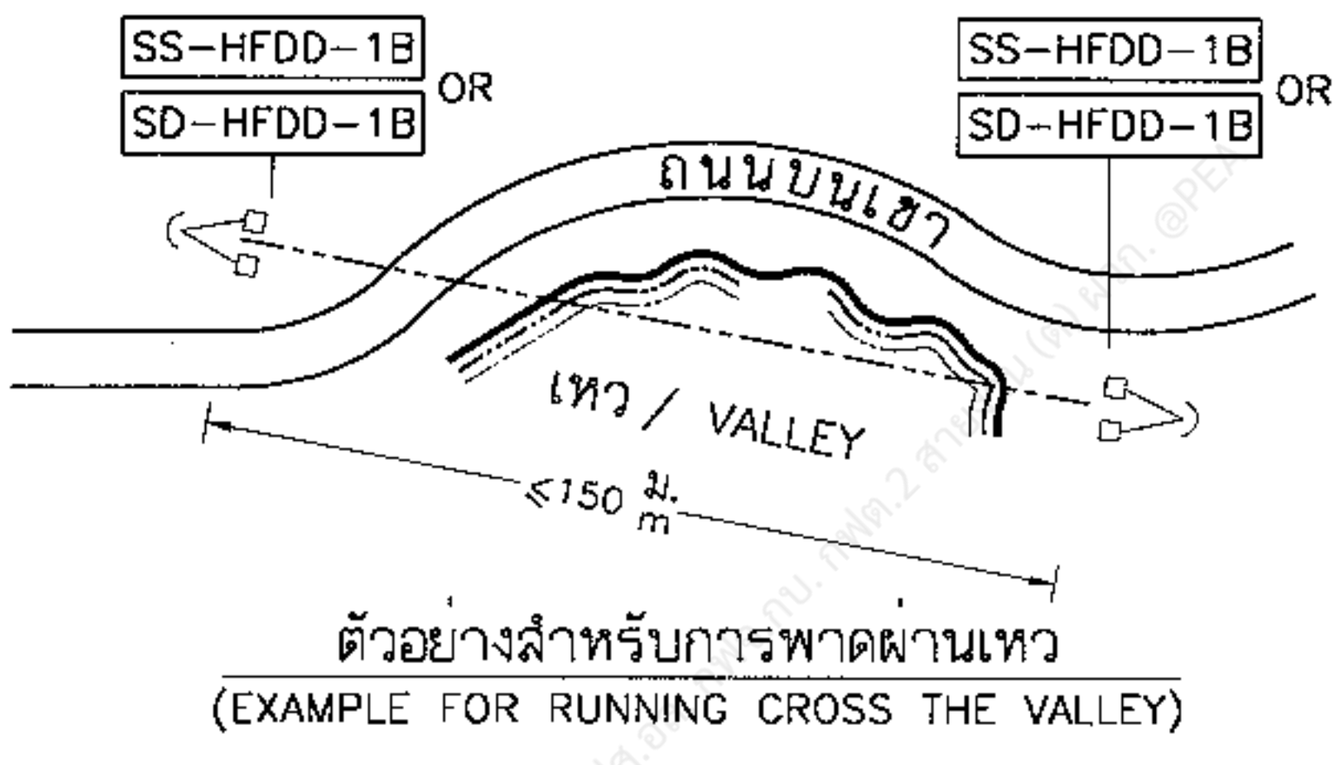


ตัวอย่างสำหรับการพาดผ่านเหว
(EXAMPLE FOR RUNNING CROSS THE VALLEY)

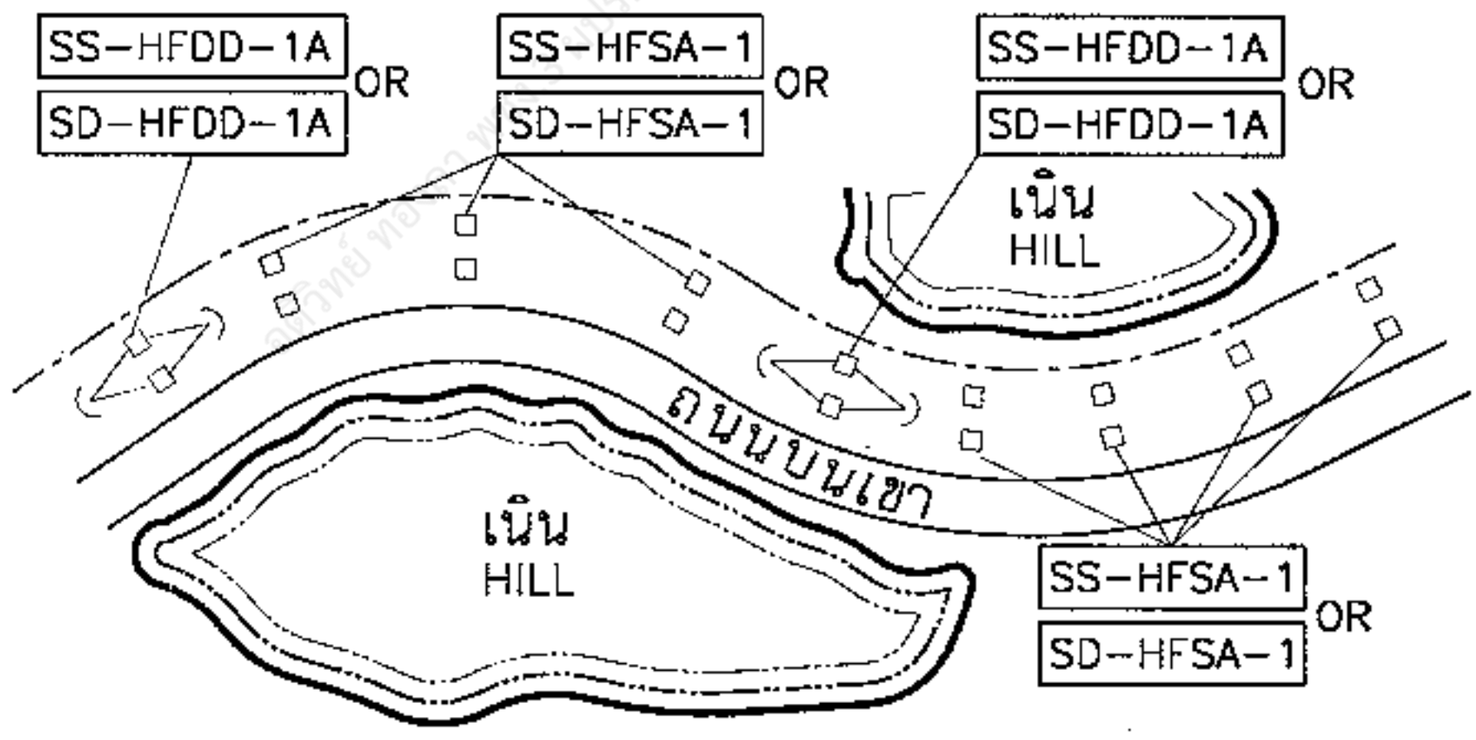


ตัวอย่างสำหรับการพาดสายทางโค้ง
(EXAMPLE FOR RUNNING IN THE SMALL ANGLE)

| | | |
|---|---|---|
| กองวิศวกรรมไฟฟ้าและเครื่องกล<br>ฝ่ายวิศวกรรม | การไฟฟ้าส่วนภูมิภาค | ใช้แทนแบบ .....<br>ถูกแทนโดยแบบ ..... |
| ผู้เขียน Supphalit Boonsaeng<br>ผู้สำรวจ.....<br>วิศวกร.....<br>หัวหน้าแผนก.....<br>ผู้อำนวยการกอง.....<br>ผู้อำนวยการฝ่าย..... | ผู้ว่าการ..... 23 ธ.ค. 2541 | เขียนเสร็จวันที่ 14 ต.ค. 2541<br>แก้แบบวันที่ .....<br>มิติเป็น.....<br>มาตราส่วน..... |
| รองผู้ว่าการเทคนิคและบริการ<br>..... | ระยะห่างระหว่างช่วงเสาสำหรับโครงสร้างสายส่ง 115 kV กรณีก่อสร้างบนเขา<br>SPAN LENGTHS FOR 115 kV STRUCTURE CONSTRUCTION IN CASE OF CONSTRUCTION ON THE MOUNTAIN | แบบเลขที่ SA1-015/41019<br>แผ่นที่ 2 ของจำนวน 2 แผ่น |

23 ธ.ค. 2541