การประกอบเลขที่ ASSEMBLY NO. 5687 C

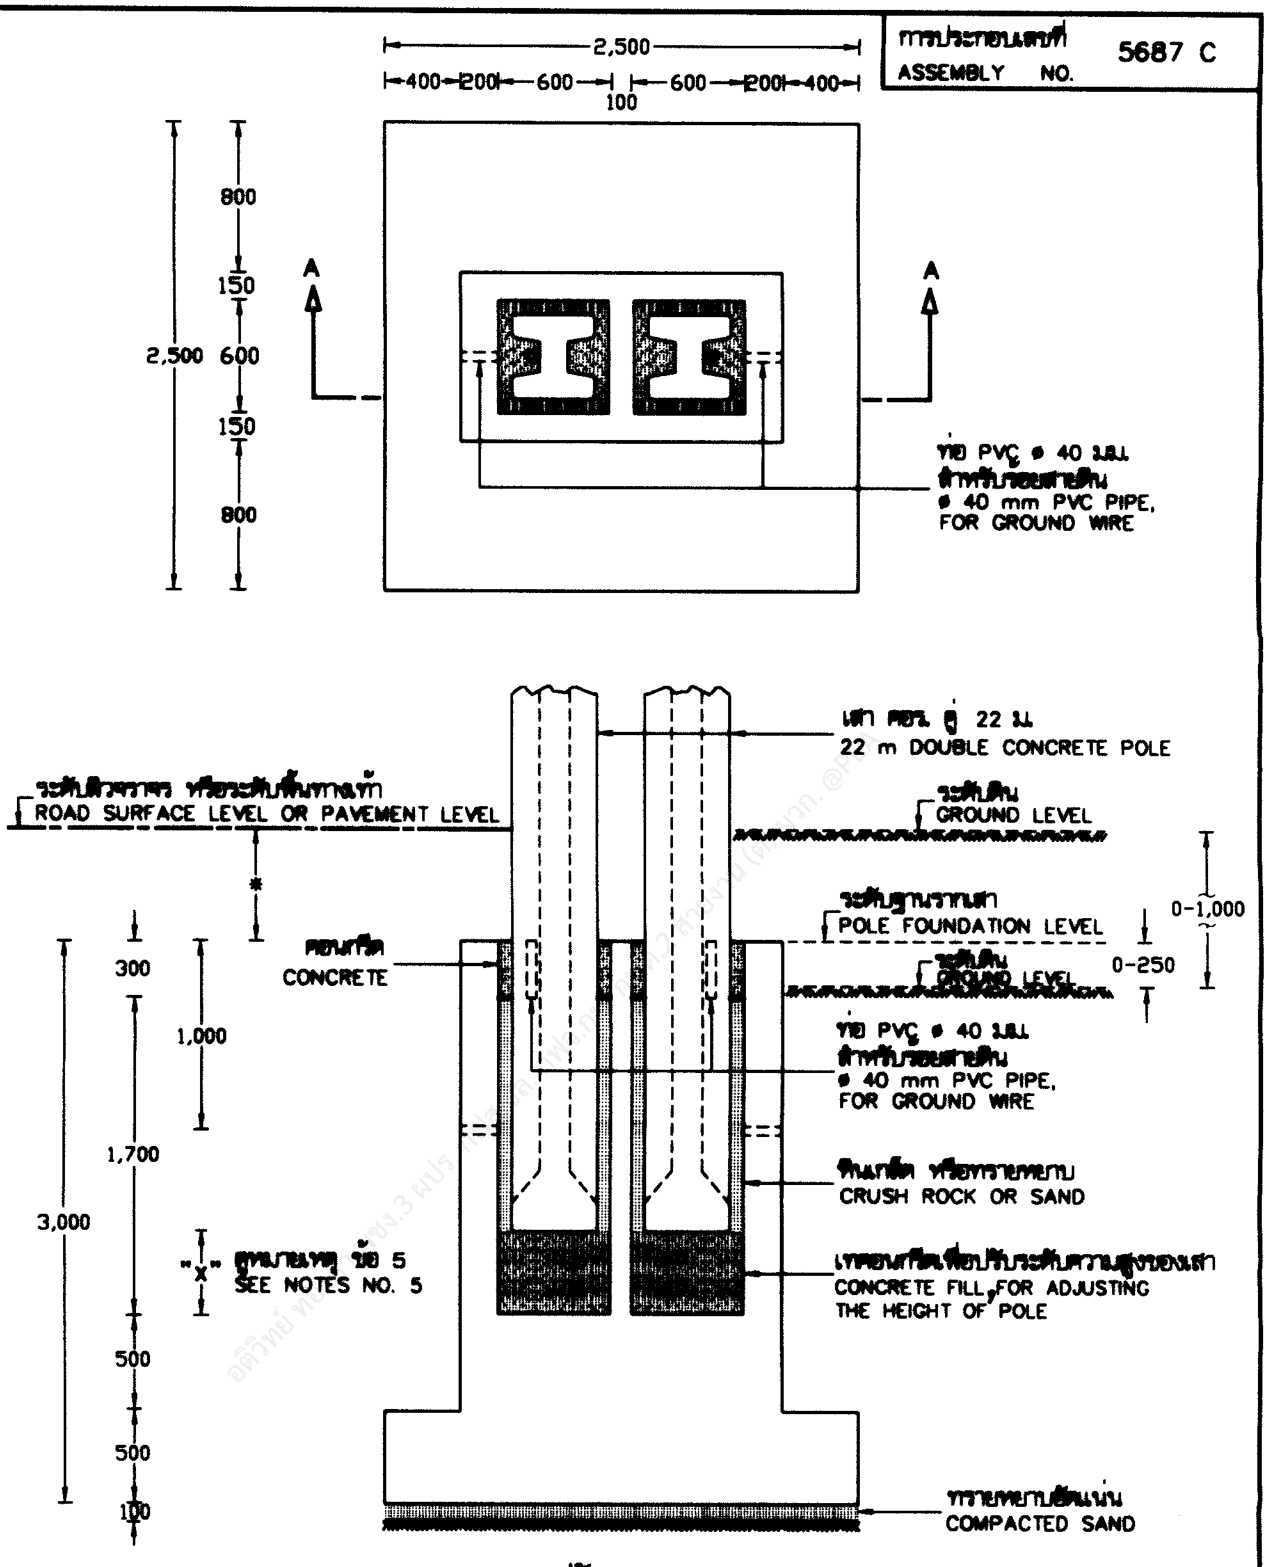
2,500
400 200 600 100 600 200 400
800
150
600
150
800
2,500
A
A
ท่อ PVC ⌀ 40 มม. สำหรับร้อยสายดิน
⌀ 40 mm PVC PIPE, FOR GROUND WIRE
เสา คอร. คู่ 22 ม.
22 m DOUBLE CONCRETE POLE
ระดับผิวจราจร หรือระดับพื้นทางเท้า
ROAD SURFACE LEVEL OR PAVEMENT LEVEL
ระดับดิน
GROUND LEVEL
*
ระดับฐานรากเสา
POLE FOUNDATION LEVEL
0-1,000
0-250
ระดับดิน
GROUND LEVEL
คอนกรีต
CONCRETE
300
1,000
1,700
3,000
ท่อ PVC ⌀ 40 มม. สำหรับร้อยสายดิน
⌀ 40 mm PVC PIPE, FOR GROUND WIRE
หินเกล็ด หรือทรายหยาบ
CRUSH ROCK OR SAND
"X" ดูหมายเหตุ ข้อ 5
SEE NOTES NO. 5
เทคอนกรีตเพื่อปรับระดับความสูงของเสา
CONCRETE FILL, FOR ADJUSTING THE HEIGHT OF POLE
500
500
100
ทรายหยาบอัดแน่น
COMPACTED SAND

รูปตัด SECTION A-A

กองมาตรฐานระบบไฟฟ้า
ฝ่ายมาตรฐานและความปลอดภัย

การไฟฟ้าส่วนภูมิภาค

ผู้เขียน ..สมชาย..............
ผู้ตรวจ ....
วิศวกร ....
หัวหน้าแผนก ....
ผู้อำนวยการกอง ....
ผู้อำนวยการฝ่าย ....

รองผู้ว่าการวางแผนและพัฒนาระบบไฟฟ้า
....

ผู้ว่าการ ....

รายละเอียดที่ 10 B 23 ก.ย. 2547
ฐานรากเสา (แบบที่ 9 ชนิดสำเร็จรูป)

DETAIL 10 B
POLE FOUNDATION (TYPE 9 , PRECAST TYPE)

ใช้แทนแบบ SA1-015/45012
ถูกแทนโดยแบบ ....
เขียนเสร็จวันที่ .10 ส.ค. 2547
แก้แบบวันที่ ....
[illegible] .[illegible]........
มาตราส่วน ....1:40..........
แบบเลขที่ .SA1-015/47020
แผ่นที่ .1. ของจำนวน .2. แผ่น

23 ก.ย. 2547

การประกอบเลขที่
ASSEMBLY NO. 5687 C

หมายเหตุ

1 ฐานรากนี้ใช้ในกรณีดินสามารถรับน้ำหนักปลอดภัย ได้ตั้งแต่ 12 ตัน/ ตารางเมตรขึ้นไป
2 ใช้ในกรณีทางตรงหรือทางโค้ง ที่มีและไม่มีสายยึดโยง (กรณีพื้นที่ก่อสร้างฐานรากเสามีระดับต่ำกว่าระดับผิวจราจร หรือระดับพื้นทางเท้า 0.00-1.00 ม.)

3 ดูรายละเอียดเพิ่มเติมใน แบบเลขที่ IB2-011/44012
4* ดูข้อกำหนดการติดตั้งฐานรากเสาในเขตทางหลวง ตามแบบเลขที่ SA1-015/43012 (การประกอบเลขที่ 5687)

5 ระยะ "X"= 450 มม. สำหรับการก่อสร้างฐานรากเสา ในพื้นที่ทางหลวงที่ไม่มีทางเท้า ส่วนพื้นที่อื่นๆ ระยะ "X"= 0 มม.

NOTES

1 THIS FOUNDATION IS USED IN CASE ALLOWABLE SOIL BEARING CAPACITY OF 12 TON/m^2 OR MORE .
2 USE FOR STRAIGHT OR ANGLE LINE WITH AND WITHOUT GUY (IN CASE OF GROUND SURFACE LEVEL IS BETWEEN 0.00–1.00 m LOWER THAN ROAD SURFACE LEVEL OR PAVEMENT LEVEL) .
3 SEE ADDITIONAL DETAIL, DWG. NO. IB2-011/44012 .
4* SEE RECOMMENDATION, FOR POLE FOUNDATION INSTALLATION IN HIGHWAY AREA, DWG. NO. SA1-015/43012 (ASSEMBLY NO. 5687) .
5 THE "X" IS 450 mm HEIGHT FOR FOUNDATION CONSTRUCTION IN HIGHWAY AREA WHICH HAVE NO PAVEMENT, OTHER AREA THE "X" IS ZERO .

อดิวิทย์ ทองลา พชง.3 ผบร. กฟส.อล. กฟจ.กน. กฟต.2 สายงาน (ต) ผวก. @PEA

กองมาตรฐานระบบไฟฟ้า
ฝ่ายมาตรฐานและความปลอดภัย

การไฟฟ้าส่วนภูมิภาค

ผู้เขียน ..สมชาย..
ผู้ตรวจ
วิศวกร
หัวหน้าแผนก
ผู้อำนวยการกอง
ผู้อำนวยการฝ่าย
รองผู้ว่าการวางแผนและพัฒนาระบบไฟฟ้า

ผู้ว่าการ

23 ก.ย. 2547

รายละเอียดที่ 10 B
ฐานรากเสา (แบบที่ 9 ชนิดสำเร็จรูป)

DETAIL 10 B
POLE FOUNDATION (TYPE 9 , PRECAST TYPE)

ใช้แทนแบบ SA1-015/45012
ถูกแทนโดยแบบ
เขียนเสร็จวันที่ 10 ส.ค. 2547
แก้แบบวันที่
มิติเป็น
มาตราส่วน
แบบเลขที่ SA1-015/47020
แผ่นที่ 2 ของจำนวน 2 แผ่น

23 ก.ย. 2547