การประกอบเลขที่ ASSEMBLY NO. **5272**

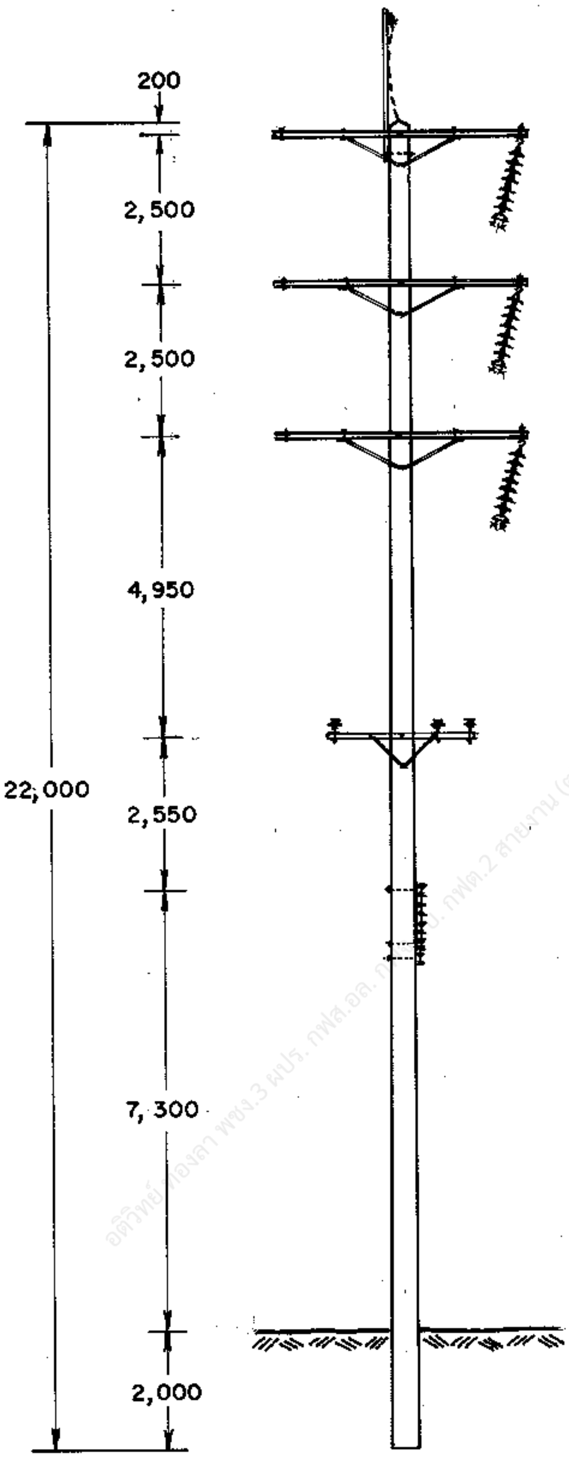

อลิวิทย์ ทองลา พชง.3 ผปร. กฟส.อล. กฟต.2 สายงาน (ต) ผวก. @PEA

กองวิศวกรรมไฟฟ้าและเครื่องกล ฝ่ายวิศวกรรม	**การไฟฟ้าส่วนภูมิภาค**	ใช้แทนแบบ ถูกแทนโดยแบบ
ผู้เขียน สมหมาย ผู้ตรวจ วิศวกร หัวหน้าแผนก ผู้อำนวยการกอง ผู้อำนวยการฝ่าย	ผู้ว่าการ 5 ม.ค. 2537	เขียนเสร็จวันที่ 15 ธค.2536 แก้แบบวันที่
	115 kV วงจรเดี่ยว สายไฟฟ้าคู่ เสาต้นทางตรง ก่อนเสาต้นเจ้าปลายสาย แบบ SD-TG-6	มิติเป็น มิลลิเมตร มาตราส่วน 1 : 125
รองผู้ว่าการฝ่ายเทคนิค	115 kV SINGLE CIRCUIT DOUBLE CONDUCTOR TANGENT STRUCTURE ADJACENT TO DEADEND POLE TYPE SD-TG-6	แบบเลขที่ SAI-015/36006 แผ่นที่ 1 ของจำนวน 3 แผ่น

2536

การประกอบเลขที่ 5272
ASSEMBLY NO. 5272

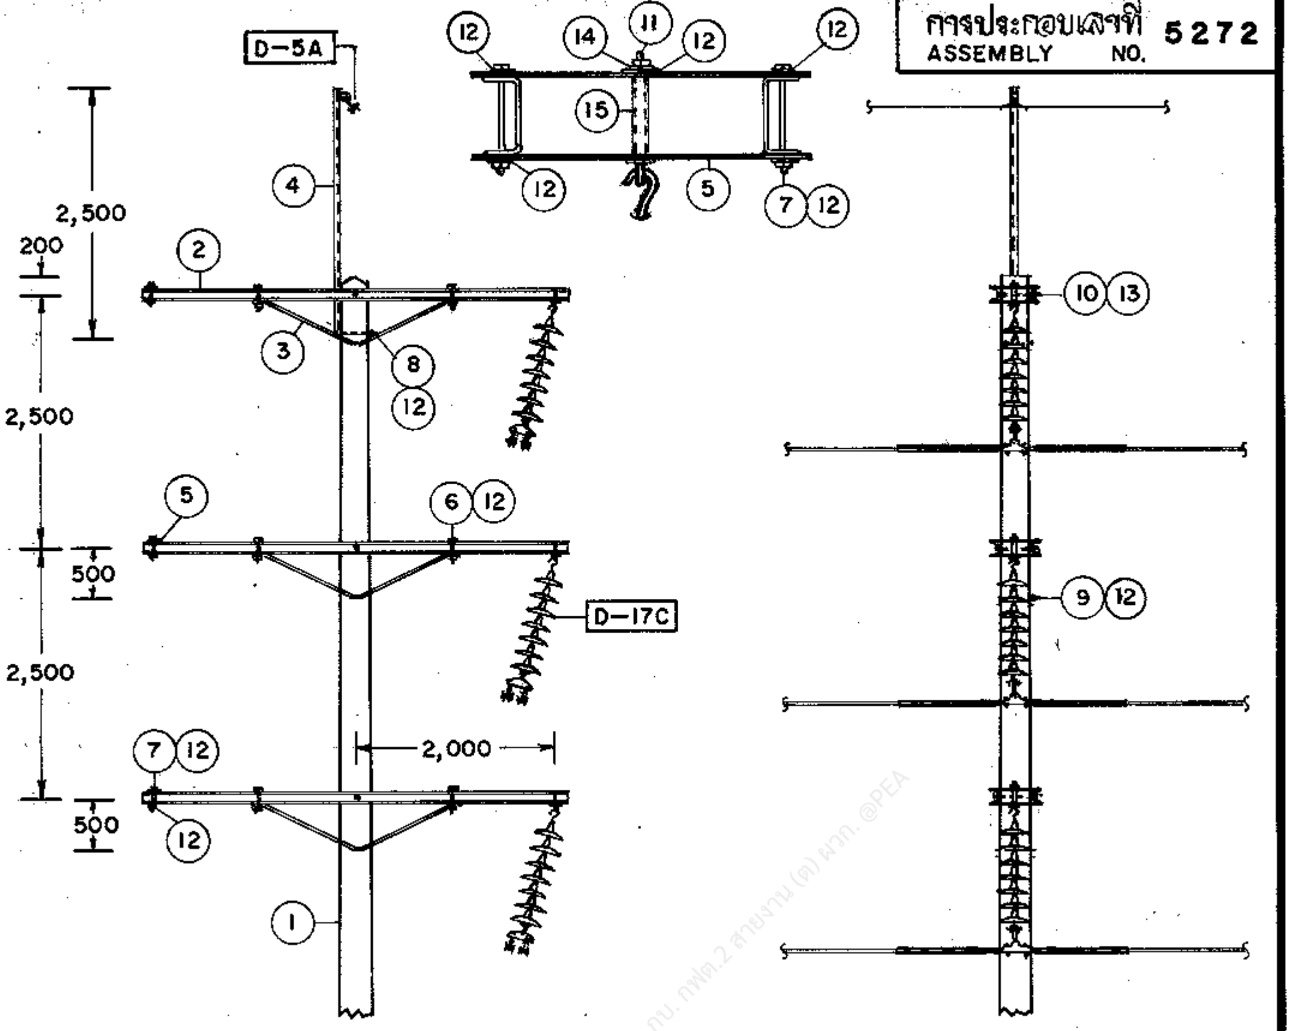

SD-TG-6

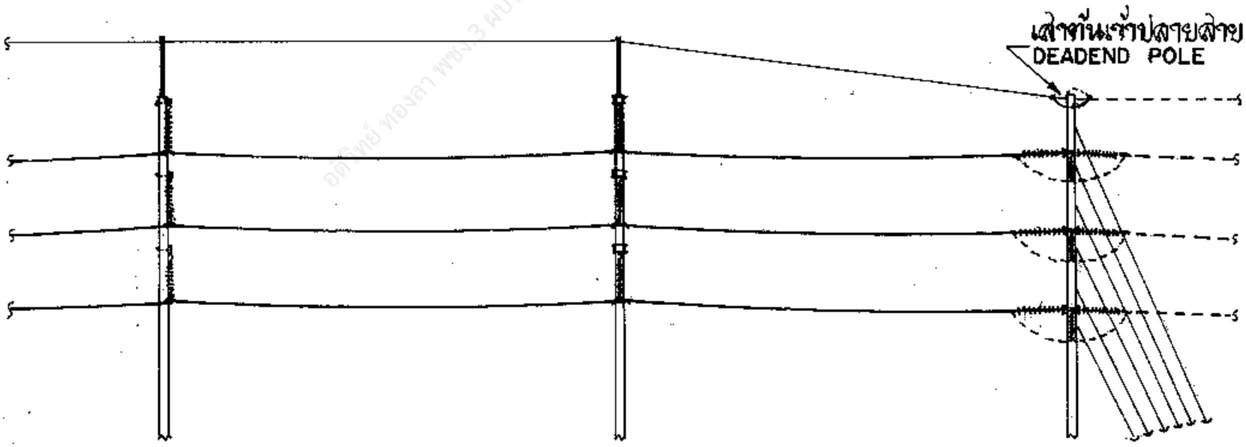

SD-TG-1

SD-TG-6

กองวิศวกรรมไฟฟ้าและเครื่องกล ฝ่ายวิศวกรรม	การไฟฟ้าส่วนภูมิภาค	ใช้แทนแบบ ถูกแทนโดยแบบ เขียนเสร็จวันที่ 15ธค.2536 แก้แบบวันที่ มิติเป็น มิลลิเมตร มาตราส่วน 1 : 75
ผู้เขียน ผู้ตรวจ วิศวกร หัวหน้าแผนก ผู้อำนวยการกอง ผู้อำนวยการฝ่าย	ผู้ว่าการ 5 ส.ค. 2537 115 kV วงจรเดี่ยว สายไฟฟ้าคู่ เสาต้นทางตรง ก่อนเสาต้นเข้าปลายสาย แบบ SD-TG-6	
รองผู้ว่าการฝ่ายเทคนิค	115 kV SINGLE CIRCUIT DOUBLE CONDUCTOR TANGENT STRUCTURE ADJACENT TO DEADEND POLE TYPE SD-TG-6	แบบเลขที่ SAI-015/36006 แผ่นที่ 2 ของจำนวน 3 แผ่น

การประกอบเลขที่
ASSEMBLY NO. **5272**

บัญชีวัสดุ
BILL OF MATERIAL

ลำดับที่ ITEM	รายละเอียด DESCRIPTION	จำนวน REQ'D	วัสดุเลขที่ MAT. NO.
1	เสาคอนกรีต 22 ม. POLE, CONCRETE 22 m LONG	1	00010011 (0041)
2	คอนสายแบบเหล็กรูปรางน้ำ ขนาด 100X50X5 มม. ยาว 4.20 ม. มอก. 116 CROSSARM, STEEL, CHANNEL 100X50X5 mm, 4.20 m LONG, TIS 116	6	
3	เหล็กฉากรับคอนสาย ขนาด 50X50X6 มม. ช่วงกว้าง 1,800 มม. ดรอพ 450 มม. BRACE, ANGLE STEEL, 50X50X6 mm, 1,800 mm WIDE, 450 mm DROP	6	01200007 (0119)
4	เหล็กฉากรับสายล่อฟ้าทางตรง ยาว 2.50 ม. OVERHEAD GROUND WIRE BAYONET, 2.50 m LONG	1	01010004 (0135)
5	เหล็กแผ่น ขนาด 6X100X450 มม. PLATE, STEEL, 6X100X450 mm	12	01030002 (0143)
6	สลักเกลียว M 16X130 มม. BOLT, MACHINE, M 16X130 mm	12	01110200 (0220)
7	สลักเกลียว M 16X170 มม. BOLT, MACHINE, M 16X170 mm	12	01110201 (0221)
8	สลักเกลียว M 16X300 มม. BOLT, MACHINE, M 16X300 mm	2	01110204 (0224)
9	สลักเกลียว M 16X350 มม. BOLT, MACHINE, M 16X350 mm	3	01110205 (0225)
10	สลักเกลียว M 20X350 มม. BOLT, MACHINE, M 20X350 mm	3	01110300
11	สลักห่วงโอแวล M 16X150 มม. BOLT, OVAL EYE, M 16X150 mm	3	01150000 (0257)
12	แหวนสี่เหลี่ยมแบน 52X52X4.5 มม. รู ø 18 มม. มอก. 258 WASHER, SQUARE, FLAT 52X52X4.5 mm, HOLE ø 18 mm, TIS 258	47	01180100 (0355)
13	แหวนสี่เหลี่ยมแบน 62X62X6 มม. รู ø 22 มม. มอก. 258 WASHER, SQUARE, FLAT 62X62X6 mm, HOLE ø 22 mm, TIS 258	6	01180101 (0356)
14	แหวนสปริง M 16 มอก. 259 WASHER, LOCK, M 16, TIS 259	3	01180301 (0365)
15	ท่อเหล็ก ขนาด 20 มม. หนา 2.65 มม. ยาว 100 มม. มอก. 277 ประเภท 2 PIPE, IRON, DIA. 20 mm I.D., 2.65 mm THICKNESS, 100 mm LONG, TIS 277, TYPE 2	3	01050000 (0905)
D-17C	การประกอบลูกถ้วยแขวน SUSPENSION INSULATOR ASSEMBLY	3	
D-5A	การต่อสายล่อฟ้า OVERHEAD GROUND WIRE CONNECTION	1	
D-10A	ฐานรากเสา POLE FOUNDATION	1	

กองวิศวกรรมไฟฟ้าและเครื่องกล
ฝ่ายวิศวกรรม

ผู้เขียน สมหวง.
ผู้สำรวจ
วิศวกร
หัวหน้าแผนก
ผู้อำนวยการกอง
ผู้อำนวยการฝ่าย

รองผู้ว่าการฝ่ายเทคนิค

การไฟฟ้าส่วนภูมิภาค

ผู้ว่าการ

2537

115 kV วงจรเดี่ยว สายไฟฟ้าคู่
เสาต้นทางตรง ก่อนเสาต้นเข้าปลายสาย
แบบ **SD-TG-6**

115 kV SINGLE CIRCUIT DOUBLE CONDUCTOR
TANGENT STRUCTURE ADJACENT TO DEADEND POLE
TYPE **SD-TG-6**

ใช้แทนแบบ
ถูกแทนโดยแบบ
เขียนเสร็จวันที่ 15 ธค. 2536
แก้แบบวันที่
มิติเป็น
มาตราส่วน

แบบเลขที่ SAI-015/36006
แผ่นที่ 3 จากจำนวน 3 แผ่น