
การประกอบเลขที่	2718 A
ASSEMBLY NO.	3713 A

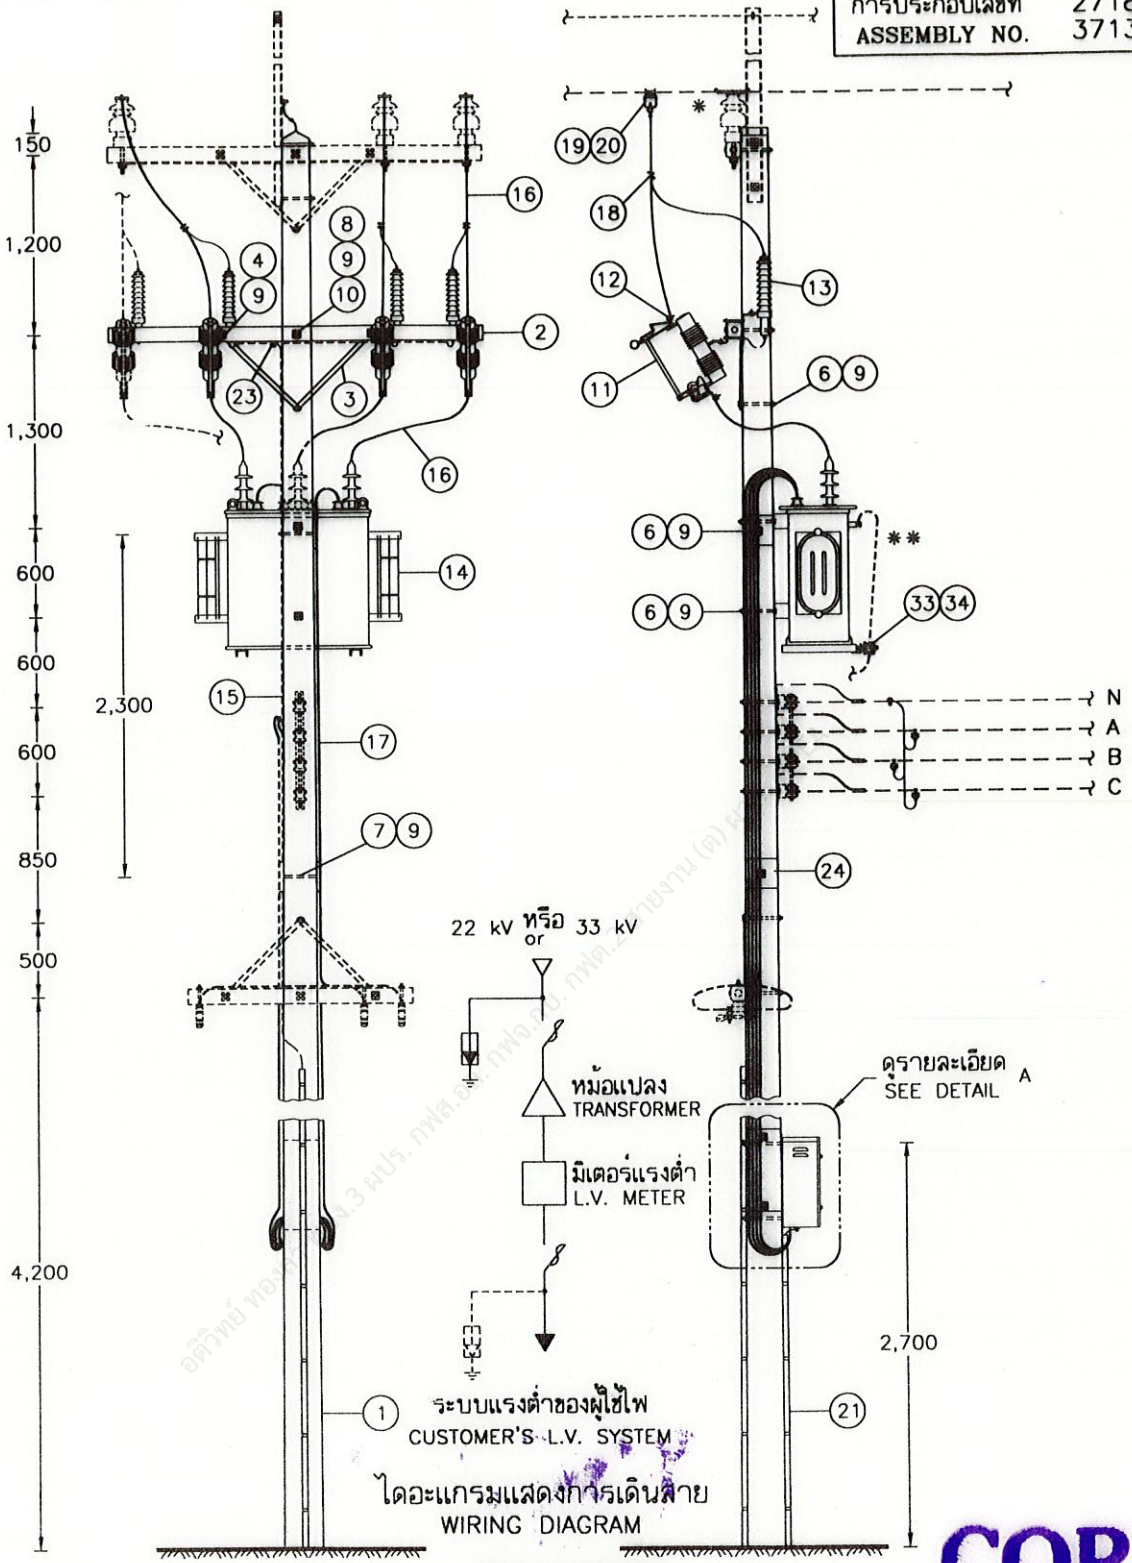


ไดอะแกรมแสดงการเดินสาย
WIRING DIAGRAM

I คอนแบบธรรมดา
CROSSARM TYPE

COPY

กองมาตรฐานระบบไฟฟ้า ฝ่ายมาตรฐานและความปลอดภัย	การไฟฟ้าส่วนภูมิภาค	ใช้แทนแบบ ..... ถูกแทนโดยแบบ .....
ผู้เขียน Supphakit Boonreung ผู้สำรวจ ..... วิศวกร ..... หัวหน้าแผนก ..... ผู้อำนวยการกอง ..... ผู้อำนวยการฝ่าย	ผู้ว่าการ ..... แทน การติดตั้งหม้อแปลง ขนาด 50 kVA 3 เฟส 22-33 kV สำหรับผู้ใช้ไฟเฉพาะราย พร้อมมิเตอร์ 3 เฟส 4 สาย 380/220 โวลต์ 30(100) แอมป์ หรือ TOU มิเตอร์ 3 เฟส 4 สาย 380/220 โวลต์ 10(100) แอมป์	เขียนเสร็จวันที่ 10 ก.ค. 2545 แก้แบบวันที่ ..... มิติเป็น มิลลิเมตร มาตราส่วน 1 : 50
รองผู้ว่าการวางแผน และพัฒนาระบบไฟฟ้า	50 kVA, 3-ø, 22-33 kV TRANSFORMER INSTALLATION FOR SPOT LOAD CUSTOMERS WITH 30(100) A, 380/220 V, 3-ø, 4-W WATTHOUR METER OR 10(100) A, 380/220 V, 3-ø, 4-W, TOU METER	แบบเลขที่ SA2-015/45013 แผ่นที่ 1 ของจำนวน 9 แผ่น

การประกอบเลขที่ ASSEMBLY NO.	2718 A 3713 A

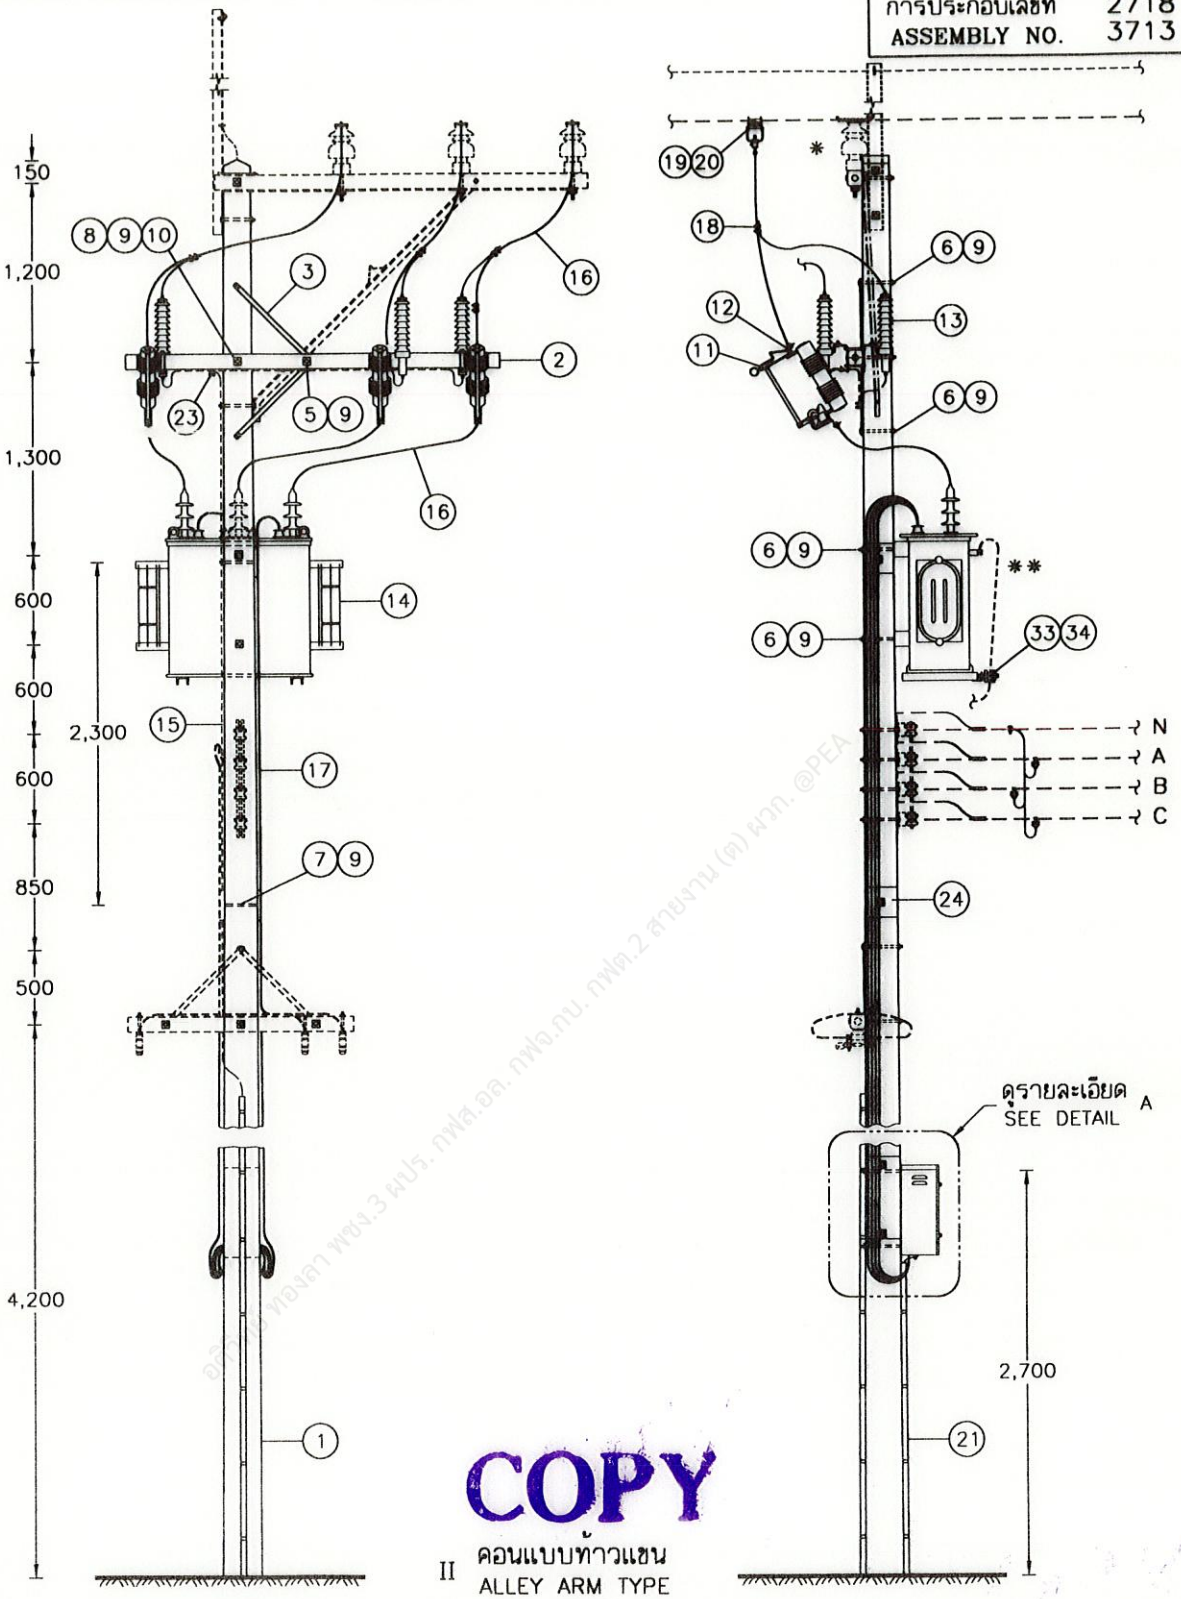


COPY

II คอนแบบท้าวแขน
ALLEY ARM TYPE


กองมาตรฐานระบบไฟฟ้า ฝ่ายมาตรฐานและความปลอดภัย	การไฟฟ้าส่วนภูมิภาค	ใช้แทนแบบ ..... ถูกแทนโดยแบบ .....
ผู้เขียน Supphakit Boonreung ผู้สำรวจ ..... วิศวกร ..... หัวหน้าแผนก ..... ผู้อำนวยการกอง ..... ผู้อำนวยการฝ่าย	ผู้ว่าการ ..... การติดตั้งหม้อแปลง ขนาด 50 kVA 3 เฟส 22-33 kV สำหรับผู้ใช้ไฟเฉพาะราย พร้อมมิเตอร์ 3 เฟส 4 สาย 380/220 โวลต์ 30(100) แอมป์ TOU มิเตอร์ 3 เฟส 4 สาย 380/220 โวลต์ 10(100) แอมป์	เขียนเสร็จวันที่ 10 ก.ค. 2545 แก้แบบวันที่ ..... มิติเป็น มิลลิเมตร มาตราส่วน 1 : 50
รองผู้ว่าการวางแผน และพัฒนาระบบไฟฟ้า	50 kVA, 3-ø, 22-33 kV TRANSFORMER INSTALLATION FOR SPOT LOAD CUSTOMERS WITH 30(100) A, 380/220 V, 3-ø, 4-W WATTHOUR METER OR 10(100) A, 380/220 V, 3-ø, 4-W, TOU METER	แบบเลขที่ SA2-015/45013 แผ่นที่ 2 ของจำนวน 9 แผ่น

การประกอบเลขที่	2718 A
ASSEMBLY NO.	3713 A

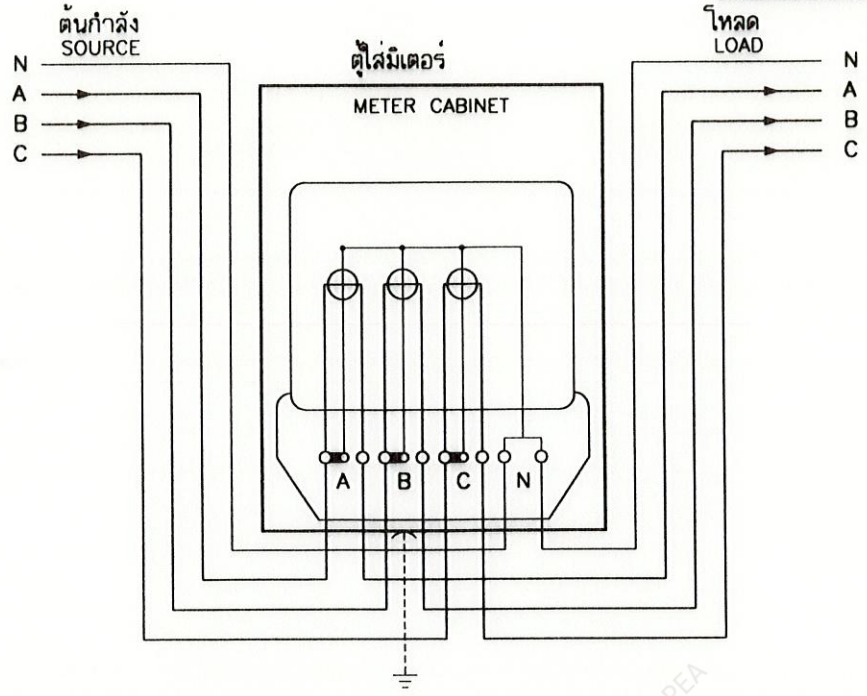

ไดอะแกรมแสดงการต่อวัตต์อาวร์มิเตอร์และ TOU มิเตอร์ (แบบต่อตรง) 3 เฟส 4 สาย

CONNECTION DIAGRAM FOR 3-PHASE 4-WIRE WATTHOUR AND TOU (DIRECT CONNECTED) METER

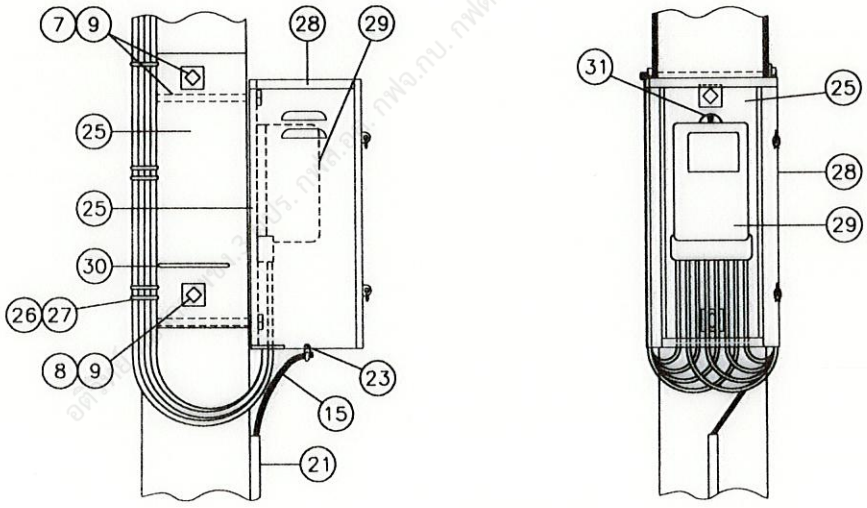



รายละเอียด A
DETAIL

COPY


กองมาตรฐานระบบไฟฟ้า ฝ่ายมาตรฐานและความปลอดภัย	การไฟฟ้าส่วนภูมิภาค	ใช้แทนแบบ ..... ถูกแทนโดยแบบ .....
ผู้เขียน Supphakit Boonreung ผู้สำรวจ ..... วิศวกร ..... หัวหน้าแผนก ..... ผู้อำนวยการกอง ..... ผู้อำนวยการฝ่าย	ผู้ว่าการ	เขียนเสร็จวันที่ 10 ก.ค. 2545 แก้แบบวันที่ ..... มิติเป็น ..... มาตราส่วน .....
รองผู้ว่าการวางแผนและพัฒนาระบบไฟฟ้า	การติดตั้งหม้อแปลง ขนาด 50 kVA 3 เฟส 22-33 kV สำหรับผู้ใช้ไฟเฉพาะราย พร้อมมิเตอร์ 3 เฟส 4 สาย 380/220 โวลต์ 30(100) แอมป์ TOU มิเตอร์ 3 เฟส 4 สาย 380/220 โวลต์ 10(100) แอมป์ 50 kVA, 3-ø, 22-33 kV TRANSFORMER INSTALLATION FOR SPOT LOAD CUSTOMERS WITH 30(100) A, 380/220 V, 3-ø, 4-W WATTHOUR METER OR 10(100) A, 380/220 V, 3-ø, 4-W, TOU METER	แบบเลขที่ SA2-015/45013 แผ่นที่ 3 ของจำนวน 9 แผ่น

การประกอบเลขที่	2718 A
ASSEMBLY NO.	3713 A

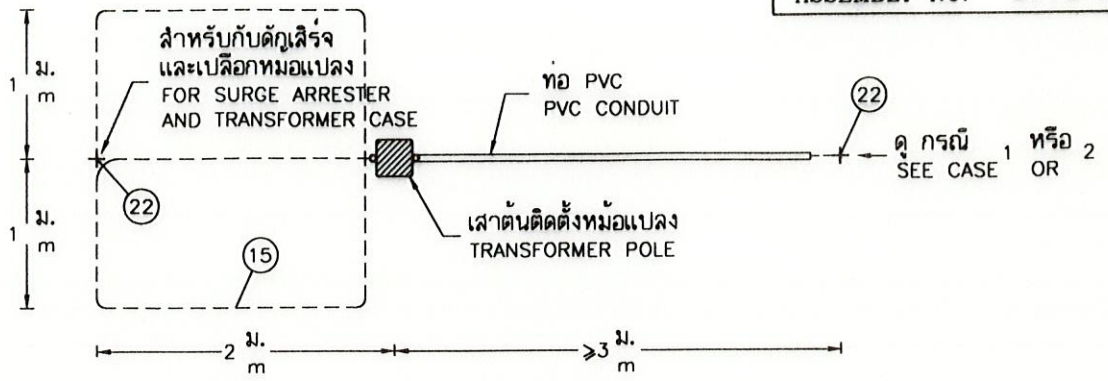

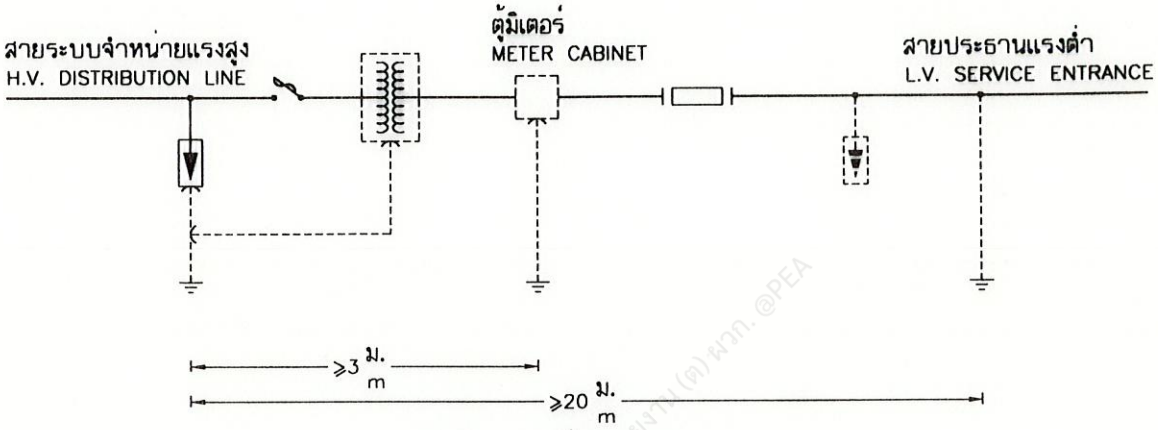

กรณี 1 (ที่แนะนำ)
CASE 1 (PREFERABLY METHOD)

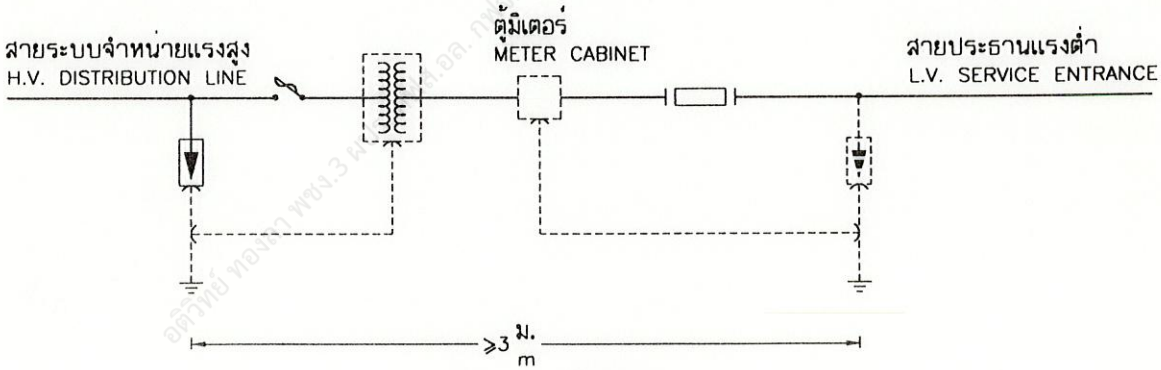

กรณี 2 (เผื่อเลือก)
CASE 2 (ALTERNATIVE)

ไดอะแกรม แสดงการต่อลงดิน
EARTHING DIAGRAM

COPY

กองมาตรฐานระบบไฟฟ้า ฝ่ายมาตรฐานและความปลอดภัย	การไฟฟ้าส่วนภูมิภาค	ใช้แทนแบบ ..... ถูกแทนโดยแบบ .....
ผู้เขียน Supphakit Boonrueng ผู้สำรวจ ..... วิศวกร ..... หัวหน้าแผนก ..... ผู้อำนวยการกอง ..... ผู้อำนวยการฝ่าย	ผู้ว่าการ ..... การติดตั้งหม้อแปลง ขนาด 50 kVA 3 เฟส 22-33 kV สำหรับผู้ใช้ไฟเฉพาะราย พร้อมมิเตอร์ 3 เฟส 4 สาย 380/220 โวลต์ 30(100) แอมป์ TOU มิเตอร์ 3 เฟส 4 สาย 380/220 โวลต์ 10(100) แอมป์	เขียนเสร็จวันที่ 10 ก.ค. 2545 แก้แบบวันที่ ..... มิติเป็น ..... มาตราส่วน .....
รองผู้ว่าการวางแผน และพัฒนาระบบไฟฟ้า	50 kVA, 3-ø, 22-33 kV TRANSFORMER INSTALLATION FOR SPOT LOAD CUSTOMERS WITH 30(100) A, 380/220 V, 3-ø, 4-W WATTHOUR METER OR 10(100) A, 380/220 V, 3-ø, 4-W, TOU METER	แบบเลขที่ SA2-015/45013 แผ่นที่ 4 ของจำนวน 9 แผ่น

การประกอบเลขที่	2718 A
ASSEMBLY NO.	3713 A

บัญชีวัสดุ
BILL OF MATERIAL

ลำดับที่ ITEM	รายละเอียด DESCRIPTION	จำนวน REQ'D I	จำนวน REQ'D II	วัสดุเลขที่ MAT. NO.
1	เสาคอนกรีต 12 ม. หรือ 12.20 ม. POLE, CONCRETE, 12 m OR 12.20 m LONG	1	1	00010004 or 00010012
2	คอน คอร. สปัน ขนาด 100x100x2,500 มม. สำหรับระบบ 22 kV CROSSARM, SPUN, PRESTRESSED, CONCRETE 100x100x2,500 mm ; FOR 22 kV SYSTEM	1	1	00110001
	คอน คอร. สปัน ขนาด 120x120x3,000 มม. สำหรับระบบ 33 kV CROSSARM, SPUN, PRESTRESSED, CONCRETE 120x120x3,000 mm ; FOR 33 kV SYSTEM			00110002
3	เหล็กประกับคอน ขนาด 30x6x760 มม. สำหรับระบบ 22 kV BRACE, FLAT, FOR CROSSARM 30x6x760 mm ; FOR 22 kV SYSTEM	2	2	01200001
	เหล็กประกับคอน ขนาด 40x6x1,000 มม. สำหรับระบบ 33 kV BRACE, FLAT, FOR CROSSARM 40x6x1,000 mm ; FOR 33 kV SYSTEM			01200002
4	สลักเกลียว M 16x130 มม. สำหรับระบบ 22 kV BOLT, MACHINE, M 16x130 mm ; FOR 22 kV SYSTEM	2	–	01110200
	สลักเกลียว M 16x170 มม. สำหรับระบบ 33 kV BOLT, MACHINE, M 16x170 mm ; FOR 33 kV SYSTEM			01110201
5	สลักเกลียว M 16x170 มม. BOLT, MACHINE, M 16x170 mm	–	1	01110201
6	สลักเกลียว M 16x250 มม. สำหรับเสาคอนกรีต 12 ม. BOLT, MACHINE, M 16x250 mm ; FOR 12 m CONCRETE POLE	4	5	01110203
	สลักเกลียว M 16x300 มม. สำหรับเสาคอนกรีต 12.20 ม. BOLT, MACHINE, M 16x300 mm ; FOR 12.20 m CONCRETE POLE			01110204
7	สลักเกลียว M 16x300 มม. สำหรับเสาคอนกรีต 12 ม. BOLT, MACHINE, M 16x300 mm ; FOR 12 m CONCRETE POLE	3	3	01110204
	สลักเกลียว M 16x350 มม. สำหรับเสาคอนกรีต 12.20 ม. BOLT, MACHINE, M 16x350 mm ; FOR 12.20 m CONCRETE POLE			01110205
8	สลักเกลียว M 16x350 มม. BOLT, MACHINE, M 16x350 mm	2	2	01110205
9	แหวนสี่เหลี่ยมแบน 52x52x4.5 มม. รู Ø 18 มม. มอก. 258 WASHER, SQUARE, FLAT, 52x52x4.5 mm, HOLE ø 18 mm, TIS 258	20	15	01180100
10	แหวนสปริง M 16 มอก. 259 WASHER, LOCK, M 16 TIS 259	1	1	01180301
11	ดรอพเอาต์ ฟิวส์คัตเอาต์ หนึ่งอินซูเลเตอร์ 22 kV 100 A CUT-OUT, FUSE, OPEN TYPE, SINGLE INSULATOR, DROPOUT, 22 kV, 100 A	3	3	04010000
	ดรอพเอาต์ ฟิวส์คัตเอาต์ หนึ่งอินซูเลเตอร์ 33 kV 100 A CUT-OUT, FUSE, OPEN TYPE, SINGLE INSULATOR, DROPOUT, 33 kV, 100 A			04010100
12	สลักต่อปลายสายเข้าอุปกรณ์ไฟฟ้าสำหรับสายอะลูมิเนียม PIN TERMINAL, FOR Al CONDUCTOR	6	6	02420400

COPY

กองมาตรฐานระบบไฟฟ้า ฝ่ายมาตรฐานและความปลอดภัย	การไฟฟ้าส่วนภูมิภาค	ใช้แทนแบบ ..... ถูกแทนโดยแบบ .....
ผู้เขียน Supphakit Boonreung ผู้สำรวจ ..... วิศวกร ..... หัวหน้าแผนก ..... ผู้อำนวยการกอง ..... ผู้อำนวยการฝ่าย	ผู้ว่าการ ..... แทน	เขียนเสร็จวันที่ 10 ก.ค. 2545 แก้แบบวันที่ ..... มิติเป็น ..... มาตราส่วน .....
รองผู้ว่าการวางแผนและพัฒนาระบบไฟฟ้า	การติดตั้งหม้อแปลง ขนาด 50 kVA 3 เฟส 22-33 kV สำหรับผู้ใช้ไฟเฉพาะราย พร้อมมิเตอร์ 3 เฟส 4 สาย 380/220 โวลต์ 30(100) แอมป์ TOU มิเตอร์ 3 เฟส 4 สาย 380/220 โวลต์ 10(100) แอมป์ 50 kVA, 3-ø, 22-33 kV TRANSFORMER INSTALLATION FOR SPOT LOAD CUSTOMERS WITH 30(100) A, 380/220 V, 3-ø, 4-W WATTHOUR METER OR 10(100) A, 380/220 V, 3-ø, 4-W, TOU METER	แบบเลขที่ SA2-015/45013 แผ่นที่ 5 ของจำนวน 9 แผ่น

การประกอบเลขที่ 2718 A
ASSEMBLY NO. 3713 A

บัญชีวัสดุ
BILL OF MATERIAL

ลำดับที่ ITEM	รายละเอียด DESCRIPTION	จำนวน REQ'D I	จำนวน REQ'D II	วัสดุเลขที่ MAT. NO.
13	กับดักเสิร์จ 20–21 kV 5 kA สำหรับระบบ 22 kV SURGE ARRESTER, 20–21 kV, 5 kA ; FOR 22 kV SYSTEM	3	3	04000000
	กับดักเสิร์จ 30 kV 5 kA สำหรับระบบ 33 kV SURGE ARRESTER, 30 kV, 5 kA ; FOR 33 kV SYSTEM			04000100
14	หม้อแปลง 50 kVA 3 เฟส 22–0.40/0.23 kV สำหรับระบบ 22 kV TRANSFORMER 50 kVA, 3–ø, 22–0.40/0.23 kV ; FOR 22 kV SYSTEM	1	1	05010005
	หม้อแปลง 50 kVA 3 เฟส 33–0.40/0.23 kV สำหรับระบบ 33 kV TRANSFORMER 50 kVA, 3–ø, 33–0.40/0.23 kV ; FOR 33 kV SYSTEM			05010102
15	ลวดเหล็กตีเกลียว 50/7 ต.มม. พร้อมอุปกรณ์ยึด (การประกอบเลขที่ 9703, 9703A) WIRE, STEEL STRANDED, 50/7 mm² COMP.WITH FIXING ACCESS (ASS.No. 9703, 9703A)	26 ม. m	26 ม. m	01100004
16	สายอะลูมิเนียมหุ้มฉนวน PVC 750 V มอก.293 หรือ PIC หรือเคเบิลอากาศ 22–33 kV ขนาด 50 ต.มม. CABLE, Al, PVC INSULATED, 750 V, TIS 293 OR PIC OR CABLE AERIAL, 22–33 kV 50 mm²	15 ม. m	15 ม. m	02070002 หรือ or 02060001 02050000 02050100
17	สายอะลูมิเนียมหรือสายทองแดงหุ้มฉนวน PVC 750 V 75°C มอก.293 หรือ มอก.11 CABLE, Al OR Cu, PVC INSULATED, 750 V, 75°C, TIS 293 OR TIS 11	ม. m	ม. m	02070002 หรือ or 02080609
18	พี.จี. คอนเนคเตอร์ สลักคู่ สำหรับสายอะลูมิเนียม 25–95 ต.มม. CONNECTOR, PARALLEL GROOVE, DOUBLE BOLT, Al, 25–95 mm²	3	3	02300102
19	ฮอทไลน์แคล้มป์ สายประธานอะลูมิเนียม 25–50 ต.มม. สายแยกอะลูมิเนียม 25–50 ต.มม. HOT LINE CLAMP, MAIN LINE, Al 25–50 mm², TAP LINE, Al 25–50 mm²	3	3	02330100
20	สเตอร์รัพแคล้มป์ หรือเบลแคล้มป์ ขนาดตามต้องการ CLAMP, STIRRUP OR BAIL CLAMP, SIZE AS REQUIRED	3	3	02330000–1
21	ท่อ พีวีซี.แข็ง ขนาด Ø20 มม. มอก. 216 พร้อมอุปกรณ์ยึด (การประกอบเลขที่ 9704, 9704 A) CONDUIT, PVC RIGID, ø20 mm, TIS 216 COMP.WITH FIXING ACCESS (ASS.No.9704, 9704A)	2	2	08040002
22	หลักดิน 60x60x5 มม. ยาว 2 ม. ROD, GROUND 60x60x5 mm, 2 m LONG	2	2	01220002
23	ยูแคล้มป์ สลัก 1 ตัว M 8 (ไวร์โรป คลิพ) CLAMP, SINGLE U–BOLT, M 8 (WIRE ROPE CLIP)	4	4	01230000
24	แป้นไม้ สำหรับยึดสายไฟ ขนาด 20x20x2 ซ.ม. CABLE PLATE, HARD WOOD, SURFACE FINISHED, 20x20x2 cm	3	3	06100000
25	แป้นไม้ รองรับมิเตอร์ใสแล้ว ขนาด 20x60x2 ซ.ม. METER PLATE, HARD WOOD, SURFACE FINISHED, 20x60x2 cm	3	3	06100001
26	เข็มขัดรัดสาย (ทำด้วยอะลูมิเนียมแบน 1x10 มม.) ช่วงระยะ 25 ซ.ม. CABLE STRAP, (MADE OF ARMOUR TAPE 1x10 mm), AT 25 cm INTERVALS	ม. m	ม. m	02200000
27	ตะปูหัวกลมแบน ยาว 15–20 มม. Ø 1.00 มม. มอก. 113 NAIL, ROUND MILD STEEL WIRE, 15–20 mm LONG, ø 1.00 mm, TIS 133	24	24	–
28	ตู้อะลูมิเนียมใช้นอกอาคาร สำหรับมิเตอร์ 3 เฟส CABINET, ALUMINIUM, OUTDOOR, FOR 3–PHASE WATTHOUR METER	1	1	06100006

COPY

กองมาตรฐานระบบไฟฟ้า
ฝ่ายมาตรฐานและความปลอดภัย

ผู้เขียน Supphakit Boonreung
ผู้สำรวจ.....
วิศวกร.....
หัวหน้าแผนก.....
ผู้อำนวยการกอง.....
ผู้อำนวยการฝ่าย.....

รองผู้ว่าการวางแผนและพัฒนาระบบไฟฟ้า
.....

การไฟฟ้าส่วนภูมิภาค

ผู้ว่าการ.....

การติดตั้งหม้อแปลง ขนาด 50 kVA 3 เฟส 22–33 kV
สำหรับผู้ใช้ไฟเฉพาะราย
พร้อมมิเตอร์ 3 เฟส 4 สาย 380/220 โวลต์ 30(100) แอมป์
TOU มิเตอร์ 3 เฟส 4 สาย 380/220 โวลต์ 10(100) แอมป์

50 kVA, 3–ø, 22–33 kV TRANSFORMER INSTALLATION
FOR SPOT LOAD CUSTOMERS
WITH 30(100) A, 380/220 V, 3–ø, 4–W WATTHOUR METER
OR 10(100) A, 380/220 V, 3–ø, 4–W, TOU METER

ใช้แทนแบบ .....
ถูกแทนโดยแบบ .....
เขียนเสร็จวันที่ 10 ก.ค. 2545
แก้แบบวันที่ .....
มิติเป็น.....
มาตราส่วน.....

แบบเลขที่ SA2–015/45013
แผ่นที่ 6 ของจำนวน 9 แผ่น

การประกอบเลขที่	2718 A
ASSEMBLY NO.	3713 A

บัญชีวัสดุ
BILL OF MATERIAL

ลำดับที่ ITEM	รายละเอียด DESCRIPTION	จำนวน REQ'D I	จำนวน REQ'D II	วัสดุเลขที่ MAT. NO.
29	วัตต์อาวร์มิเตอร์ 3 เฟส 4 สาย 380/220 โวลท์ 30(100) แอมป์ METER, WATTHOUR, 3-PHASE, 4-WIRE, 380/220 V, 30(100) A	1	1	06000108
	ทีโอยูมิเตอร์ 3 เฟส 4 สาย 380/220 โวลท์ 10(100) แอมป์ แบบต่อตรง METER, TOU, 3-PHASE, 4-WIRE, 380/220 V, 10(100) A, DIRECT CONNECTED			06000509
30	หมายเลขผู้ใช้ไฟ NUMBER OF CUSTOMERS	1	1	–
31	ตะปูเกลียวชุบโครเมียม ยาว 20 มม. SCREW, CHROME PLATED, 20 mm LONG	3	3	–
32				
บัญชีวัสดุสำหรับหม้อแปลงที่ขั้วต่อสายแรงต่ำอยู่ด้านข้างหม้อแปลงเท่านั้น (ดูหมายเหตุ 2 ประกอบ) BILL OF MATERIAL FOR L.V. BUSHINGS ARE ON THE SIDE OF TRANSFORMER TANK ONLY (SEE NOTE 2)				
33	เหล็กจับขอบถังหม้อแปลง สำหรับยึดสายแรงต่ำ ดูหมายเหตุข้อ 2 BRACKET, STEEL, FOR TRANSFORMER SECONDARY LEAD ; SEE NOTE 2	4	4	05100003
34	ลูกรอกแรงต่ำ มอก. 227 แบบ ข. (แบบ 53-2) INSULATOR, SPOOL TYPE, L.V., TIS 227 TYPE B (CLASS 53-2)	4	4	03030000

COPY

กองมาตรฐานระบบไฟฟ้า ฝ่ายมาตรฐานและความปลอดภัย	การไฟฟ้าส่วนภูมิภาค	ใช้แทนแบบ ..... ถูกแทนโดยแบบ .....
ผู้เขียน Supphakit Boonreung ผู้สำรวจ ..... วิศวกร ..... หัวหน้าแผนก ..... ผู้อำนวยการกอง ..... ผู้อำนวยการฝ่าย	ผู้ว่าการ ..... การติดตั้งหม้อแปลง ขนาด 50 kVA 3 เฟส 22-33 kV สำหรับผู้ใช้ไฟเฉพาะราย พร้อมมิเตอร์ 3 เฟส 4 สาย 380/220 โวลต์ 30(100) แอมป์ TOU มิเตอร์ 3 เฟส 4 สาย 380/220 โวลต์ 10(100) แอมป์	เขียนเสร็จวันที่ 10 ก.ค. 2545 แก้แบบวันที่ ..... มิติเป็น ..... มาตราส่วน .....
รองผู้ว่าการวางแผน และพัฒนาระบบไฟฟ้า	50 kVA, 3-ø, 22-33 kV TRANSFORMER INSTALLATION FOR SPOT LOAD CUSTOMERS WITH 30(100) A, 380/220 V, 3-ø, 4-W WATTHOUR METER OR 10(100) A, 380/220 V, 3-ø, 4-W, TOU METER	แบบเลขที่ SA2-015/45013 แผ่นที่ 7 ของจำนวน 9 แผ่น

การประกอบเลขที่ ASSEMBLY NO.	2718 A 3713 A

ลำดับที่ ITEM	แบบอ้างอิง PEFERENCE DRAWING	แบบเลขที่ DWG. No.	การประกอบเลขที่ ASSEMBLY No.
1	การประกอบคอน คอร. สปัน กับเสาคอนกรีต ระบบ 22 kV, 33 kV SPUN PRESTRESSED CONCRETE CROSSARM ASSENBLY 22 kV, 33 kV SYSTEM	SA1-015/21015 SA1-015/21021	2802 3803
2	การประกอบคอน คอร. สปัน แบบท้าวแขนกับเสาคอนกรีต ระบบ 22 kV, 33 kV SPUN PRESTRESSED CONCRETE ALLEY ARM ASSEMBLY 22 kV, 33 kV SYSTEM	SA1-015/21016 SA1-015/21022	2803 3804
3	การประกอบคอน คอร. สปัน กับเสาคอนกรีต ระบบ 11-22 kV, 33 kV สำหรับเข้าปลายสาย SPUN PRESTRESSED CONCRETE CROSSARM ASSEMBLY 11-22 kV, 33 kV SYSTEM DEADEND STRUCTURE	SA1-015/24014 SA1-015/24017	2806 3807
4	การติดตั้งอุปกรณ์ที่เสาเข้าปลายสายแบบท้าวแขน ระบบ 22 kV, 33 kV DEADEND CONSTRUCTION ON ALLEY ARM 22kV, 33 kV SYSTEM	SA1-015/27025 SA1-015/21068	2814 3212 A
5	การติดตั้งมิเตอร์แรงต่ำ 3 เฟส 4 สาย 3-PHASE 4-WIRE L.T. METER INSTALLATION	SA1-015/23056	0522
6	มาตรฐานระยะห่างที่ปลอดภัยในการก่อสร้างทางไฟฟ้า STANDARD MINIMUM SAFE CLEARANCES FOR ELECTRICAL CONSTRUCTION	S02-015/17068	9301
7	การต่อลงดินระบบแรงสูงและแรงต่ำสำหรับอุปกรณ์ในระบบจำหน่าย และสายระบบจำหน่าย H.T. AND L.T. EARTHING SYSTEM FOR DISTRIBUTION EQUIPMENT AND DISTRIBUTION LINE	S02-015/20039	9701
8	การประกอบสายลงดิน วิธียึดลวดเหล็ก GROUND LEAD ASSEMBLY STEEL WIRE FITTING	S02-015/19166 SA1-015/31012	9703 9703 A
9	การประกอบที่ยึดท่อ PVC สำหรับสายดิน PVC PIPE FITTING AS ASSEMBLY FOR GROUND WIRE	S02-015/19128 SA1-015/31013	9704 9704 A
10	ฐานรากเสาต้นหม้อแปลง TRANSFORMER POLE FOUNDATION	SA1-015/32016	8234
11	การต่อสายแรงต่ำออกจากหม้อแปลง SECONDARY LEAD FROM TRANSFORMER	SA1-015/22011	0603

COPY

กองมาตรฐานระบบไฟฟ้า ฝ่ายมาตรฐานและความปลอดภัย	การไฟฟ้าส่วนภูมิภาค	ใช้แทนแบบ ..... ถูกแทนโดยแบบ .....
ผู้เขียน Supphakit Boonreung ผู้สำรวจ ..... วิศวกร ..... หัวหน้าแผนก ..... ผู้อำนวยการกอง ..... ผู้อำนวยการฝ่าย	ผู้ว่าการ ..... การติดตั้งหม้อแปลง ขนาด 50 kVA 3 เฟส 22-33 kV สำหรับผู้ใช้ไฟเฉพาะราย พร้อมมิเตอร์ 3 เฟส 4 สาย 380/220 โวลต์ 30(100) แอมป์ TOU มิเตอร์ 3 เฟส 4 สาย 380/220 โวลต์ 10(100) แอมป์	เขียนเสร็จวันที่ 10 ก.ค. 2545 แก้แบบวันที่ ..... มิติเป็น ..... มาตราส่วน .....
รองผู้ว่าการวางแผน และพัฒนาระบบไฟฟ้า	50 kVA, 3-ø, 22-33 kV TRANSFORMER INSTALLATION FOR SPOT LOAD CUSTOMERS WITH 30(100) A, 380/220 V, 3-ø, 4-W WATTHOUR METER OR 10(100) A, 380/220 V, 3-ø, 4-W, TOU METER	แบบเลขที่ SA2-015/45013 แผ่นที่ 8 ของจำนวน 9 แผ่น

การประกอบเลขที่	2718 A
ASSEMBLY NO.	3713 A

หมายเหตุ ;

1. * กรณีต้องการพาดสายแรงสูง แบบเข้าปลายสายด้วยลูกถ้วยแขวน ให้ดูรายละเอียดในแบบอ้างอิงลำดับที่ 3, 4 (ควรเป็นเสาต้นไม่รับแรงดึง และไม่มีสายยึดโยง)
2. ** กรณีขั้วต่อสายแรงต่ำอยู่ด้านข้างหม้อแปลง ให้ลดจำนวนวัสดุลำดับที่ 6, 9, 24 ในบัญชีวัสดุลงอย่างละ 1 อัน
3. ฟิวส์สวิตช์แรงต่ำที่เสาต้นหม้อแปลงไม่จำเป็นต้องมีถ้าหากการพาดสายไปยังแผงสวิตช์มีระยะสั้น ๆ และสามารถป้องกันสายไฟฟ้ามิให้ชำรุดเนื่องจากทางกลได้
4. ในกรณีที่ต้องการใช้ดีมานด์มิเตอร์ (แบบสะสม) ให้ติดตั้งตามแบบเลขที่ SA1-015/32017 (การประกอบเลขที่ 2718) หรือ แบบเลขที่ SA1-015/33008 (การประกอบเลขที่ 3713)
5. การต่อสาย TOU มิเตอร์ (แบบต่อตรง) ตามแผนผังนี้ ใช้สำหรับผลิตภัณฑ์ของ ISKRA เท่านั้น ส่วนการต่อสายเข้ามิเตอร์อื่น ๆ ให้ดูตามแผนผังที่แนบมากับมิเตอร์ นั้น ๆ

NOTES ;

1. * IN CASE OF H.V. DEAD END STRUCTURE, USING SUSPENSION INSULATOR, SEE DETAIL IN REFERENCE DRAWING ON ITEM 3, 4 . (IT SHOULD BE SLACK SPAN AND NO GUY.)
2. ** IN CASE OF L.V. BUSHINGS ARE ON THE SIDE OF TRANSFORMER TANK, THE REQ'D OF ITEM 7, 10, 25, IN THE BILL OF MATERIAL MUST SHALL BE REDUCED BY 1 .
3. L.V. FUSE-SWITCH AT TRANSFORMER POLE MAY BE OMITTED, IF THE WIRING DISTANCE TO MAIN SWITCHBOARD IS SHORT AND THE CONDUCTORS ARE PROTECTED SUITABLY FROM MECHANICAL DAMAGE .
4. IN CASE OF USING CUMULATIVE DEMAND METER, IT SHALL BE INSTALLED ACCORDING TO DWG No. SA1-015/32017 (ASSEMBLY No. 2718) OR DWG. No. SA1-015/33008 (ASSEMBLY No. 3713) .
5. THE CONNECTION DIAGRAM OF TOU METER (DIRECT CONNECTED) ARE ONLY METERS MANUFACTURED BY ISKRA, FOR CONNECTION DIAGRAM OF ANY TYPE SEE DIAGRAM ATTACHES TO THE METER .

COPY

กองมาตรฐานระบบไฟฟ้า ฝ่ายมาตรฐานและความปลอดภัย	การไฟฟ้าส่วนภูมิภาค	ใช้แทนแบบ ..... ถูกแทนโดยแบบ .....
ผู้เขียน Supphakit Boonruang ผู้สำรวจ ..... วิศวกร ..... หัวหน้าแผนก ..... ผู้อำนวยการกอง ..... ผู้อำนวยการฝ่าย	ผู้ว่าการ	เขียนเสร็จวันที่ 10 ก.ค. 2545 แก้แบบวันที่ ..... มิติเป็น ..... มาตราส่วน .....
รองผู้ว่าการวางแผนและพัฒนาระบบไฟฟ้า	การติดตั้งหม้อแปลง ขนาด 50 kVA 3 เฟส 22-33 kV สำหรับผู้ใช้ไฟเฉพาะราย พร้อมมิเตอร์ 3 เฟส 4 สาย 380/220 โวลท์ 30(100) แอมป์ TOU มิเตอร์ 3 เฟส 4 สาย 380/220 โวลท์ 10(100) แอมป์ 50 kVA, 3-ø, 22-33 kV TRANSFORMER INSTALLATION FOR SPOT LOAD CUSTOMERS WITH 30(100) A, 380/220 V, 3-ø, 4-W WATTHOUR METER OR 10(100) A, 380/220 V, 3-ø, 4-W, TOU METER	แบบเลขที่ SA2-015/45013 แผ่นที่ 9 ของจำนวน 9 แผ่น