การประกอบเลขที่ 0515
ASSEMBLY NO. 0515

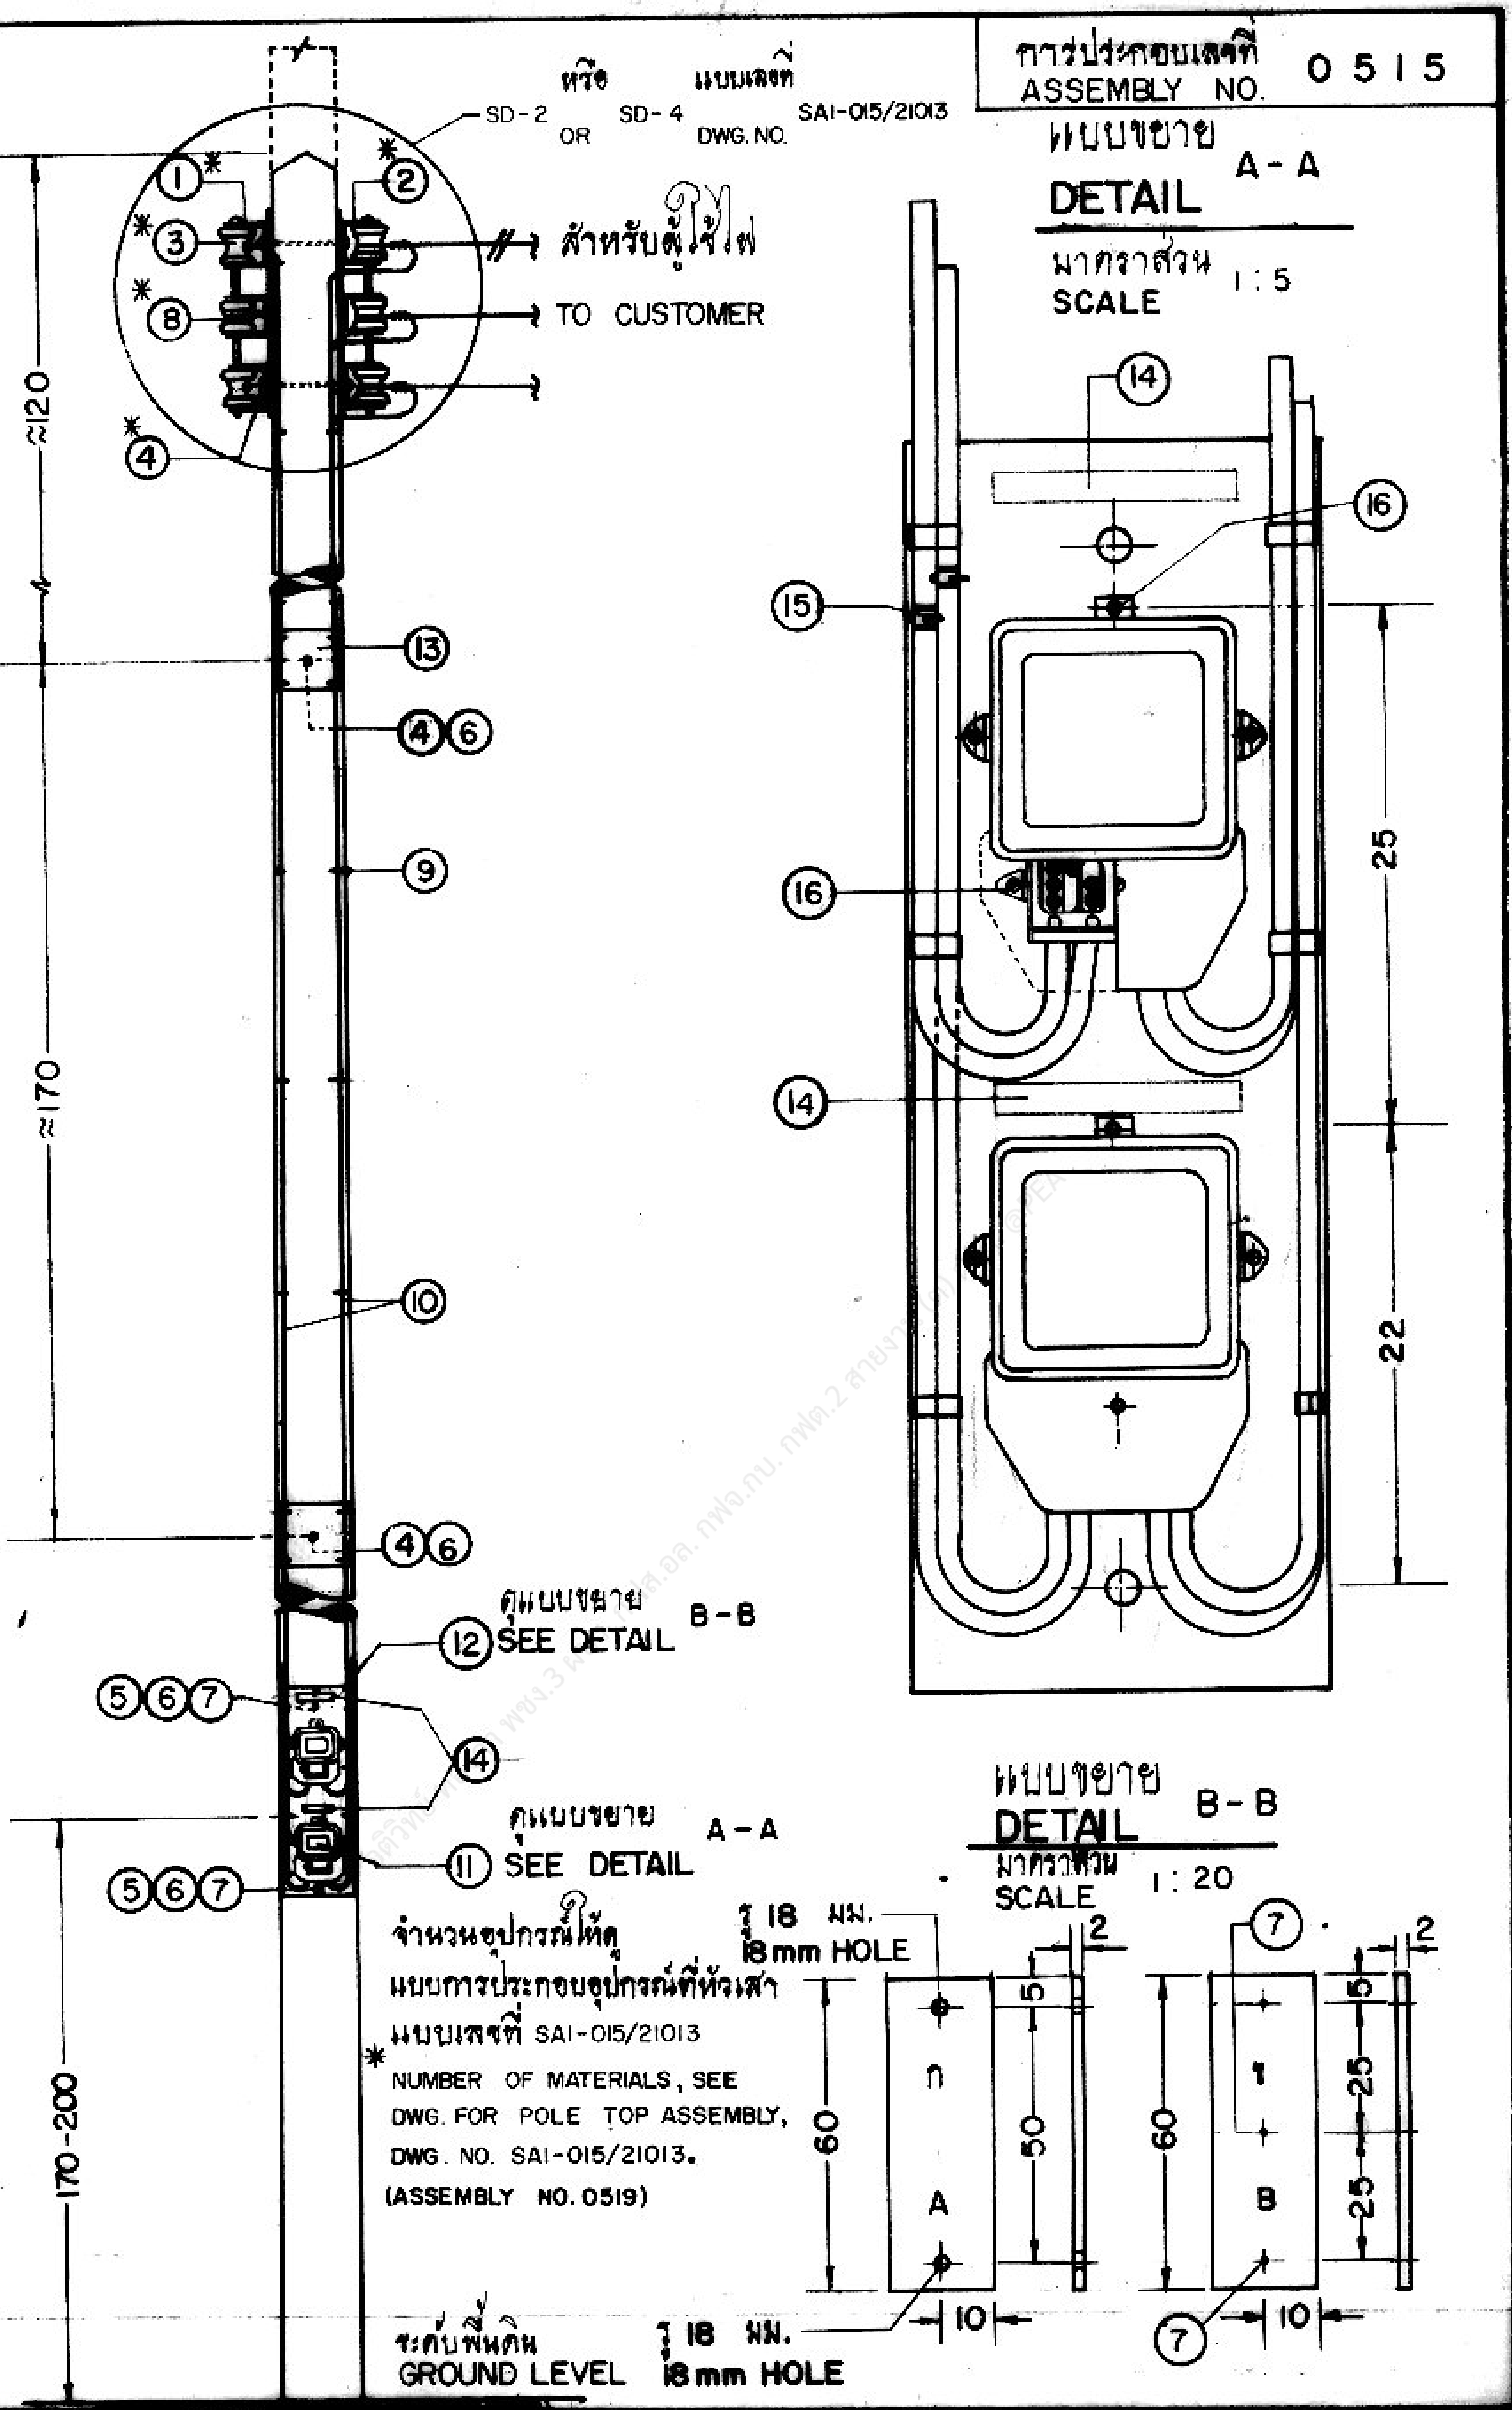

จำนวนอุปกรณ์ให้ดู
แบบการประกอบอุปกรณ์ที่หัวเสา
แบบเลขที่ SAI-015/21013

* NUMBER OF MATERIALS, SEE DWG. FOR POLE TOP ASSEMBLY, DWG. NO. SAI-015/21013.
(ASSEMBLY NO. 0519)

กองวิศวกรรมและวางแผน	การไฟฟ้าส่วนภูมิภาค	ใช้แทนแบบ ISI-11002/1 OF 2 ถูกแทนโดยแบบ
ผู้เขียน สถาปนิก วิศวกร หัวหน้าแผนก ผู้อำนวยการกอง	ผู้ว่าการ	เขียนเสร็จวันที่ 13 ม.ค. 15 แก้แบบวันที่ 17 กค. 21 มิติเป็น ซม. มาตราส่วน
	การติดตั้งมิเตอร์ 1 เฟส สำหรับมิเตอร์ 2 ตัว ขนาด 3-5 แอมแปร์	
รองผู้ว่าการฝ่ายเทคนิค	1-Ø METER INSTALLATION FOR 2 METERS RATING 3-5 AMPERES	แบบเลขที่ I50-015/150002 แผ่นที่ 1 ของจำนวน 2 แผ่น

การประกอบเลขที่
ASSEMBLY NO. 0515

บัญชีวัสดุ
BILL OF MATERIAL

ลำดับที่ ITEM	รายละเอียด DESCRIPTION	จำนวน REQ'D ก/A	จำนวน REQ'D ข/B	วัสดุเลขที่ MAT. NO.
1	แร็คตามต้องการ RACK, SECONDARY, AS REQUIRED	–	–	03130000-2
2	แร็คสำหรับต่อเข้าบ้านผู้ใช้ไฟตามต้องการ RACK, SECONDARY, TO CUSTOMER AS REQUIRED	–	–	03130000-2
3	ลูกรอกแรงต่ำ มอก. 227 แบบ ข (แบบ 53-2) INSULATOR, SPOOL TYPE, L.T. TIS 227 TYPE B (CLASS 53-2)	–	–	03030000
4	สลักเกลียวหัวเหลี่ยม M 16X200มม. พร้อมนัทเหลี่ยม BOLT, MACHINE M 16 X200 mm COMPLETE WITH SQUARE NUT	2	-	01110202
5	สลักเกลียวหัวเหลี่ยม M 16X250มม. พร้อมนัทเหลี่ยม BOLT, MACHINE M 16 X 250 mm COMPLETE WITH SQUARE NUT	1	-	01110203
6	แหวนเหลี่ยมแบนหนา 52 X 52 X 4.5 มม. รู Ø 18 มม. มอก. 258 WASHER, SQUARE FLAT, 52 X 52 X 4.5 mm, HOLE Ø 18 mm, TIS 258	8	-	01180100
7	ตะปูเหล็กหัวกลมแบน ยาว 60 มม. Ø 2.80 มม. มอก. 113 NAIL, ROUND MILD STEEL WIRE 60 mm LONG Ø 2.80 mm TIS 113	-	3	
8	คอนเนคเตอร์สำหรับสายอะลูมิเนียมกับสายอะลูมิเนียมพันด้วย PVC เทป, หุ้มด้วยคอมเปาด์ CONNEC. Al TO Al WRAPPED WITH PVC TAPE & COATED WITH INSUL.COM.	–	–	02300100-1 and 02180001
9	เข็มขัดรัดสายไฟ ช่วงระยะ 50 ซม. STRAP, CABLE, AT 50 cm INTERVALS			
10	สายอะลูมิเนียมหุ้มฉนวนเข้ามิเตอร์แรงต่ำ 0.6/1 kV CONDUCTOR, NAYY OR NAY 0.6/1 kV, Al	ม. m	ม. m	02070100-1
11	วัตต์อาวร์มิเตอร์ 1 เฟส METER, WATTHOUR 1-Ø WITH EXTENDED TERMINAL COVER	2	2	06000000-1
12	แป้นไม้รองรับมิเตอร์ไสแล้ว ขนาด 60X20X2ซม. METER PLATE (HARD WOOD) SURFACE FINISHED, SIZE 60X20X2cm	1	1	
13	แป้นไม้สำหรับยึดสายเข้าและออก จากมิเตอร์ไสแล้ว ขนาด 20X20X2 ซม. CABLE PLATE (HARD WOOD) SURFACE FINISHED, SIZE 20X20X2 cm	2	-	
14	หมายเลขผู้ใช้ไฟ NUMBER OF CUSTOMER	2	2	
15	พีจี.คอนเนคเตอร์สลักเดี่ยว สำหรับสายอะลูมิเนียมกับสายอะลูมิเนียมพันด้วย PVCเทป CONNECTOR, Al TO Al WRAPPED WITH PVC TAPE	2	2	02300201 to 02180001
16	ตะปูเกลียวขนาด 25 มม. SCREW, WOOD, SIZE 25 mm	6	6	

หมายเหตุ

1. ก. สำหรับเสาคอนกรีตแรงต่ำ และ ข. สำหรับเสาไม้แรงต่ำ
2. บัญชีวัสดุใช้เฉพาะการติดตั้งมิเตอร์แรงต่ำเท่านั้น ส่วนการประกอบอุปกรณ์ที่หัวเสาดูแบบเลขที่ SAI-015/21013
3. สำหรับการติดตั้งบนเสาคอนกรีตแรงสูง 12 ม.ให้ใช้บัญชีวัสดุของเสาคอนกรีตแรงต่ำแต่ให้เพิ่มความยาวของสลักเกลียวอีก 50 มม.

NOTES

1. A. FOR L.T. CONCRETE POLE & B. FOR L.T. WOOD POLE.
2. BILL OF MATERIALS USE ONLY FOR L.T. METER INSTALLATION, SEE DWG. FOR POLE TOP ASSEMBLY, DWG. NO. SAI-015/21013. (ASSEMBLY NO. 0519)
3. FOR INSTALLATION ON 12 m H.T. CONCRETE POLE, USE BILL OF MATERIAL FOR L.T. CONCRETE POLE BUT ADD 50 mm TO THE LENGTH OF MACHINE BOLT.

กองวิศวกรรมและวางแผน	การไฟฟ้าส่วนภูมิภาค	ใช้แทนแบบ I51-11002/20F2 ถูกแทนโดยแบบ
ผู้เขียน สถาปนิก วิศวกร หัวหน้าแผนก ผู้อำนวยการกอง	ผู้ว่าการ	เขียนเสร็จวันที่ 13 ม.ค. 15 แก้แบบวันที่ 17 กค. 21 มิติเป็น มาตราส่วน
	การติดตั้งมิเตอร์ 1 เฟส สำหรับมิเตอร์ 2 ตัว ขนาด 3-5 แอมแปร์	
รองผู้ว่าการฝ่ายเทคนิค	1Ø METER INSTALLATION FOR 2 METERS RATING 3-5 AMPERES	แบบเลขที่ I50/015/160002 แผ่นที่ 2 ของจำนวน 2 แผ่น

25 มี.ค. 2515