การประกอบเลขที่ ASSEMBLY NO. **5356**

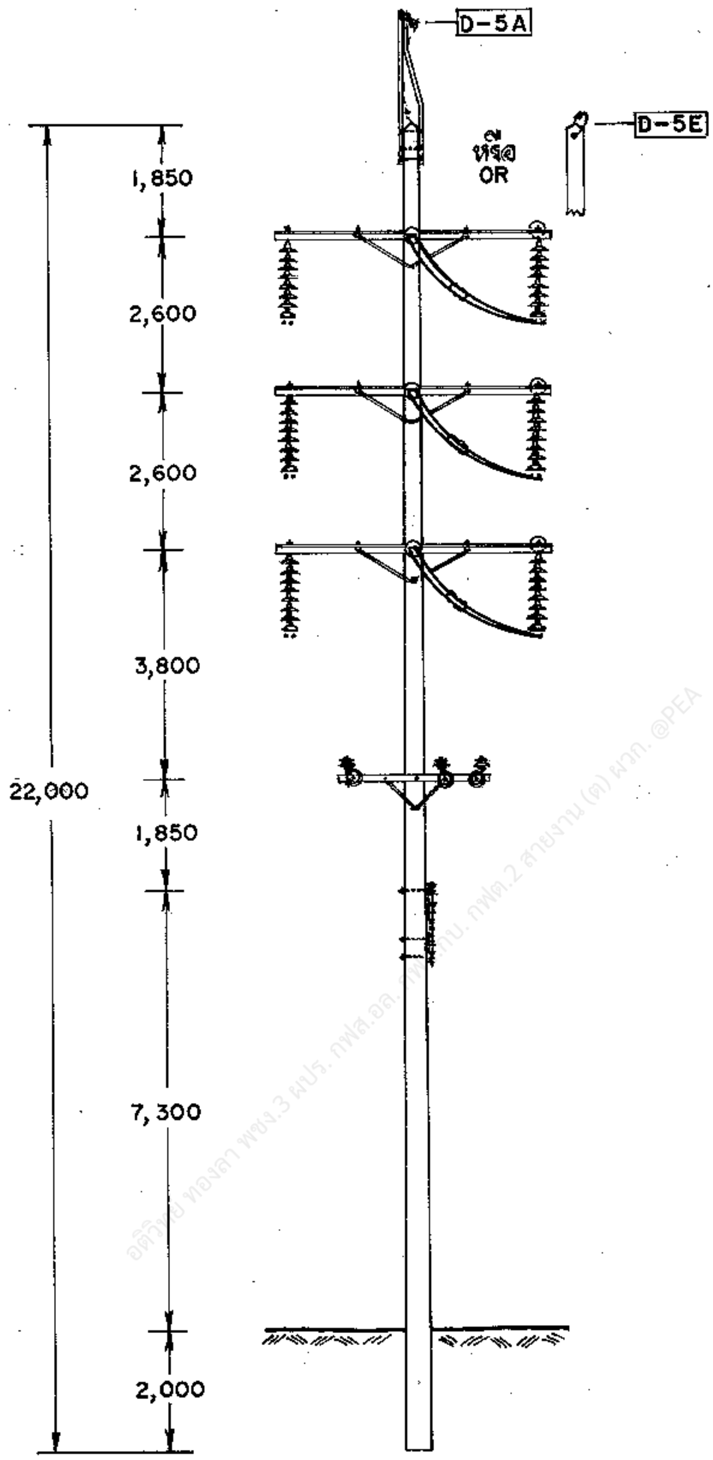

อดิวิทย์ ทองลา พชง.3 ผปร. กฟส.อล. [illegible] กฟต.2 สายงาน (ต) ผวก. @PEA

กองวิศวกรรมไฟฟ้าและเครื่องกล
ฝ่ายวิศวกรรม

ผู้เขียน [illegible]
ผู้ตรวจ ______
วิศวกร ______
หัวหน้าแผนก ______
ผู้อำนวยการกอง ______
ผู้อำนวยการฝ่าย ______
รองผู้ว่าการฝ่ายเทคนิค

การไฟฟ้าส่วนภูมิภาค

ผู้ว่าการ 22 ก.ค. 2535 (แทน)

115 kV วงจรคู่ สายไฟฟ้าคู่
โครงสร้างเสาปลายสายสองข้าง ก่อนเสาข้างทางโค้ง
แบบ DD-AS-2

115 kV DOUBLE CIRCUIT DOUBLE CONDUCTOR
DOUBLE DEADEND STRUCTURE ADJACENT POLE TO ANGLE
TYPE DD-AS-2

ใช้แทนแบบ ______
ถูกแทนโดยแบบ ______
เขียนเสร็จวันที่ 13 ก.ค. 35
แก้แบบวันที่ ______
มิติเป็น มิลลิเมตร
มาตราส่วน 1 : 125
แบบเลขที่ SAI-015/35024
แผ่นที่ 1 ของจำนวน 4 แผ่น

21 ก.ค. 2535

การประกอบเลขที่ 5356
ASSEMBLY NO.

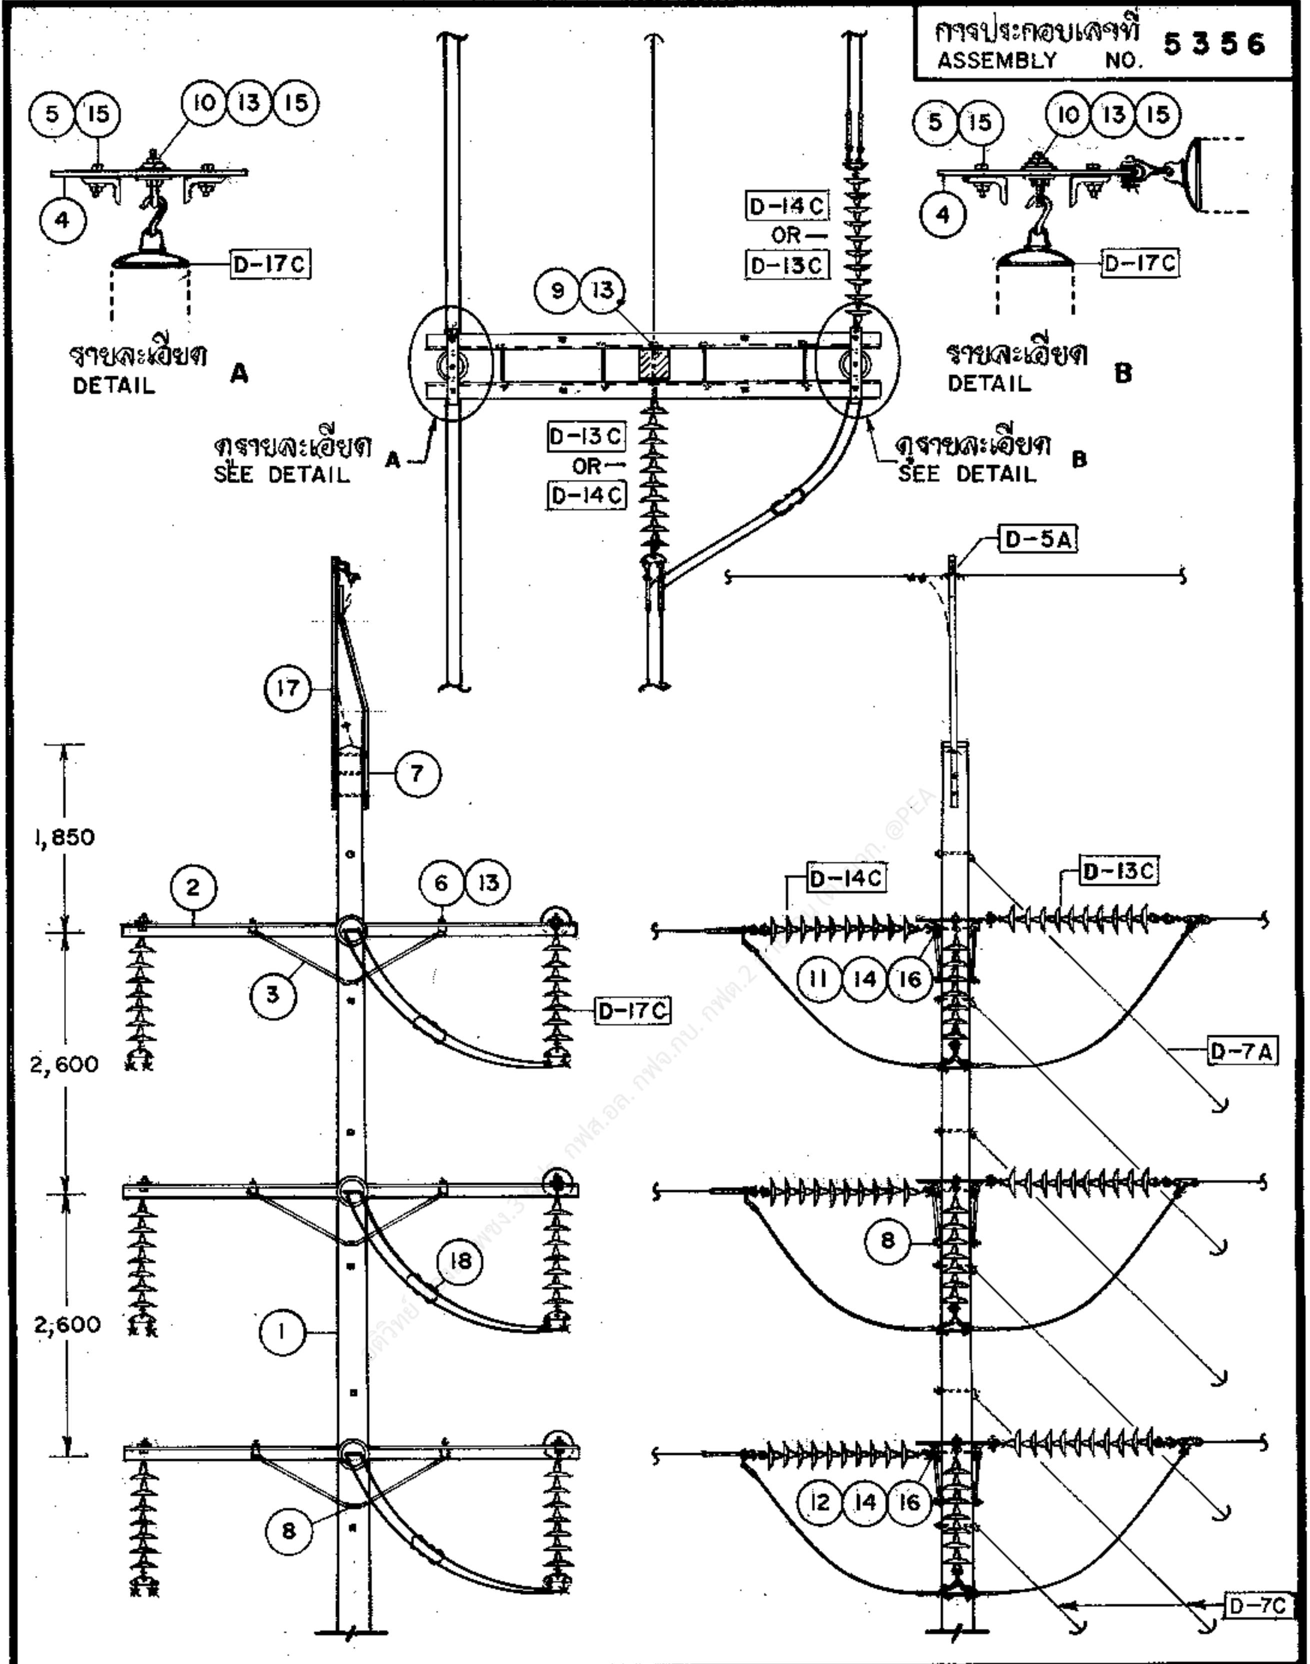

กองวิศวกรรมไฟฟ้าและเครื่องกล
ฝ่ายวิศวกรรม

ผู้เขียน สมหวง.
ผู้ตรวจ
วิศวกร
หัวหน้าแผนก
ผู้อำนวยการกอง
ผู้อำนวยการฝ่าย

รองผู้ว่าการฝ่ายเทคนิค

21 ก.ค. 2535

การไฟฟ้าส่วนภูมิภาค

ผู้ว่าการ 22 ก.ค. 2535 (ลงนาม)

115 kV วงจรคู่ สายไฟฟ้าคู่
โครงสร้างเสาเข้าปลายสายสองข้าง ก่อนเสาช่วงทางโค้ง
แบบ DD-AS-2

115 kV DOUBLE CIRCUIT DOUBLE CONDUCTOR
DOUBLE DEADEND STRUCTURE ADJACENT POLE TO ANGLE
TYPE DD-AS-2

ใช้แทนแบบ
ถูกแทนโดยแบบ
เขียนเสร็จวันที่ 13 ก.ค. 35
แก้แบบวันที่ 15 ก.ย. 40
มิติเป็น มิลลิเมตร
มาตราส่วน 1 : 75

แบบเลขที่ SAI-015/35024
แผ่นที่ 2 ของจำนวน 4 แผ่น

การประกอบเลขที่
ASSEMBLY NO. **5356**

บัญชีวัสดุ
BILL OF MATERIAL

ลำดับที่ ITEM	รายละเอียด DESCRIPTION	จำนวน REQ'D	วัสดุเลขที่ MAT. NO.
1	เสาคอนกรีต 22 ม. POLE, CONCRETE 22 m LONG	1	00010011 (0041)
2	คอนสายแบบเหล็กฉาก ขนาด 150X100X12 มม. ยาว 4.50 ม. CROSSARM, STEEL ANGLE 150X100X12 mm, 4.50 m LONG	6	00120002 (6001)
3	เหล็กฉากรับคอนสาย ขนาด 50X50X6 มม. ช่วงกว้าง 1,800 มม. ดรอพ 450 มม. BRACE, ANGLE STEEL, 50X50X6 mm, 1,800 mm WIDE, 450 mm DROP	6	01200007 (0119)
4	เหล็กแผ่นยึดสองปลาย ขนาด 12X100X650 มม. PLATE, STEEL, DOUBLE ARMING 12X100X650 mm	6	01030100 (0145)
5	สลักเกลียว M 16X75 มม. พร้อมแหวนกลม 2 อัน BOLT, MACHINE, M 16X75 mm, COMPLETE WITH 2 ROUND WASHERS	12	01110400 (0236)
6	สลักเกลียว M 16X170 มม. BOLT, MACHINE, M 16X170 mm	12	01110201 (0221)
7	สลักเกลียว M 16X300 มม. BOLT, MACHINE, M 16X300 mm	3	01110204 (0224)
8	สลักเกลียว M 16X350 มม. BOLT, MACHINE, M 16X350 mm	3	01110205 (0225)
9	สลักเกลียวตลอด M 16X450 มม. BOLT, DOUBLE ARMING, M 16X450 mm	12	01120001 (0244)
10	สลักห่วงโอแวล M 16X150 มม. (เพิ่มน๊อตอีกหนึ่งอัน) BOLT, OVAL EYE M 16X150 mm (ADD ONE SQUARE NUT)	6	01150000 (0257)
11	สลักห่วงโอแวล M 20X350 มม. BOLT, OVAL EYE M 20X350 mm	2	01150100 (0260)
12	สลักห่วงโอแวล M 20X450 มม. BOLT, OVAL EYE M 20X450 mm	1	01150101 (0261)
13	แหวนสี่เหลี่ยมแบน 52X52X4.5 มม. รู ø 18 มม. มอก. 258 WASHER, SQUARE, FLAT 52X52X4.5 mm HOLE ø 18 mm TIS 258	69	01180100 (0355)
14	แหวนสี่เหลี่ยมแบน 62X62X6 มม. รู ø 22 มม. มอก. 258 WASHER, SQUARE, FLAT 62X62X6 mm HOLE ø 22 mm TIS 258	6	01180101 (0356)
15	แหวนสปริง M 16 มอก. 259 WASHER, LOCK, M 16, TIS 259	18	01180301 (0365)
16	แหวนสปริง M 20 มอก. 259 WASHER, LOCK, M 20, TIS 259	3	01180302 (0366)
17	เหล็กฉากรับสายล่อฟ้า ทางโค้ง OVERHEAD GROUND WIRE CORNER BAYONET	1	01010005 (0136)
18	ปรีฟอร์มแยกสาย SPACER, HELICAL ROD, PREFORMED	6	02240000 (0918)

กองวิศวกรรมไฟฟ้าและเครื่องกล ฝ่ายวิศวกรรม	**การไฟฟ้าส่วนภูมิภาค**	ใช้แทนแบบ ________ ถูกแทนโดยแบบ ______
ผู้เขียน สมพ ว. ผู้ตรวจ ________ วิศวกร ________ หัวหน้าแผนก ________ ผู้อำนวยการกอง ________ ผู้อำนวยการฝ่าย ________	ผู้ว่าการ ________ 22 ก.ค. 2535 (แทน) 115 kV วงจรคู่ สายไฟฟ้าคู่ โครงสร้างเสาต้นปลายสายสองข้าง ก่อนเสาข้างทางโค้ง แบบ DD-AS-2	เขียนเสร็จวันที่ 13 ก.ค.35 แก้แบบวันที่ ________ มิติเป็น ________ มาตราส่วน —
รองผู้ว่าการฝ่ายเทคนิค	115 kV DOUBLE CIRCUIT DOUBLE CONDUCTOR DOUBLE DEADEND STRUCTURE ADJACENT POLE TO ANGLE TYPE DD-AS-2	แบบเลขที่ SAI-015/35024 แผ่นที่ 3 ของจำนวน 4 แผ่น

21 ก.ค. 2535

การประกอบเลขที่ ASSEMBLY NO. **5356**

D-13C	การประกอบลูกถ้วยแขวน SUSPENSION INSULATOR ASSEMBLY	3	
D-14C	การประกอบลูกถ้วยแขวน SUSPENSION INSULATOR ASSEMBLY	3	
D-17C	การประกอบลูกถ้วยแขวน SUSPENSION INSULATOR ASSEMBLY	6	
D-5A OR * D-5E	การต่อสายล่อฟ้า OVERHEAD GROUND WIRE CONNECTION	1	
D-7A	การประกอบสายยึดโยงลวดเหล็ก 95 ต.มม. STEEL STRANDED WIRE 95 mm² GUY ASSEMBLY	4	
D-7C	การประกอบสายยึดโยงลวดเหล็ก 95 ต.มม. STEEL STRANDED WIRE 95 mm² GUY ASSEMBLY	2	
D-9B	สมอบกคอนกรีต CONCRETE ANCHOR	1	
D-10A	ฐานรากเสา POLE FOUNDATION	1	

* กรณีใช้ D-5E ให้ตัดรายการ ที่ 7 และ 17 ออก
IN CASE OF USING D-5E, ITEM NO. 7 AND 17 SHALL BE OMITTED .

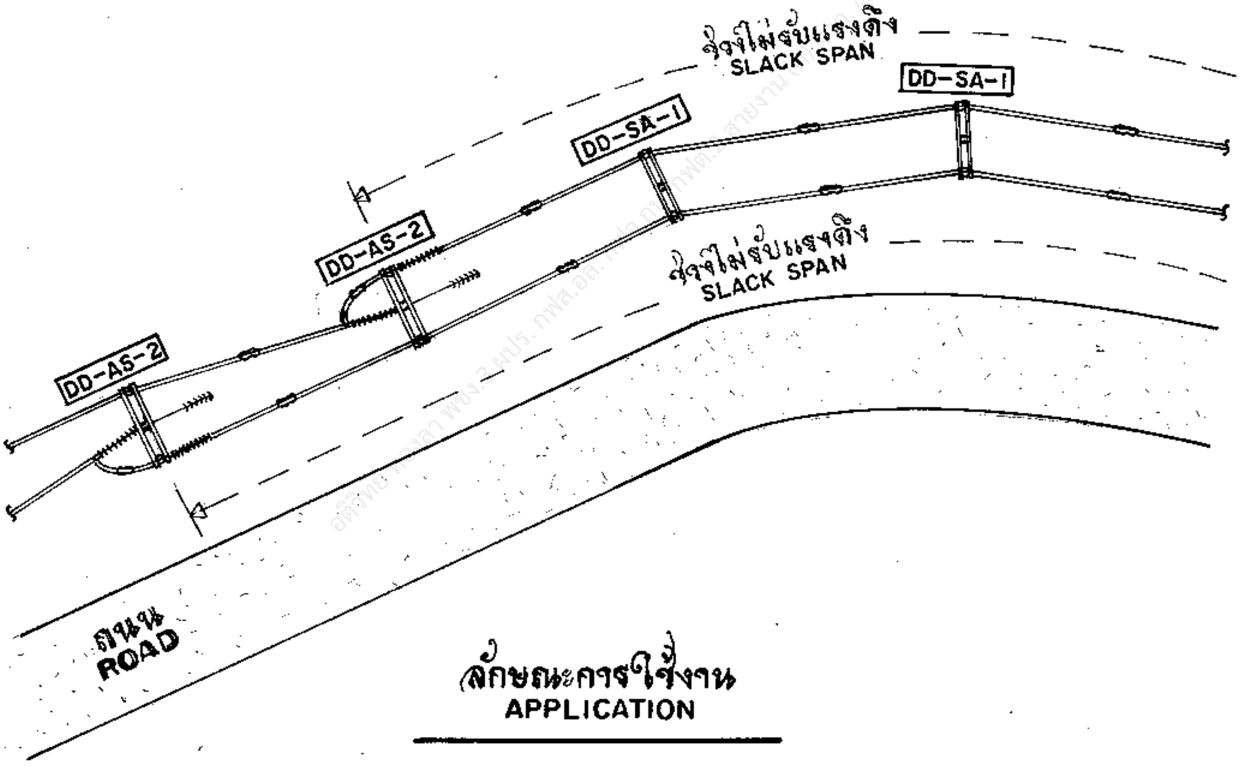

ลักษณะการใช้งาน
APPLICATION

กองวิศวกรรมไฟฟ้าและเครื่องกล ฝ่ายวิศวกรรม	การไฟฟ้าส่วนภูมิภาค	ใช้แทนแบบ ถูกแทนโดยแบบ
ผู้เขียน ผู้สำรวจ วิศวกร หัวหน้าแผนก ผู้อำนวยการกอง ผู้อำนวยการฝ่าย	ผู้ว่าการ 22 ก.ค. 2535	เขียนเสร็จวันที่ 13 ก.ค. 35 แก้แบบวันที่ 15 ก.ย. 40 มิติเป็น — มาตราส่วน
	115 kV วงจรคู่ สายไฟฟ้าคู่ โครงสร้างเสาเข้าปลายสายสองข้าง ก่อนเสาซึ่งทางโค้ง แบบ DD-AS-2	
รองผู้ว่าการฝ่ายเทคนิค	115 kV DOUBLE CIRCUIT DOUBLE CONDUCTOR DOUBLE DEADEND STRUCTURE ADJACENT POLE TO ANGLE TYPE DD -AS-2	แบบเลขที่ SAI-015/35024 แผ่นที่ 4 ของจำนวน 4 แผ่น

21 ก.ค. 2535