การประกอบเลขที่ 5359
ASSEMBLY NO. 5359

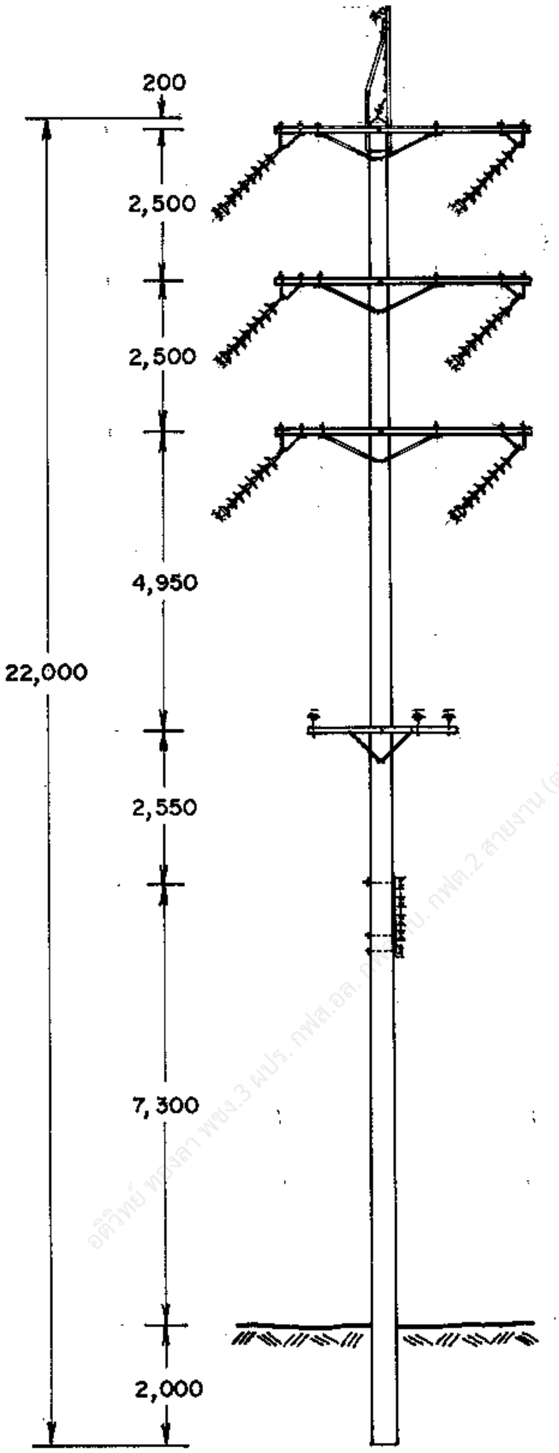

อดิวิทย์ ทองลา พชง.3 ผปร. กฟส.อล. [illegible] กฟฉ.2 สายงาน (ต) ผวก. @PEA

กองวิศวกรรมไฟฟ้าและเครื่องกล ฝ่ายวิศวกรรม	การไฟฟ้าส่วนภูมิภาค	ใช้แทนแบบ ________ ถูกแทนโดยแบบ ________
ผู้เขียน ________ ผู้สำรวจ ________ วิศวกร ________ หัวหน้าแผนก ________ ผู้อำนวยการกอง ________ ผู้อำนวยการฝ่าย ________	ผู้ว่าการ ________ -5 ส.ค. 2537 115 kV วงจรคู่ สายไฟฟ้าคู่ เสาสำหรับต้นทางโค้ง แบบ DD-SA-2	เขียนเสร็จวันที่ 15 ตค. 2536 แก้แบบวันที่ ________ มิติเป็น มิลลิเมตร มาตราส่วน 1 : 125
รองผู้ว่าการฝ่ายเทคนิค	115 kV DOUBLE CIRCUIT DOUBLE CONDUCTOR SMALL ANGLE STRUCTURE TYPE DD-SA-2	แบบเลขที่ SAI-015/36005 แผ่นที่ 1 รวมจำนวน 3 แผ่น

การประกอบเลขที่ **5359**
ASSEMBLY NO.

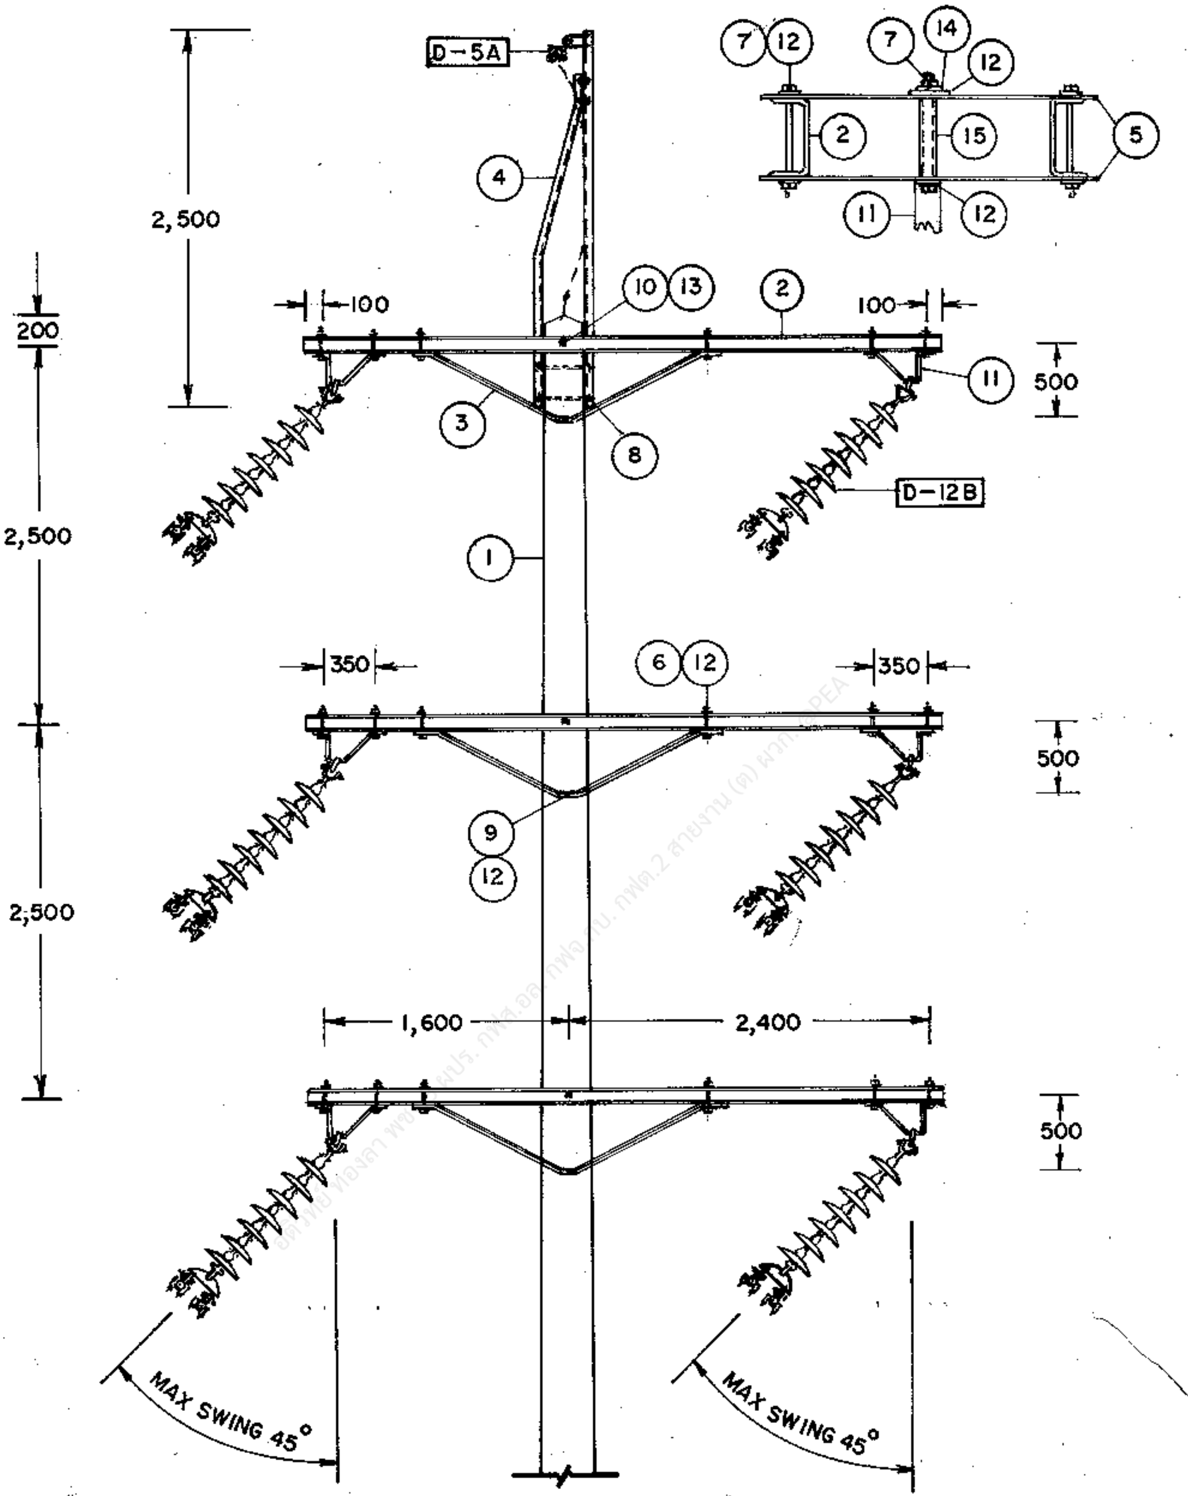

กองวิศวกรรมไฟฟ้าและเครื่องกล ฝ่ายวิศวกรรม	การไฟฟ้าส่วนภูมิภาค	ใช้แทนแบบ ถูกแทนโดยแบบ
ผู้เขียน ผู้สำรวจ วิศวกร หัวหน้าแผนก ผู้อำนวยการกอง ผู้อำนวยการฝ่าย	ผู้ว่าการ 5 ส.ค. 2537	เขียนเสร็จวันที่ 15 ธค. 2536 แก้แบบวันที่
	115 kV วงจรคู่ สายไฟฟ้าคู่ เสาสำหรับต้นทางโค้ง แบบ DD-SA-2	มิติเป็น มิลลิเมตร มาตราส่วน 1 : 50
รองผู้ว่าการฝ่ายเทคนิค	115 kV DOUBLE CIRCUIT DOUBLE CONDUCTOR SMALL ANGLE STRUCTURE TYPE DD-SA-2	แบบเลขที่ SAI-015/36005 แผ่นที่ 2 ของจำนวน 3 แผ่น

27 ธ.ค. 2536

การประกอบเลขที่ 5359
ASSEMBLY NO.

บัญชีวัสดุ
BILL OF MATERIAL

ลำดับที่ ITEM	รายละเอียด DESCRIPTION	จำนวน REQ'D	วัสดุเลขที่ MAT. NO.
1	เสาคอนกรีต 22 ม. POLE, CONCRETE 22 m LONG	1	00010011 (0041)
2	คอนสายแบบเหล็กรูปรางน้ำ ขนาด 100X50X5 มม. ยาว 4.20 ม. มอก. 116 CROSSARM, STEEL, CHANNEL 100X50X5 mm, 4.20 m LONG, TIS 116	6	
3	เหล็กฉากรับคอนสาย ขนาด 50X50X6 มม. ช่วงกว้าง 1,800 มม. ดรอพ 450 มม. BRACE, ANGLE STEEL, 50X50X6 mm, 1,800 mm WIDE, 450 mm DROP	6	01200007 (0119)
4	เหล็กฉากรับสายล่อฟ้าทางโค้ง OVERHEAD GROUND WIRE BAYONET	1	01010005 (0136)
5	เหล็กแผ่น ขนาด 6X100X450 มม. PLATE, STEEL, 6X100X450 mm	24	01030002 (0143)
6	สลักเกลียว M 16X130 มม. BOLT, MACHINE, M 16X130 mm	12	01110200 (0220)
7	สลักเกลียว M 16X170 มม. BOLT, MACHINE, M 16X170 mm	36	01110201 (0221)
8	สลักเกลียว M 16X300 มม. BOLT, MACHINE M 16X300 mm	3	01110204 (0224)
9	สลักเกลียว M 16X350 มม. BOLT, MACHINE M 16X350 mm	3	01110205 (0225)
10	สลักเกลียว M 20X350 มม. BOLT, MACHINE M 20X350 mm	3	01110300
11	ที่แขวนลูกถ้วยทางโค้ง BRACKET, CORNER SUSPENSION	6	03140012 (0489)
12	แหวนสี่เหลี่ยมแบน 52X52X4.5 มม. รู ø 18 มม. มอก. 258 WASHER, SQUARE, FLAT 52X52X4.5 mm, HOLE ø 18 mm, TIS 258	87	01180100 (0355)
13	แหวนสี่เหลี่ยมแบน 62X62X6 มม. รู ø 22 มม. มอก. 258 WASHER, SQUARE, FLAT 62X62X6 mm, HOLE ø 22 mm, TIS 258	6	01180101 (0356)
14	แหวนสปริง M 16 มอก. 259 WASHER, LOCK, M 16, TIS 259	12	01180301 (0365)
15	ท่อเหล็ก ชื่อขนาด 20 มม. หนา 2.65 มม. ยาว 100 มม. มอก. 277 ประเภท 2 PIPE, IRON, DIA. 20 mm I.D., 2.65 mm THICKNESS, 100 mm LONG, TIS 277, TYPE 2	12	01050000 (0905)
D-12B	การประกอบลูกถ้วยแขวน SUSPENSION INSULATOR ASSEMBLY	6	
D-5A	การต่อสายล่อฟ้า OVERHEAD GROUND WIRE CONNECTION	1	
D-10A	ฐานรากเสา POLE FOUNDATION	1	

กองวิศวกรรมไฟฟ้าและเครื่องกล ฝ่ายวิศวกรรม	การไฟฟ้าส่วนภูมิภาค	ใช้แทนแบบ ถูกแทนโดยแบบ เขียนเสร็จวันที่ 15 ธค. 2536 แก้แบบวันที่ มีค่าเป็น มาตราส่วน
ผู้เขียน ผู้สำรวจ วิศวกร หัวหน้าแผนก ผู้อำนวยการกอง ผู้อำนวยการฝ่าย	ผู้ว่าการ 5 ส.ค. 2537 115 kV วงจรคู่ สายไฟฟ้าคู่ เสาสำหรับงานทางโค้ง แบบ DD-SA-2	
รองผู้ว่าการฝ่ายเทคนิค	115 kV DOUBLE CIRCUIT DOUBLE CONDUCTOR SMALL ANGLE STRUCTURE TYPE DD-SA-2	แบบเลขที่ SAI-015/36005 แผ่นที่ 3 ของจำนวน 3 แผ่น