การประกอบเลขที่
ASSEMBLY NO. 3215

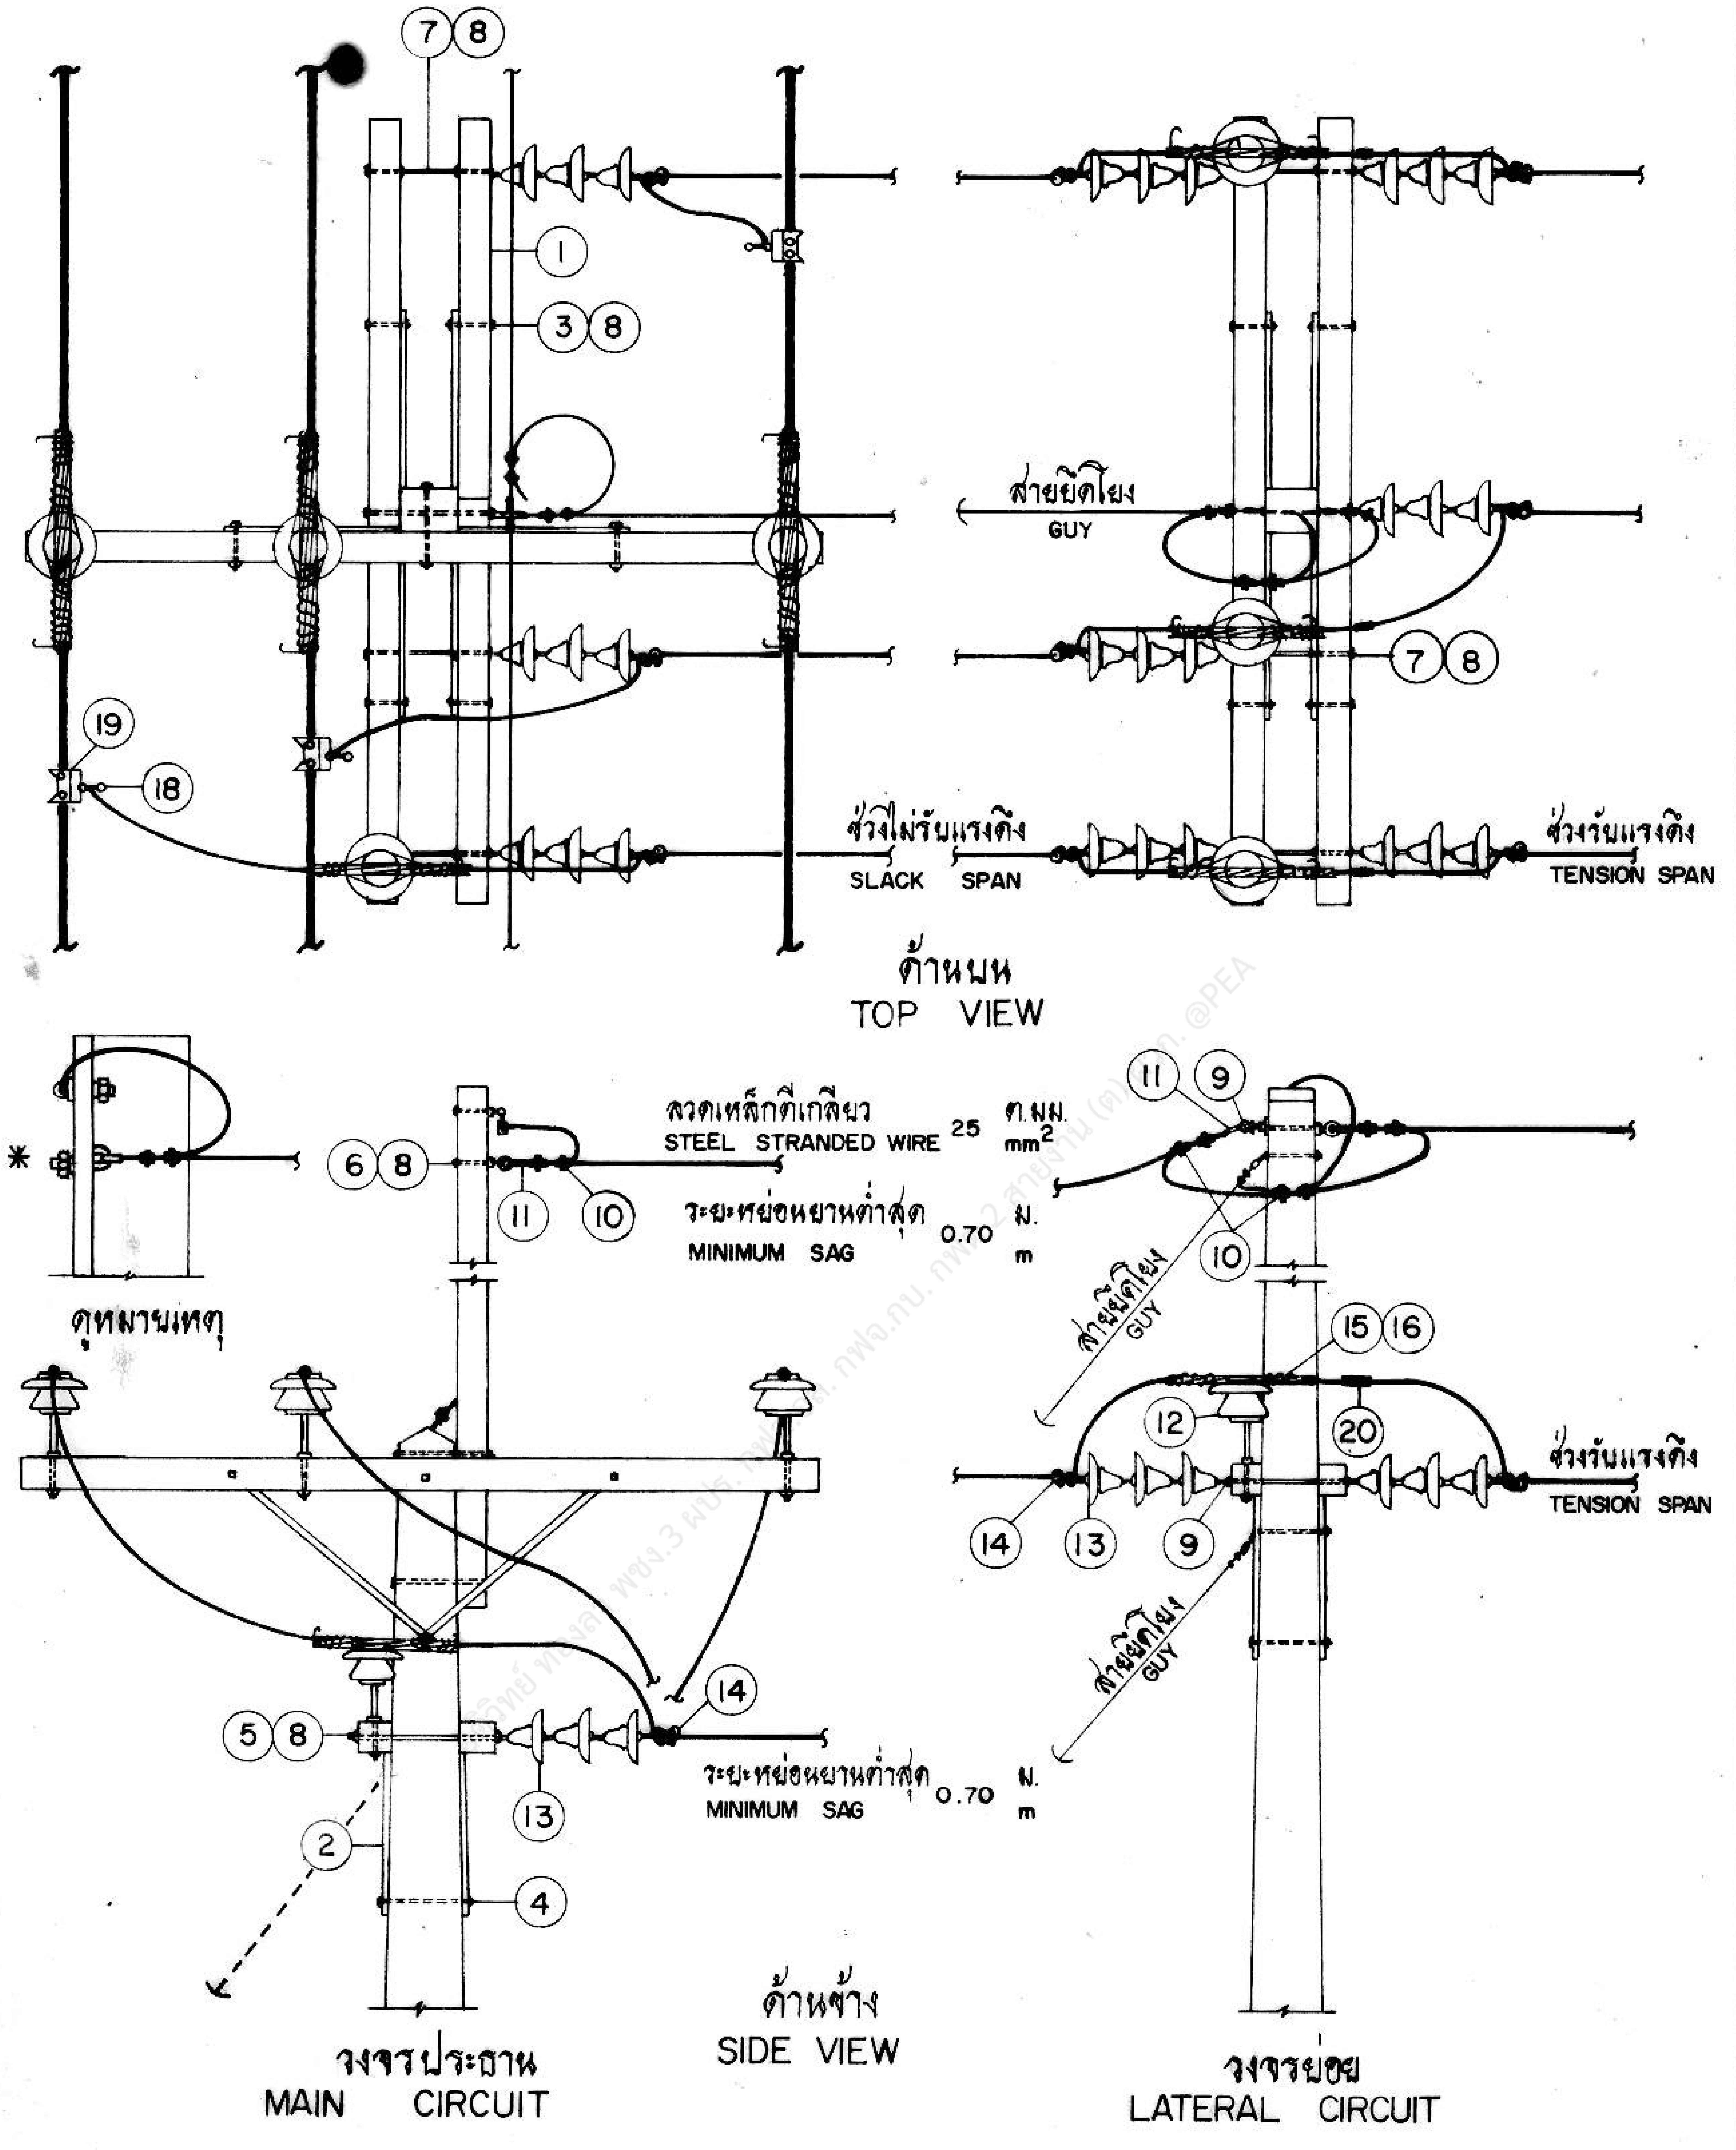

กองวิศวกรรม	การไฟฟ้าส่วนภูมิภาค	ใช้แทนแบบ ถูกแทนโดยแบบ เขียนเสร็จวันที่ 23 ก.พ.19 แก้แบบวันที่ ผิดเป็น มาตราส่วน 1 : 40 แบบเลขที่ S02-015/19012 แผ่นที่ 1 ของจำนวน 4 แผ่น
ผู้เขียน สถาปนิก วิศวกร หัวหน้าแผนก ผู้อำนวยการกอง	ผู้ว่าการ 12 มี.ค. 2519	
	การติดตั้งบัคอาร์มระบบ 33 kV ก สำหรับการต่อสายตรง	
รองผู้ว่าการฝ่ายเทคนิค	BUCKARM INSTALLATION 33 kV A FOR DIRECT CONNECTION	

การประกอบเลขที่
ASSEMBLY NO. 3215

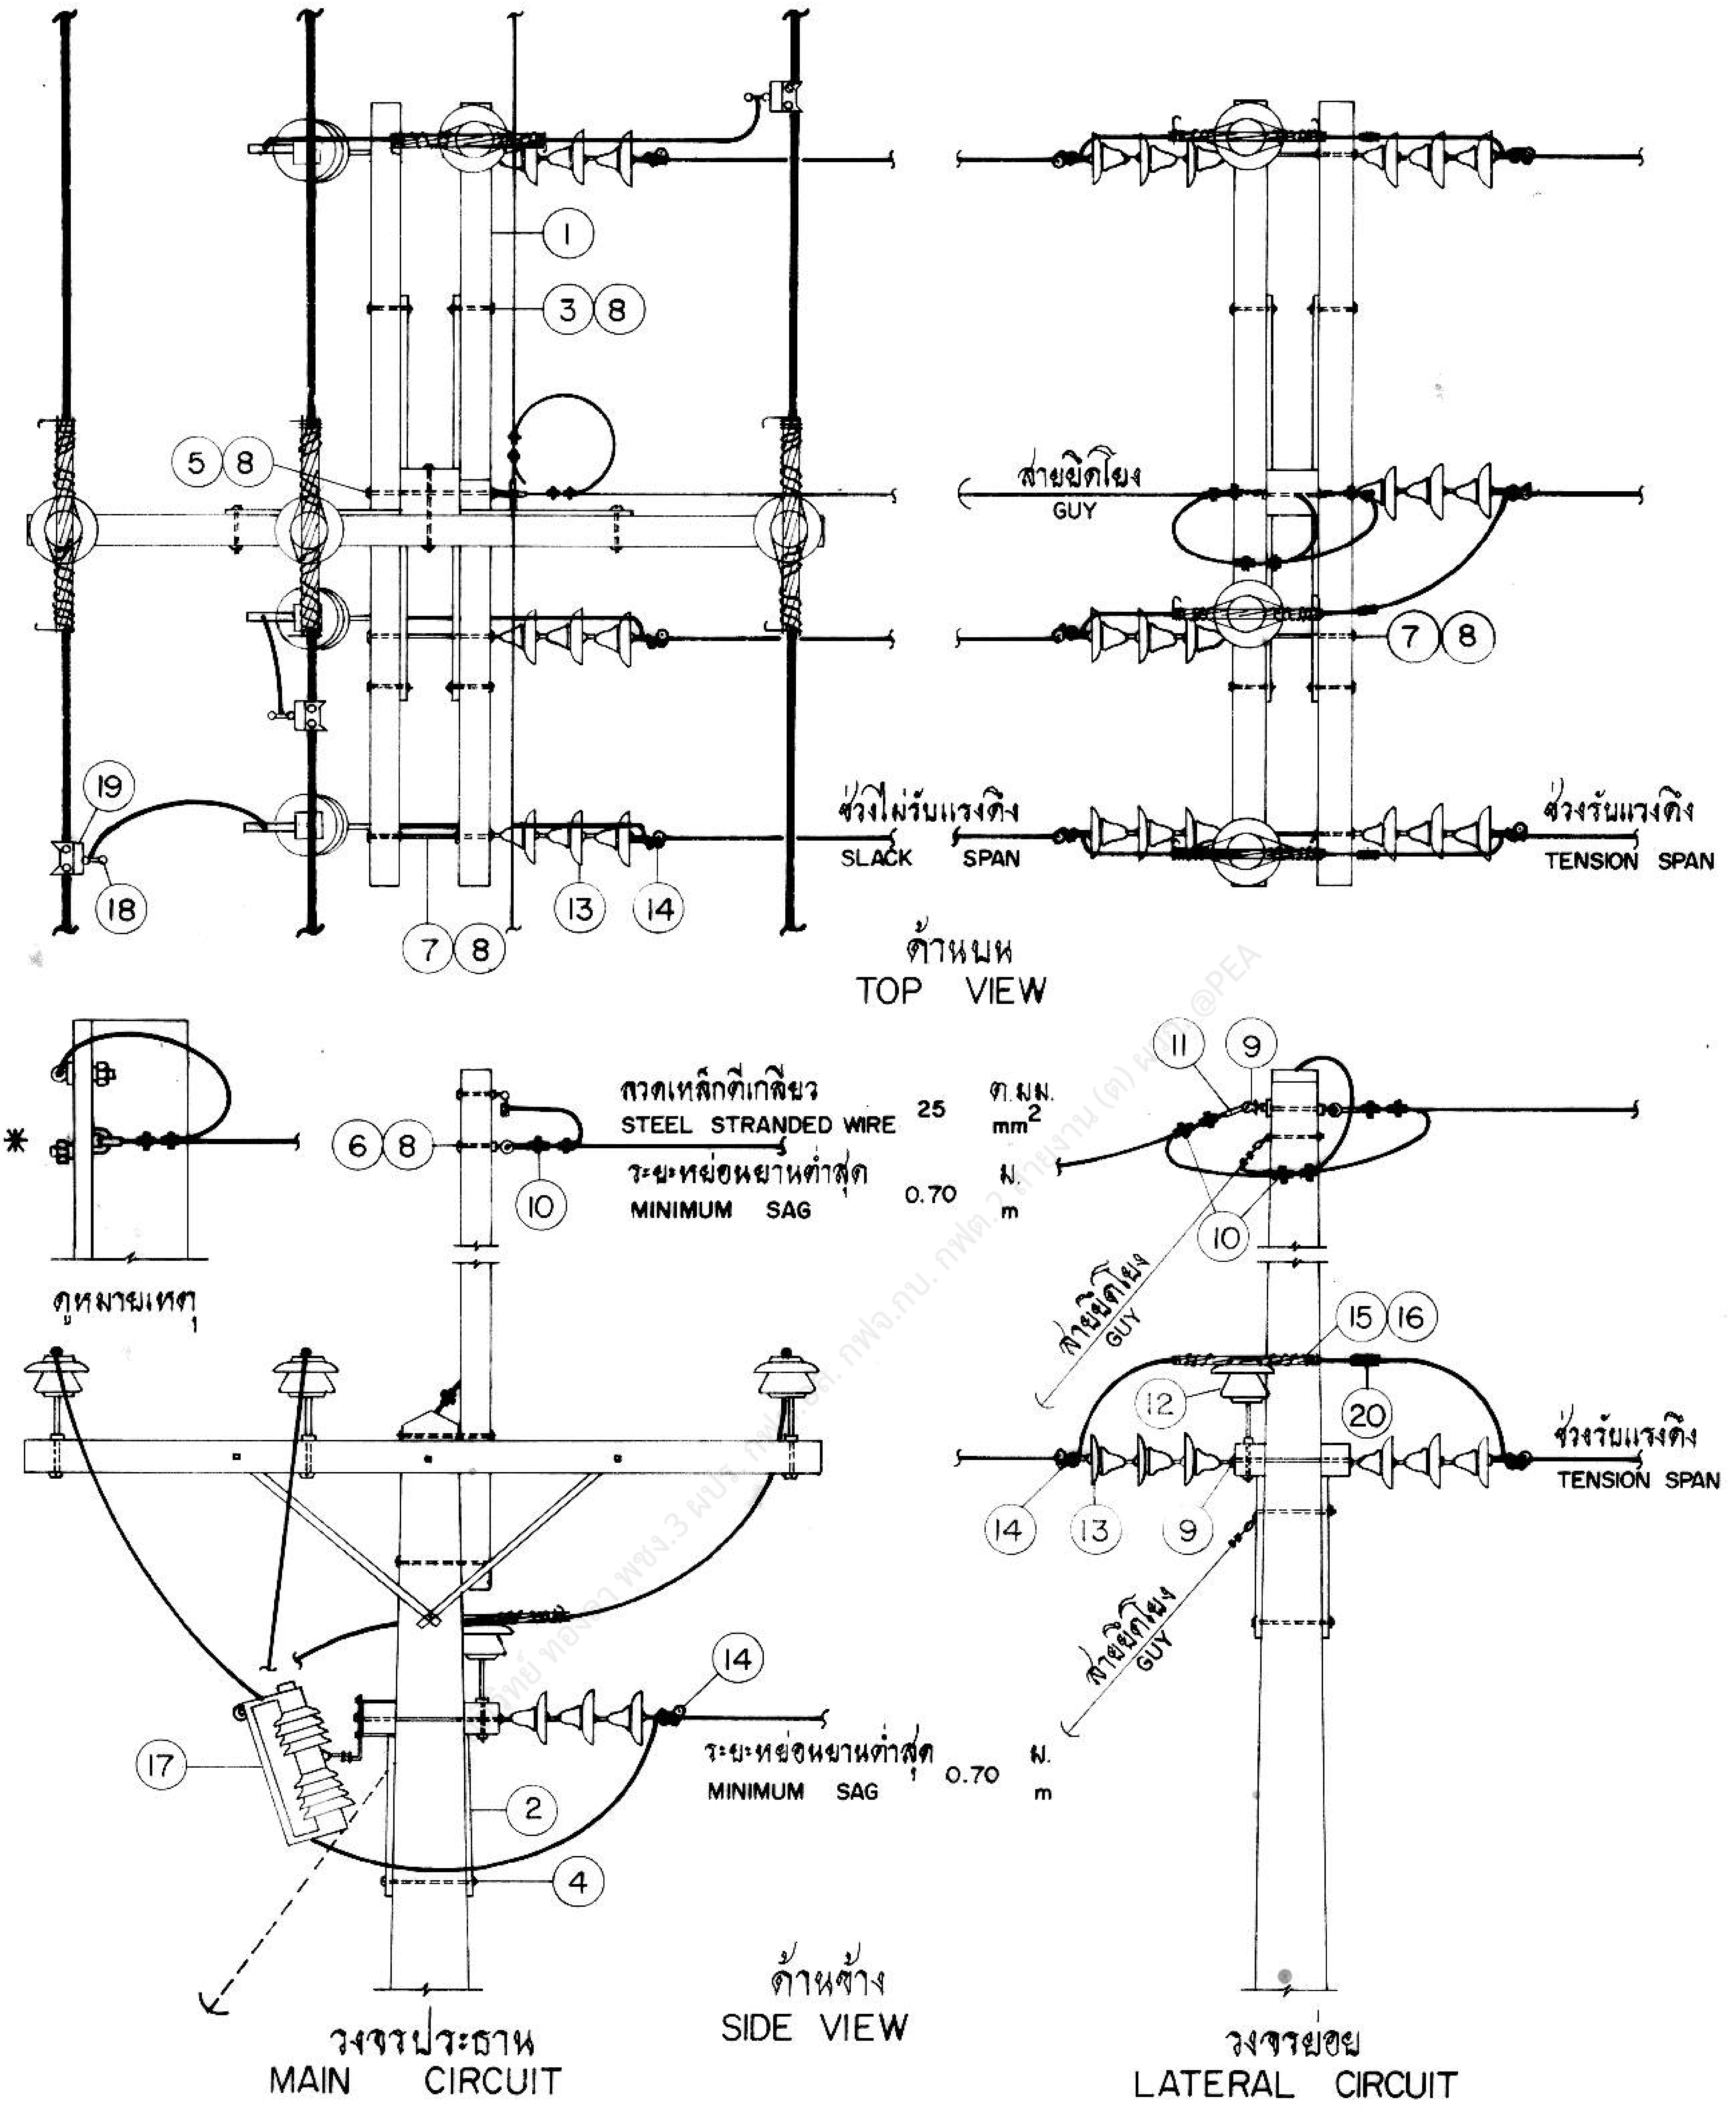

กองวิศวกรรม

การไฟฟ้าส่วนภูมิภาค

ผู้เขียน
สถาปนิก
วิศวกร
หัวหน้าแผนก
ผู้อำนวยการกอง
รองผู้ว่าการฝ่ายเทคนิค

ผู้ว่าการ

12 มี.ค. 2519

การติดตั้งบัคอาร์มระบบ 33 kV
ข สำหรับการต่อสายผ่านคัตเอาต์

BUCKARM INSTALLATION 33 kV
B FOR CONNECTION WITH CUTOUTS

ใช้แทนแบบ
ถูกแทนโดยแบบ
เขียนเสร็จวันที่ 23 ก.พ. 19
แก้แบบวันที่
ผิดเป็น
มาตราส่วน 1:40
แบบเลขที่ S02-015/19012
แผ่นที่ 2 ของจำนวน 4 แผ่น

การประกอบเลขที่
ASSEMBLY NO. 3215

บัญชีวัสดุ
BILL OF MATERIAL

ลำดับที่ ITEM	รายละเอียด DESCRIPTION	จำนวน REQ'D ก /A	ข /B	วัสดุเลขที่ MAT. NO.
1	ไม้คอนสายแรงสูง 100 X 120 X 3,000 มม. CROSSARM, WOOD, H.T. 100 X 120 X 3,000 mm	2	2	00100003 (0101)
2	เหล็กประกับไม้คอน 40 X 6 X 1,000 มม. BRACE, FLAT, FOR CROSSARM 40 X 6 X 1,000 mm	4	4	01200002 (0121)
3	สลักเกลียว M 16 X 130 มม. BOLT, MACHINE, M 16 X 130 mm	4	4	01110200 (0220)
4	สลักเกลียว M 16 X 250 มม. BOLT, MACHINE, M 16 X 250 mm	1	1	01110203 (0223)
5	สลักเกลียว M 16 X 450 มม. BOLT, MACHINE, M 16 X 450 mm	1	1	01110207 (0227)
6	สลักห่วงกลม M 16 X 200 มม. BOLT, ROUND EYE, M 16 X 200 mm	1	1	01140001 (0253)
7	สลักเกลียวห่วงกลม M 16 X 450 มม. BOLT, ROUND EYE, M 16 X 450 mm	4	4	01130001 (0247)
8	แหวนสี่เหลี่ยมแบน 52 X 52 X 4.5 มม. รู Ø 18 มม มอก. 258 WASHER, SQUARE FLAT 52 X 52 X 4.5 mm HOLE Ø 18 mm TIS 258	24	24	01180100 (0355)
9	นัทรูปห่วง M 16 DIN 582 NUT, EYE, M 16 DIN 582	3	3	01180001 (0345)
10	ยูแคล้มป์ สลัก 1 ตัว M 8 CLAMP, SINGLE U-BOLT, M 8	8	8	01230000 (0165)
11	กายทิมเบิ้ล สำหรับสายยึดโยงขนาด 50-95 ต.มม. THIMBLE, GUY, FOR STEEL WIRE 50-95 mm^2	2	2	01210304 (0150)
12	ลูกถ้วยก้านตรง 33 kV มอก. 279 แบบ ค (แบบ 56-3) พร้อมก้าน INSULATOR, PIN TYPE, 33 kV, TIS 279 TYPE C (CLASS 56-3) COMP. WITH PIN	4	4	03000002 03100001
13	ลูกถ้วยแขวน มอก. 354 แบบ ง (แบบ 52-4) INSULATOR, SUSPENSION TYPE, TIS 354 TYPE D (CLASS 52-4)	18	18	03020002 (0415)
14	สเตรนแคล้มป์ สำหรับสายอะลูมิเนียม ขนาดตามต้องการ CLAMP, STRAIN, FOR Al SIZE AS REQUIRED	6	6	03110000 - 03110002
15	ลวดอะลูมิเนียมแบน 1 X 10 มม. ความยาวตามต้องการ TAPE, ARMOR, Al 1 X 10 mm LENGTH AS REQUIRED			02200000 (0700)
16	ลวดอะลูมิเนียมกลม 4 มม. TIE, WIRE, Al 4 mm			02200002 (0704)
17	ดรอพเอาท์ ฟิวส์คัทเอาท์ หนึ่งอินซูเลเตอร์ 33 kV CUT-OUT, FUSE, OPEN TYPE, SINGLE INSULATOR, DROP-OUT 33 kV	–	3	04010100 or 04010101
18	ฮอทไลน์แคล้มป์ สำหรับสายอะลูมิเนียม ขนาดตามต้องการ CLAMP, HOTLINE, MAIN LINE, Al SIZE AS REQUIRED	3	3	02330100 - 02330101

กองวิศวกรรม

ผู้เขียน
สถาปนิก
วิศวกร
หัวหน้าแผนก
ผู้อำนวยการกอง
รองผู้ว่าการฝ่ายเทคนิค

การไฟฟ้าส่วนภูมิภาค

ผู้ว่าการ

12 พ.ค. 2519

การติดตั้งบัคอาร์มระบบ 33 kV
ค บัญชีวัสดุ

BUCKARM INSTALLATION 33 kV
C BILL OF MATERIAL

ใช้แทนแบบ
ถูกแทนโดยแบบ
เขียนเสร็จวันที่ 23 ก.พ. 19
แก้แบบวันที่
มิติเป็น
มาตราส่วน
แบบเลขที่ S02-015/19012
แผ่นที่ 3 ของจำนวน 4 แผ่น

การประกอบเลขที่ ASSEMBLY NO.	3215

บัญชีวัสดุ
BILL OF MATERIAL

ลำดับที่ ITEM	รายละเอียด DESCRIPTION	จำนวน REQ'D ก/A	 ข/B	วัสดุเลขที่ MAT NO.
19	สเตอร์รัพแคล้มป์ หรือเบลแคล้มป์ฮอทไลน์ ขนาดตามต้องการ CLAMP, STIRRUP OR BAIL, HOTLINE, MAIN LINE, Al SIZE AS REQUIRED	3	3	02330000 or 02330001
20	หลอดต่อสายชนิดบีบไม่รับแรงดึง ขนาดตามต้องการ CONNECTOR, SPLICE, COMPRESSION TYPE, TENSIONLESS SIZE AS REQUIRED	3	3	02410001-5 02410101-8

หมายเหตุ * ในกรณีเป็นเหล็กฉากรับสายล่อฟ้าต้องเพิ่มยูแคล้มป์สลักเกลียว (วัสดุเลขที่ 01230000) 2 ตัว และกราวด์วายแคล้มป์ (วัสดุเลขที่ 01230205) 1 ตัว

ข้อแนะนำในการติดตั้ง

1 ขนาดสายของวงจรย่อย; สายอะลูมิเนียม หรืออะลูมิเนียมอัลลอย 120 ต.มม.
สายอะลูมิเนียมแกนเหล็ก 95/15 ต.มม.

2 ระยะห่างระหว่างช่วงเสาไม่รับแรงดึงไม่เกิน 15 ม.

3 ต้องทำการยึดโยงที่เสาวงจรประธาน ในกรณีต่อไปนี้

3.1 ระยะห่างระหว่างเสาช่วงไม่รับแรงดึงมากกว่า 15 ม. แต่ไม่เกิน 50 ม. (เมื่อใช้ไม้คอนรับสายล่อฟ้า)

3.2 ขนาดสายของวงจรย่อยใหญ่กว่าที่กำหนดไว้ในข้อ 1

4 ในกรณีขาดแคลนหลอดต่อสาย อนุโลมให้ใช้พี.จี. คอนเนคเตอร์ 2 อัน แทนได้

INSTALLATION SUGGESTION

1 LATERAL CIRCUIT CONDUCTOR SIZE; Al OR Al-ALLOY 120 mm^2
ACSR 95/15 mm^2

2 MAXIMUM SLACK SPAN LATERAL 15 m

3 MAIN CIRCUIT POLE SHALL BE GUYED IN THE FOLLOWING CASES

3.1 SLACK SPAN IS MORE THAN 15 m BUT NOT MORE THAN 50 m (USING WOOD CROSSARM AS BAYONET)

3.2 LATERAL CIRCUIT CONDUCTOR IS BIGGER THAN SPECIFIED VALUE OF ITEM 1

4 IN CASE OF LACKING TENSIONLESS SPLICE CONNECTOR, PERMIT TO USE 2 P.G. CONNECTORS

กองวิศวกรรม	การไฟฟ้าส่วนภูมิภาค	ใช้แทนแบบ -
ผู้เขียน Nopadol สมบูรณ์ สถาปนิก วิศวกร หัวหน้าแผนก ผู้อำนวยการกอง	ผู้ว่าการ 12 มี.ค. 2519	ถูกแทนโดยแบบ เขียนเสร็จวันที่ 23 ก.พ. 19 แก้แบบวันที่ ผิดเป็น
	การติดตั้งบัคอาร์มระบบ 33 kV ค บัญชีวัสดุ	มาตราส่วน
รองผู้ว่าการฝ่ายเทคนิค	BUCKARM INSTALLATION 33 kV C BILL OF MATERIAL	แบบเลขที่ S02-015/19012 แผ่นที่ 4 ของจำนวน 4 แผ่น