การประกอบเลขที่
ASSEMBLY NO. **5252**

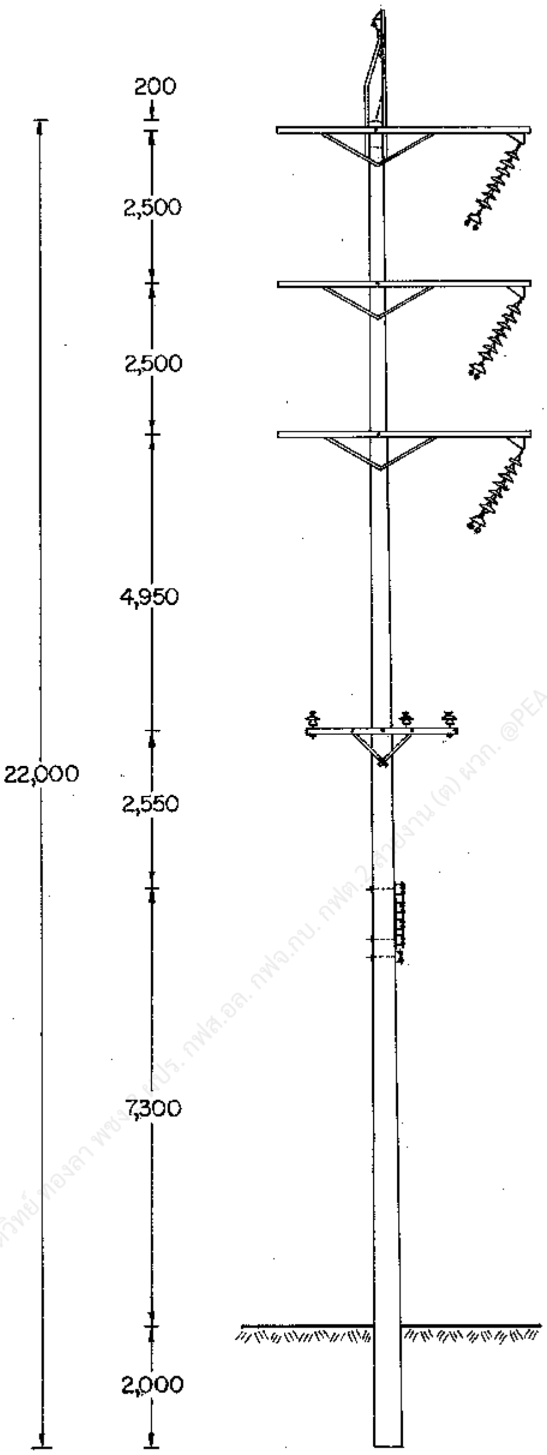

อดิวิทย์ ทองลา พชง. หปร. กฟส.อล. กฟจ.กบ. กฟต.2 สายงาน (ต) ผวก. @PEA

กองวิศวกรรมไฟฟ้าและเครื่องกล
ฝ่ายวิศวกรรม

ผู้เขียน
ผู้สำรวจ
วิศวกร
หัวหน้าแผนก ธีรวัฒน์
หัวหน้ากอง
ผู้อำนวยการฝ่าย

รองผู้ว่าการฝ่ายเทคนิค
3

การไฟฟ้าส่วนภูมิภาค

ผู้ว่าการ 24 มี.ค. 23

115 kV วงจรเดี่ยว สายไฟฟ้าคู่
เสาสำหรับทางโค้ง
แบบ SD–SA–1

115 kV SINGLE CIRCUIT DOUBLE CONDUCTOR
SMALL ANGLE STRUCTURE
TYPE **SD–SA–1**

ใช้แทนแบบ
ถูกแทนโดยแบบ
เขียนเสร็จวันที่ 2 ม.ค. 23
แก้แบบวันที่
มิติเป็น มม.
มาตราส่วน 1 : 125
แบบเลขที่ SA1-015/23006
แผ่นที่ 1 ของจำนวน 3 แผ่น

1 มี.ค. 2523

การประกอบเลขที่ ASSEMBLY NO.	5252

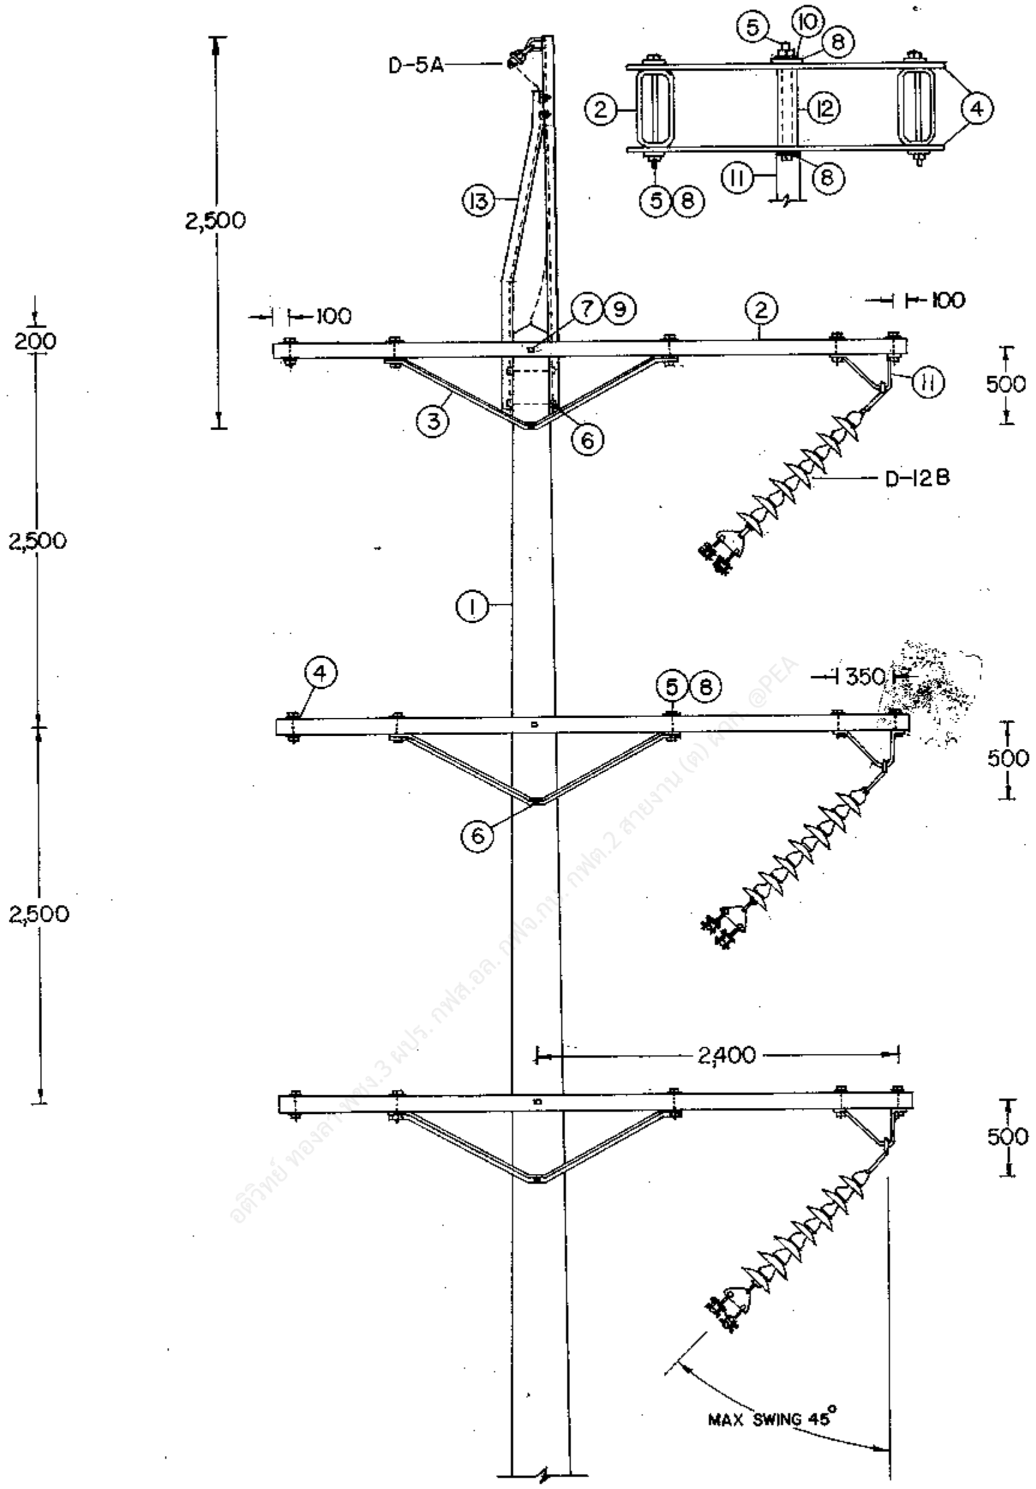

กองวิศวกรรมไฟฟ้าและเครื่องกล ฝ่ายวิศวกรรม	การไฟฟ้าส่วนภูมิภาค	ใช้แทนแบบ....... ถูกแทนโดยแบบ.......
ผู้เขียน....... ผู้สำรวจ....... วิศวกร....... หัวหน้าแผนก....... หัวหน้ากอง....... ผู้อำนวยการฝ่าย.......	ผู้ว่าการ....... 24 มิ.ย. 23	เขียนเสร็จวันที่ 2 ม.ค. 23 แก้แบบวันที่....... คิดเป็น มม. มาตราส่วน 1 : 50
	115 kV วงจรเดี่ยว สายไฟฟ้าคู่ เสาสำหรับทางโค้ง แบบ SD-SA-1	
รองผู้ว่าการฝ่ายเทคนิค	115 kV SINGLE CIRCUIT DOUBLE CONDUCTOR SMALL ANGLE STRUCTURE TYPE SD-SA-1	แบบเลขที่ SAI-015/23006 แผ่นที่ 2 ของจำนวน 3 แผ่น

1 ก.ค. 2523

การประกอบเลขที่ 5252
ASSEMBLY NO.

บัญชีวัสดุ
BILL OF MATERIAL

ลำดับที่ ITEM	รายละเอียด DESCRIPTION	จำนวน REQ'D	วัสดุเลขที่ MAT. NO.
1	เสาคอนกรีต 22 ม. POLE, CONCRETE 22 m. LONG	1	0001001I (0041)
2	คอนสายแบบเหล็ก ขนาด 100X50X3.2 มม. ยาว 4.20 ม. CROSSARM, STEEL 100X50X3.2 mm, 4.20 m LONG	6	00120001 (0116)
3	เหล็กฉากรับคอนสาย ขนาด 50X50X6 มม. ช่วงกว้าง 1,800 มม. ดรอพ 450 มม. BRACE, ANGLE STEEL 50X50X6 mm, 1,800 mm WIDE 450 mm. DROP	6	01200007 (0119)
4	แผ่นเหล็ก ขนาด 6X100X450 มม. PLATE, STEEL 6X100X450 mm.	18	01110200 (0220)
5	สลักเกลียว M 16X170 มม. BOLT, MACHINE, M 16X170 mm.	36	01110201 (0221)
6	สลักเกลียว M 16X350 มม. BOLT, MACHINE, M 16X350 mm.	6	01110205 (0225)
7	สลักเกลียว M 20X450 มม. BOLT, MACHINE, M 20X450 mm.	3	01110302 (0234)
8	แหวนสี่เหลี่ยมแบน 52X52X4.5 มม. รู Ø 18 มม. มอก. 258 WASHER, SQUARE, FLAT 52X52X4.5 mm, HOLE Ø 18 mm, TIS 258	60	01180100 (0355)
9	แหวนสี่เหลี่ยมแบน 62X62X6 มม. รู Ø 22 มม. มอก. 258 WASHER, SQUARE, FLAT 62X62X6 mm, HOLE Ø 22 mm, TIS 258	6	01180101 (0356)
10	แหวนสปริง M 16 มอก. 259 WASHER, LOCK, M 16, TIS 259	6	01180301 (0365)
11	ที่แขวนลูกถ้วยทางโค้ง BRACKET, CORNER SUSPENSION	3	03140012 (0489)
12	ท่อเหล็ก ชื่อขนาด 20 มม. หนา 2.65 มม. ยาว 100 มม. มอก. 277 ประเภท 2 PIPE, IRON DIA 20 mm I.D., 2.65 mm THICKNESS, 100 mm LONG, TIS 277, TYPE 2	6	01050000 (0905)
13	เหล็กฉากรับสายล่อฟ้าทางโค้ง OVERHEAD GROUND WIRE CORNER BAYONET	1	01010005 (0136)
	รายละเอียด DETAIL		
D-12B	การประกอบลูกถ้วยแขวน SUSPENSION INSULATOR ASSEMBLY	3	
D-5A	การต่อสายล่อฟ้า OVERHEAD GROUND WIRE CONNECTION	1	
D-10A	ฐานรากเสา POLE FOUNDATION	1	

กองวิศวกรรมไฟฟ้าและเครื่องกล
ฝ่ายวิศวกรรม

ผู้เขียน
ผู้สำรวจ
วิศวกร
หัวหน้าแผนก ธีรวัฒ
หัวหน้ากอง
ผู้อำนวยการฝ่าย
23
รองผู้ว่าการฝ่ายเทคนิค

การไฟฟ้าส่วนภูมิภาค

ผู้ว่าการ 24 มิ.ย. 23

115 kV วงจรเดี่ยว สายไฟฟ้าคู่
เสาสำหรับทางโค้ง
แบบ SD-SA-1

115 kV SINGLE CIRCUIT DOUBLE CONDUCTOR
SMALL ANGLE STRUCTURE
TYPE SD-SA-1

ใช้แทนแบบ
ถูกแทนโดยแบบ
เขียนเสร็จวันที่ 2 ม.ค. 23
แก้แบบวันที่
มิติเป็น
มาตราส่วน

แบบเลขที่ SAL-015/23006
แผ่นที่ 3 ของจำนวน 3 แผ่น