การประกอบเลขที่ 2431
ASSEMBLY NO. 3419

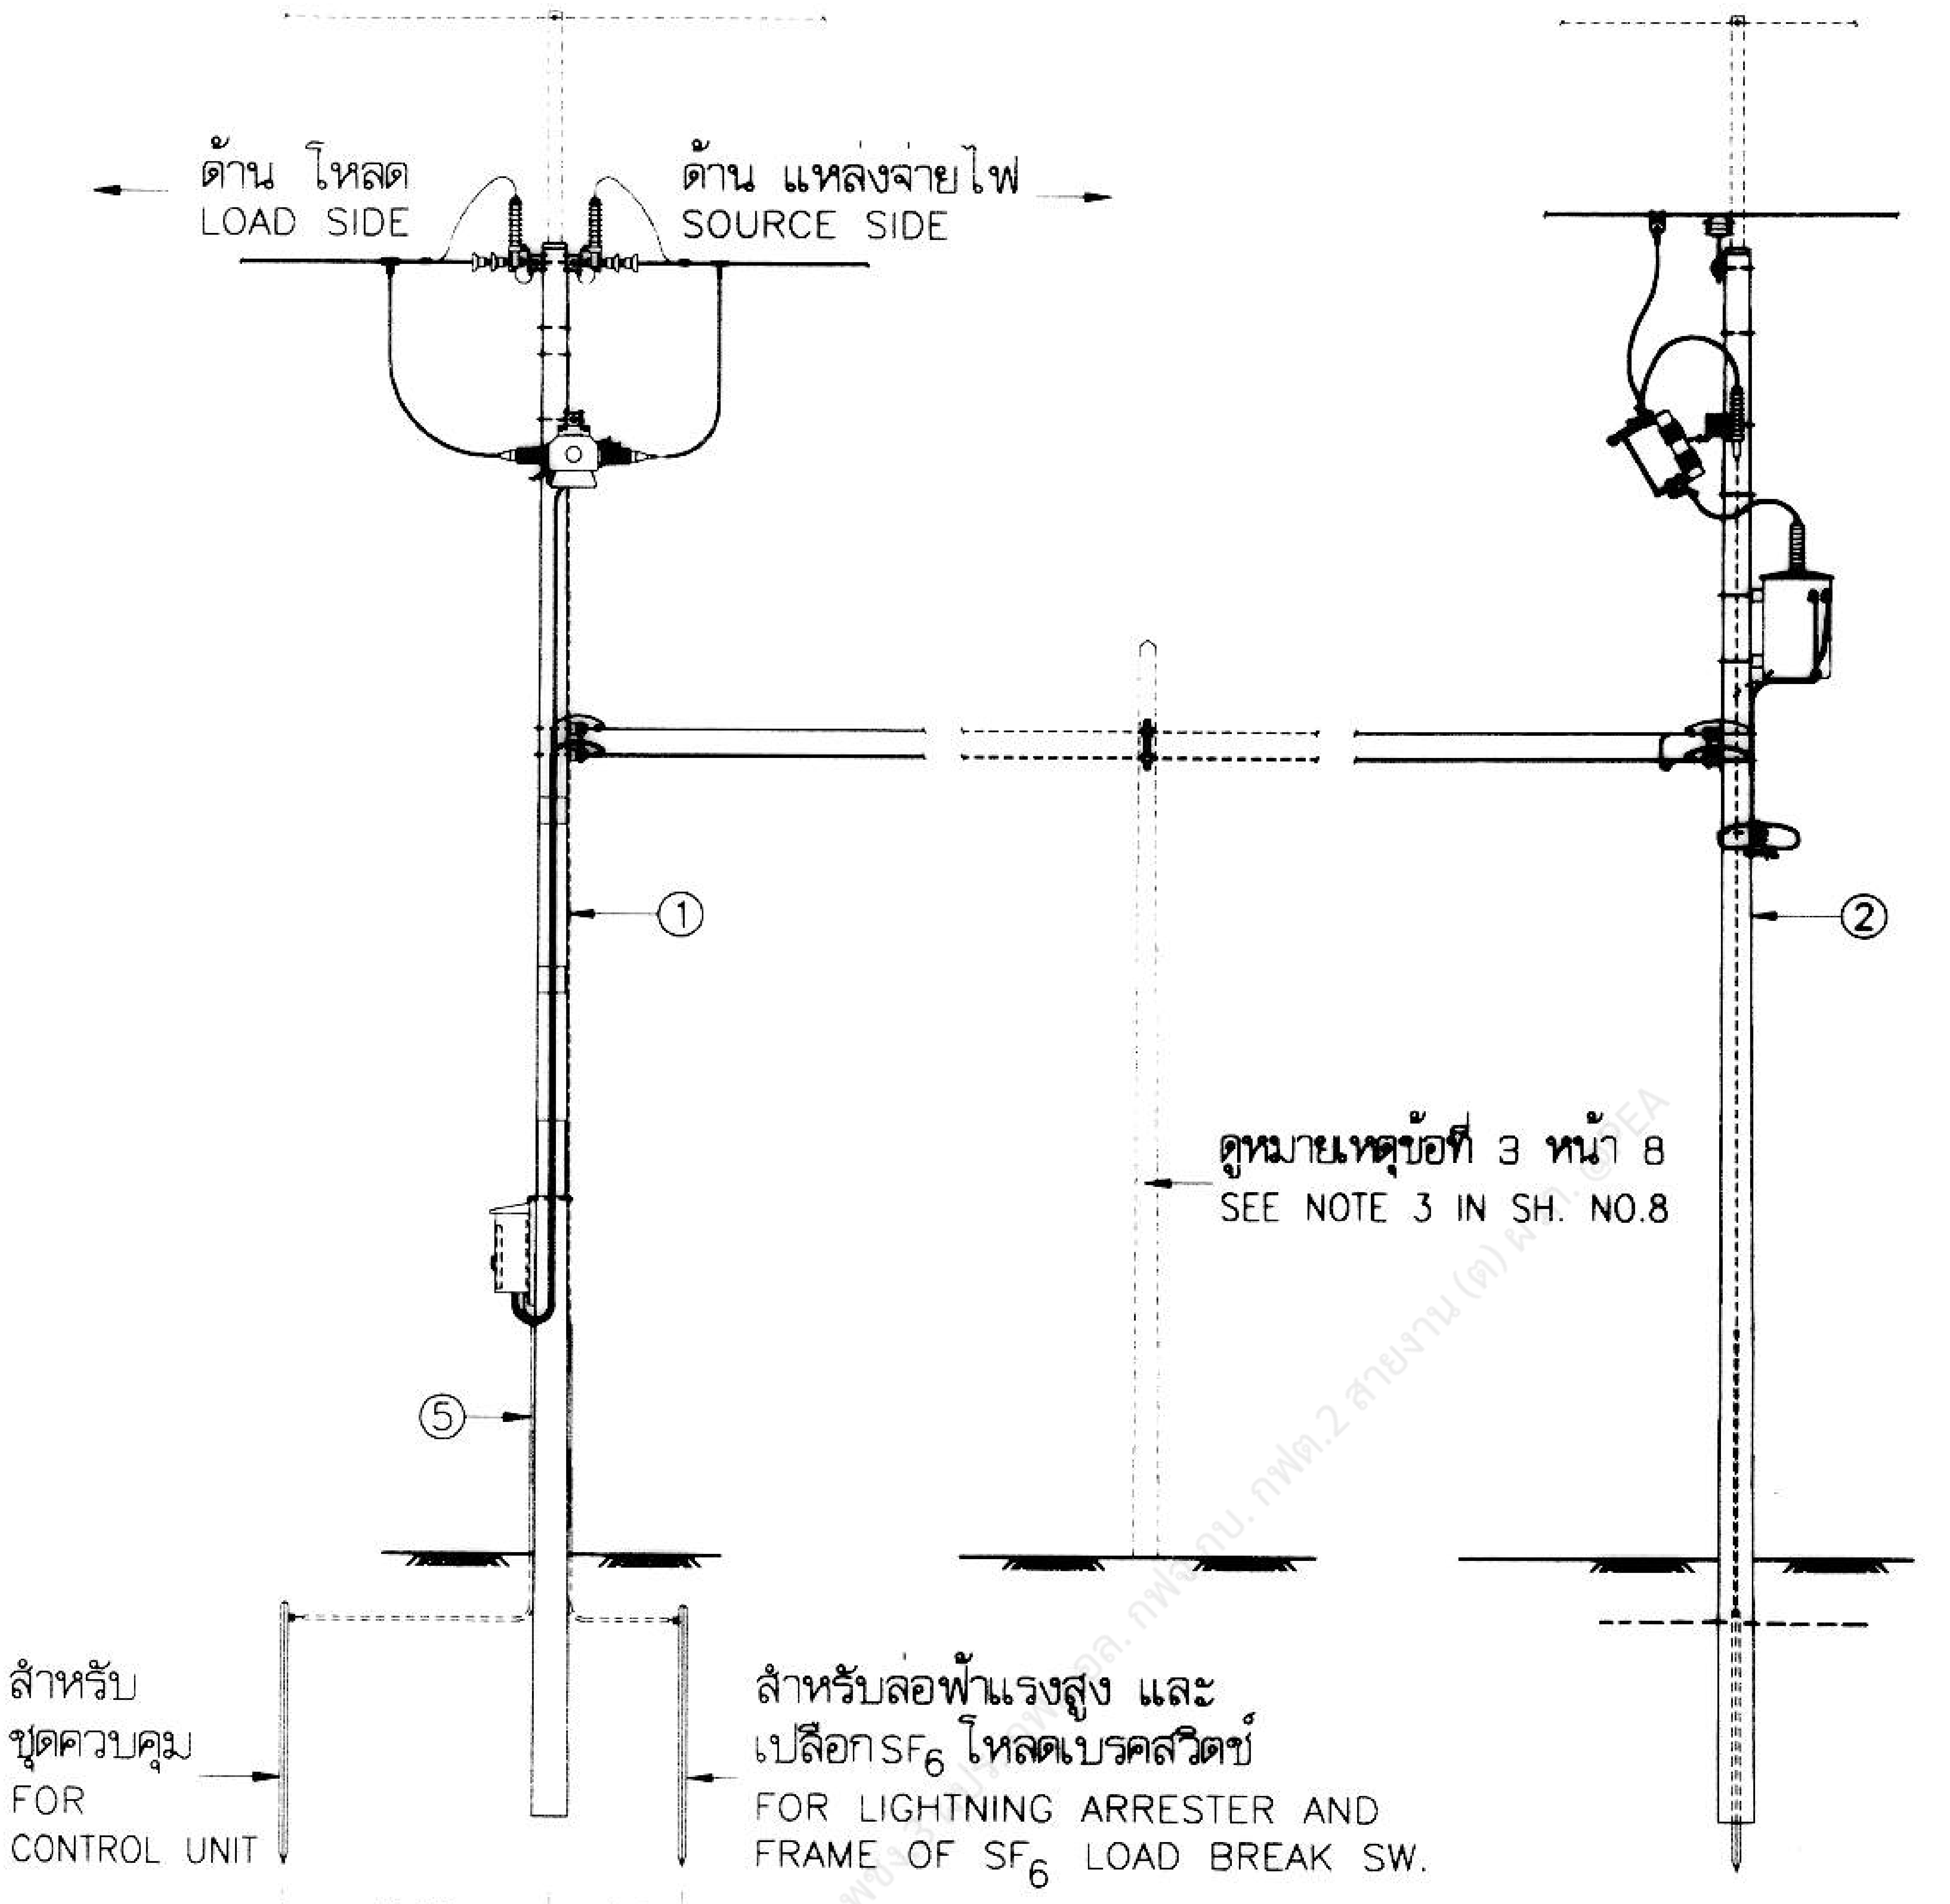
ด้าน โหลด
LOAD SIDE
ด้าน แหล่งจ่ายไฟ
SOURCE SIDE
①
②
⑤
ดูหมายเหตุข้อที่ 3 หน้า 8
SEE NOTE 3 IN SH. NO.8
สำหรับ
ชุดควบคุม
FOR
CONTROL UNIT
สำหรับล่อฟ้าแรงสูง และ
เปลือก SF_6 โหลดเบรคสวิตช์
FOR LIGHTNING ARRESTER AND
FRAME OF SF_6 LOAD BREAK SW.
2.00
1.00

เสาต้นที่ติดตั้ง
SF_6 โหลดเบรคสวิตช์ (ดูรายละเอียด A)
SF_6 LOAD BREAK SW. POLE
(SEE DETAIL A)

เสาต้นที่ติดตั้งหม้อแปลง
ซัพพลายแรงต่ำจาก
ด้านแหล่งจ่ายไฟ
TRANSFORMER POLE
AC-SUPPLY FROM
SOURCE SIDE

แบบที่ 1 แหล่งจ่ายไฟแหล่งเดียว
TYPE 1 SINGLE POWER SOURCE

กองวิศวกรรมไฟฟ้าและเครื่องกล
ฝ่ายวิศวกรรม

การไฟฟ้าส่วนภูมิภาค

ผู้เขียน ศุภกิจ บุญเรือง
ผู้สำรวจ
วิศวกร
หัวหน้าแผนก
ผู้อำนวยการกอง
ผู้อำนวยการฝ่าย
รองผู้ว่าการ

ผู้ว่าการ

การติดตั้งชุดควบคุมการปลดสับ SF_6 โหลดเบรคสวิตช์

CONTROL CABINET OF SF_6 LOAD BREAK SWITCH INSTALLATION

ใช้แทนแบบ
ถูกแทนโดยแบบ
เขียนเสร็จวันที่ 31 ก.ค. 2539
แก้แบบวันที่
มิติเป็น มิลลิเมตร
มาตราส่วน 1 : 100
แบบเลขที่ SA4-015/39015
แผ่นที่ 1 ของจำนวน 8 แผ่น

การประกอบเลขที่ ASSEMBLY NO.	2431 3419

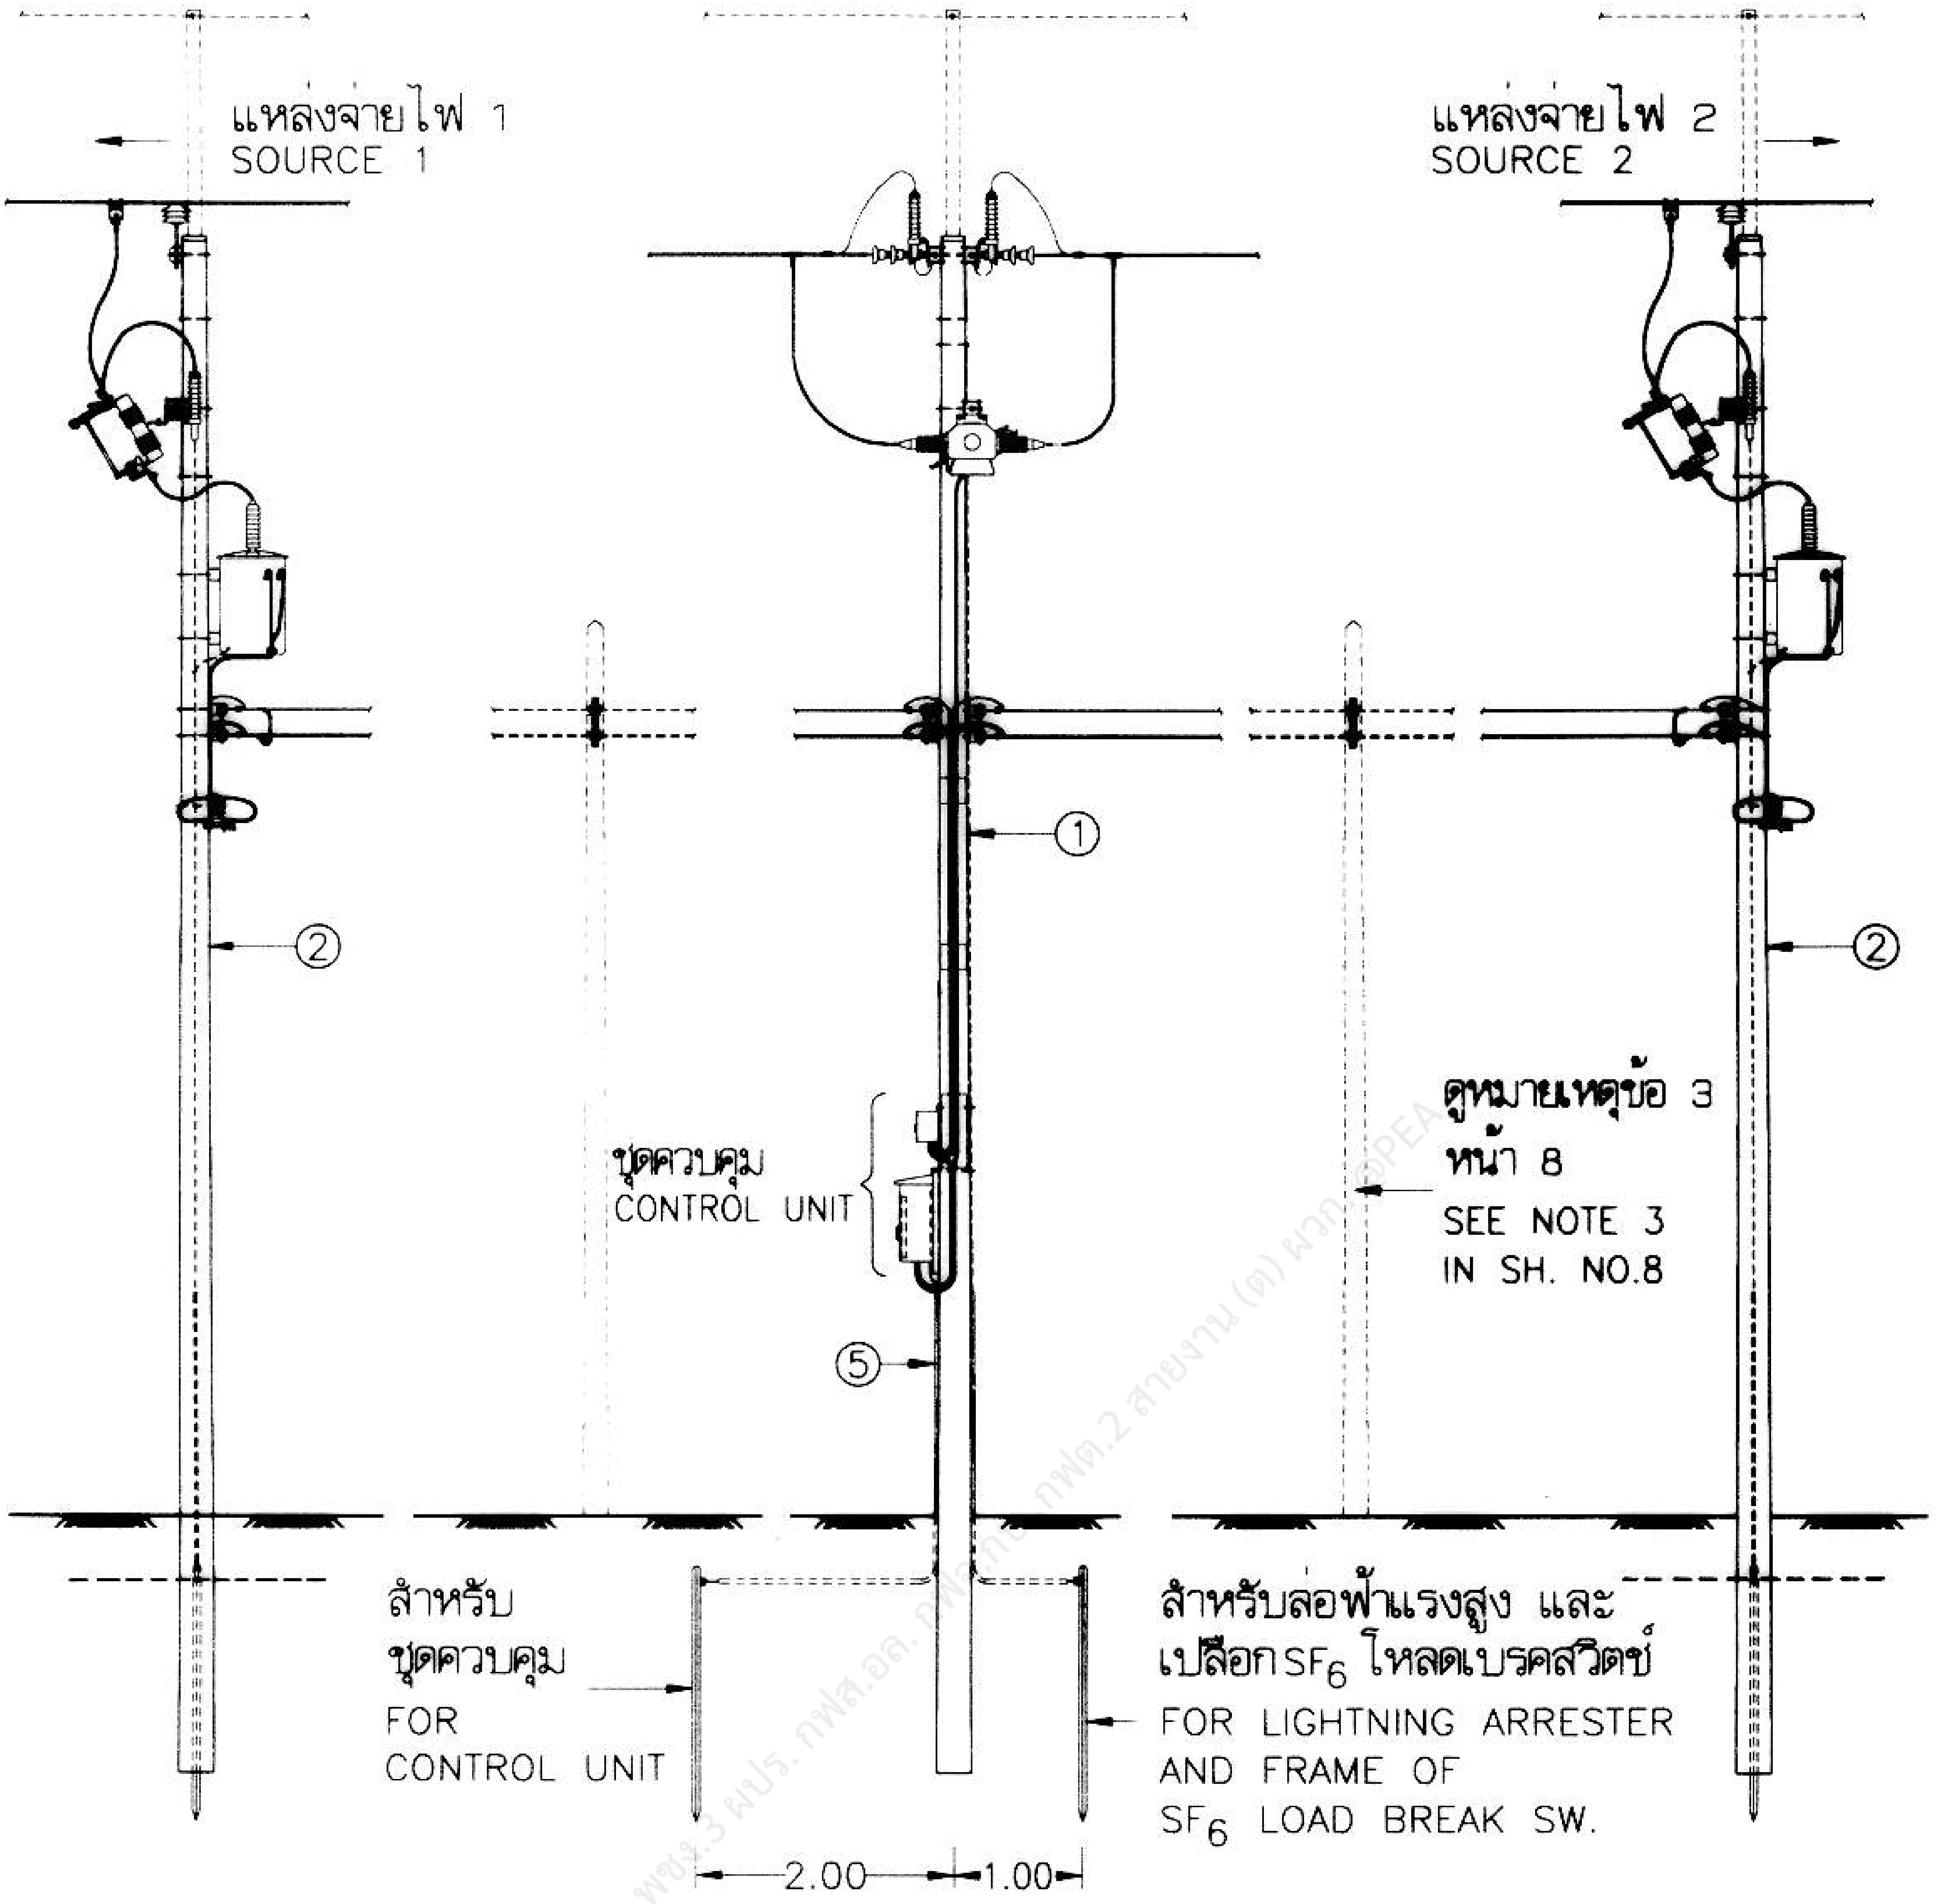
แหล่งจ่ายไฟ 1
SOURCE 1
แหล่งจ่ายไฟ 2
SOURCE 2
①
②
②
ชุดควบคุม
CONTROL UNIT
⑤
ดูหมายเหตุข้อ 3
หน้า 8
SEE NOTE 3
IN SH. NO.8
สำหรับ
ชุดควบคุม
FOR
CONTROL UNIT
สำหรับล่อฟ้าแรงสูง และ
เปลือก SF6 โหลดเบรคสวิตช์
FOR LIGHTNING ARRESTER
AND FRAME OF
SF6 LOAD BREAK SW.
2.00
1.00

อดิวิทย์ ทองลา พชง.3 ผปร. กฟส.อล. กฟต.2 สายงาน (ต) ผวก. @PEA

เสาต้นที่ติดตั้งหม้อแปลง
ซัพพลายแรงต่ำ
จากแหล่งจ่ายไฟ 1
TRANSFORMER POLE
AC-SUPPLY FROM
SOURCE 1

เสาต้นที่ติดตั้ง
SF_6 โหลดเบรคสวิตช์
(ดูรายละเอียด B)
SF_6 LOAD BREAK SW. POLE
(SEE DETAIL B)

เสาต้นที่ติดตั้งหม้อแปลง
ซัพพลายแรงต่ำ
จากแหล่งจ่ายไฟ 2
TRANSFORMER POLE
AC-SUPPLY FROM
SOURCE 2

แบบที่ 2 แหล่งจ่ายไฟ 2 แหล่ง
TYPE 2 TWO POWER SOURCE (OPEN TIE SWITCH)

กองวิศวกรรมไฟฟ้าและเครื่องกล ฝ่ายวิศวกรรม	การไฟฟ้าส่วนภูมิภาค	ใช้แทนแบบ .... ถูกแทนโดยแบบ ....
ผู้เขียน ศุภกิจ บุญเรือง ผู้สำรวจ .... วิศวกร .... หัวหน้าแผนก .... ผู้อำนวยการกอง .... ผู้อำนวยการฝ่าย	ผู้ว่าการ .... **การติดตั้งชุดควบคุมการปลดสับ** **SF_6 โหลดเบรคสวิตช์**	เขียนเสร็จวันที่ 31 ก.ค. 2539 แก้แบบวันที่ .... มิติเป็น มิลลิเมตร มาตราส่วน 1 : 100
รองผู้ว่าการ	**CONTROL CABINET OF SF_6 LOAD BREAK SWITCH INSTALLATION**	แบบเลขที่ SA4-015/39015 แผ่นที่ 2 ของจำนวน 8 แผ่น

การประกอบเลขที่ 2431
ASSEMBLY NO. 3419

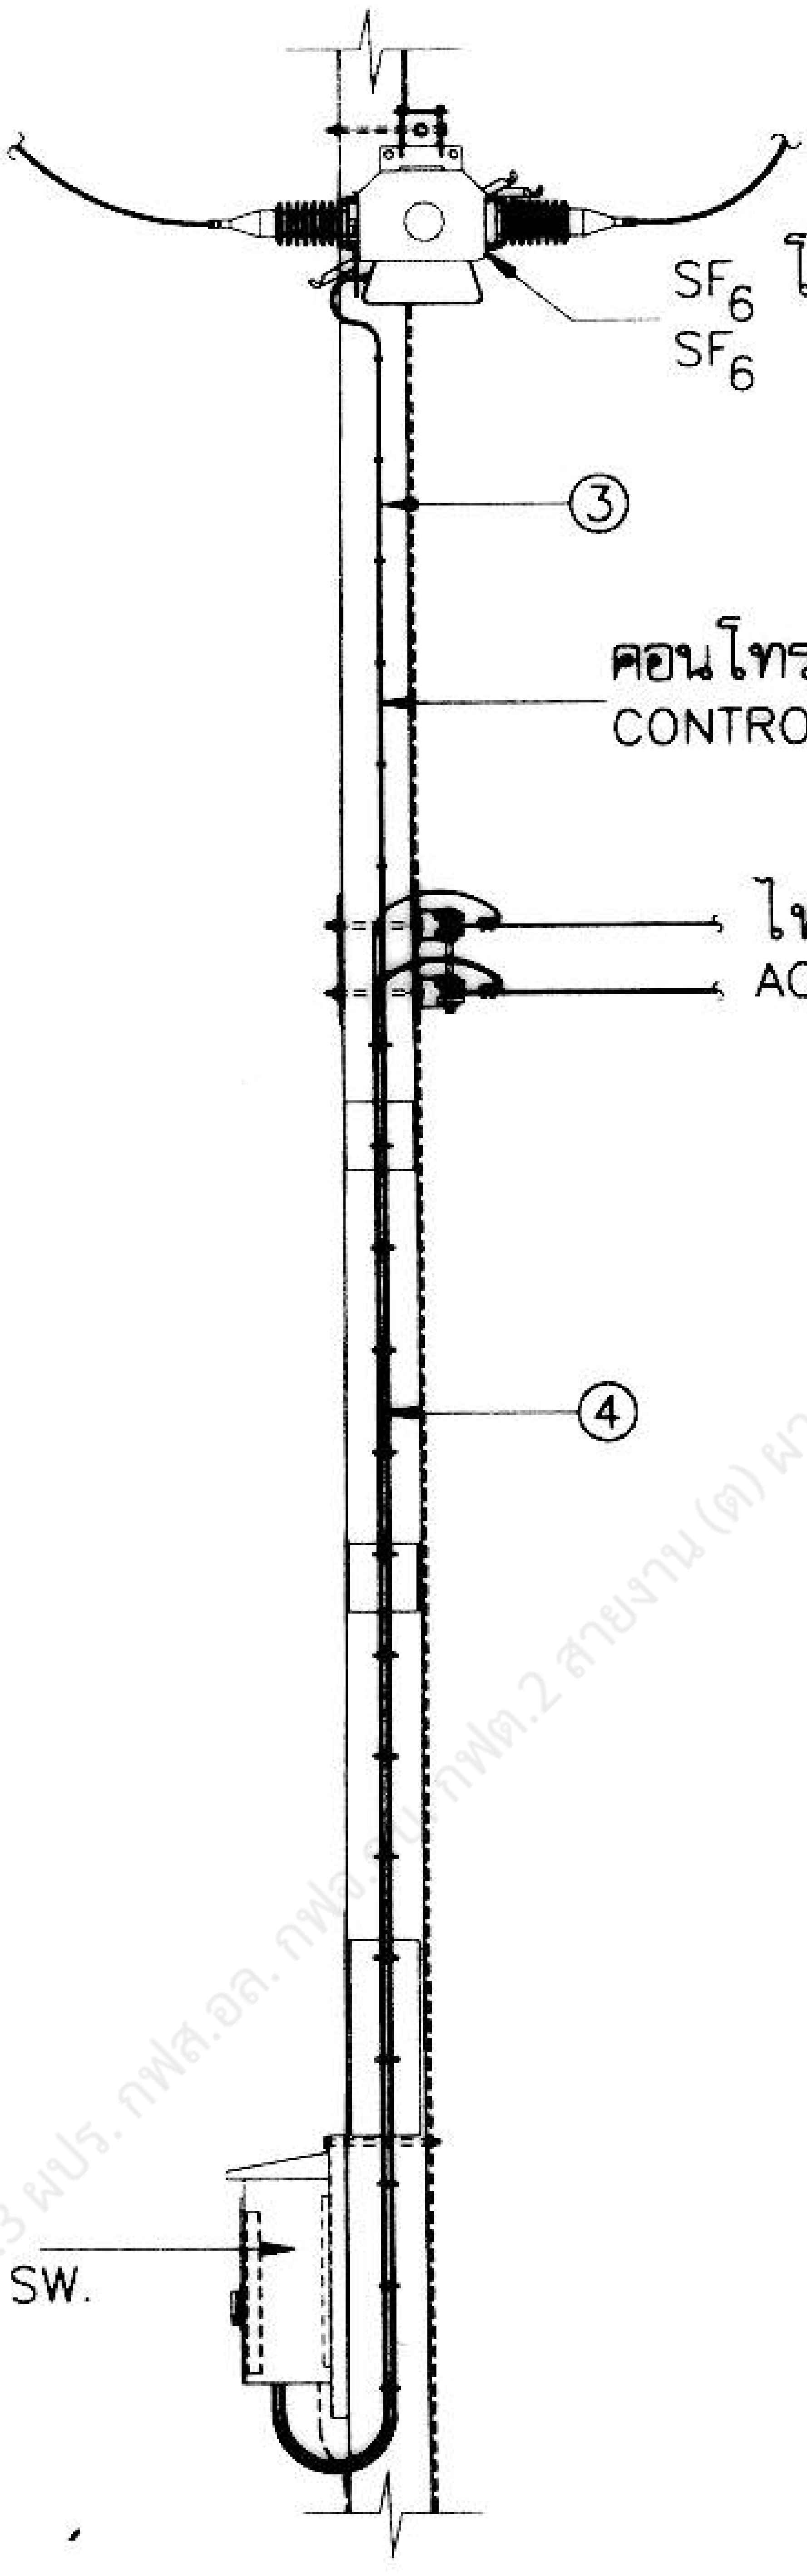

SF_6 โหลดเบรคสวิตช์
SF_6 LOAD BREAK SW.
③
คอนโทรลเคเบิล (จัดโดยผู้ผลิต)
CONTROL CABLE (SUPPLY BY MFG.)
ไฟเลี้ยงจากแหล่งจ่ายไฟ
AC-SUPPLY FROM SOURCE SIDE
④
ตู้ควบคุม SF_6
โหลดเบรคสวิตช์
SF_6 LOAD BREAK SW.
CONTROL CABINET

รายละเอียด A
SEE DETAIL A

อติวิทย์ ทอง[illegible] ผปร. กฟส.อล. กฟ[illegible].2 สายงาน (ต) ผวก. @PEA

กองวิศวกรรมไฟฟ้าและเครื่องกล
ฝ่ายวิศวกรรม

การไฟฟ้าส่วนภูมิภาค

ผู้เขียน ศุภกิจ บุญเรือง
ผู้สำรวจ
วิศวกร
หัวหน้าแผนก
ผู้อำนวยการกอง
ผู้อำนวยการฝ่าย

ผู้ว่าการ

การติดตั้งชุดควบคุมการปลดสับ
SF_6 โหลดเบรคสวิตช์

รองผู้ว่าการ
[illegible]

CONTROL CABINET OF SF_6 LOAD BREAK SWITCH INSTALLATION

ใช้แทนแบบ
ถูกแทนโดยแบบ
เขียนเสร็จวันที่ 31 ก.ค. 2539
แก้แบบวันที่
มิติเป็น มิลิเมตร
มาตราส่วน 1 : 50
แบบเลขที่ SA4-015/39015
แผ่นที่ 3 ของจำนวน 8 แผ่น

การประกอบเลขที่	2431
ASSEMBLY NO.	3419

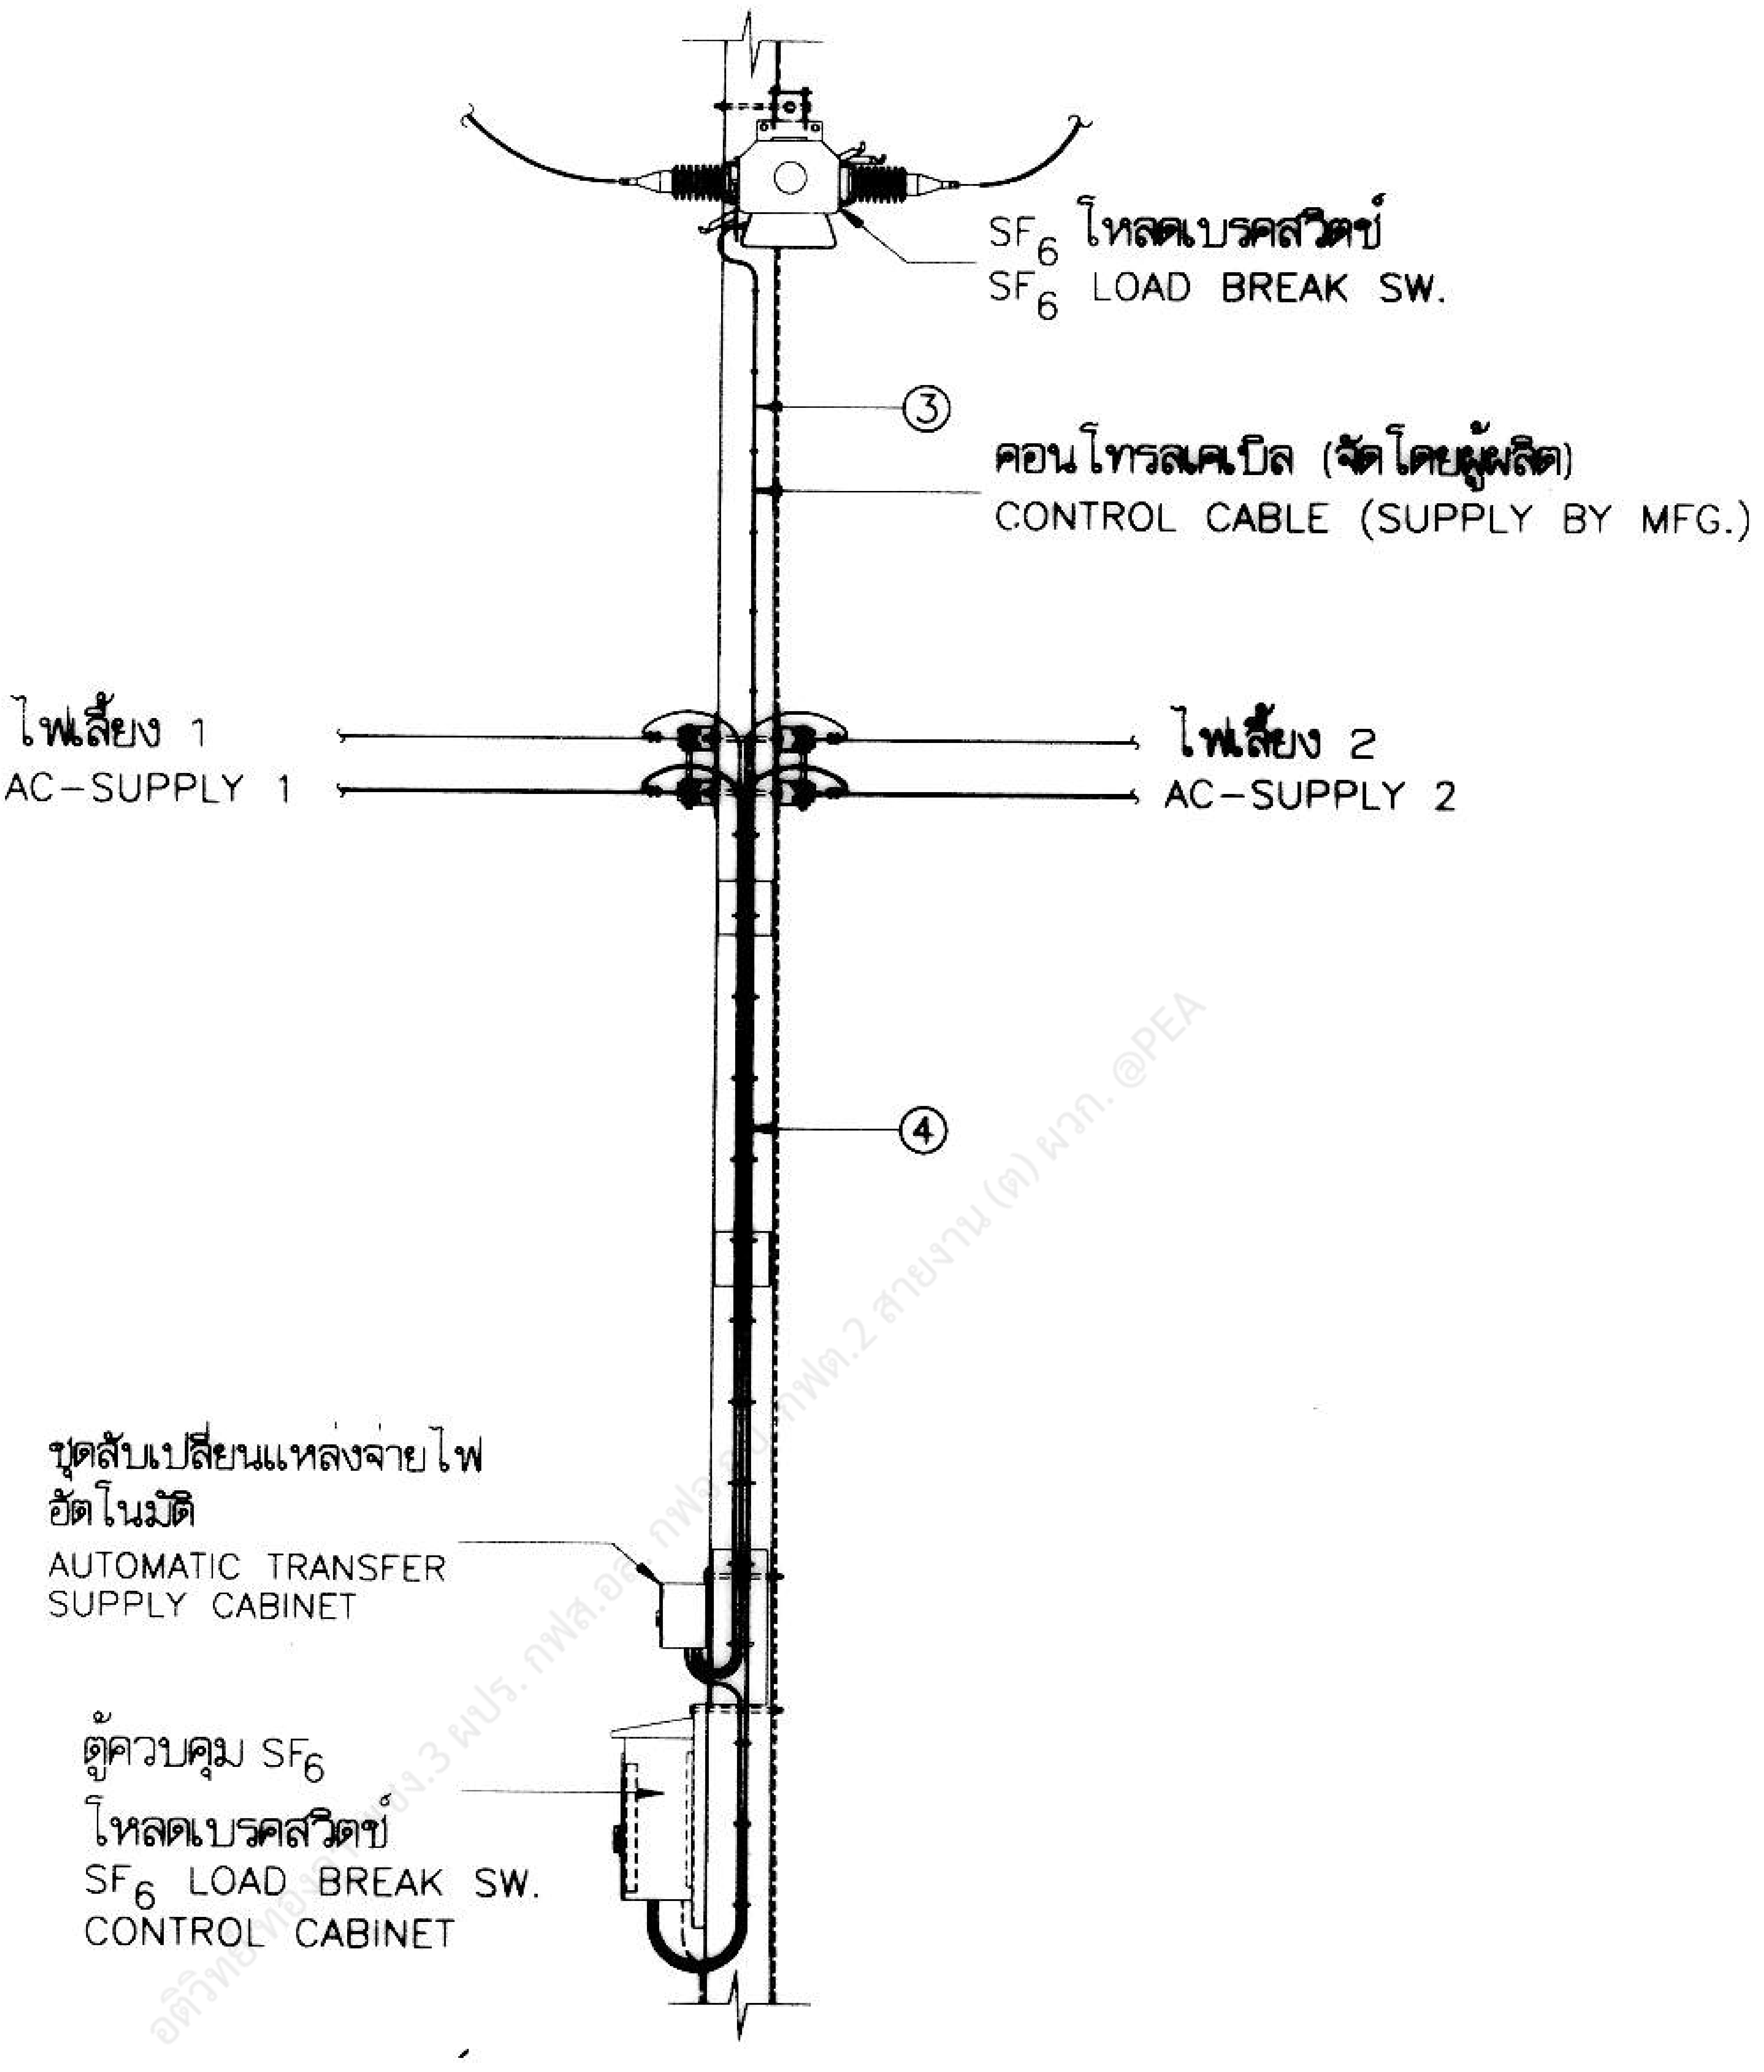
SF$_6$ โหลดเบรคสวิตช์
SF$_6$ LOAD BREAK SW.
③
คอนโทรลเคเบิล (จัดโดยผู้ผลิต)
CONTROL CABLE (SUPPLY BY MFG.)
ไฟเลี้ยง 1
AC-SUPPLY 1
ไฟเลี้ยง 2
AC-SUPPLY 2
④
ชุดสับเปลี่ยนแหล่งจ่ายไฟอัตโนมัติ
AUTOMATIC TRANSFER SUPPLY CABINET
ตู้ควบคุม SF$_6$ โหลดเบรคสวิตช์
SF$_6$ LOAD BREAK SW. CONTROL CABINET

รายละเอียด B
SEE DETAIL B

อดิวิทย์ [illegible] ง.3 ผปร. กฟส.อล [illegible] กฟต.2 สายงาน (ต) ผวก. @PEA

กองวิศวกรรมไฟฟ้าและเครื่องกล
ฝ่ายวิศวกรรม

การไฟฟ้าส่วนภูมิภาค

ผู้เขียน ....ศุภกิจ บุญเรือง....
ผู้สำรวจ ....
วิศวกร ....
หัวหน้าแผนก ....
ผู้อำนวยการกอง ....
ผู้อำนวยการฝ่าย ....
รองผู้ว่าการ ....

ผู้ว่าการ ....

การติดตั้งชุดควบคุมการปลดสับ SF$_6$ โหลดเบรคสวิตช์

CONTROL CABINET OF SF$_6$ LOAD BREAK SWITCH INSTALLATION

ใช้แทนแบบ ....
ถูกแทนโดยแบบ ....
เขียนเสร็จวันที่ 31 ก.ค. 2539
แก้แบบวันที่ ....
มิติเป็น ....มิลิเมตร....
มาตราส่วน ....1 : 50....
แบบเลขที่ SA4-015/39015
แผ่นที่ 4 ของจำนวน 8 แผ่น

การประกอบเลขที่ 2431
ASSEMBLY NO. 3419

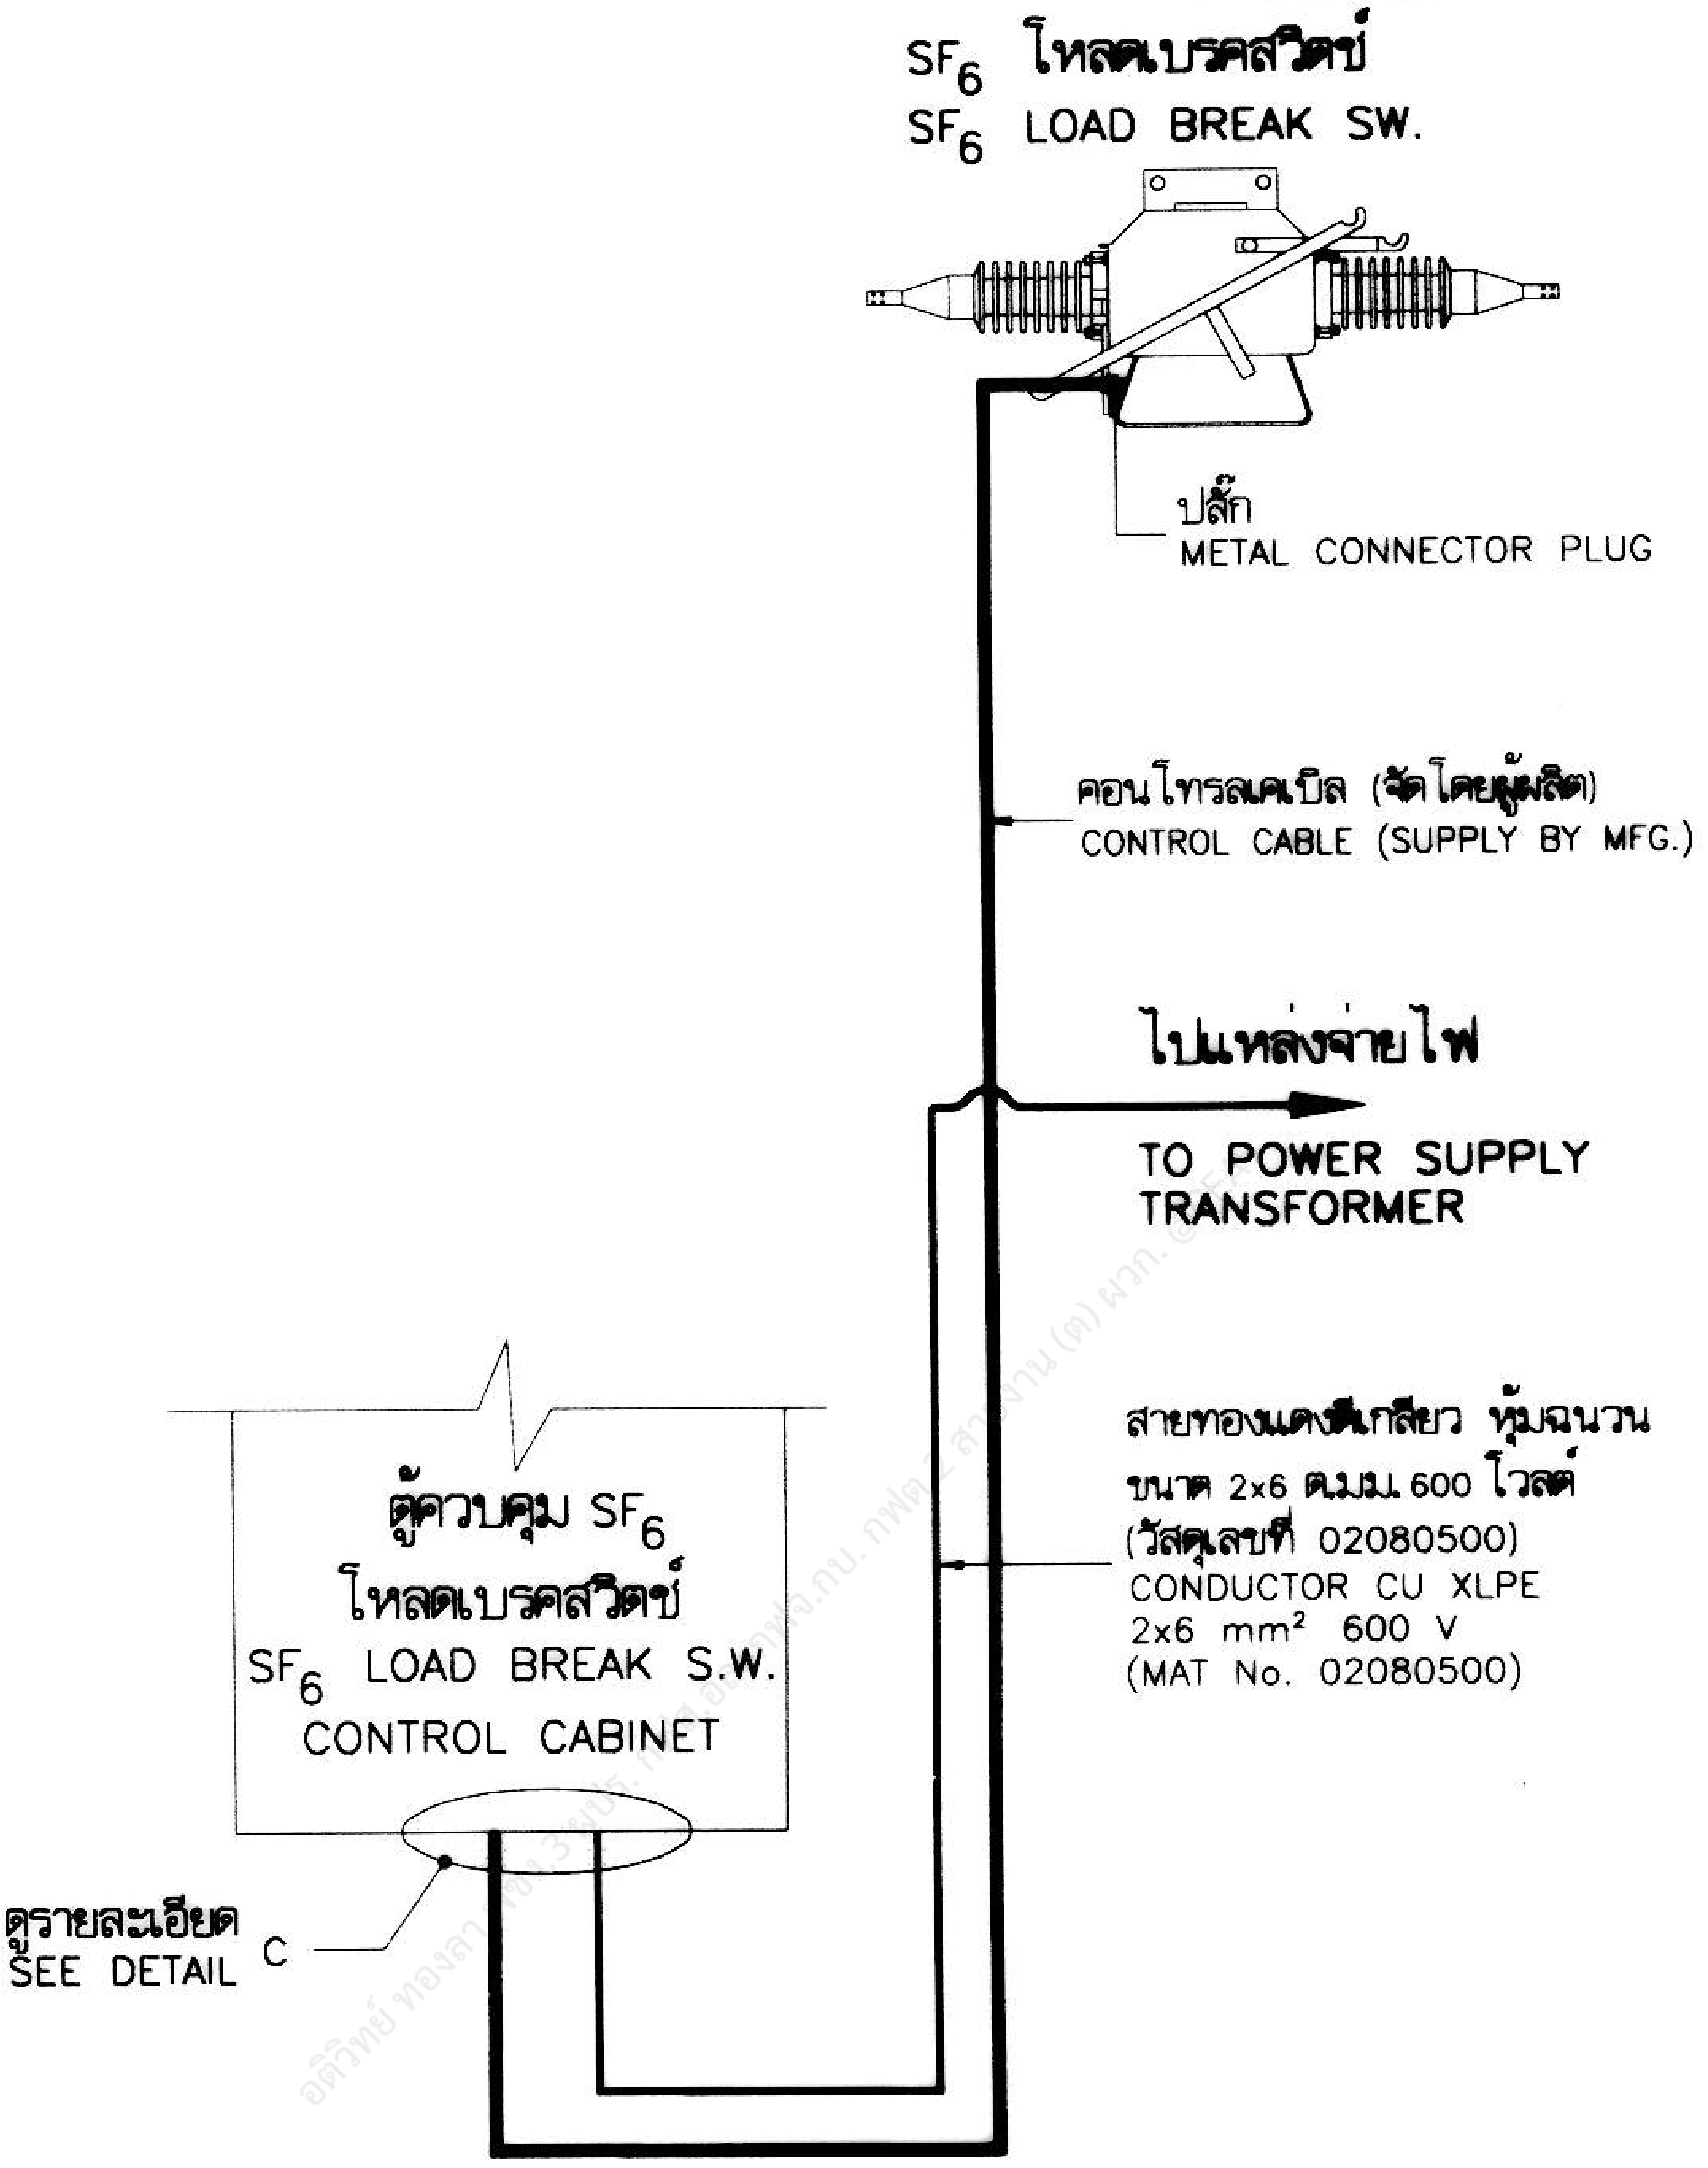
SF$_6$ โหลดเบรคสวิตช์
SF$_6$ LOAD BREAK SW.
ปลั๊ก
METAL CONNECTOR PLUG
คอนโทรลเคเบิล (จัดโดยผู้ผลิต)
CONTROL CABLE (SUPPLY BY MFG.)
ไปแหล่งจ่ายไฟ
TO POWER SUPPLY TRANSFORMER
สายทองแดงตีเกลียว หุ้มฉนวน
ขนาด 2x6 ต.มม. 600 โวลต์
(วัสดุเลขที่ 02080500)
CONDUCTOR CU XLPE
2x6 mm² 600 V
(MAT No. 02080500)
ตู้ควบคุม SF$_6$
โหลดเบรคสวิตช์
SF$_6$ LOAD BREAK S.W.
CONTROL CABINET
ดูรายละเอียด
SEE DETAIL C

แหล่งจ่ายไฟแหล่งเดียว
SINGLE POWER SOURCE

กองวิศวกรรมไฟฟ้าและเครื่องกล ฝ่ายวิศวกรรม	การไฟฟ้าส่วนภูมิภาค	ใช้แทนแบบ .... ถูกแทนโดยแบบ .... เขียนเสร็จวันที่ 31 ก.ค. 2539 แก้แบบวันที่ .... มิติเป็น มิลลิเมตร มาตราส่วน –
ผู้เขียน ศุภกิจ บุญเรือง ผู้สำรวจ .... วิศวกร .... หัวหน้าแผนก .... ผู้อำนวยการกอง .... ผู้อำนวยการฝ่าย	ผู้ว่าการ .... การติดตั้งชุดควบคุมการปลดสับ SF$_6$ โหลดเบรคสวิตช์	
รองผู้ว่าการ 14 ส.ค. 39	**CONTROL CABINET OF SF$_6$ LOAD BREAK SWITCH INSTALLATION**	แบบเลขที่ SA4–015/39015 แผ่นที่ 5 ของจำนวน 8 แผ่น

การประกอบเลขที่ 2431
ASSEMBLY NO. 3419

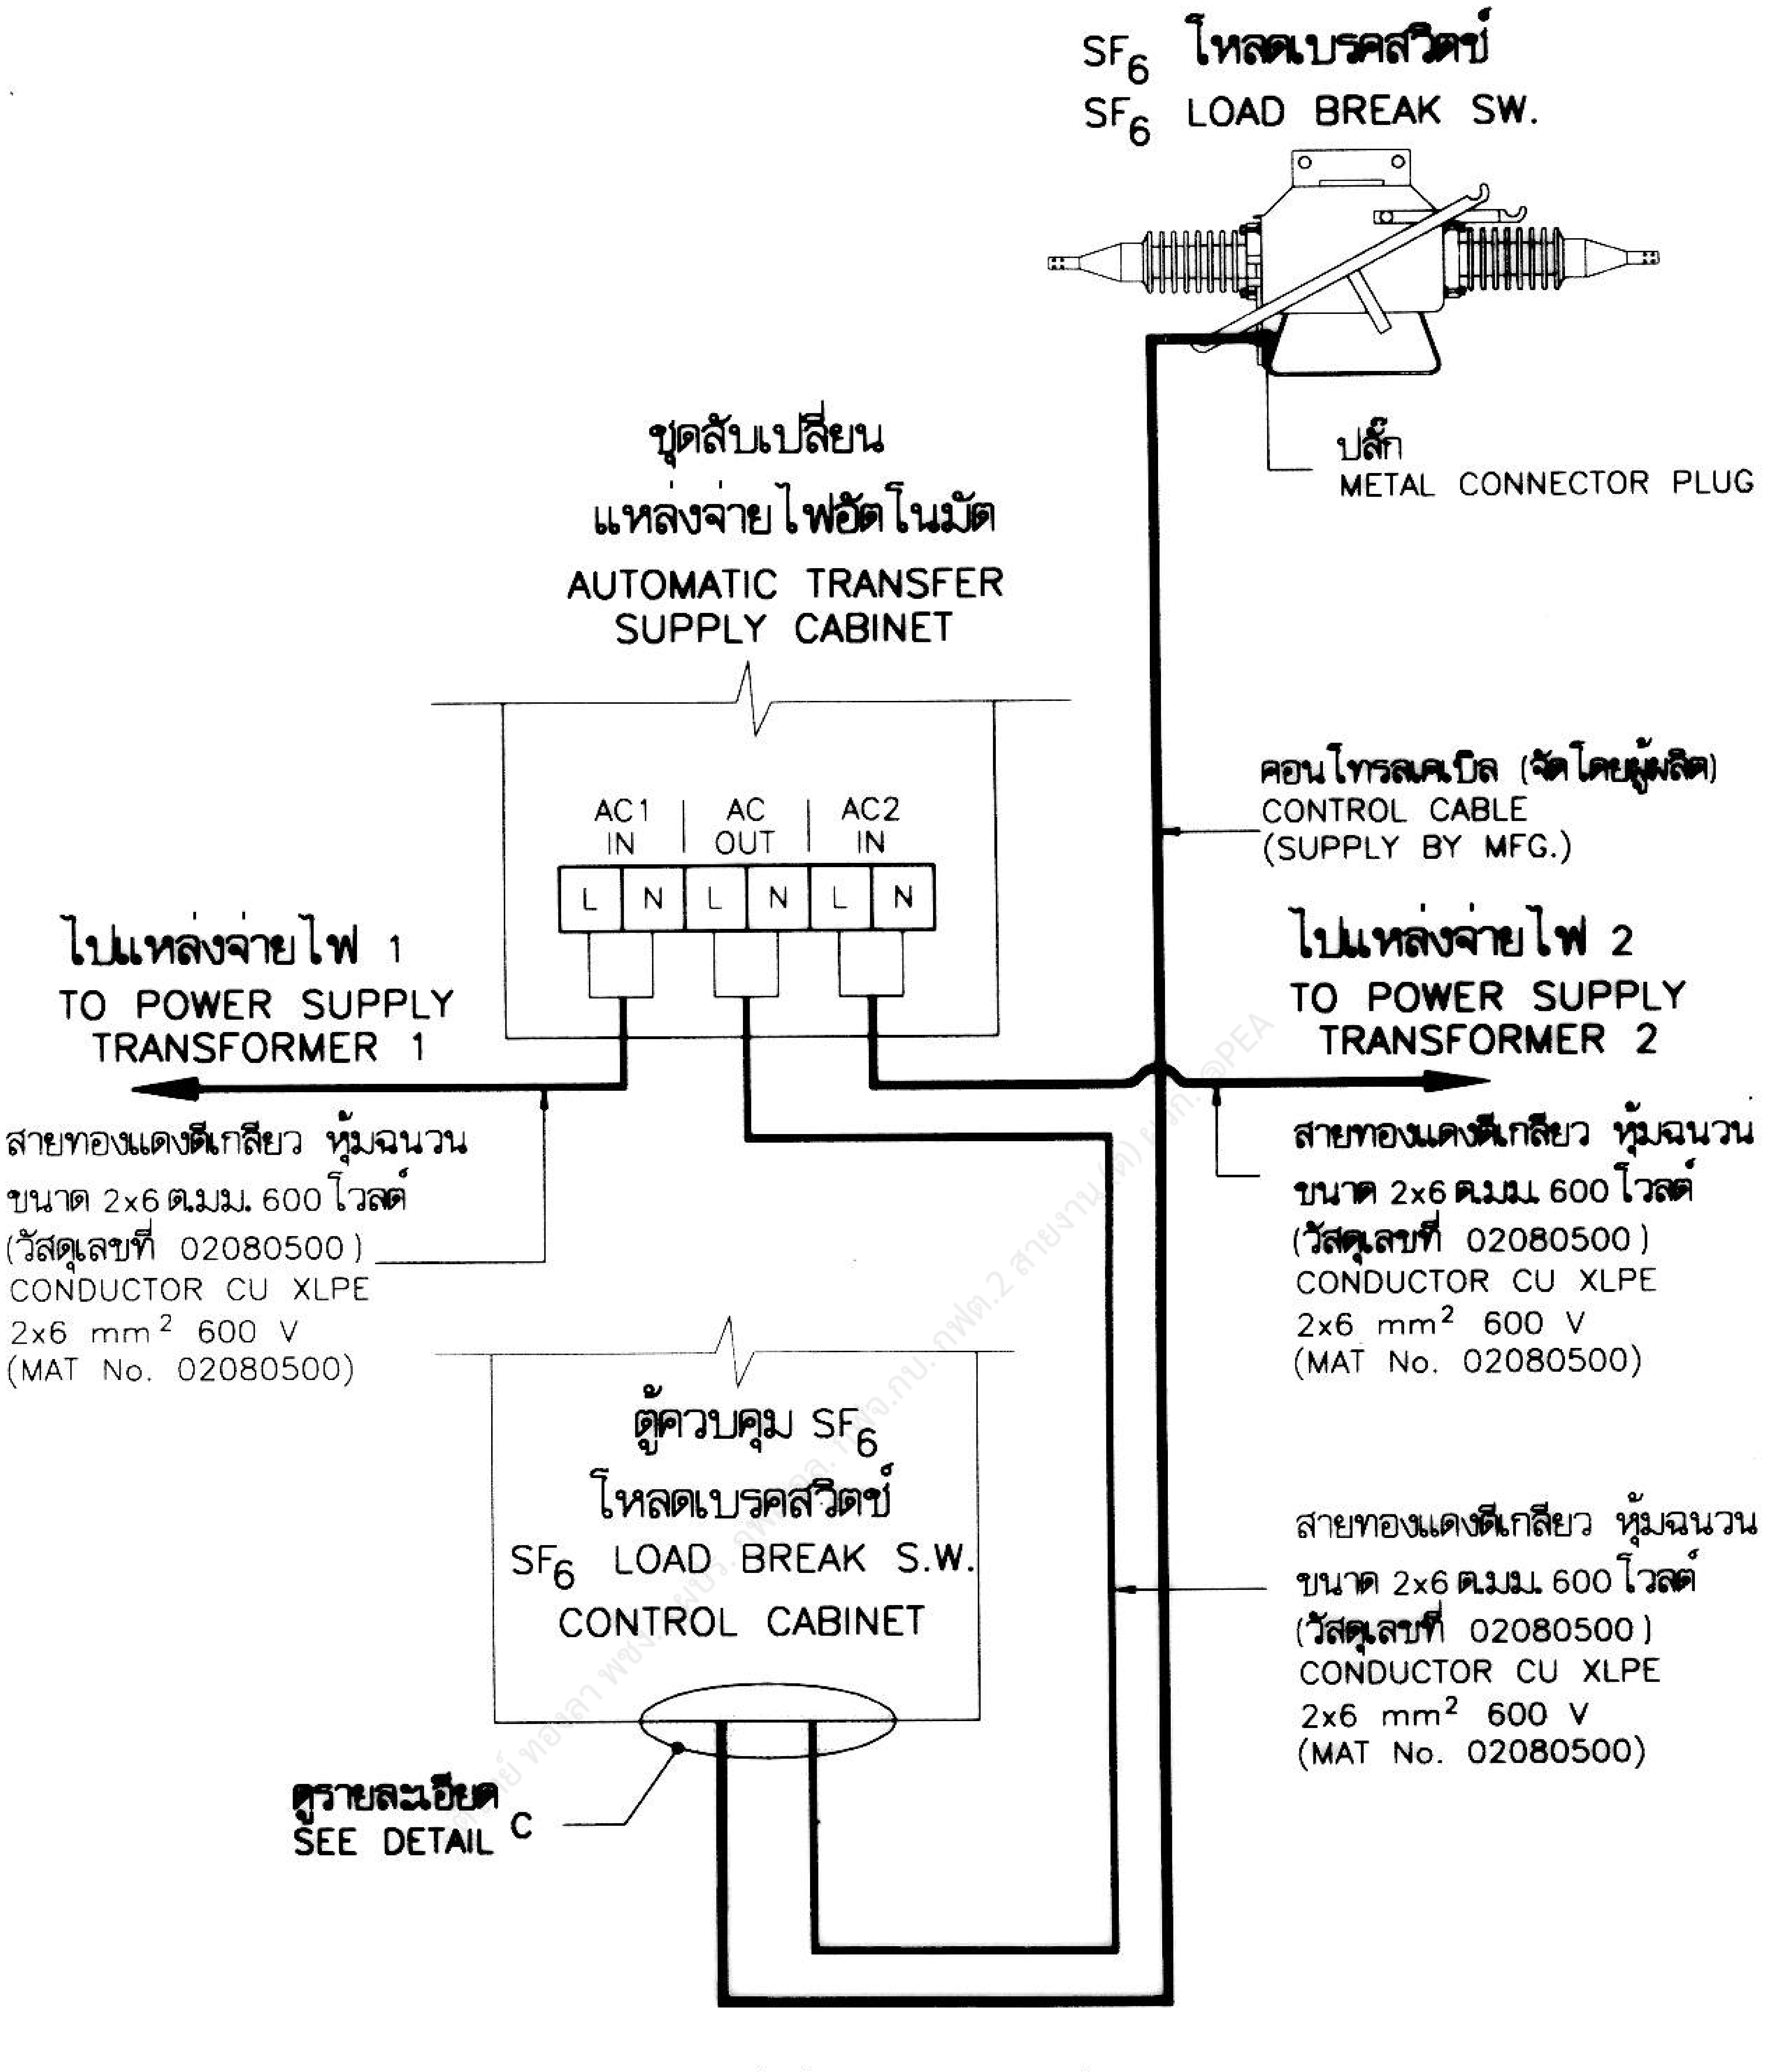

SF6 โหลดเบรคสวิตช์
SF6 LOAD BREAK SW.
ปลั๊ก
METAL CONNECTOR PLUG
ชุดสับเปลี่ยนแหล่งจ่ายไฟอัตโนมัติ
AUTOMATIC TRANSFER SUPPLY CABINET
AC1 IN
AC OUT
AC2 IN
L
N
L
N
L
N
คอนโทรลเคเบิล (จัดโดยผู้ผลิต)
CONTROL CABLE (SUPPLY BY MFG.)
ไปแหล่งจ่ายไฟ 1
TO POWER SUPPLY TRANSFORMER 1
ไปแหล่งจ่ายไฟ 2
TO POWER SUPPLY TRANSFORMER 2
สายทองแดงตีเกลียว หุ้มฉนวน ขนาด 2x6 ต.มม. 600 โวลต์ (วัสดุเลขที่ 02080500) CONDUCTOR CU XLPE 2x6 mm² 600 V (MAT No. 02080500)
สายทองแดงตีเกลียว หุ้มฉนวน ขนาด 2x6 ต.มม. 600 โวลต์ (วัสดุเลขที่ 02080500) CONDUCTOR CU XLPE 2x6 mm² 600 V (MAT No. 02080500)
ตู้ควบคุม SF6 โหลดเบรคสวิตช์
SF6 LOAD BREAK S.W. CONTROL CABINET
สายทองแดงตีเกลียว หุ้มฉนวน ขนาด 2x6 ต.มม. 600 โวลต์ (วัสดุเลขที่ 02080500) CONDUCTOR CU XLPE 2x6 mm² 600 V (MAT No. 02080500)
ดูรายละเอียด
SEE DETAIL C

แหล่งจ่ายไฟ 2 แหล่ง
TWO POWER SOURCE

กองวิศวกรรมไฟฟ้าและเครื่องกล
ฝ่ายวิศวกรรม

การไฟฟ้าส่วนภูมิภาค

ผู้เขียน ศุภกิจ บุญเรือง
ผู้สำรวจ
วิศวกร
หัวหน้าแผนก
ผู้อำนวยการกอง
ผู้อำนวยการฝ่าย
รองผู้ว่าการ

ผู้ว่าการ

การติดตั้งชุดควบคุมการปลดสับ SF$_6$ โหลดเบรคสวิตช์

CONTROL CABINET OF SF$_6$ LOAD BREAK SWITCH INSTALLATION

ใช้แทนแบบ
ถูกแทนโดยแบบ
เขียนเสร็จวันที่ 31 ก.ค. 2539
แก้แบบวันที่
มิติเป็น มิลลิเมตร
มาตราส่วน –
แบบเลขที่ SA4-015/39015
แผ่นที่ 6 ของจำนวน 8 แผ่น

การประกอบเลขที่ ASSEMBLY NO.	2431 3419

1. ชนิดที่สายควบคุมและสาย POWER SUPPLY มีปลั๊กประกอบมาด้วย
METAL CONNECTOR CABLE–PLUG TYPE

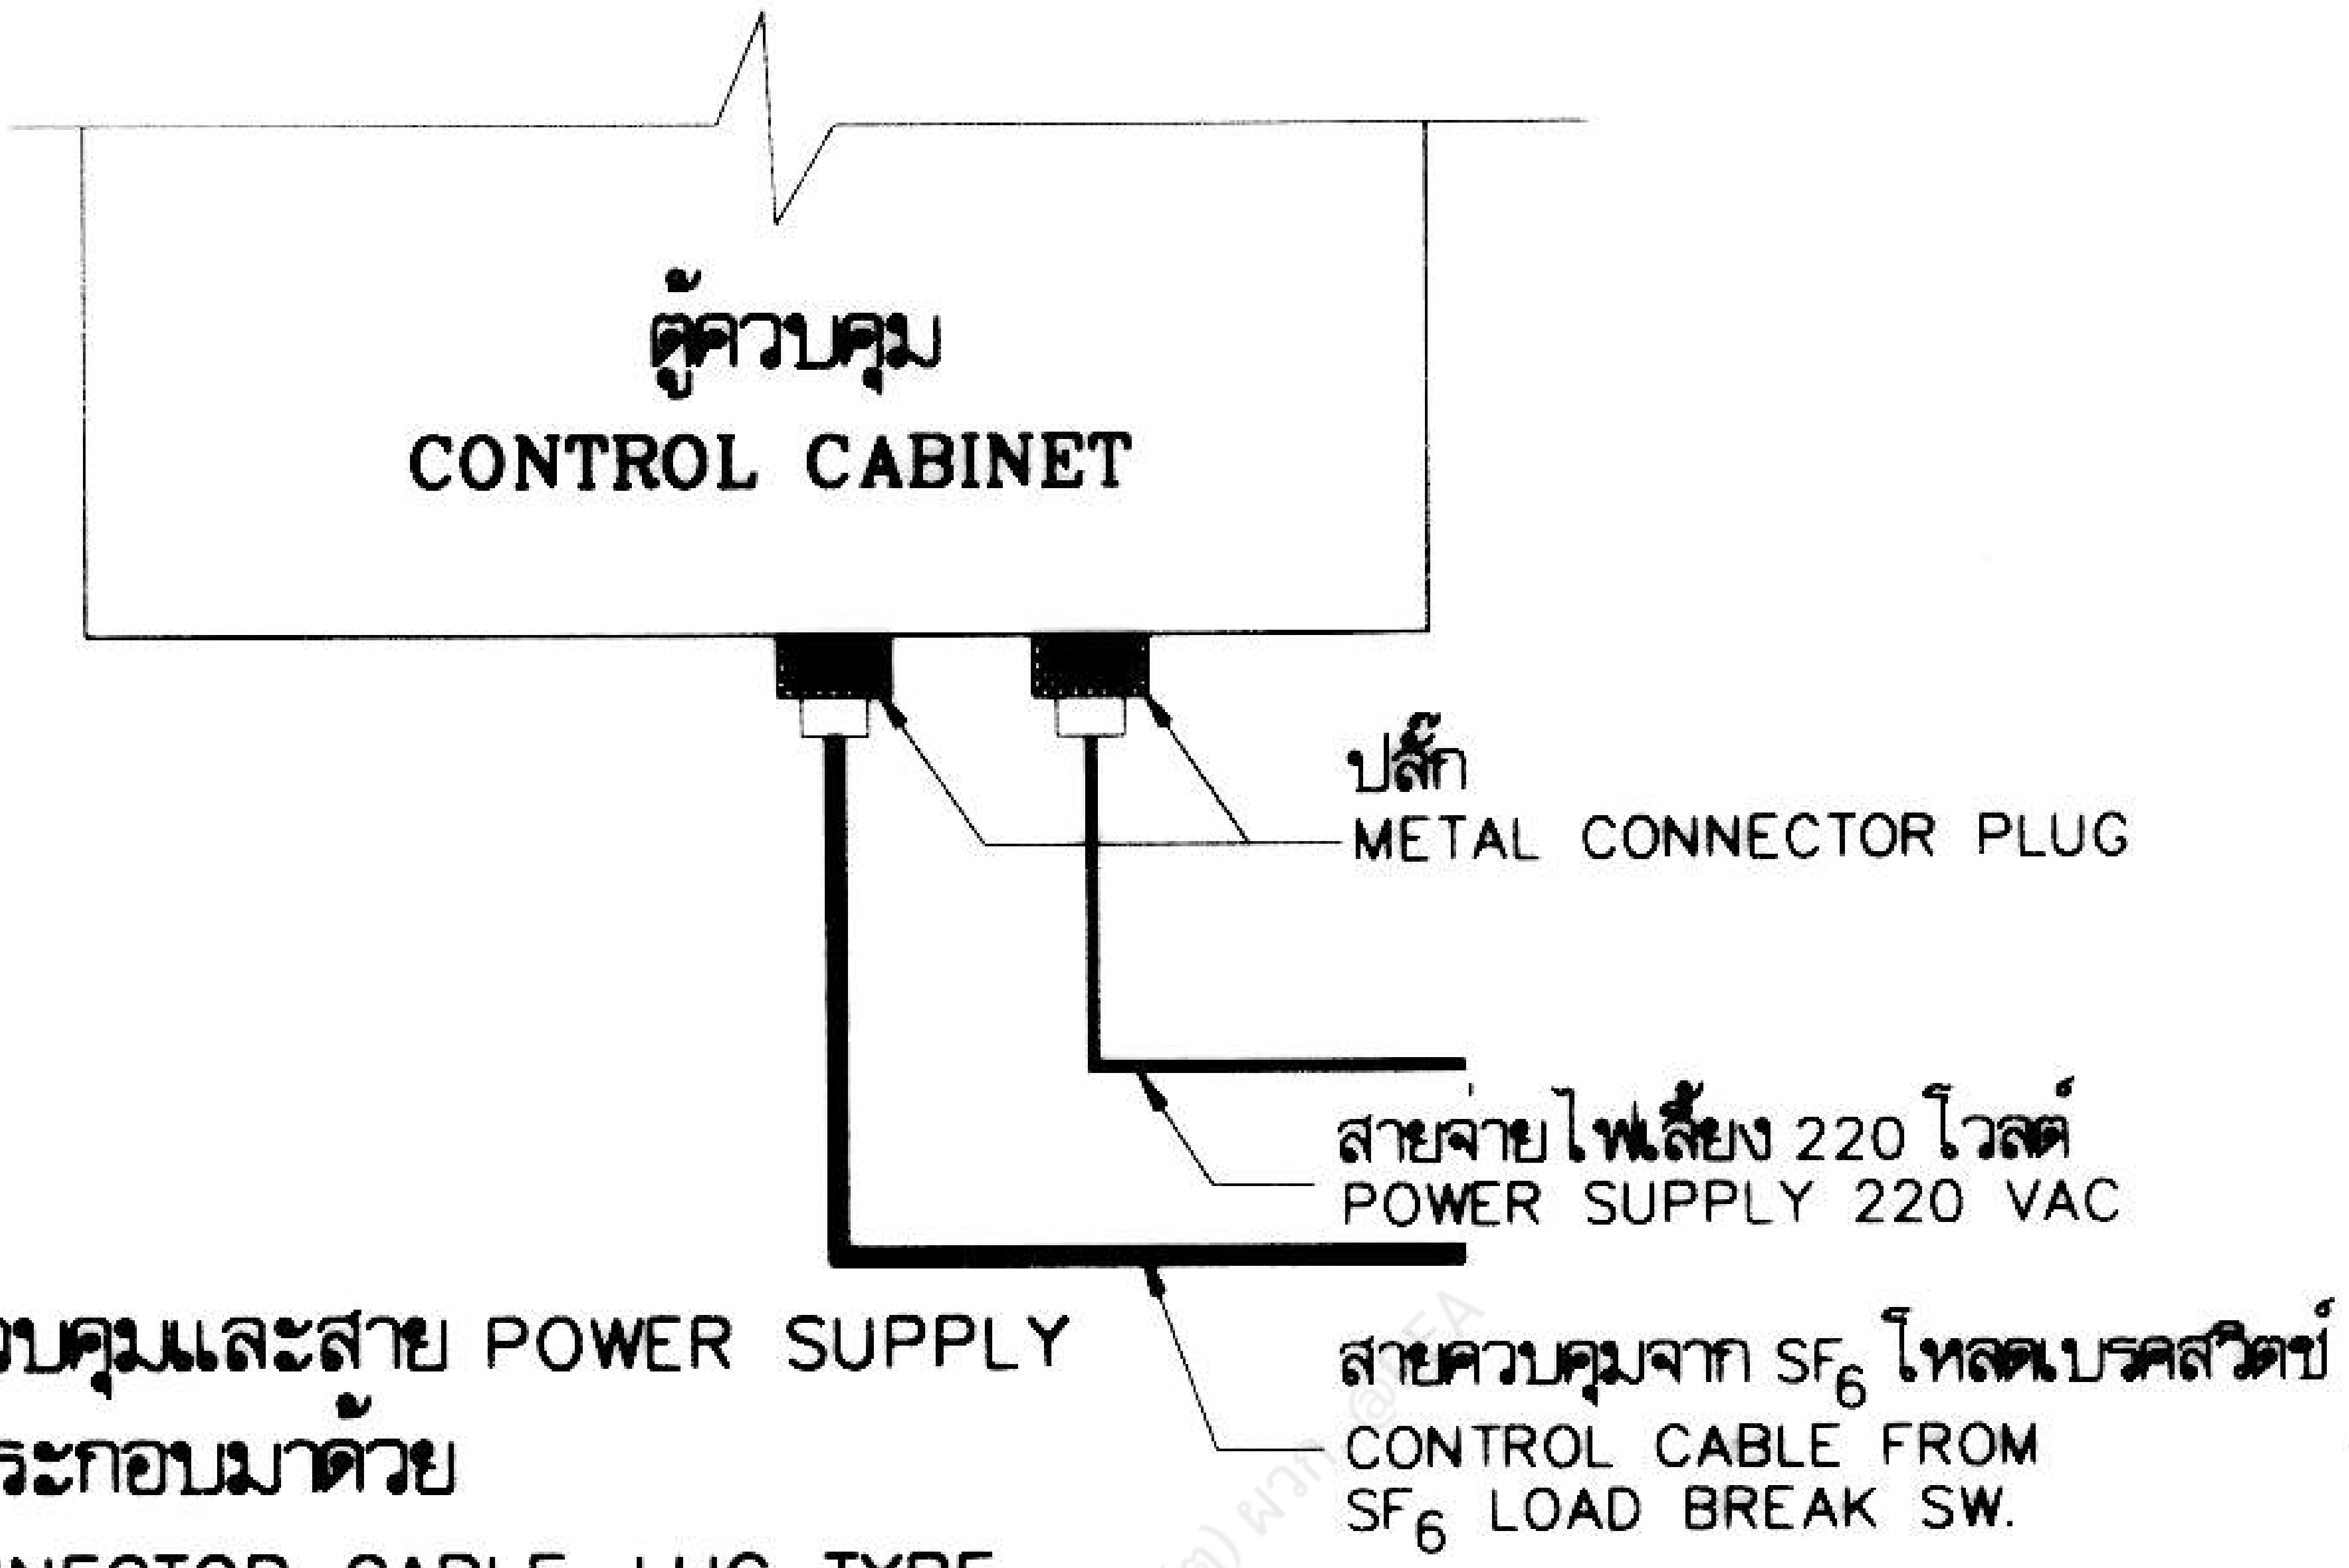
ตู้ควบคุม
CONTROL CABINET
ปลั๊ก
METAL CONNECTOR PLUG
สายจ่ายไฟเลี้ยง 220 โวลต์
POWER SUPPLY 220 VAC
สายควบคุมจาก SF6 โหลดเบรคสวิตช์
CONTROL CABLE FROM
SF6 LOAD BREAK SW.

2. ชนิดที่สายควบคุมและสาย POWER SUPPLY มีหางปลาประกอบมาด้วย
METAL CONNECTOR CABLE–LUG TYPE

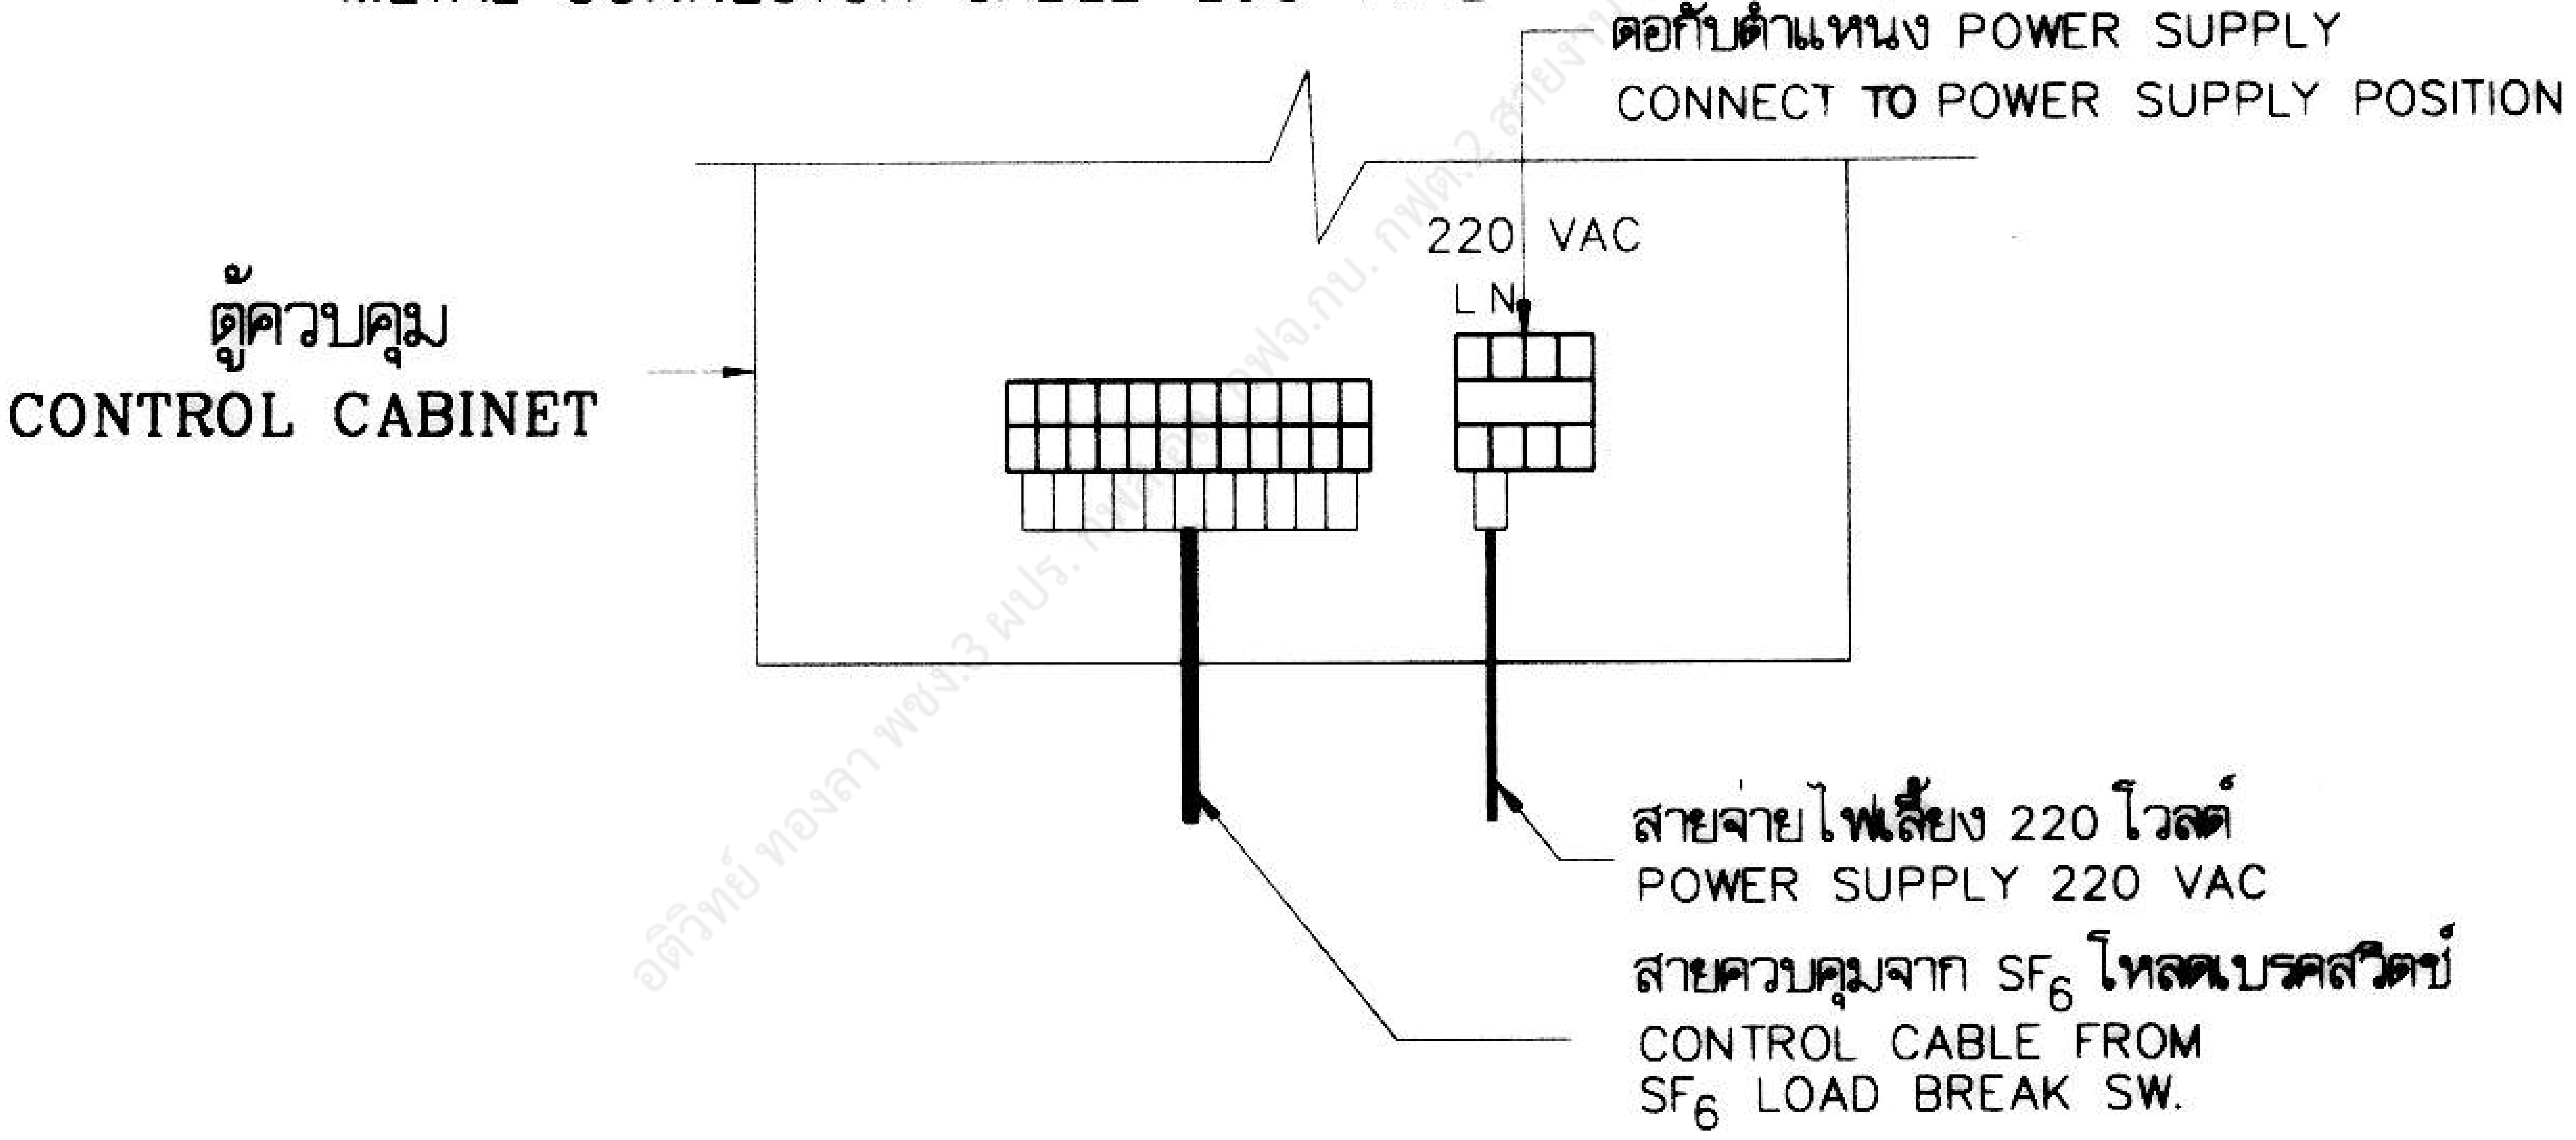
ต่อกับตำแหน่ง POWER SUPPLY
CONNECT TO POWER SUPPLY POSITION
220 VAC
L N
ตู้ควบคุม
CONTROL CABINET
สายจ่ายไฟเลี้ยง 220 โวลต์
POWER SUPPLY 220 VAC
สายควบคุมจาก SF6 โหลดเบรคสวิตช์
CONTROL CABLE FROM
SF6 LOAD BREAK SW.

รายละเอียด C
DETAIL

อดิวิทย์ ทองลา พชง.3 ผปร. กฟจ.กบ. กฟต.2 สายงาน (ต) ผวก. PEA

กองวิศวกรรมไฟฟ้าและเครื่องกล ฝ่ายวิศวกรรม	การไฟฟ้าส่วนภูมิภาค	ใช้แทนแบบ.................. ถูกแทนโดยแบบ............
ผู้เขียน ศุภกิจ บุญเรือง ผู้สำรวจ.......... วิศวกร.......... หัวหน้าแผนก.......... ผู้อำนวยการกอง.......... ผู้อำนวยการฝ่าย..........	ผู้ว่าการ.......... การติดตั้งชุดควบคุมการปลดสับ SF$_6$ โหลดเบรคสวิตช์	เขียนเสร็จวันที่ 31 ก.ค. 2539 แก้แบบวันที่ .... มิติเป็น มิลิเมตร มาตราส่วน –..........
รองผู้ว่าการ	**CONTROL CABINET OF SF$_6$ LOAD BREAK SWITCH INSTALLATION**	แบบเลขที่ SA4–015/39015 แผ่นที่ 7 ของจำนวน 8 แผ่น

การประกอบเลขที่ 2431
ASSEMBLY NO. 3419

	แบบอ้างอิง REFERENCE DRAWING	แบบเลขที่ DWG.No.	การประกอบเลขที่ ASSEMBLY NO.
1	การติดตั้ง SF$_6$ สวิตช์เปิดปิดได้เมื่อมีโหลด 22 หรือ 33 kV ในระบบจำหน่าย 22 OR 33 kV LOAD BREAK SWITCH INSTALLATION IN DISTRIBUTION LINE	SA1-015/34005 SA1-015/34006	2430 3417
2	การติดตั้งหม้อแปลง 1 เฟส 19 หรือ 22 kV 1-PHASE TRANSFORMER INSTALLATION, 19 OR 22 kV	SA1-015/25017 SA1-015/26007 SA1-015/20075 SA1-015/26008 SA1-015/31011 SA1-015/34009	2701 2701B 3701 3101B 3701C 3701D
3	การประกอบสายคอนโทรลเคเบิล กับเสา คอร. CONTROL CABLE ASSEMBLY ON CONCRETE POLE	S02-015/19166 SA1-015/31012 S02-015/19128 SA1-015/31013	9703 9703A 9704 9704A
4	การประกอบสายคอนโทรลเคเบิล และสายทองแดงตีเกลียวหุ้มฉนวน กับเสา คอร. CONTROL CABLE AND CONDUCTOR, CU, ASSEMBLY ON CONCRETE POLE	SA1-015/21039	0518
5	การต่อสายลงดินระบบแรงสูงและแรงต่ำ สำหรับอุปกรณ์ในระบบจำหน่าย และสายระบบจำหน่าย (พร้อมเครื่องวัดแรงต่ำ) H.T. AND L.T. EARTHING SYSTEM FOR DISTRIBUTION EQUIPMENT AND DISTRIBUTION LINE (WITH L.T. METERING)	S02-015/20039	9701

หมายเหตุ :

1. การติดตั้งในลักษณะนี้ เป็นการติดตั้งในกรณีที่ไม่มีสายแรงต่ำพาดผ่านแต่จำเป็นต้องมีแหล่งจ่ายไฟเพื่อจ่ายให้ชุดควบคุมการปลดสับ
2. ในกรณีที่มีสายแรงต่ำพาดผ่านอยู่แล้ว ไม่ต้องติดตั้งหม้อแปลงในแบบที่ 1 และด้านใดด้านหนึ่งของแบบที่ 2
3. สำหรับสายไฟเลี้ยง กรณีระยะระหว่างเสาต้นติดตั้ง SF$_6$ โหลดเบรคสวิตช์ และเสาต้นติดตั้งหม้อแปลงเกิน 80 ม. ให้ปักเสา 9 ม. แซมกลางช่วงเสา

NOTES :

1. THIS INSTALLATION FOR USE IN CASE OF NO L.T. LINE PASSING, BUT NEED TO HAVE POWER SUPPLY FOR CONTROL CABINET.
2. TRANSFORMER IN TYPE 1 OR ANY SIDE OF TYPE 2 SHALL NOT BE INSTALLED IN CASE OF L.T. LINE PASSING.
3. FOR AC-SUPPLY LINE, IN CASE OF SPAN LENGHT BETWEEN SF$_6$ LOAD BREAK SWITCH AND TRANSFORMER POLE **EXCEEDED 80** m, 9 m CONCRETE POLE SHALL BE INSTALLED AT MID SPAN.

กองวิศวกรรมไฟฟ้าและเครื่องกล
ฝ่ายวิศวกรรม

ผู้เขียน ศุภกิจ บุญเรือง
ผู้สำรวจ
วิศวกร
หัวหน้าแผนก
ผู้อำนวยการกอง
ผู้อำนวยการฝ่าย

รองผู้ว่าการฯ

การไฟฟ้าส่วนภูมิภาค

ผู้ว่าการ

การติดตั้งชุดควบคุมการปลดสับ SF$_6$ โหลดเบรคสวิตช์

CONTROL CABINET OF SF$_6$ LOAD BREAK SWITCH INSTALLATION

ใช้แทนแบบ
ถูกแทนโดยแบบ
เขียนเสร็จวันที่ 31 ก.ค. 2539
แก้แบบวันที่
หน่วยเป็น มิลลิเมตร
มาตราส่วน -

แบบเลขที่ SA4-015/39015
แผ่นที่ 8 ของจำนวน 8 แผ่น