

การประกอบเลขที่ ASSEMBLY NO. 3801

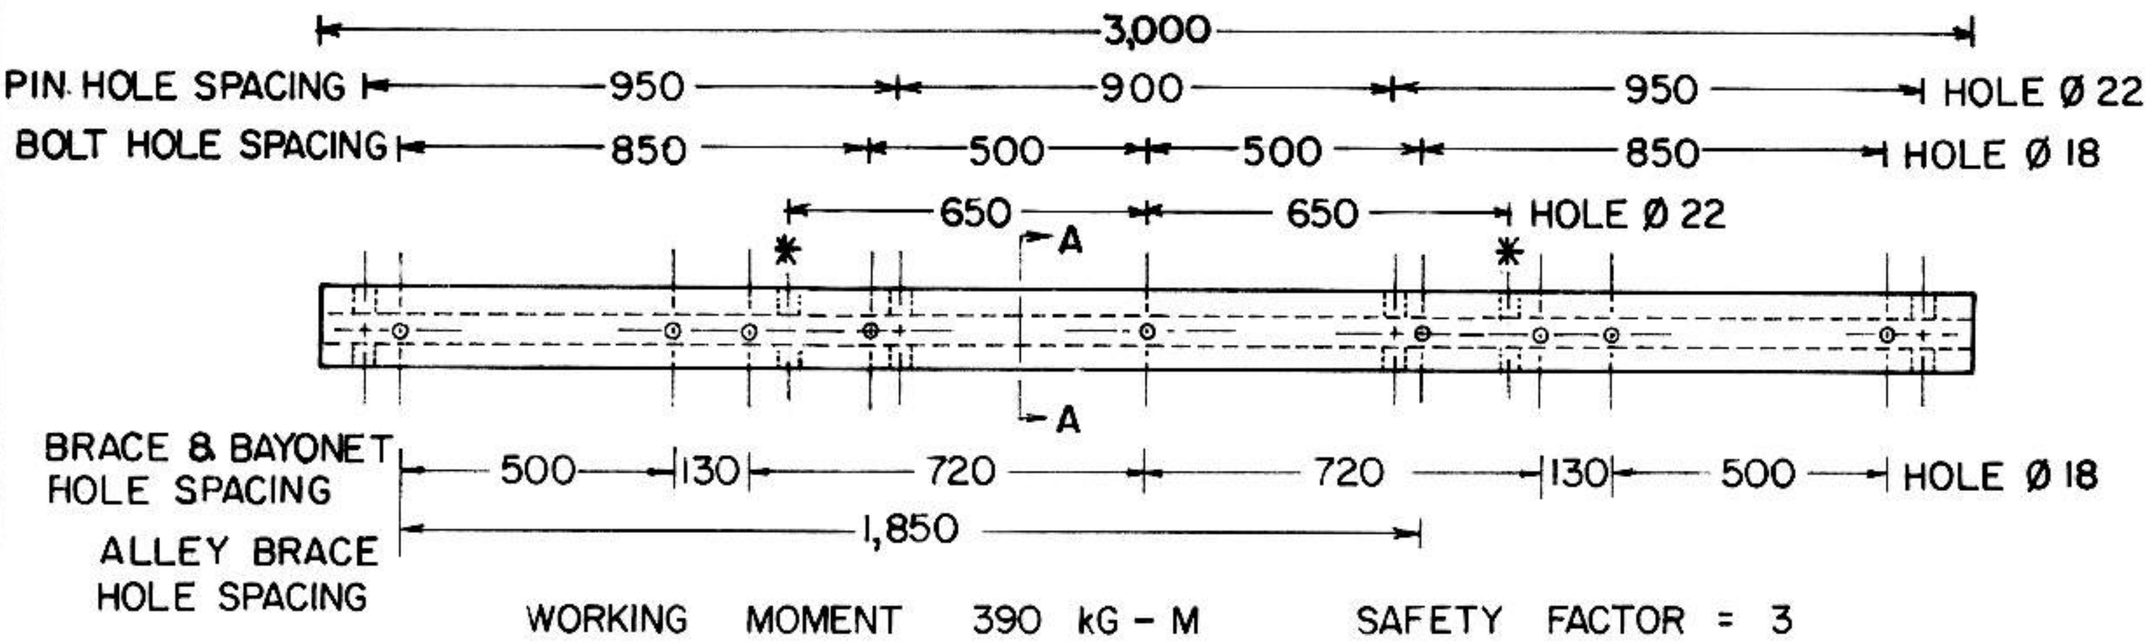


WORKING MOMENT 390 kG – M SAFETY FACTOR = 3

รูปตัด SECTION A – A

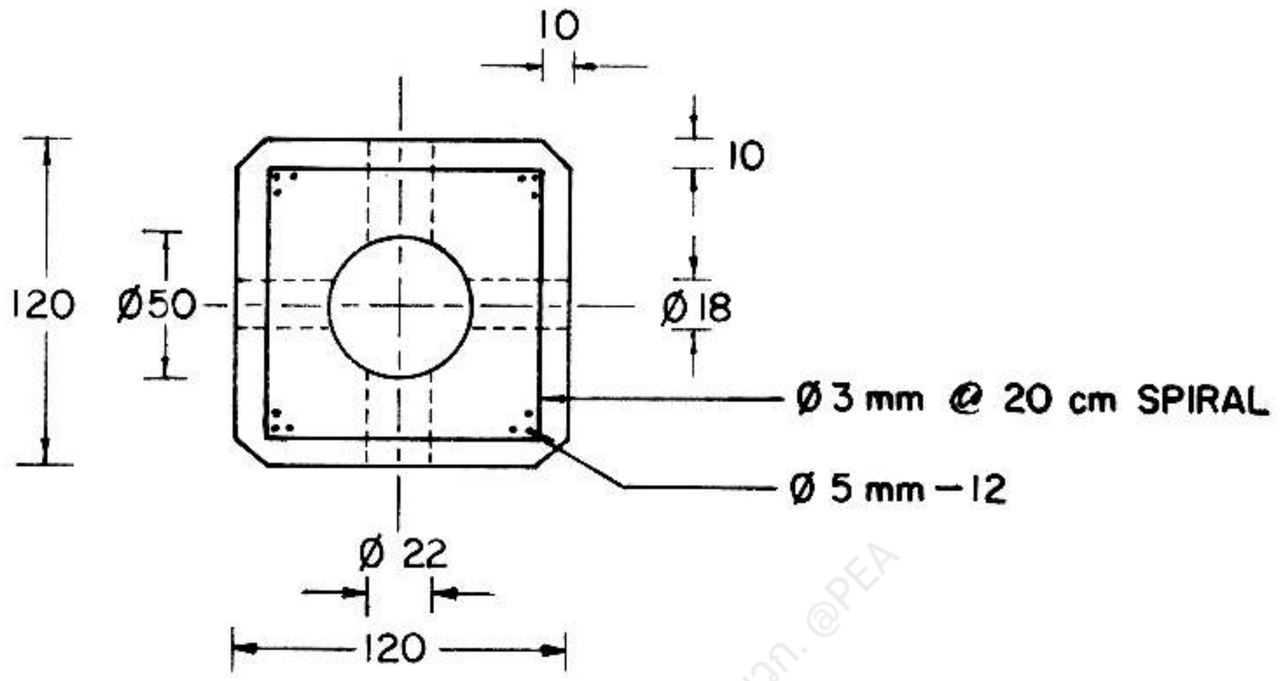


คอน คอนกรีตอัดแรงแบบสปัน ขนาด 120 X 120 X 3,000 มม. (จัดคุเลขที่ 0104)

1 ติดตั้งกันเสาคอนกรีต เป็นคอนพาดสายในระบบจำหน่าย 33 kV ให้จัดทำสายดินลวดเหล็กกลม เส้นเดี่ยว ขนาด Ø 4 มม. ต่อระหว่างก้านลูกถ้วยทุกอัน แล้วต่อลงดินที่จุดเชื่อมสายล่อฟ้ากับสายดิน ที่หัวเสา

2 ติดตั้งกันเสาคอนกรีต เป็นที่รับสายล่อฟ้า ระบบ 33 kV ใช้งานได้ดังรายละเอียด ตามแบบเลขที่ SAI-015/21029

3 เป็นคอนพาดสายในแนวทางตรง และทางโค้งไม่เกิน 30°

4 * ใช้ติดตั้งลูกถ้วยก้านตรง เฉพาะเมื่อประกอบบนเสา คอร. ขนาด 22 ม. เท่านั้น

SPUN PRESTRESSED CONCRETE CROSSARM, 120 X 120 X 3,000 mm (MAT. NO. 0104)

1 FOR MOUNTING ON CONCRETE POLE AS 33 kV CROSSARM : BOND ALL THE INSULATOR PINS BY A SOLID STEEL WIRE Ø 4 mm CONNECTED TO THE OVERHEAD GROUND WIRE AND GROUND LEAD AT THE TOP OF THE POLE.

2 FOR MOUNTING ON CONCRETE POLE AS 33 kV OVERHEAD GROUND WIRE BAYONET : DETAIL OF THE APPLICATION IS ACCORDING TO DRAWING NO. SAI-015/21029 .

3 AS CROSSARM FOR TANGENT AND ANGLE STRUCTURE NOT EXCEEDING 30°.

4 * USE FOR PIN TYPE INSULATOR ASSEMBLY ONLY ON 22 m CONCRETE POLE .

| | | |
|---|---|---|
| กองวิศวกรรม | การไฟฟ้าส่วนภูมิภาค | ใช้แทนแบบ ..... |
| ผู้เขียน ..... | ผู้ว่าการ ..... 5/มิ.ย.20 | ถูกแทนโดยแบบ ..... |
| ผู้สำรวจ ..... | | เขียนเสร็จวันที่ 16 มี.ค. 20 |
| วิศวกร ..... | คอน คอนกรีตอัดแรงแบบสปัน (คอน คอร. สปัน) | แก้แบบวันที่ 5 ก.พ. 24, 24 เม.ย. 21, 28 มี.ค. 27, 28 ก.ค. 36 |
| หัวหน้าแผนก ..... | 120 X 120 X 3,000 มม. | มิติเป็น มม. |
| หัวหน้ากอง ..... | | มาตราส่วน 1:5 , 1:25 |
| รองผู้ว่าการฝ่ายเทคนิค ..... | SPUN PRESTRESSED CONCRETE CROSSARM 120 X 120 X 3,000 mm | แบบเลขที่ S02-015/20043 |
| | | แผ่นที่ 1 ของจำนวน 1 แผ่น |