การประกอบเลขที่ ASSEMBLY NO. 5687 F

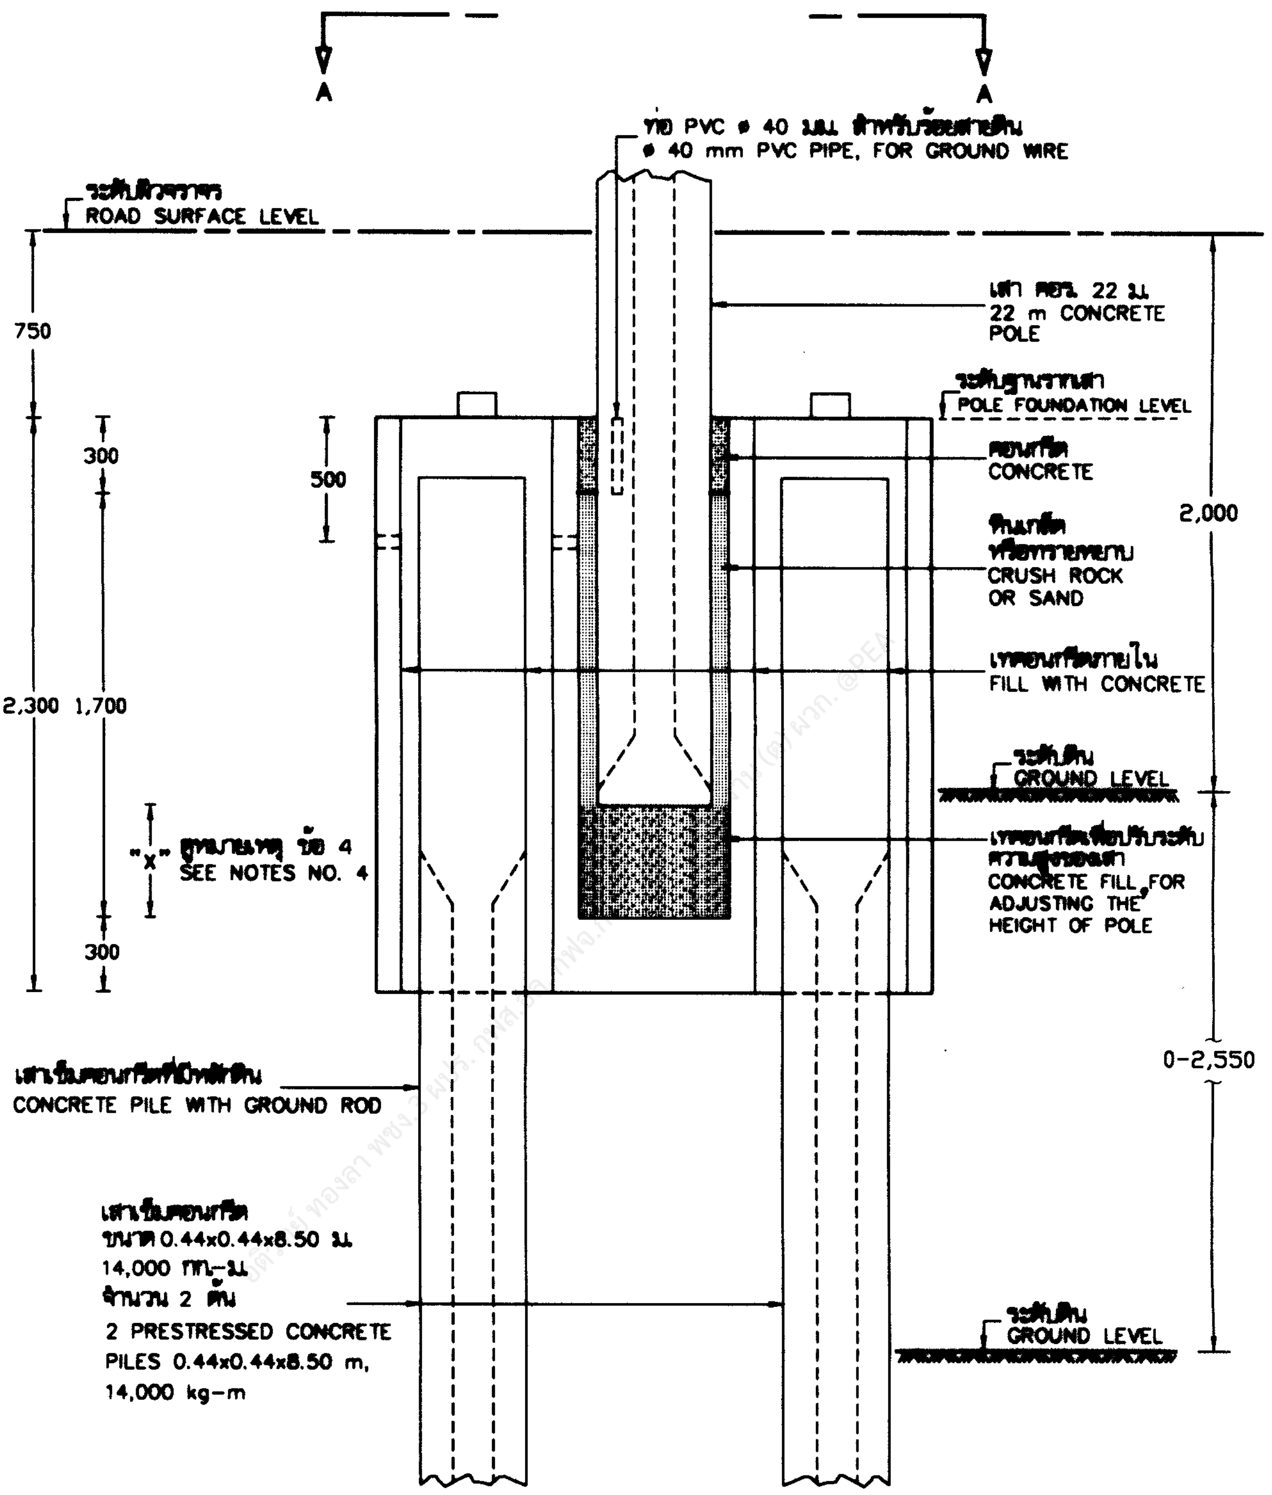

กองมาตรฐานระบบไฟฟ้า
ฝ่ายมาตรฐานและความปลอดภัย

ผู้เขียน ...สมชาย...
ผู้ตรวจ ....
วิศวกร ...
หัวหน้าแผนก ...
ผู้อำนวยการกอง ...
ผู้อำนวยการฝ่าย ...

รองผู้ว่าการวางแผนและพัฒนาระบบไฟฟ้า

การไฟฟ้าส่วนภูมิภาค

ผู้ว่าการ ....

รายละเอียดที่ 10ก 23 ก.ย. 2547
ฐานรากเสา (แบบที่ 20 ชนิดสำเร็จรูป)

DETAIL 10A
POLE FOUNDATION (TYPE 20, PRECAST TYPE)

ใช้แทนแบบ SA1-015/45015
ถูกแทนโดยแบบ ....
เขียนเสร็จวันที่ 10 มี.ค. 2547
แก้แบบวันที่ ....
หน่วย มิลลิเมตร
มาตราส่วน 1:30
แบบเลขที่ SA1-015/47023
แผ่นที่ 1 ของจำนวน 2 แผ่น

23 ก.ย. 2547

การประกอบเลขที่ ASSEMBLY NO.	5687 F

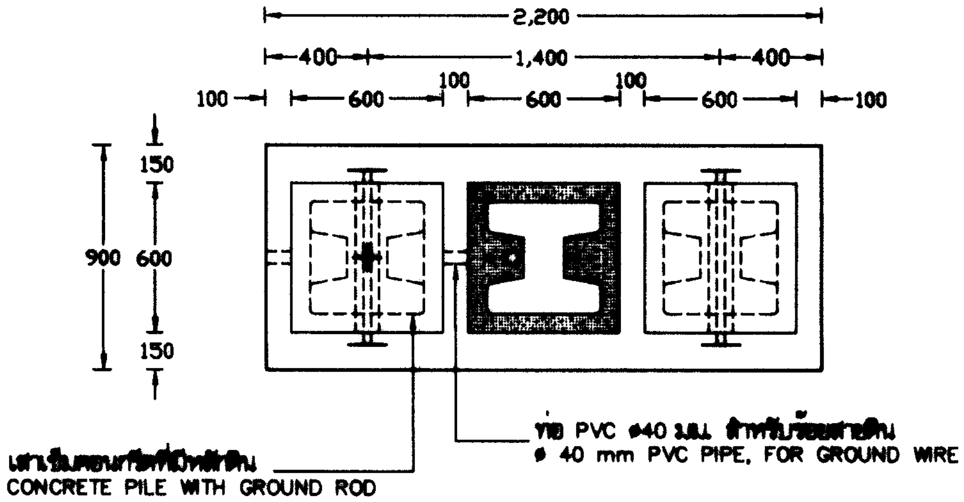
2,200
400
1,400
400
100
600
100
600
100
600
100
900
150
600
150
ท่อ PVC ⌀40 มม. สำหรับร้อยสายดิน
⌀ 40 mm PVC PIPE, FOR GROUND WIRE
เสาเข็มคอนกรีตที่มีหลักดิน
CONCRETE PILE WITH GROUND ROD

รูปตัด
SECTION A–A

หมายเหตุ

1 ใช้ในกรณีทางตรงหรือทางโค้ง ที่ไม่มีสายยึดโยง (กรณีพื้นที่ก่อสร้างฐานรากเสามีระดับต่ำกว่าระดับผิวจราจร 2.00-4.55 ม.)
2 ดูรายละเอียดเพิ่มเติมใน แบบเลขที่ IB2–011/44015
3 ดูข้อกำหนดการติดตั้งฐานรากเสาในเขตทางหลวง ตามแบบเลขที่ SA1–015/43012 (การประกอบเลขที่ 5687)
4 ระยะ "X"= 450 มม. สำหรับการก่อสร้างฐานรากเสา ในพื้นที่ทางหลวงที่ไม่มีทางเท้า ส่วนพื้นที่อื่นๆ ระยะ "X"= 0 มม.

NOTES

1 USE FOR STRAIGHT OR ANGLE LINE WITHOUT GUY (IN CASE OF GROUND SURFACE LEVEL IS BETWEEN 2.00–4.55 m LOWER THAN ROAD SURFACE LEVEL) .
2 SEE ADDITIONAL DETAIL, DWG. NO. IB2–011/44015 .
3 SEE RECOMMENDATION, FOR POLE FOUNDATION INSTALLATION IN HIGHWAY AREA, DWG. NO SA1–015/43012 (ASSEMBLY NO. 5687) .
4 THE "X" IS 450 mm HEIGHT FOR FOUNDATION CONSTRUCTION IN HIGHWAY AREA WHICH HAVE NO PAVEMENT, OTHER AREA THE "X" IS ZERO .

กองมาตรฐานระบบไฟฟ้า ฝ่ายมาตรฐานและความปลอดภัย	การไฟฟ้าส่วนภูมิภาค	ใช้แทนแบบ SA1–015/45015 ถูกแทนโดยแบบ ....
ผู้เขียน ..สมชาย.......... ผู้ตรวจ .... วิศวกร .... หัวหน้าแผนก .... ผู้อำนวยการกอง .... ผู้อำนวยการฝ่าย	ผู้ว่าการ .... รายละเอียดที่ 10A 23 ก.ย. 47 ฐานรากเสา (แบบที่ 20 ชนิดสำเร็จรูป)	เขียนเสร็จวันที่ .10 ส.ค. 2547. แก้แบบวันที่ .... มิติเป็น .มิลลิเมตร.......... มาตราส่วน .....1:30..........
รองผู้ว่าการวางแผนและพัฒนาระบบไฟฟ้า	DETAIL 10A POLE FOUNDATION (TYPE 20, PRECAST TYPE)	แบบเลขที่ .SA1–015/47023. แผ่นที่ .2. ของจำนวน .2. แผ่น

23 ก.ย. 2547