
การประกอบเลขที่ ASSEMBLY NO.	0209


สายเป็นกลาง
N – NEUTRAL LINE

สายเฟส
A,B,C – PHASE LINE

สายดับไฟถนน
L – STREET LIGHTING LINE

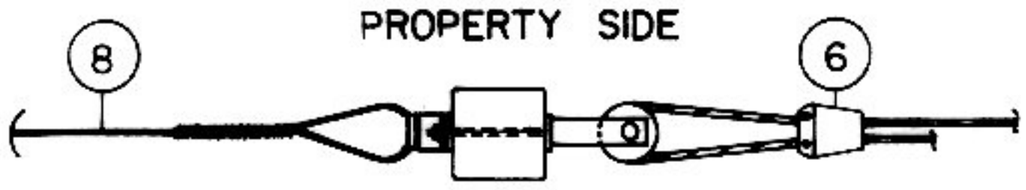

ด้านถนน
STREET SIDE

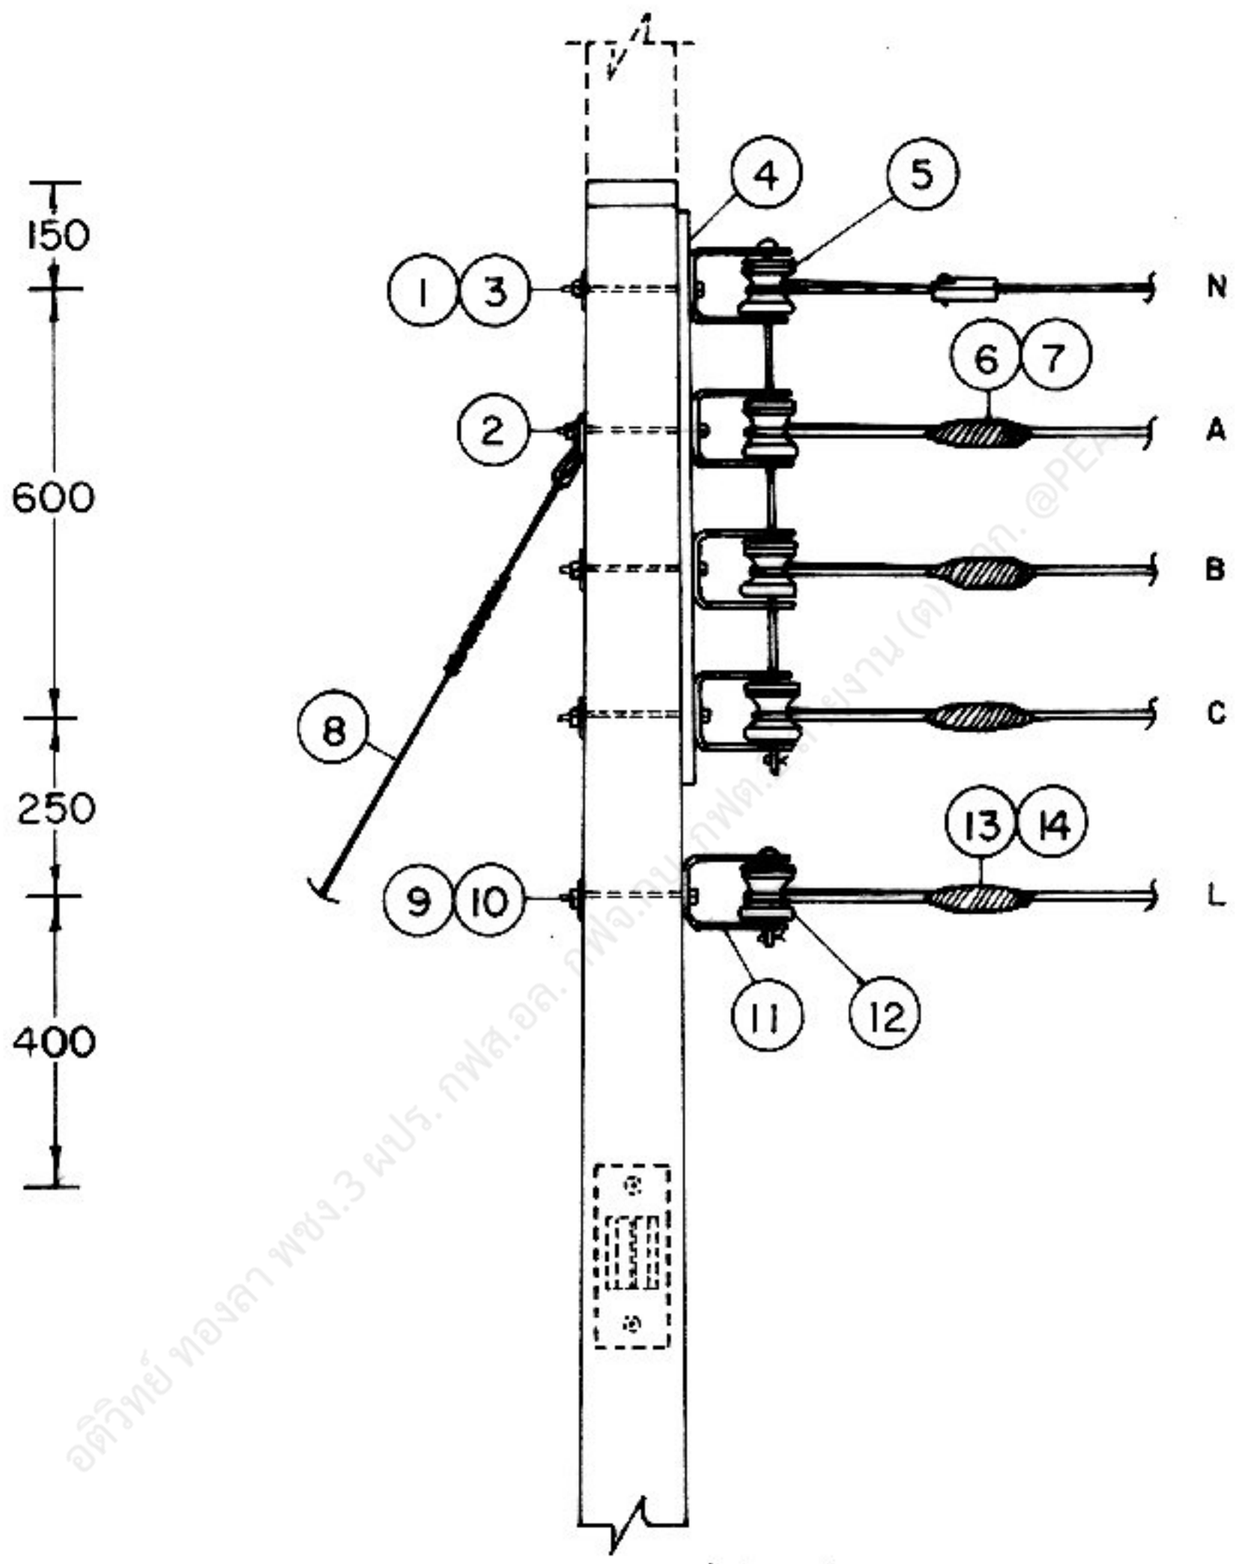

แบบ 3 เฟส 4 สาย
3-PHASES 4-WIRES

หมายเหตุ- ให้พันหุ้มคอนเนคเตอร์เข้าปลายสายสำหรับสายหุ้มฉนวนด้วย PVC เทป

NOTE: DEADEND CONNECTOR FOR INSULATED CONDUCTOR SHALL BE INSULATED WITH PVC TAPE.

กองวิศวกรรมไฟฟ้าและเครื่องกล ฝ่ายวิศวกรรม	การไฟฟ้าส่วนภูมิภาค	ใช้แทนแบบ ถูกแทนโดยแบบ เขียนเสร็จวันที่ 15 สค. 21 แก้แบบวันที่ มิติเป็น มม. มาตราส่วน 1:20
ผู้เขียน ผู้สำรวจ วิศวกร หัวหน้าแผนก หัวหน้ากอง ผู้อำนวยการฝ่าย	ผู้ว่าการ การติดตั้งแร็คแรงต่ำกับเสาคอนกรีต 9 ม. สำหรับเข้าปลายสายเสาต้นสุดท้าย	
รองผู้ว่าการฝ่ายเทคนิค	SECONDARY RACK INSTALLATION ON 9m CONCRETE POLE FOR DEADEND STRUCTURE	แบบเลขที่ SAI-015/21045 แผ่นที่ 1 รวมจำนวน 2 แผ่น

การประกอบเลขที่ ASSEMBLY NO. 0209

บัญชีวัสดุ
BILL OF MATERIAL

ลำดับที่ ITEM	รายละเอียด DESCRIPTION	จำนวน REQ'D	วัสดุเลขที่ MAT. NO.
1	สลักเกลียว M 16 X 170 มม. BOLT, MACHINE , M 16 X 170 mm	3	01110201
1a	สลักเกลียว M 16 X 250 มม. สำหรับเสาคอนกรีต 12 ม. BOLT, MACHINE , M 16X 250 mm FOR 12 m CONCRETE POLE	3	01110203
2	สลักเกลียว M 16X 200 มม. BOLT, MACHINE , M 16X200 mm	1	01110202
2a	สลักเกลียว M 16X250 มม. สำหรับเสาคอนกรีต 12 ม. BOLT, MACHINE , M 16X250 mm FOR 12 m CONCRETE POLE	1	01110203
3	แหวนสี่เหลี่ยมแบน 52 X 52X4.5 มม.รู Ø 18 มม. มอก. 258 WASHER, SQUARE , FLAT 52X52X 4.5mm HOLE Ø 18 mm TIS 258	3	01180100
4	แร็ค 4 X 200 มม. แบบหลังผึ่น RACK, SECONDARY, MEDIUM PRESSED STEEL 4X 200 mm EXTENSION BACK	1	03130002
5	ลูกรอกแรงต่ำ มอก. 227 แบบ ข (แบบ 53-2) INSULATOR , SPOOL TYPE , L.T., TIS 277, TYPE B (CLASS 53-2)	4	03030000
6	คอนเนคเตอร์เข้าปลายสายอะลูมิเนียม ขนาดตามต้องการ CONNECTOR , DEADEND, Al SIZE AS REQUIRED	4	02310000-2
7	PVC เทป กว้าง 19 มม. (ใช้ความยาว 2 ม. ต่อ จุด) มอก. 386 PVC TAPE 19 mm WIDE (2 m LONG PER POINT) TIS 386		02180001 or 02180002
8	การประกอบสายผึกโยง GY—01 GUY ASSEMBLY GY—01	1	—
8a	การประกอบสายผึกโยง GY—02 สำหรับเสาคอนกรีต 12 ม. GUY ASSEMBLY GY—02 FOR 12 m CONCRETE POLE	1	—
	สำหรับ การติดตั้งสายดับไฟถนน FOR STREET LIGHTING INSTALLATION		
9	สลักเกลียว M 16 X 170 มม. BOLT, MACHINE , M 16X170 mm	1	01110201
9a	สลักเกลียว M 16X 250 มม. สำหรับเสาคอนกรีต 12 ม. BOLT, MACHINE, M 16 X 250 mm FOR 12 m. CONCRETE POLE	1	01110203
10	แหวนสี่เหลี่ยมแบน 52X52X4.5มม.รู Ø 18 มม. มอก. 258 WASHER , SQUARE, FLAT 52 X 52 X 4.5 mm HOLE Ø 18 mm TIS 258	1	01180100
11	ที่จับลูกรอก สำหรับลูกรอก มอก. 227 (แบบ 53-2) CLEVIS, FLAT STEEL , FOR INSULATOR, TIS 227. (CLASS 53-2)	1	03130100
12	ลูกรอกแรงต่ำ มอก. 227 แบบ ข (แบบ 53-2) INSULATOR, SPOOL TYPE , L.T., TIS 227, TYPE B (CLASS 53-2)	1	03030000
13	คอนเนคเตอร์เข้าปลายสายอะลูมิเนียม 25-35 ตามม. CONNECTOR, DEADEND, Al 25—35 mm^2	1	02310000
14	PVC เทป กว้าง 19 มม. (ใช้ความยาว 2 ม. ต่อ จุด) มอก. 386 PVC TAPE 19 mm WIDE (2 m LONG PER POINT) TIS 386		02180001 or 02180002

กองวิศวกรรมไฟฟ้าและเครื่องกล ฝ่ายวิศวกรรม	การไฟฟ้าส่วนภูมิภาค	ใช้แทนแบบ ถูกแทนโดยแบบ เขียนเสร็จวันที่ 15 สค. 21 แก้แบบวันที่ นิติเป็น มาตราส่วน
ผู้เขียน ผู้สำรวจ วิศวกร หัวหน้าแผนก หัวหน้ากอง ผู้อำนวยการฝ่าย	ผู้ว่าการ	
รองผู้ว่าการฝ่ายเทคนิค	การติดตั้งแร็คแรงต่ำกับเสาคอนกรีต 9 ม. สำหรับเข้าปลายสายเสาต้นสุดท้าย SECONDARY RACK INSTALLATION ON 9m CONCRETE POLE FOR DEADEND STRUCTURE	แบบเลขที่ SAI-015/21045 แผ่นที่ 2 ของจำนวน 2 แผ่น