


การประกอบเลขที่ ASSEMBLY NO. 5698

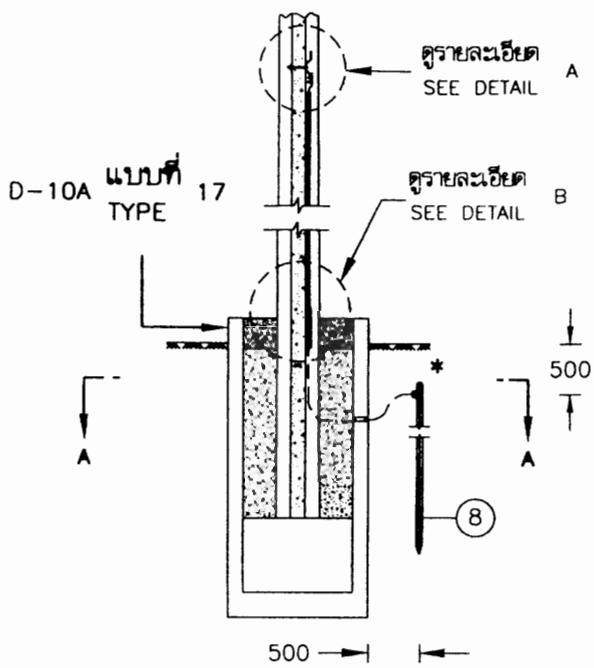

D-25A

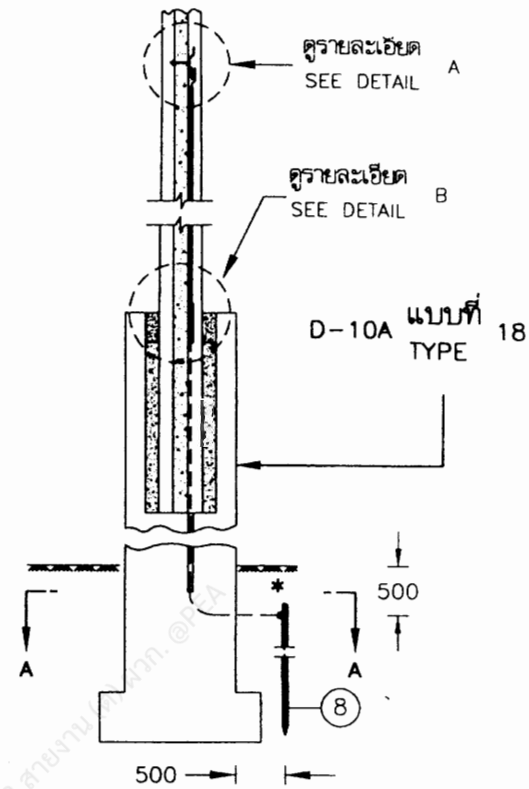

D-25B

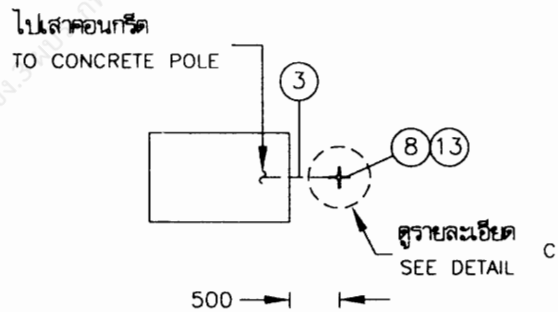


รูปตัด A-A
SECTION


ตัวอย่าง

กองมาตรฐานระบบไฟฟ้า ฝ่ายมาตรฐานและความปลอดภัย	การไฟฟ้าส่วนภูมิภาค	ใช้แทนแบบ SA1-015/46004 ถูกแทนโดยแบบ ....-....
ผู้เขียน ..... ผู้สำรวจ ..... วิศวกร ..... หัวหน้าแผนก ..... ผู้อำนวยการกอง ..... ผู้อำนวยการฝ่าย	ผู้ว่าการ ..... รายละเอียดที่ 25 รายละเอียดการต่อลงดิน สำหรับเสา คอร. 22 ม. ชนิดกราวด์เพลท	เขียนเสร็จวันที่ 20 มิ.ย. 2550 แก้แบบวันที่ ..... มิติเป็น มิลลิเมตร มาตราส่วน 1:75
รองผู้ว่าการวางแผนและพัฒนาระบบไฟฟ้า	DETAIL NO. 25 GROUNDING FOR CONCRETE POLE, GROUND PLATE TYPE	แบบเลขที่ SA1-015/50014 แผ่นที่ 1 ของจำนวน 9 แผ่น


การประกอบเลขที่ ASSEMBLY NO. 5698

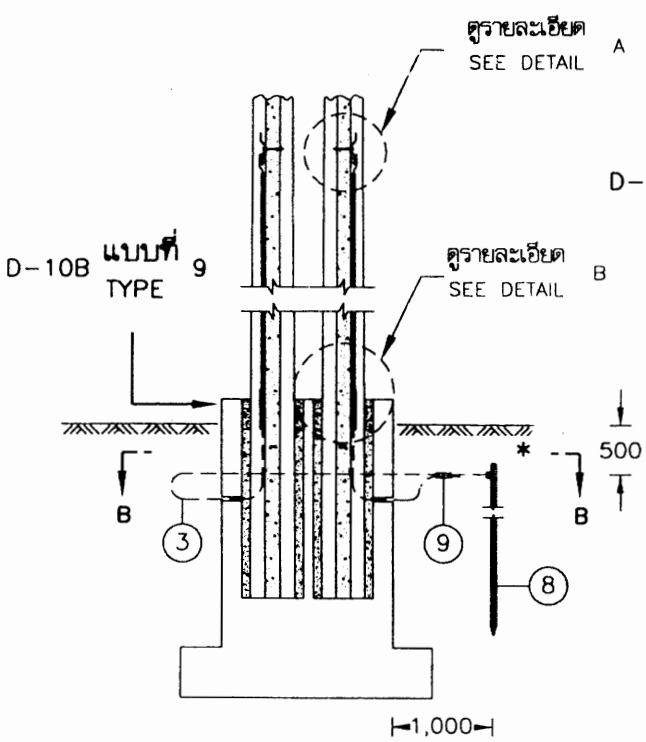


D-25C

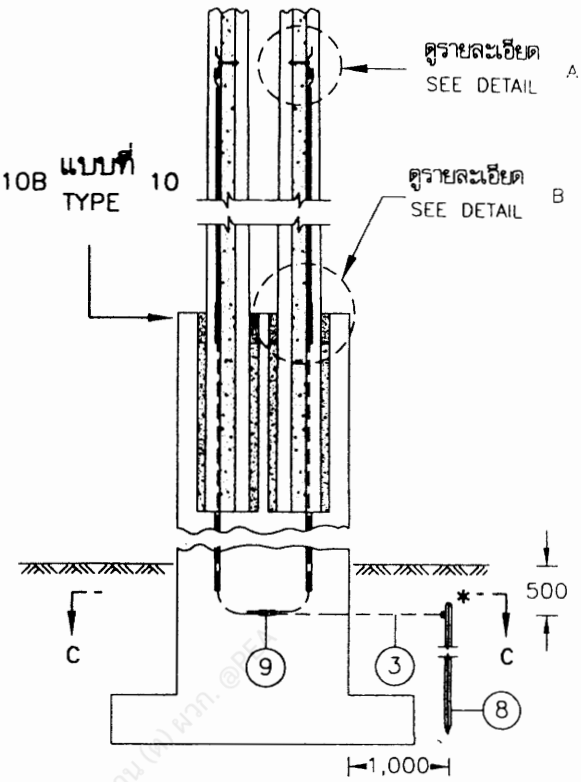

D-25D

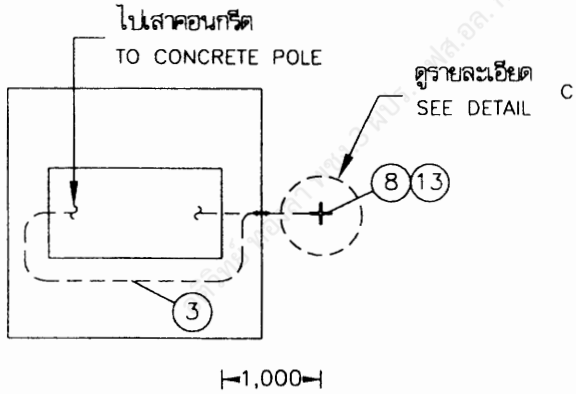


รูปตัด SECTION B-B

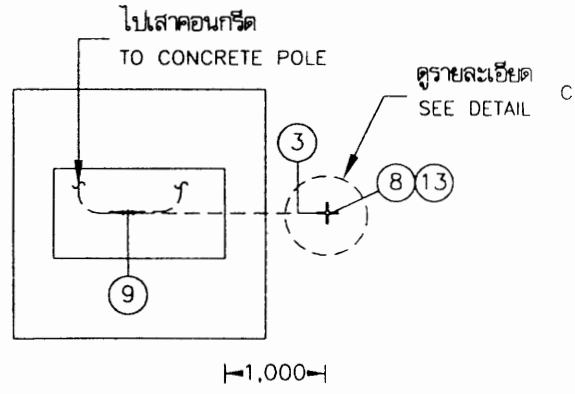


รูปตัด SECTION C-C


กองมาตรฐานระบบไฟฟ้า ฝ่ายมาตรฐานและความปลอดภัย	การไฟฟ้าส่วนภูมิภาค	ใช้แทนแบบ SA1-015/46004 ถูกแทนโดยแบบ -
ผู้เขียน ..... ผู้สำรวจ ..... วิศวกร ..... หัวหน้าแผนก ..... ผู้อำนวยการกอง ..... ผู้อำนวยการฝ่าย	ผู้ว่าการ	เขียนเสร็จวันที่ 20 มิ.ย. 2550 แก้แบบวันที่ - มิติเป็น มิลลิเมตร มาตราส่วน 1:75
รองผู้ว่าการวางแผนและพัฒนาระบบไฟฟ้า	รายละเอียดที่ 25 รายละเอียดการต่อลงดิน สำหรับเสา คอร. 22 ม. ชนิดกราวด์เพลท DETAIL NO. 25 GROUNDING FOR CONCRETE POLE, GROUND PLATE TYPE	แบบเลขที่ SA1-015/50014 แผ่นที่ 2 ของจำนวน 9 แผ่น

การประกอบเลขที่ ASSEMBLY NO. 5698

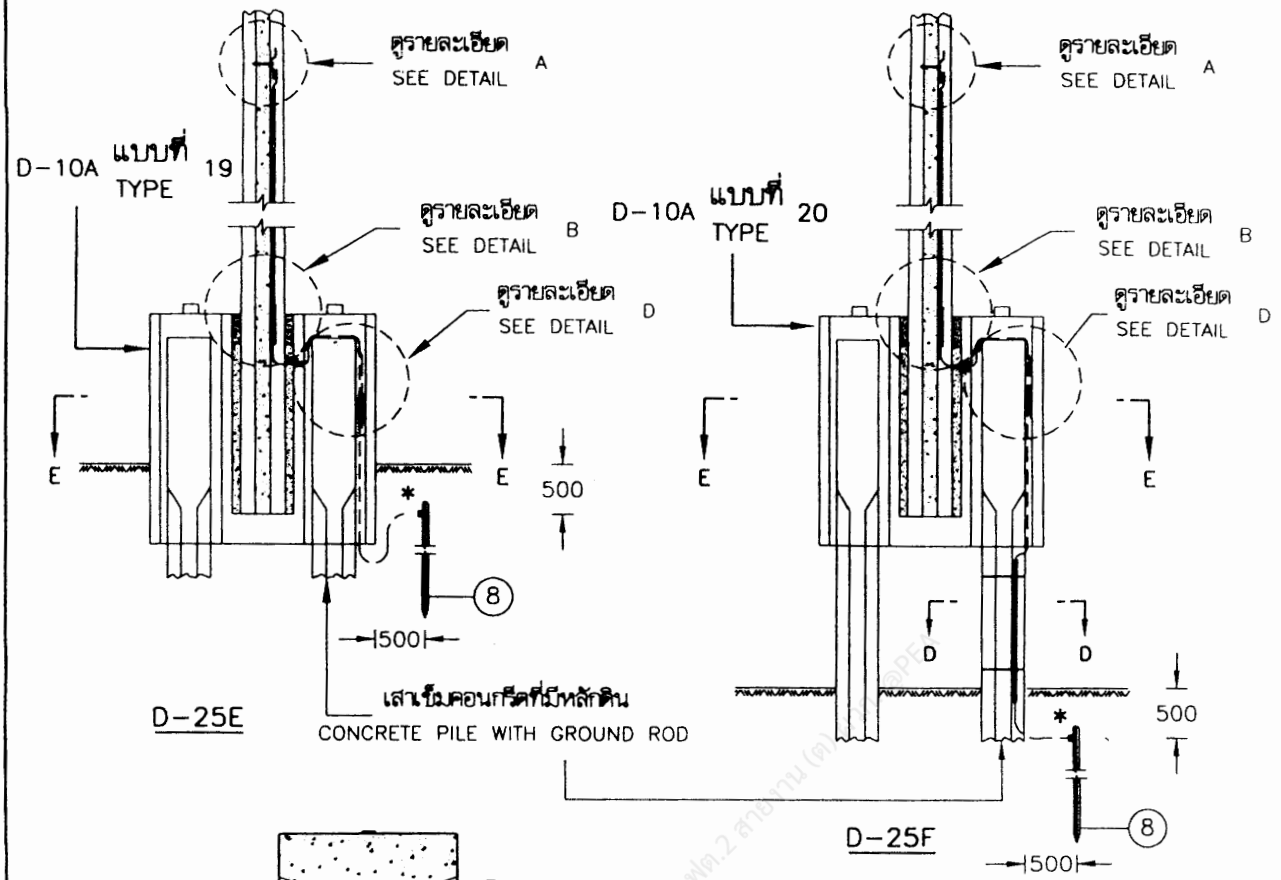


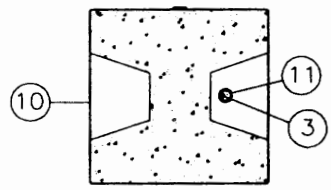

รูปตัด SECTION D-D

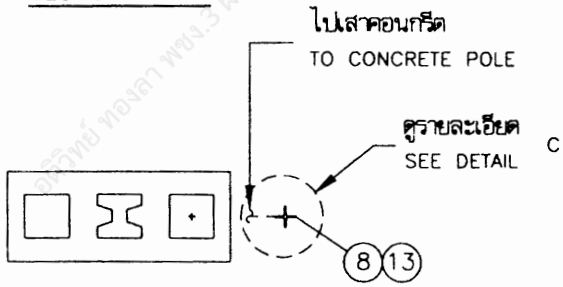


รูปตัด SECTION E-E

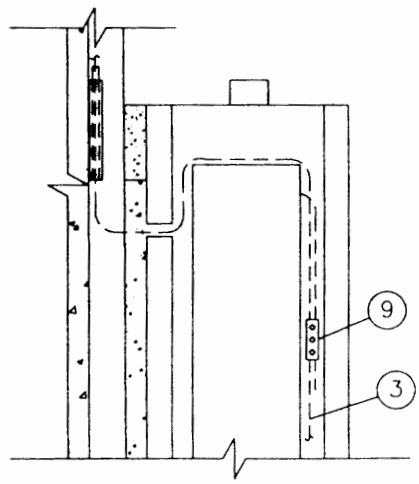

รายละเอียด DETAIL D


กองมาตรฐานระบบไฟฟ้า ฝ่ายมาตรฐานและความปลอดภัย	การไฟฟ้าส่วนภูมิภาค	ใช้แทนแบบ SA1-015/46004 ถูกแทนโดยแบบ - เขียนเสร็จวันที่ 20 มิ.ย. 2550 แก้แบบวันที่ - มิติเป็น มิลลิเมตร มาตราส่วน 1:75
ผู้เขียน ผู้สำรวจ วิศวกร หัวหน้าแผนก ผู้อำนวยการกอง ผู้อำนวยการฝ่าย	ผู้ว่าการ	
รองผู้ว่าการวางแผนและพัฒนาระบบไฟฟ้า	รายละเอียดที่ 25 รายละเอียดการต่อลงดิน สำหรับเสา คอร. 22 ม. ชนิดกราวด์เพลท DETAIL NO. 25 GROUNDING FOR CONCRETE POLE, GROUND PLATE TYPE	แบบเลขที่ SA1-015/50014 แผ่นที่ 3 ของจำนวน 9 แผ่น

การประกอบเลขที่ ASSEMBLY NO. 5698

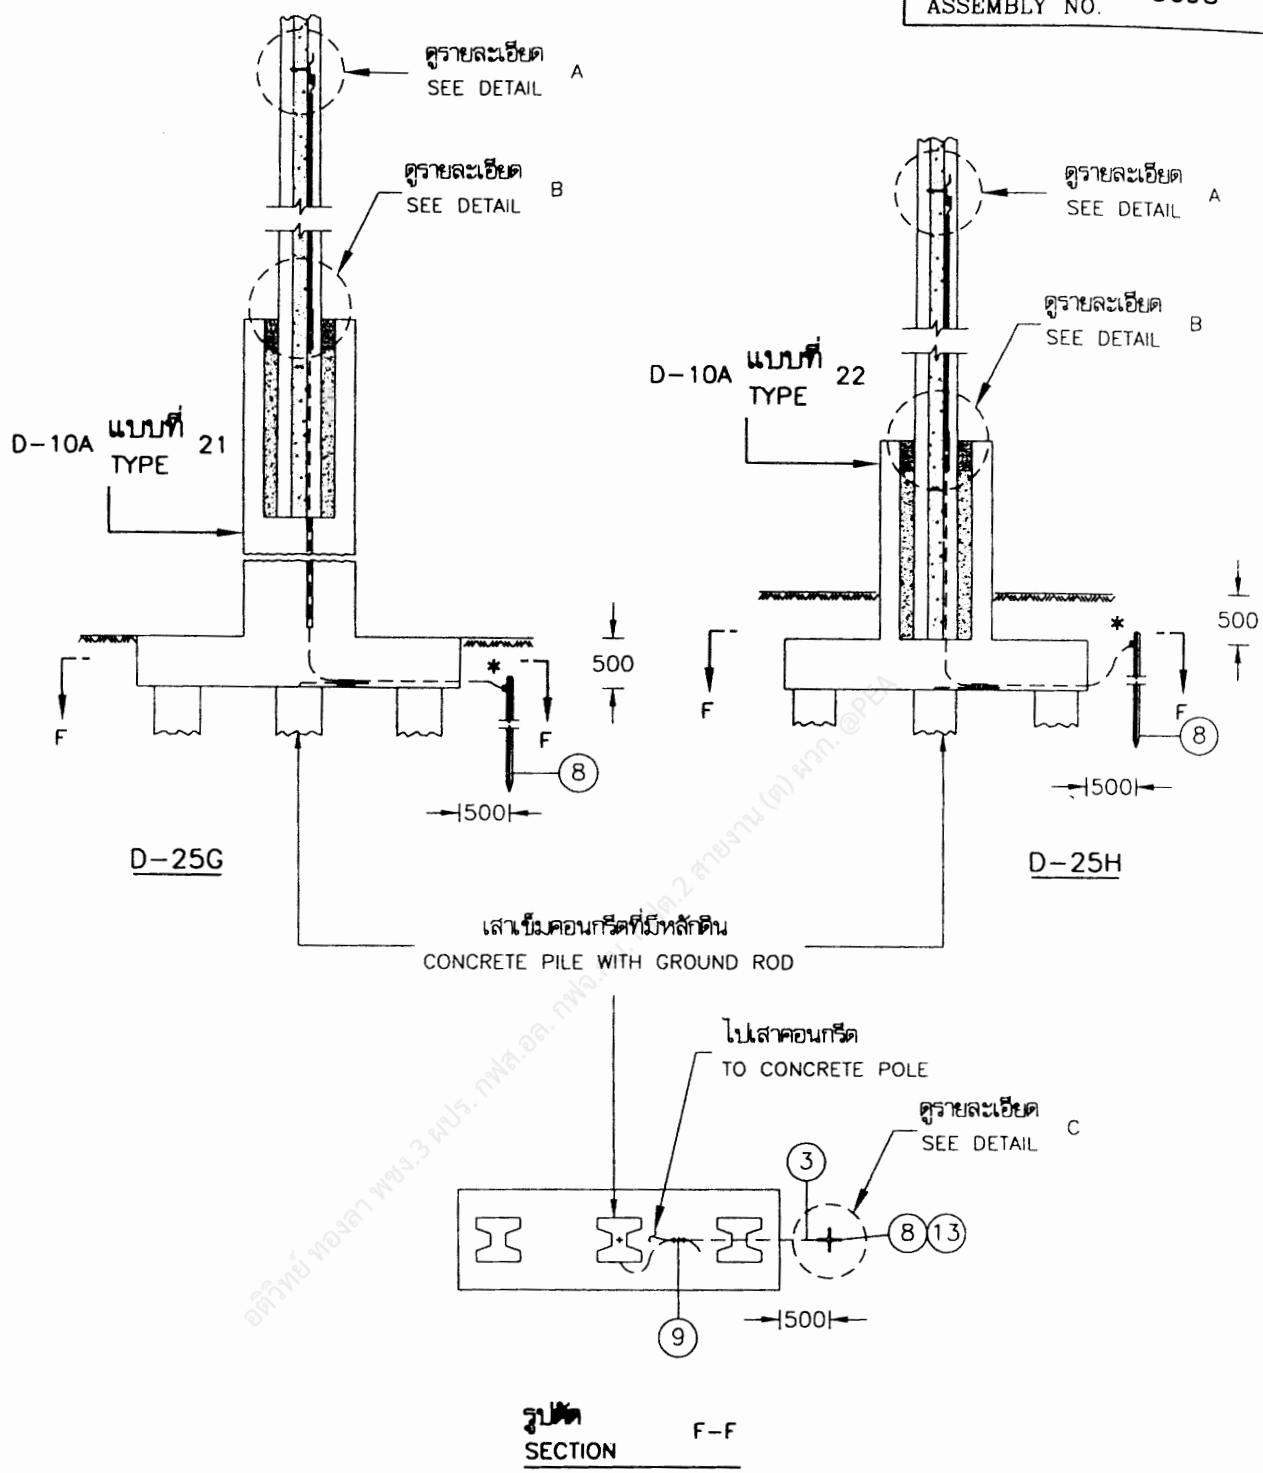


กองมาตรฐานระบบไฟฟ้า ฝ่ายมาตรฐานและความปลอดภัย	การไฟฟ้าส่วนภูมิภาค	ใช้แทนแบบ SA1-015/46004 ถูกแทนโดยแบบ - เขียนเสร็จวันที่ 20 มิ.ย. 2550 แก้แบบวันที่ - มิติเป็น มิลลิเมตร มาตราส่วน 1:75
ผู้เขียน ผู้สำรวจ วิศวกร หัวหน้าแผนก ผู้อำนวยการกอง ผู้อำนวยการฝ่าย	ผู้ว่าการ 5 ก.ค. 2550	
รองผู้ว่าการวางแผนและพัฒนาระบบไฟฟ้า	รายละเอียดที่ 25 รายละเอียดการต่อลงดิน สำหรับเสา คอร. 22 ม. ชนิดกราวด์เพลท	
	DETAIL NO. 25 GROUNDING FOR CONCRETE POLE, GROUND PLATE TYPE	แบบเลขที่ SA1-015/50014 แผ่นที่ 4 ของจำนวน 9 แผ่น


การประกอบเลขที่ ASSEMBLY NO. 5698

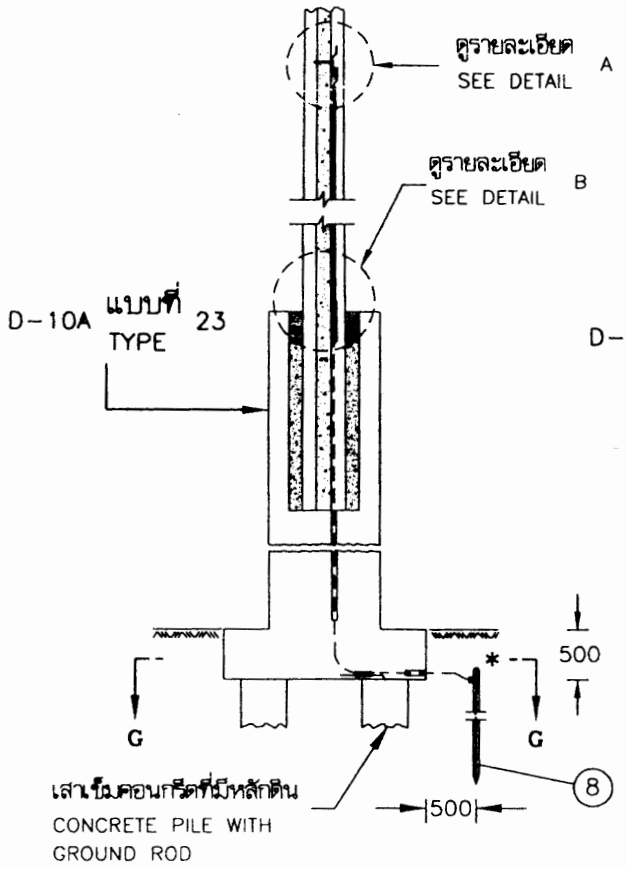


D-25I

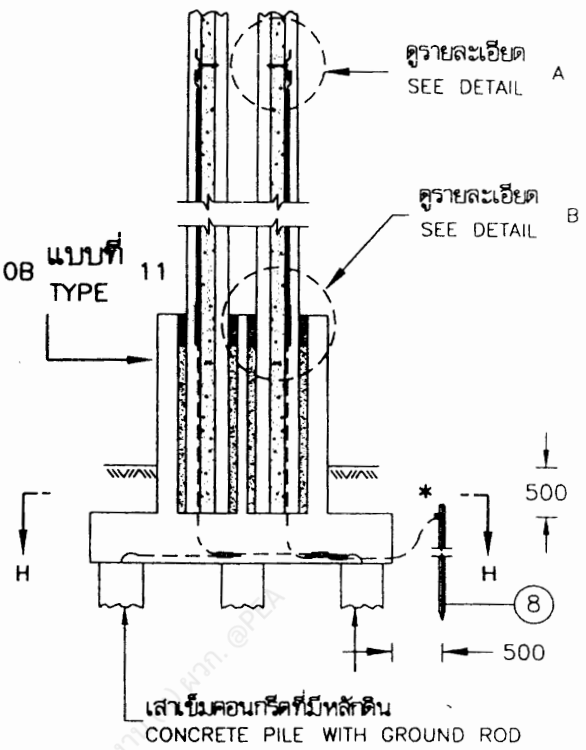

D-25J

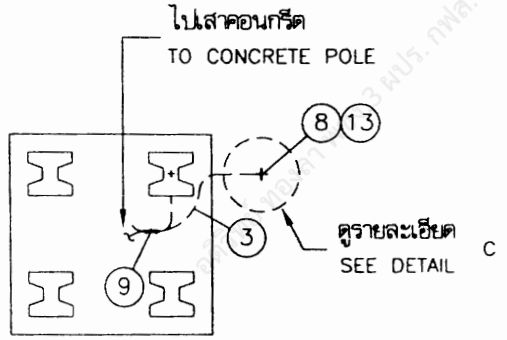


รูปตัด SECTION G-G

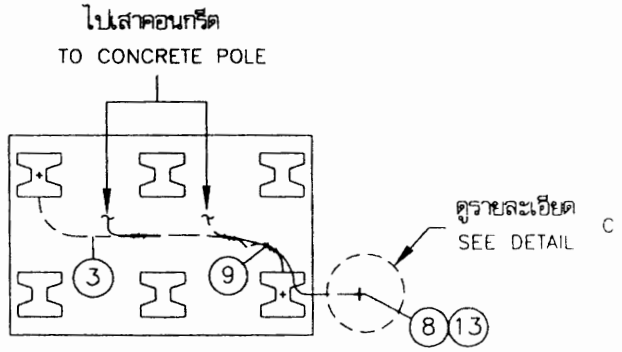


รูปตัด SECTION H-H

กองมาตรฐานระบบไฟฟ้า ฝ่ายมาตรฐานและความปลอดภัย	การไฟฟ้าส่วนภูมิภาค	ใช้แทนแบบ SA1-015/46004 ถูกแทนโดยแบบ ... เขียนเสร็จวันที่ 20 มิ.ย. 2550 แก้แบบวันที่ ... มิติเป็น มิลลิเมตร มาตราส่วน 1:75
ผู้เขียน ..... ผู้สำรวจ ..... วิศวกร ..... หัวหน้าแผนก ..... ผู้อำนวยการกอง ..... ผู้อำนวยการฝ่าย	ผู้ว่าการ ..... 5 ก.ค. 2550 รายละเอียดที่ 25 รายละเอียดการต่อลงดิน สำหรับเสา คอร. 22 ม. ชนิดกราวด์เพลท	
รองผู้ว่าการวางแผนและพัฒนาระบบไฟฟ้า	DETAIL NO. 25 GROUNDING FOR CONCRETE POLE, GROUND PLATE TYPE	แบบเลขที่ SA1-015/50014 แผ่นที่ 5 ของจำนวน 9 แผ่น

การประกอบเลขที่ ASSEMBLY NO.	5698

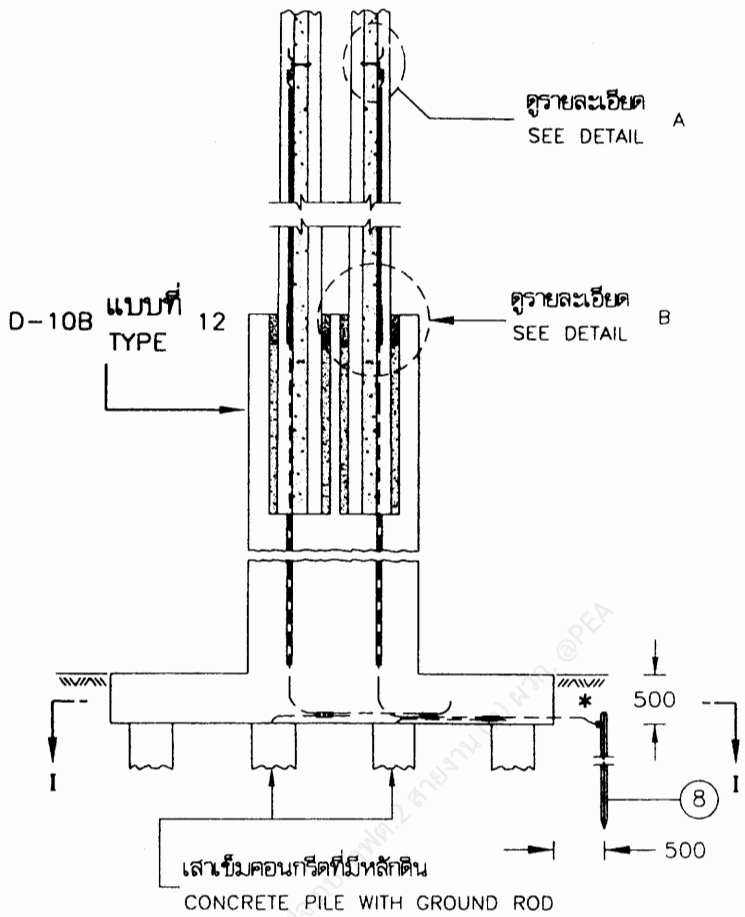


D-25K

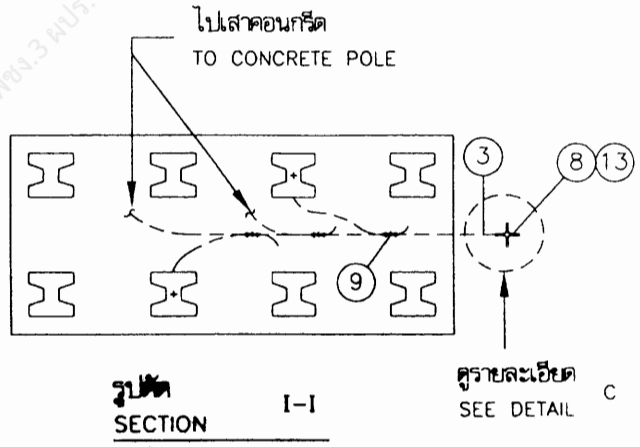


รูปตัด I-I
SECTION I-I

กองมาตรฐานระบบไฟฟ้า ฝ่ายมาตรฐานและความปลอดภัย	การไฟฟ้าส่วนภูมิภาค	ใช้แทนแบบ SA1-015/46004 ถูกแทนโดยแบบ ... เขียนเสร็จวันที่ 20 มิ.ย. 2550 แก้แบบวันที่ ... มิติเป็น มิลลิเมตร มาตราส่วน 1:75
ผู้เขียน ..... ผู้สำรวจ ..... วิศวกร ..... หัวหน้าแผนก ..... ผู้อำนวยการกอง ..... ผู้อำนวยการฝ่าย	ผู้ว่าการ ..... 5 ก.ค. 2550 รายละเอียดที่ 25 รายละเอียดการต่อลงดิน สำหรับเสา คอร. 22 ม. ชนิดกราวด์เพลท	
รองผู้ว่าการวางแผนและพัฒนาระบบไฟฟ้า	DETAIL NO. 25 GROUNDING FOR CONCRETE POLE, GROUND PLATE TYPE	แบบเลขที่ SA1-015/50014 แผ่นที่ 6 ของจำนวน 9 แผ่น


การประกอบเลขที่ ASSEMBLY NO. 5698

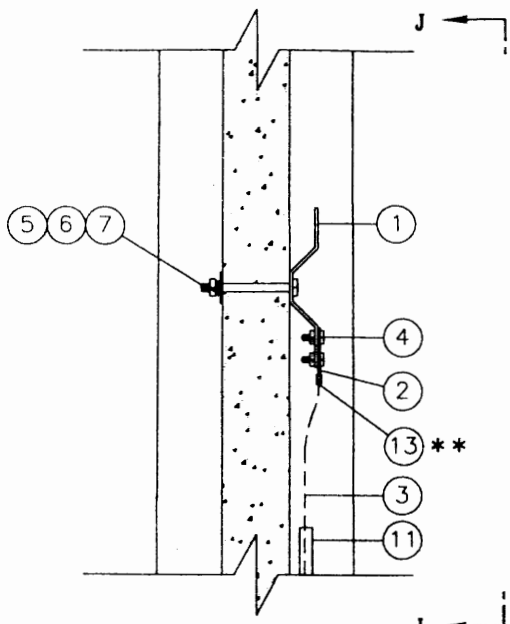


รายละเอียด DETAIL A

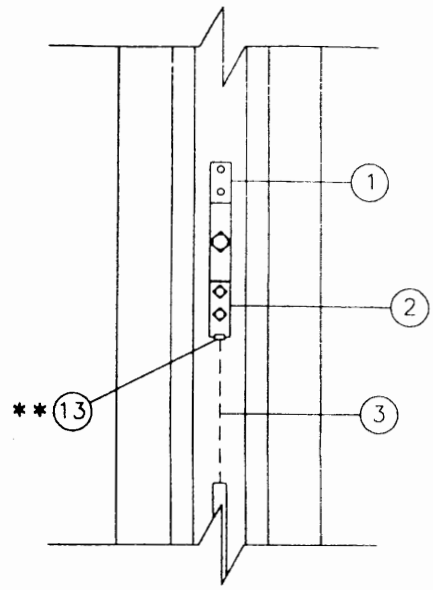


รูปตัด SECTION J–J

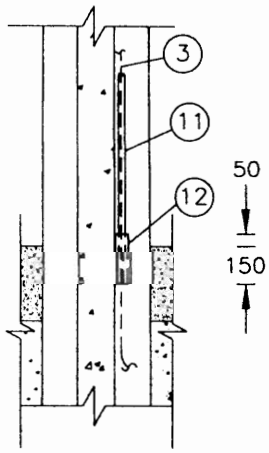


รายละเอียด DETAIL B

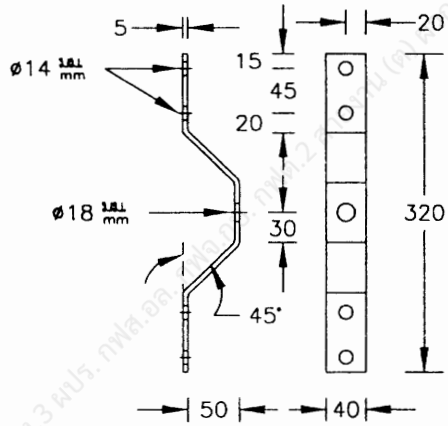

วัสดุลำดับที่ (1) *** MATERIAL ITEM

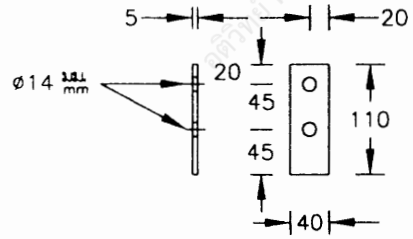

วัสดุลำดับที่ (2) *** MATERIAL ITEM

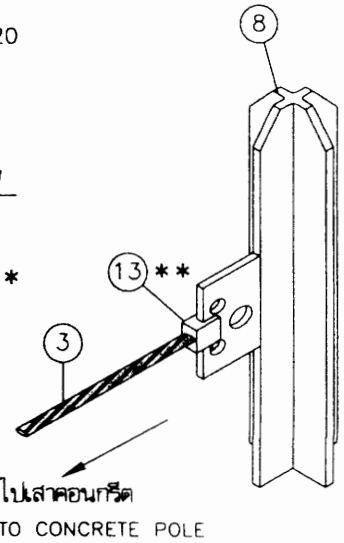

รายละเอียด DETAIL C

กองมาตรฐานระบบไฟฟ้า ฝ่ายมาตรฐานและความปลอดภัย	การไฟฟ้าส่วนภูมิภาค	ใช้แทนแบบ SA1-015/46004 ถูกแทนโดยแบบ ....-....
ผู้เขียน ..... ผู้สำรวจ ..... วิศวกร ..... หัวหน้าแผนก ..... ผู้อำนวยการกอง ..... ผู้อำนวยการฝ่าย	ผู้ว่าการ ..... 5 ก.ค. 2550 รายละเอียดที่ 25 รายละเอียดการต่อลงดิน สำหรับเสา คอร. 22 ม. ชนิดกราวด์เพลท	เขียนเสร็จวันที่ 20 มิ.ย. 2550 แก้แบบวันที่ ....-.... มิติเป็น มิลลิเมตร มาตราส่วน 1:75
รองผู้ว่าการวางแผนและพัฒนาระบบไฟฟ้า	DETAIL NO. 25 GROUNDING FOR CONCRETE POLE, GROUND PLATE TYPE	แบบเลขที่ SA1-015/50014 แผ่นที่ 7 ของจำนวน 9 แผ่น

การประกอบเลขที่ ASSEMBLY NO.	5698

บัญชีวัสดุ
BILL OF MATERIAL

ลำดับที่ ITEM	รายละเอียด DESCRIPTION	จำนวน REQ'D D-25											วัสดุเลขที่ MAT. NO.
		A	B	C	D	E	F	G	H	I	J	K	
1	แผ่นเหล็กประกอบโคนเสา PLATE, STEEL, FOR GROUND WIRE	1	1	2	2	1	1	1	1	1	2	2	1010030007
2	แผ่นเหล็ก ขนาด 40x110x5 มม. PLATE, STEEL, 40x110x5 mm	1	1	2	2	1	1	1	1	1	2	2	1010030008
3	ลวดเหล็กตีเกลียว 50/7 ต.มม. มอก. 404 WIRE, STEEL STRANDED 50/7 mm² TIS 404	6 ม.	10 ม.	12 ม.	23 ม.	10 ม.	12 ม.	12 ม.	9 ม.	13 ม.	18 ม.	24 ม.	1010100004
4	สลักเกลียว M 12x35 มม. BOLT, MACHINE M 12x35 mm	2	2	4	4	2	2	2	2	2	4	4	1010110100
5	สลักเกลียว M 16x170 มม. BOLT, MACHINE M.16x170 mm	1	1	2	2	1	1	1	1	1	2	2	1010110201
6	แหวนสี่เหลี่ยมแบน 52x52x4.5 มม. รู ø18 มม. มอก. 258 WASHER, SQUARE, FLAT, 52x52x4.5 mm, HOLE ø18 mm, TIS 258	1	1	2	2	1	1	1	1	1	2	2	1010180100
7	แหวนรองแบบสปริง ขนาดระบุ 16 มม. WASHER, LOCK, SPRING, SIZE 16 mm	1	1	2	2	1	1	1	1	1	2	2	1010180301
8	หลักดิน 60x60x5 มม. ยาว 2,000 มม. GROUND ROD, 60x60x5 mm, 2,000 mm LONG	1	1	1	1	1	1	1	1	1	1	1	1010220002
9	แคล้มป์ สลัก 3 ตัว สำหรับลวดเหล็กตีเกลียว 50 ต.มม. CLAMP, TRIPLE BOLTS FOR STEEL STRANDED WIRE 50 mm²	–	–	1	1	1	1	1	1	1	3	3	1010230004
10	ลวดอลูมิเนียมแบน 1x10 มม. TAPE,ARMOR,AL 1x10 mm.	–	–	–	–	–	4 ม.	–	–	–	–	–	1020200000
11	ท่อพีวีซีแข็ง ขนาด ø20 มม.ยาว 2,000 มม. CONDUIT,PVC,RIGID,ø20 mm, 2,000 mm LONG	1	1	2	2	1	2	1	1	1	2	2	1080040005
12	ท่อพีวีซีแข็ง ขนาด ø50 มม. ยาว 200 มม. CONDUIT,PVC,RIGID,ø50 mm,200 mm LONG	1	1	2	2	1	1	1	1	1	2	2	1080040006
13	จุดต่อสายดินกับแผ่นเหล็กหรือหลักดินแบบเชื่อมด้วยความร้อน EXOTHERMIC WELDING POINT BETWEEN GROUND WIRE AND STEEL PLATE OR GROUND ROD	2	2	3	3	2	2	2	2	2	3	3	–

กองมาตรฐานระบบไฟฟ้า
ฝ่ายมาตรฐานและความปลอดภัย

ผู้เขียน .....
ผู้สำรวจ .....
วิศวกร .....
หัวหน้าแผนก .....
ผู้อำนวยการกอง .....
ผู้อำนวยการฝ่าย .....

รองผู้ว่าการวางแผนและพัฒนาระบบไฟฟ้า
.....

การไฟฟ้าส่วนภูมิภาค

ผู้ว่าการ .....

รายละเอียดที่ 25 5 ส.ค. 2551
รายละเอียดการต่อลงดิน สำหรับเสา คอร. 22 ม.
ชนิดก่อราวด์เพลท

DETAIL NO. 25
GROUNDING FOR CONCRETE POLE,
GROUND PLATE TYPE

ใช้แทนแบบ SA1-015/46004
ถูกแทนโดยแบบ .....
เขียนเสร็จวันที่ 20 มิ.ย. 2550
แก้แบบวันที่ .....
มิติเป็น มิลลิเมตร
มาตราส่วน .....

แบบเลขที่ SA1-015/50014
แผ่นที่ 8 ของจำนวน 9 แผ่น

การประกอบเลขที่ ASSEMBLY NO.	5698

แบบอ้างอิง REFERENCE DRAWING	แบบเลขที่ DWG. NO.	การประกอบเลขที่ ASSEMBLY NO.
การประกอบยึดท่อ พีวีซี. กับเสาคอนกรีต RIGID PVC CONDUIT ASSEMBLY ON CONCRETE POLE	SA1-015/31013	9704A
การต่อลงดินสำหรับระบบจำหน่ายและระบบสายส่ง GROUNDING SYSTEMS FOR DISTRIBUTION AND TRANSMISSION SYSTEM	SA1-015/50003	5190

* สามารถเพิ่มจำนวนแท่งกราวด์ร็อด และ/หรือเปลี่ยนวิธีการต่อลงดินได้ตามความเหมาะสม
THE GROUNDING METHOD AND/OR NUMBER OF GROUND RODS CAN BE MODIFIED TO WORK PROPERLY ACCORDING TO SITE CONDITION.

* * ก่อนเชื่อมให้ขัดเอาสังกะสีบริเวณที่จะเชื่อมออก และเมื่อเชื่อมเสร็จแล้วให้พ่น SPRAY ZINC ทับรอยเชื่อมด้วย
BEFORE WELDING, ZINC COATED SURFACE HAS TO BE REMOVED. THE WELDING POINT HAS TO BE ZINC SPRAYED AFTER FINISHING WELDING PROCESS.

* * * อาบสังกะสีตามมาตรฐาน กฟภ.
HOT DIP GALVANIZE ACCORDING TO PEA. STANDARD

อดิวิทย์ ทองลา พงง.3 ศปร. กฟส.อล. กฟส.กน. กฟต.2 สายงาน (ค) ฝวก. @PEA

กองมาตรฐานระบบไฟฟ้า ฝ่ายมาตรฐานและความปลอดภัย	การไฟฟ้าส่วนภูมิภาค	ใช้แทนแบบ SA1-015/46004
ผู้เขียน ..... ผู้สำรวจ ..... วิศวกร ..... หัวหน้าแผนก ..... ผู้อำนวยการกอง ..... ผู้อำนวยการฝ่าย	ผู้ว่าการ ..... 25 ก.ค. 2550	ถูกแทนโดยแบบ ..... เขียนเสร็จวันที่ 20 มิ.ย. 2550 แก้แบบวันที่ .....
รองผู้ว่าการวางแผนและพัฒนาระบบไฟฟ้า	รายละเอียดที่ 25 รายละเอียดการต่อลงดิน สำหรับเสา คอร. 22 ม. ชนิดกราวด์เพลท	มิติเป็น มิลลิเมตร มาตราส่วน .....
	DETAIL NO. 25 GROUNDING FOR CONCRETE POLE, GROUND PLATE TYPE	แบบเลขที่ SA1-015/50014 แผ่นที่ 9 ของจำนวน 9 แผ่น