

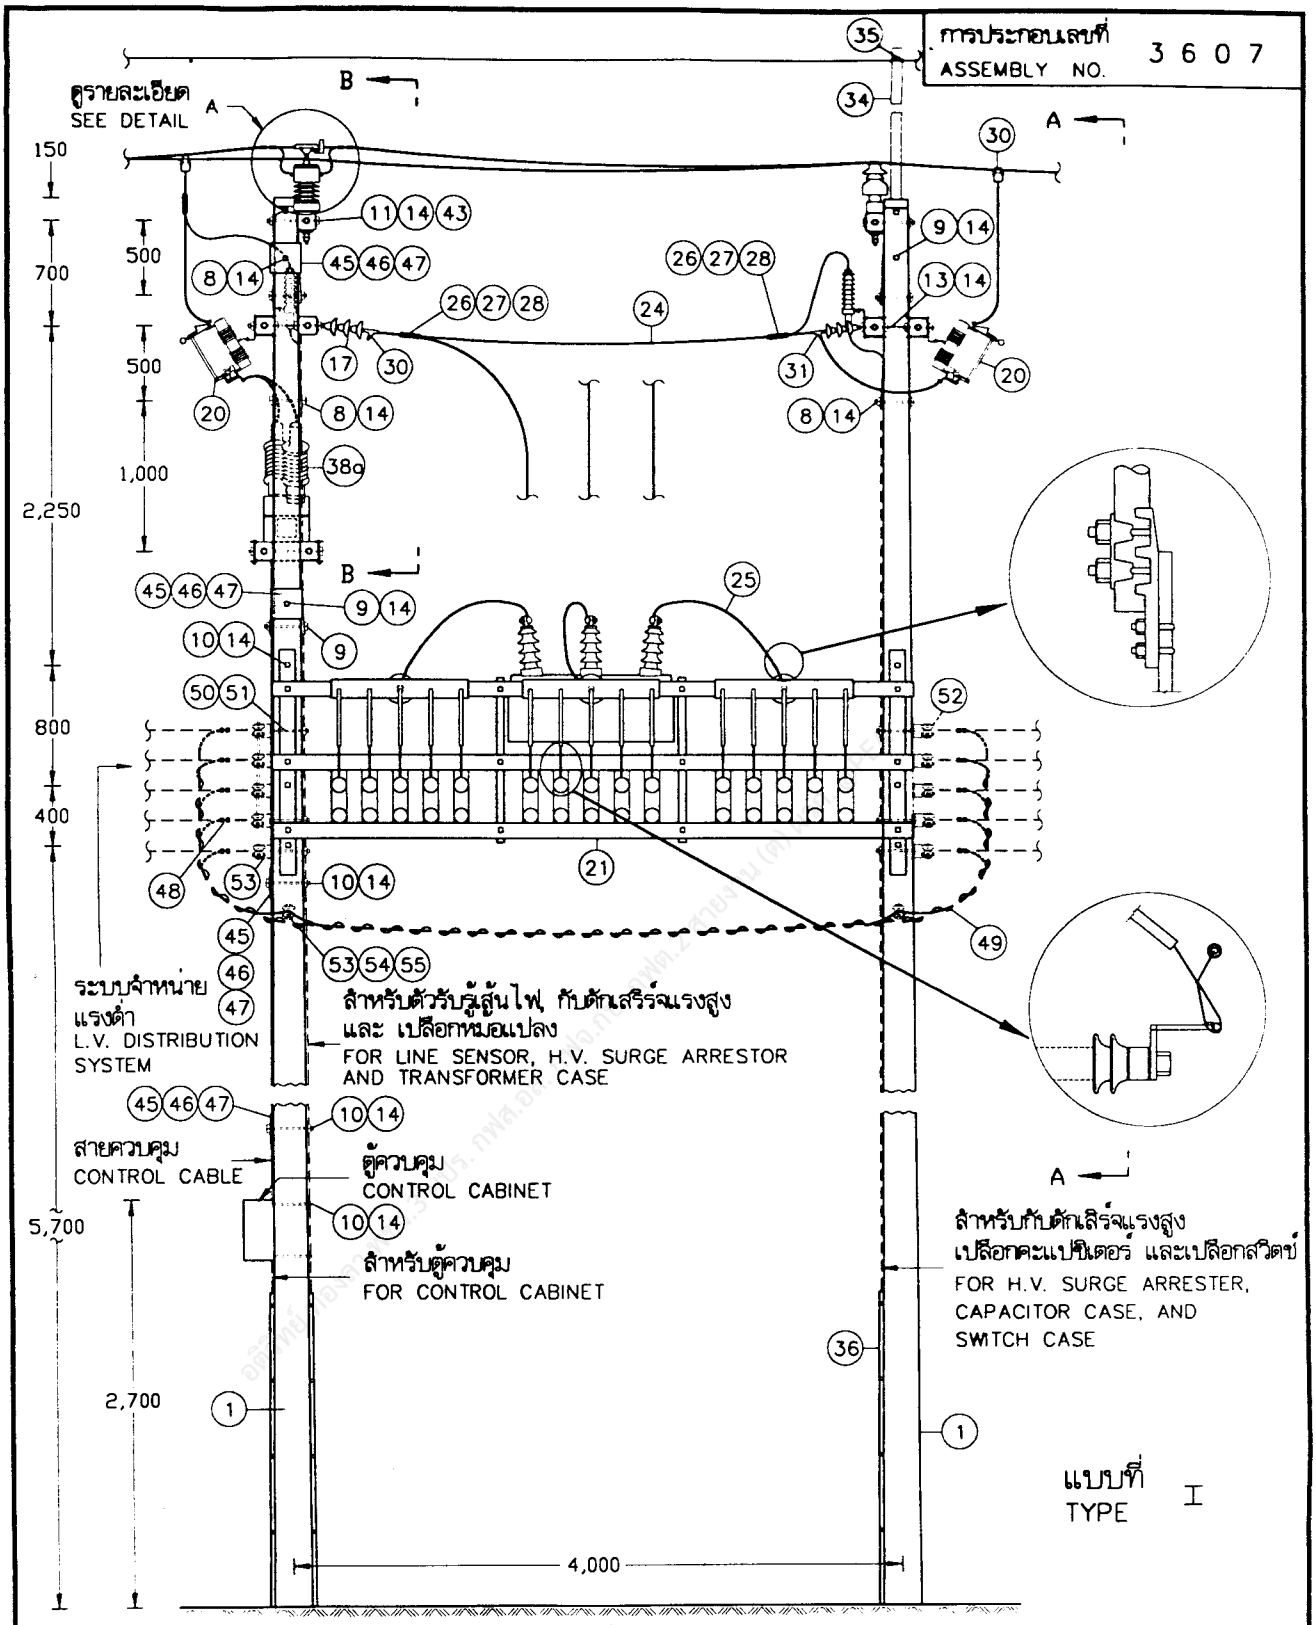


กองมาตรฐานระบบไฟฟ้า ฝ่ายมาตรฐานและความปลอดภัย	การไฟฟ้าส่วนภูมิภาค	ใช้แทนแบบ
ผู้เขียน พงศักดิ์ ศิริสมบูรณ์	ผู้ว่าการ - 9 มี.ค. 2548	ถูกแทนโดยแบบ
ผู้สำรวจ		เขียนเสร็จวันที่ 8 ก.พ. 2548
วิศวกร	การติดตั้งชุดคะแปซิเตอร์ระบบ 33 kV ขนาด 1,200–1,500 kvar พร้อมอุปกรณ์ตัดตอน แบบควบคุมด้วยวาร์	แก้แบบวันที่
หัวหน้าแผนก		มิติเป็น มิลลิเมตร
ผู้อำนวยการกอง		มาตราส่วน 1:50
ผู้อำนวยการฝ่าย		
รองผู้ว่าการวางแผนและพัฒนาระบบไฟฟ้า - 8 มี.ค. 2548	33 kV SWITCHING CAPACITOR BANK INSTALLATION 1,200–1,500 kvar, var CONTROL	แบบเลขที่ SA2-015/48002 แผ่นที่ 1 ของจำนวน 10 แผ่น

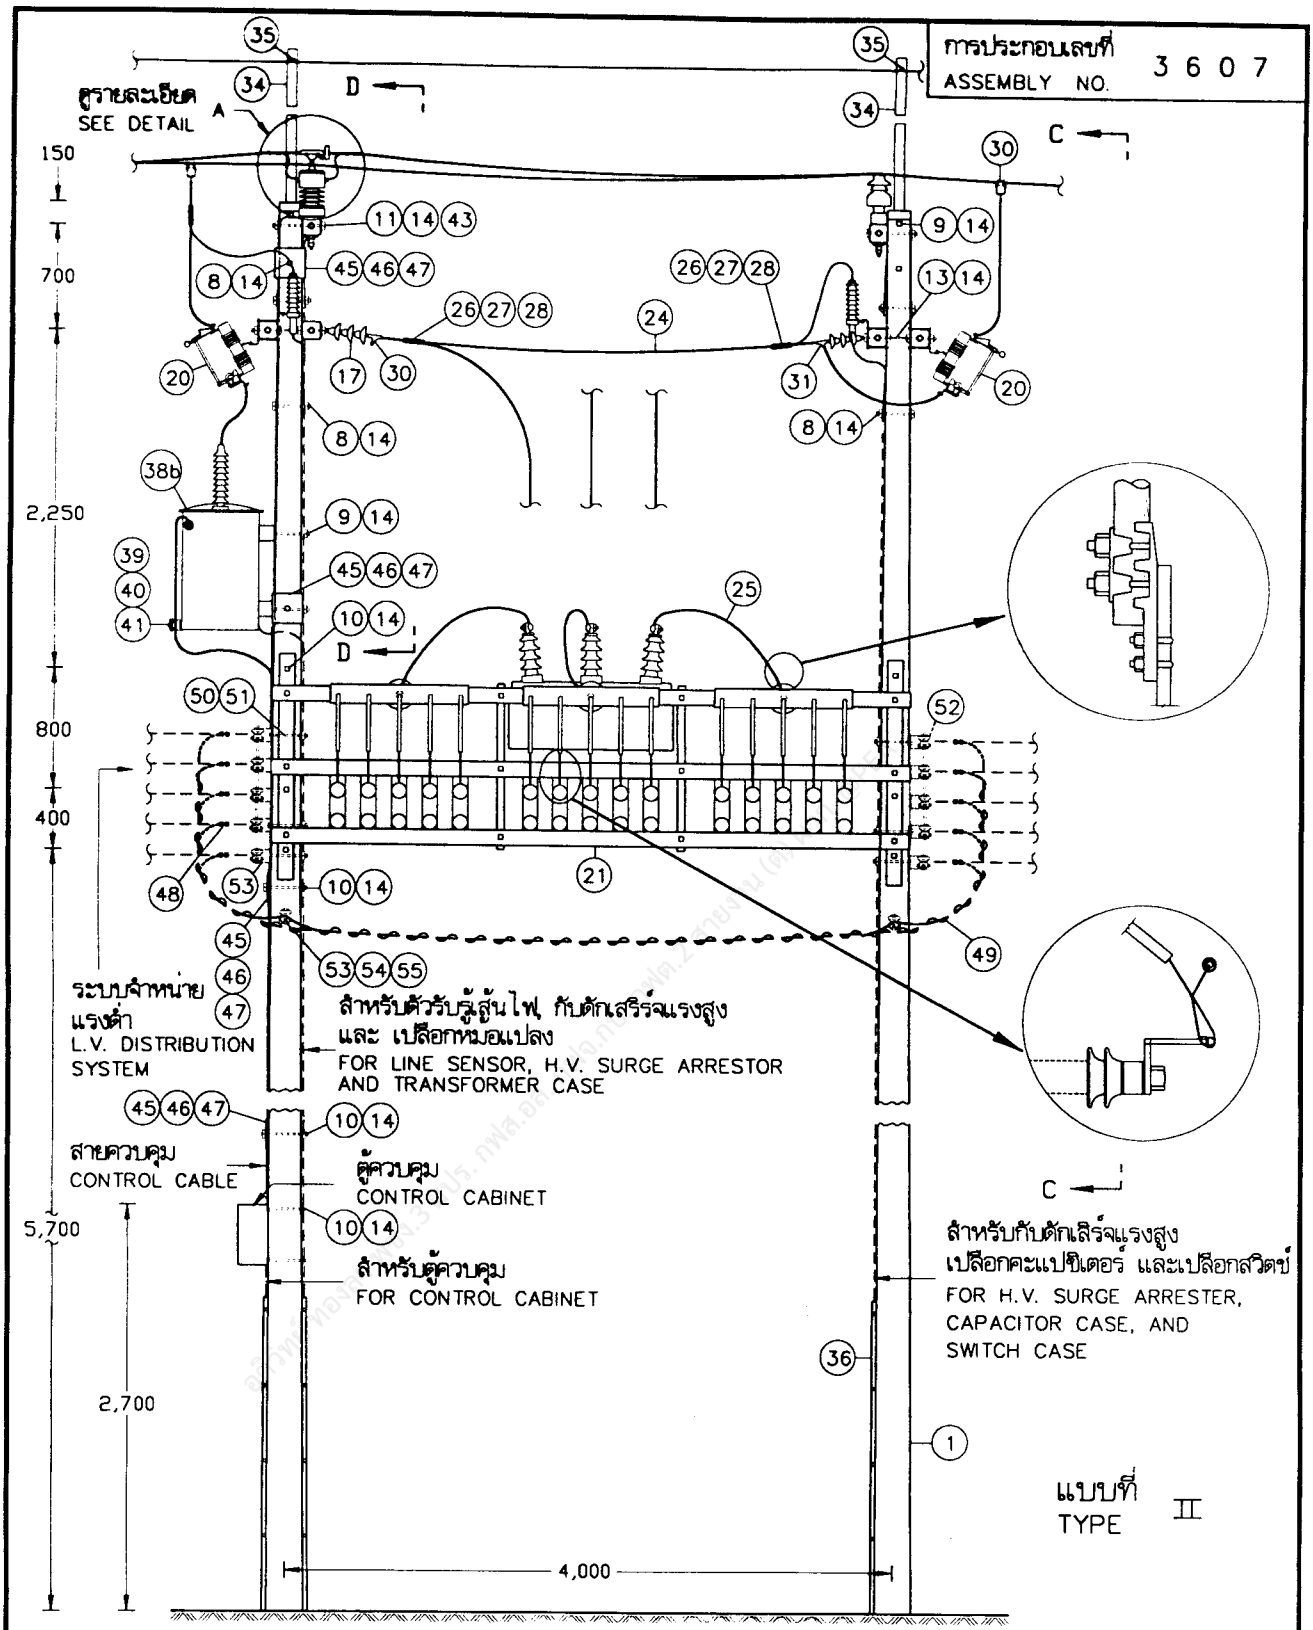


กองมาตรฐานระบบไฟฟ้า ฝ่ายมาตรฐานและความปลอดภัย	การไฟฟ้าส่วนภูมิภาค	ใช้แทนแบบ ถูกแทนโดยแบบ
ผู้เขียน พยุงศักดิ์ ศิริสมบูรณ์ ผู้สำรวจ วิศวกร หัวหน้าแผนก ผู้อำนวยการกอง ผู้อำนวยการฝ่าย	ผู้ว่าการ - 8 มี.ค. 2548 การติดตั้งชุดคะแปซิเตอร์ระบบ 33 kV ขนาด 1,200–1,500 kvar พร้อมอุปกรณ์ตัดตอน แบบควบคุมด้วยวาร์	เขียนเสร็จวันที่ 8 ก.พ. 2548 แก้แบบวันที่ มิติเป็น มิลลิเมตร มาตราส่วน 1:50
รองผู้ว่าการวางแผนและพัฒนาระบบไฟฟ้า - 8 มี.ค. 2548	33 kV SWITCHING CAPACITOR BANK INSTALLATION 1,200–1,500 kvar, var CONTROL	แบบเลขที่ SA2-015/48002 แผ่นที่ 2 ของจำนวน 10 แผ่น


การประกอบเลขที่ ASSEMBLY NO. 3607

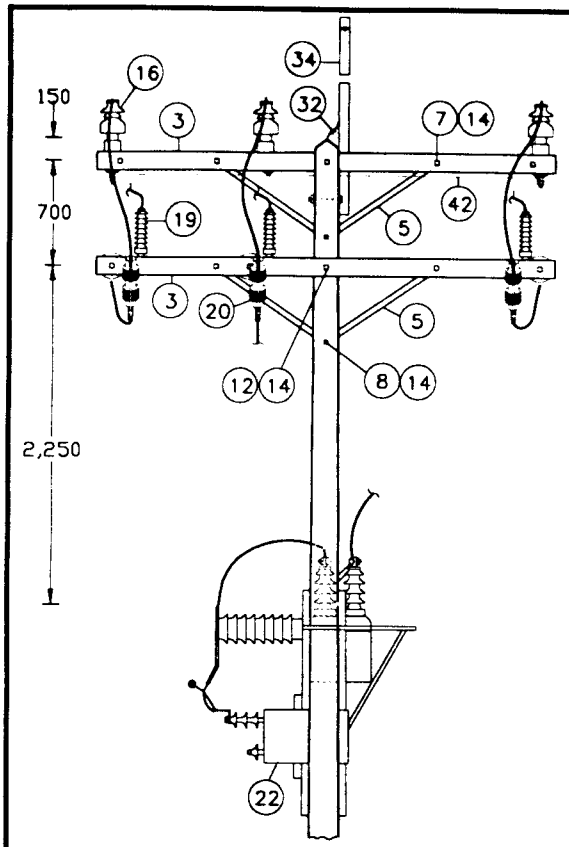

รูปตัด SECTION A-A

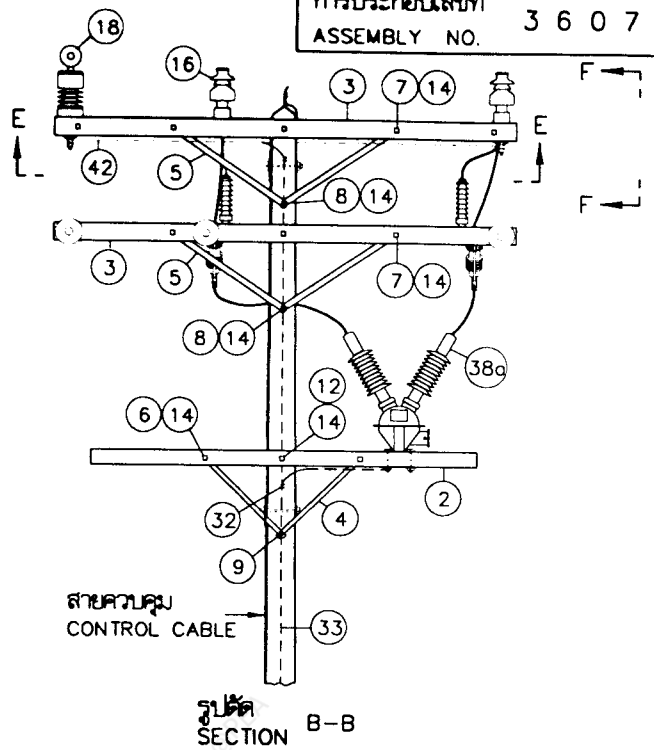


รูปตัด SECTION B-B

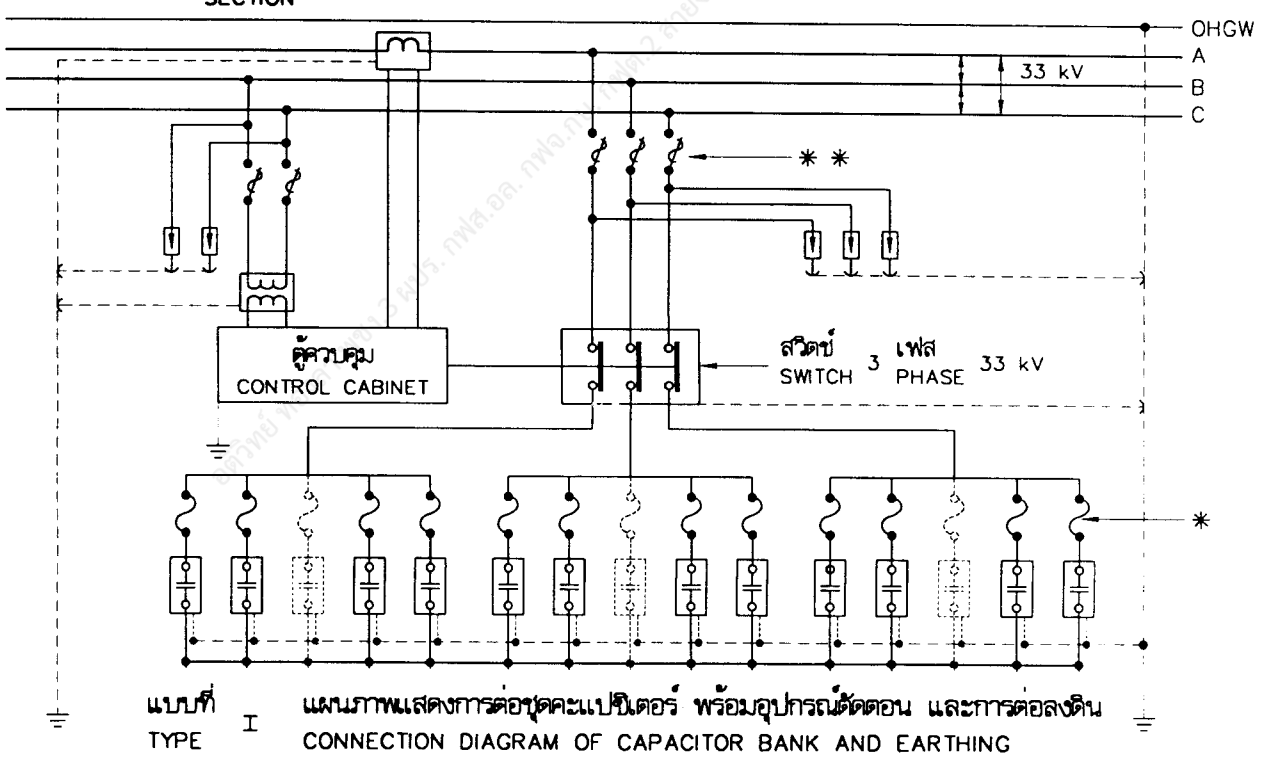


แบบที่ TYPE I แผนภาพแสดงการต่อชุดคะแปซิเตอร์ พร้อมอุปกรณ์ตัดตอน และการต่อลงดิน
CONNECTION DIAGRAM OF CAPACITOR BANK AND EARTHING

กองมาตรฐานระบบไฟฟ้า ฝ่ายมาตรฐานและความปลอดภัย	การไฟฟ้าส่วนภูมิภาค	ใช้แทนแบบ ..... ถูกแทนโดยแบบ .....
ผู้เขียน พงษ์ศักดิ์ ศิริสมบูรณ์ ผู้สำรวจ ..... วิศวกร ..... หัวหน้าแผนก ..... ผู้อำนวยการกอง ..... ผู้อำนวยการฝ่าย	ผู้ว่าการ ..... - 8 มี.ค. 2548	เขียนเสร็จวันที่ 8 ก.พ. 2548 แก้แบบวันที่ .....
	การติดตั้งชุดคะแปซิเตอร์ระบบ 33 kV ขนาด 1,200-1,500 kvar พร้อมอุปกรณ์ตัดตอน แบบควบคุมด้วยวาร์	มิติเป็น มิลลิเมตร มาตราส่วน 1:50
รองผู้ว่าการวางแผนและพัฒนาระบบไฟฟ้า ..... - 8 มี.ค. 2548	33 kV SWITCHING CAPACITOR BANK INSTALLATION 1,200-1,500 kvar, var CONTROL	แบบเลขที่ SA2-015/48002 แผ่นที่ 3 ของจำนวน 10 แผ่น


การประกอบเลขที่ ASSEMBLY NO. 3607

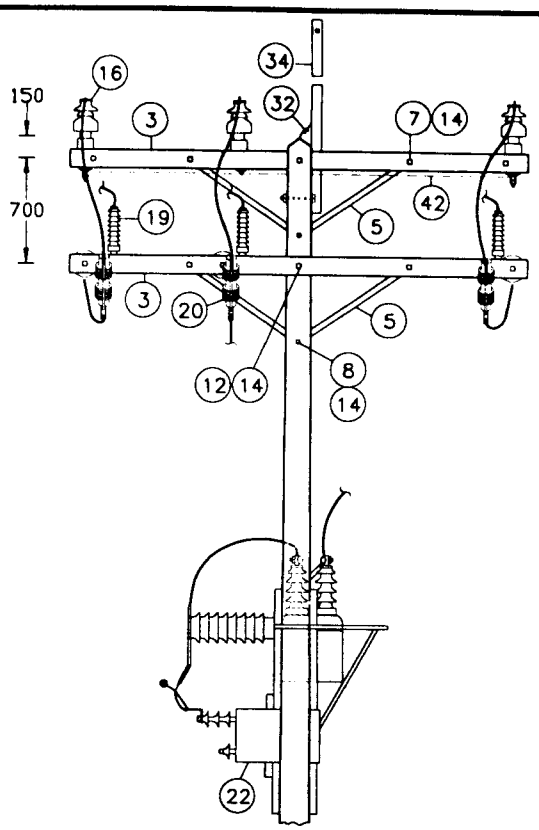

รูปตัด SECTION C–C

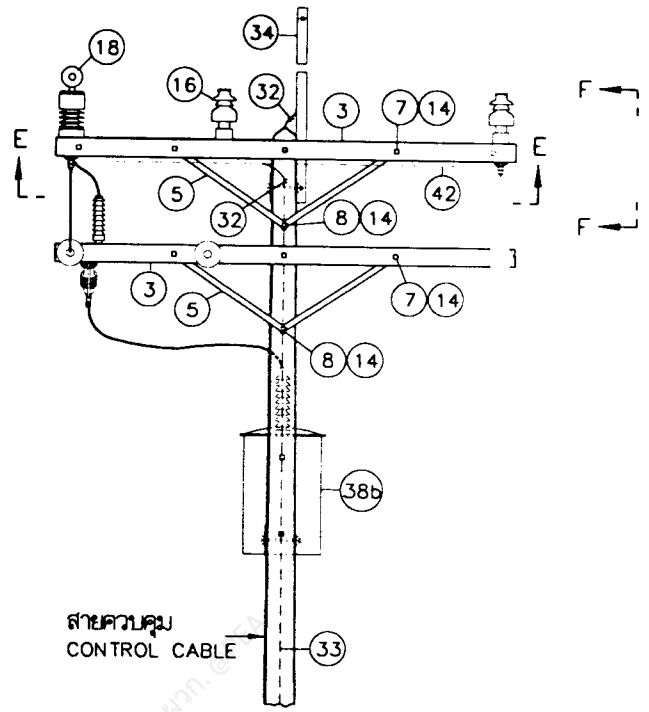


รูปตัด SECTION D–D

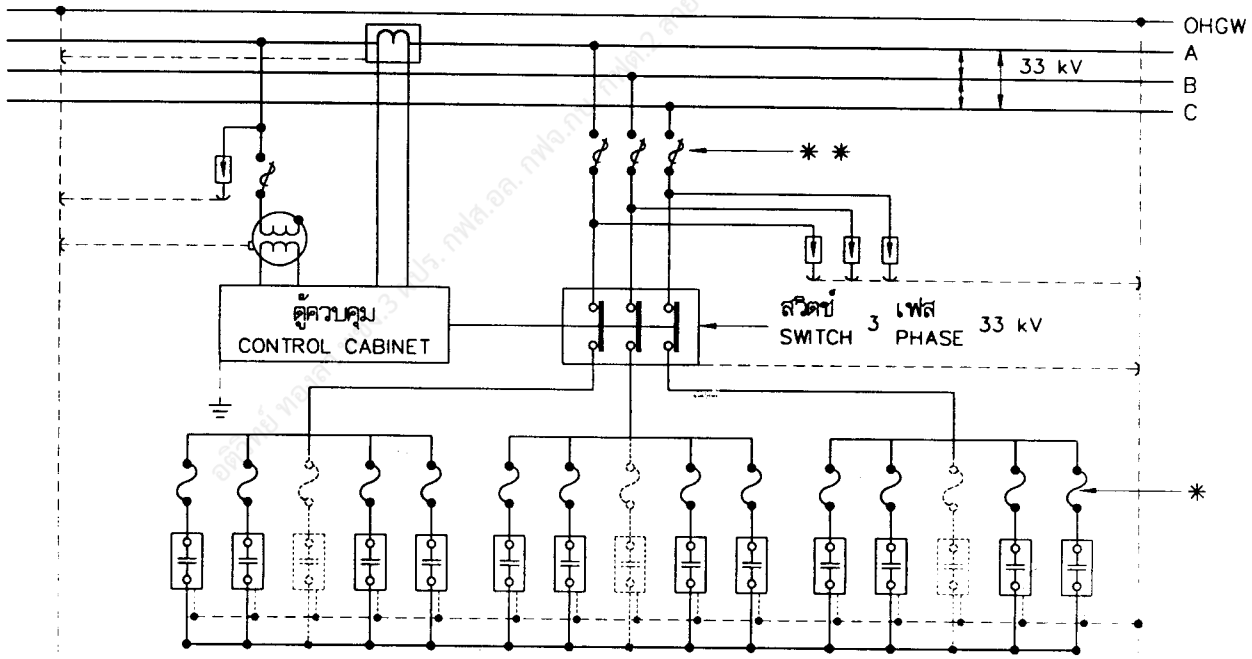


แบบที่ II TYPE แผนภาพแสดงการต่อชุดคะแปซิเตอร์ พร้อมอุปกรณ์ตัดตอน และการต่อลงดิน
CONNECTION DIAGRAM OF CAPACITOR BANK AND EARTHING

กองมาตรฐานระบบไฟฟ้า ฝ่ายมาตรฐานและความปลอดภัย	การไฟฟ้าส่วนภูมิภาค	ใช้แทนแบบ ถูกแทนโดยแบบ เขียนเสร็จวันที่ 8 ก.พ. 2548
ผู้เขียน พงศักดิ์ ศิริสมบูรณ์ ผู้สำรวจ วิศวกร หัวหน้าแผนก ผู้อำนวยการกอง ผู้อำนวยการฝ่าย	ผู้ว่าการ - 8 มี.ค. 2548 การติดตั้งชุดคะแปซิเตอร์ระบบ 33 kV ขนาด 1,200–1,500 kvar พร้อมอุปกรณ์ตัดตอน แบบควบคุมด้วยวาร์	แก้แบบวันที่ มิติเป็น มิลลิเมตร มาตราส่วน 1:50
รองผู้ว่าการวางแผนและพัฒนาระบบไฟฟ้า - 8 มี.ค. 2548	33 kV SWITCHING CAPACITOR BANK INSTALLATION 1,200–1,500 kvar, var CONTROL	แบบเลขที่ SA2-015/48002 แผ่นที่ 4 ของจำนวน 10 แผ่น


การประกอบเลขที่ ASSEMBLY NO.	3607

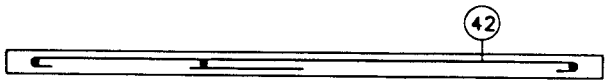

รูปตัด SECTION E-E

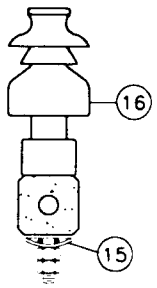


รูปตัด SECTION F-F

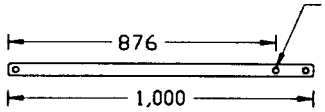

รู HOLE ø18 มม. mm

วัสดุลำดับที่ MAT. ITEM (5) (เจาะรูพิเศษ) (SPECIAL DRILLING)

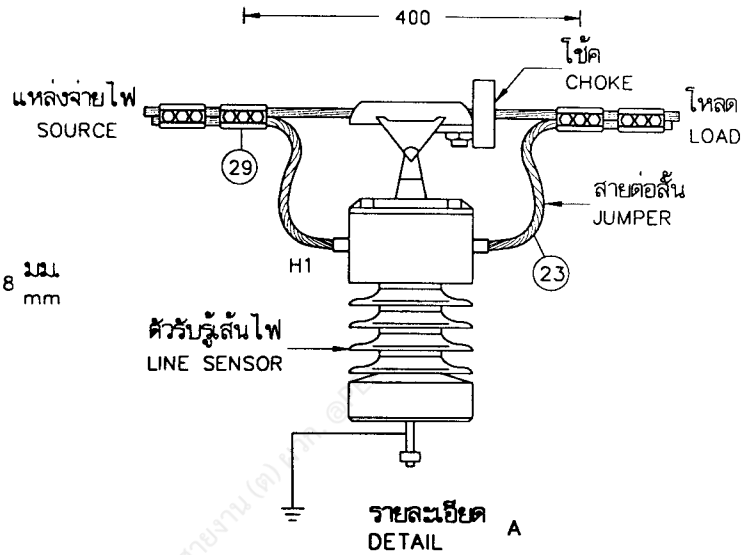

รายละเอียด DETAIL A

ตัวรับรู้สัญญาณไฟ ผลิตภัณฑ์ LINDSEY, MODEL CVMI 9670/C30CO, U.S.A.
LINE SENSOR, TRADE MARK LINDSEY, MODEL CVMI 9670/C30CO, U.S.A.


* *


kvar รวม ของ เพาเวอร์คะแปซิเตอร์ TOTAL POWER CAPACITOR (kvar)	จำนวน x ขนาด (kvar) ของ เพาเวอร์คะแปซิเตอร์ NO. x SIZE (kvar) OF POWER CAPACITOR UNITS	พิกัดกระแสฟิวส์ของสวิตช์ (แอมป์) FUSE RATINGS (AMP)
1,200	12 x 100	30 K
1,500	15 x 100	40 K

* คะแปซิเตอร์ซึ่งมีฟิวส์ป้องกันแต่ละตัว (พิกัดของฟิวส์เป็นขนาด 10 K)
CAPACITOR UNIT WITH INDIVIDUAL FUSE (FUSE RATING SHALL BE 10 K)

กองมาตรฐานระบบไฟฟ้า ฝ่ายมาตรฐานและความปลอดภัย	การไฟฟ้าส่วนภูมิภาค	ใช้แทนแบบ ถูกแทนโดยแบบ
ผู้เขียน พงศักดิ์ ศิริสมบูรณ์ ผู้สำรวจ วิศวกร หัวหน้าแผนก ผู้อำนวยการกอง ผู้อำนวยการฝ่าย	ผู้ว่าการ - 8 มี.ค. 2548	เขียนเสร็จวันที่ 8 กพ. 2548 แก้แบบวันที่
	การติดตั้งชุดคะแปซิเตอร์ระบบ 33 kV ขนาด 1,200-1,500 kvar พร้อมอุปกรณ์ตัดตอน แบบควบคุมด้วยวาร์	มิติเป็น มิลลิเมตร มาตราส่วน
รองผู้ว่าการวางแผนและพัฒนาระบบไฟฟ้า - 8 มี.ค. 2548	33 kV SWITCHING CAPACITOR BANK INSTALLATION 1,200-1,500 kvar, var CONTROL	แบบเลขที่ SA2-015/48002 แผ่นที่ 5 ของจำนวน 10 แผ่น

การประกอบเลขที่ ASSEMBLY NO. 3607

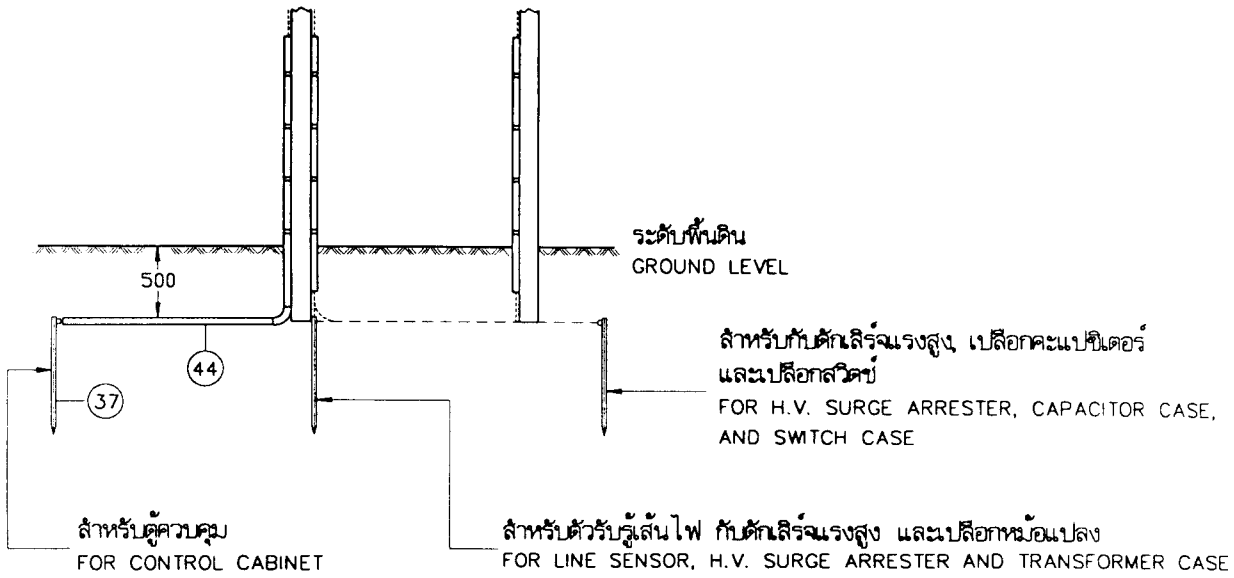

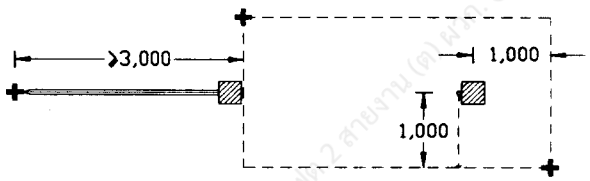

แผนภาพแสดงการต่อลงดิน
EARTHING DIAGRAM

บัญชีวัสดุ
BILL OF MATERIAL

ลำดับที่ ITEM	รายละเอียด DESCRIPTION	จำนวน REQ'D I	จำนวน REQ'D II	วัสดุเลขที่ MAT. NO.
1	เสาคอนกรีต 12 ม. POLE, CONCRETE 12 m LONG	2	2	00010003
2	คอน คอร.สปัน ขนาด 100x100x2,500 มม. CROSSARM, SPUN, PRESTRESSED CONCRETE, 100x100x2,500 mm	2	–	00110001
3	คอน คอร.สปัน ขนาด 120x120x3,000 มม. CROSSARM, SPUN, PRESTRESSED CONCRETE, 120x120x3,000 mm	6	6	00110002
4	เหล็กประกับคอน 30x6x760 มม. BRACE, FLAT, FOR CROSSARM 30x6x760 mm	4	–	01200001
5	เหล็กประกับคอน 40x6x1,000 มม. (เจาะรูพิเศษ) BRACE, FLAT, FOR CROSSARM 40x6x1,000 mm (SPECIAL DRILLING)	8	8	01200002

กองมาตรฐานระบบไฟฟ้า ฝ่ายมาตรฐานและความปลอดภัย	การไฟฟ้าส่วนภูมิภาค	ใช้แทนแบบ ถูกแทนโดยแบบ
ผู้เขียน พงษ์ศักดิ์ ศิริสมบูรณ์ ผู้สำรวจ วิศวกร หัวหน้าแผนก ผู้อำนวยการกอง ผู้อำนวยการฝ่าย	ผู้ว่าการ - 8 มี.ค. 2548	เขียนเสร็จวันที่ 8 ก.พ. 2548 แก้แบบวันที่
	การติดตั้งชุดคะแปซิเตอร์ระบบ 33 kV ขนาด 1,200–1,500 kvar พร้อมอุปกรณ์ตัดตอน แบบควบคุมด้วยวาร์	มิติเป็น มิลลิเมตร มาตราส่วน
รองผู้ว่าการวางแผนและพัฒนาระบบไฟฟ้า - 8 มี.ค. 2548	33 kV SWITCHING CAPACITOR BANK INSTALLATION 1,200–1,500 kvar, var CONTROL	แบบเลขที่ SA2-015/48002 แผ่นที่ 6 ของจำนวน 10 แผ่น

การประกอบเลขที่ ASSEMBLY NO. 3607

บัญชีวัสดุ BILL OF MATERIAL

ลำดับที่ ITEM	รายละเอียด DESCRIPTION	จำนวน REQ'D I	จำนวน REQ'D II	วัสดุเลขที่ MAT. NO.
6	สลักเกลียว M 16x130 มม. BOLT, MACHINE, M 16x130 mm	4	–	01110200
7	สลักเกลียว M 16x170 มม. BOLT, MACHINE, M 16x170 mm	8	8	01110201
8	สลักเกลียว M 16x200 มม. BOLT, MACHINE, M 16x200 mm	5	5	01110202
9	สลักเกลียว M 16x250 มม. BOLT, MACHINE, M 16x250 mm	4	7	01110203
10	สลักเกลียว M 16x300 มม. BOLT, MACHINE, M 16x300 mm	10	10	01110204
11	สลักเกลียว M 16x350 มม. BOLT, MACHINE, M 16x350 mm	2	2	01110205
12	สลักเกลียว M 16x400 มม. BOLT, MACHINE, M 16x400 mm	3	2	01110206
13	สลักเกลียวห่วงกลม M 16x400 มม. BOLT, DOUBLE ARMING, ROUND EYE M 16x400 mm	6	6	01130000
14	แหวนสี่เหลี่ยมแบน 52x52x4.5 มม. รู ø18 มม. มอก. 258 WASHER, SQUARE, FLAT 52x52x4.5 mm HOLE ø18 mm TIS 258	56	62	01180100
15	แหวนสี่เหลี่ยมโค้ง 60x60x5 มม. รู ø22 มม. WASHER, SQUARE, CURVED 60x60x5 mm HOLE ø22 mm	6	6	01180201
16	ลูกถ้วย 33 kV แบบตามต้องการ INSULATOR 33 kV, CLASS AS REQUIRED	5	5	03010003-4 03010102-3 03000003
17	ลูกถ้วยแขวน มอก. 354 แบบ ง (แบบ 52-4) INSULATOR, SUSPENSION TYPE, TIS 354, TYPE D (CLASS 52-4)	18	18	03020002
18	ตัวรับรู้เส้นไฟ LINE SENSOR	1 ชุด set	1 ชุด set	04070308
19	กับดักเสิร์จ 30 kV, 10 kA SURGE ARRESTER, 30 kV, 10 kA	5	4	04000101
20	ดรอพเอาต์ ฟิวส์คัตเอาต์ หนึ่งอินซูเลเตอร์ 33 kV, 100 แอมป์ CUT-OUT, FUSE, OPEN TYPE, SINGLE INSULATOR DROPOUT 33 kV, 100 A	5	4	04010100
21	โครงเหล็กแขวนสำหรับคะแปซิเตอร์ต่อร่วมกัน พร้อมด้วยสวิตช์ ฟิวส์ป้องกันแต่ละตัว ตู้ควบคุม และเคเบิลควบคุม สำหรับระบบ 33 kV STEEL STRUCTURE FOR BANK CAPACITOR COMPLETE WITH SWITCH, INDIVIDUAL CAPACITOR, FUSE, CONTROL CABINET AND CONTROL CABLE FOR 33 kV SYSTEM	1 ชุด set	1 ชุด set	04030105 04070302 04070110-1 05110002
22	คะแปซิเตอร์ 1 เฟส หนึ่งบุชชิ่ง ใช้นอกอาคาร 33 GRDY/19 kV, 100kvar จำนวนตามต้องการ CAPACITOR, POWER, SINGLE-PHASE, SINGLE BUSHING, OUTDOOR 33 GRDY/19 kV, 100 kvar, QUANTITY AS REQUIRED	ชุด set	ชุด set	05050100

กองมาตรฐานระบบไฟฟ้า ฝ่ายมาตรฐานและความปลอดภัย	การไฟฟ้าส่วนภูมิภาค	ใช้แทนแบบ ถูกแทนโดยแบบ
ผู้เขียน พยุงศักดิ์ ศิริสมบูรณ์ ผู้สำรวจ วิศวกร หัวหน้าแผนก ผู้อำนวยการกอง ผู้อำนวยการฝ่าย	ผู้ว่าการ - 8 มี.ค. 2548 การติดตั้งชุดคะแปซิเตอร์ระบบ 33 kV ขนาด 1,200-1,500 kvar พร้อมอุปกรณ์ตัดตอน แบบควบคุมด้วยวาร์	เขียนแล้วเสร็จวันที่ 8 ก.พ. 2548 แก้แบบวันที่ มิติเป็น มาตราส่วน
รองผู้ว่าการวางแผนและพัฒนาระบบไฟฟ้า - 8 มี.ค. 2548	33 kV SWITCHING CAPACITOR BANK INSTALLATION 1,200-1,500 kvar, var CONTROL	แบบเลขที่ SA2-015/48002 แผ่นที่ 7 ของจำนวน 10 แผ่น

การประกอบเลขที่ ASSEMBLY NO. 3607

บัญชีวัสดุ
BILL OF MATERIAL

ลำดับที่ ITEM	รายละเอียด DESCRIPTION	จำนวน REQ'D I	จำนวน REQ'D II	วัสดุเลขที่ MAT. NO.
23	สายอะลูมิเนียมเปลือย 185 ตร.มม. CONDUCTOR, Al, BARE 185 mm²	1.2 ม. m	1.2 ม. m	02010007
24	สายอะลูมิเนียมหุ้มฉนวน PVC 750 V, 75° C หรือสายอะลูมิเนียมหุ้มฉนวนแบบไม่เต็มพิกัด 33 kV หรือเคเบิลอากาศ 33 kV ขนาด 50–95 ตร.มม. CABLE, Al, PVC INSULATED, 750 V, 75° C OR PARTIALLY INSULATED 33 kV OR CABLE, AERIAL, Al 33 kV, 50–95 mm²	30 ม. m	30 ม. m	02070002-4 or 02050100-1 02060101-2
25	เคเบิลอากาศ 33 kV, 1x50 ตร.มม. หรือขนาดที่ต้องการ ตามความเหมาะสม CABLE, AERIAL Al 33 kV, 1x50 mm² OR SIZE AS REQUIRED	24 ม. m	24 ม. m	02050100
26	เทปพันเคเบิลอากาศแรงสูง ELECTRICAL SPLICING TAPE, FOR H.T. AERIAL CABLE	4 ม้วน roll	4 ม้วน roll	02180003
27	เทปไฟฟ้า PVC หรือเทปไฟฟ้ายางซิลิโคน PVC. PLASTIC OR SILICONE RUBBER ELECTRICAL TAPE	10 ม. m	10 ม. m	02180002 or 02180004
28	P.G. คอนเนคเตอร์ สลักคู่ สำหรับสายอะลูมิเนียม ขนาด 25–95 ตร.มม. CONNECTOR, PARALLEL GROOVE, DOUBLE BOLT, Al 25–95 mm²	8	7	02300102
29	P.G. คอนเนคเตอร์ 3 สลัก สำหรับสายอะลูมิเนียม ขนาด 70–185 ตร.มม. CONNECTOR, PARALLEL GROOVE, TRIPLE BOLT, Al 70–185 mm²	4	4	02300103
30	สเตอร์รัพแคล้มป์ หรือเบลแคล้มป์ และฮอทไลน์แคล้มป์ ขนาดตามต้องการ CLAMP, STIRRUP OR BAIL AND CLAMP, HOT LINE, SIZE AS REQUIRED	5	4	02330000-1 02330100-1
31	สเตรนแคล้มป์ สำหรับสายอะลูมิเนียม 50–95 ตร.มม. CLAMP, STRAIN, Al 50–95 mm²	6	6	03110000-1
32	ยูแคล้มป์ สลัก 1 ตัว M 8 CLAMP, SINGLE U-BOLT M 8	25	27	01230000
33	ลวดเหล็กตีเกลียว 50/7 ตร.มม. พร้อมอุปกรณ์ยึด (การประกอบเลขที่ 9703,9703A) WIRE, STEEL STRANDED, 50/7 mm², COMP. WITH FIXING ACCESS. (ASSEMBLY NO. 9703, 9703A)	60 ม. m	60 ม. m	01100004
34	เหล็กฉากรับสายล่อฟ้าทางตรง ขนาด 65x65x6 มม. ยาว 2.25 ม. OVERHEAD GROUND WIRE BAYONET ANGLE STEEL, 65x65x6 mm, 2.25 m LONG	1	2	01010003
35	กราวด์ไวร์แคล้มป์ แบบ J 1152 GROUND WIRE CLAMP, J 1152	1	2	01230205
36	ท่อ PVC ขนาด ø 20x2,500–4,000 มม. พร้อมอุปกรณ์ยึด แบบเลขที่ SA1-015/31013 PIPE, PVC ø 20x2,500–4,000 mm COMPLETE WITH FIXING ACCESS. DWG. NO. SA1-015/31013	3	3	08040002
37	หลักดิน ขนาด 60x60x5 มม. ยาว 2 ม. ROD, GROUND 60x60x5 mm 2 m LONG	3	3	01220002
38a	หม้อแปลงหนึ่งเฟส 500 VA, 33/0.22 kV พร้อมอุปกรณ์ติดตั้ง TRANSFORMER, 1ø, 500 VA, 33/0.22 kV, COMP. WITH MOUNTING ACCESS.	1	–	04070310
38b	หม้อแปลงหนึ่งเฟส 19/0.22 kV สำหรับจ่ายไฟให้ชุดควบคุมอัตโนมัติ TRANSFORMER, 1ø, 19/0.22 kV, FOR CONTROL UNIT	–	1	

กองมาตรฐานระบบไฟฟ้า ฝ่ายมาตรฐานและความปลอดภัย	การไฟฟ้าส่วนภูมิภาค	ใช้แทนแบบ ..... ถูกแทนโดยแบบ .....
ผู้เขียน พยุงศักดิ์ ศิริสมบูรณ์ ..... ผู้สำรวจ ..... วิศวกร ..... หัวหน้าแผนก ..... ผู้อำนวยการกอง ..... ผู้อำนวยการฝ่าย	ผู้ว่าการ ..... - 8 มี.ค. 2548	เขียนเสร็จวันที่ 8 ก.พ. 2548 แก้แบบวันที่ ..... มิติเป็น ..... มาตราส่วน .....
รองผู้ว่าการวางแผนและพัฒนาระบบไฟฟ้า ..... - 8 มี.ค. 2548	การติดตั้งชุดคะแปซิเตอร์ระบบ 33 kV ขนาด 1,200–1,500 kvar พร้อมอุปกรณ์ตัดตอน แบบควบคุมด้วยวาร์ 33 kV SWITCHING CAPACITOR BANK INSTALLATION 1,200–1,500 kvar, var CONTROL	แบบเลขที่ SA2-015/48002 แผ่นที่ 8 ของจำนวน 10 แผ่น

การประกอบเลขที่ ASSEMBLY NO. 3607

บัญชีวัสดุ
BILL OF MATERIAL

ลำดับที่ ITEM	รายละเอียด DESCRIPTION	จำนวน REQ'D I	จำนวน REQ'D II	วัสดุเลขที่ MAT. NO.
39	เหล็กจับขอบถังหม้อแปลง สำหรับยึดสายแรงต่ำ BRACKET, STEEL, FOR TRANSFORMER SECONDARY LEAD	–	1	05100003
40	ลูกรอกแรงต่ำ มอก. 227 แบบ ข (แบบ 53-2) INSULATOR, SPOOL TYPE, TIS 227 TYPE B (CLASS 53-2)	–	1	03030000
41	ลวดอะลูมิเนียมกลม 4 มม. ความยาวตามต้องการ TIE WIRE, Al 4 mm LENGTH AS REQUIRED	–	3.5 ม. m	01100000
42	ลวดเหล็กกลม เส้นผ่านศูนย์กลาง 4 มม. เส้นเดี่ยว (มอก. 71) WIRE, STEEL, SOLID, DIAMETER 4 mm (TIS 71)	8 ม. m	8 ม. m	01100000
43	แหวนรองแบบสปริง M 16 มม. มอก. 259 WASHER, LOCK, SPRING M 16 TIS 259	2	2	01180301
44	ท่อ PVC แข็ง ขนาด ø 20x4,000 มม. พร้อมท่อโค้ง 90° CONDUIT, PVC RIGID, ø 20x4,000 mm COMP. WITH 90° ELBOW	1	1	08040001
45	แป้นไม้สำหรับยึดสายเข้า และออกจากมิเตอร์ ไสแล้ว ขนาด 20x20x2 ซม. CABLE PLATE, HARD WOOD, SURFACE FINISHED, 20x20x2 cm	4	4	06100000
46	เข็มขัดรัดสาย (ทำด้วยลวดอะลูมิเนียมแบน 1x10 มม.) CABLE STRAP (MADE OF ARMOUR TAPE 1x10 mm)	1 ม. m	1 ม. m	01100000
47	ตะปูหัวกลมแบน ยาว 15-20 มม. ø 1 มม. มอก. 113 NAIL, ROUND, MILD STEEL WIRE 15-20 mm LONG ø 1 mm TIS 113	8	8	——
	สำหรับการติดตั้งระบบจำหน่ายแรงต่ำ (กรณีที่ต้องการ) FOR LOW VOLTAGE SYSTEM INSTALLATION (IF REQUIRED)			
48	คอนเน็คเตอร์เข้าปลายสายอะลูมิเนียม ขนาด และจำนวนตามต้องการ CONNECTOR, DEAD END, Al; SIZE AND QUANTITY AS REQUIRED			02310000-2
49	สายอะลูมิเนียมหุ้มฉนวน PVC, 750 V, 75° C ขนาด และความยาวตามต้องการ CABLE, Al PVC, INSULATED, 750 V, 75° C SIZE AND LENGTH AS REQUIRED	ม. m	ม. m	02070002-4
50	สลักเกลียว M 16x250 มม. จำนวนตามต้องการ BOLT, MACHINE, M 16x250 mm ; QUANTITY AS REQUIRED			01110203
51	แหวนสี่เหลี่ยมแบน 52x52x4.5 มม. รู ø18 มม. มอก. 258 จำนวนตามต้องการ WASHER, SQUARE, FLAT 52x52x4.5 mm HOLE ø18 mm TIS 258 QUANTITY AS REQUIRED			01180100
52	แร็คแรงต่ำแบบหลังยื่น ขนาดตามต้องการ RACK, SECONDARY MEDIUM PRESSED STEEL EXTENDED BACK, SIZE AS REQUIRED	2	2	03130000 03130002
53	ที่จับลูกรอก สำหรับลูกรอกแรงต่ำ จำนวนตามต้องการ CELVIS, FLAT STEEL FOR SPOOL INSULATOR ; QUANTITY AS REQUIRED			03130100
54	ลูกรอกแรงต่ำ มอก. 227 แบบ ข (แบบ 53-2) จำนวนตามต้องการ INSULATOR, SPOOL TYPE, TIS 227 TYPE B (CLASS 53-2) QUANTITY AS REQUIRED			03030000
55	ลวดอะลูมิเนียมกลม ขนาด ø 4 มม. จำนวนตามต้องการ TIE WIRE Al ø 4 mm ; QUANTITY AS REQUIRED	กก. kg	กก. kg	01100000

กองมาตรฐานระบบไฟฟ้า
ฝ่ายมาตรฐานและความปลอดภัย

ผู้เขียน พงษ์ศักดิ์ ศิริสมบูรณ์
ผู้สำรวจ
วิศวกร
หัวหน้าแผนก
ผู้อำนวยการกอง
ผู้อำนวยการฝ่าย

รองผู้ว่าการวางแผนและพัฒนาระบบไฟฟ้า
- 8 มี.ค. 2548

การไฟฟ้าส่วนภูมิภาค

ผู้ว่าการ - 8 มี.ค. 2548

การติดตั้งชุดคะแปซิเตอร์ระบบ 33 kV ขนาด 1,200-1,500 kvar
พร้อมอุปกรณ์ปิดตอน แบบควบคุมด้วยวาร์

33 kV SWITCHING CAPACITOR BANK INSTALLATION
1,200-1,500 kvar, var CONTROL

ใช้แทนแบบ
ถูกแทนโดยแบบ
เขียนเสร็จวันที่ 8 กพ. 2548
แก้แบบวันที่
มิติเป็น
มาตราส่วน

แบบเลขที่ SA2-015/48002
แผ่นที่ 9 ของจำนวน 10 แผ่น

การประกอบเลขที่ ASSEMBLY NO.	3607

ลำดับที่ ITEM	แบบอ้างอิง REFERENCE DRAWING	แบบเลขที่ DWG. NO.	การประกอบเลขที่ ASSEMBLY NO.
1	มาตรฐานระยะห่างที่ปลอดภัยในการก่อสร้างทางไฟฟ้า STANDARD MINIMUM SAFE CLEARANCES FOR ELECTRICAL CONSTRUCTION	SA2-015/45017	9301

คำแนะนำในการติดตั้ง

1 ติดตั้งตัวรับรู้สัญญาณไฟแทนที่ลูกถ้วยเดิมที่มีอยู่
2 ส่วนที่เป็นโลหะของตัวรับรู้สัญญาณไฟ ต้องต่อลงดิน
3 เสียบสายสัญญาณจากตู้ควบคุมเข้ากับตัวต่อ ที่ฐานของตัวรับรู้สัญญาณไฟ
4 วางตัวนำบนตัวรับรู้สัญญาณไฟ ยึดให้แน่น แต่ห้ามปิดโช้กก่อนติดตั้งสายต่อลัด (JUMPER)
5 ติดตั้งสายต่อลัด แล้วจึงปิดโช้ค

INSTALLATION INSTRUCTION

1 THE LINE SENSOR IS USED TO REPLACE AN EXISTING INSULATOR .
2 THE LINE SENSOR HARDWARE SHALL BE BONDED TO GROUND .
3 PLUG THE SIGNAL WIRE FROM CONTROL CABINET IN TO THE CONNECTOR AT THE BASE OF LINE SENSOR .
4 PLACE THE CONDUCTOR ON TOP OF THE LINE SENSOR AND SECURE ; BUT DO NOT CLOSE THE CHOKE UNTIL AFTER THE JUMPER HAS BEEN INSTALLED .
5 INSTALL THE JUMPER AND CLOSE THE CHOKE .

หมายเหตุ :

แบบการติดตั้งนี้ใช้สำหรับชุดควบคุมการปลด – สับคะแปซิเตอร์ แบบควบคุมด้วยวาร์พร้อมตัวรับรู้สัญญาณไฟ (LINE SENSOR) ทำโดยบริษัท ซัมมิท เพาเวอร์ ซิสเต็ม จำกัด โดยมีตัวรับรู้สัญญาณไฟเป็นผลิตภัณฑ์ LINDSEY รุ่น CVMI 9670/C30CO, U.S.A.

NOTE :

THIS DRAWING IS APPLICABLE FOR var CONTROL SWITCHING CAPACITOR CONTROL UNIT MADE BY SUMMIT POWER SYSTEM CO., LTD. WITH LINE SENSOR OF LINDSEY PRODUCT, MODEL CVMI 9670/C30CO, U.S.A.

กองมาตรฐานระบบไฟฟ้า ฝ่ายมาตรฐานและความปลอดภัย	การไฟฟ้าส่วนภูมิภาค	ใช้แทนแบบ ถูกแทนโดยแบบ
ผู้เขียน พยุงศักดิ์ ศิริสมบูรณ์ ผู้สำรวจ วิศวกร หัวหน้าแผนก ผู้อำนวยการกอง ผู้อำนวยการฝ่าย	ผู้ว่าการ - 8 มี.ค. 2548 การติดตั้งชุดคะแปซิเตอร์ระบบ 33 kV ขนาด 1,200-1,500 kvar พร้อมอุปกรณ์ตัดตอน แบบควบคุมด้วยวาร์	เขียนเสร็จวันที่ 8 ก.พ. 2548 แก้แบบวันที่ มิติเป็น มาตราส่วน
รองผู้ว่าการวางแผนและพัฒนาระบบไฟฟ้า - 8 มี.ค. 2548	33 kV SWITCHING CAPACITOR BANK INSTALLATION 1,200-1,500 kvar, var CONTROL	แบบเลขที่ SA2-015/45002 แผ่นที่ 10 ของจำนวน 10 แผ่น