การประกอบเลขที่
ASSEMBLY NO. **3707**

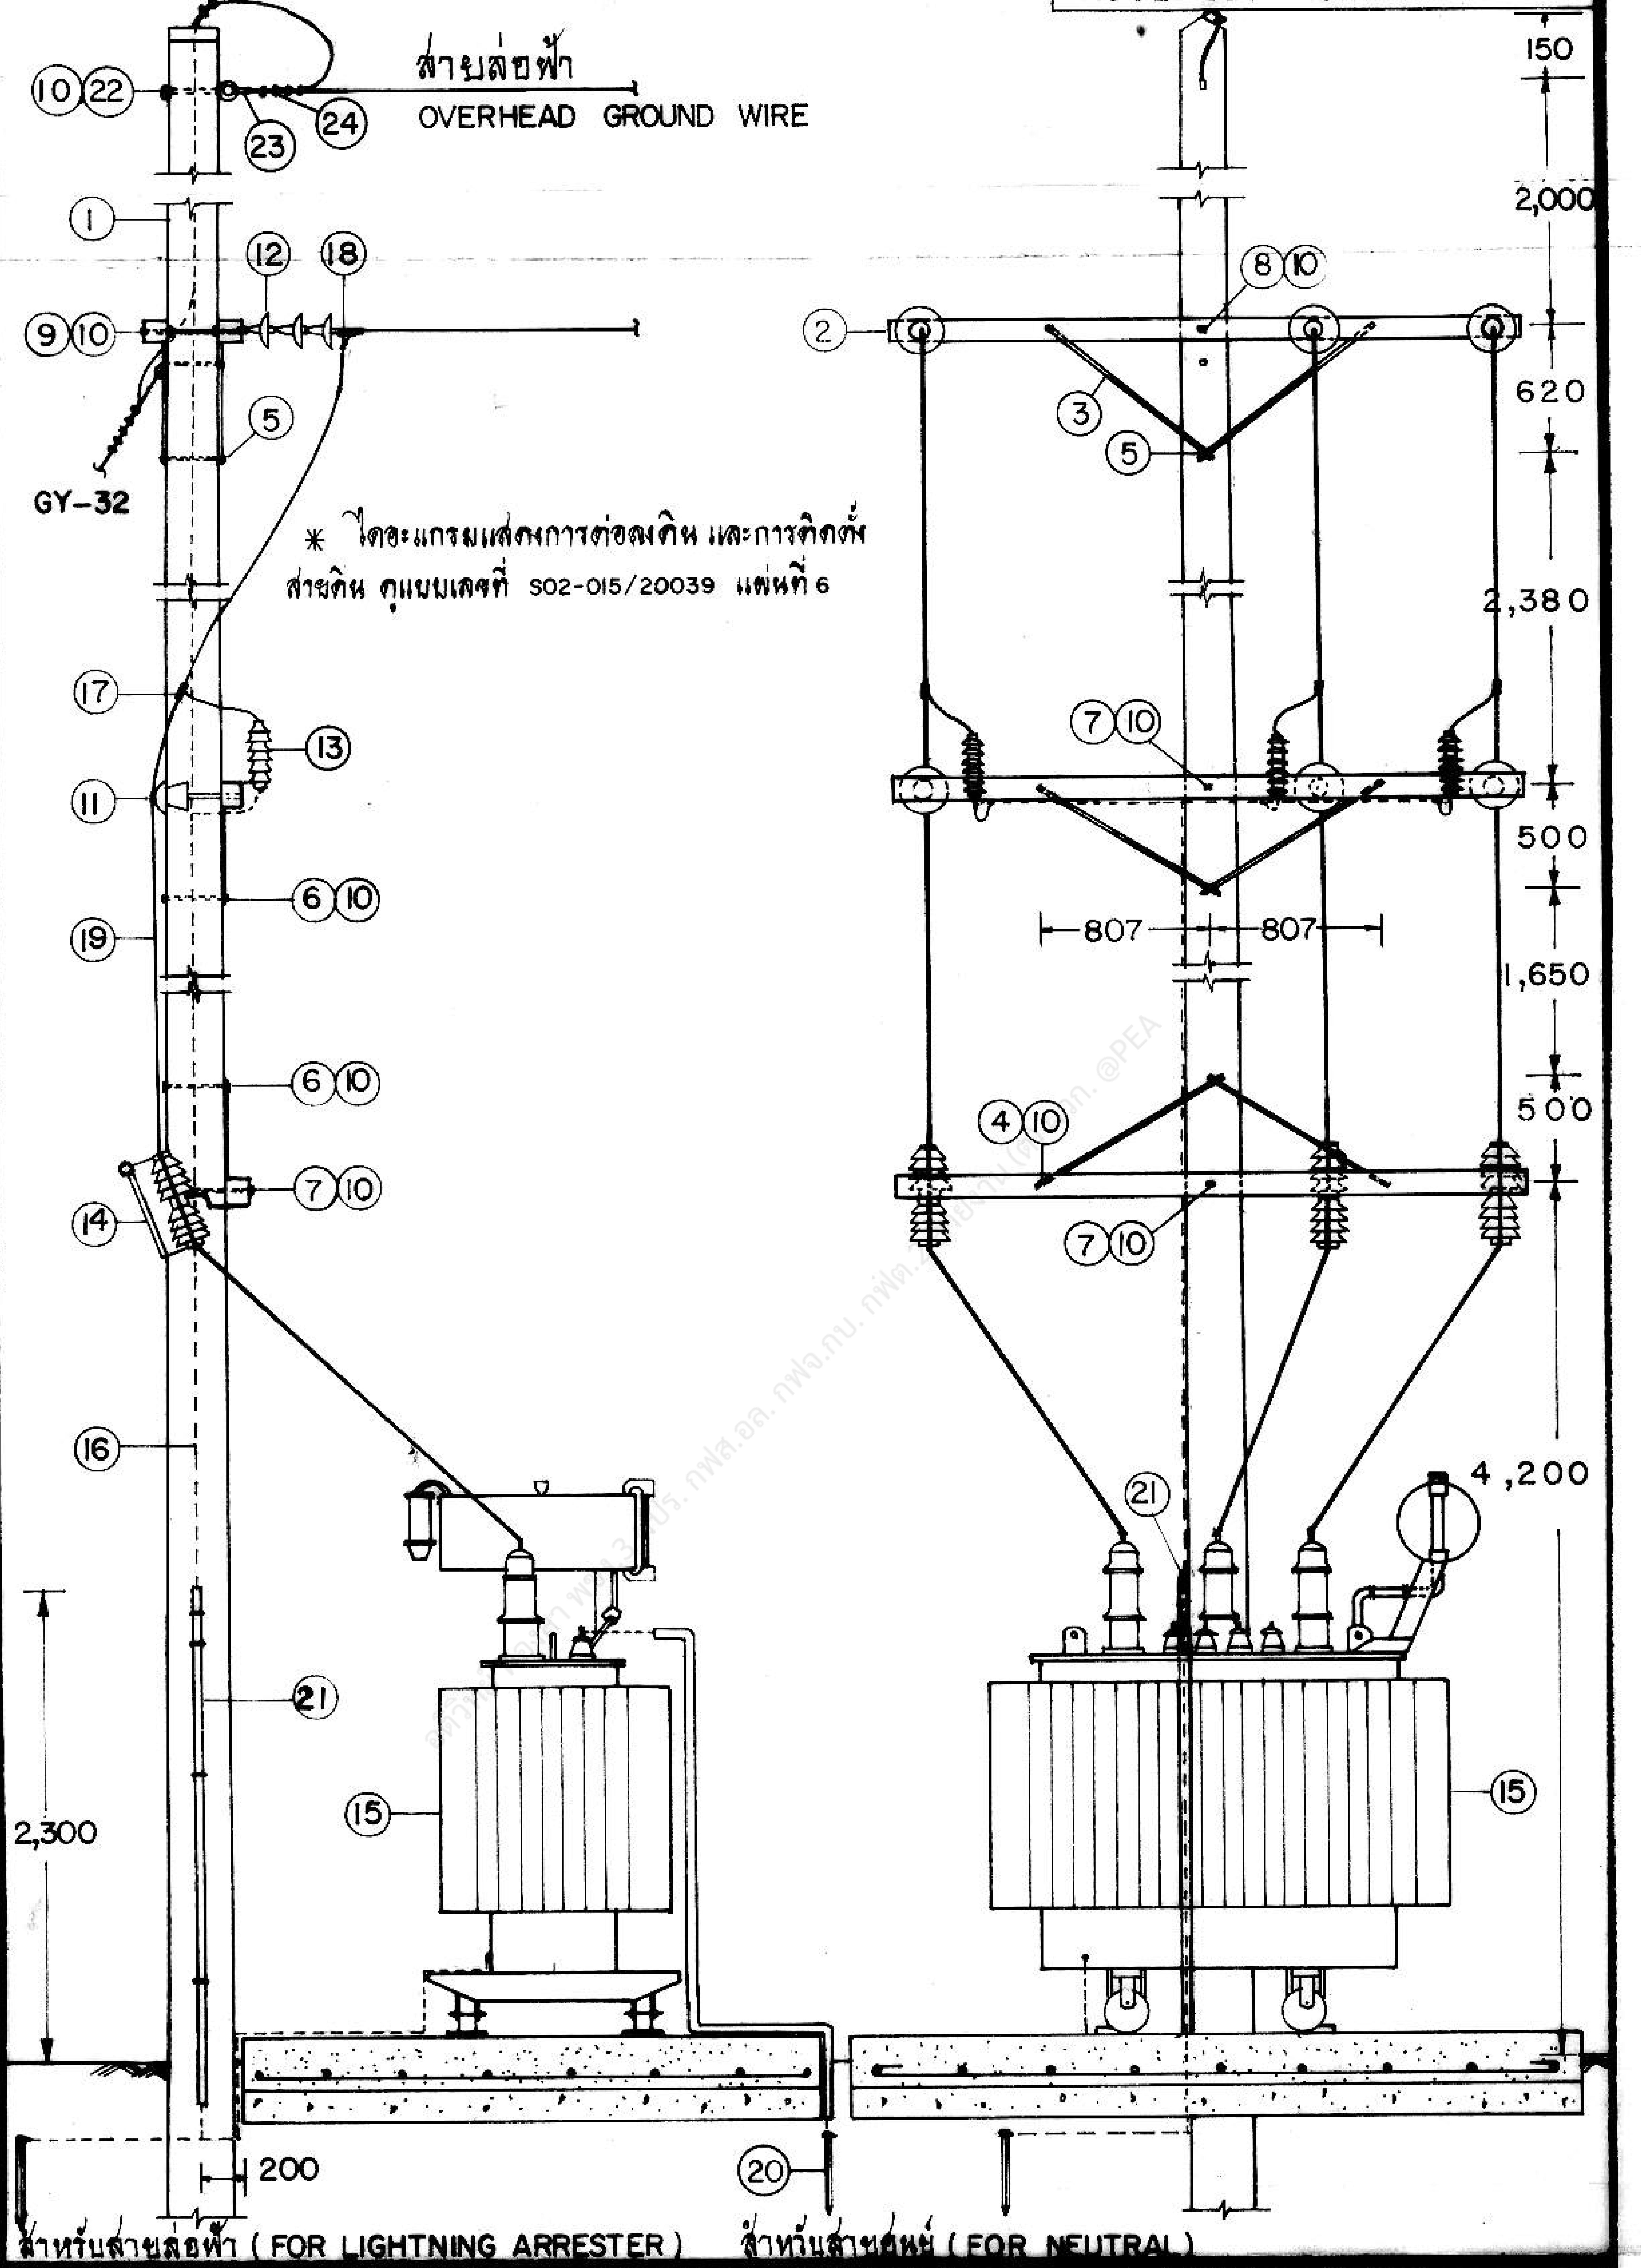

* ไดอะแกรมแสดงการต่อลงดิน และการติดตั้ง
สายดิน ดูแบบเลขที่ S02-015/20039 แผ่นที่ 6

กองวิศวกรรม

ผู้เขียน..........
สถาปนิก..........
วิศวกร..........
หัวหน้าแผนก..........
ผู้อำนวยการกอง..........
รองผู้ว่าการฝ่ายเทคนิค
....

การไฟฟ้าส่วนภูมิภาค

ผู้ว่าการ..........

การติดตั้งหม้อแปลง ระบบ 33 kV
315 – 2000 kVA สำหรับโรงงานอุตสาหกรรม
ก. เสาเดี่ยวต้นสุดท้าย เสาคอนกรีต 14 เมตร

TRANSFORMER INSTALLATION 33 kV
315 – 2000 kVA FOR INDUSTRIAL
A SINGLE POLE, DEADEND, CONCRETE POLE 14 m

ใช้แทนแบบ..........
ถูกแทนโดยแบบ..........
เขียนเสร็จวันที่ 21 มิ.ย. 17
แก้แบบวันที่..........
มิติเป็น มม.
มาตราส่วน 1 : 50

แบบเลขที่ S02-015/17040

แผ่นที่ 1 ของจำนวน 3 แผ่น

การประกอบเลขที่
ASSEMBLY NO. 3707

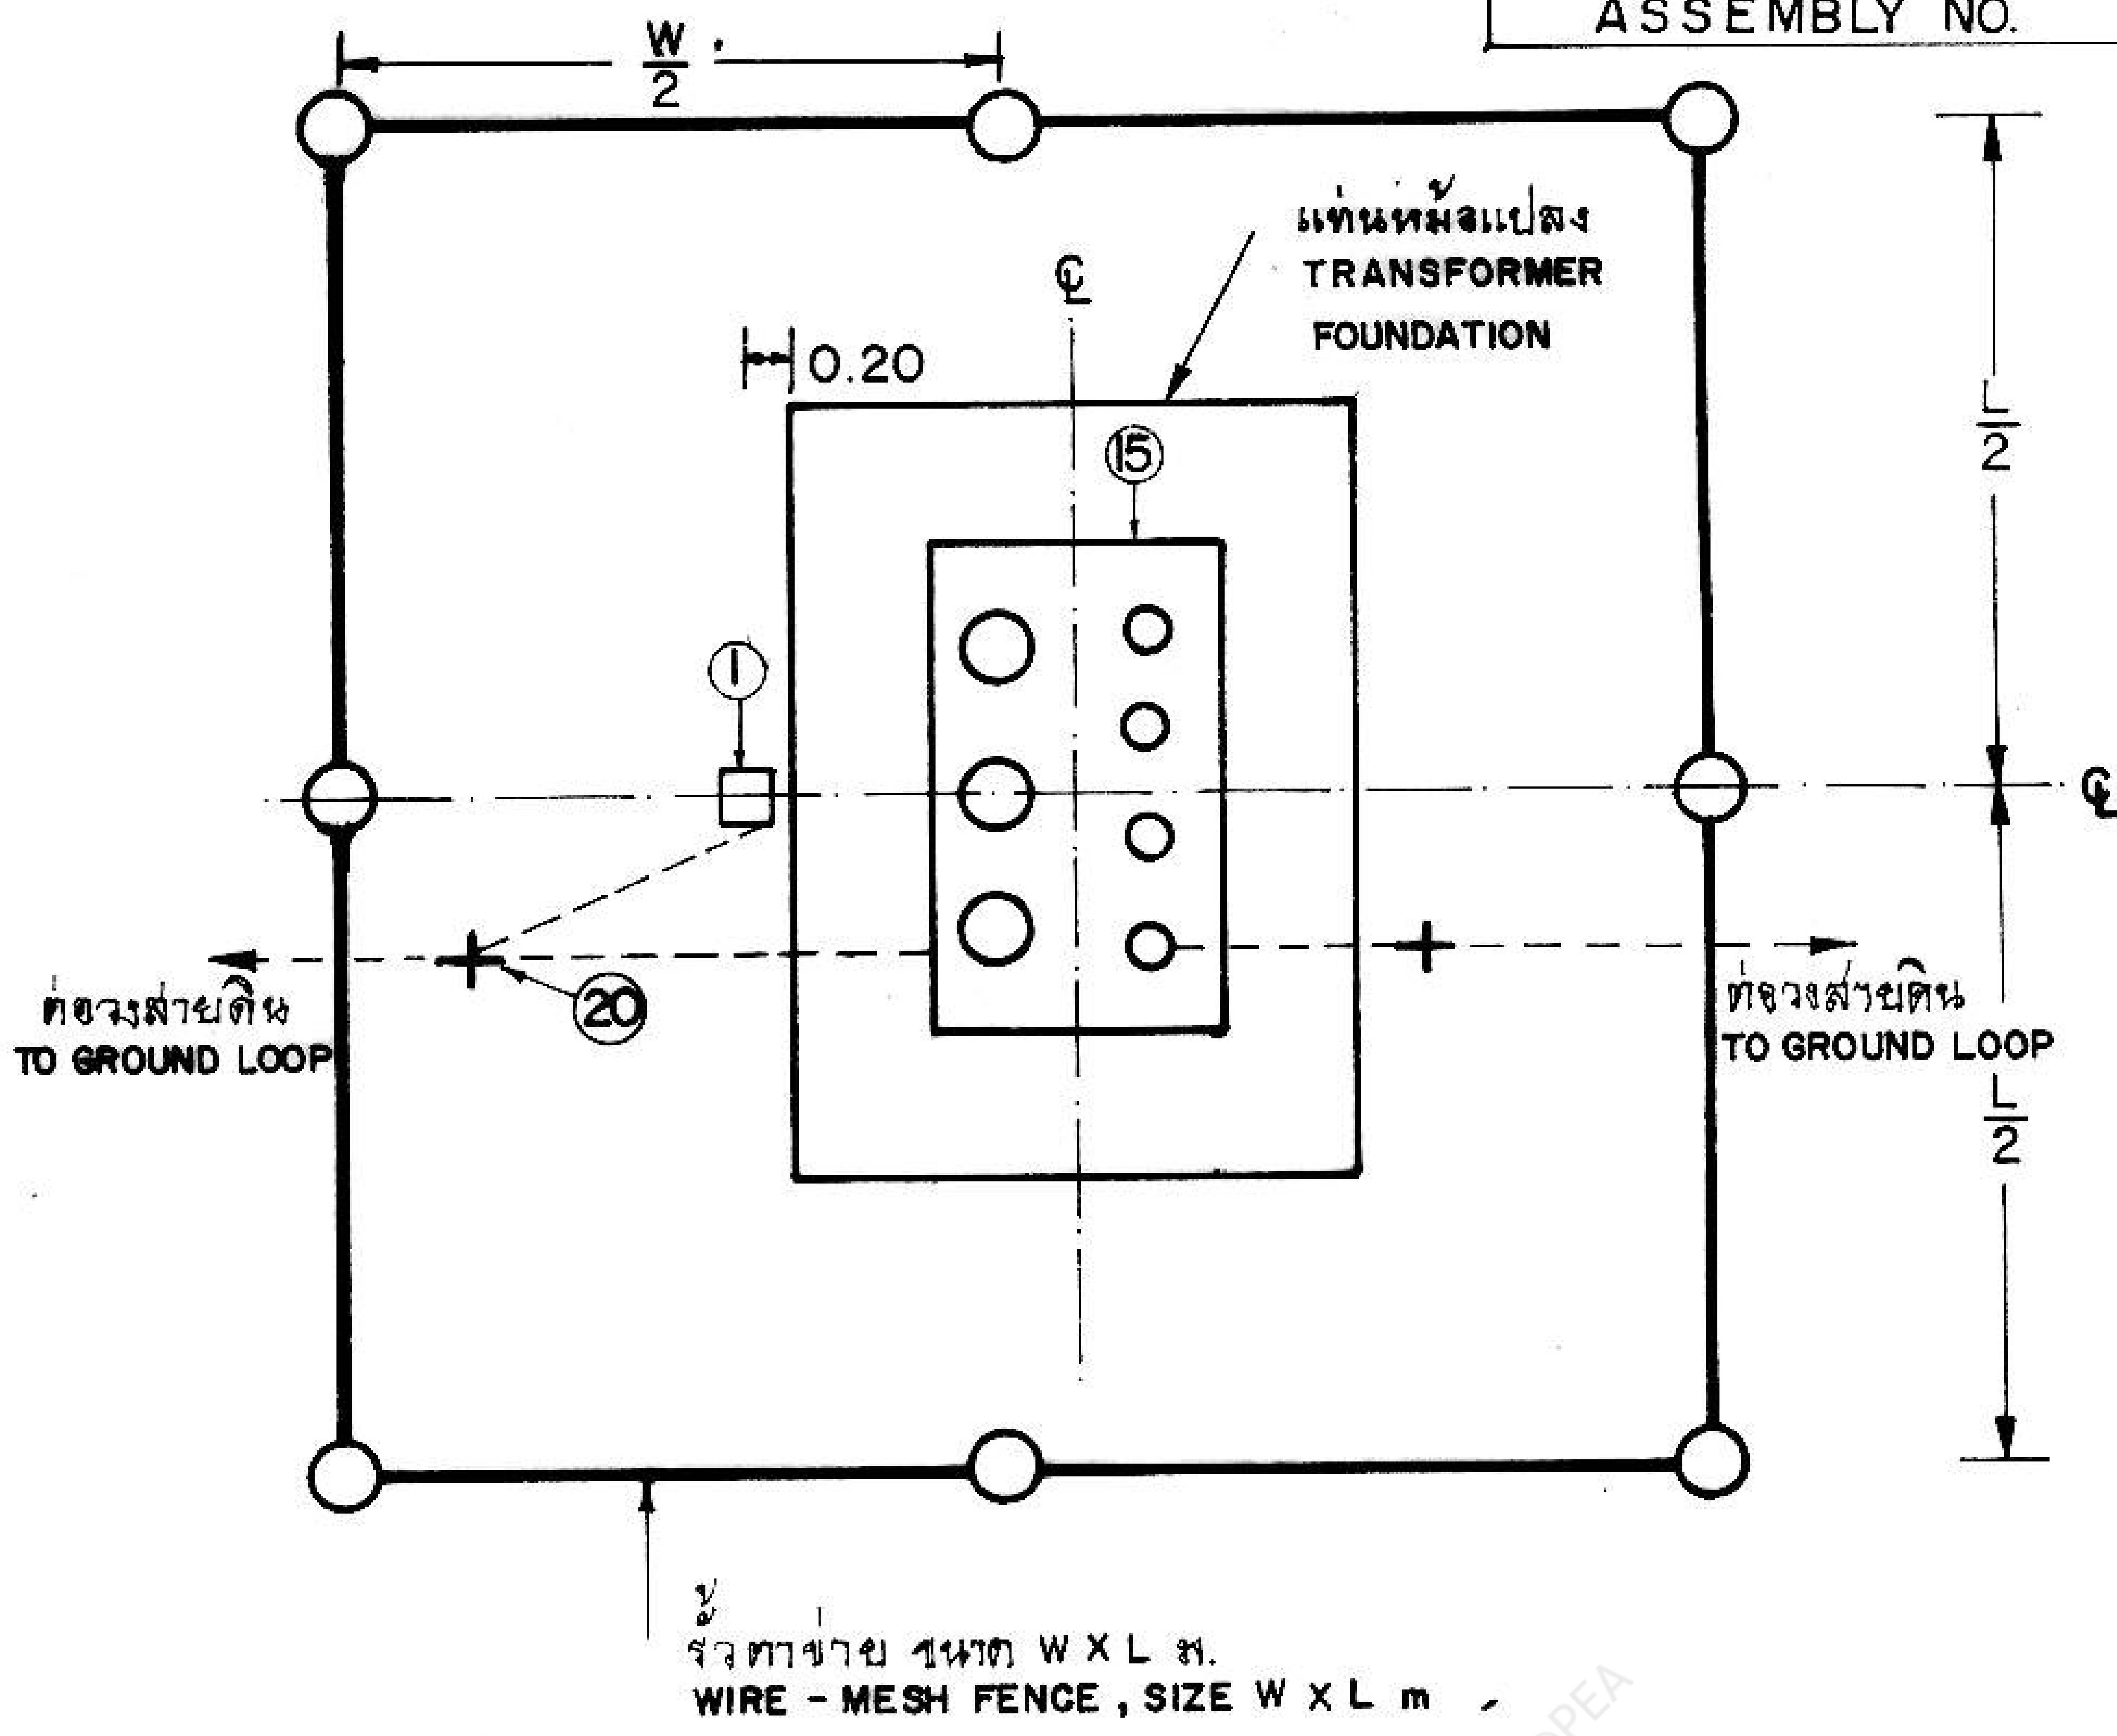

หมายเหตุ

1 แท่นตั้งหม้อแปลง ดูแบบเลขที่ I 41-015/090466
2 รั้วตาข่ายล้อมหม้อแปลง และการต่อลงดิน ดูแบบเลขที่ SAI-015/23061
3 ล้อหม้อแปลงทั้งหมดจะต้องจัดทำที่สำหรับกั้นไม่ให้หม้อแปลงเคลื่อนที่ได้
4 เลือกตำแหน่งประตู ช่องรั้วถอดได้ ตามแต่เหมาะสม
5 ด้านแรงต่ำผู้ใช้ไฟเป็นผู้จัดทำ

NOTES

1 TRANSFORMER FOUNDATION SEE DRAWING NO. I 41-015/090466.
2 TRANSFORMER WIRE-MESH FENCE AND GROUNDING SEE DRAWING NO. SAI-015/23061
3 ALL ROLLERS SHALL BE FIXED TO THE TRANSFORMER FOUNDATION.
4 SUITABLE POSITION FOR GATE AND MOVABLE CHANNEL.
5 LOW TENSION SIDE SHALL BE PROVIDED BY CUSTOMER.

กองวิศวกรรม
ผู้เขียน
สถาปนิก
วิศวกร
หัวหน้าแผนก
ผู้อำนวยการกอง
รองผู้ว่าการฝ่ายเทคนิค

การไฟฟ้าส่วนภูมิภาค
ผู้ว่าการ

การติดตั้งหม้อแปลง ระบบ 33 kV
315-2000 kVA สำหรับโรงงานอุตสาหกรรม
ค แผนผังการติดตั้ง และการต่อลงดิน

TRANSFORMER INSTALLATION 33 kV
315-2000 kVA FOR INDUSTRIAL
C FOUNDATION AND GROUNDING

ใช้แทนแบบ
ถูกแทนโดยแบบ
เขียนเสร็จวันที่ 25 มิ.ย.17
แก้แบบวันที่
มิติเป็น เมตร
มาตราส่วน 1 : 75
แบบเลขที่ S02-015/17040
แผ่นที่ 3 ของจำนวน 3 แผ่น

การประกอบเลขที่
ASSEMBLY NO. 3707

บัญชีวัสดุ
BILL OF MATERIAL

ลำดับที่ ITEM	รายละเอียด DESCRIPTION	จำนวน REQ' D	วัสดุเลขที่ MAT. NO.
1	เสาคอนกรีต 14 เมตร POLE, CONCRETE 14 m LONG	1	00010006
2	ไม้คอนสาย แรงสูง 100X120X3000 มม. CROSSARM WOOD, H.T. 100X120X3000 mm	4	00100003
3	เหล็กประกับไม้คอน 40 X 6 X 1000 มม. BRACE, FLAT, FOR CROSS ARM 40X6X1000 mm	8	01200002
4	สลักเกลียว M 16X130 มม. BOLT, MACHINE M 16X130 mm	8	01110200
5	สลักเกลียว M 16X200 มม. BOLT, MACHINE M 16X 200 mm	1	01110202
6	สลักเกลียว M 16X250 มม. BOLT, MACHINE M 16X250 mm	2	01110203
7	สลักเกลียว M 16X350 มม. BOLT, MACHINE M 16X350 mm	2	01110205
8	สลักเกลียว M 16X400 มม. BOLT, MACHINE M 16X400 mm	1	01110206
9	สลักเกลียวห่วงกลม M 16 X 400 มม. BOLT, DOUBLE ARMING, ROUND EYE M 16X400 mm	3	01100000
10	แหวนสี่เหลี่ยมแบน 52X52X4.5 มม. รู Ø 18 มม. มอก. 258 WASHER, SQUARE, FLAT 52X52X4.5 mm HOLE Ø 18 mm TIS 258	30	01180100
11	ลูกถ้วยก้านตรง 33 kV มอก. 279 แบบ ค (แบบ 56-3) พร้อมก้าน INSULATOR, PIN TYPE, 33 kV TIS 279 TYPE C (CLASS 56-3) COMP.	3	03000002 03100001
12	ลูกถ้วยแขวน มอก.354 แบบ ง (แบบ 52-4) WITH PIN INSULATOR, SUSPENSION TYPE, TIS 354 TYPE D (CLASS 52-4)	9	03020002
13	ล่อฟ้าแรงสูง 30 kV 5 กิโลแอมป์ LIGHTNING ARRESTER, 30 kV 5 kA	3	04000100
14	ดรอพเอาท์ ฟิวส์คัทเอาท์ หนึ่งอินซูเลเตอร์ 33 kV 100 แอมป์ CUTOUT, FUSE, OPEN TYPE, SINGLE INSULATOR, DROP OUT 33 kV 100 A	3	04010100
15	หม้อแปลง 315-2000 kVA 3 เฟส 33-0.4 TRANSFORMER, 315-2000 kVA, 3-PHASE 33-04 kV	1	05010107 05010111
16	ลวดเหล็กตีเกลียว 50/7 ต.มม. มอก. 404 WIRE STEEL STRANDED 50/7 mm^2 TIS 404		01100004
17	พีจี คอนเนคเตอร์ สลักคู่ สำหรับสายอะลูมิเนียม ขนาด 25-95 ต.มม. CONNECTOR, PARALLEL GROOVED, DOUBLE BOLTS, Al 25-95 mm^2	3	02300102
18	สเตรนแคล้มป์อะลูมิเนียม 35-95 ต.มม. อะลูมิเนียมแกนเหล็ก 35-70 ต.มม. CLAMP, STRAIN, Al 35-95 mm^2, ACSR 35-70 mm^2	3	03110000 03110006
19	สายอะลูมิเนียมเปลือย 50/7 ต.มม. มอก. 85 CONDUCTOR 50/7 mm^2 TIS 85		02010002
20	หลักดิน 60X60X5 มม. ยาว 2 เมตร ROD, GROUND 60 X 60 X 5 mm 2 m LONG	2	01220002
21	ท่อเอสล่อน ขนาด 20X2500 มม. พร้อมเทปรัด PIPE, S'LON Ø 20X2500 mm COMPLETE WITH PERFORATED TAPE	2	08040001
22	สลักเกลียวห่วงกลม M 16X 200 มม. BOLT, ROUND EYE M 16 X 200 mm	1	01140001
23	กายทิมเบิลสำหรับสายยึดโยง 50 - 75 ต.มม. THIMBLE, GUY FOR STEEL WIRE 50-75 mm^2	1	01210304
24	ยูแคล้มป์ สลัก 1 ตัว M 8 CLAMP, SINGLE U-BOLT M 8	7	01230000

กองวิศวกรรม

ผู้เขียน
สถาปนิก
วิศวกร
หัวหน้าแผนก
ผู้อำนวยการกอง

รองผู้ว่าการฝ่ายเทคนิค

การไฟฟ้าส่วนภูมิภาค

ผู้ว่าการ

การติดตั้งหม้อแปลง ระบบ 33 kV
315 - 2000 kVA สำหรับโรงงานอุตสาหกรรม
ข บัญชีวัสดุ

TRANSFORMER INSTALLATION 33 kV
315 - 2000 kVA FOR INDUSTRIAL
B BILL OF MATERIAL

ใช้แทนแบบ
ถูกแทนโดยแบบ
เขียนเสร็จวันที่ 24 มิ.ย. 17
แก้แบบวันที่
ผิดเป็น
มาตราส่วน
แบบเลขที่ S02-015/17040
แผ่นที่ 2 ของจำนวน 3 แผ่น