
การประกอบเลขที่ ASSEMBLY NO. 3205

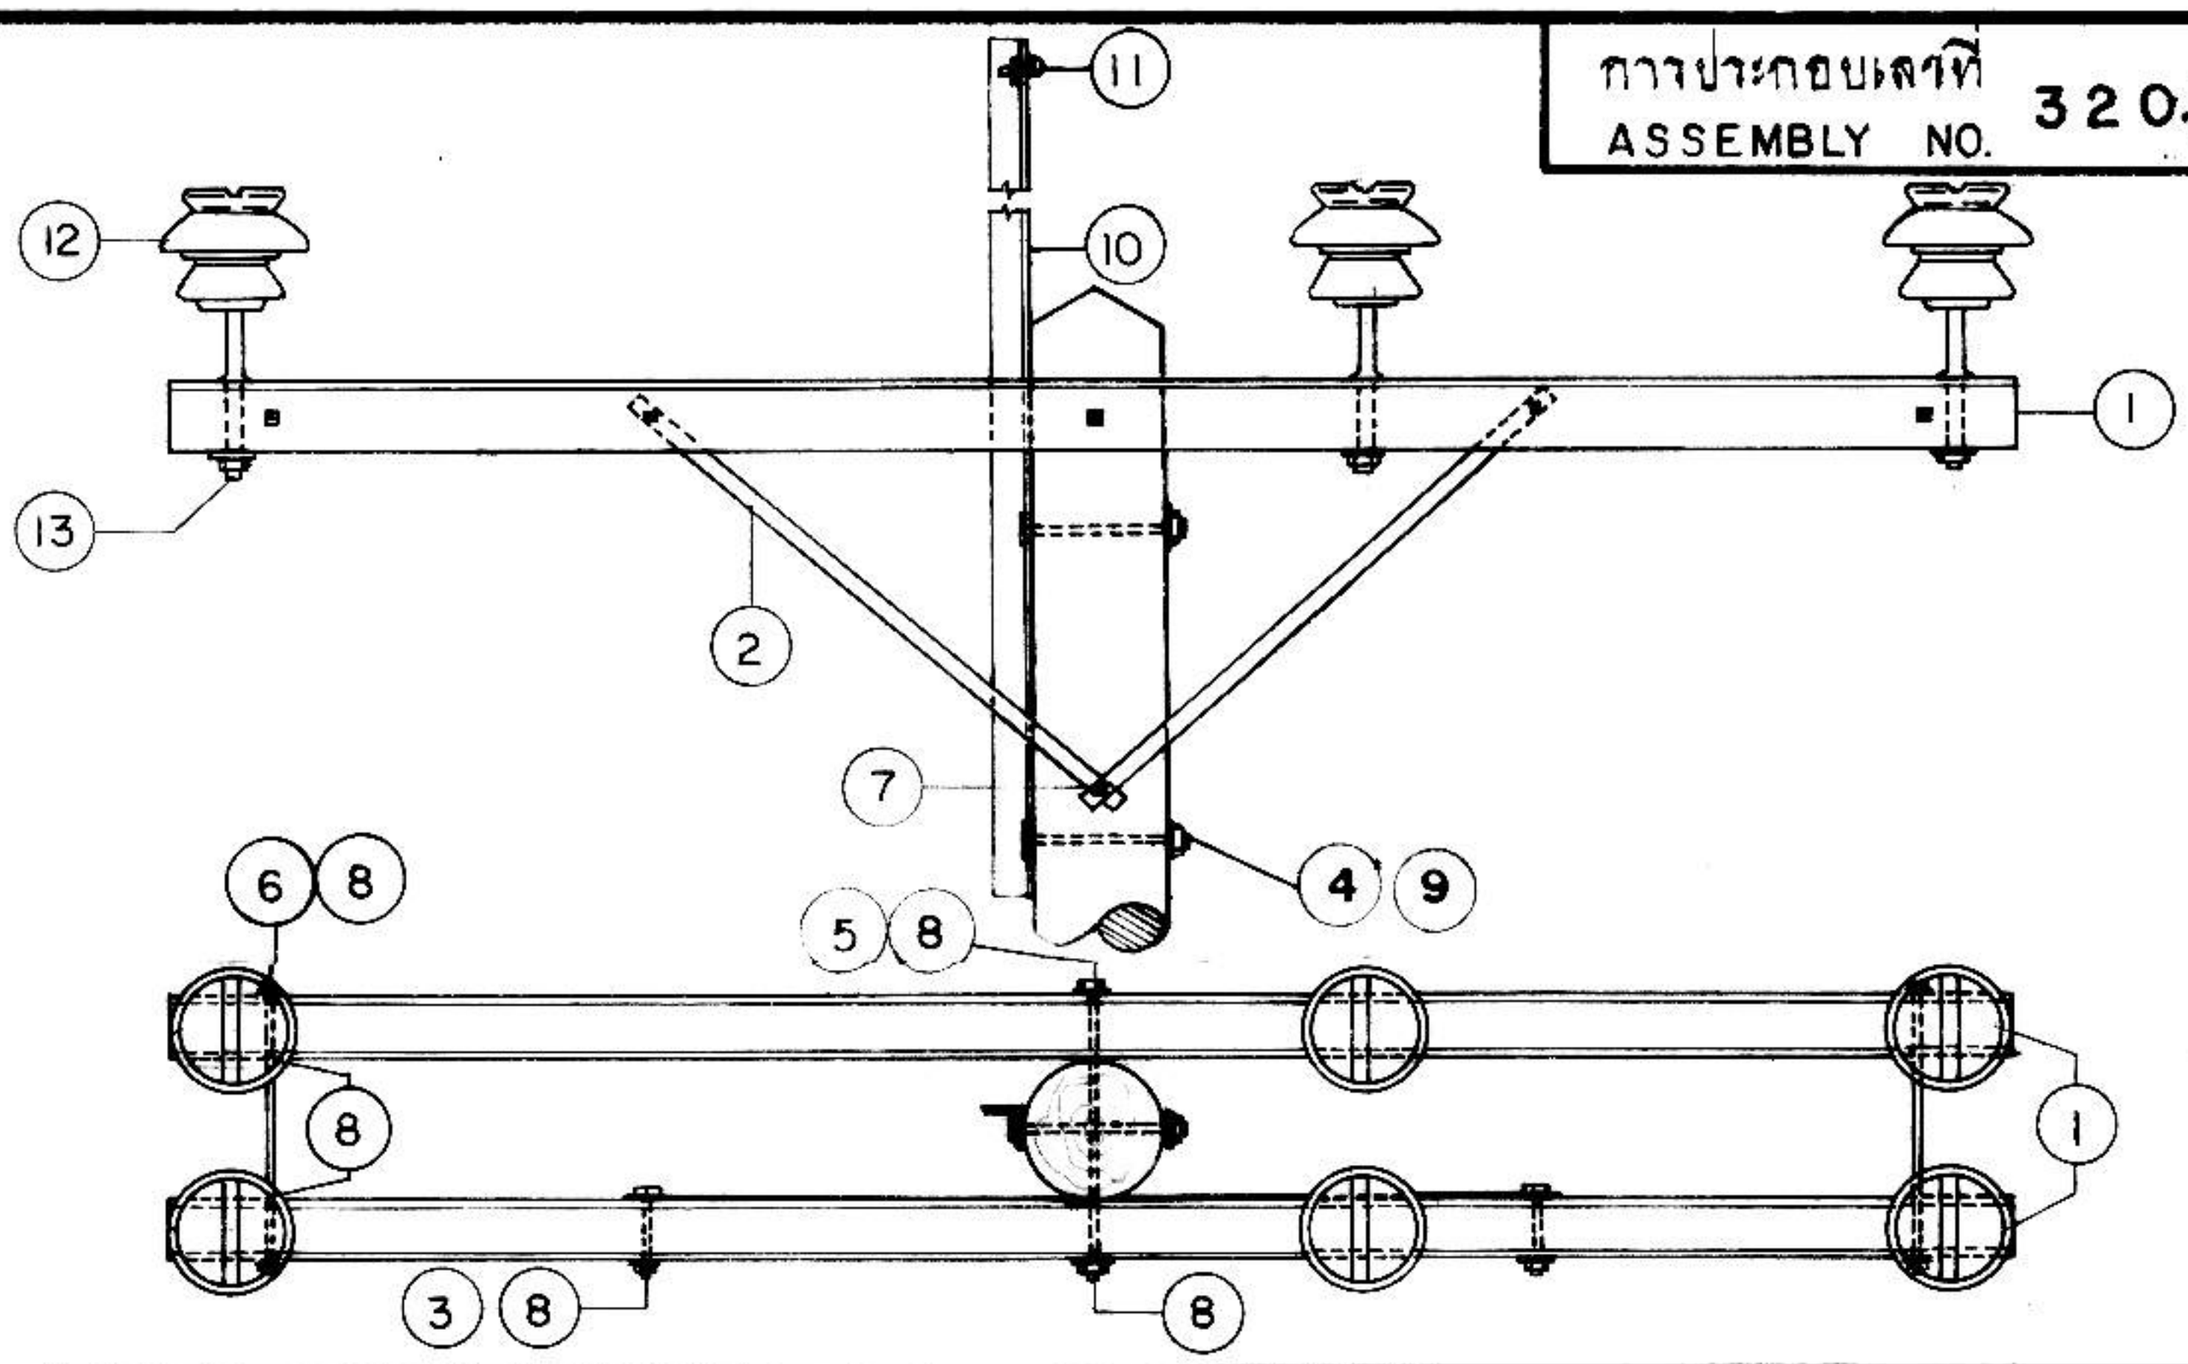

BILL OF MATERIAL

ITEM	DESCRIPTION	REQ'D	MAT. NO.
1	ไม้คอนสายขนาด 100X120X3,000 มม. CROSSARM (HT.) WOOD, 100X120X3,000 mm	2	00100003 (0101)
2	เหล็กประกับไม้คอน 40X6X1,000 มม BRACE,FLAT, FOR CROSSARM , 40X6X1,000 mm	2	01200002 (0121)
3	สลักเกลียว M 16X130 มม. BOLT, MACHINE , M 16X130 mm	2	01110200 (0220)
4	สลักเกลียว M 16X300 มม. BOLT, MACHINE , M 16X300 mm	2	01110204 (0224)
5	สลักเกลียว M 16X450 มม. BOLT, MACHINE , M 16X450 mm	1	01110207 (0227)
6	สลักเกลียวตลอด M 16X500 มม. BOLT, DOUBLE ARMING , M16X500 mm	2	01120002 (0245)
7	สลักเกลียวปล่อยขนาด 16X130 มม. SCREW , LAG , 16X130 mm	1	01170001 (0325)
8	แหวนสี่เหลี่ยมแบน 52X52X4.5 มม. ขนาดรู Ø 18 มม. มอก. 258 WASHER , SQUARE , FLAT, 52X52X4.5 mm HOLE Ø 18 mm TIS 258	12	01180100 (0355)
9	แหวนสี่เหลี่ยมโค้ง 50X50X5 มม. ขนาดรู Ø 18 มม. WASHER , SQUARE, CURVED, 50X50X5 mm HOLE Ø 18 mm	2	01180201 (0360)
10	เหล็กฉากรับสายล่อฟ้า OVERHEAD GROUND WIRE BAYONET	1	01010006 (0128)
11	กราวด์ไวร์แคล็มป์แบบ J 1152 GROUND WIRE CLAMP J 1152	1	01230205 (0296)
12	ลูกถ้วยก้านตรง 33 kV มอก. 279 แบบ ค (แบบ 56-3) INSULATOR, PIN TYPE, 33 kV TIS 279 TYPE C (CLASS 56-3)	6	03000002 (0409)
13	ก้านลูกถ้วยแรงสูง 33 kV PIN , INSULATOR	6	03100001 (0422)

กองวิศวกรรมและวางแผน	การไฟฟ้าส่วนภูมิภาค	ใช้แทนแบบ ถูกแทนโดยแบบ
ผู้เขียน สถาปนิก วิศวกร หัวหน้าแผนก ผู้อำนวยการกอง	ผู้ว่าการ การประกอบไม้คอนคู่กับเสาไม้ ระบบ 33 kV , 3 เฟส, มุม 5°-30°	เขียนเสร็จวันที่ 17 ตค. 12 แก้แบบวันที่ มิติเป็น มม. มาตราส่วน 1:25
ร่องผู้ว่าการฝ่ายเทคนิค	33 kV, DOUBLE CROSSARM ASSEMBLY ON WOOD POLE, 3-PHASE, 5° - 30°	แบบเลขที่ I50-015/120306 แผ่นที่ 1 ของจำนวน 1 แผ่น