

การประกอบเลขที่ ASSEMBLY NO. 3701 B

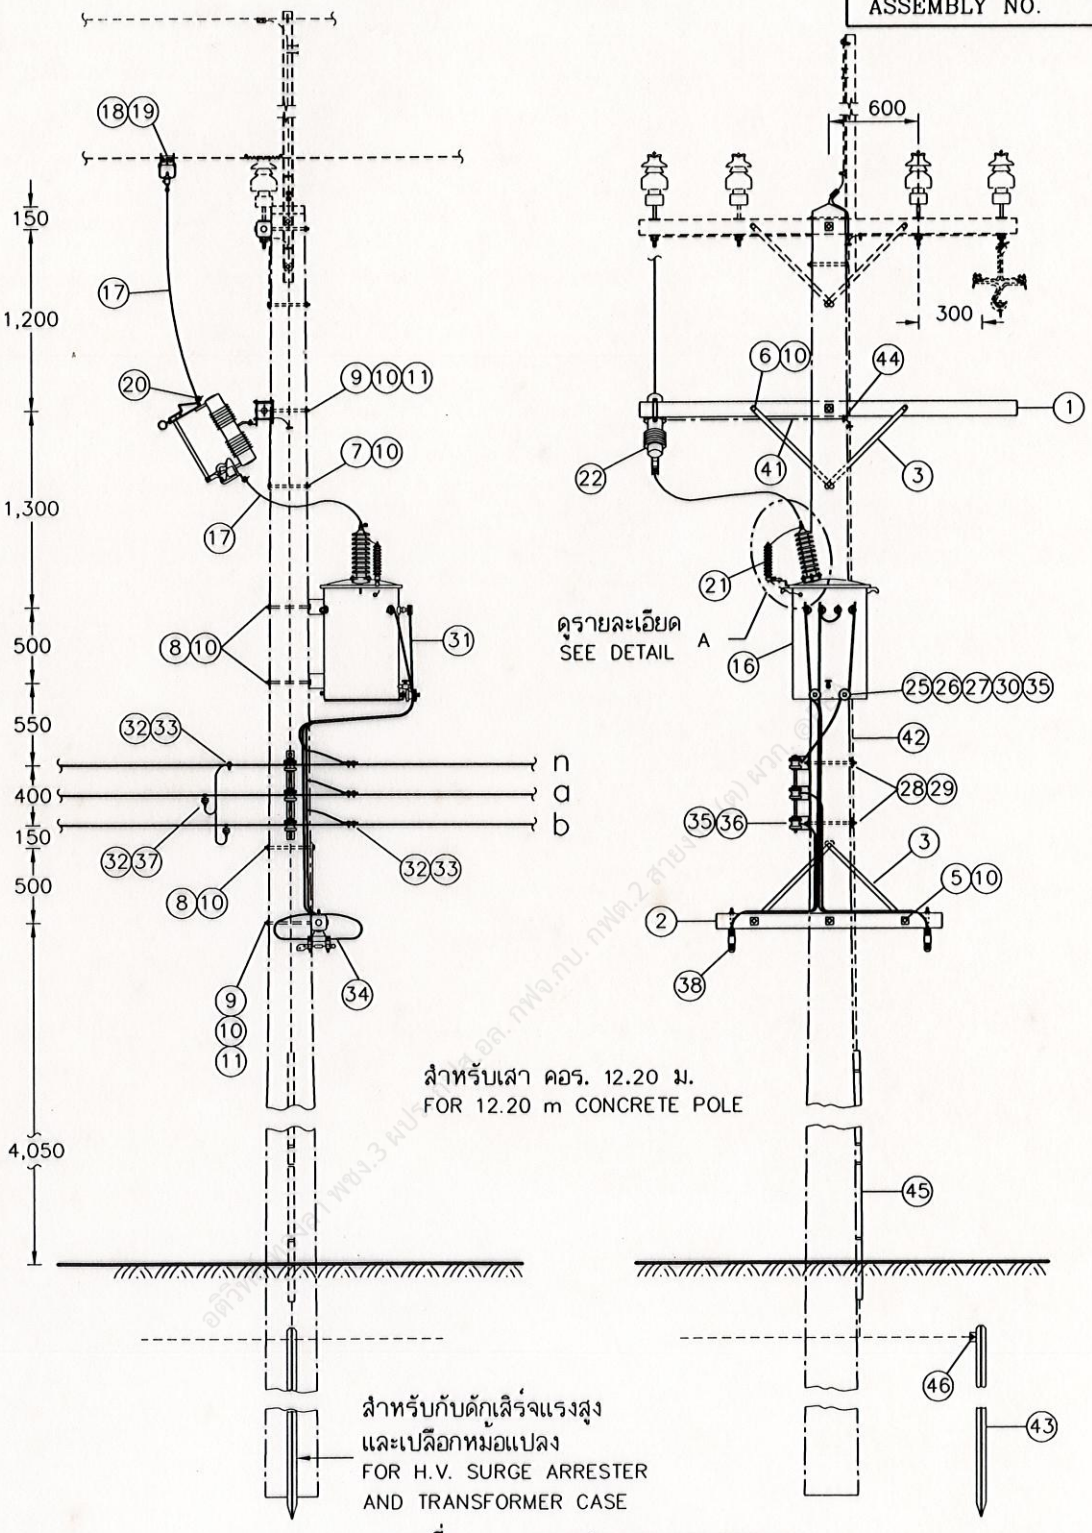


แบบที่ TYPE I การประกอบคอนธรรมดา CROSSARM ASSEMBLY

กองมาตรฐานระบบไฟฟ้า ฝ่ายมาตรฐานและความปลอดภัย	การไฟฟ้าส่วนภูมิภาค	ใช้แทนแบบ ..... ถูกแทนโดยแบบ .....
ผู้เขียน Supphakit Boonreung ผู้สำรวจ ..... วิศวกร วิทยา เชื้อสิงห์ หัวหน้าแผนก ..... ผู้อำนวยการกอง ..... ผู้อำนวยการฝ่าย	ผู้ว่าการ ..... 14 ม.ค. 2554	เขียนเสร็จวันที่ 6 ม.ค. 2554 แก้แบบวันที่ ..... มิติเป็น มิลลิเมตร มาตราส่วน 1 : 50
รองผู้ว่าการวางแผน และพัฒนาระบบไฟฟ้า	การติดตั้งหม้อแปลง 1 เฟส ระบบ 33 kV ที่มีกับดักเสิร์จที่ตัวถังหม้อแปลง ขนาด 10–50 kVA แขวนบนเสาเดี่ยว 33 kV 10–50 kVA 1 PHASE TRANSFORMER INSTALLATION WITH SURGE ARRESTER ON TRANSFORMER TANK ON SINGLE POLE	แบบเลขที่ SA2-015/54003 แผ่นที่ 1 ของจำนวน 8 แผ่น

การประกอบเลขที่ ASSEMBLY NO.	3701 B

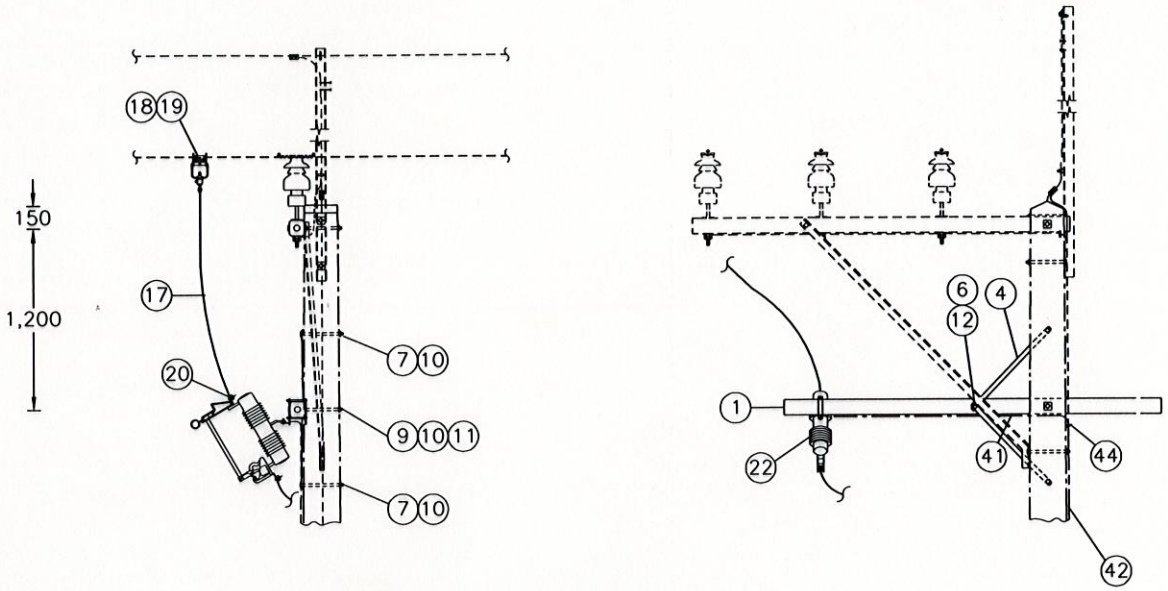


แบบที่ II การประกอบคอนท้าวแขน
TYPE ALLEY ARM ASSEMBLY

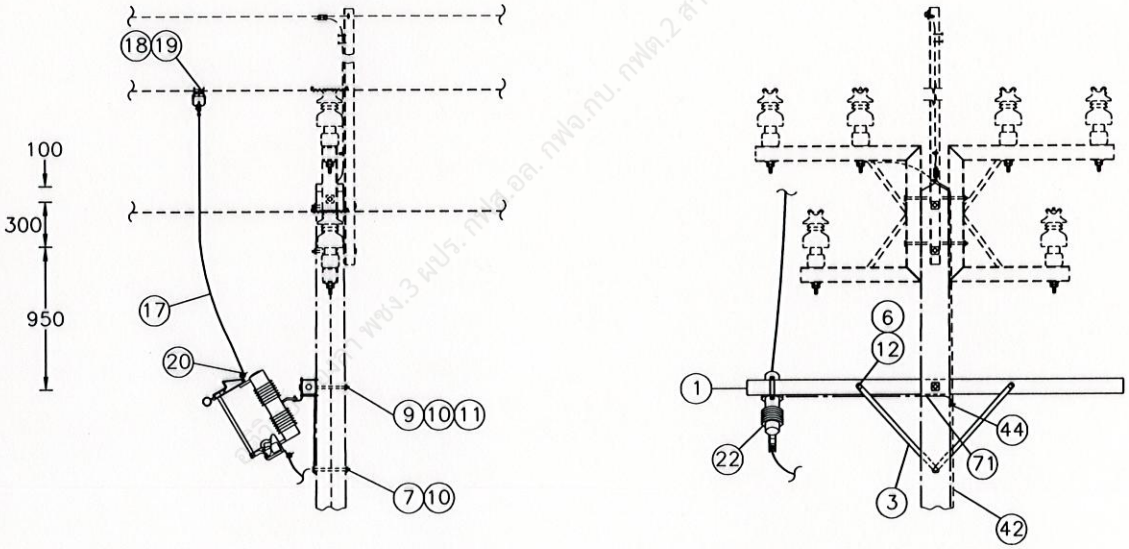


แบบที่ III การประกอบเหล็กคอนเคเบิลอากาศ
TYPE AERIAL CABLE SUPPORT BRACKET ASSEMBLY

กองมาตรฐานระบบไฟฟ้า ฝ่ายมาตรฐานและความปลอดภัย	การไฟฟ้าส่วนภูมิภาค	ใช้แทนแบบ ..... ถูกแทนโดยแบบ .....
ผู้เขียน Supphakit Boonreung ผู้สำรวจ ..... วิศวกร วิทยา เชื้อสิงห์ หัวหน้าแผนก ..... ผู้อำนวยการกอง ..... ผู้อำนวยการฝ่าย	ผู้ว่าการ ..... 14 ม.ค. 2554	เขียนเสร็จวันที่ 6 ม.ค. 2554 แก้แบบวันที่ ..... มิติเป็น มิลลิเมตร มาตราส่วน 1 : 50
รองผู้ว่าการวางแผนและพัฒนาระบบไฟฟ้า	การติดตั้งหม้อแปลง 1 เฟส ระบบ 33 kV ที่มีกับดักเสิร์จที่ตัวถังหม้อแปลง ขนาด 10-50 kVA แขวนบนเสาเดี่ยว 33 kV 10-50 kVA 1 PHASE TRANSFORMER INSTALLATION WITH SURGE ARRESTER ON TRANSFORMER TANK ON SINGLE POLE	แบบเลขที่ SA2-015/54003 แผ่นที่ 2 ของจำนวน 8 แผ่น

การประกอบเลขที่ ASSEMBLY NO.	3701 B

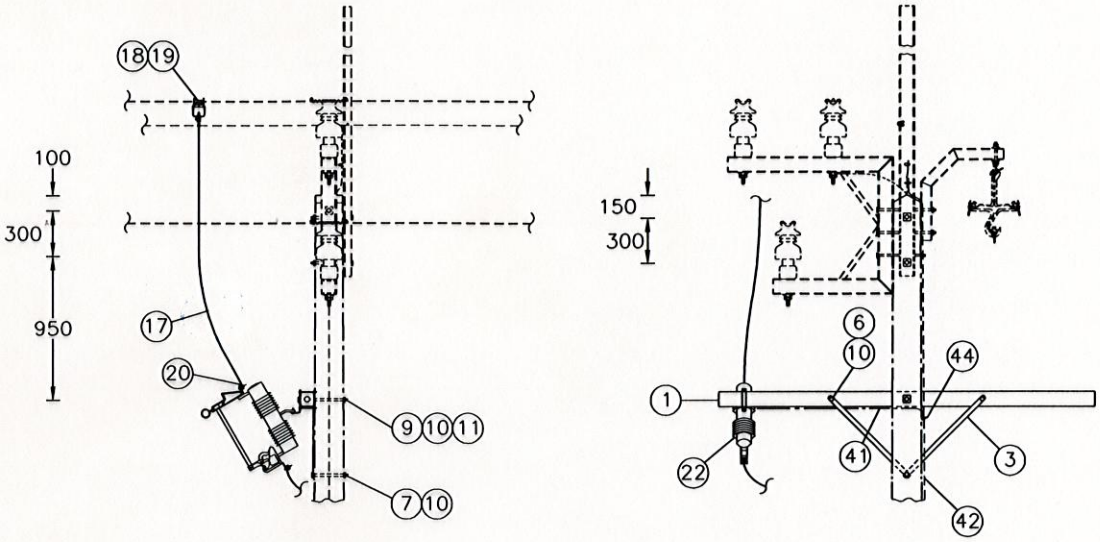

* แบบที่ IV การประกอบเหล็กคอนเคเบิลอากาศพร้อมสายสะพาน
TYPE AERIAL CABLE SUPPORT BRACKET ASSEMBLY WITH MESSENGER WIRE

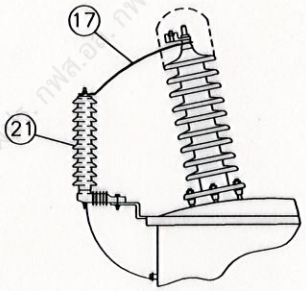


รายละเอียด A
DETAIL

* รูปแบบที่ 4 ให้ใช้สำหรับต่อแยกสายไปที่หม้อแปลง โดยการใช้เหล็กคอนเคเบิลอากาศทางโค้ง เมื่อระบบจำหน่ายแรงสูงช่วงนั้นเป็นเคเบิลอากาศติดตั้งบนเคเบิลสเปเซอร์
TYPE 4 : PROVIDES FOR THE TAPPING LINE TO TRANSFORMER BY USING THE STEEL BRACKETS. WHEN THE HIGH VOLTAGE DISTRIBUTION SYSTEM THAT IS SPACED AERIAL CABLE ON CABLE SPACER.


กองมาตรฐานระบบไฟฟ้า ฝ่ายมาตรฐานและความปลอดภัย	การไฟฟ้าส่วนภูมิภาค	ใช้แทนแบบ ..... ถูกแทนโดยแบบ .....
ผู้เขียน Supphakit Boonreung ผู้สำรวจ ..... วิศวกร วิทยา เชื้อสิงห์ หัวหน้าแผนก ..... ผู้อำนวยการกอง ..... ผู้อำนวยการฝ่าย	ผู้ว่าการ ..... 14 ม.ค. 2554 การติดตั้งหม้อแปลง 1 เฟส ระบบ 33 kV ที่มีกับดักเสิร์จที่ตัวถังหม้อแปลง ขนาด 10–50 kVA แขวนบนเสาเดี่ยว	เขียนเสร็จวันที่ 6 ม.ค. 2554 แก้แบบวันที่ ..... มิติเป็น มิลลิเมตร มาตราส่วน 1:50, 1:20
รองผู้ว่าการวางแผน และพัฒนาระบบไฟฟ้า	33 kV 10–50 kVA 1 PHASE TRANSFORMER INSTALLATION WITH SURGE ARRESTER ON TRANSFORMER TANK ON SINGLE POLE	แบบเลขที่ SA2–015/54003 แผ่นที่ 3 ของจำนวน 8 แผ่น

การประกอบเลขที่ ASSEMBLY NO.	3701 B


ไดอะแกรมแสดงการต่อหม้อแปลง
TRANSFORMER WIRING DIAGRAM

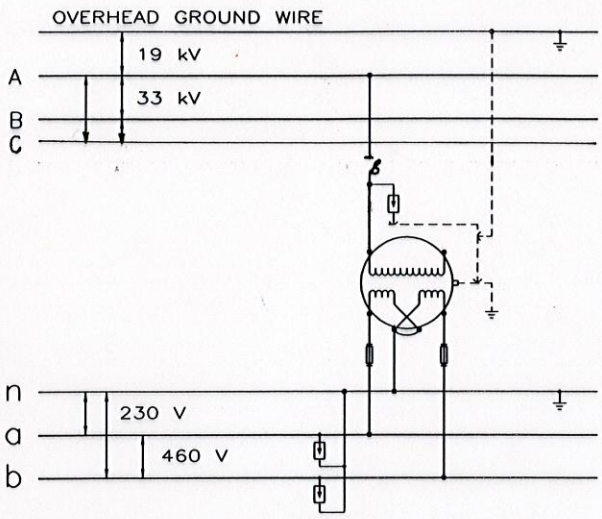

ไดอะแกรมแสดงการต่อหม้อแปลง 1 เฟส 3 สาย
1-PHASE 3-WIRE TRANSFORMER WIRING DIAGRAM

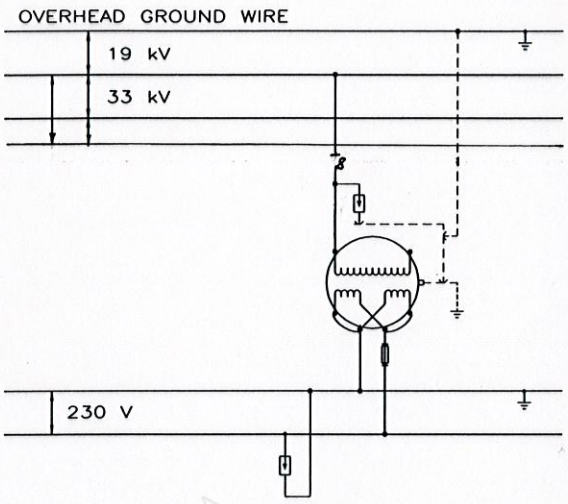

ไดอะแกรมแสดงการต่อหม้อแปลง 1 เฟส 2 สาย
1-PHASE 2-WIRE TRANSFORMER WIRING DIAGRAM

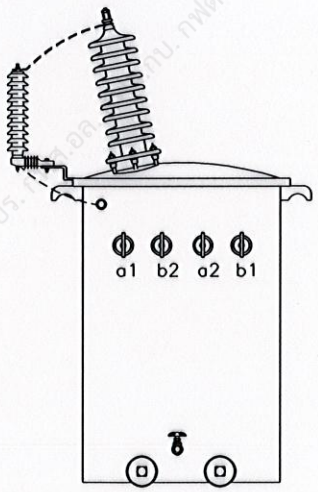

หม้อแปลง 1 เฟส ชิงเกิลบุชชิง 19 kV
TRANSFORMER 1 PHASE SINGLE BUSHING 19 kV

กองมาตรฐานระบบไฟฟ้า ฝ่ายมาตรฐานและความปลอดภัย	การไฟฟ้าส่วนภูมิภาค	ใช้แทนแบบ ..... ถูกแทนโดยแบบ .....
ผู้เขียน Supphakit Boonreung ผู้สำรวจ ..... วิศวกร วิทยา เชื้อสิงห์ หัวหน้าแผนก ..... ผู้อำนวยการกอง ..... ผู้อำนวยการฝ่าย	ผู้ว่าการ ..... 14 ม.ค. 2554 การติดตั้งหม้อแปลง 1 เฟส ระบบ 33 kV ที่มีกับดักเสิร์จที่ตัวถังหม้อแปลง ขนาด 10-50 kVA แขวนบนเสาเดี่ยว	เขียนเสร็จวันที่ 6 ม.ค. 2554 แก้แบบวันที่ ..... มิติเป็น ..... มาตราส่วน .....
รองผู้ว่าการวางแผน และพัฒนาระบบไฟฟ้า	33 kV 10-50 kVA 1 PHASE TRANSFORMER INSTALLATION WITH SURGE ARRESTER ON TRANSFORMER TANK ON SINGLE POLE	แบบเลขที่ SA2-015/54003 แผ่นที่ 4 ของจำนวน 8 แผ่น

การประกอบเลขที่ ASSEMBLY NO. 3701 B

บัญชีวัสดุ
BILL OF MATERIAL

ลำดับที่ ITEM	รายละเอียด DESCRIPTION	จำนวน REQ'D I	II	III	IV	วัสดุเลขที่ MAT. NO.
	การประกอบคอน คอร. และสลักเกลียวสำหรับการติดตั้งหม้อแปลงและอุปกรณ์ป้องกัน CROSSARM AND MACHINE BOLT ASSEMBLY FOR TRANSFORMER & PROTECTION EQUIPMENT INSTALLATION					
1	คอน คอร. สปัน ขนาด 120x120x3,000 มม. CROSSARM, SPUN, PRESTRESSED CONCRETE, 120x120x3,000 mm	1	1	1	1	1000110002
2	คอน คอร. สปัน ขนาด 100x100x1,500 มม. CROSSARM, SPUN, PRESTRESSED CONCRETE, 100x100x1,500 mm	1	1	1	1	1000110000
3	เหล็กประกับคอน ขนาด 30x6x760 มม. BRACE, FLAT, FOR CROSSARM 30x6x760 mm	4	2	4	4	1010200001
4	เหล็กประกับคอน ขนาด 40x6x1,000 มม. BRACE, FLAT, FOR CROSSARM 40x6x1,000 mm	–	2	–	–	1010200002
5	สลักเกลียว M 16x130 มม. BOLT, MACHINE, M 16x130 mm	2	2	2	2	1010110200
6	สลักเกลียว M 16x170 มม. BOLT, MACHINE, M 16x170 mm	2	1	2	2	1010110201
7	สลักเกลียว M 16x250 มม. BOLT, MACHINE, M 16x250 mm	1	2	1	1	1010110203
8	สลักเกลียว M 16x300 มม. BOLT, MACHINE, M 16x300 mm	3	3	3	3	1010110204
9	สลักเกลียว M 16x400 มม. BOLT, MACHINE, M 16x400 mm	2	2	2	2	1010110206
10	แหวนสี่เหลี่ยมแบน 52x52x4.5 มม. รู ø18 มม. มอก. 258 WASHER, SQUARE, FLAT, 52x52x4.5 mm, HOLE ø18 mm, TIS 258	14	14	14	14	1010180100
11	แหวนสปริง M 16 มอก. 259 WASHER, LOCK, SPRING, M 16, TIS 259	2	2	2	2	1010180301
12						
13						
14						
15						

กองมาตรฐานระบบไฟฟ้า
ฝ่ายมาตรฐานและความปลอดภัย

ผู้เขียน Supphakit Boonreung
ผู้สำรวจ .....
วิศวกร วิทยา เชื้อสิงห .....
หัวหน้าแผนก .....
ผู้อำนวยการกอง .....
ผู้อำนาจการฝ่าย .....

รองผู้ว่าการวางแผนและพัฒนาระบบไฟฟ้า
.....

การไฟฟ้าส่วนภูมิภาค

ผู้ว่าการ ..... 14 ม.ค. 2554

การติดตั้งหม้อแปลง 1 เฟส ระบบ 33 kV
ที่มีกับดักเสิร์จที่ตัวถังหม้อแปลง ขนาด 10-50 kVA
แขวนบนเสาเดี่ยว

33 kV 10-50 kVA 1 PHASE TRANSFORMER INSTALLATION
WITH SURGE ARRESTER ON TRANSFORMER TANK
ON SINGLE POLE

ใช้แทนแบบ .....
ถูกแทนโดยแบบ .....
เขียนเสร็จวันที่ 6 ม.ค. 2554
แก้แบบวันที่ .....
มิติเป็น .....
มาตราส่วน .....

แบบเลขที่ SA2-015/54003
แผ่นที่ 5 ของจำนวน 8 แผ่น

การประกอบเลขที่ ASSEMBLY NO. 3701 B

บัญชีวัสดุ
BILL OF MATERIAL

ลำดับที่ ITEM	รายละเอียด DESCRIPTION	จำนวน REQ'D I	II	III	IV	วัสดุเลขที่ MAT. NO.
	การประกอบสายแรงสูง หม้อแปลง และอุปกรณ์ป้องกัน **H.V. LEAD AND TRANSFORMER AND PROTECTION EQUIPMENT ASSEMBLY**					
16	หม้อแปลง 1 เฟส ชิงเกิลบุชชิง 19 kV ขนาด 10-50 kVA TRANSFORMER 1 PHASE, SINGLE BUSHING 19 kV, 10-50 kVA	1	1	1	1	105000200-3
17	สายเคเบิลอากาศอะลูมิเนียม 33 kV ขนาด 50 ต.มม. AERIAL CABLE, Al, 33 kV ; SIZE 50 mm^2	ม. 10 m	ม. 10 m	ม. 10 m	ม. 10 m	1020050100
18	ฮอทไลน์แคล้มป์ ขนาดตามต้องการ HOT LINE CLAMP, SIZE AS REQUIRED	1	1	1	1	1020330100-1
19	สเตอร์รัพแคล้มป์ หรือเบลแคล้มป์ ขนาดตามต้องการ CLAMP, STIRRUP OR BAIL, SIZE AS REQUIRED	1	1	1	1	1020330000-1
20	สลักต่อปลายสายเข้าอุปกรณ์ไฟฟ้า สำหรับสายอะลูมิเนียมขนาด 50 ต.มม. PIN TERMINAL, FOR Al CONDUCTOR 50 mm^2	2	2	2	2	1020420400
21	กับดักเสิร์จแรงสูง 5 kA, 30 kV พร้อมอุปกรณ์ติดตั้ง SURGE ARRESTER , 5 kA, 30 kV ; COMPLETE WITH ACCESSORIES	1	1	1	1	1040000100-6
22	ดรอพเอาต์ ฟิวส์คัตเอาต์ หนึ่งอินซูเลเตอร์ 33 kV 100 A CUT-OUT, FUSE, OPEN TYPE, SINGLE INSULATOR, DROPOUT, 33 kV, 100 A	1	1	1	1	1040010100
23						
24						
	การประกอบสายแรงต่ำและอุปกรณ์ป้องกัน **L.V. WIRING AND FUSE SWITCH ASSEMBLY**					
25	ลวดอะลูมิเนียมกลมหุ้มฉนวน ø 4.0 มม. ความยาวตามต้องการ COVERED, TIE WIRE, Al, ø 4.0 mm ; LENGTH AS REQUIRED	ม. m	ม. m	ม. m	ม. m	1020200003
26	เหล็กจับขอบถังหม้อแปลงสำหรับยึดสายแรงต่ำ BRACKET, STEEL, FOR TRANSFORMER SECONDARY LEAD	2	2	2	2	1050100003
27	สลักเกลียว M 16x130 มม. BOLT, MACHINE, M 16x130 mm	2	2	2	2	1010110200
28	สลักเกลียว M 16x300 มม. BOLT, MACHINE, M 16x300 mm	2	2	2	2	1010110204
29	แหวนสี่เหลี่ยมแบน 52x52x4.5 มม. รู ø18 มม. มอก. 258 WASHER, SQUARE, FLAT, 52x52x4.5 mm, HOLE ø18 mm, TIS 258	2	2	2	2	1010180100
30	แหวนรองแบบสปริง M 16 มอก. 259 WASHER, LOCK, SPRING M 16 TIS 259	2	2	2	2	1010180301
31	สายอะลูมิเนียมหุ้มฉนวน PVC 750 V 70° C มอก. 293 ขนาดตามต้องการ CABLE, Al, PVC INSULATED, 750 V 70° C, TIS 293 ; SIZE AS REQUIRED	ม. 16 m	ม. 16 m	ม. 16 m	ม. 16 m	1020070001-4
32	เทปไฟฟ้า พี.วี.ซี. กว้าง 19 มม. (ใช้ความยาว 2 ม. ต่อ 1 จุด) มอก. 386 PVC TAPE, 19 mm WIDE (2 m LONG PER POINT), TIS 386	ม้วน 3 roll	ม้วน 3 roll	ม้วน 3 roll	ม้วน 3 roll	1020180001
33	คอนเนคเตอร์ ชนิดบีบ รูปตัว H สำหรับสายอะลูมิเนียม ขนาดตามต้องการ CONNECTOR, COMPRESSION, H-TYPE, FOR Al CONDUCTOR ; SIZE AS REQUIRED	4	4	4	4	1020320002-3

กองมาตรฐานระบบไฟฟ้า
ฝ่ายมาตรฐานและความปลอดภัย

ผู้เขียน Supphakit Roonreung
ผู้สำรวจ .....
วิศวกร วิทยา เชื้อสิงห์
หัวหน้าแผนก .....
ผู้อำนวยการกอง .....
ผู้อำนวยการฝ่าย .....

รองผู้ว่าการวางแผนและพัฒนาระบบไฟฟ้า
.....

การไฟฟ้าส่วนภูมิภาค

ผู้ว่าการ ..... 14 ม.ค. 2554

การติดตั้งหม้อแปลง 1 เฟส ระบบ 33 kV
ที่มีกับดักเสิร์จที่ตัวถังหม้อแปลง ขนาด 10-50 kVA
แขวนบนเสาเดี่ยว

33 kV 10-50 kVA 1 PHASE TRANSFORMER INSTALLATION
WITH SURGE ARRESTER ON TRANSFORMER TANK
ON SINGLE POLE

ใช้แทนแบบ .....
ถูกแทนโดยแบบ .....
เขียนเสร็จวันที่ 6 ม.ค. 2554
แก้แบบวันที่ .....
มิติเป็น .....
มาตราส่วน .....

แบบเลขที่ SA2-015/54003
แผ่นที่ 6 ของจำนวน 8 แผ่น

การประกอบเลขที่ ASSEMBLY NO. 3701 B

บัญชีวัสดุ
BILL OF MATERIAL

ลำดับที่ ITEM	รายละเอียด DESCRIPTION	จำนวน REQ'D I	II	III	IV	วัสดุเลขที่ MAT. NO.
	การประกอบสายแรงต่ำและอุปกรณ์ป้องกัน (ต่อ) L.V. WIRING AND FUSE SWITCH ASSEMBLY (CONTINUE)					
34	ทางปลา เจาะรูตามมาตรฐาน NEMA สำหรับสายอะลูมิเนียม ขนาดตามต้องการ CABLE LUG, NEMA HOLE, COMPRESSION TYPE, FOR AI CONDUCTOR ; SIZE AS REQUIRED	4	4	4	4	1020420102-4
35	ลูกรอกแรงต่ำ มอก. 227 แบบ ข (แบบ 53-2) INSULATOR, SPOOL TYPE, L.V., TIS 227, TYPE B (53-2)	5	5	5	5	1030030000
36	แร็ค 3x200 มม. (3x8") แบบหลังยื่น RACK, SECONDARY, MEDIUM PRESSED STEEL, 3x200 mm (3x8"), EXT. BACK	1	1	1	1	1030130001
37	กับดักเสิร์จแรงต่ำ 250-500 V 2.5-5.0 kA SURGE ARRESTER, 250-500 V, 2.5-5.0 kA	2	2	2	2	1040000300
38	ฟิวส์สวิตช์แรงต่ำ 1x400 A, 500 V L.V. FUSE SWITCH, 1x400 A, 500 V	2	2	2	2	1040020100
39						
40						
	การประกอบอุปกรณ์ต่อลงดิน GROUNDING EQUIPMENT ASSEMBLY					
41	ลวดเหล็กกลม ขนาด ø4.0 มม. เส้นเดี่ยว มอก. 71 (น้ำหนักประมาณ 0.1 กก/ม.) WIRE, STEEL, SOLID, ø4.0 mm, TIS 71 (WEIGHT 0.1 kg/m)	กก. 0.4 kg	กก. 0.4 kg	กก. 0.4 kg	กก. 0.4 kg	1010100000
42	ลวดเหล็กตีเกลียว 50/7 ต.มม. มอก. 404 พร้อมอุปกรณ์จับยึด WIRE, STEEL STRANDED, 50/7 mm^2, TIS 404 ; COMP. WITH FIXING ACCESS.	ม. 28 m	ม. 28 m	ม. 28 m	ม. 28 m	1010100004
43	หลักดิน 60x60x5 มม. ยาว 2 ม. ROD, GROUND 60x60x5 mm, 2 m LONG	1	1	1	1	1010220002
44	ยูแคล้มป์ สลักเดี่ยว M 8 (ไวร์ โร้ป คลิพ) CLAMP, SINGLE U-BOLT, M 8 (WIRE ROPE CLIP)	3	3	3	3	1010230000
45	ท่อ พี.วี.ซี. แข็ง ขนาด ø20 มม. มอก. 216 พร้อมอุปกรณ์จับยึด CONDUIT, PVC RIGID, ø20 mm, TIS 216 COMPLETE WITH FIXING ACCESS.	1	1	1	1	1080040001
46	จุดต่อสายดินกับหลักดินแบบเชื่อมด้วยความร้อน EXOTHERMIC WELDING POINT BETWEEN GROUND WIRE AND GROUND ROD	1	1	1	1	-
47						
48						

กองมาตรฐานระบบไฟฟ้า
ฝ่ายมาตรฐานและความปลอดภัย

ผู้เขียน Supphakit Boonreung
ผู้สำรวจ .....
วิศวกร วิทยา เชื้อสิงห์
หัวหน้าแผนก .....
ผู้อำนวยการกอง .....
ผู้อำนวยการฝ่าย .....

รองผู้ว่าการวางแผนและพัฒนาระบบไฟฟ้า
.....

การไฟฟ้าส่วนภูมิภาค

ผู้ว่าการ ..... 14 ม.ค. 2554

การติดตั้งหม้อแปลง 1 เฟส ระบบ 33 kV
ที่มีกับดักเสิร์จที่ตัวถังหม้อแปลง ขนาด 10-50 kVA
แขวนบนเสาเดี่ยว

33 kV 10-50 kVA 1 PHASE TRANSFORMER INSTALLATION WITH SURGE ARRESTER ON TRANSFORMER TANK ON SINGLE POLE

ใช้แทนแบบ .....
ถูกแทนโดยแบบ .....
เขียนเสร็จวันที่ 6 ม.ค. 2554
แก้แบบวันที่ .....
มิติเป็น .....
มาตราส่วน .....

แบบเลขที่ SA2-015/54003
แผ่นที่ 7 ของจำนวน 8 แผ่น

การประกอบเลขที่ ASSEMBLY NO.	3701 B

หมายเหตุ

1. เพื่อป้องกันปัญหาไฟฟ้าขัดข้องเนื่องจากสัตว์ ให้ใช้เทปพันเคเบิลอากาศแรงสูง (วัสดุเลขที่ 1020180003) และเทปพันสาย พี.วี.ซี. (วัสดุเลขที่ 1020180001) พันหัวบุชชิ่ง หรือติดตั้งฉนวนครอบขั้วต่อสายหรือบุชชิ่งของอุปกรณ์ไฟฟ้าตามแบบเลขที่ SA2-015/53007 (การประกอบเลขที่ 9576)
2. เสาต้นติดตั้งหม้อแปลง ต้องเป็นต้นทางตรง มุมเบี่ยงเบนไม่เกิน 1°
3. ระยะห่างระหว่างส่วนที่มีไฟฟ้าและเปิดโล่งทางด้านแรงสูงกับโครงสร้างอื่น (ผนังด้านเปิด , สะพาน , เสาสัญญาณไฟจราจร) ต้องไม่น้อยกว่า 1.80 ม.

NOTES

1. TO PREVENT THE FAULTS DUE TO THE ANIMALS, IT SHALL BE WRAPPED WITH ELECTRICAL SPLICING TAPE (MAT. No. 1020180003) AND PVC TAPE (MAT. No. 1020180001) OR INSTALLED INSULATION COVER FOR TERMINAL OR BUSHING OF ELECTRICAL EQUIPMENT SEE DWG. NO. SA2-015/53007 (ASSEMBLY NO. 9576).
2. THE POLE WHICH INSTALLED TRANSFORMER SHALL BE TANGENT STRUCTURE AND LINE DEFLECTION ANGLE NOT MORE THAN 1°.
3. CLEARANCE BETWEEN EXPOSE LIVE PART OF H.V. LEADS AND OTHER STRUCTURES (OPEN WALLS , BRIDGES , TRAFFIC LIGHT POSTS) NOT LESS THAN 1.80 m.

ลำดับที่ ITEM	แบบอ้างอิง REFERANCE DRAWING	แบบเลขที่ DWG. No.	การประกอบเลขที่ ASSEMBLY No.
1	การต่อสายเป็นกลางแรงต่ำลงดินสำหรับหม้อแปลงและสายระบบจำหน่าย SECONDARY NEUTRAL EARTHING FOR TRANSFORMER AND DISTRIBUTION LINE	S02-015/20066	0403
2	การติดตั้งฟิวส์สวิตช์บนคอน คอร. 100x100x1,500 มม. L.T. FUSE-SWITCH INSTALLATION ON PRESTRESSED CROSSARM 100x100x1,500 mm	SA1-015/22012	0406
3	ขนาดสายไฟฟ้าแรงต่ำออกจากหม้อแปลง THE SIZE OF L.V. CABLE FROM TRANSFORMER	SA1-015/22034	0601
4	พิกัด HRC ฟิวส์แรงต่ำ สำหรับหม้อแปลงระบบจำหน่าย RATING OF L.T. HRC FUSE FOR DISTRIBUTION TRANSFORMER	S01-015/18006	0602
5	การต่อสายแรงต่ำออกจากหม้อแปลง (แบบแขวนกับเสาไฟฟ้า) SECONDARY LEAD FROM TRANSFORMER (MOUNTED ON POLE)	SA1-015/22011	0603
6	ตารางขนาดฟิวส์สำหรับหม้อแปลง 1 เฟส ระบบ 33 kV FUSE RATING TABLE FOR 33 kV 1-ø TRANSFORMER	I50-015/130048	2104
7	มาตรฐานระยะห่างที่ปลอดภัย ในการก่อสร้างทางไฟฟ้า STANDARD MINIMUM SAFE CLEARANCE FOR ELECTRICAL CONSTRUCTION	SA2-015/45017	9301
8	ลักษณะการต่อสายแยกเข้าหม้อแปลง 1 เฟส แบบต่างๆ TYPICAL OF 1-ø TRANSFORMER JUMPER TAPPING OFF THE MAIN LINE	SA1-015/21058	9603
9	การต่อลงดิน สำหรับหม้อแปลงระบบจำหน่าย EARTHING CONNECTION FOR DISTRIBUTION TRANSFORMER	SA2-015/50017	9701 A
10	การประกอบยึดสายดินกับเสาคอนกรีต GROUND WIRE ASSEMBLY ON CONCRETE POLE	SA1-015/31012	9703 A
11	การประกอบที่ยึดท่อ พี.วี.ซี. กับเสาคอนกรีต RIGID PVC CONDUIT ASSEMBLY ON CONCRETE POLE	SA1-015/31013	9704 A

กองมาตรฐานระบบไฟฟ้า ฝ่ายมาตรฐานและความปลอดภัย	การไฟฟ้าส่วนภูมิภาค	ใช้แทนแบบ ..... ถูกแทนโดยแบบ .....
ผู้เขียน Supphakit Boonreung ผู้สำรวจ ..... วิศวกร วิทยา เชื้อสิงห์ หัวหน้าแผนก ..... ผู้อำนวยการกอง ..... ผู้อำนวยการฝ่าย	ผู้ว่าการ ..... 14 ม.ค. 2554	เขียนเสร็จวันที่ 6 ม.ค. 2554 แก้แบบวันที่ ..... มิติเป็น ..... มาตราส่วน .....
รองผู้ว่าการวางแผนและพัฒนาระบบไฟฟ้า	การติดตั้งหม้อแปลง 1 เฟส ระบบ 33 kV ที่มีกับดักเสิร์จที่ตัวถังหม้อแปลง ขนาด 10-50 kVA แขวนบนเสาเดี่ยว 33 kV 10-50 kVA 1 PHASE TRANSFORMER INSTALLATION WITH SURGE ARRESTER ON TRANSFORMER TANK ON SINGLE POLE	แบบเลขที่ SA2-015/54003 แผ่นที่ 8 ของจำนวน 8 แผ่น