การประกอบเลขที่ 3421
ASSEMBLY NO.

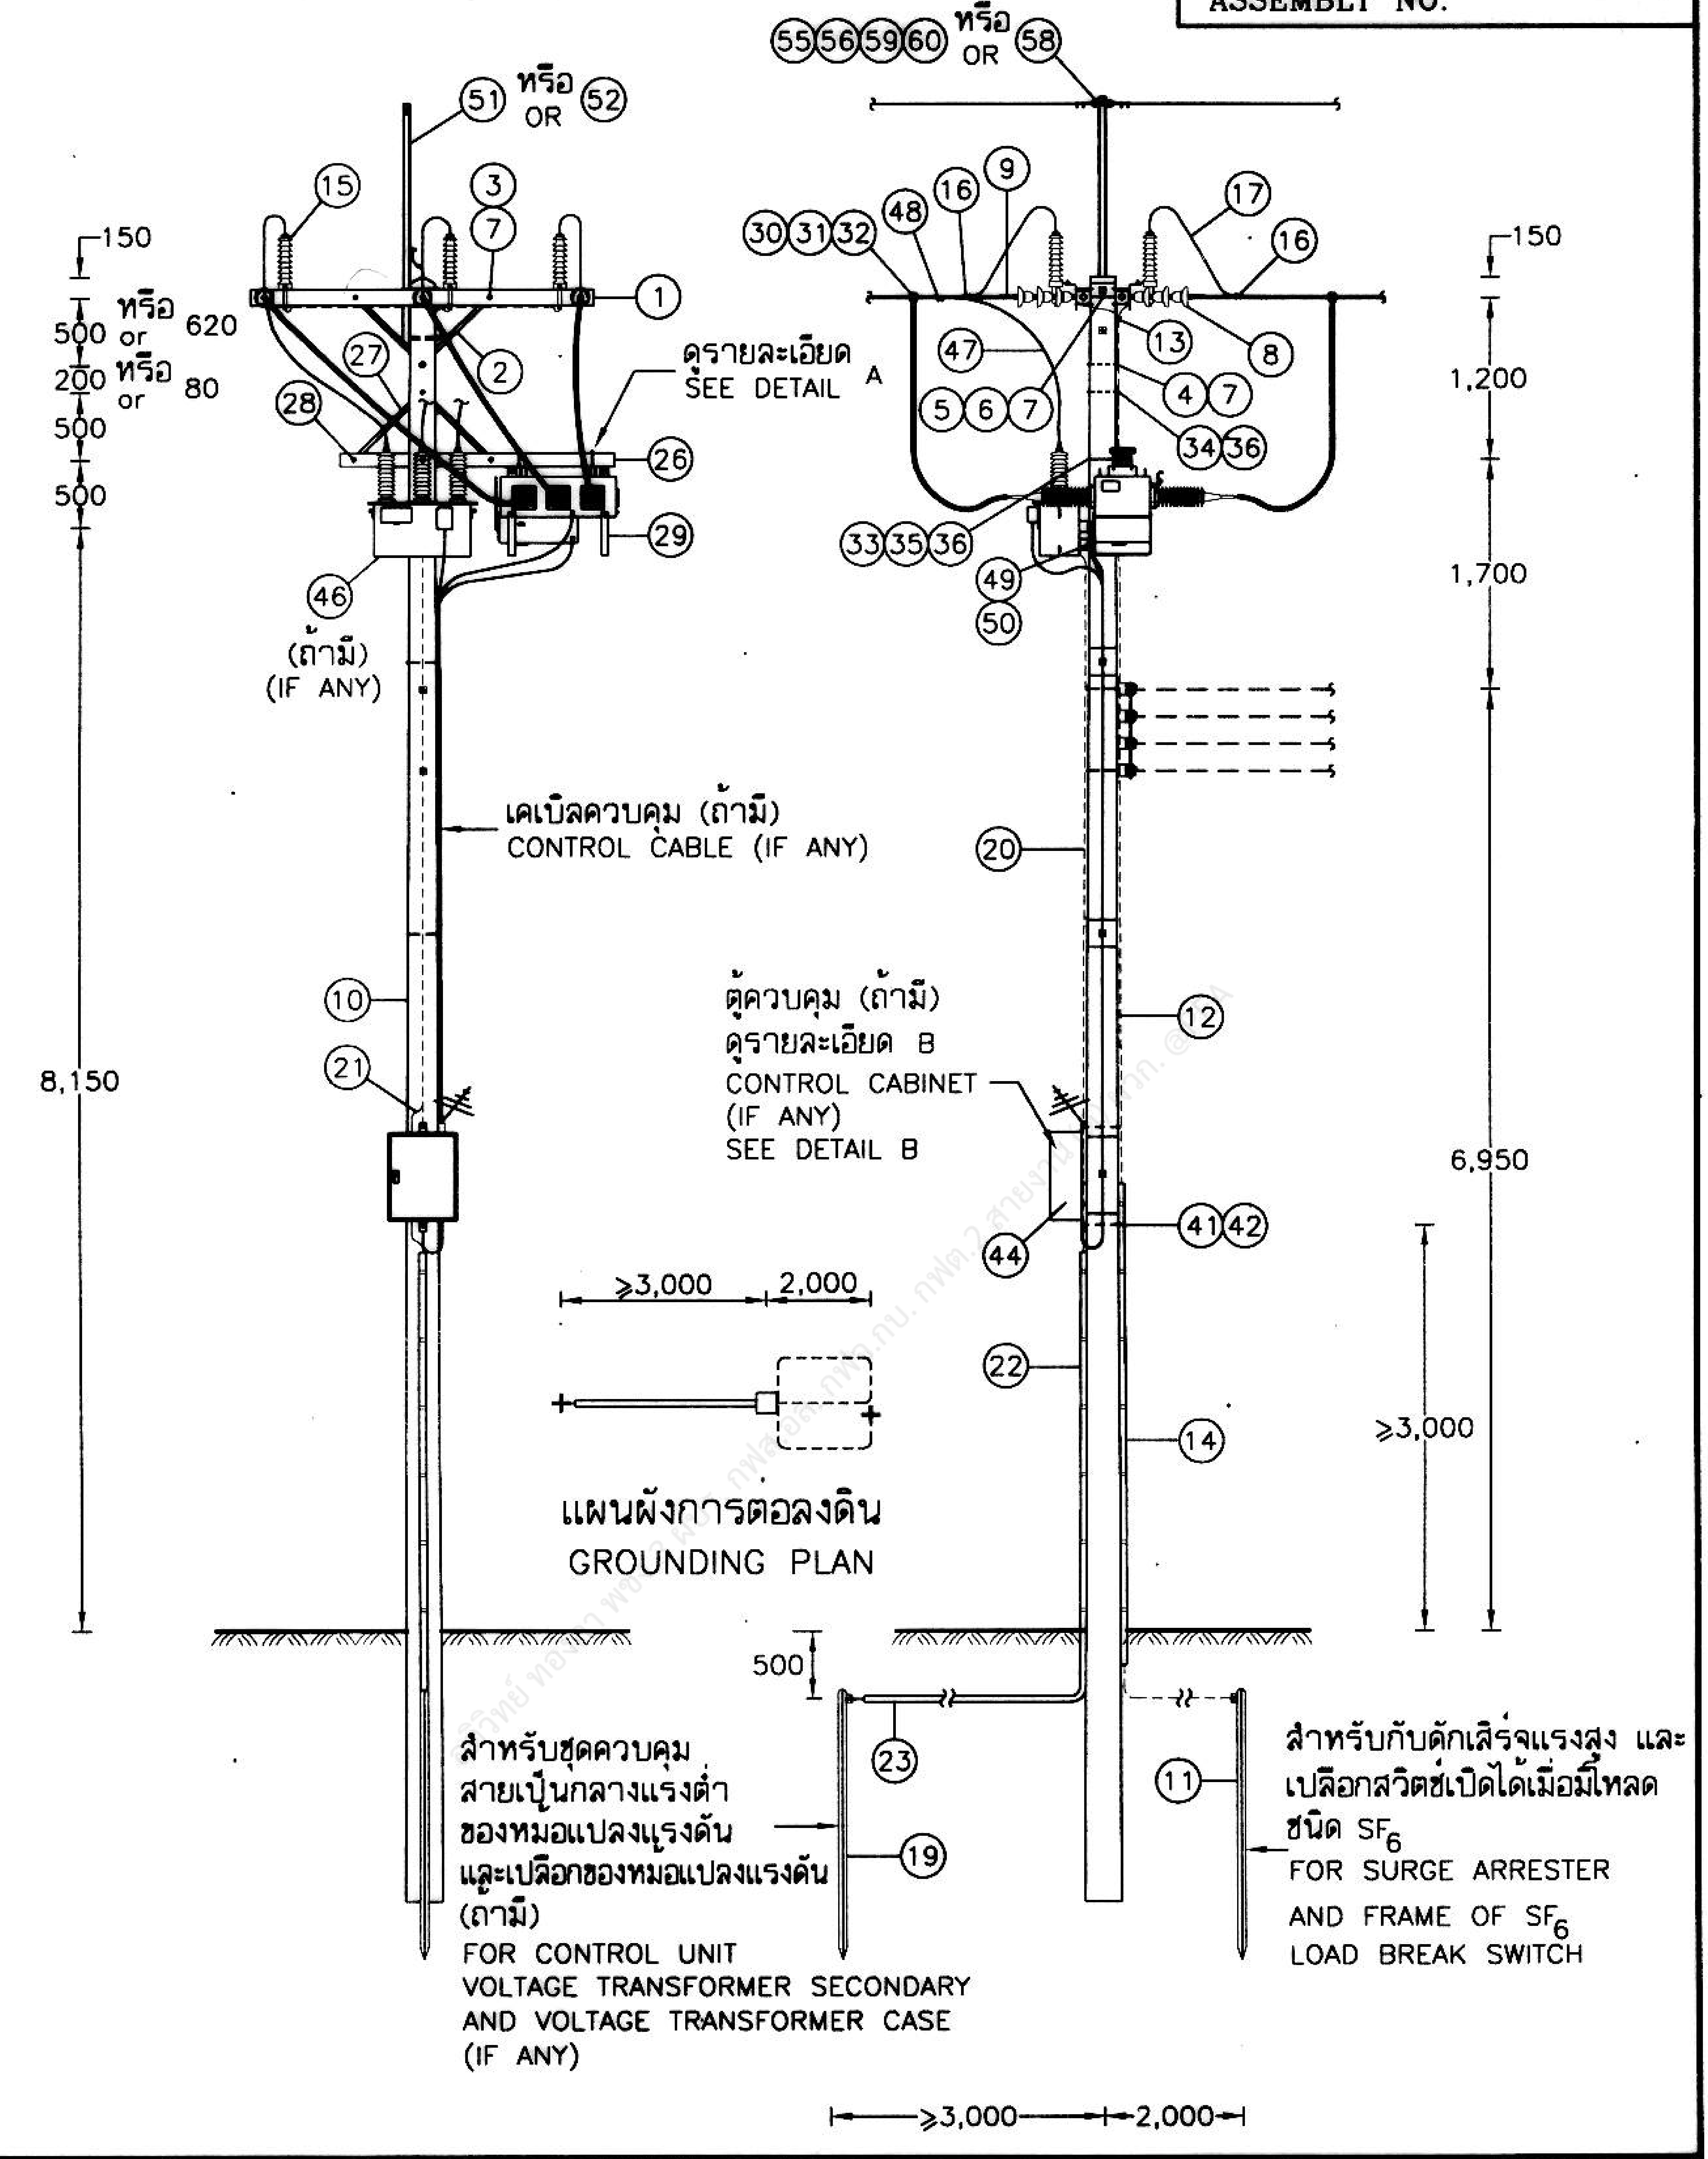

(55)(56)(59)(60) หรือ OR (58)
(51) หรือ OR (52)
(15)
(3)
(7)
(1)
(2)
(27)
(28)
(26)
(29)
(46)
(ถ้ามี) (IF ANY)
ดูรายละเอียด A SEE DETAIL A
150
500 หรือ or 620
200 หรือ or 80
500
500
8,150
(30)(31)(32)
(48)
(16)
(9)
(17)
(16)
150
1,200
(47)
(13)
(8)
(5)(6)(7)
(4)(7)
(34)(36)
(33)(35)(36)
(49)
(50)
1,700
เคเบิลควบคุม (ถ้ามี) CONTROL CABLE (IF ANY)
(20)
(10)
(12)
(21)
ตู้ควบคุม (ถ้ามี) ดูรายละเอียด B CONTROL CABINET (IF ANY) SEE DETAIL B
6,950
(41)(42)
(44)
≥3,000
2,000
(22)
(14)
≥3,000
แผนผังการต่อลงดิน GROUNDING PLAN
500
(23)
(11)
(19)
สำหรับชุดควบคุม สายเป็นกลางแรงต่ำ ของหม้อแปลงแรงดัน และเปลือกของหม้อแปลงแรงดัน (ถ้ามี)
FOR CONTROL UNIT VOLTAGE TRANSFORMER SECONDARY AND VOLTAGE TRANSFORMER CASE (IF ANY)
สำหรับกับดักเสิร์จแรงสูง และ เปลือกสวิตช์เปิดได้เมื่อมีโหลด ชนิด SF6
FOR SURGE ARRESTER AND FRAME OF SF6 LOAD BREAK SWITCH
≥3,000
2,000

กองวิศวกรรมไฟฟ้าและเครื่องกล
ฝ่ายวิศวกรรม

การไฟฟ้าส่วนภูมิภาค

ผู้เขียน
ผู้สำรวจ
วิศวกร
หัวหน้าแผนก
ผู้อำนวยการกอง
ผู้อำนวยการฝ่าย
รองผู้ว่าการเทคนิคและบริการ

ผู้ว่าการ 30 เม.ย. 2542

การติดตั้งสวิตช์เปิดได้เมื่อมีโหลดชนิด SF_6 สามารถใช้การควบคุมระยะไกล 33 kV 400 A
ผลิตภัณฑ์ G&W U.S.A. ทำโดย PRECISE

SWITCH SF_6, LOAD BREAK, REMOTE CONTROLLED 33 kV 400 A INSTALLATION
TRADE-MARK : **G&W U.S.A.**
MANUFACTURED BY **PRECISE**

ใช้แทนแบบ
ถูกแทนโดยแบบ
เขียนเสร็จวันที่ 26 ก.พ. 2542
แก้แบบวันที่
มิติเป็น มิลลิเมตร
มาตราส่วน 1 : 75
แบบเลขที่ SA4-015/42006
แผ่นที่ 1 ของจำนวน 10 แผ่น

30 เม.ย. 2542

การประกอบเลขที่
ASSEMBLY NO. 3421

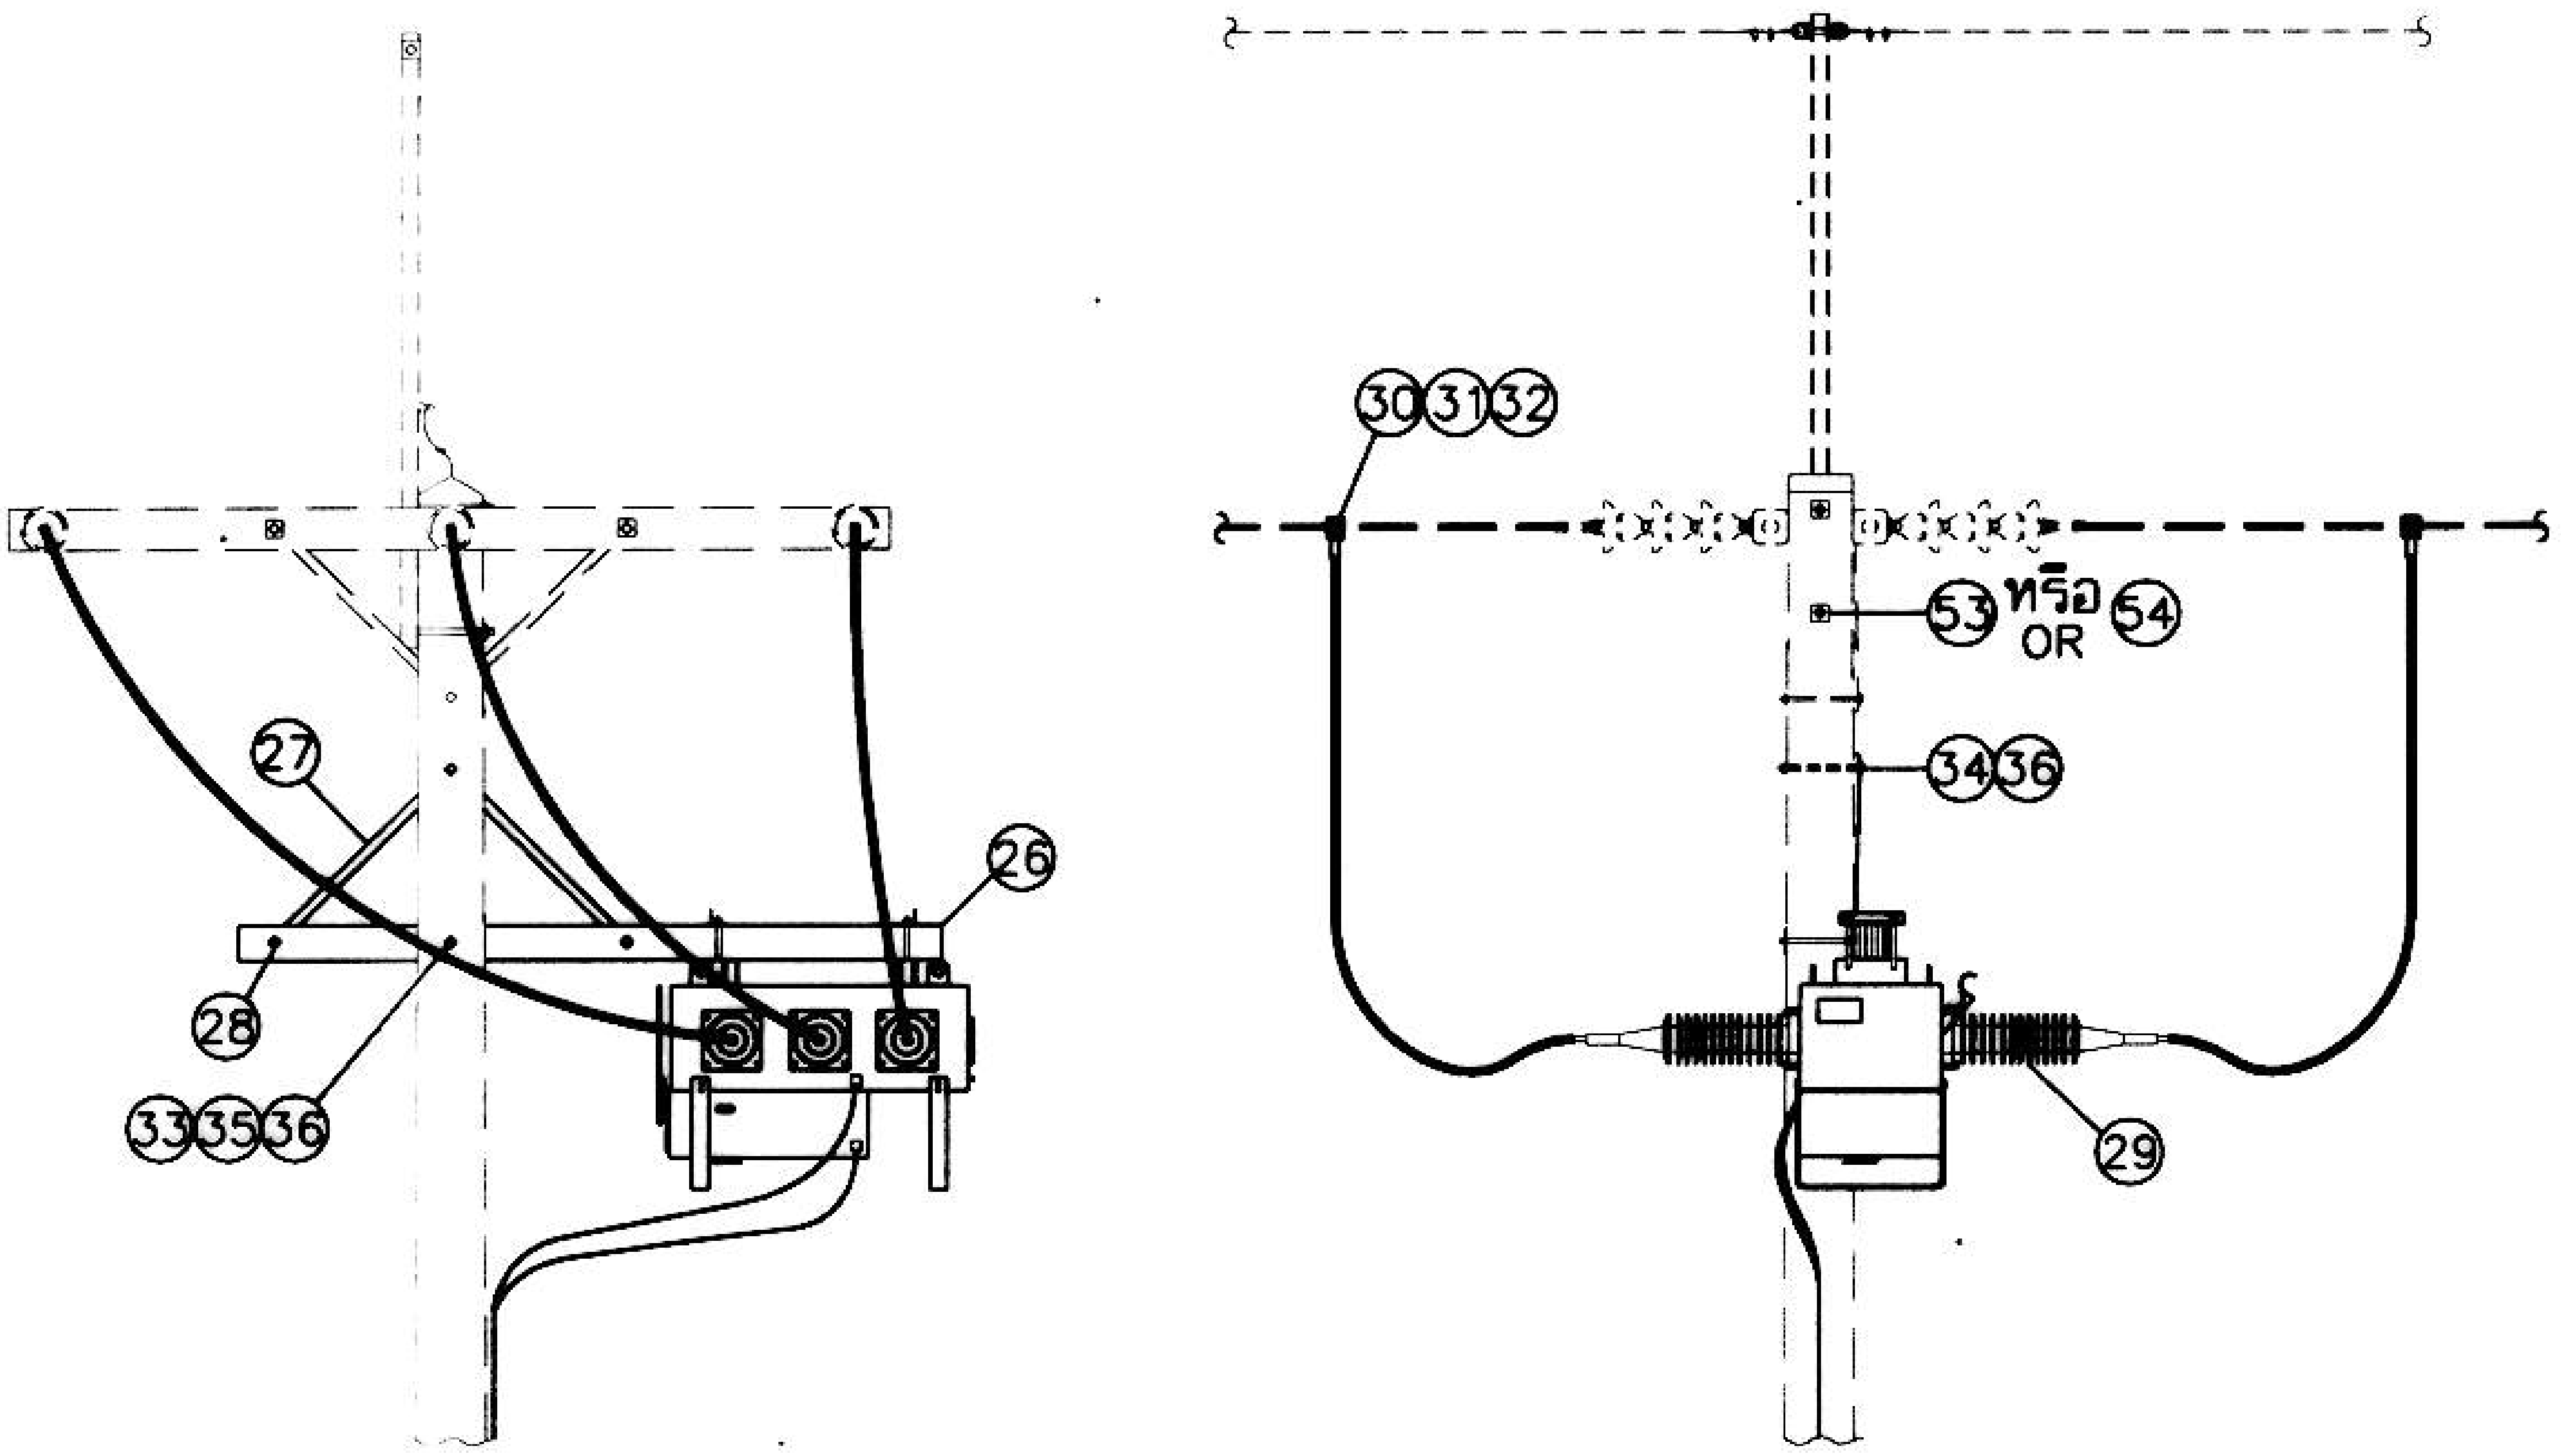

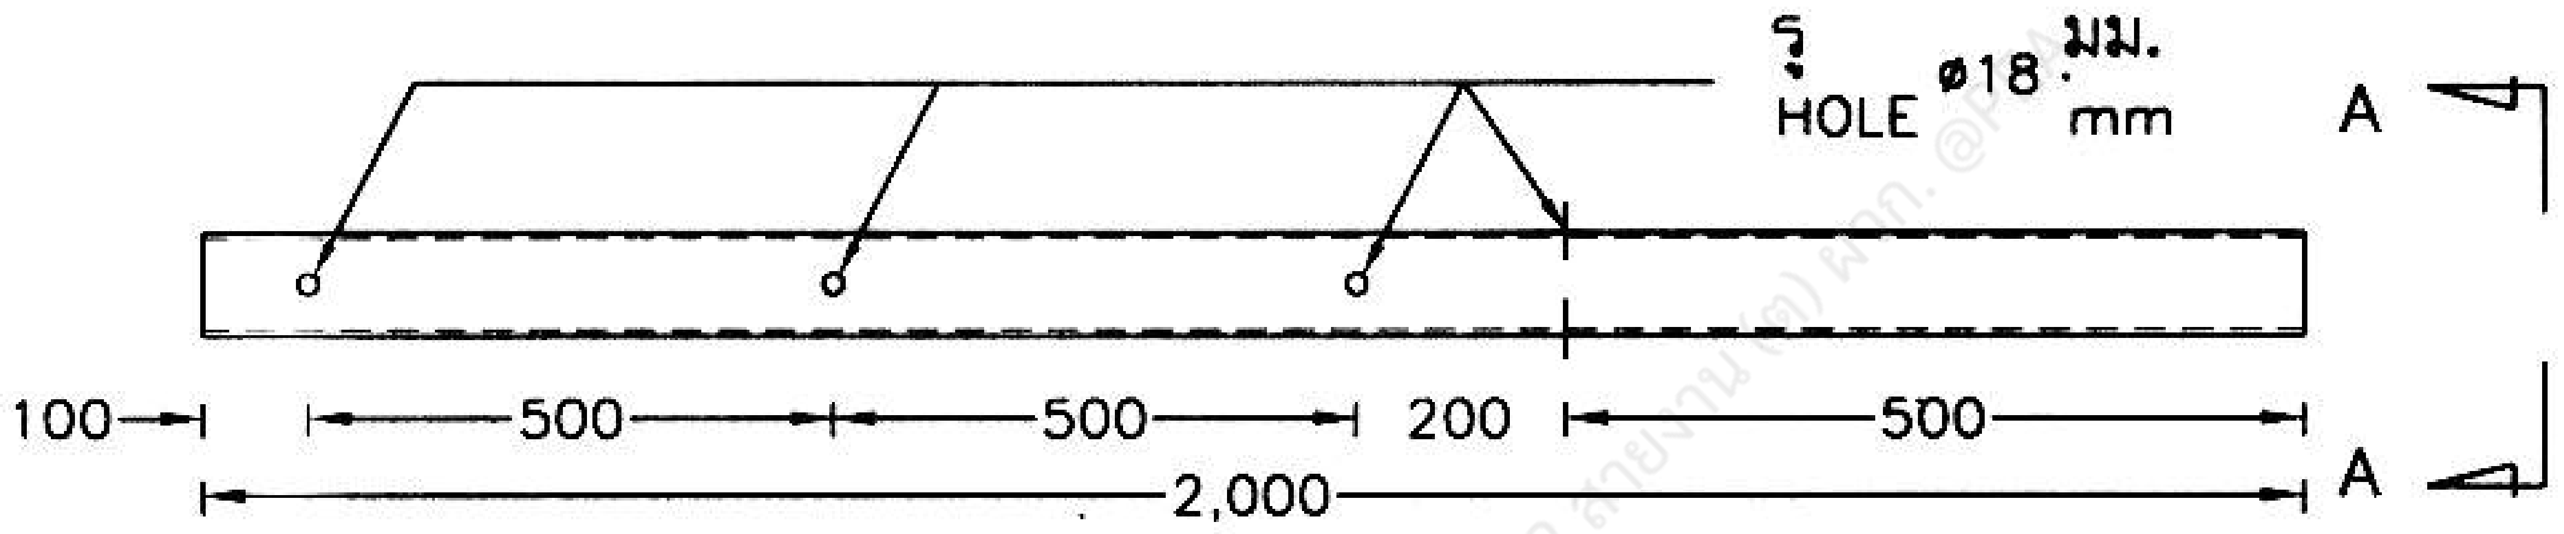

(26) เหล็กกลวงสี่เหลี่ยมจัตุรัส ขนาด 100x100x3.2 มม. ยาว 2,000 มม.
STEEL, SQUARE, 100x100x3.2 mm, 2,000 mm LONG

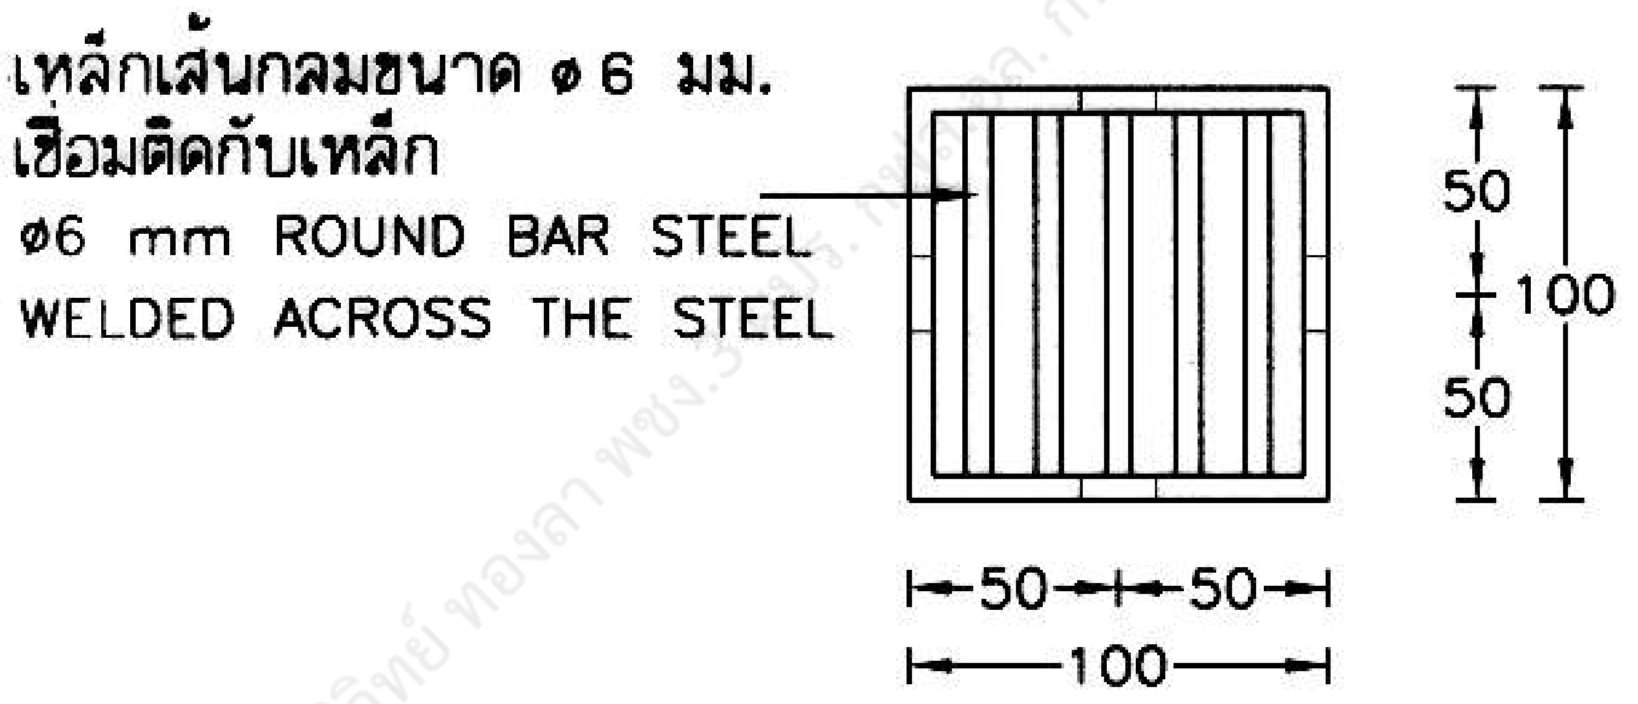

รูปตัด
SECTION A–A

รายละเอียด
DETAIL A

การติดตั้งสวิตช์เปิดได้เมื่อมีโหลด ชนิด SF_6 33 kV
33 kV SF_6 LOAD BREAK SWITCH INSTALLATION

กองวิศวกรรมไฟฟ้าและเครื่องกล
ฝ่ายวิศวกรรม

ผู้เขียน ....
ผู้สำรวจ ....
วิศวกร ....
หัวหน้าแผนก ....
ผู้อำนวยการกอง ....
ผู้อำนวยการฝ่าย ....
รองผู้ว่าการเทคนิคและบริการ
....

การไฟฟ้าส่วนภูมิภาค

ผู้ว่าการ 30 เม.ย. 2542

การติดตั้งสวิตช์เปิดได้เมื่อมีโหลดชนิด SF_6
สามารถใช้การควบคุมระยะไกล 33 kV 400 A
ผลิตภัณฑ์ G&W U.S.A. ทำโดย PRECISE

SWITCH SF_6, LOAD BREAK, REMOTE CONTROLLED
33 kV 400 A INSTALLATION
TRADE–MARK : **G&W U.S.A.**
MANUFACTURED BY **PRECISE**

ใช้แทนแบบ ....
ถูกแทนโดยแบบ ....
เขียนเสร็จวันที่ 26 ก.พ. 2542
แก้แบบวันที่ ....
มิติเป็น มิลลิเมตร
มาตราส่วน 1:10,1:20,1:50
แบบเลขที่ SA4–015/42006
แผ่นที่ 2 ของจำนวน 10 แผ่น

30 เม.ย. 2542

การประกอบเลขที่ **ASSEMBLY NO.** 3421

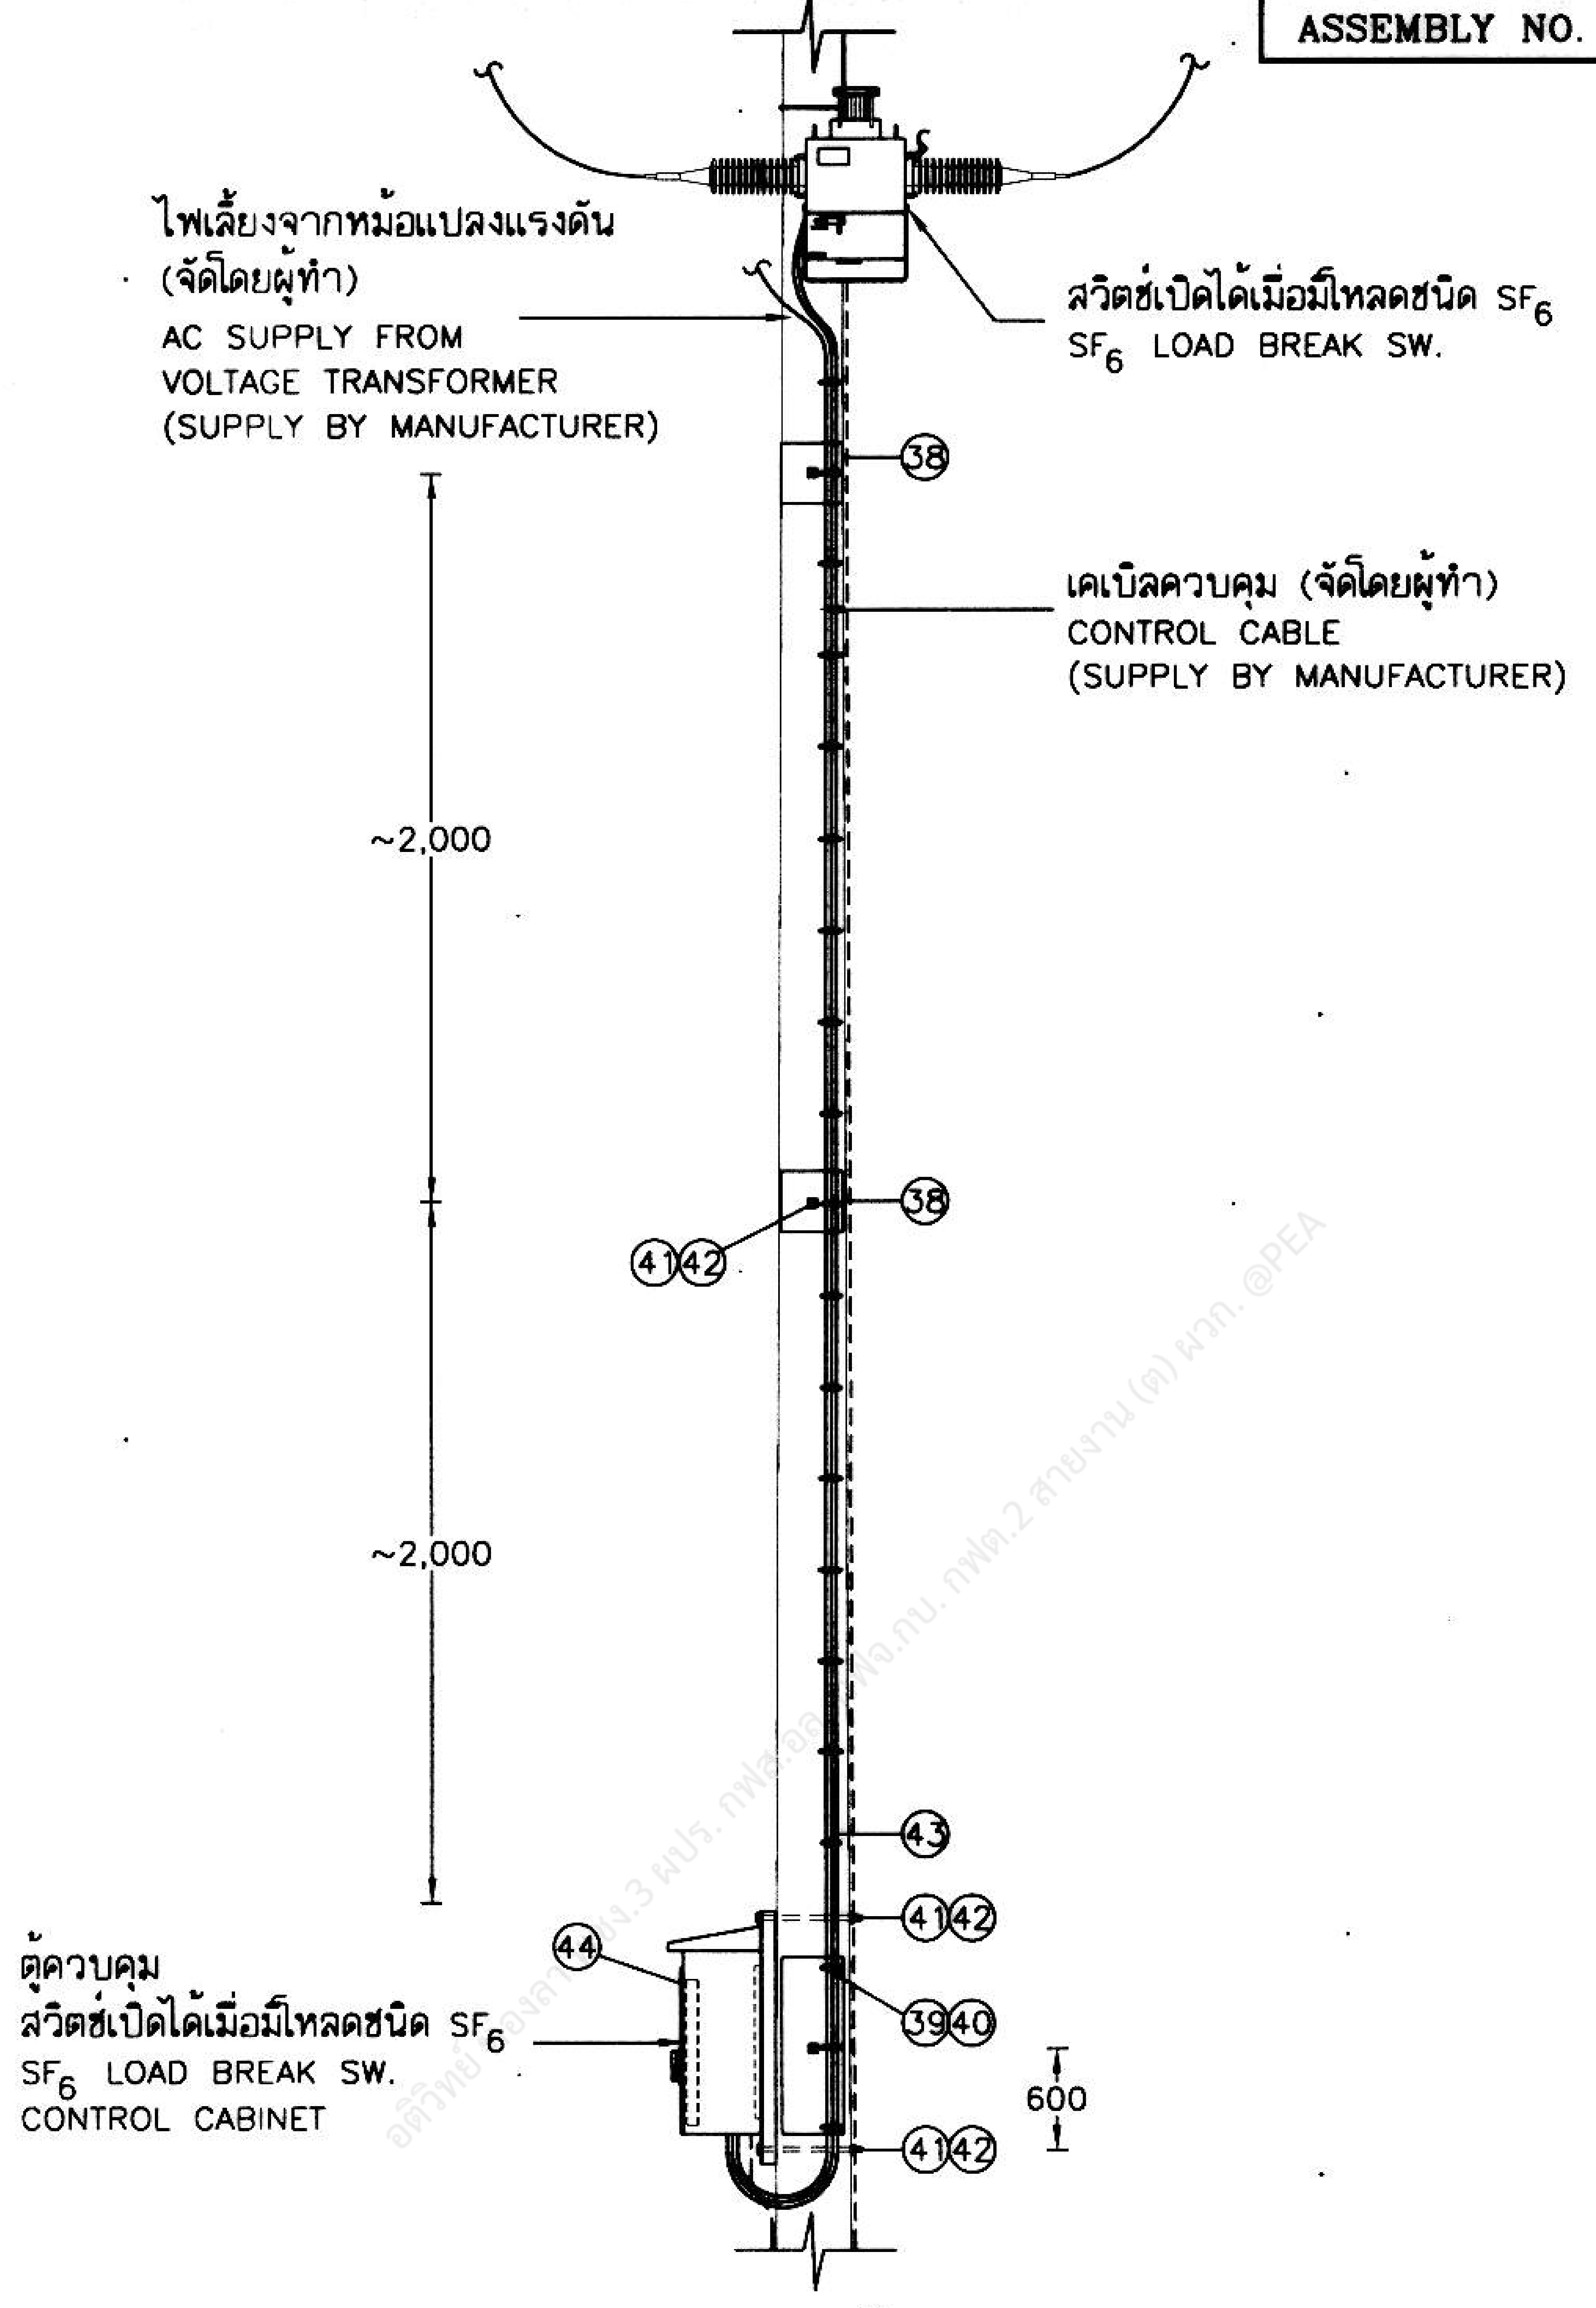

ไฟเลี้ยงจากหม้อแปลงแรงดัน (จัดโดยผู้ทำ)
AC SUPPLY FROM VOLTAGE TRANSFORMER (SUPPLY BY MANUFACTURER)
สวิตช์เปิดได้เมื่อมีโหลดชนิด SF6
SF6 LOAD BREAK SW.
38
เคเบิลควบคุม (จัดโดยผู้ทำ)
CONTROL CABLE (SUPPLY BY MANUFACTURER)
~2,000
38
41 42
~2,000
43
41 42
44
ตู้ควบคุม สวิตช์เปิดได้เมื่อมีโหลดชนิด SF6
SF6 LOAD BREAK SW. CONTROL CABINET
39 40
600
41 42

รายละเอียด B
DETAIL B

รายละเอียดการติดตั้งชุดควบคุมการปลดสับสวิตช์เปิดได้เมื่อมีโหลดชนิด SF_6
CONTROL CABINET OF SF_6 LOAD BREAK SWITCH INSTALLATION DETAIL

กองวิศวกรรมไฟฟ้าและเครื่องกล
ฝ่ายวิศวกรรม

การไฟฟ้าส่วนภูมิภาค

ใช้แทนแบบ ....
ถูกแทนโดยแบบ ....
เขียนเสร็จวันที่ 26 ก.พ. 2542
แก้แบบวันที่ ....
มิติเป็น มิลลิเมตร
มาตราส่วน...............

ผู้เขียน ....
ผู้สำรวจ...............
วิศวกร...............
หัวหน้าแผนก...............
ผู้อำนวยการกอง...............
ผู้อำนวยการฝ่าย...............
รองผู้ว่าการเทคนิคและบริการ
....

ผู้ว่าการ 30 เม.ย. 2542 ....

การติดตั้งสวิตช์เปิดได้เมื่อมีโหลดชนิด SF_6
สามารถใช้การควบคุมระยะไกล 33 kV 400 A
ผลิตภัณฑ์ G&W U.S.A. ทำโดย PRECISE

SWITCH SF_6, LOAD BREAK, REMOTE CONTROLLED
33 kV 400 A INSTALLATION
TRADE-MARK : **G&W U.S.A.**
MANUFACTURED BY **PRECISE**

แบบเลขที่ SA4-015/42006
แผ่นที่ 3 ของจำนวน 10 แผ่น

30 เม.ย. 2542

การประกอบเลขที่ **ASSEMBLY NO.** 3421

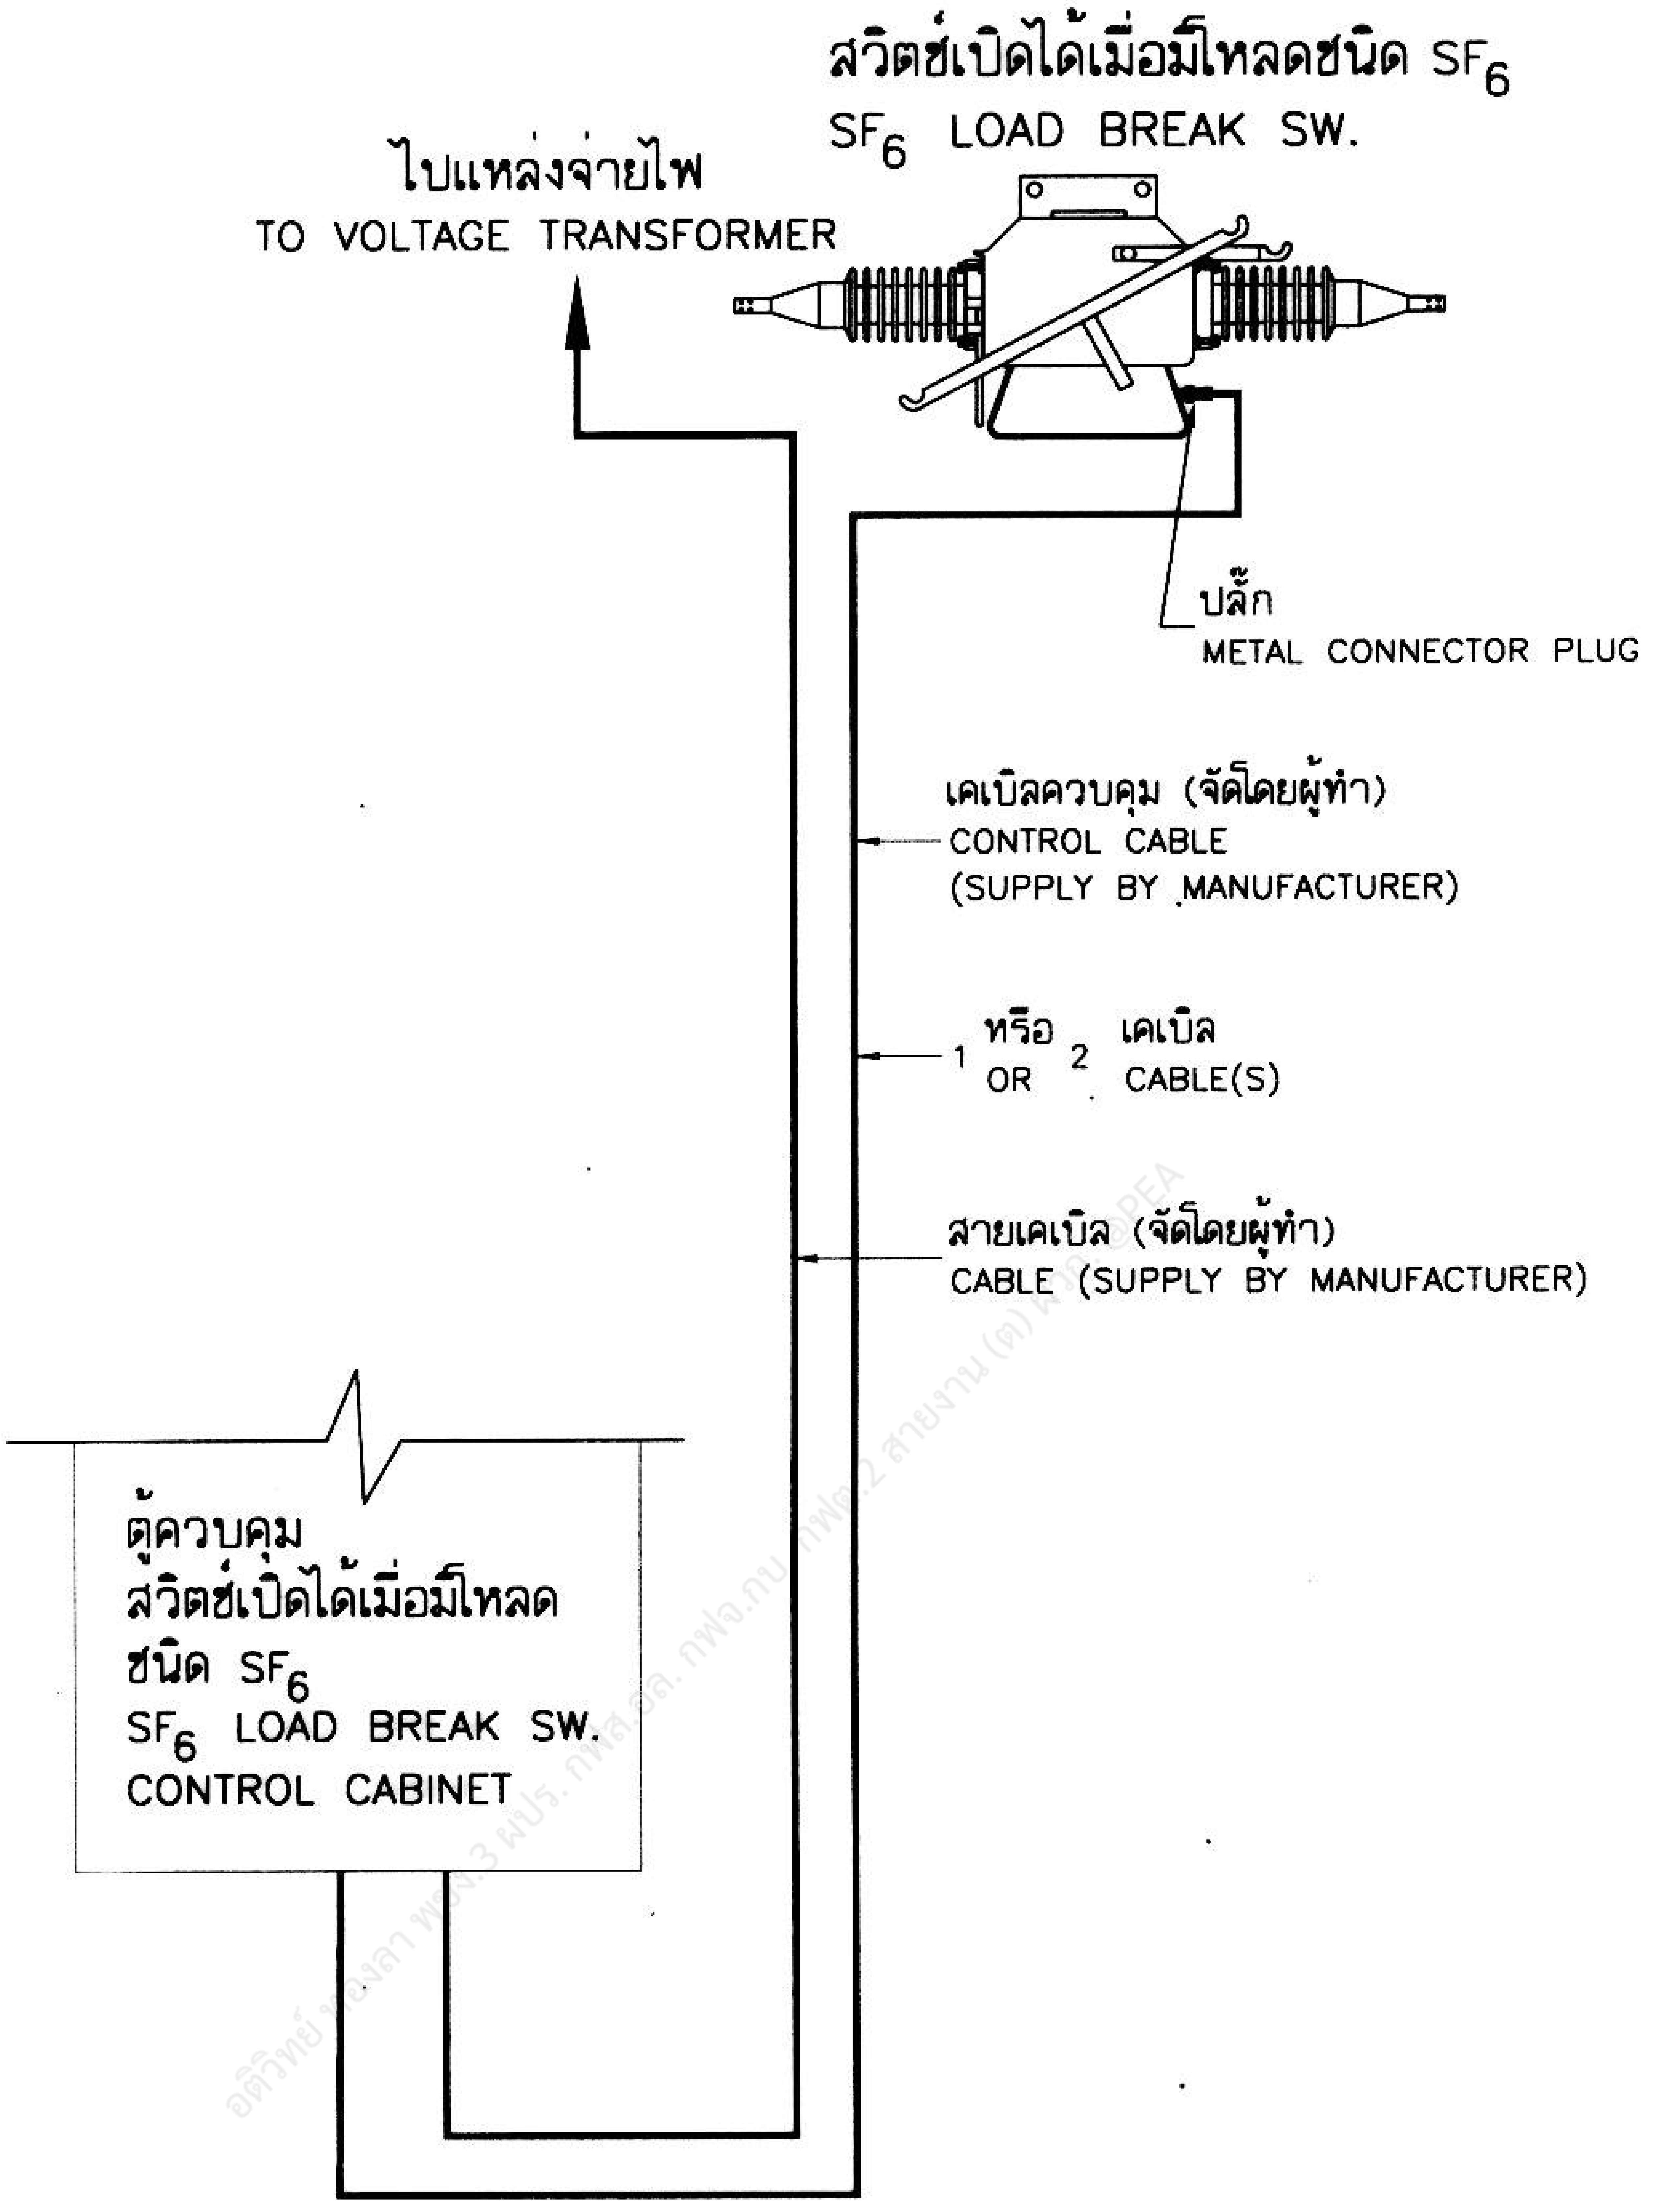

รายละเอียดการติดตั้งชุดควบคุมการปลดสับ สวิตช์เปิดได้เมื่อมีโหลดชนิด SF_6
CONTROL CABINET OF SF_6 LOAD BREAK SWITCH INSTALLATION DETAIL

อดิวิทย์ ทองลา พชง.3 ผปร. กพส.อล. กฟจ.กบ. กฟฉ.2 สายงาน (ต) PEA

กองวิศวกรรมไฟฟ้าและเครื่องกล ฝ่ายวิศวกรรม	การไฟฟ้าส่วนภูมิภาค	ใช้แทนแบบ .... ถูกแทนโดยแบบ .... เขียนเสร็จวันที่ 26 ก.พ. 2542
ผู้เขียน .... ผู้สำรวจ .... วิศวกร .... หัวหน้าแผนก .... ผู้อำนวยการกอง .... ผู้อำนวยการฝ่าย	ผู้ว่าการ ....30 เม.ย. 2542.... การติดตั้งสวิตช์เปิดได้เมื่อมีโหลดชนิด SF_6 สามารถใช้การควบคุมระยะไกล 33 kV 400 A **ผลิตภัณฑ์ G&W U.S.A. ทำโดย PRECISE**	แก้แบบวันที่ .... มิติเป็น มิลลิเมตร มาตราส่วน ....
รองผู้ว่าการเทคนิคและบริการ	SWITCH SF_6, LOAD BREAK, REMOTE CONTROLLED 33 kV 400 A INSTALLATION TRADE-MARK : **G&W U.S.A.** MANUFACTURED BY **PRECISE**	แบบเลขที่ SA4-015/42006 แผ่นที่ 4 ของจำนวน 10 แผ่น

30 เม.ย. 2542

การประกอบเลขที่ 3421
ASSEMBLY NO.

บัญชีวัสดุ
BILL OF MATERIAL

ลำดับที่ ITEM	รายละเอียด DESCRIPTION	จำนวน REQ'D	วัสดุเลขที่ MAT. NO.
A	สำหรับการประกอบคอน คอร. กับเสา คอร. แบบเข้าปลายสายสองข้าง FOR CONCRETE CROSSARM ASSEMBLY, DOUBLE DEADEND STRUCTURE		
1	คอน คอร. สปัน 120x120x2,500 มม. CROSSARM, PRESTRESSED CONCRETE, SPUN, 120x120x2,500 mm	2	00110004
2	เหล็กประกับคอน ขนาด 30x6x760 มม. หรือ 40x6x1,000 มม. BRACE, FLAT, FOR CROSSARM, 30x6x760 mm or 40x6x1,000 mm	2	01200001 or 01200002
3	สลักเกลียว M 16x170 มม. BOLT, MACHINE, M 16x170 mm	2	01110200
4	สลักเกลียว M 16 ความยาวตามต้องการ BOLT, MACHINE, M 16 ; LENGTH AS REQUIRED	1	01110202 01110203 01110204
5	สลักเกลียวห่วงกลม M 16 ความยาวตามต้องการ BOLT, DOUBLE ARMING, ROUND EYE M 16 ; LENGTH AS REQUIRED	3	01130001 01130002 01130002
6	นัทรูปห่วง M 16 DIN 582 NUT, EYE, M 16, DIN 582	3	01180001
7	แหวนสี่เหลี่ยมแบน 52x52x4.5 มม. รู ø18 มม. มอก. 258 WASHER, SQUARE, FLAT, 52x52x4.5 mm, HOLE. ø18 mm, TIS 258	13	01180100
8	ลูกถ้วยแขวน มอก 354 แบบ ง (แบบ 52-4) INSULATOR, SUSPENSION TYPE, TIS 354, TYPE D (CLASS 52-4)	18	03020001
9	สเตรนแคล้มป์แบบตรง สำหรับสายอะลูมิเนียม ขนาดตามต้องการ CLAMP, STRAIN, STRAIGHT TYPE, Al ; SIZE AS REQUIRED	6	03110002 03110007
10	เสาคอนกรีต 12.00 ม., 12.20 ม., 14.00 ม. หรือ 14.30 ม. POLE, CONCRETE, 12.00 m, 12.20 m, 14.00 m OR 14.30 m LONG	1	00010004 00010012 or 00010006 00010013
B	สำหรับการต่อลงดิน ระบบแรงสูง และการติดตั้งอุปกรณ์ป้องกัน FOR H.T. GROUNDING AND PROTECTIVE EQUIPMENT INSTALLATION		
11	หลักดิน 60x60x5 มม. ยาว 2,000. มม. GROUND ROD, 60x60x5 mm, 2,000 mm LONG	1	01220002
12	ลวดเหล็กตีเกลียว 50/7 ต.มม. มอก. 404 พร้อมอุปกรณ์ยึด (การประกอบเลขที่ 9703, 9703A) WIRE, STEEL STRANDED, 50/7 mm^2, TIS 404 ; COMP. WITH FIXING ACCESSORIES (ASSEMBLY No. 9703, 9703A)	26 ม. m	01100004
13	ยูแคล้มป์ สลัก 1 ตัว M 8 CLAMP, SINGLE U-BOLT, M 8	13	01230000
14	ท่อ PVC แข็งขนาด ø 20x2,500-4,000 มม. พร้อมอุปกรณ์ยึด (การประกอบเลขที่ 9704, 9704A) CONDUIT, PVC RIGID, ø 20x2,500-4,000 mm ; COMP. WITH FIXING ACCESS. (ASSEMBLY No. 9704, 9704A)	1	08040002 or 08040001
15	กับดักเสิร์จแรงสูง 30 kV 5 kA หรือ 30 kV 10 kA SURGE ARRESTER, 30 kV, 5 kA or 30 kV, 10 kA	6	04000100 04000101
16	พีจี.คอนเนคเตอร์ 3 สลัก สำหรับสายอะลูมิเนียม 70-185 ต.มม. CONNECTOR,PARALLEL GROOVE,TRIPLE BOLT,Al , 70-185 sq.mm.	6	02300103

กองวิศวกรรมไฟฟ้าและเครื่องกล
ฝ่ายวิศวกรรม

ผู้เขียน
ผู้สำรวจ..................
วิศวกร
หัวหน้าแผนก
ผู้อำนวยการกอง
ผู้อำนวยการฝ่าย

รองผู้ว่าการเทคนิคและบริการ
....

การไฟฟ้าส่วนภูมิภาค

ผู้ว่าการ....30 เม.ย. 2542..........

การติดตั้งสวิตช์เปิดได้เมื่อมีโหลดชนิด SF$_6$
สามารถใช้การควบคุมระยะไกล 33 kV 400 A
ผลิตภัณฑ์ G&W U.S.A. ทำโดย PRECISE

SWITCH SF$_6$, LOAD BREAK, REMOTE CONTROLLED
33 kV 400 A INSTALLATION
TRADE-MARK : **G&W U.S.A.**
MANUFACTURED BY **PRECISE**

ใช้แทนแบบ ....
ถูกแทนโดยแบบ ....
เขียนเสร็จวันที่ 26 ก.พ. 2542
แก้แบบวันที่ ....
มิติเป็น....................
มาตราส่วน..................

แบบเลขที่ SA4-015/42006
แผ่นที่ 5 ของจำนวน 10 แผ่น

30 เม.ย. 2542

การประกอบเลขที่ 3421
ASSEMBLY NO.

บัญชีวัสดุ
BILL OF MATERIAL

ลำดับที่ ITEM	รายละเอียด DESCRIPTION	จำนวน REQ'D	วัสดุเลขที่ MAT. NO.
17	สายอะลูมิเนียมหุ้มฉนวน พี วี ซี 750 V 75 °C มอก. 293 CABLE, Al, PVC INSULATED, 750 V, 75 °C, TIS 293	6 ม. m	02070003 or 02070004
18			
C	**สำหรับการต่อลงดิน ระบบแรงต่ำ** **FOR L.T. GROUNDING**		
19	หลักดิน 60x60x5 มม. ยาว 2,000 มม. GROUND ROD, 60x60x5 mm, 2,000 mm LONG	1	01220002
20	ลวดเหล็กตีเกลียว 50/7 ต.มม. มอก. 404 พร้อมอุปกรณ์ยึด (การประกอบเลขที่ 9703, 9703A) WIRE, STEEL STRANDED, 50/7 mm², TIS 404 ; COMP. WITH FIXING ACCESSORIES (ASSEMBLY No. 9703, 9703A)	13 ม. m	01100004
21	ยูแคล้มป์ สลัก 1 ตัว M 8 CLAMP, SINGLE U-BOLT, M 8	2	01230000
22	ท่อ PVC แข็งขนาด ø 20x2,500-4,000 มม. พร้อมอุปกรณ์ยึด (การประกอบเลขที่ 9704, 9704A) CONDUIT, PVC RIGID, ø 20x2,500-4,000 mm ; COMP. WITH FIXING ACCESS. (ASSEMBLY No. 9704, 9704A)	1	08040002 or 08040001
23	ท่อ PVC แข็งขนาด ø 20x2,500 มม. พร้อมท่อโค้ง 90° CONDUIT, PVC RIGID, ø 20x2,500 mm ; COMP. WITH 90° ELBOW	1	
24			
25			
D	**สำหรับการติดตั้ง สวิตช์เปิดได้เมื่อมีโหลดชนิด SF_6 33 kV** **FOR 33 kV SF_6 LOAD BREAK SWITCH INSTALLATION**		
26	เหล็กกลวง สี่เหลี่ยมจัตุรัส ขนาด 100x100x3.2 มม. ยาว 2,000 มม. มอก. 107 เจาะรูตามรายละเอียดแผ่นที่ 2 STEEL, SQUARE, 100x100x3.2 mm, 2,000 mm LONG, TIS 107 ; PUNCH HOLE AS DWG. ON SHEET NO. 2	1	
27	เหล็กประกับคอน ขนาด 30x6x760 มม. BRACE, FLAT, FOR CROSSARM, 30x6x760 mm	2	01200001
28	สลักเกลียว M 16x130 มม. BOLT, MACHINE, M 16x130 mm	3	01110200

กองวิศวกรรมไฟฟ้าและเครื่องกล
ฝ่ายวิศวกรรม

ผู้เขียน
ผู้สำรวจ
วิศวกร
หัวหน้าแผนก
ผู้อำนวยการกอง
ผู้อำนวยการฝ่าย

รองผู้ว่าการเทคนิคและบริการ

การไฟฟ้าส่วนภูมิภาค

ผู้ว่าการ 30 เม.ย. 2542

การติดตั้งสวิตช์เปิดได้เมื่อมีโหลดชนิด SF_6
สามารถใช้การควบคุมระยะไกล 33 kV 400 A
ผลิตภัณฑ์ G&W U.S.A. ทำโดย PRECISE

SWITCH SF_6, LOAD BREAK, REMOTE CONTROLLED
33 kV 400 A INSTALLATION
TRADE-MARK : **G&W U.S.A.**
MANUFACTURED BY **PRECISE**

ใช้แทนแบบ ....
ถูกแทนโดยแบบ ....
เขียนเสร็จวันที่ 26 ก.พ. 2542
แก้แบบวันที่ ....
มิติเป็น ....
มาตราส่วน ....

แบบเลขที่ SA4-015/42006
แผ่นที่ 6 ของจำนวน 10 แผ่น

30 เม.ย. 2542

การประกอบเลขที่
ASSEMBLY NO. 3421

บัญชีวัสดุ
BILL OF MATERIAL

ลำดับที่ ITEM	รายละเอียด DESCRIPTION	จำนวน REQ'D	วัสดุเลขที่ MAT. NO.
29	สวิตช์เปิดได้เมื่อมีโหลด 3 เฟส 33 kV 400 แอมป์ สามารถใช้การควบคุมระยะไกล พร้อมอุปกรณ์จับยึดและขั้วต่อสาย SWITCH, SF_6 , LOAD BREAK, 3-PHASE, 33 kV, 400 A, REMOTE CONTROLLED COMPLETE WITH MOUNTING HARDWARE AND TERMINAL CONNECTOR	1 ชุด SET	04070107
30	คอมเปาด์ ช่วยสัมผัสทางไฟฟ้า COMPOUND, ELECTRICAL CONTACT AID	กก. kg	09080000
31	เทปพันเคเบิลอากาศแรงสูง ELECTRICAL SPLICING TAPE, FOR H.T. AERIAL CABLE	8 ม้วน rolls	02180003
32	เทปไฟฟ้า PVC หรือเทปไฟฟ้ายางซิลิโคน PVC PLASTIC OR SILICONE RUBBER ELECTRICAL TAPE	40 ม. m	02180002 or 02180004
33	แหวนรองแบบสปริง ขนาดระบุ 16 มม. ประเภทใช้งานทั่วไป มอก. 259 WASHER, LOCK, SPRING, SIZE 16 mm, GENERAL PURPOSE, TIS 259	1	01180301
34	สลักเกลียว M 16x200 มม. สำหรับเสาคอนกรีต 12.00 ม. BOLT, MACHINE, M 16x200 mm FOR 12.00 m CONCRETE POLE	1	01110202
	สลักเกลียว M 16x250 มม. สำหรับเสาคอนกรีต 12.20 ม. และ 14.00 ม. BOLT, MACHINE, M 16x250 mm FOR 12.20 m AND 14.00 m CONCRETE POLE		01110203
	สลักเกลียว M 16x300 มม. สำหรับเสาคอนกรีต 14.30 ม. BOLT, MACHINE, M 16x300 mm FOR 14.30 m CONCRETE POLE		01110204
35	สลักเกลียว M 16x300 มม. สำหรับเสาคอนกรีต 12.00 ม. BOLT, MACHINE, M 16x300 mm FOR 12.00 m CONCRETE POLE	1	01110204
	สลักเกลียว M 16x350 มม. สำหรับเสาคอนกรีต 12.20 ม. และ 14.00 ม. BOLT, MACHINE, M 16x350 mm FOR 12.20 m AND 14.00 m CONCRETE POLE		01110205
	สลักเกลียว M 16x400 มม. สำหรับเสาคอนกรีต 14.30 ม. BOLT, MACHINE, M 16x400 mm FOR 14.30 m CONCRETE POLE		01110206
36	แหวนสี่เหลี่ยมแบน 52x52x4.5 มม. รู ø18 มม. มอก. 258 WASHER, SQUARE, FLAT, 52x52x4.5 mm, HOLE. ø18 mm, TIS 258	2	01180100
37			
E	สำหรับการติดตั้งชุดควบคุมการปลดสับสวิตช์เปิดได้เมื่อมีโหลดชนิด SF_6 FOR CONTROL CABINET OF SF_6 LOAD BREAK SWITCH INSTALLATION		
38	แป้นไม้สำหรับยึดสายเข้า และออกจากตู้ควบคุม ไสแล้ว ขนาด 20x20x2 ซ.ม. CABLE PLATE, HARD WOOD, SURFACE FINISHED, 20x20x2 cm	2	–
39	เข็มขัดรัดสาย (ทำด้วยลวดอะลูมิเนียมแบน 1x10 มม.) ช่วงระยะ 50 ซ.ม. CABLE STRAP (MADE OF ARMOUR TAPE 1x10 mm) AT 50 cm INTERVALS	2 ม. m	02200000
40	ตะปูหัวกลมแบน ยาว 15-20 มม. ø1 มม. มอก. 113 NAIL, ROUND, MILD STEEL WIRE 15-20 mm LONG ø 1 mm TIS 113	24	–

กองวิศวกรรมไฟฟ้าและเครื่องกล
ฝ่ายวิศวกรรม

ผู้เขียน
ผู้สำรวจ..................
วิศวกร
หัวหน้าแผนก
ผู้อำนวยการกอง
ผู้อำนวยการฝ่าย
รองผู้ว่าการเทคนิคและบริการ

การไฟฟ้าส่วนภูมิภาค

ผู้ว่าการ......3 0 เม.ย. 2542..................

การติดตั้งสวิตช์เปิดได้เมื่อมีโหลดชนิด SF_6
สามารถใช้การควบคุมระยะไกล 33 kV 400 A
ผลิตภัณฑ์ G&W U.S.A. ทำโดย PRECISE

SWITCH SF_6, LOAD BREAK, REMOTE CONTROLLED
33 kV 400 A INSTALLATION
TRADE-MARK : **G&W U.S.A.**
MANUFACTURED BY **PRECISE**

ใช้แทนแบบ ....
ถูกแทนโดยแบบ ....
เขียนเสร็จวันที่ 26 ก.พ. 2542
แก้แบบวันที่ ....
มิติเป็น..................
มาตราส่วน...............
แบบเลขที่ SA4-015/42006
แผ่นที่ 7 ของจำนวน 10 แผ่น

3 0 เม.ย. 2542

การประกอบเลขที่ **ASSEMBLY NO.** 3421

บัญชีวัสดุ
BILL OF MATERIAL

ลำดับที่ ITEM	รายละเอียด DESCRIPTION	จำนวน REQ'D	วัสดุเลขที่ MAT. NO.
41	สลักเกลียว M 16x300 มม. สำหรับเสาคอนกรีต 12.00 ม. BOLT, MACHINE, M 16x300 mm FOR 12.00 m CONCRETE POLE	5	01110204
	สลักเกลียว M 16x350 มม. สำหรับเสาคอนกรีต 12.20 ม. และ 14.00 ม. BOLT, MACHINE, M 16x350 mm FOR 12.20 m AND 14.00 m CONCRETE POLE		01110205
	สลักเกลียว M 16x400 มม. สำหรับเสาคอนกรีต 14.30 ม. BOLT, MACHINE, M 16x400 mm FOR 14.30 m CONCRETE POLE		01110206
42	แหวนสี่เหลี่ยมแบน 52x52x4.5 มม. รู ø18 มม. มอก. 258 WASHER, SQUARE, FLAT, 52x52x4.5 mm, HOLE. ø18 mm, TIS 258	8	01180100
43	แป้นไม้รองรับมิเตอร์ ไสแล้ว ขนาด 60x20x2 ซ.ม. METER PLATE, HARD WOOD, SURFACE FINISHED, 60x20x2 cm	1	
44	ชุดควบคุมอัตโนมัติ สามารถใช้การควบคุมระยะไกล สำหรับสวิตช์เปิดได้เมื่อมีโหลด ชนิด SF_6 หรือแบบอื่นตามต้องการ CONTROL UNIT, AUTOMATIC REMOTE CONTROLLED, FOR SF_6 LOAD BREAK SWITCH, OR OTHER TYPE AS REQUIRED	1	04070305
45			
F	สำหรับการติดตั้งหม้อแปลงแรงดัน FOR VOLTAGE TRANSFORMER INSTALLATION		
46	หม้อแปลงแรงดัน 3 เฟส ใช้นอกอาคาร เรโช 33,000/110 V 10 VA 220 V 500 VA TRANSFORMER, VOLTAGE, 3 PHASE OUTDOOR, RATIO 33,000/110 V, 10 VA, 220 V 500 VA	1	06020150
47	สายหุ้มฉนวนแบบไม่เต็มพิกัด 33 kV หรือสายอะลูมิเนียมหุ้มฉนวน PVC 750 V 75 °C มอก. 293 ขนาด 95-120 ต.มม. ความยาวตามต้องการ CONDUCTOR, PARTIALLY INSULATED, 33 kV OR CABLE, Al PVC INSULATED, 750 V, 75 °C, TIS 293, SIZE 95-120 mm^2 ; LENGTH AS REQUIRED	ม. m	02060102-3 or 02070003-4
48	พีจี. คอนเนคเตอร์ 3 สลัก สำหรับสายอะลูมิเนียม 70-185 ต.มม. CONNECTOR, PARALLEL GROOVE, TRIPLE BOLT, Al, 70-185 mm^2	6	02300103
49	สลักเกลียว M 16x200 มม. สำหรับเสาคอนกรีต 12.00 ม. BOLT, MACHINE, M 16x200 mm FOR 12.00 m CONCRETE POLE	2	01110202
	สลักเกลียว M 16x250 มม. สำหรับเสาคอนกรีต 12.20 ม. และ 14.00 ม. BOLT, MACHINE, M 16x250 mm FOR 12.20 m AND 14.00 m CONCRETE POLE		01110203
	สลักเกลียว M 16x300 มม. สำหรับเสาคอนกรีต 14.30 ม. BOLT, MACHINE, M 16x300 mm FOR 14.30 m CONCRETE POLE		01110204
50	แหวนสี่เหลี่ยมแบน 52x52x4.5 มม. รู ø 18 มม. มอก. 258 WASHER, SQUARE, FLAT, 52x52x4.5 mm, HOLE ø18 mm, TIS 258	2	01180100

กองวิศวกรรมไฟฟ้าและเครื่องกล
ฝ่ายวิศวกรรม

การไฟฟ้าส่วนภูมิภาค

ใช้แทนแบบ ....
ถูกแทนโดยแบบ ....
เขียนเสร็จวันที่ 26 ก.พ. 2542

ผู้เขียน
ผู้สำรวจ
วิศวกร
หัวหน้าแผนก
ผู้อำนวยการกอง
ผู้อำนวยการฝ่าย

ผู้ว่าการ ....

30 เม.ย. 2542

แก้แบบวันที่ ....
มิติเป็น ....
มาตราส่วน ....

การติดตั้งสวิตช์เปิดได้เมื่อมีโหลดชนิด SF_6
สามารถใช้การควบคุมระยะไกล 33 kV 400 A
ผลิตภัณฑ์ G&W U.S.A. ทำโดย PRECISE

รองผู้ว่าการเทคนิคและบริการ
....

SWITCH SF_6, LOAD BREAK, REMOTE CONTROLLED
33 kV 400 A INSTALLATION
TRADE-MARK : **G&W U.S.A.**
MANUFACTURED BY **PRECISE**

แบบเลขที่ SA4-015/42006
แผ่นที่ 8 ของจำนวน 10 แผ่น

30 เม.ย. 2542

การประกอบเลขที่ ASSEMBLY NO.	3421

บัญชีวัสดุ
BILL OF MATERIAL

ลำดับที่ ITEM	รายละเอียด DESCRIPTION	จำนวน REQ'D I	 II	 III	วัสดุเลขที่ MAT. NO.
G	**สำหรับการติดตั้งสายล่อฟ้า FOR OHGW INSTALLATION**				
51	เหล็กฉากรับสายล่อฟ้าทางตรง OVERHEAD GROUND WIRE BAYONET	1	–	–	01010003
52	เหล็กรูปรางน้ำรับสายล่อฟ้า ต้นเข้าปลายสาย OVERHEAD GROUND WIRE DEADEND BAYONET, CHANNEL STEEL	–	1	1	01000100
53	สลักเกลียว M 16x250 มม. สำหรับเสาคอนกรีต 12, 12.20 ม. และ 14.00 ม. BOLT, MACHINE, M 16x250 mm FOR 12, 12.20 m AND 14.00 m CONCRETE POLE	2	–	2	01110203
	สลักเกลียว M 16x300 มม. สำหรับเสาคอนกรีต 14.30 ม. BOLT, MACHINE, M 16x300 mm FOR 14.30 m CONCRETE POLE				01110204
54	สลักเกลียว M 16x350 มม. สำหรับเสาคอนกรีต 12, 12.20 ม. และ 14.00 ม. BOLT, MACHINE, M 16x350 mm FOR 12, 12.20 m AND 14.00 m CONCRETE POLE	–	2	–	01110205
	สลักเกลียว M 16x400 มม. สำหรับเสาคอนกรีต 14.30 ม. BOLT, MACHINE, M 16x400 mm FOR 14.30 m CONCRETE POLE				01110206
55	สลักห่วงกลม M 16x200 มม. BOLT, ROUND EYE M 16x200 mm	–	–	1	01140201
56	นัทรูปห่วง. M 16 DIN 582 NUT, EYE, M 16 DIN 582	–	–	1	01180001
57	แหวนสี่เหลี่ยมแบน 52x52x4.5 มม. รู Ø 18 มม. มอก. 258 WASHER, SQUARE, FLAT, 52x52x4.5 mm, HOLE Ø 18 mm, TIS 258	2	2	4	01180100
58	กราวด์วายร์แคล้มป์ แบบ J 1152 GROUND WIRE CLAMP, J 1152	1	1	–	01230205
59	กายทิมเบิล สำหรับสายยึดโยง 50-95 ต.มม. THIMBLE, GUY, FOR STEEL WIRE 50-95 mm²	–	–	2	01210304
60	ยูแคล้มป์ สลักเกลียว 1 ตัว M 8 CLAMP, SINGLE U-BOLT, M 8	1	1	7	01230000

อติวิทย์ ทองลา พชง.3 ผปร. กฟส.อล. กฟจ.กบ. กฟต.2 (ต) ผวก. @PEA

กองวิศวกรรมไฟฟ้าและเครื่องกล
ฝ่ายวิศวกรรม

การไฟฟ้าส่วนภูมิภาค

ผู้เขียน ....
ผู้สำรวจ ....
วิศวกร ....
หัวหน้าแผนก ....
ผู้อำนวยการกอง ....
ผู้อำนวยการฝ่าย ....
รองผู้ว่าการเทคนิคและบริการ
....

ผู้ว่าการ 30 เม.ย. 2542

การติดตั้งสวิตช์เปิดโดเมื่อมีโหลดชนิด SF6
สามารถใช้การควบคุมระยะไกล 33 kV 400 A
ผลิตภัณฑ์ G&W U.S.A. ทำโดย PRECISE

SWITCH SF6, LOAD BREAK, REMOTE CONTROLLED
33 kV 400 A INSTALLATION
TRADE-MARK : **G&W U.S.A.**
MANUFACTURED BY **PRECISE**

ใช้แทนแบบ ....
ถูกแทนโดยแบบ ....
เขียนเสร็จวันที่ 26 ก.พ. 2542
แก้แบบวันที่ ....
มิติเป็น ....
มาตราส่วน ....

แบบเลขที่ SA4-015/42006
แผ่นที่ 9 ของจำนวน 10 แผ่น

3 0 เม.ย. 2542