
การประกอบเลขที่ ASSEMBLY NO. 5212A

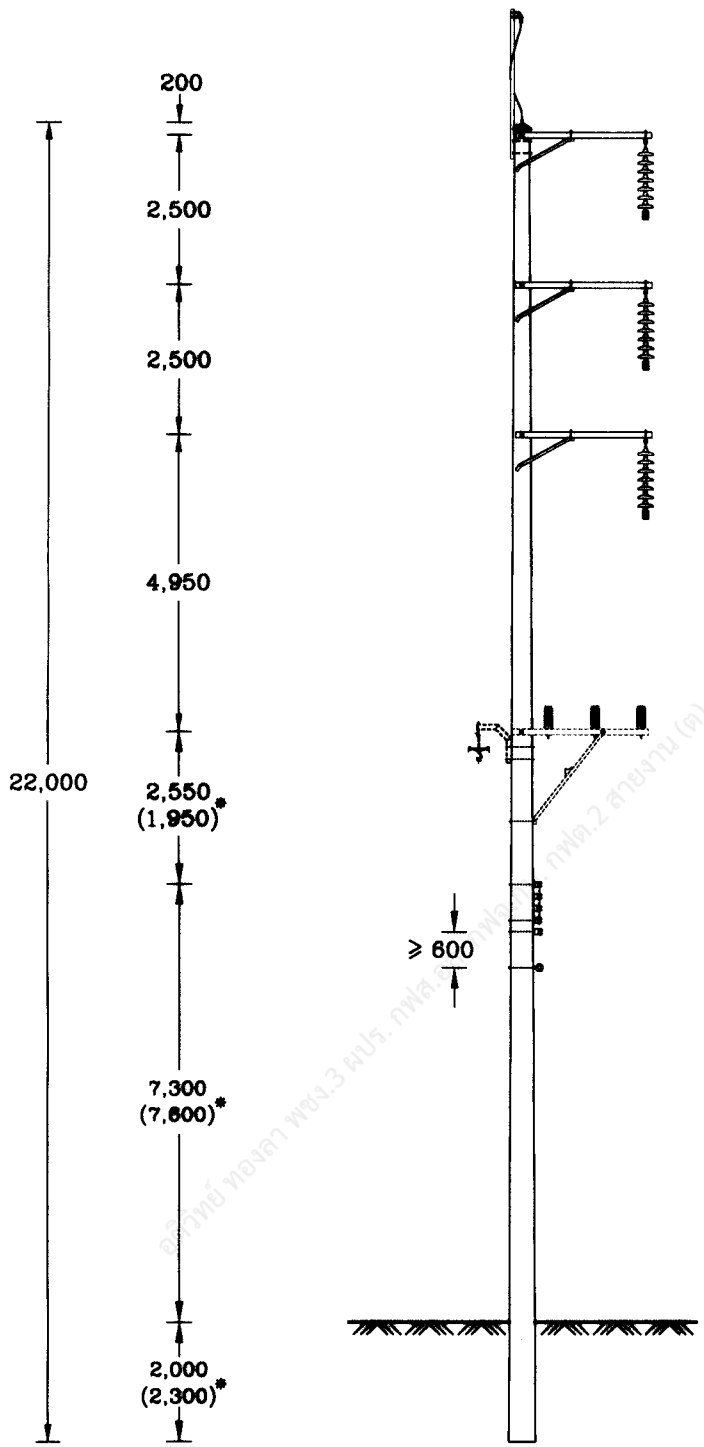


* ดูหมายเหตุ SEE NOTE 1

กองมาตรฐานระบบไฟฟ้า ฝ่ายมาตรฐานและความปลอดภัย	**การไฟฟ้าส่วนภูมิภาค**	ใช้แทนแบบ ..... ถูกแทนโดยแบบ .....
ผู้เขียน ...สมชาย..... ผู้สำรวจ ..... วิศวกร ..... หัวหน้าแผนก ..... ผู้อำนวยการกอง ..... ผู้อำนวยการฝ่าย	ผู้ว่าการ ..... - 4 ก.ค. 2548	เขียนเสร็จวันที่ 3 มิ.ค. 2548 แก้แบบวันที่ ..... มิติเป็น มิลลิเมตร มาตราส่วน 1:125
รองผู้ว่าการฝ่ายวางแผนและพัฒนาระบบไฟฟ้า	115 kV วงจรเดี่ยว สายไฟฟ้าเดี่ยว เสา คอร. (ยนิดมีกราวด์เพลทในเสา) สำหรับทางตรง แบบ SS-TG-2 115 kV SINGLE CIRCUIT SINGLE CONDUCTOR CONCRETE POLE (WITH GROUND PLATE IN POLE), TANGENT STRUCTURE TYPE SS-TG-2	แบบเลขที่ SA1-015/48002 แผ่นที่ 1 ของจำนวน 3 แผ่น

- 4 ก.ค. 2548

การประกอบเลขที่ ASSEMBLY NO. 5212A

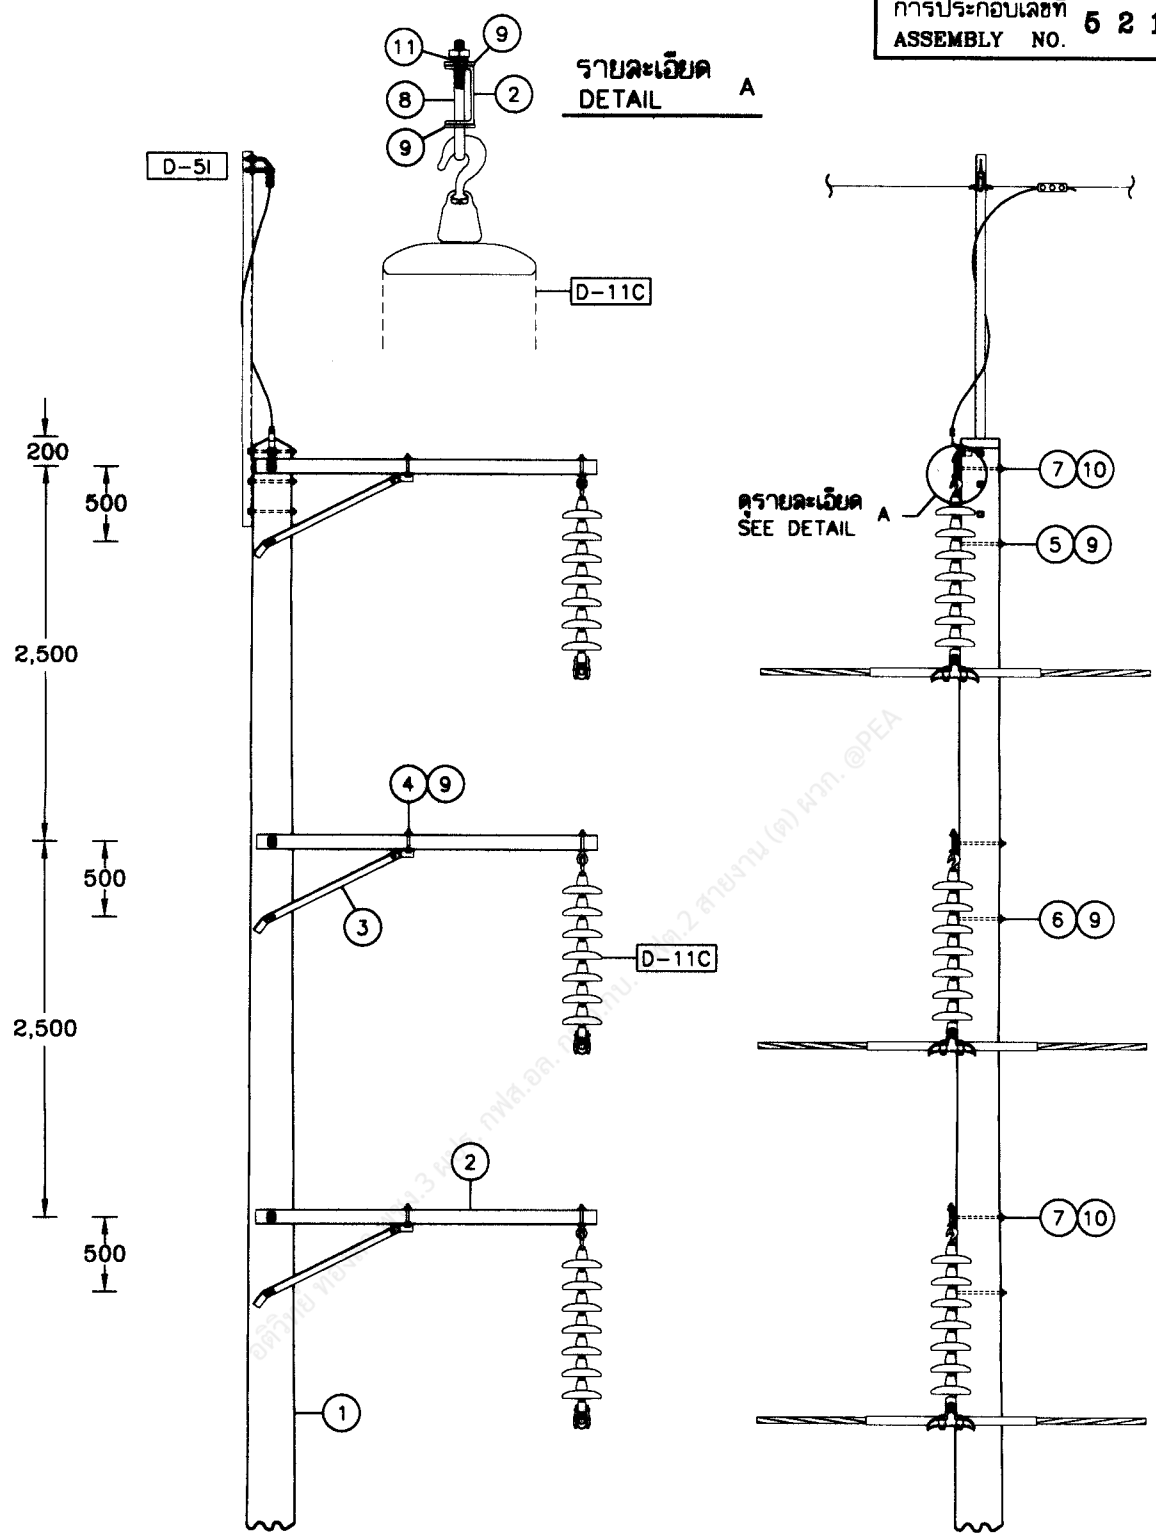

กองมาตรฐานระบบไฟฟ้า ฝ่ายมาตรฐานและความปลอดภัย	**การไฟฟ้าส่วนภูมิภาค**	ใช้แทนแบบ ..... ถูกแทนโดยแบบ .....
ผู้เขียน สมชาย ผู้สำรวจ ..... วิศวกร ..... หัวหน้าแผนก ..... ผู้อำนวยการกอง ..... ผู้อำนวยการฝ่าย	ผู้ว่าการ ..... - 4 ก.ค. 2548	เขียนเสร็จวันที่ 3 มี.ค. 2548 แก้แบบวันที่ ..... มิติเป็น มิลลิเมตร มาตราส่วน 1:50
รองผู้ว่าการฝ่ายวางแผนและพัฒนาระบบไฟฟ้า	115 kV วงจรเดี่ยว สายไฟฟ้าเดี่ยว เสา คอร. (ชนิดมีกราวด์เพลทในเสา) สำหรับทางตรง แบบ SS-TG-2 115 kV SINGLE CIRCUIT SINGLE CONDUCTOR CONCRETE POLE (WITH GROUND PLATE IN POLE), TANGENT STRUCTURE TYPE SS-TG-2	แบบเลขที่ SA1-015/48002 แผ่นที่ 2 ของจำนวน 3 แผ่น

- 4 ก.ค. 2548

การประกอบเลขที่ ASSEMBLY NO. 5212A

บัญชีวัสดุ
BILL OF MATERIAL

ลำดับที่ ITEM	รายละเอียด DESCRIPTION	จำนวน REQ,D	วัสดุเลขที่ MAT. NO.
1	เสา คอร. ยาว 22.00 ม. ชนิดมีกราวด์เพลทในเสา POLE, CONCRETE, 22.00 m LONG, WITH GROUND PLATE IN POLE	1	00010015
2	เหล็กรูปรางน้ำ ขนาด 100x50x5 มม. ยาว 2,250 มม. มอก. 1227 STEEL CHANNEL, 100x50x5 mm, 2,250 mm LONG, TIS 1227	3	01000100
3	เหล็กประกับคอนสายแบบทางแขน ขนาด 50x50x6 มม. ยาว 1,000 มม. BRACE, ALLEY ARM, 50x50x6 mm, 1,000 mm LONG	3	01200009
4	สลักเกลียว M 16x130 มม. BOLT, MACHINE, M 16x130 mm	3	01110200
5	สลักเกลียว M 16x300 มม. BOLT, MACHINE, M 16x300 mm	1	01110204
6	สลักเกลียว M 16x350 มม. BOLT, MACHINE, M 16x350 mm	2	01110205
7	สลักเกลียว M 20x350 มม. BOLT, MACHINE, M 20x350 mm	3	01110300
8	สลักทางโอแวล M 16x150 มม. BOLT, OVAL EYE, M 16x150 mm	3	01150000
9	แหวนสี่เหลี่ยมแบน 52x52x4.5 มม. รู ø18 มม. มอก.258 WASHER, SQUARE, FLAT 52x52x4.5 mm, HOLE ø 18 mm, TIS 258	12	01180100
10	แหวนสี่เหลี่ยมแบน 62x62x6 มม. รู ø22 มม. มอก.258 WASHER, SQUARE, FLAT 62x62x6 mm, HOLE ø 22 mm, TIS 258	6	01180101
11	แหวนสปริง M 16 มอก. 259 WASHER, LOCK, M 16, TIS 259	3	01180301

รายละเอียด
DETAIL

D-11C	การประกอบลูกถ้วยแขวน SUSPENSION INSULATOR ASSEMBLY	3	
D-5I	การประกอบสายลอฟ้า OVERHEAD GROUND WIRE ASSEMBLY	1	
D-10A	ฐานรากเสา POLE FOUNDATION	1	
D-25	การต่อลงดิน GROUNDING	1	

หมายเหตุ

1.* กรณีก่อสร้างในพื้นที่เขตทางหลวง ให้ใช้ค่าระยะห่างตามแนวดิ่งในวงเล็บ โดยดูรายละเอียดเพิ่มเติมในแบบเลขที่ SA1-015/43012 (การประกอบเลขที่ 5687)

2. ระยะห่างระหว่างช่วงเสาของโครงสร้างสายส่ง 115 kV ให้ดูแบบเลขที่ SA1-015/48001 (การประกอบเลขที่ 5151)

NOTES

1.* IN CASE OF CONSTRUCTING IN HIGHWAY AREA, USE THE VERTICAL CLEARANCE IN THE PARENTHESIS. FOR ADDITIONAL DETAIL, SEE DWG NO. SA1-015/43012 (ASSEMBLY NO. 5687) .

2. SPAN LENGTHS FOR 115 kV CONSTRUCTION STRUCTURE, SEE DWG. NO. SA1-015/48001 (ASSEMBLY NO. 5151) .

กองมาตรฐานระบบไฟฟ้า ฝ่ายมาตรฐานและความปลอดภัย	การไฟฟ้าส่วนภูมิภาค	ใช้แทนแบบ ..... ถูกแทนโดยแบบ .....
ผู้เขียน ...สมชาย..... ผู้สำรวจ ..... วิศวกร ..... หัวหน้าแผนก ..... ผู้อำนวยการกอง ..... ผู้อำนวยการฝ่าย	ผู้ว่าการ ... - 4 ก.ค. 2548	เขียนเสร็จวันที่ 3 มี.ค. 2548 แก้แบบวันที่ ..... มิติเป็น ..... มาตราส่วน .....
	115 kV วงจรเดี่ยว สายไฟฟ้าเดี่ยว เสา คอร. (ชนิดมีกราวด์เพลทในเสา) สำหรับทางตรง แบบ SS-TG-2	
รองผู้ว่าการฝ่ายวางแผนและพัฒนาระบบไฟฟ้า	115 kV SINGLE CIRCUIT SINGLE CONDUCTOR CONCRETE POLE (WITH GROUND PLATE IN POLE), TANGENT STRUCTURE TYPE SS-TG-2	แบบเลขที่ SA1-015/48002 แผ่นที่ 3 ของจำนวน 3 แผ่น

- 4 ก.ค. 2548