
การประกอบเลขที่
ASSEMBLY NO. 5213A

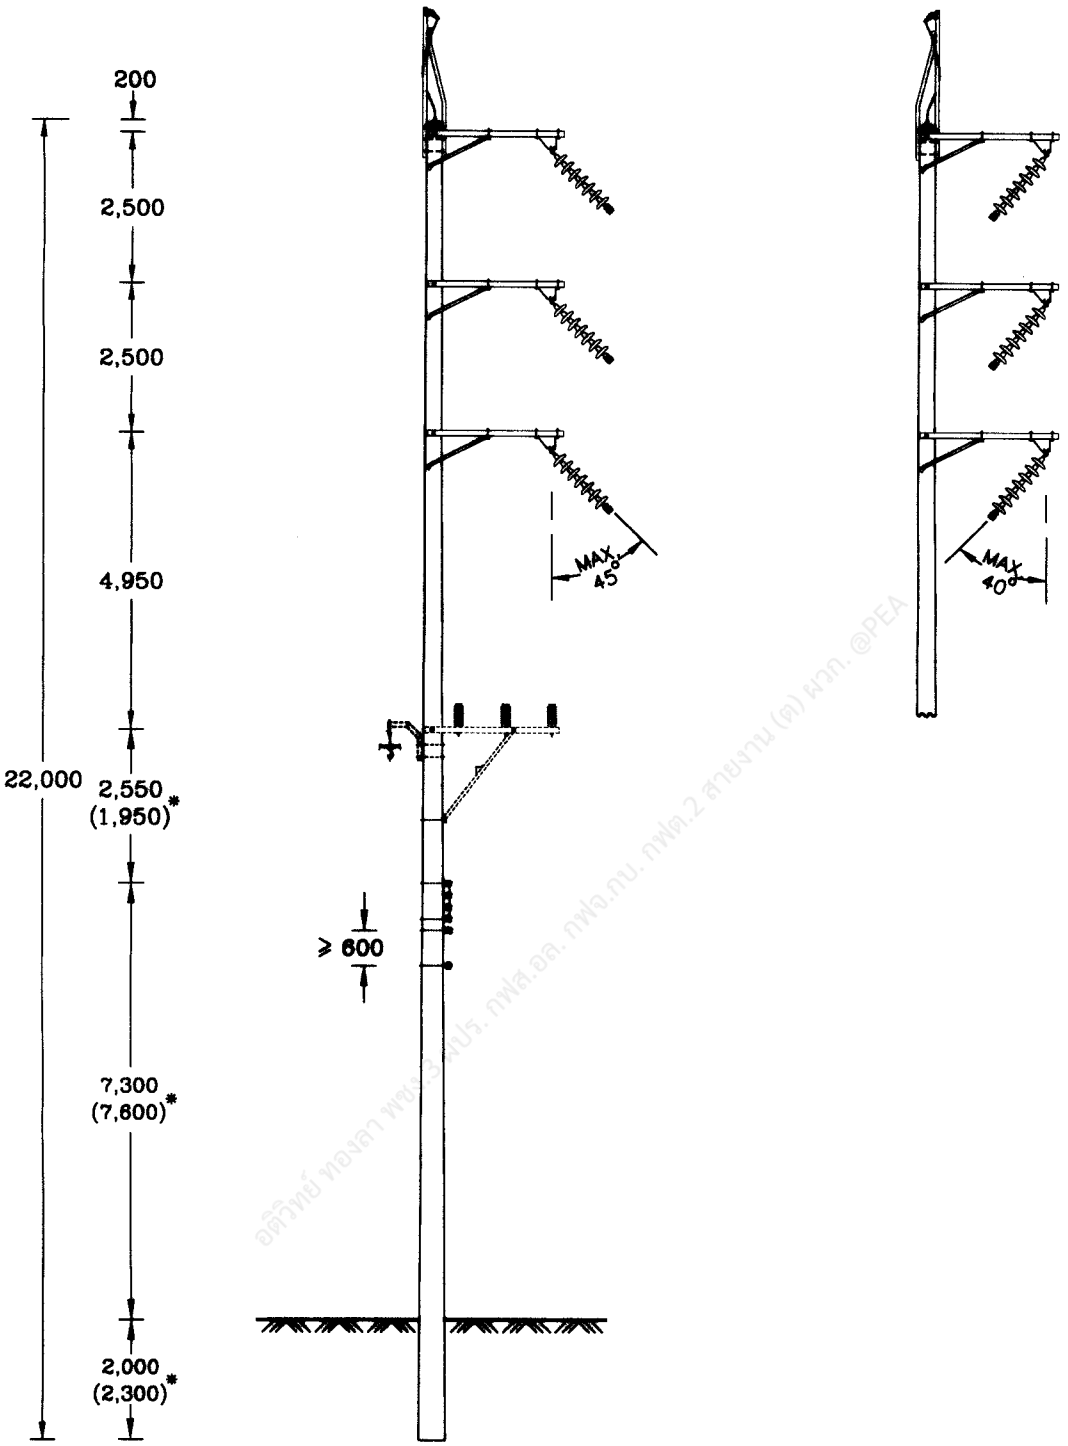


* ดูหมายเหตุ SEE NOTE 1

กองมาตรฐานระบบไฟฟ้า ฝ่ายมาตรฐานและความปลอดภัย	**การไฟฟ้าส่วนภูมิภาค**	ใช้แทนแบบ ..... ถูกแทนโดยแบบ .....
ผู้เขียน สมชาย ผู้สำรวจ ..... วิศวกร ..... หัวหน้าแผนก ..... ผู้อำนวยการกอง ..... ผู้อำนวยการฝ่าย	ผู้ว่าการ ..... - 4 ก.ค. 2548	เขียนเสร็จวันที่ 3 มี.ค. 2548 แก้แบบวันที่ ..... มิติเป็น มิลลิเมตร มาตราส่วน 1:125
รองผู้ว่าการฝ่ายวางแผนและพัฒนาระบบไฟฟ้า	115 kV วงจรเดี่ยว สายไฟฟ้าเดี่ยว เสา คอร. (ชนิดมีกราวด์เพลทในเสา) สำหรับทางโค้ง แบบ SS-SA-2 115 kV SINGLE CIRCUIT SINGLE CONDUCTOR CONCRETE POLE (WITH GROUND PLATE IN POLE), ANGLE STRUCTURE TYPE SS-SA-2	แบบเลขที่ SA1-015/48003 แผ่นที่ 1 ของจำนวน 3 แผ่น

- 4 ก.ค. 2548

การประกอบเลขที่ ASSEMBLY NO. 5213A

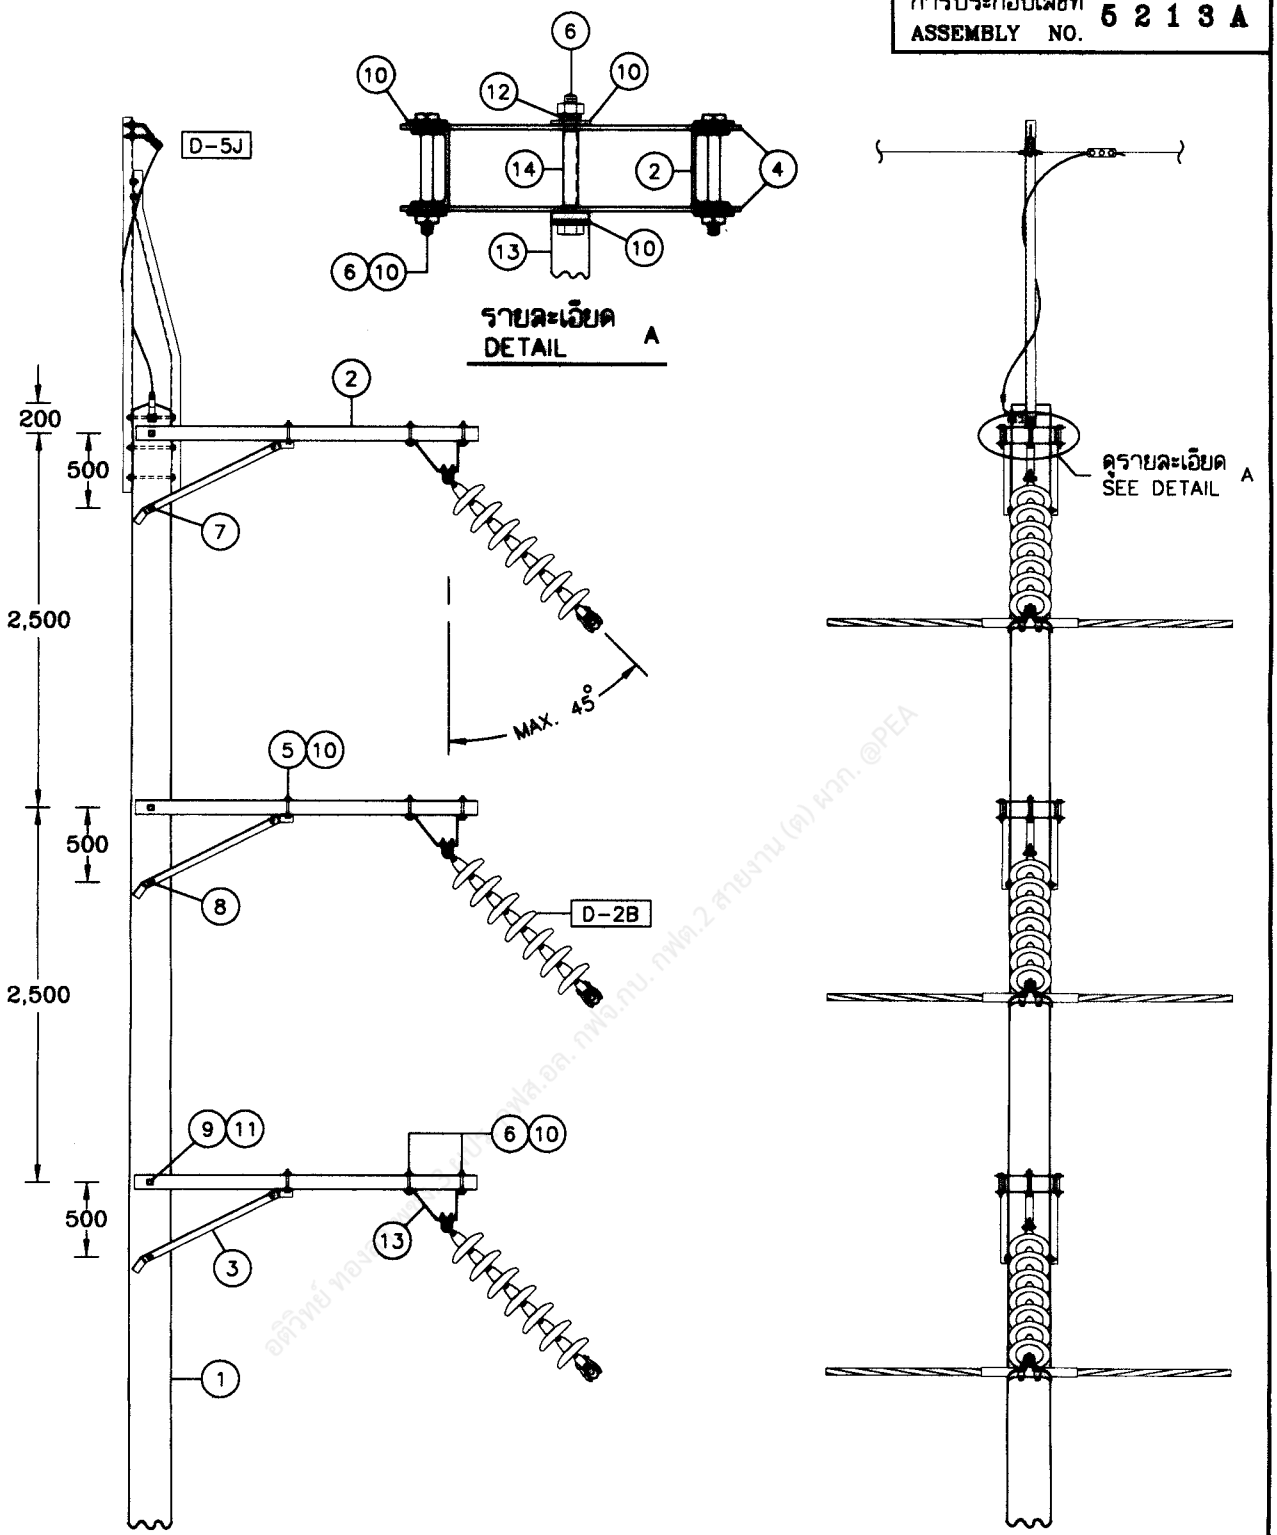

กองมาตรฐานระบบไฟฟ้า
ฝ่ายมาตรฐานและความปลอดภัย

การไฟฟ้าส่วนภูมิภาค

ใช้แทนแบบ .....
ถูกแทนโดยแบบ .....

ผู้เขียน ...สมชาย.....
ผู้สำรวจ .....
วิศวกร .....
หัวหน้าแผนก .....
ผู้อำนวยการกอง .....
ผู้อำนวยการฝ่าย .....

ผู้ว่าการ ... - 4 ก.ค. 2548

เขียนเสร็จวันที่ 3 มี.ค. 2548
แก้แบบวันที่ .....
มิติเป็น ..มิลลิเมตร.....
มาตราส่วน ...1:50.....

รองผู้ว่าการฝ่ายวางแผนและพัฒนาระบบไฟฟ้า
.....

115 kV วงจรเดี่ยว สายไฟฟ้าเดี่ยว
เสา คอร. (ชนิดมีกราวด์เพลทในเสา) สำหรับทางโค้ง
แบบ SS-SA-2

115 kV SINGLE CIRCUIT SINGLE CONDUCTOR
CONCRETE POLE (WITH GROUND PLATE IN POLE), ANGLE STRUCTURE
TYPE SS-SA-2

แบบเลขที่ SA1-015/48003
แผ่นที่ 2 ของจำนวน 3 แผ่น

- 4 ก.ค. 2548

การประกอบเลขที่ ASSEMBLY NO. **5213A**

บัญชีวัสดุ
BILL OF MATERIAL

ลำดับที่ ITEM	รายละเอียด DESCRIPTION	จำนวน REQ,D	วัสดุเลขที่ MAT. NO.
1	เสา คอร. ยาว 22.00 ม. ชนิดมีกราวด์เพลทในเสา POLE, CONCRETE 22.00 m LONG, WITH GROUND PLATE IN POLE	1	00010015
2	เหล็กรูปรางน้ำ ขนาด 100x50x5 มม. ยาว 2,250 มม. มอก. 1227 STEEL CHANNEL, 100x50x5 mm, 2,250 mm LONG, TIS 1227	6	01000100
3	เหล็กประกับคอนสายแบบทางแขน ขนาด 50x50x6 มม. ยาว 1,000 มม. BRACE, ALLEY ARM 50x50x6 mm, 1,000 mm LONG	6	01200009
4	แผ่นเหล็ก ขนาด 6x100x450 มม. PLATE, STEEL 6x100x450 mm	12	01030002
5	สลักเกลียว M 16x130 มม. BOLT, MACHINE, M 16x130 mm	6	01110200
6	สลักเกลียว M 16x170 มม. BOLT, MACHINE, M 16x170 mm	18	01110201
7	สลักเกลียว M 16x300 มม. BOLT, MACHINE, M 16x300 mm	1	01110204
8	สลักเกลียว M 16x350 มม. BOLT, MACHINE, M 16x350 mm	2	01110205
9	สลักเกลียว M 20x350 มม. BOLT, MACHINE, M 20x350 mm	3	01110300
10	แหวนสี่เหลี่ยมแบน 52x52x4.5 มม. รู ø18 มม. มอก.258 WASHER, SQUARE, FLAT 52x52x4.5 mm, HOLE ø 18 mm, TIS 258	42	01180100
11	แหวนสี่เหลี่ยมแบน 62x62x6 มม. รู ø22 มม. มอก.258 WASHER, SQUARE, FLAT 62x62x6 mm, HOLE ø 22 mm, TIS 258	6	01180101
12	แหวนสปริง M 16 มอก. 258 WASHER, LOCK, M 16, TIS 259	6	01180301
13	ที่แขวนลูกถ้วยทางโค้ง BRACKET, CORNER SUSPENSION	3	03140012
14	ท่อเหล็ก ขนาดระบุ 20 ยาว 100 มม. มอก.277 ประเภทที่ 2 แต่ไม่มีเกลียวที่ปลาย PIPE, STEEL, SIZE 20, 100 mm LONG, TIS 277, TYPE 2, BUT WITHOUT THREADED END	6	01050000
	รายละเอียด DETAIL		
D-2B	การประกอบลูกถ้วยแขวน SUSPENSION INSULATOR ASSEMBLY	3	
D-5J	การประกอบสายลอฟ้า OVERHEAD GROUND WIRE ASSEMBLY	1	
D-10A	ฐานรากเสา POLE FOUNDATION	1	
D-25	การต่อลงดิน GROUNDING	1	

หมายเหตุ 1.* กรณีก่อสร้างในพื้นที่เขตทางหลวง ให้ใช้ค่าระยะห่างตามแนวดิ่งในวงเล็บ โดยดูรายละเอียดเพิ่มเติมในแบบเลขที่ SA1-015/43012 (การประกอบเลขที่ 5687)

2. ระยะห่างระหว่างช่วงเสาของโครงสร้างสายส่ง 115 kV ให้ดูแบบเลขที่ SA1-015/48001 (การประกอบเลขที่ 5151)

NOTES 1.* IN CASE OF CONSTRUCTING IN HIGHWAY AREA, USE THE VERTICAL CLEARANCE IN THE PARENTHESIS. FOR ADDITIONAL DETAIL, SEE DWG NO. SA1-015/43012 (ASSEMBLY NO. 5687).

2. SPAN LENGTHS FOR 115 kV CONSTRUCTION STRUCTURE, SEE DWG. NO. SA1-015/48001 (ASSEMBLY NO. 5151).

กองมาตรฐานระบบไฟฟ้า ฝ่ายมาตรฐานและความปลอดภัย	**การไฟฟ้าส่วนภูมิภาค**	ใช้แทนแบบ ..... ถูกแทนโดยแบบ .....
ผู้เขียน ...สมชาย..... ผู้สำรวจ ..... วิศวกร ..... หัวหน้าแผนก ..... ผู้อำนวยการกอง ..... ผู้อำนวยการฝ่าย	ผู้ว่าการ ..... - 4 ก.ค. 2548	เขียนเสร็จวันที่ 3 มี.ค. 2548 แก้แบบวันที่ ..... มิติเป็น ..... มาตราส่วน .....
	115 kV วงจรเดี่ยว สายไฟฟ้าเดี่ยว เสา คอร. (ชนิดมีกราวด์เพลทในเสา) สำหรับทางโค้ง แบบ SS-SA-2	
รองผู้ว่าการฝ่ายวางแผนและพัฒนาระบบไฟฟ้า	115 kV SINGLE CIRCUIT SINGLE CONDUCTOR CONCRETE POLE (WITH GROUND PLATE IN POLE), ANGLE STRUCTURE TYPE SS-SA-2	แบบเลขที่ SA1-015/48003 แผ่นที่ 3 ของจำนวน 3 แผ่น

- 4 ก.ค. 2548