การประกอบเลขที่ ASSEMBLY NO. 5304

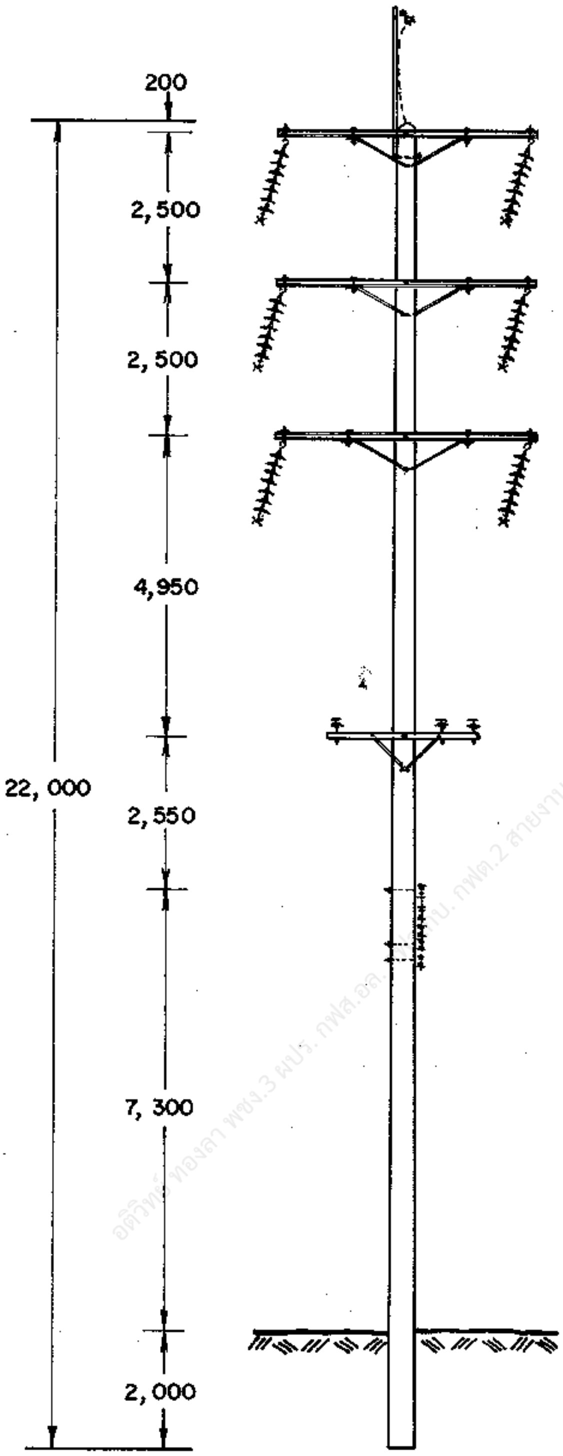

อติวิทย์ ทองลา พชง.3 ผปร. กฟส.ฉล. กฟต.2 สายงาน (ต) ผวก. @PEA

กองวิศวกรรมไฟฟ้าและเครื่องกล
ฝ่ายวิศวกรรม

ผู้เขียน ______
ผู้สำรวจ ______
วิศวกร ______
หัวหน้าแผนก ______
ผู้อำนวยการกอง ______
ผู้อำนวยการฝ่าย ______

รองผู้ว่าการฝ่ายเทคนิค ______

การไฟฟ้าส่วนภูมิภาค

ผู้ว่าการ ______

5 ส.ค. 2537

115 kV วงจรคู่ สายไฟฟ้าเดี่ยว
เสาต้นทางตรง ก่อนเสาต้นเข้าปลายสาย
แบบ DS-TG-2

115 kV DOUBLE CIRCUIT SINGLE CONDUCTOR
TANGENT STRUCTURE ADJACENT TO DEADEND POLE
TYPE DS-TG-2

ใช้แทนแบบ ______
ถูกแทนโดยแบบ ______
เขียนเสร็จวันที่ 15 ธค. 2536
แก้แบบวันที่ ______
มิติเป็น มิลลิเมตร
มาตราส่วน 1 : 125

แบบเลขที่ SAI-015/36010
แผ่นที่ 1 ของจำนวน 3 แผ่น

2536

การประกอบเลขที่ **5304**
ASSEMBLY NO.

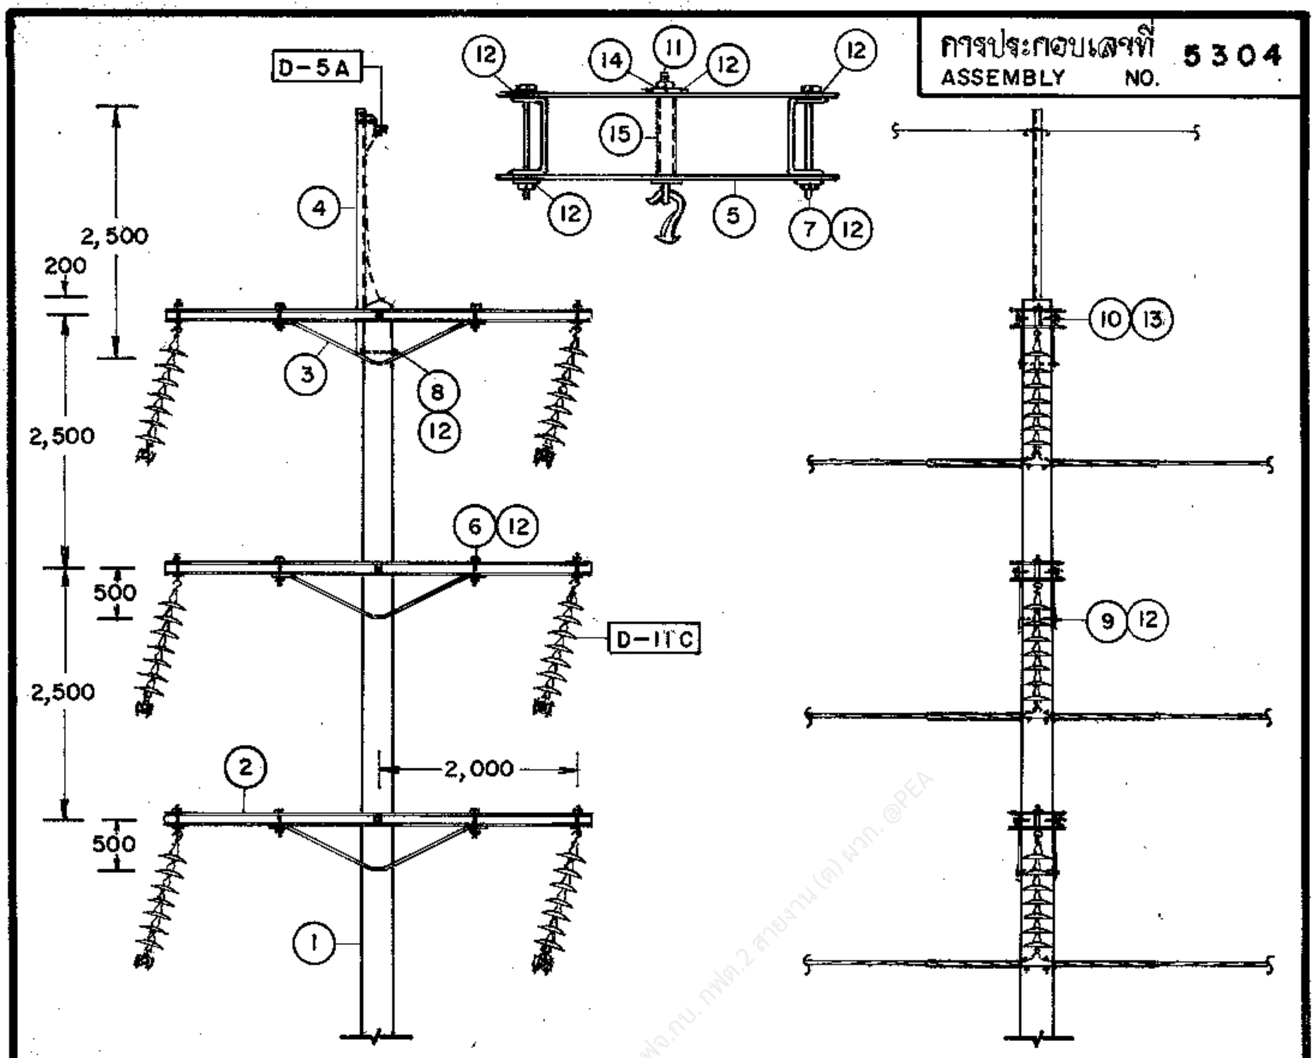

DS – TG – 2

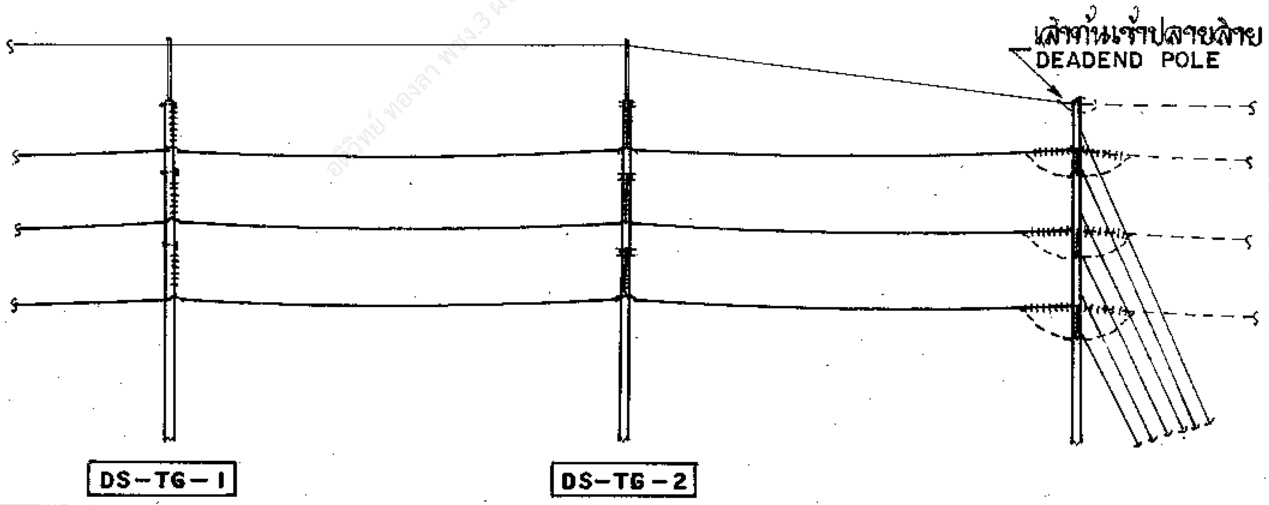

อภิทักษ์ ทองลา พชง.3 ผบร. กฟจ.กบ. กฟต.2 สายงาน (ต) ผวก. @PEA

กองวิศวกรรมไฟฟ้าและเครื่องกล ฝ่ายวิศวกรรม	การไฟฟ้าส่วนภูมิภาค	ใช้แทนแบบ ________
ผู้เขียน ________ ผู้สำรวจ ________ วิศวกร ________ หัวหน้าแผนก ________ ผู้อำนวยการกอง ________ ผู้อำนวยการฝ่าย ________	ผู้ว่าการ ________ 5 มี.ค. 2537	ถูกแทนโดยแบบ ________ เขียนเสร็จวันที่ 15 ธค. 2536 แก้แบบวันที่ ________ มิติเป็น มิลลิเมตร มาตราส่วน 1 : 75
	115 kV วงจรคู่ สายไฟฟ้าเดี่ยว เสาต้นทางตรง ก่อนเสาต้นเข้าปลายสาย แบบ DS-TG-2	
รองผู้ว่าการฝ่ายเทคนิค ________	115 kV DOUBLE CIRCUIT SINGLE CONDUCTOR TANGENT STRUCTURE ADJACENT TO DEADEND POLE TYPE DS–TG–2	แบบเลขที่ SAI-015/36010 แผ่นที่ 2 ของจำนวน 3 แผ่น

การประกอบเลขที่
ASSEMBLY NO. **5304**

บัญชีวัสดุ
BILL OF MATERIAL

ลำดับที่ ITEM	รายละเอียด DESCRIPTION	จำนวน REQ'D	วัสดุเลขที่ MAT. NO.
1	เสาคอนกรีต 22 ม. POLE, CONCRETE 22 m LONG	1	00010011 (0041)
2	คอนสายแบบเหล็กรูปรางน้ำ ขนาด 100X50X5 มม.ยาว 4.20 ม.มอก.116 CROSSARM, STEEL, CHANNEL 100X50X5 mm 4.20 m LONG TIS 116	6	
3	เหล็กฉากรับคอนสาย ขนาด 50X50X6 มม.ช่วงกว้าง 1,800 มม.ดรอพ450มม. BRACE, ANGLE STEEL, 50X50X 6 mm, 1,800 mm WIDE, 450 mm DROP	6	01200007 (0119)
4	เหล็กฉากรับสายล่อฟ้าทางตรง ยาว 2.50 ม. OVERHEAD GROUND WIRE BAYONET, 2.50 m LONG	1	01010004 (0135)
5	เหล็กแผ่น ขนาด 6X100X450 มม. PLATE, STEEL, 6X100X450 mm	12	01030002 (0143)
6	สลักเกลียว M 16X130 มม. BOLT, MACHINE, M 16X130 mm	12	01110200 (0220)
7	สลักเกลียว M 16X170 มม. BOLT, MACHINE, M 16X170 mm	12	01110201 (0221)
8	สลักเกลียว M 16X300 มม. BOLT, MACHINE, M 16X300 mm	2	01110204 (0224)
9	สลักเกลียว M 16X350 มม. BOLT, MACHINE, M 16X350 mm	3	01110205 (0225)
10	สลักเกลียว M 20X350 มม. BOLT, MACHINE, M 20X350 mm	3	01110300
11	สลักห่วงโอเวล M 16X150 มม. BOLT, OVAL EYE, M 16X150 mm	6	01150000 (0257)
12	แหวนสี่เหลี่ยมแบน 52X52X4.5 มม. รู Ø 18 มม. มอก. 258 WASHER, SQUARE, FLAT 52X52X4.5 mm, HOLE Ø 18 mm, TIS 258	53	01180100 (0355)
13	แหวนสี่เหลี่ยมแบน 62X62X6 มม. รู Ø 22 มม. มอก. 258 WASHER, SQUARE, FLAT 62X62X6 mm, HOLE Ø 22 mm, TIS 258	6	01180101 (0356)
14	แหวนสปริง M 16 มอก. 259 WASHER, LOCK, M 16, TIS 259	6	01180301 (0365)
15	ท่อเหล็ก ชื่อขนาด 20 มม. หนา 2.65 มม. ยาว 100 มม. มอก. 277 ประเภท 2 PIPE, IRON, DIA. 20 mm I.D., 2.65 mm THICKNESS, 100 mm LONG, TIS 277, TYPE 2	6	01050000 (0905)
D-11C	การประกอบลูกถ้วยแขวน SUSPENSION INSULATOR ASSEMBLY	6	
D-5A	การต่อสายล่อฟ้า OVERHEAD GROUND WIRE CONNECTION	1	
D-10A	ฐานรากเสา POLE FOUNDATION	1	

กองวิศวกรรมไฟฟ้าและเครื่องกล
ฝ่ายวิศวกรรม

ผู้เขียน
ผู้สำรวจ
วิศวกร
หัวหน้าแผนก
ผู้อำนวยการกอง
ผู้อำนวยการฝ่าย

รองผู้ว่าการฝ่ายเทคนิค

การไฟฟ้าส่วนภูมิภาค

ผู้ว่าการ
5 ส.ค. 2537

115 kV วงจรคู่ สายไฟฟ้าเดี่ยว
เสาต้นทางตรง ก่อนเสาต้นเข้าปลายสาย
แบบ DS-TG-2

115 kV DOUBLE CIRCUIT SINGLE CONDUCTOR
TANGENT STRUCTURE ADJACENT TO DEADEND POLE
TYPE DS-TG-2

ใช้แทนแบบ
ถูกแทนโดยแบบ
เขียนเสร็จวันที่ 15 ธค.2536
แก้แบบวันที่
มิติเป็น
มาตราส่วน

แบบเลขที่ SAI-015/36010
แผ่นที่ 3 ของจำนวน 3 แผ่น