การประกอบเลขที่ 2321 or
ASSEMBLY NO. 3906

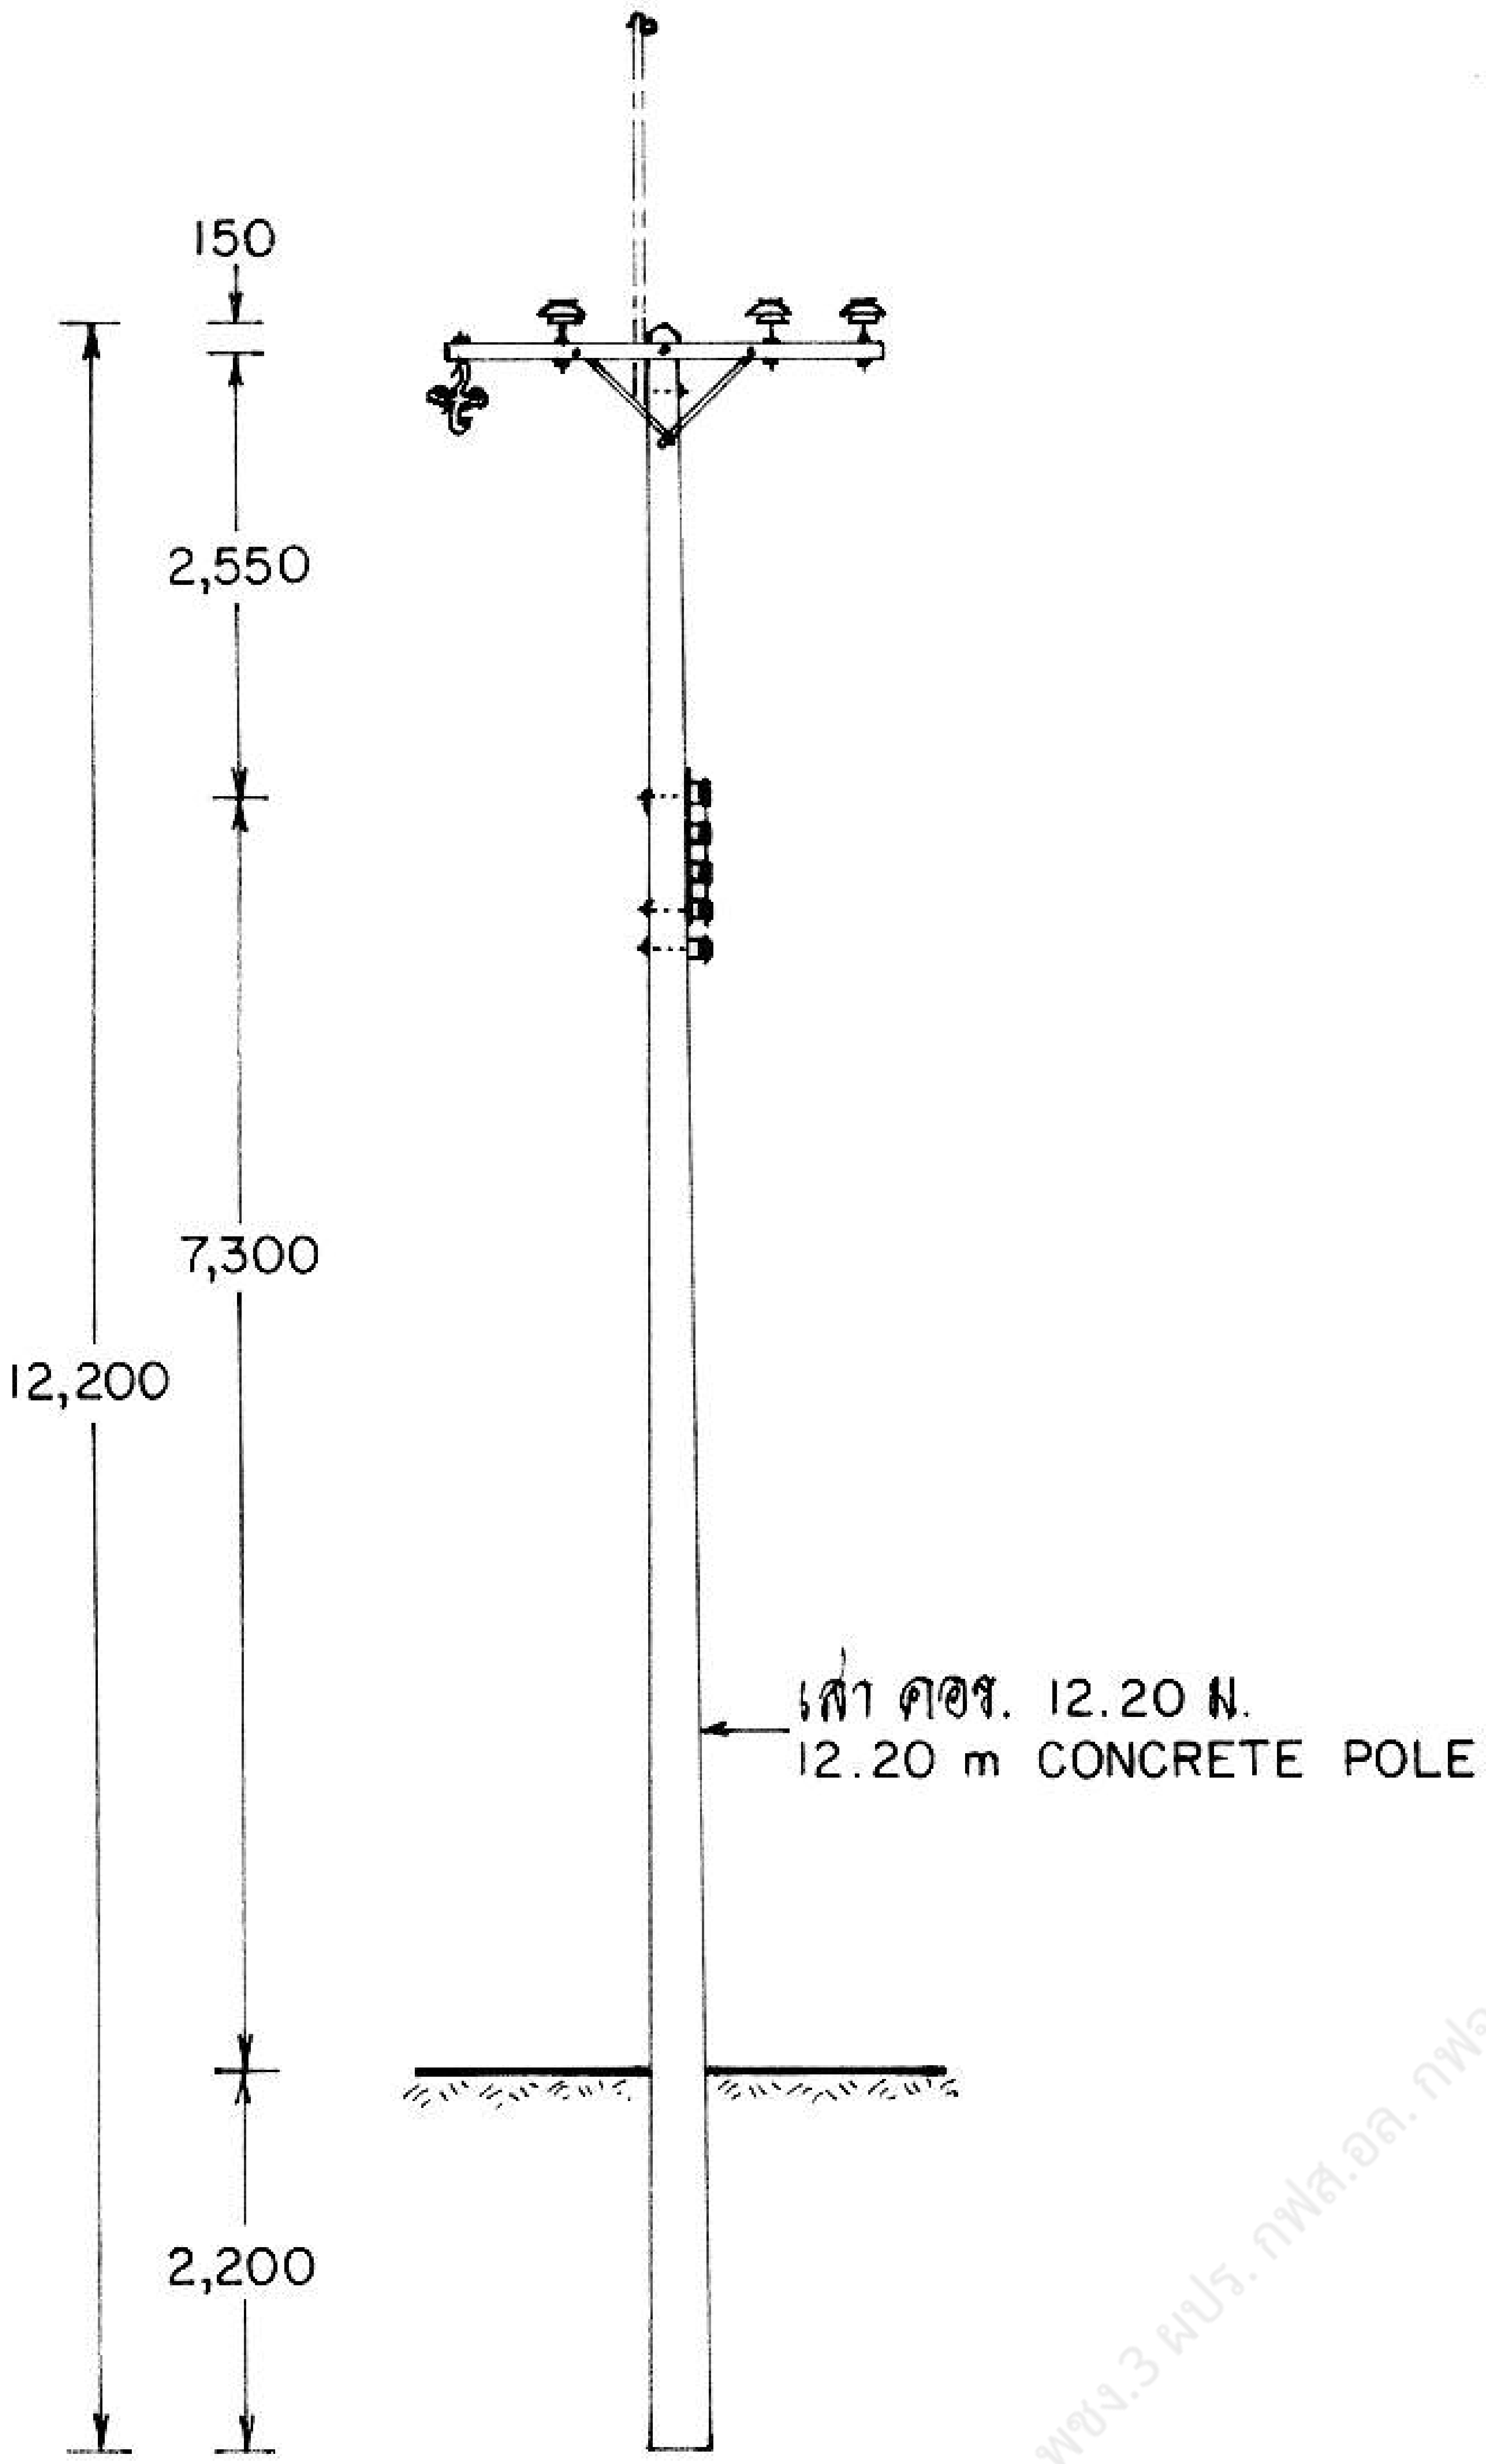

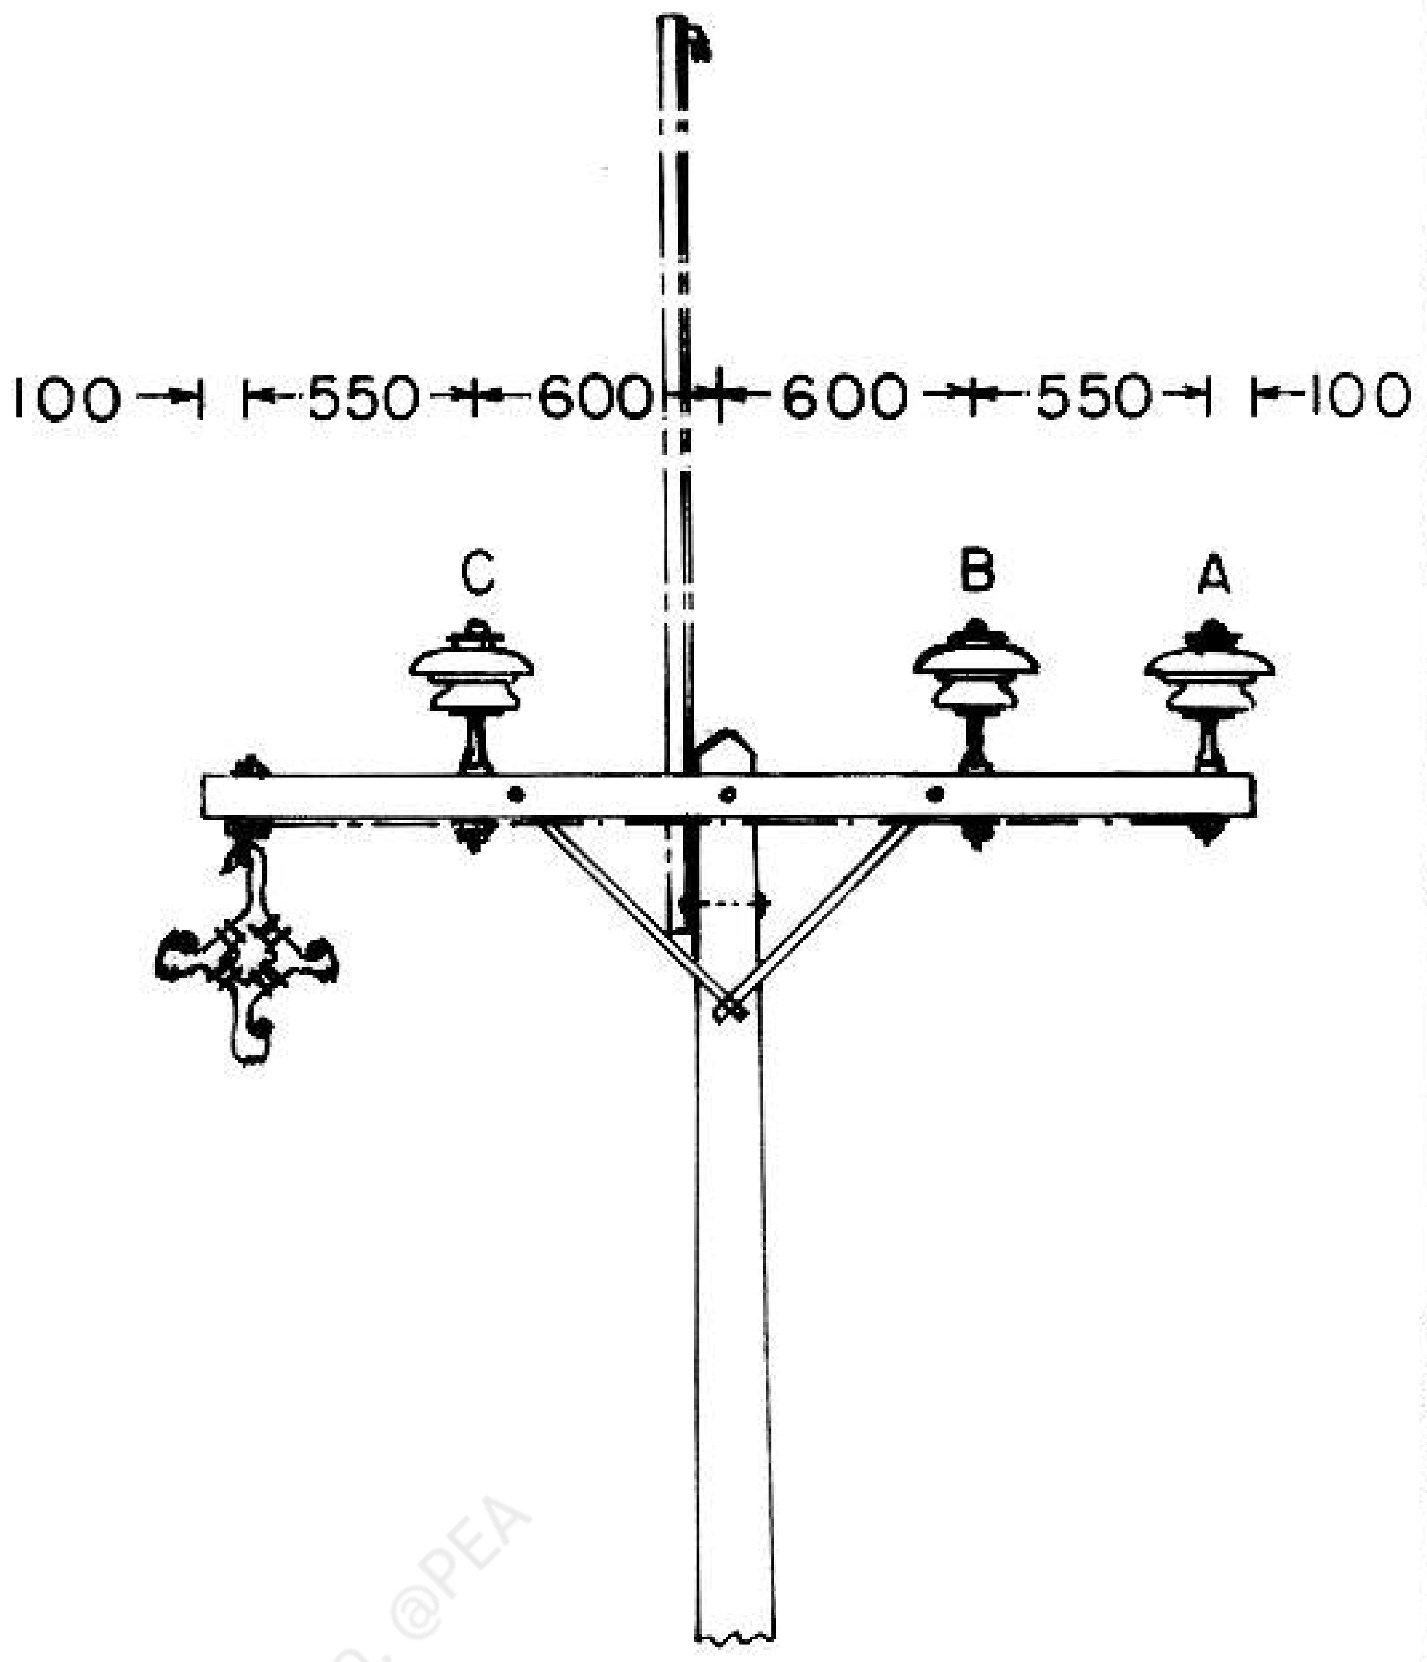

ข้อกำหนดการใช้งาน ระยะห่างระหว่างช่วงเสา และระยะหย่อนยานของสายที่มุมเบี่ยงเบนต่างๆ ดูรายละเอียดจากแบบเลขที่ IBI-015/37037 (การประกอบเลขที่ 8246)

THE RECOMMENDATION OF SPAN LENGTH AND SAG OF CONDUCTOR AT ANY LINE DEFLECTION ANGLE, SEE DETAIL IN DRAWING NO. IBI-015/37037 (ASSEMBLY NO. 8246)

อดิวิทย์ ทองลา พชง.3 ผปร. กฟส.อล. กฟจ. กฟต.2 สายงาน (ต) ผวก. @PEA

กองวิศวกรรมไฟฟ้าและเครื่องกล
ฝ่ายวิศวกรรม

ผู้เขียน
ผู้สำรวจ
วิศวกร
หัวหน้าแผนก
ผู้อำนวยการกอง
ผู้อำนวยการฝ่าย

รองผู้ว่าการฝ่ายเทคนิค

21 ต.ค. 2537

การไฟฟ้าส่วนภูมิภาค

ผู้ว่าการ 25.ต.ค.2537

การประกอบคอนกับเสาคอนกรีต 22kV, 33 kV
2 วงจร
(กรณีพาดสายหุ้มฉนวนแบบไม่เต็มพิกัด (PIC))

22 kV, 33 kV CROSSARM ASSEMBLY ON CONCRETE POLE
2 CIRCUIT
(PARTIALLY INSULATED CONDUCTOR STRINGING)

ใช้แทนแบบ
ถูกแทนโดยแบบ
เขียนเสร็จวันที่ 11 ต.ค. 37
แก้แบบวันที่
มิติเป็น มิลลิเมตร
มาตราส่วน 1:50, 1:100

แบบเลขที่ SA4-015/37026
แผ่นที่ 1 ของจำนวน 9 แผ่น

การประกอบเลขที่	2321 or
ASSEMBLY NO.	3906

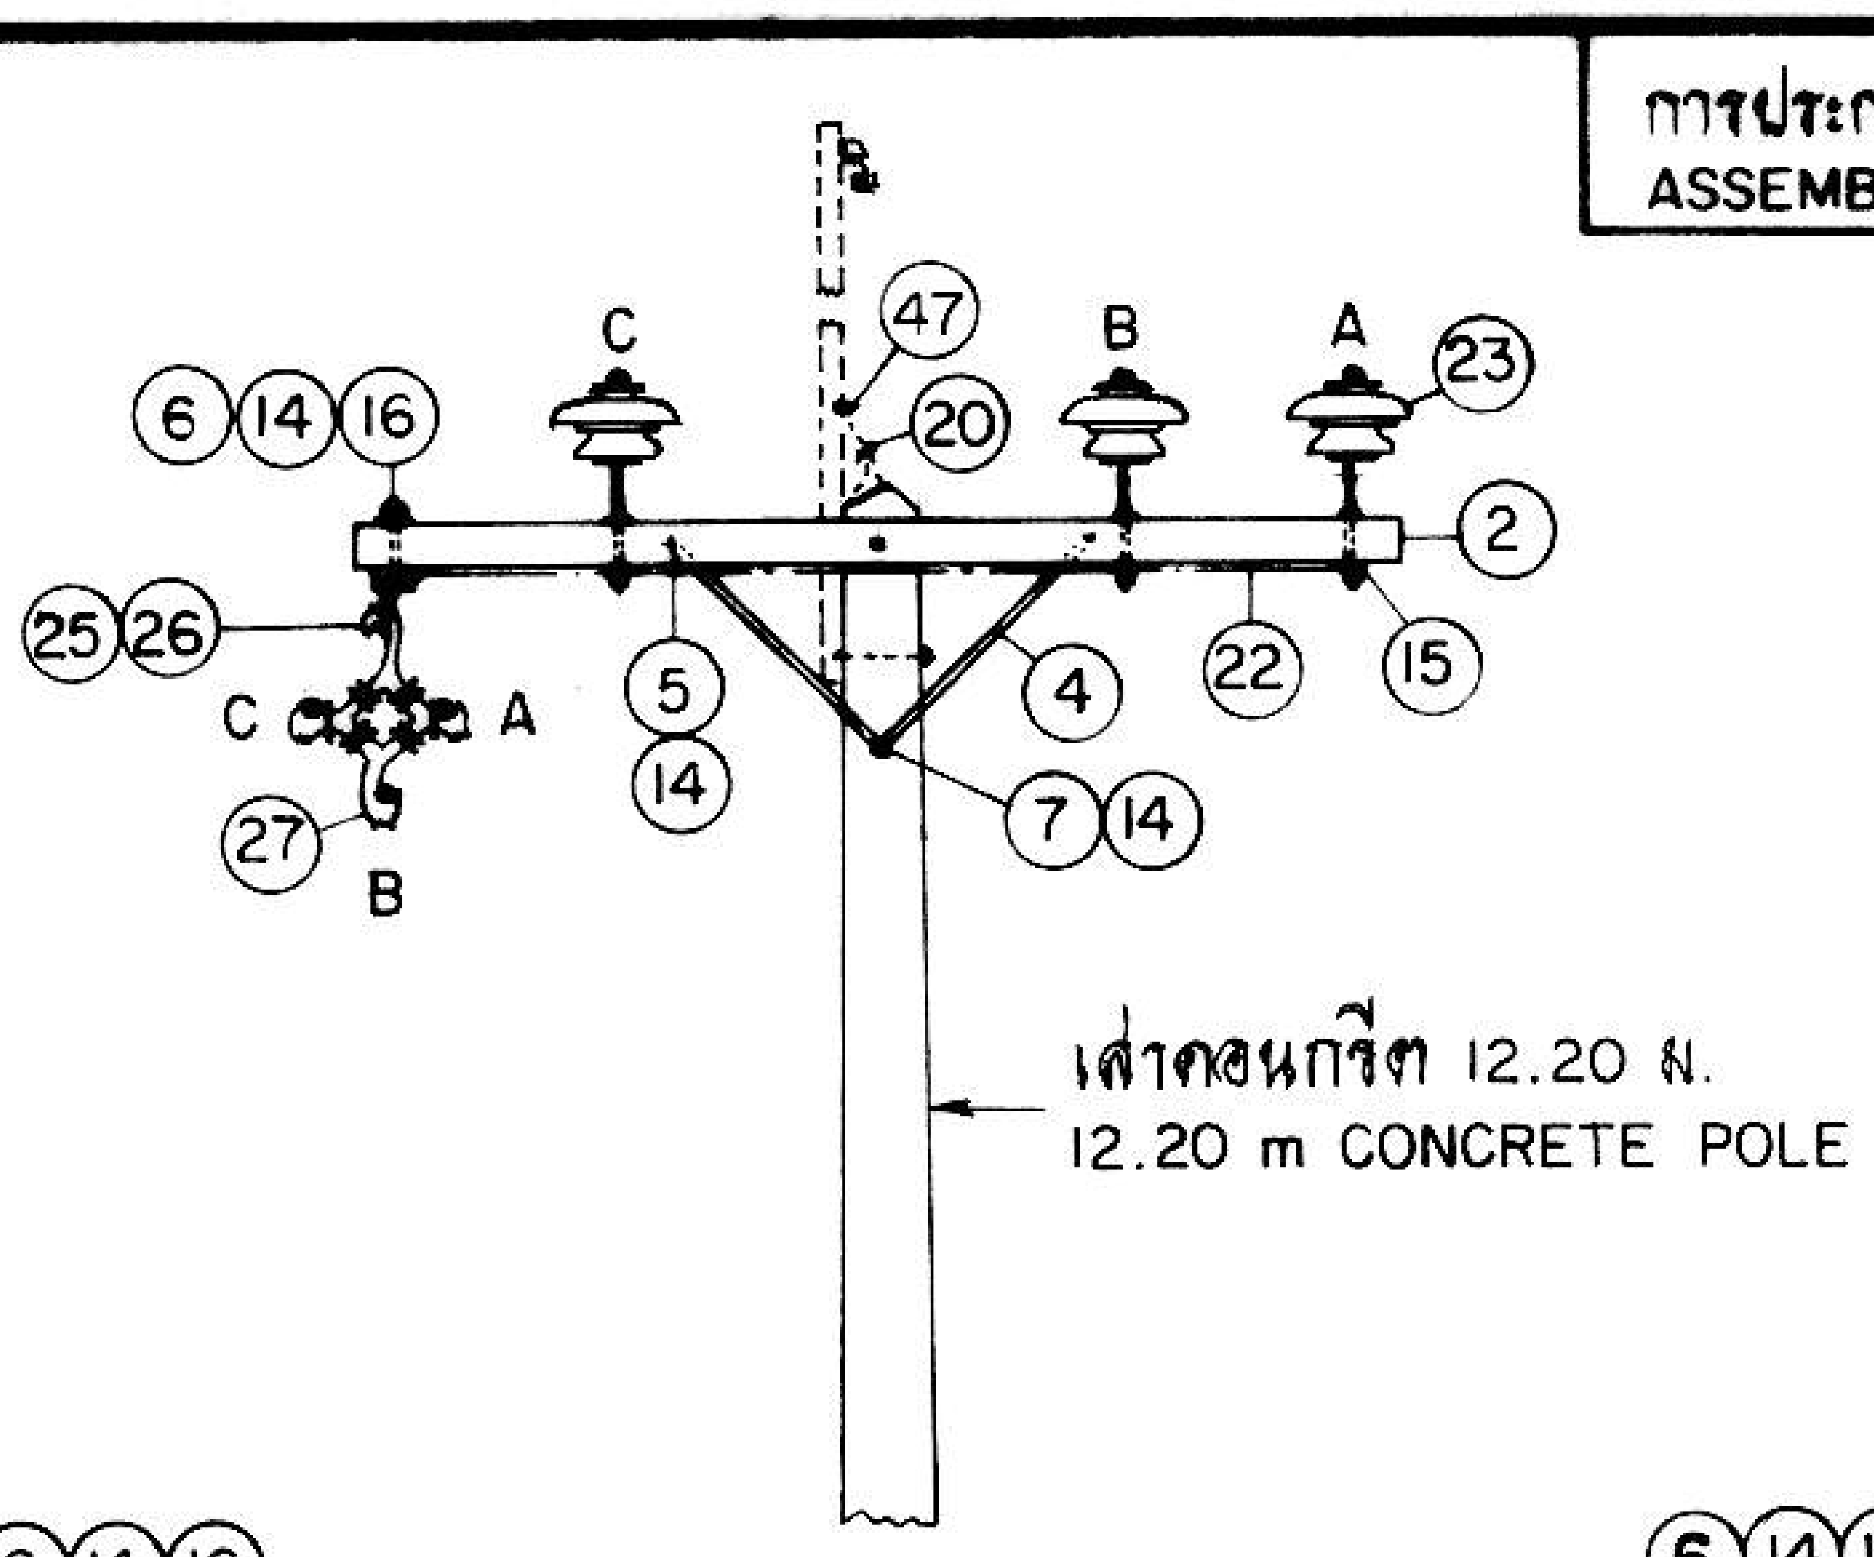

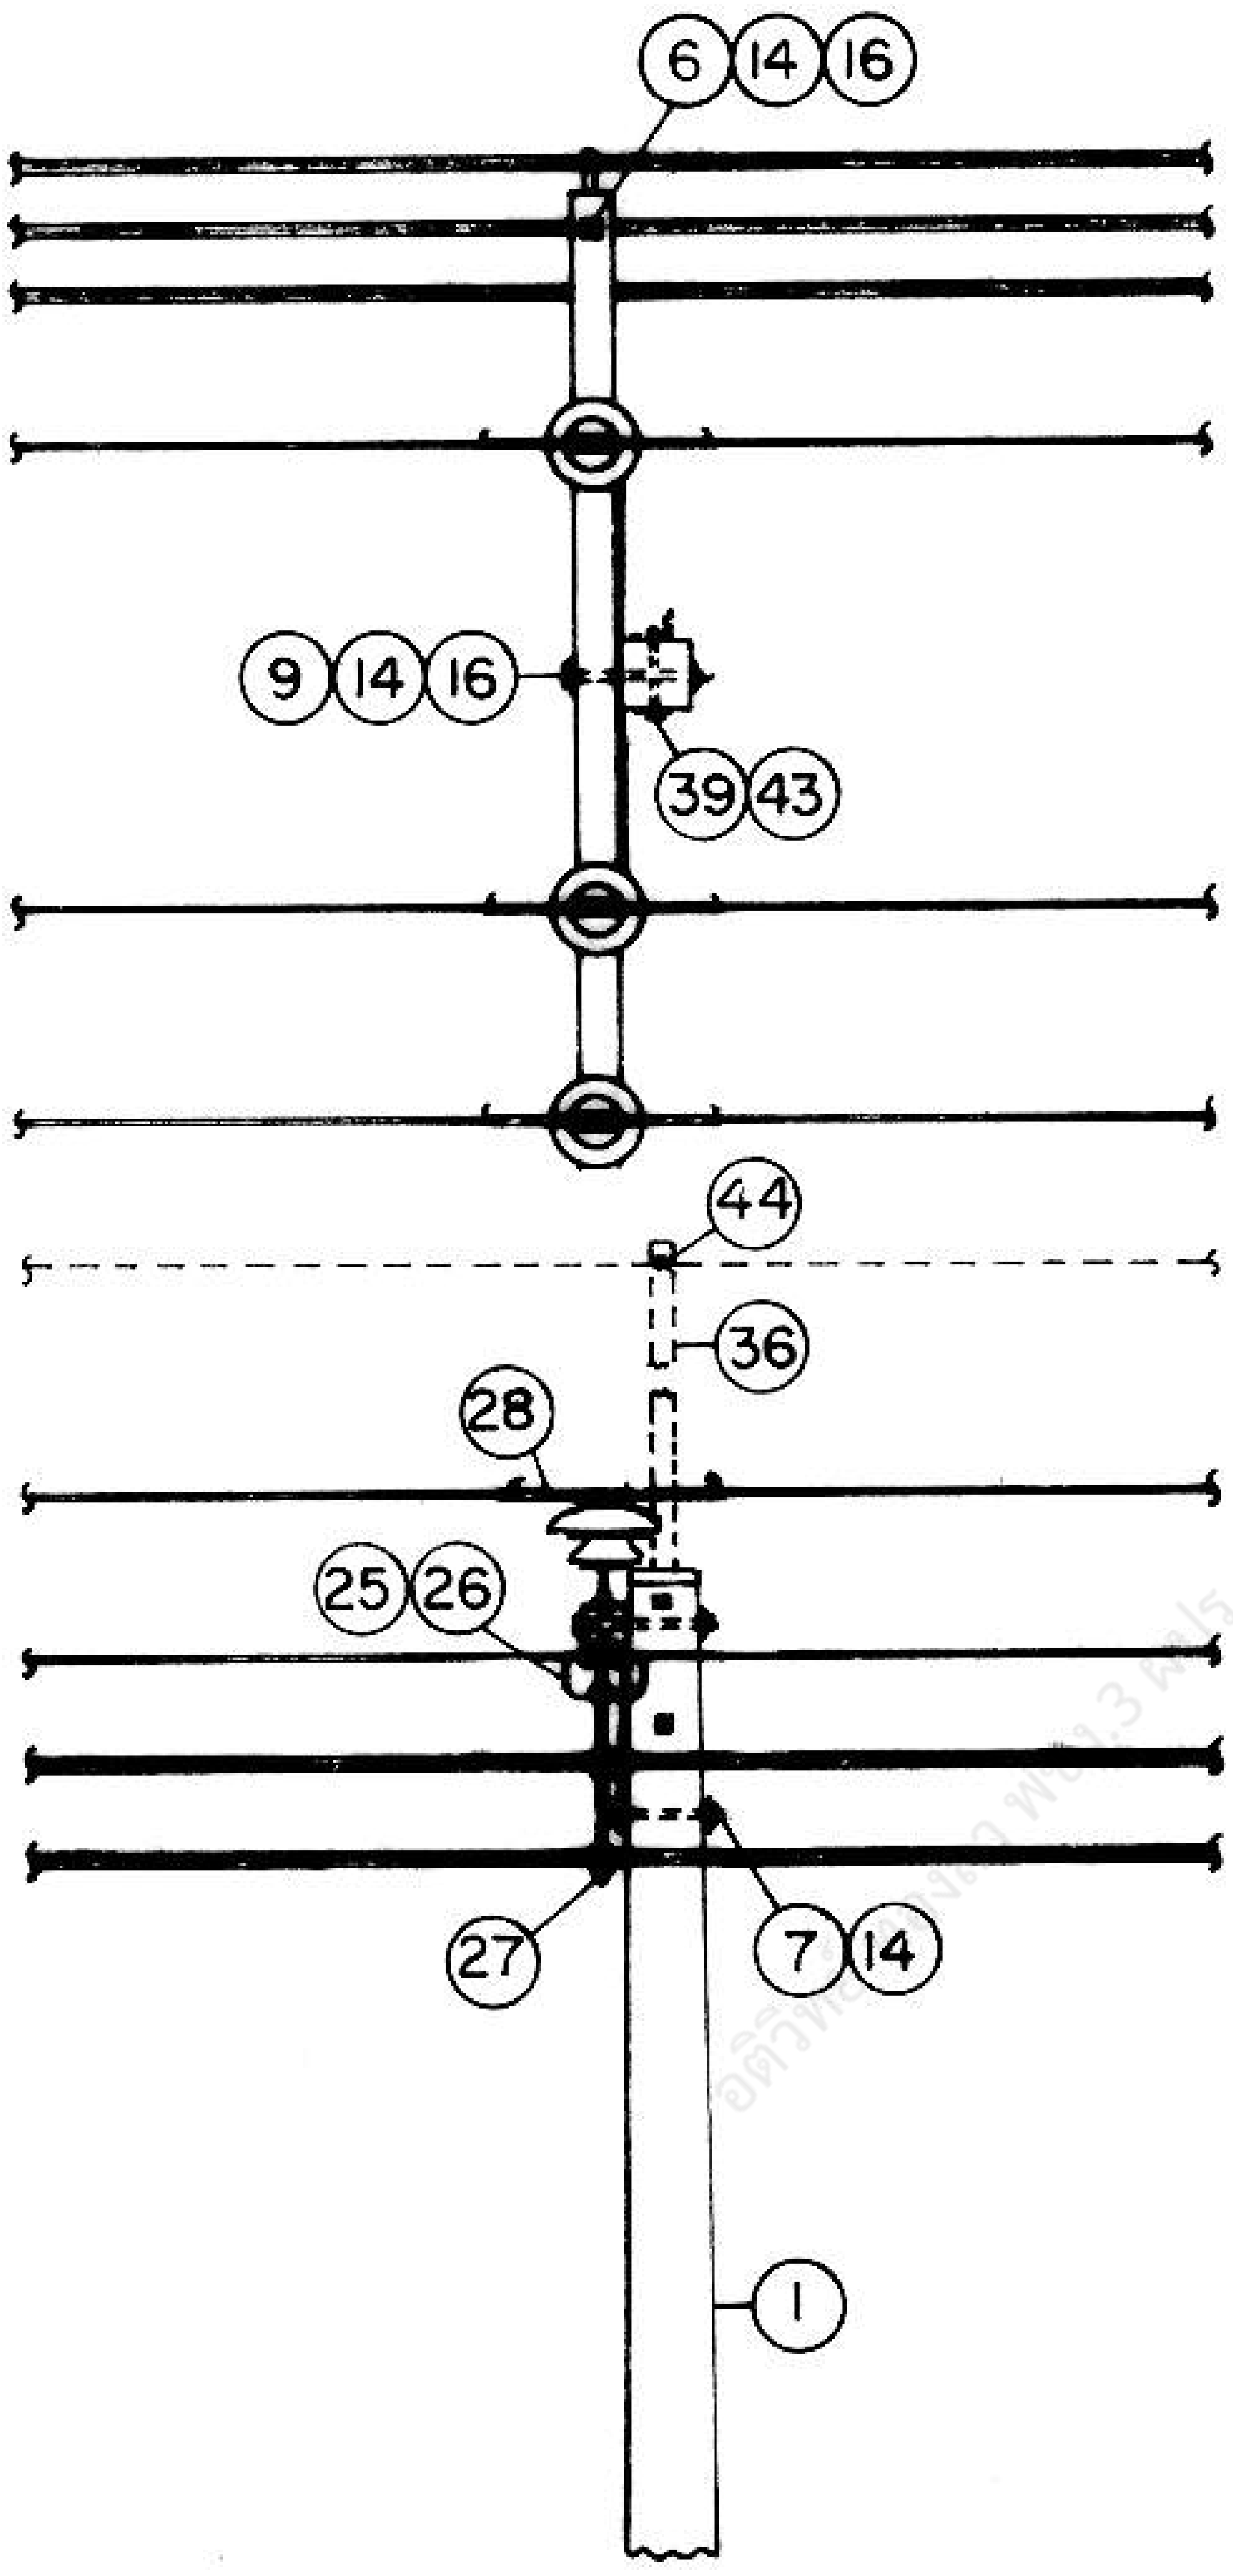

I สำหรับทางตรง FOR LINE ANGLE 0°-5°

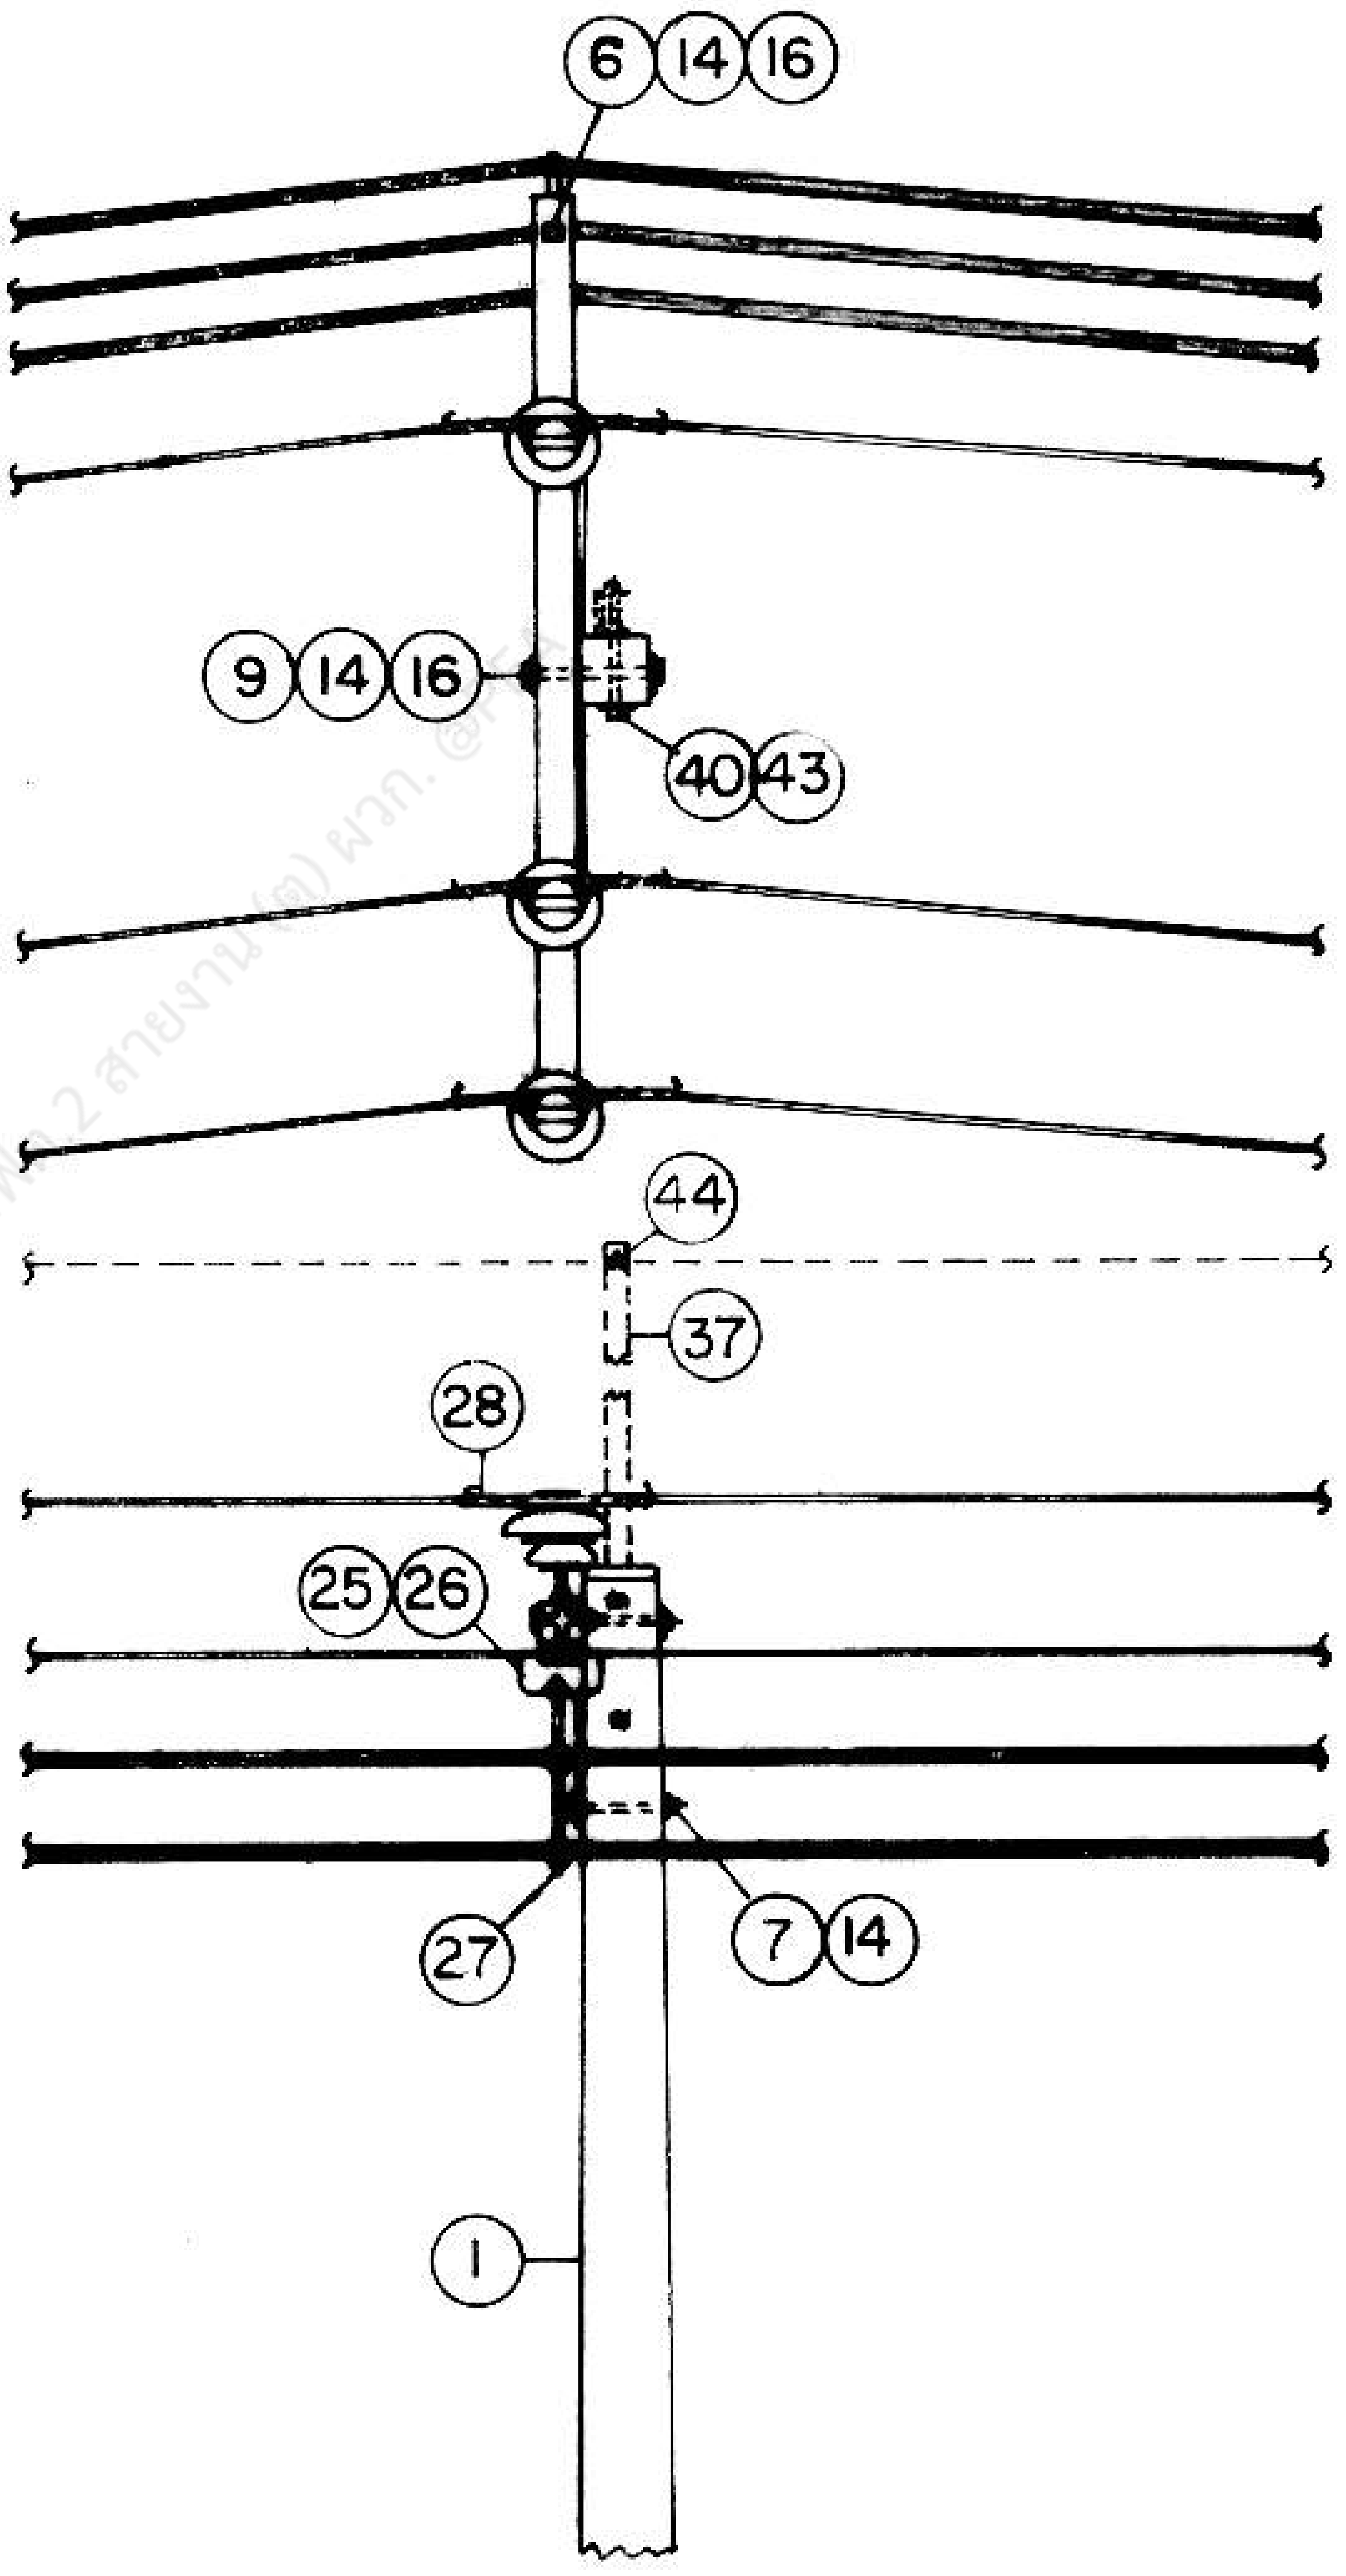

II สำหรับทางโค้ง FOR LINE ANGLE 5°-30° (θ)

กองวิศวกรรมไฟฟ้าและเครื่องกล ฝ่ายวิศวกรรม	**การไฟฟ้าส่วนภูมิภาค**	ใช้แทนแบบ....... ถูกแทนโดยแบบ.......
ผู้เขียน ผู้ตรวจ วิศวกร หัวหน้าแผนก ผู้อำนวยการกอง ผู้อำนวยการฝ่าย	ผู้ว่าการ .... 25 ต.ค. 2537 ผวก. การประกอบคอนบนเสาคอนกรีต 22 kV, 33 kV 2 วงจร (กรณีพาดสายหุ้มฉนวนแบบไม่เต็มพิกัด (PIC))	เขียนเสร็จวันที่ 11 ต.ค. 37 แก้แบบวันที่....... มิติเป็น มิลลิเมตร มาตราส่วน 1 : 50
รองผู้ว่าการฝ่ายเทคนิค 21 ต.ค. 2537	22 kV, 33 kV CROSSARM ASSEMBLY ON CONCRETE POLE 2 CIRCUIT (PARTIALLY INSULATED CONDUCTOR STRINGING)	แบบเลขที่ S44-015/37026 แผ่นที่ 2 ของจำนวน 9 แผ่น

การประกอบเลขที่ 2321 or 3906
ASSEMBLY NO.

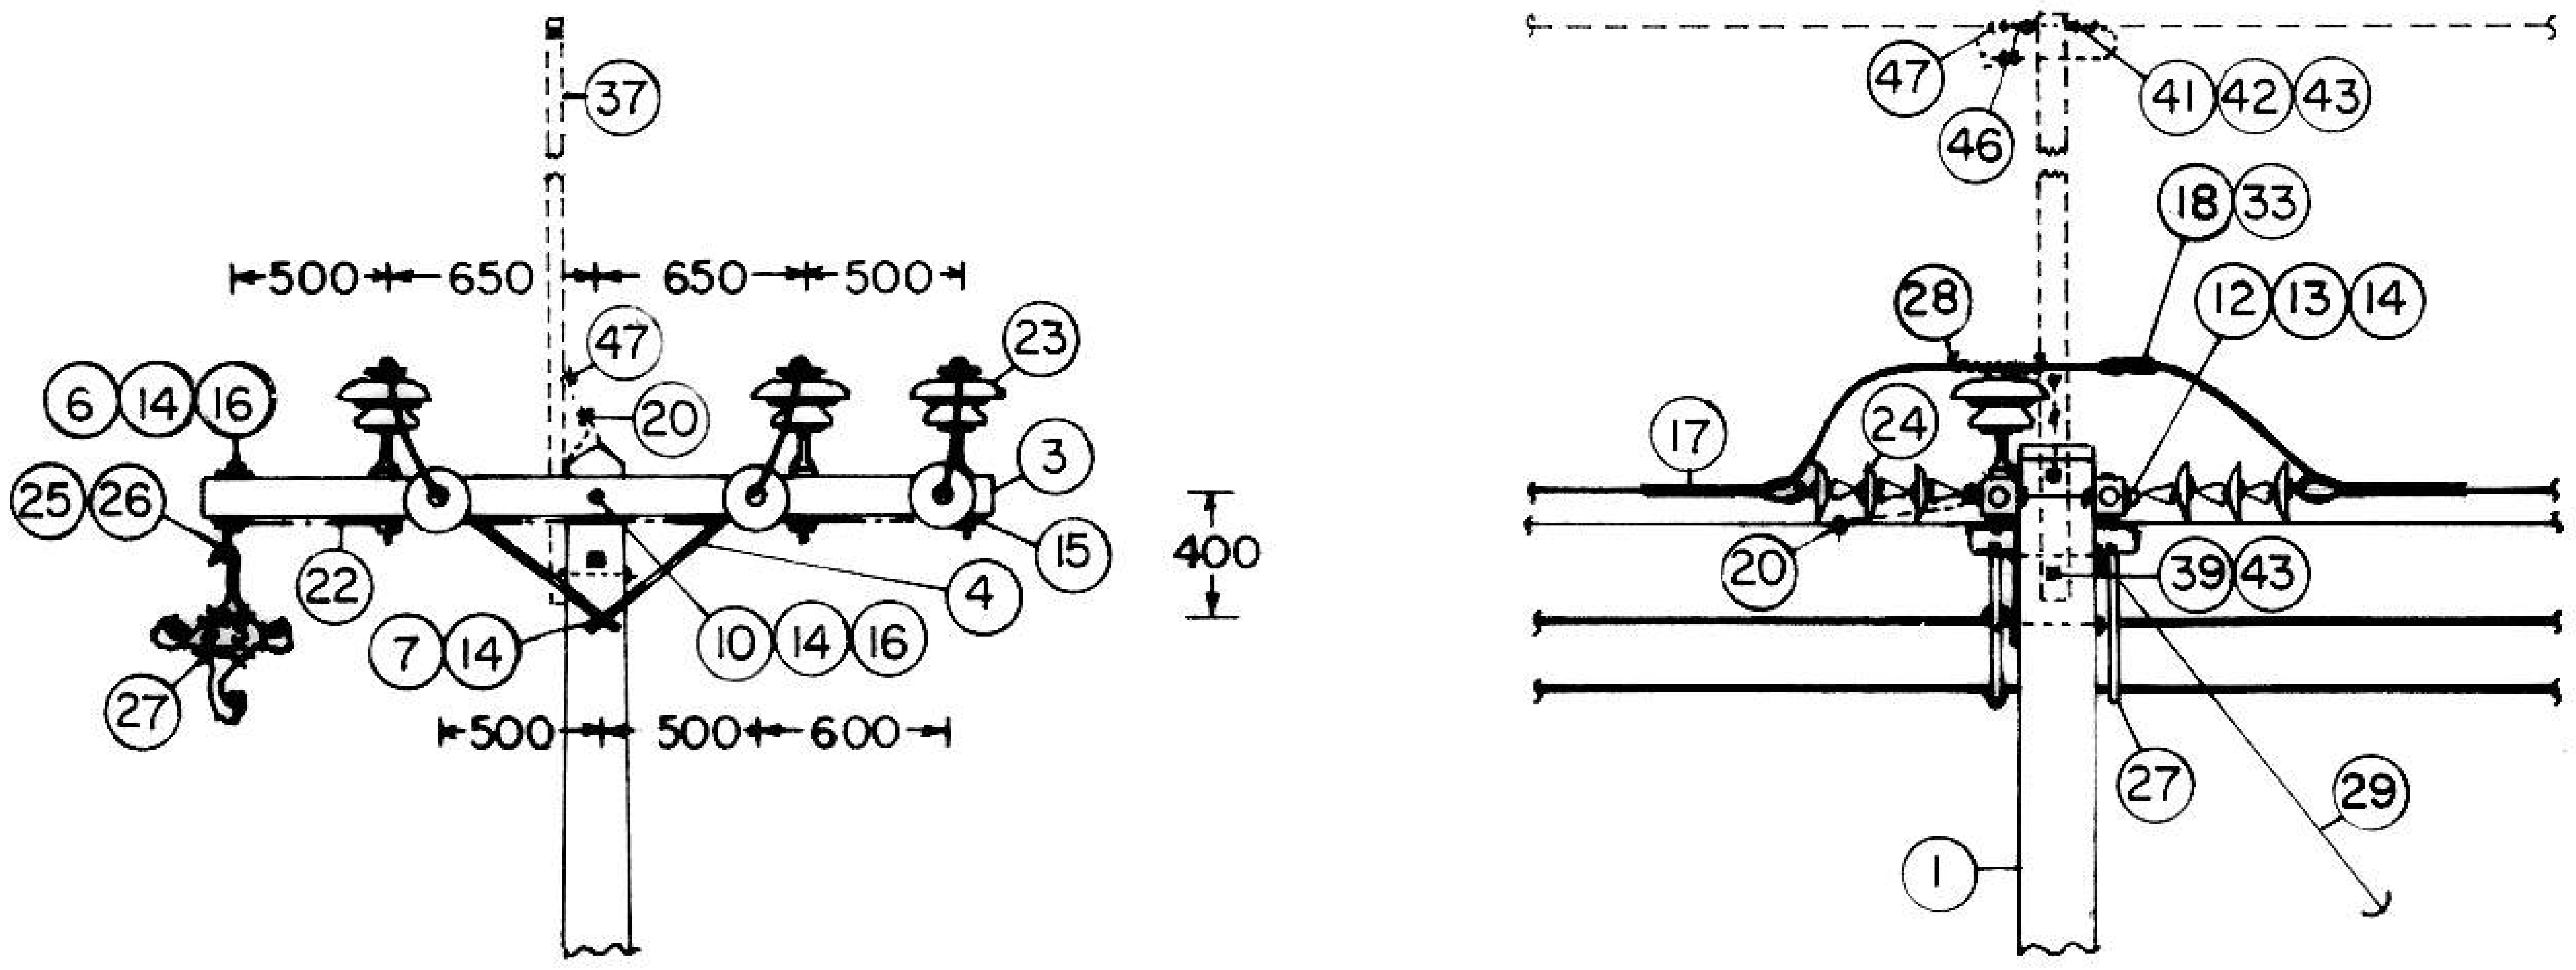

III สำหรับเข้าปลายสายสองข้าง ของวงจรสาย PIC
FOR DOUBLE DEADEND OF PIC

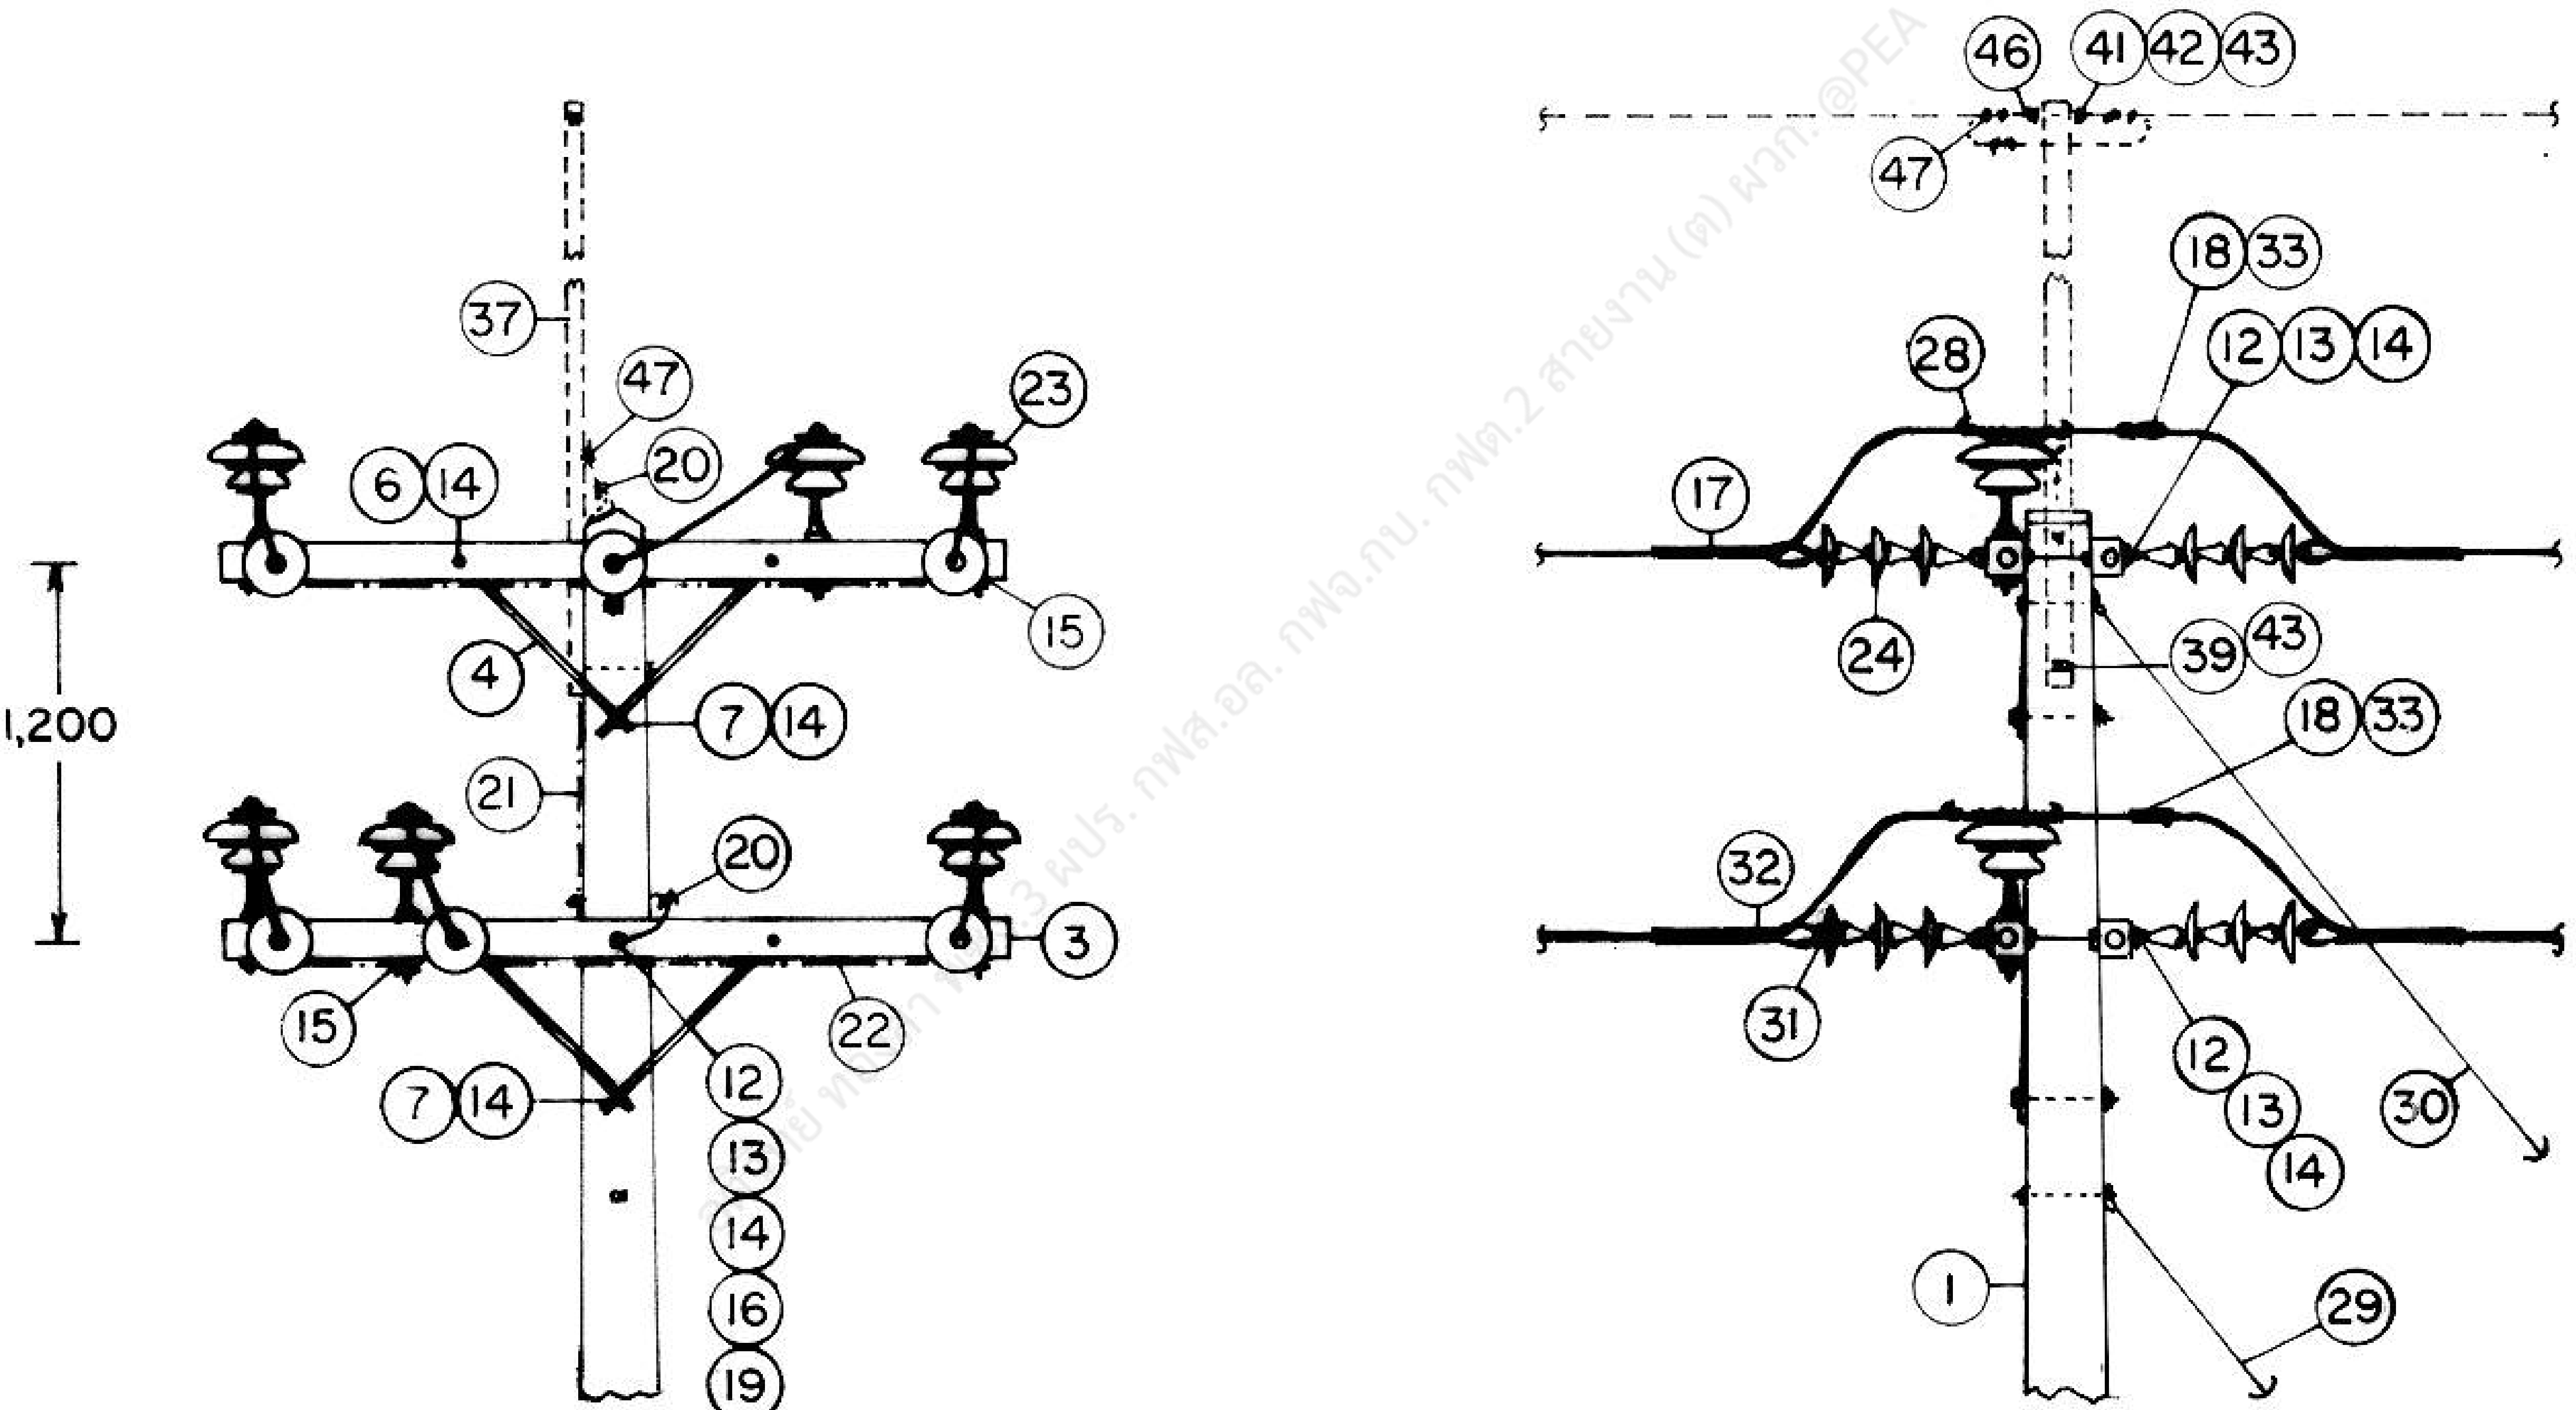

IV สำหรับเข้าปลายสายสองข้าง ทั้ง 2 วงจร
FOR 2 CIRCUITS DOUBLE DEADEND

กองวิศวกรรมไฟฟ้าและเครื่องกล
ฝ่ายวิศวกรรม

ผู้เขียน
ผู้สำรวจ
วิศวกร
หัวหน้าแผนก
ผู้อำนวยการกอง
ผู้อำนวยการฝ่าย

รองผู้ว่าการฝ่ายเทคนิค

การไฟฟ้าส่วนภูมิภาค

ผู้ว่าการ 25 ต.ค. 2537

การประกอบคอนกับเสาคอนกรีต 22 kV, 33 kV
2 วงจร
(กรณีพาดสายหุ้มฉนวนแบบไม่เต็มพิกัด (PIC))

22 kV, 33 kV CROSSARM ASSEMBLY ON CONCRETE POLE
2 CIRCUIT
(PARTIALLY INSULATED CONDUCTOR STRINGING)

ใช้แทนแบบ
ถูกแทนโดยแบบ
เขียนเสร็จวันที่ 11 ต.ค. 37
แก้แบบวันที่
มิติเป็น มิลลิเมตร
มาตราส่วน 1:50
แบบเลขที่ SA4-015/37026
แผ่นที่ 3 จากจำนวน 9 แผ่น

21 ต.ค. 2537

การประกอบเลขที่ ASSEMBLY NO.	2321 or 3906

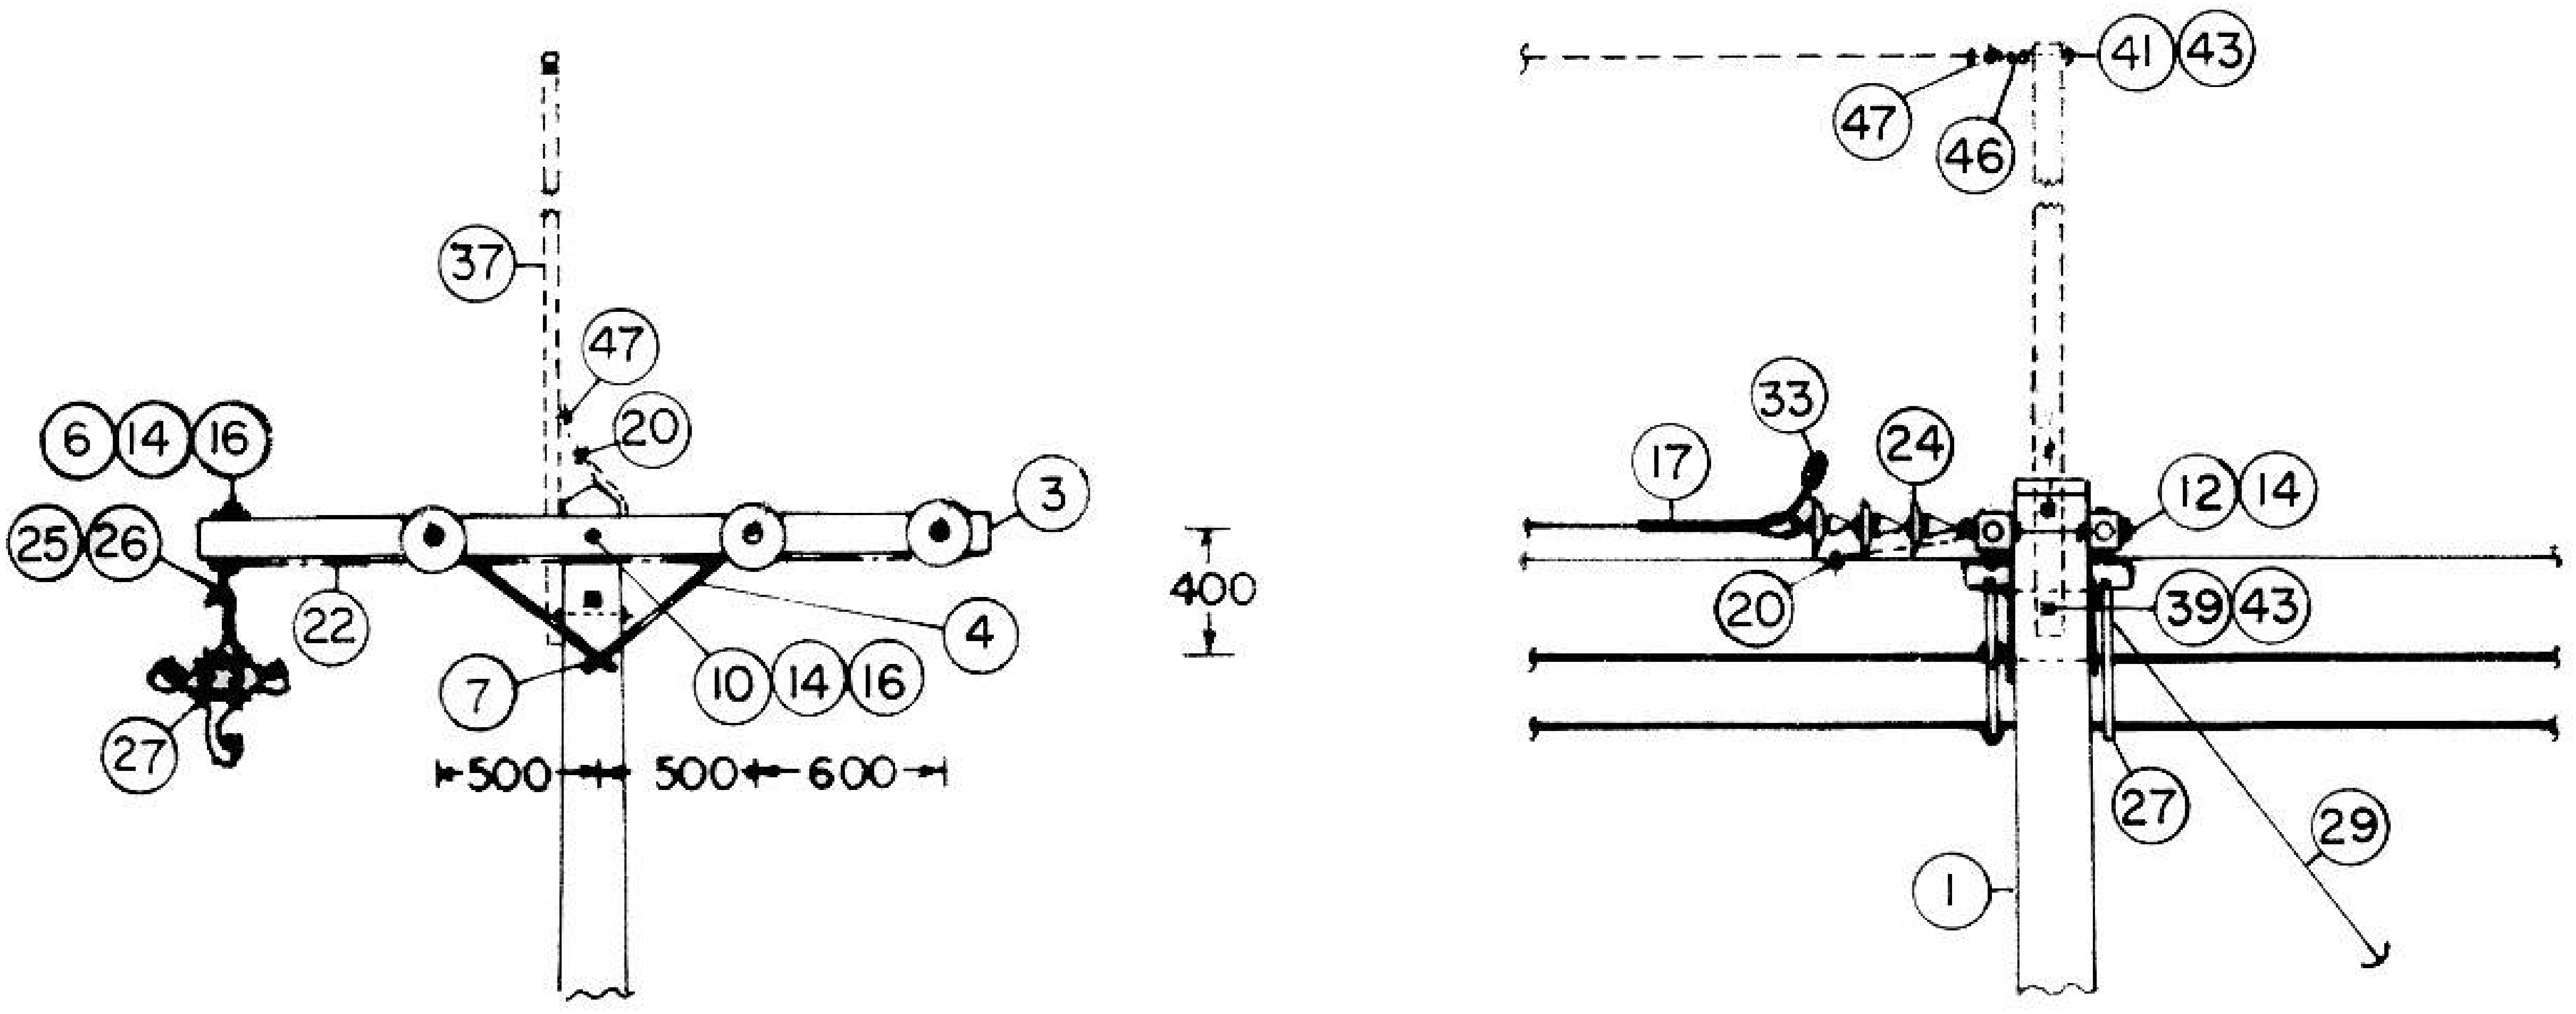

V สำหรับเข้าปลายสาย ของวงจร PIC
FOR DEADEND OF PIC

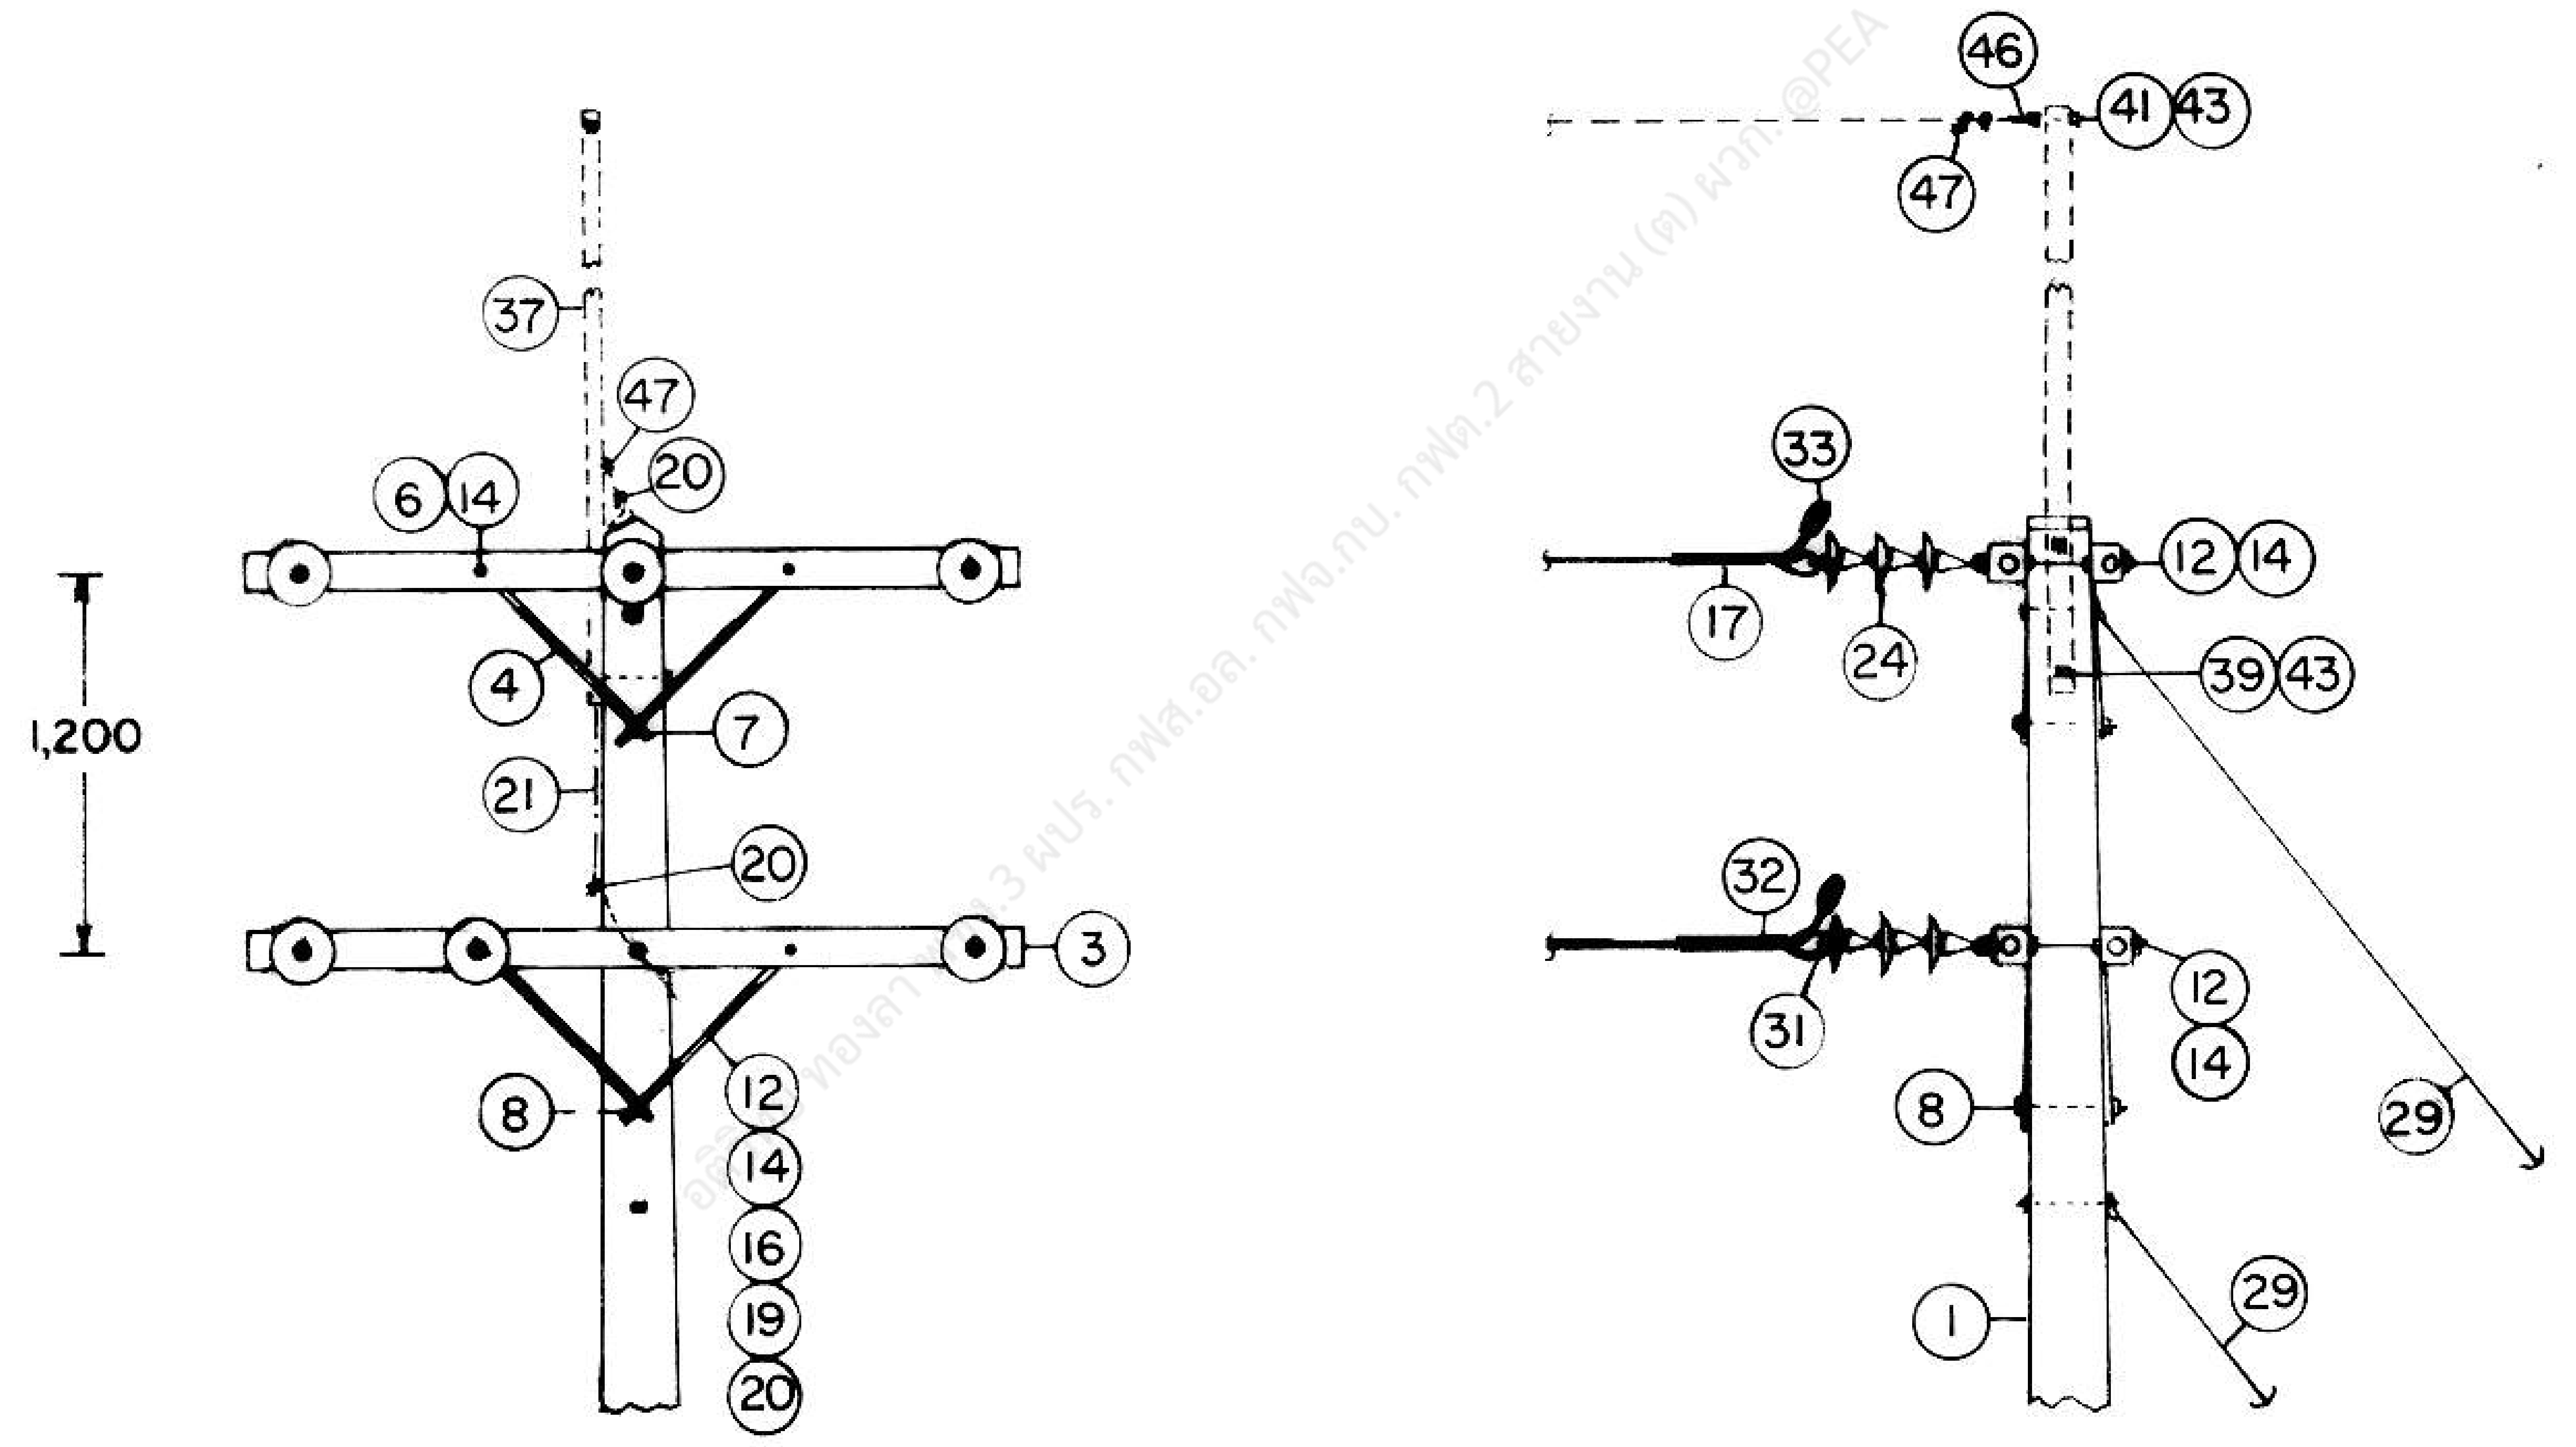

VI สำหรับเข้าปลายสายทั้ง 2 วงจร
FOR 2 CIRCUITS DEADEND

กฟจ.กบ. กฟต.2 สายงาน (ต) ผวก. @PEA

กองวิศวกรรมไฟฟ้าและเครื่องกล
ฝ่ายวิศวกรรม

ผู้เขียน
ผู้สำรวจ
วิศวกร
หัวหน้าแผนก
ผู้อำนวยการกอง
ผู้อำนวยการฝ่าย

รองผู้ว่าการฝ่ายเทคนิค

การไฟฟ้าส่วนภูมิภาค

ผู้ว่าการ 25 ต.ค. 2537

การประกอบคอนกับเสาคอนกรีต 22 kV, 33 kV
2 วงจร
(กรณีพาดสายหุ้มฉนวนแบบไม่เต็มพิกัด (PIC))

22 kV, 33 kV CROSSARM ASSEMBLY ON CONCRETE POLE
2 CIRCUIT
(PARTIALLY INSULATED CONDUCTOR STRINGING)

ใช้แทนแบบ
ถูกแทนโดยแบบ
เขียนเสร็จวันที่ 11 ต.ค. 37
แก้แบบวันที่
หน่วยเป็น มิลลิเมตร
มาตราส่วน 1 : 50
แบบเลขที่ SA4-015/37026
แผ่นที่ 4 รวมจำนวน 9 แผ่น

21 ต.ค. 2537

การประกอบเลขที่ **2321** or
ASSEMBLY NO. **3906**

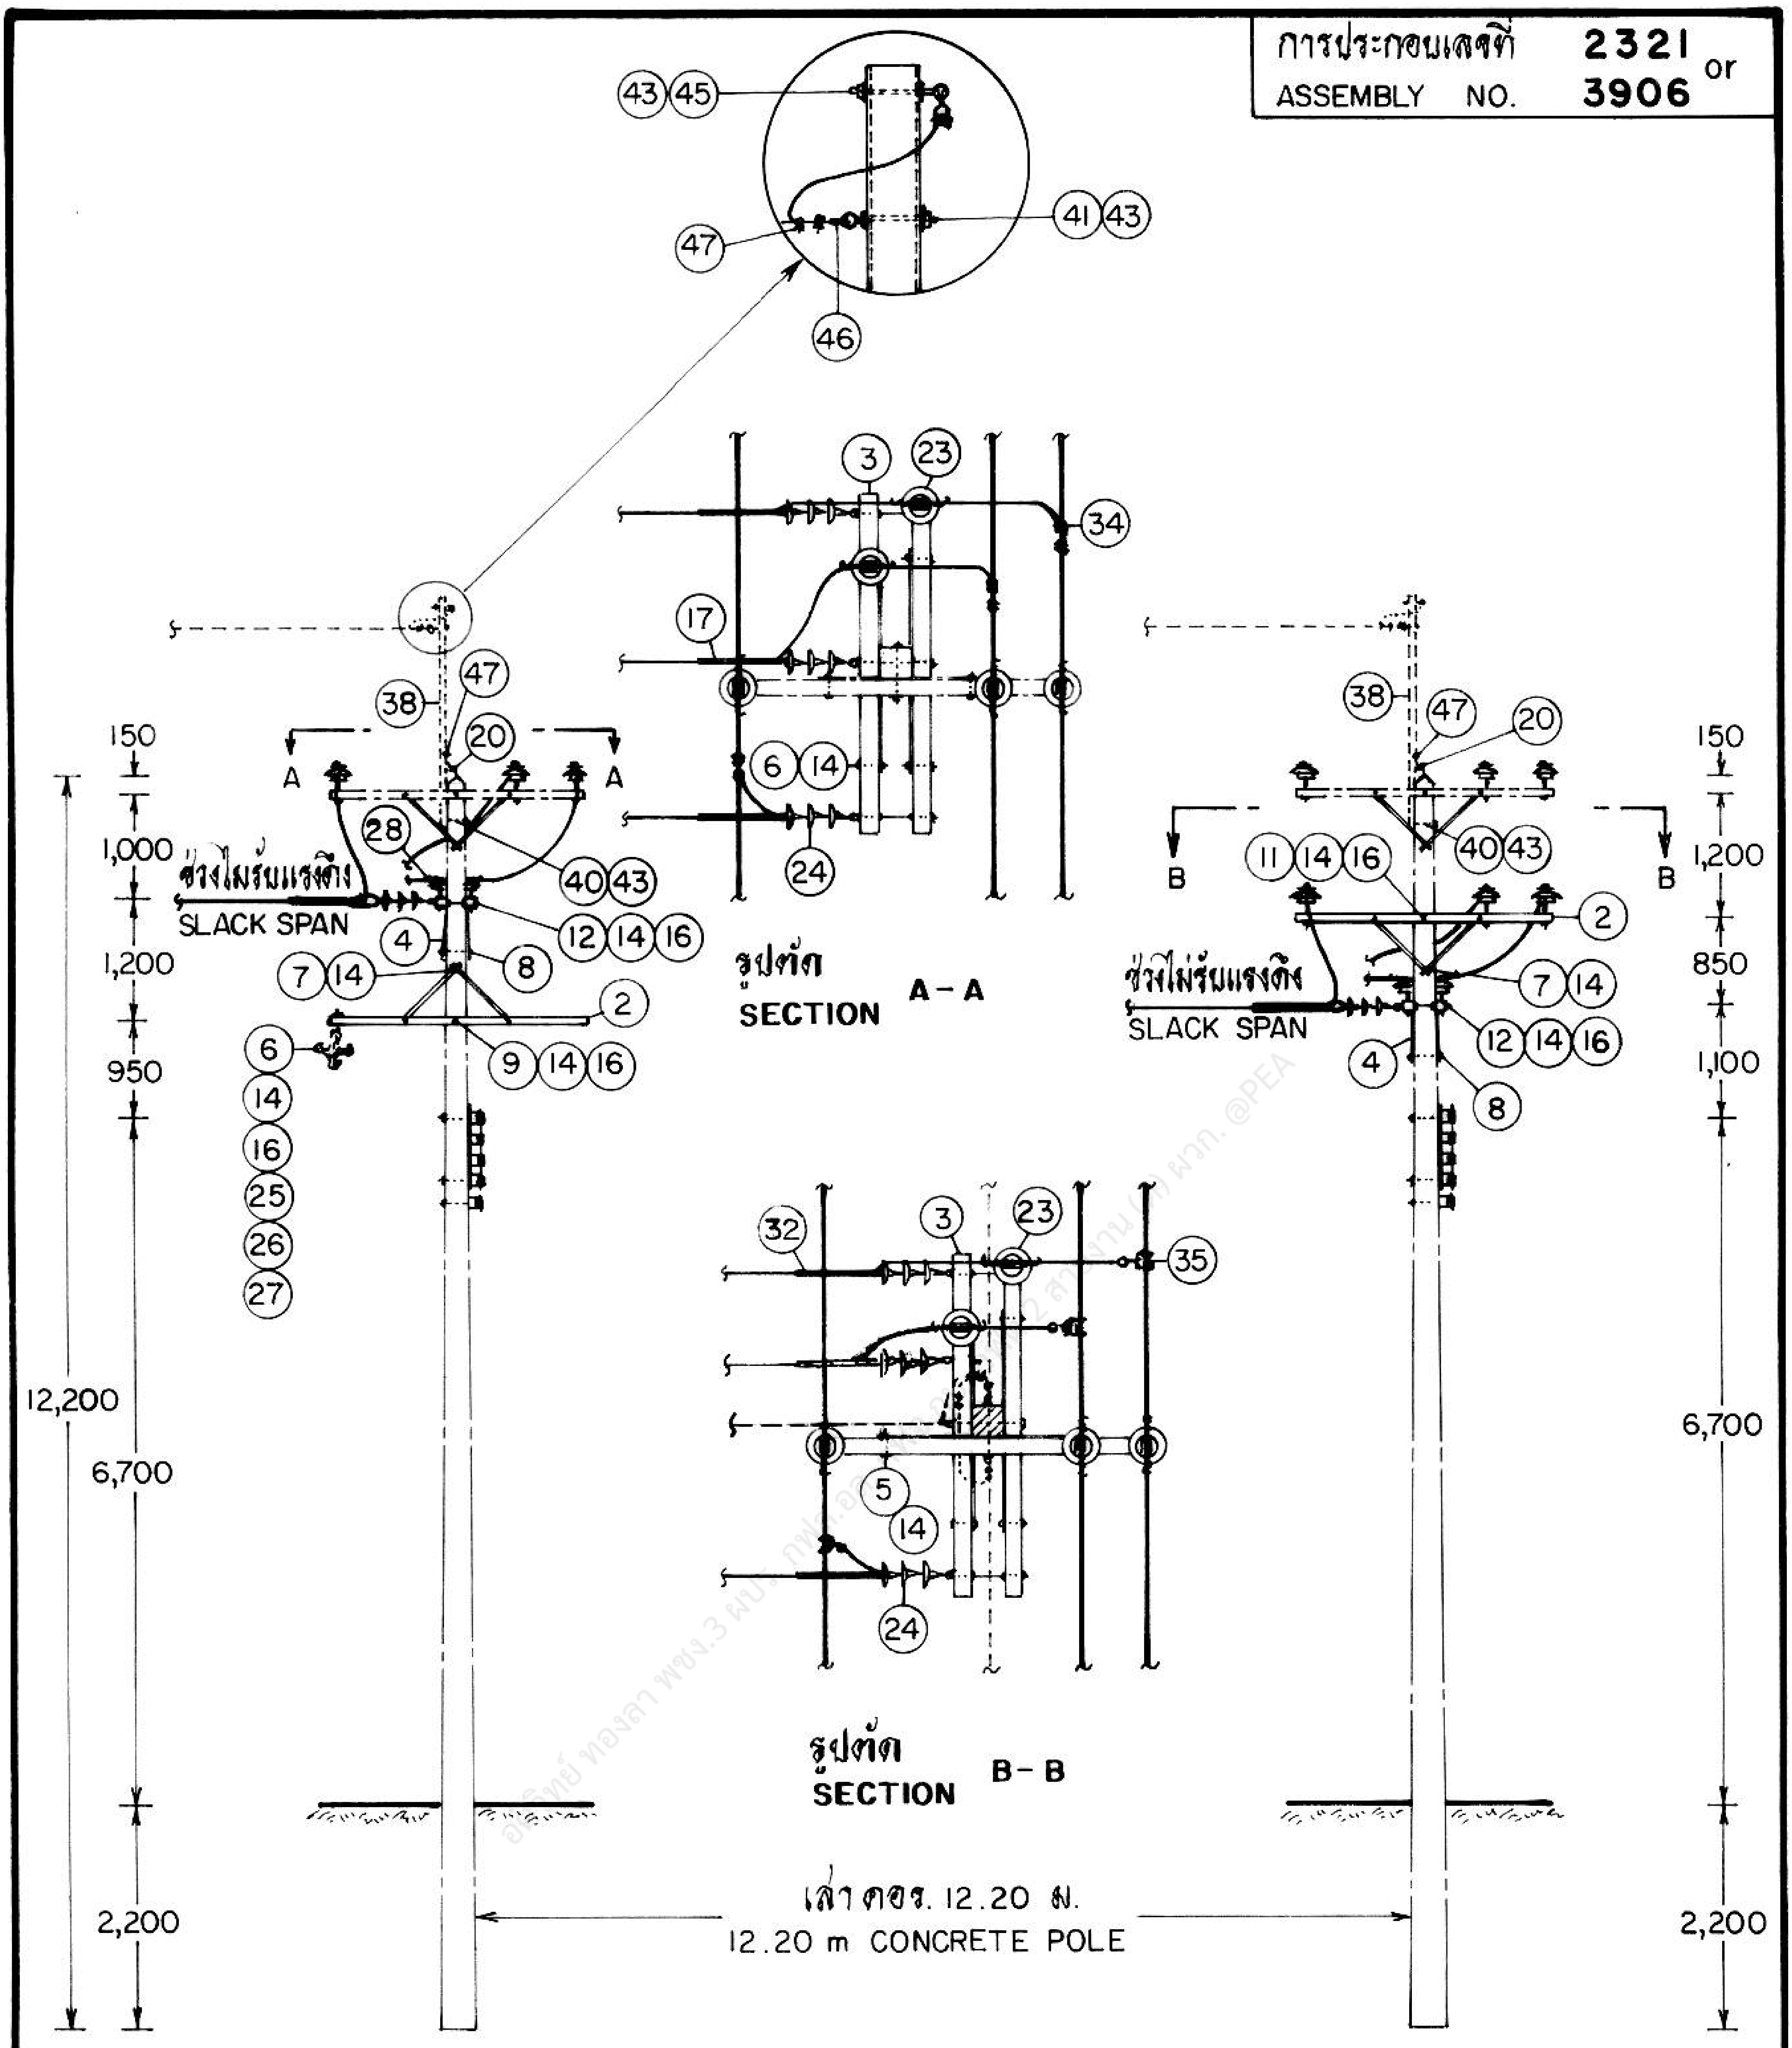

VII สำหรับต่อแยกสาย PIC
FOR TAP LINE OF PIC

VIII สำหรับต่อแยกสายเคเบิลอากาศ
FOR TAP LINE OF AERIAL CABLE

กองวิศวกรรมไฟฟ้าและเครื่องกล
ฝ่ายวิศวกรรม

ผู้เขียน
ผู้สำรวจ
วิศวกร
หัวหน้าแผนก
ผู้อำนวยการกอง
ผู้อำนวยการฝ่าย

รองผู้ว่าการฝ่ายเทคนิค

การไฟฟ้าส่วนภูมิภาค

ผู้ว่าการ 25 ต.ค. 2537

การประกอบคอนกับเสาคอนกรีต 22 kV, 33 kV
2 วงจร
(กรณีพาดสายหุ้มฉนวนแบบไม่เต็มพิกัด (PIC))

22 kV, 33 kV CROSSARM ASSEMBLY ON CONCRETE POLE
2 CIRCUIT
(PARTIALLY INSULATED CONDUCTOR STRINGING)

ใช้แทนแบบ
ถูกแทนโดยแบบ
เขียนเสร็จวันที่ 11 ต.ค. 37
แก้แบบวันที่
มิติเป็น มิลลิเมตร
มาตราส่วน 1 : 75 , 1 : 100

แบบเลขที่ SA4-015/37026
แผ่นที่ 5 ของจำนวน 9 แผ่น

การประกอบเลขที่ **2321** or
ASSEMBLY NO. **3906**

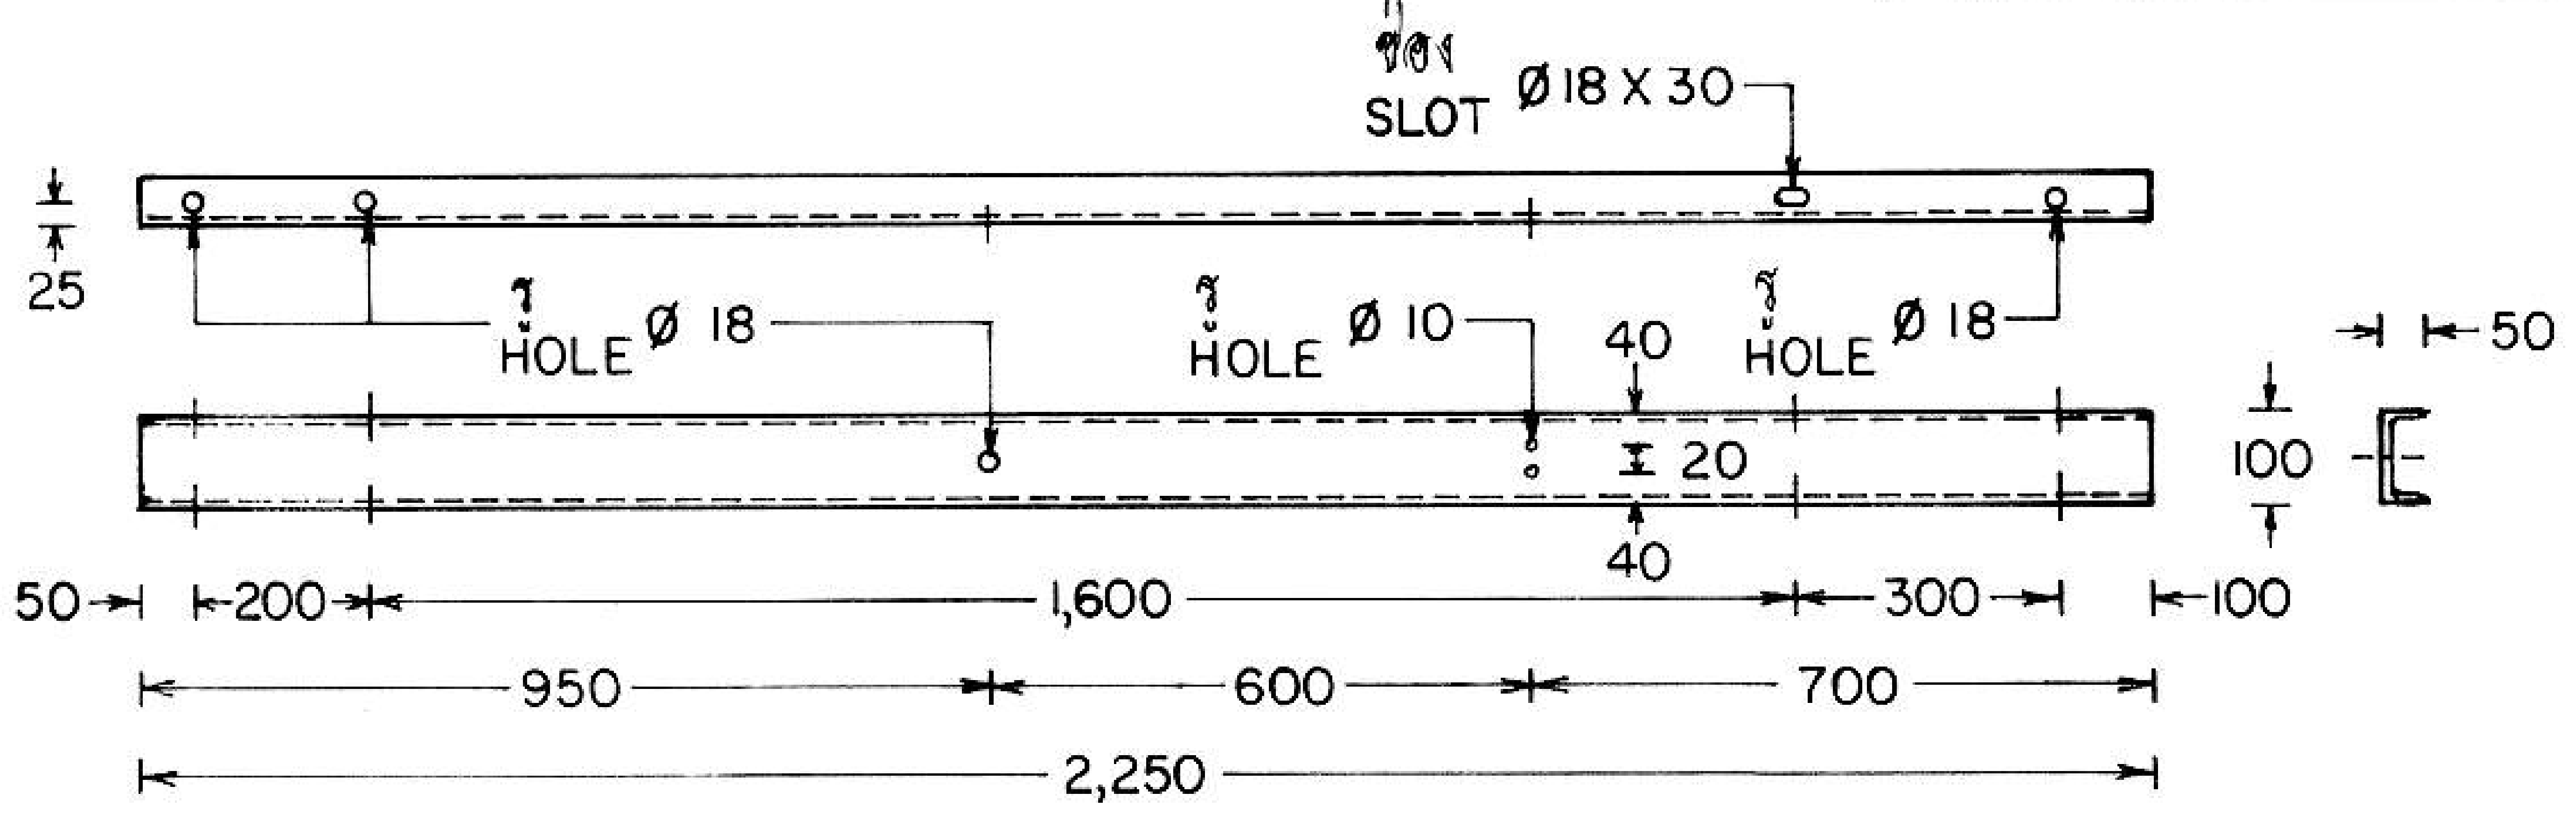

㊳ เหล็กรูปรางน้ำ ชนิดรีดร้อน ขนาด 100 X 50 X 5 มม. ยาว 2.25 ม. มอก. 116
(อาจทำจากเหล็กรูปรางน้ำ วัสดุเลขที่ 01000100 ได้)
STEEL, CHANNEL, 100 X 50 X 5 mm, 2.25 m LONG TIS 116
(MAY BE MADE FROM CHANNEL STEEL MAT. NO. 01000100)

บัญชีวัสดุ
BILL OF MATERIAL

ลำดับที่ ITEM	รายละเอียด DESCRIPTION	จำนวน REQ'D I	II	III	IV	V	VI	VII	VIII	วัสดุเลขที่ MAT. NO.
1	เสาคอนกรีต ขนาด 12.20 ม. POLE, CONCRETE, 12.20 m LONG	1	1	1	1	1	1	–	–	
2	คอน คอร. สปัน ขนาด 100 X 100 X 2,500 มม. CROSSARM, SPUN, PRESTRESSED CONCRETE, 100 X 100 X 2,500 mm	1	1	–	–	–	–	1	1	00110001
3	คอน คอร. สปัน (สำหรับเข้าปลายสาย) ขนาด 120 X 120 X 2,500 มม. CROSSARM, SPUN, PRESTRESSED (FOR DEADENDING) 120 X 120 X 2,500 mm	–	–	2	4	2	4	2	2	00110004
4	เหล็กประกับคอน ขนาด 30 X 6 X 760 มม. BRACE, FLAT, FOR CROSSARM, 30 X 6 X 760 mm	2	2	2	4	4	8	6	6	01200001
5	สลักเกลียว M 16 X 130 มม. BOLT, MACHINE, M 16 X 130 mm	2	2	–	–	–	–	2	2	01110200
6	สลักเกลียว M 16 X 170 มม. BOLT, MACHINE, M 16 X 170 mm	1	1	2	3	2	6	4	4	01110201
7	สลักเกลียว M 16 X 250 มม. BOLT, MACHINE, M 16 X 250 mm	1	1	1	1	2	1	1	1	01110203
8	สลักเกลียว M 16 X 300 มม. BOLT, MACHINE, M 16 X 300 mm	–	–	–	–	–	1	1	1	01110204
9	สลักเกลียว M 16 X 350 มม. BOLT, MACHINE, M 16 X 350 mm	1	1	–	–	–	–	1	–	01110205
10	สลักเกลียว M 16 X 500 มม. BOLT, MACHINE, M 16 X 500 mm	–	–	1	–	1	–	–	–	01110208
11	สลักเกลียวห่วงกลม M 16 X 400 มม. BOLT, DOUBLE ARMING, ROUND EYE, M 16 X 400 mm	–	–	–	–	–	–	–	1	01130000

กองวิศวกรรมไฟฟ้าและเครื่องกล
ฝ่ายวิศวกรรม

ผู้เขียน
ผู้สำรวจ
วิศวกร
หัวหน้าแผนก
ผู้อำนวยการกอง
ผู้อำนวยการฝ่าย

รองผู้ว่าการฝ่ายเทคนิค
21 ต.ค. 2537

การไฟฟ้าส่วนภูมิภาค

ผู้ว่าการ 25 ต.ค. 2537 ผวก.

การประกอบคอนกับเสาคอนกรีต 22 kV, 33 kV
2 วงจร
(กรณีพาดสายหุ้มฉนวนแบบไม่เต็มพิกัด (PIC))

22 kV, 33 kV CROSSARM ASSEMBLY ON CONCRETE POLE
2 CIRCUIT
(PARTIALLY INSULATED CONDUCTOR STRINGING)

ใช้แทนแบบ
ถูกแทนโดยแบบ
เขียนเสร็จวันที่ 11 ต.ค. 37
แก้แบบวันที่
มิติเป็น มิลลิเมตร
มาตราส่วน 1 : 20
แบบเลขที่ SA4-015/37026
แผ่นที่ 6 ของจำนวน 9 แผ่น

การประกอบเลขที่ 2321 or
ASSEMBLY NO. 3906

บัญชีวัสดุ
BILL OF MATERIAL

ลำดับที่ ITEM	รายละเอียด DESCRIPTION	จำนวน REQ'D								วัสดุเลขที่ MAT. NO.
		I	II	III	IV	V	VI	VII	VIII	
12	สลักเกลียวห่วงกลม M 16 X 500 มม. BOLT, DOUBLE ARMING, ROUND EYE, M 16 X 500 mm	–	–	3	7	3	7	3	3	01130002
13	นัทรูปห่วง M 16 DIN 582 NUT, EYE, M 16, DIN 582	–	–	3	7	–	–	–	–	01180001
14	แหวนสี่เหลี่ยมแบน 52 X 52 X 4.5 มม. รู Ø 18 มม. มอก. 258 WASHER, SQUARE, FLAT, 52 X 52 X 4.5 mm, HOLE Ø 18 mm, TIS 258	8	8	19	28	16	28	22	19	01180100
15	แหวนสี่เหลี่ยมโค้ง 60X60X5 มม. รู Ø 22 มม. WASHER, SQUARE, CURVED, 60X60X5 mm, HOLE Ø 22 mm	3	3	3	6	–	–	–	–	01180201
16	แหวนรองแบบสปริง ขนาดระบุ 16 มม. มอก. 259 WASHER, LOCK, SPRING, SIZE 16 mm, TIS 259	2	2	3	1	3	2	2	2	01180300
17	สเตรนแคล้มป์ หรือปรีฟอร์มเข้าปลายสาย พร้อมทิมเบิลเคลวิส ขนาดตามต้องการ CLAMP, STRAIN; OR PREFORMED DEADEND WITH THIMBLE CLEVIS IS SIZE AS REQUIRED	–	–	6	6	3	3	3	3	03110000-4 02260000-4 03140011
18	หลอดต่อสายชนิดบีบไม่รับแรงดึง สายอะลูมิเนียม ขนาดตามต้องการ CONNECTOR, SPLICE, COMPRESSION TYPE, TENSIONLESS, Al ; SIZE AS REQUIRED	–	–	3	6	–	–	–	–	02410001-7
19	กายทิมเบิล สำหรับสายยึดโยง 50-95 ต.มม. THIMBLE, GUY, FOR STEEL WIRE 50-95 mm^2	–	–	–	2	–	1	–	2	01210304
20	ยูแคล้มป์ สลัก 1 ตัว M 8 CLAMP, SINGLE U-BOLT, M 8	2	2	2	9	2	4	1	7	01230000
21	ลวดเหล็กตีเกลียว 25 ต.มม. มอก. 404 WIRE, STEEL STRANDED, 25 mm^2; TIS 404	–	–	–	2 ม. m	–	2 ม. m	–	–	01100002
22	ลวดเหล็กกลม เส้นผ่านศูนย์กลาง 4 มม. มอก. 71 (นน. ประมาณ 0.1 กก./ม.) WIRE, STEEL, SOLID, DIA. 4 mm, TIS 71 (WEIGHT 0.1 kg/m)	4 ม. m	4 ม. m	4 ม. m	8 ม. m	2 ม. m	–	–	–	01100000
23	ลูกถ้วยก้านตรง มอก. 279 แบบ ข หรือ แบบ ค พร้อมก้าน INSULATOR, PIN TYPE, TIS 279, TYPE B OR C (CLASS 56-2 OR 56-3); COMP. WITH PIN	3	3	3	6	–	–	2	5	03000001 or 03000002 03100000 or 03100001
24	ลูกถ้วยแขวน มอก. 354 แบบ ก หรือ แบบ ง INSULATOR, SUSPENSION TYPE, TIS 354, TYPE A OR D (CLASS 52-1 OR 52-2)	–	–	18	36	9	18	9	9	03020000 or 03020002
25	แคล้มป์แขวนสายเคเบิล หรือ กายแคล้มป์ สลัก 3 ตัว CLAMP, CABLE SUSPENSION; OR CLAMP, GUY, TRIPLE BOLT	1	1	2	–	2	–	1	–	02440100 or 02440102
26	ที่จับเคเบิลสเปเซอร์ หรือ ห่วงแขวนเคเบิลสเปเซอร์ CLEVIS, FLAT STEEL, FOR CABLE SPACER; OR LINK, CABLE SPACER	1	1	2	–	2	–	1	–	02440101 or 02440103
27	เคเบิลสเปเซอร์ ชนิดอะลูมินา 22-33 kV พร้อมห่วงรัด SPACER, CABLE, ALUMINA, 22-33 kV; WITH SNAP TIES	1	1	2	–	2	–	1	–	02440001_ 02440003
28	ลวดอะลูมิเนียมกลม 4.0 มม. ความยาวตามต้องการ TIE, WIRE, Al, 4.0 mm; LENGTH AS REQUIRED	ม. m	ม. m	ม. m	ม. m	–	–	ม. m	ม. m	02200002

กองวิศวกรรมไฟฟ้าและเครื่องกล
ฝ่ายวิศวกรรม

ผู้เขียน
ผู้สำรวจ
วิศวกร
หัวหน้าแผนก
ผู้อำนวยการกอง
ผู้อำนวยการฝ่าย

รองผู้ว่าการฝ่ายเทคนิค

21 ต.ค. 2537

การไฟฟ้าส่วนภูมิภาค

ผู้ว่าการ 25 ต.ค. 2537 ขวก.

การประกอบคอนกับเสาคอนกรีต 22 kV, 33 kV
2 วงจร
(กรณีพาดสายหุ้มฉนวนแบบไม่เต็มพิกัด (PIC))

22 kV, 33 kV CROSSARM ASSEMBLY ON CONCRETE POLE
2 CIRCUIT
(PARTIALLY INSULATED CONDUCTOR STRINGING)

ใช้แทนแบบ
ถูกแทนโดยแบบ
เขียนเสร็จวันที่ 11 ต.ค. 37
แก้แบบวันที่
มิติเป็น
มาตราส่วน

แบบเลขที่ SA4-015/37026
แผ่นที่ 7 ของจำนวน 9 แผ่น

การประกอบเลขที่ ASSEMBLY NO.	2321 or 3906

บัญชีวัสดุ
BILL OF MATERIAL

ลำดับที่ ITEM	รายละเอียด DESCRIPTION	จำนวน REQ'D								วัสดุเลขที่ MAT. NO.
		I	II	III	IV	V	VI	VII	VIII	
29	สายยึดโยงแบบ GY-21 หรือ GY-32 GUY ASSEMBLY, GY-21 OR GY-32	–	–	1	1	1	2	–	–	
30	สายยึดโยงแบบ GY-22 หรือ GY-32 GUY ASSEMBLY, GY-22 OR GY-32	–	–	–	1	–	–	–	–	
31	ทิมเบิลเคลวิส สำหรับปรีฟอร์มเข้าปลายสาย CLEVIS, THIMBLE, FOR PREFORMED DEADEND	–	–	–	6	–	3	–	–	03140011
32	ปรีฟอร์มเข้าปลายสาย สำหรับเคเบิลอากาศอะลูมิเนียม 22 kV, 33 kV ขนาดตามต้องการ PREFORMED DEADEND, FOR 22 kV, 33 kV AERIAL CABLE SIZE AS REQUIRED	–	–	–	6	–	3	–	–	02260000-4 02260100-4
33	เทปพันเคเบิลอากาศแรงสูง ขนาด 3/4" X 30' ELECTRICAL SPLICING TAPE, FOR H.T. AERIAL CABLE SIZE 3/4" X 30'	–	–	ม้วน roll	ม้วน roll	ม้วน roll	ม้วน roll	–	–	02180003
34	พี.จี. คอนเนคเตอร์ สำหรับสายอะลูมิเนียม ขนาดตามต้องการ CONNECTOR, PARALLEL GROOVE, Al; SIZE AS REQUIRED	–	–	–	–	–	–	6	–	02300102-4
35	สเตอร์รัพแคล้มป์ หรือ เบลแคล้มป์ และฮอทไลน์แคล้มป์ ขนาดตามต้องการ CLAMP, STIRRUP OR BAIL AND HOT LINE CLAMP; SIZE AS REQUIRED	–	–	–	–	–	–	–	3	02330100-1 02330000-1
	บัญชีวัสดุสำหรับติดตั้งสายล่อฟ้า BILL OF MATERIAL, FOR OHGW INSTALLATION									
36	เหล็กฉากรับสายล่อฟ้าทางตรง OVERHEAD GROUND WIRE BAYONET	1	–	–	–	–	–	–	–	01010003
37	เหล็กรูปรางน้ำรับสายล่อฟ้า ต้นเข้าปลายสาย OVERHEAD GROUND WIRE DEADEND BAYONET, CHANNEL STEEL	–	1	1	1	1	1	–	–	01000100
38	เหล็กรูปรางน้ำ ขนาด 100X50X5 มม. ยาว 2.25 ม. มอก. 116 เจาะรูตามแบบแผ่นที่ 6 STEEL, CHANNEL 100 X 50 X 5 mm, 2.25 m LONG, TIS 116; PUNCH HOLE AS DWG. ON SHEET NO. 6	–	–	–	–	–	–	1	1	01000100
39	สลักเกลียว M 16 X 250 มม. BOLT, MACHINE, M 16 X 250 mm	2	–	2	2	2	2	–	–	01110203
40	สลักเกลียว M 16 X 350 มม. BOLT, MACHINE, M 16 X 350 mm	–	2	–	–	–	–	2	2	01110205
41	สลักห่วงกลม M 16 X 200 มม. BOLT, ROUND EYE M 16 X 200 mm	–	–	1	1	1	1	1	1	01140001
42	นัทรูปห่วง M 16 DIN 582 NUT, EYE, M 16 DIN 582	–	–	1	1	–	–	–	–	01180001
43	แหวนสี่เหลี่ยมแบน 52X52X4.5 มม. รู Ø 18 มม. มอก. 258 WASHER, SQUARE, FLAT, 52 X 52 X 4.5 mm, HOLE Ø 18 mm, TIS 258	2	2	4	4	4	4	6	6	01180100
44	กราวด์วายร์แคล้มป์ แบบ J 1152 GROUND WIRE CLAMP, J 1152	1	1	–	–	–	–	–	–	01230205

กองวิศวกรรมไฟฟ้าและเครื่องกล
ฝ่ายวิศวกรรม

ผู้เขียน
ผู้สำรวจ
วิศวกร
หัวหน้าแผนก
ผู้อำนวยการกอง
ผู้อำนวยการฝ่าย

รองผู้ว่าการฝ่ายเทคนิค
21 ต.ค. 2537

การไฟฟ้าส่วนภูมิภาค

ผู้ว่าการ 25.ต.ค.2537

การประกอบคอนทับเสาคอนกรีต 22 kV, 33 kV
2 วงจร
(กรณีพาดสายหุ้มฉนวนแบบไม่เต็มพิกัด (PIC))

22 kV, 33 kV CROSSARM ASSEMBLY ON CONCRETE POLE
2 CIRCUIT
(PARTIALLY INSULATED CONDUCTOR STRINGING)

ใช้แทนแบบ
ถูกแทนโดยแบบ
เขียนเสร็จวันที่ 11 ต.ค. 37
แก้แบบวันที่
มิติเป็น
มาตราส่วน

แบบเลขที่ SA4-015/37026
แผ่นที่ 8 ของจำนวน 9 แผ่น

การประกอบเลขที่ 2321 or
ASSEMBLY NO. 3906

บัญชีวัสดุสำหรับติดตั้งสายล่อฟ้า (ต่อ)
BILL OF MATERIAL, FOR OHGW INSTALLATION (CONT.)

ลำดับที่ ITEM	รายละเอียด DESCRIPTION	จำนวน REQ'D								วัสดุเลขที่ MAT. NO.
		I	II	III	IV	V	VI	VII	VIII	
45	กราวด์วายร์แคล้มป์ สำหรับคอนสาย GROUND WIRE SUPPORT AND CLAMP, FOR WOOD BAYONET	–	–	–	–	–	–	1	1	01230200
46	กายทิมเบิล สำหรับสายยึดโยง 50-95 ต.มม. THIMBLE, GUY, FOR STEEL WIRE 50-95 mm^2	–	–	2	2	1	1	1	1	01210304
47	ยูแคล้มป์ สลัก 1 ตัว M 8 CLAMP, SINGLE U-BOLT, M 8	1	1	7	7	3	3	5	5	01230000

	แบบอ้างอิง REFERENCE DRAWING	แบบเลขที่ DWG. NO.	การประกอบเลขที่ ASSEMBLY NO.
1	โครงสร้างเสาระบบจำหน่าย 22 kV, 33 kV 2 วงจร 22 kV, 33 kV DISTRIBUTION POLE STRUCTURE, 2 CIRCUIT	IB1-015/37037	8246
2	การประกอบคอน คอร. กับเสาคอนกรีต ระบบ 22 kV SPUN PRESTRESSED CONCRETE CROSSARM ASSEMBLY 22 kV SYSTEM	SA1-015/21015	2802
3	การติดตั้งเคเบิลอากาศ ระบบ 22 kV 22 kV AERIAL CABLE INSTALLATION	S02-015/19162 S02-015/16021	2301 2302
4	หลักของการก่อสร้างระบบจำหน่าย 22 kV, 33 kV (เฉพาะแบบเหนือดิน) PRICIPLES OF 22 kV, 33 kV DISTRIBUTION CONSTRUCTION (OVERHEAD LINE ONLY)	SA4-015/37001 SA4-015/37017	9503 9505
5	การต่อสายเคเบิลอากาศแรงสูง COMPRESSION SLEEVE, FOR H.T. AERIAL CABLE	SA1-015/22020	9562
6	การต่อปลายสายลวดเหล็กตีเกลียว STEEL STRANDED WIRE SPLICING	SA1-015/23053 SA1-015/28010	9563 9563A
7	การประกอบสายลงดิน วิธีรัดลวดเหล็ก GROUND LEAD ASSEMBLY, STEEL WIRE FITTING	S02-015/19166 SA1-015/31012	9703 9703A

กองวิศวกรรมไฟฟ้าและเครื่องกล
ฝ่ายวิศวกรรม

ผู้เขียน
ผู้สำรวจ
วิศวกร
หัวหน้าแผนก
ผู้อำนวยการกอง
ผู้อำนวยการฝ่าย

รองผู้ว่าการฝ่ายเทคนิค

21 ต.ค. 2537

การไฟฟ้าส่วนภูมิภาค

ผู้ว่าการ 25 ต.ค. 2537

การประกอบคอนกับเสาคอนกรีต 22 kV, 33 kV
2 วงจร
(กรณีพาดสายหุ้มฉนวนแบบไม่เต็มพิกัด (PIC))

22 kV, 33 kV CROSSARM ASSEMBLY ON CONCRETE POLE
2 CIRCUIT
(PARTIALLY INSULATED CONDUCTOR STRINGING)

ใช้แทนแบบ
ถูกแทนโดยแบบ
เขียนเสร็จวันที่ 11 ต.ค. 37
แก้แบบวันที่
ผิดเป็น
มาตราส่วน
แบบเลขที่ SA4-015/37026
แผ่นที่ 9 ของจำนวน 9 แผ่น