การประกอบเลขที่
ASSEMBLY NO. 0207

N – สายเป็นกลาง
NEUTRAL LINE

A,B,C – สายเฟส
PHASE LINE

L – สายดับไฟถนน
STREET LIGHTING LINE

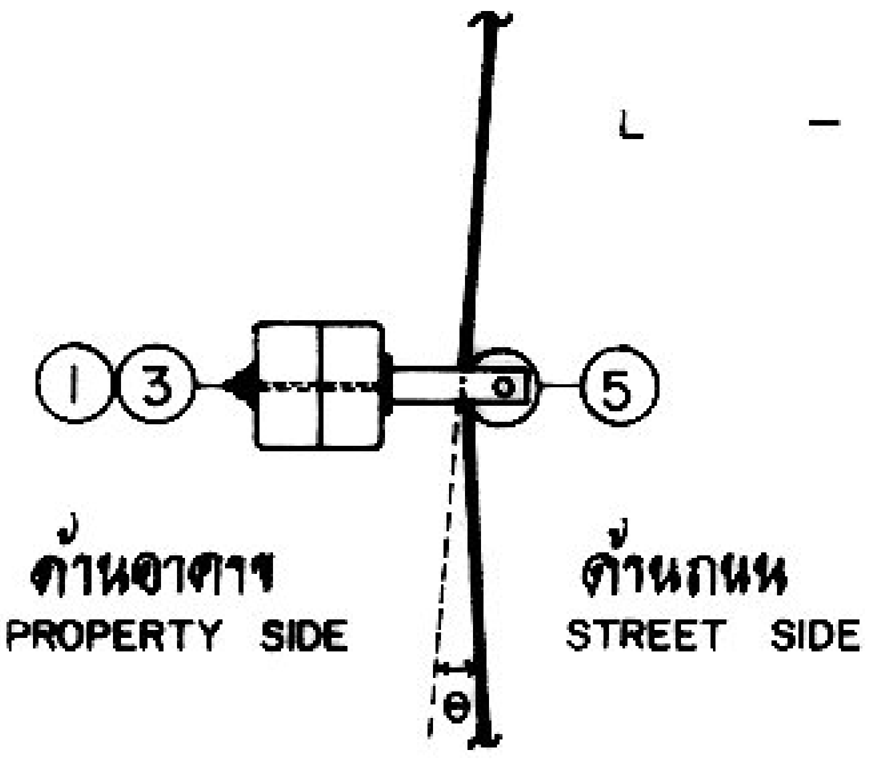
①③
⑤
ด้านอาคาร
PROPERTY SIDE
ด้านถนน
STREET SIDE
θ

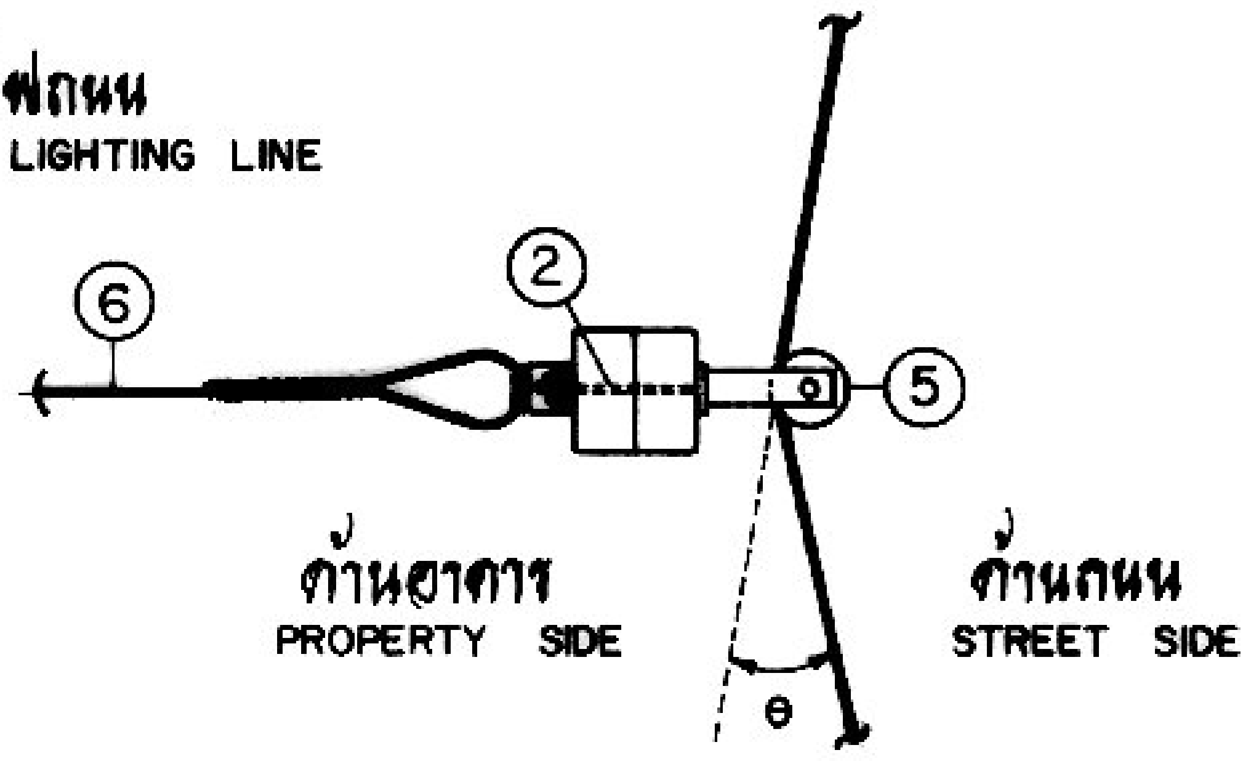
⑥
②
⑤
ด้านอาคาร
PROPERTY SIDE
ด้านถนน
STREET SIDE
θ

## แบบ 3 เฟส 4 สาย
## 3-PHASES 4-WIRE

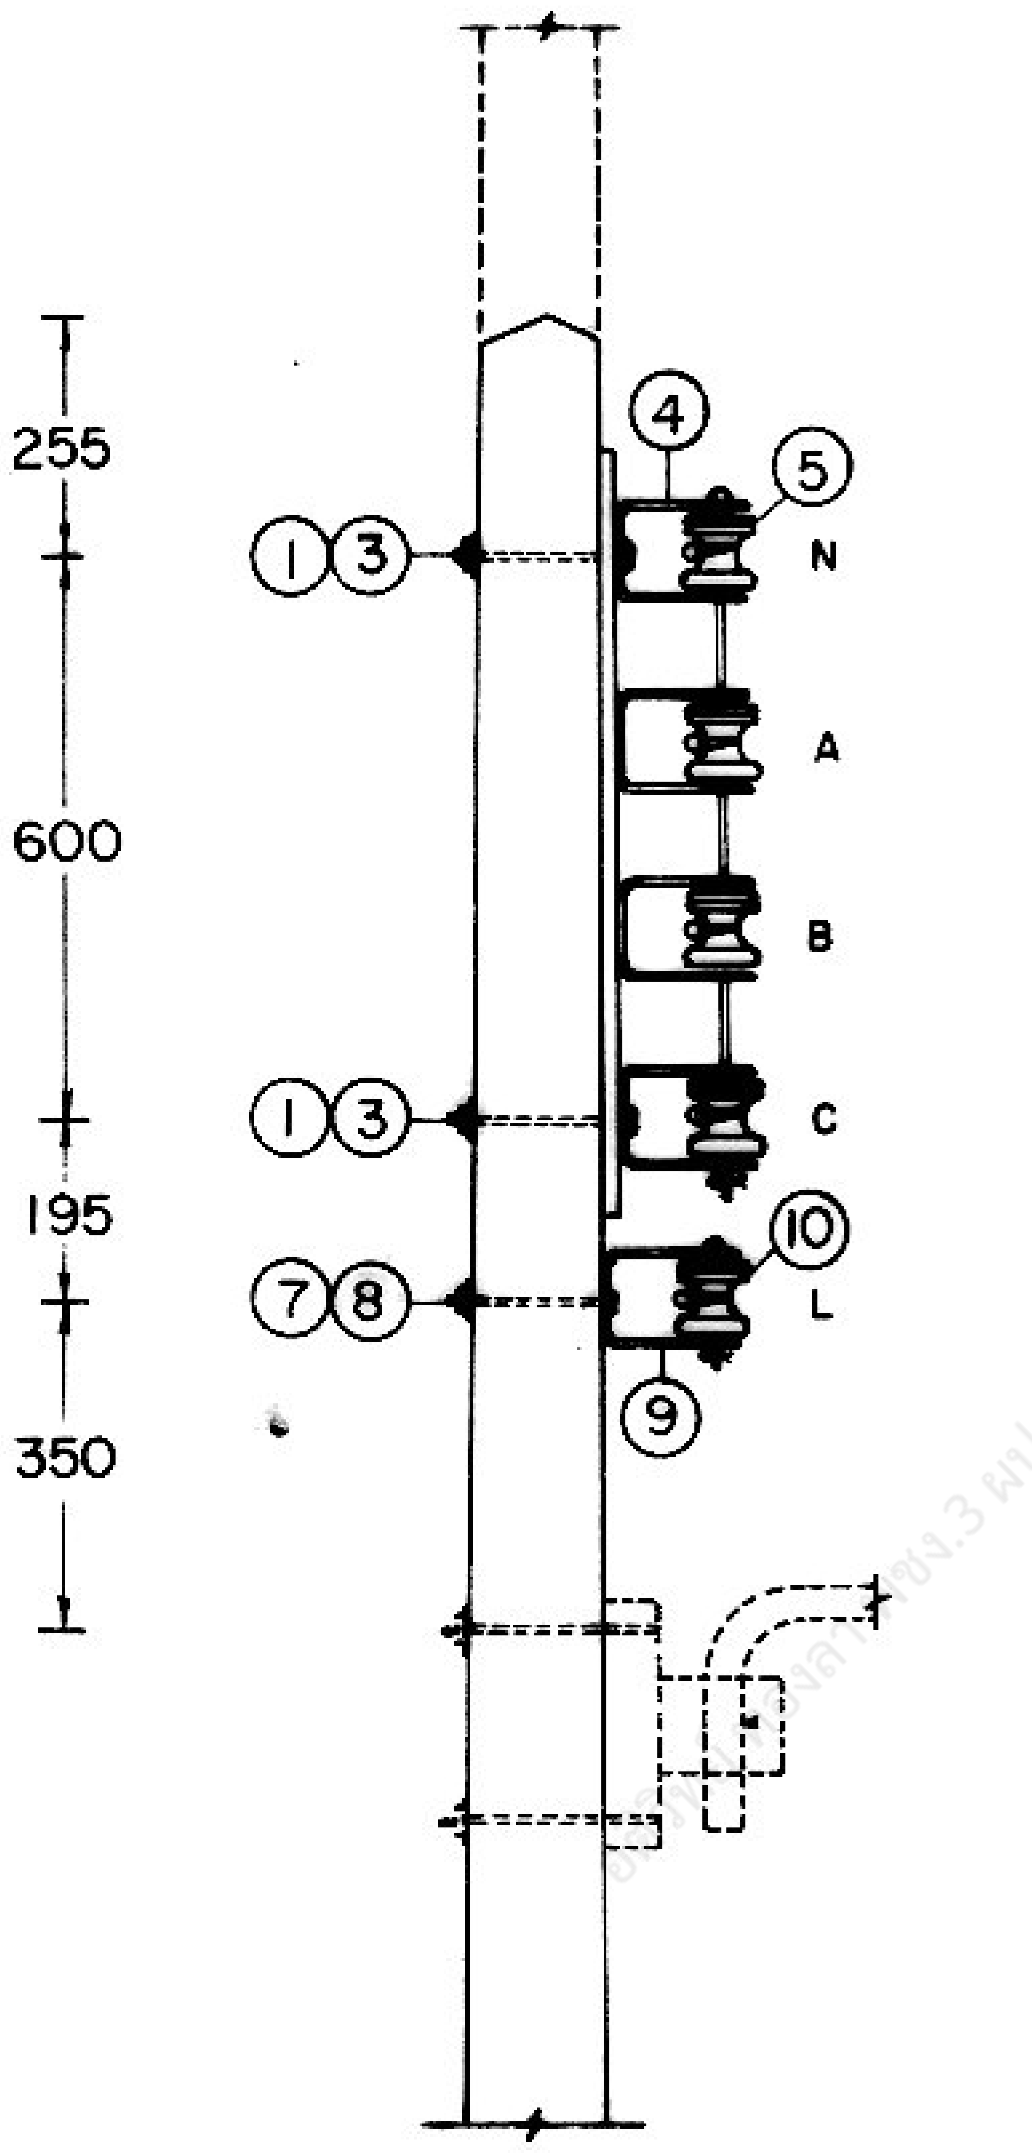
255
600
195
350
①③
①③
⑦⑧
④
⑤
N
A
B
C
⑩
L
⑨

สำหรับทางตรง 0°-5° (θ)
FOR TANGENT STRUCTURE 0°-5° (θ)

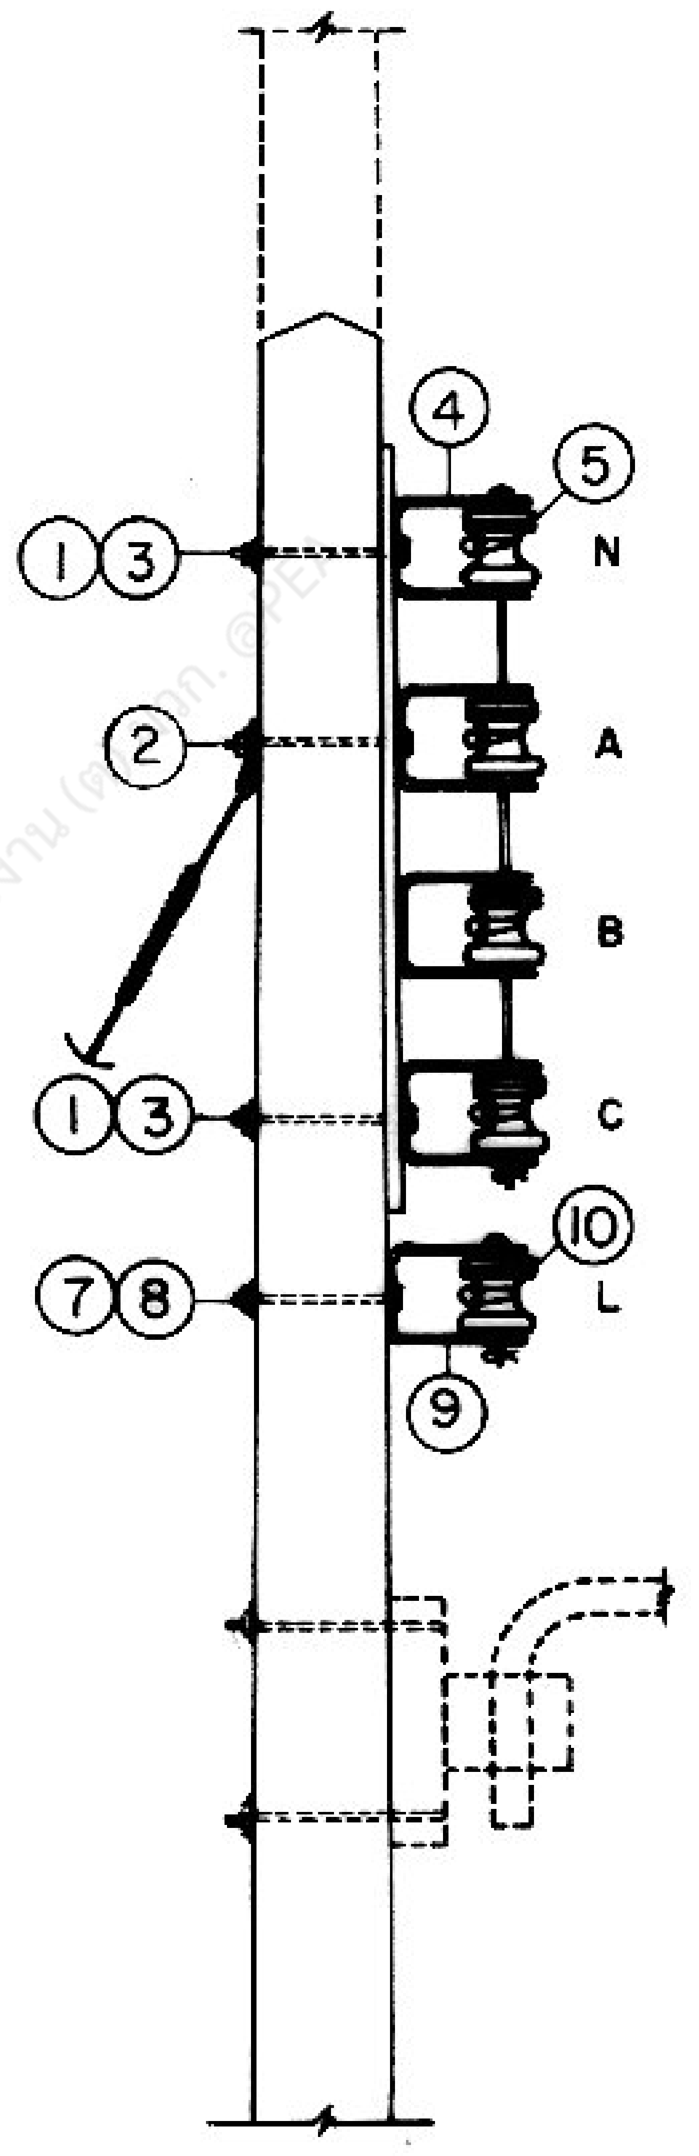
①③
②
①③
⑦⑧
④
⑤
N
A
B
C
⑩
L
⑨

สำหรับทางโค้ง 5°-60° (θ)
FOR ANGLE STRUCTURE 5°-60° (θ)

กองวิศวกรรมไฟฟ้าและเครื่องกล
ฝ่ายวิศวกรรม

ผู้เขียน
ผู้สำรวจ
วิศวกร
หัวหน้าแผนก
หัวหน้ากอง
ผู้อำนวยการฝ่าย
รองผู้ว่าการฝ่ายเทคนิค

21 เม.ย. 2521

# การไฟฟ้าส่วนภูมิภาค

ผู้ว่าการ 24 เม.ย. 21.

การติดตั้งแร็คแรงต่ำกับเสาคอนกรีต 9 ม.
สำหรับทางตรง 0°-5° และ สำหรับทางโค้ง 5°-60°

SECONDARY RACK INSTALLATION ON 9 m CONCRETE POLE
FOR TANGENT STRUCTURE 0°-5° & ANGLE STRUCTURE 5°-60°

ใช้แทนแบบ
ถูกแทนโดยแบบ
เขียนเสร็จวันที่ 14 เม.ย. 21
แก้แบบวันที่
มิติเป็น มม.
มาตราส่วน 1 : 20
แบบเลขที่ SAI-015/21028
แผ่นที่ 1 ของจำนวน 2 แผ่น

การประกอบเลขที่ ASSEMBLY NO. 0207

## บัญชีวัสดุ
## BILL OF MATERIAL

| ลำดับที่<br>ITEM | รายละเอียด<br>DESCRIPTION | จำนวน REQ'D<br>0°-5° | <br>5°-60° | วัสดุเลขที่<br>MAT. NO. |
|---|---|---|---|---|
| 1 | สลักเกลียว M 16 X 170 มม.<br>BOLT, MACHINE, M 16 X 170 mm | 2 | 2 | 01110201 |
| 1a | สลักเกลียว M 16 X 250 มม. สำหรับเสาคอนกรีต 12 ม.<br>BOLT, MACHINE, M 16 X 250 mm FOR 12 m CONCRETE POLE | 2 | 2 | 01110203 |
| 2 | สลักเกลียว M 16 X 200 มม.<br>BOLT, MACHINE, M 16 X 200 mm | – | 1 | 01110202 |
| 2a | สลักเกลียว M 16 X 300 มม. สำหรับเสาคอนกรีต 12 ม.<br>BOLT, MACHINE, M 16 X 300 mm FOR 12 m CONCRETE POLE | – | 1 | 01110204 |
| 3 | แหวนสี่เหลี่ยมแบน 52 X 52 X 4.5 มม. รู Ø 18 มม. มอก. 258<br>WASHER, SQUARE FLAT 52 X 52 X 4.5 mm HOLE Ø 18 mm TIS 258 | 2 | 2 | 01180100 |
| 4 | แร็ค 4 X 200 มม. แบบหลังยื่น<br>RACK, SECONDARY, MEDIUM PRESSED STEEL 4 X 200 mm EXT. BACK | 1 | 1 | 03130002 |
| 5 | ลูกรอกแรงต่ำ มอก. 227 แบบ ข (แบบ 53-2)<br>INSULATOR, SPOOL TYPE, L.T. TIS 227 TYPE B (CLASS 53-2) | 4 | 4 | 03030000 |
| 6 | การประกอบสายยึดโยง GY-01<br>GUY ASSEMBLY GY-01 | – | 1 | – |
| 6a | การประกอบสายยึดโยง GY-02 สำหรับเสาคอนกรีต 12 ม<br>GUY ASSEMBLY GY-02 FOR 12 m CONCRETE POLE | – | 1 | – |
| | สำหรับการติดตั้งไฟถนน<br>FOR STREET LIGHTING INSTALLATION | | | |
| 7 | สลักเกลียว M 16 X 170 มม.<br>BOLT, MACHINE, M 16 X 170 mm | 1 | 1 | 01110201 |
| 7a | สลักเกลียว M 16 X 250 มม. สำหรับเสาคอนกรีต 12 ม.<br>BOLT, MACHINE, M 16 X 250 mm FOR 12 m CONCRETE POLE | 1 | 1 | 01110203 |
| 8 | แหวนสี่เหลี่ยมแบน 52 X 52 X 4.5 มม. รู Ø 18 มม. มอก. 258<br>WASHER, SQUARE FLAT 52 X 52 X 4.5 mm HOLE Ø 18 mm TIS 258 | 1 | 1 | 01180100 |
| 9 | ที่จับลูกรอก สำหรับลูกรอก มอก. 227 (แบบ 53-2)<br>CLEVIS, FLAT STEEL, FOR INSULATOR TIS 227 (CLASS 53-2) | 1 | 1 | 03130001 |
| 10 | ลูกรอกแรงต่ำ มอก. 227 แบบ ข (แบบ 53-2)<br>INSULATOR, SPOOL TYPE, L.T. TIS 227 TYPE B (CLASS 53-2) | 1 | 1 | 03030000 |

กองวิศวกรรมไฟฟ้าและเครื่องกล
ฝ่ายวิศวกรรม

ผู้เขียน
ผู้ตรวจ
วิศวกร
หัวหน้าแผนก
หัวหน้ากอง
ผู้อำนวยการฝ่าย
รองผู้ว่าการฝ่ายเทคนิค
21 เม.ย. 2521

# การไฟฟ้าส่วนภูมิภาค

ผู้ว่าการ 24 เม.ย. 21

การติดตั้งแร็คแรงต่ำกับเสาคอนกรีต 9 ม.
สำหรับทางตรง 0°-5° และ สำหรับทางโค้ง 5°-60°

SECONDARY RACK INSTALLATION ON 9 m CONCRETE POLE
FOR TANGENT STRUCTURE 0°-5° & ANGLE STRUCTURE 5°-60°

ใช้แทนแบบ
ถูกแทนโดยแบบ
เขียนเสร็จวันที่ 14 เม.ย. 21
แก้แบบวันที่
มิติเป็น
มาตราส่วน
แบบเลขที่ SAI-015/21028
แผ่นที่ 2 ของจำนวน 2 แผ่น