

การประกอบเลขที่ ASSEMBLY NO. 5229

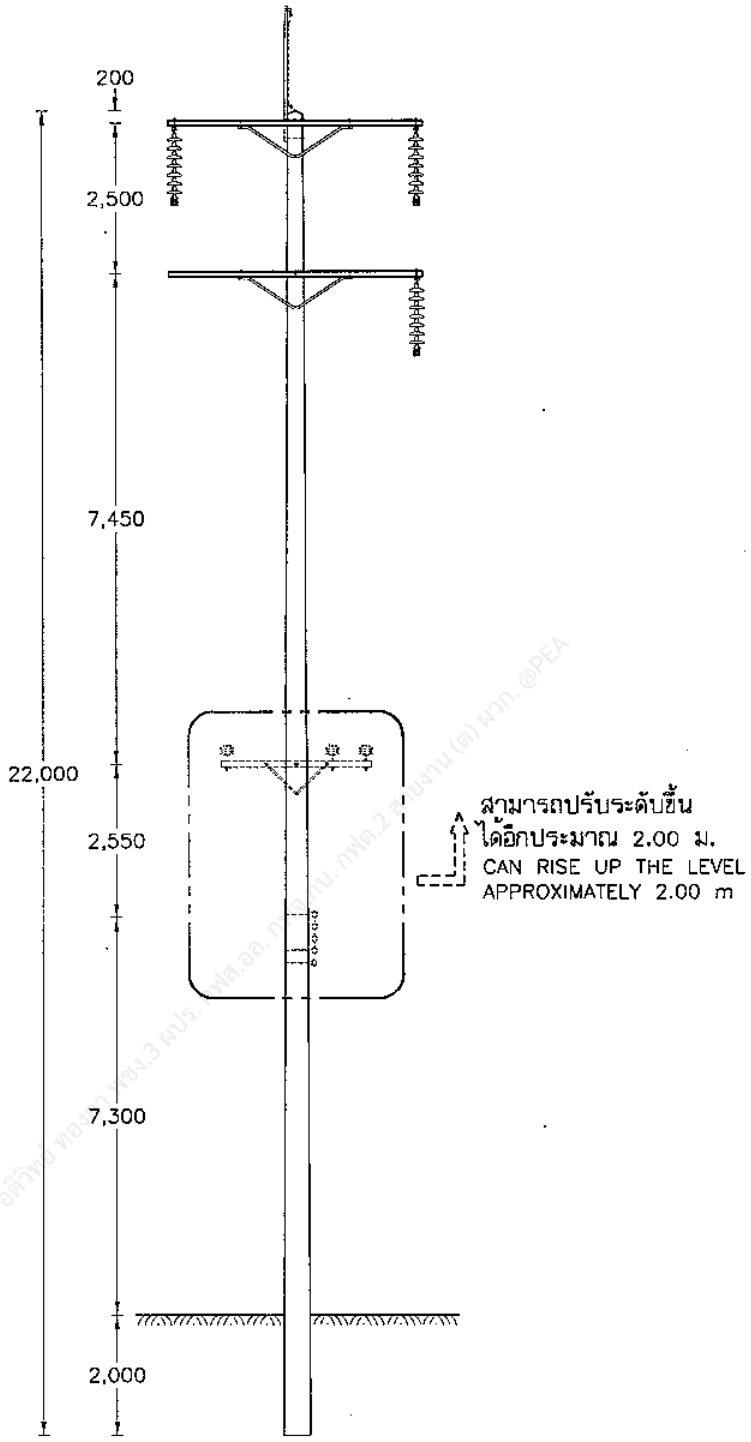

กองวิศวกรรมไฟฟ้าและเครื่องกล ฝ่ายวิศวกรรม	การไฟฟ้าส่วนภูมิภาค	ใช้แทนแบบ ..... ถูกแทนโดยแบบ .....
ผู้เขียน ..... ผู้สำรวจ ..... วิศวกร ..... หัวหน้าแผนก ..... ผู้อำนวยการกอง ..... ผู้อำนวยการฝ่าย	ผู้ว่าการ ..... - 3 มี.ค. 2542	เขียนเสร็จวันที่ 22 ก.พ. 2542 แก้แบบวันที่ .....
	115 kV วงจรเดี่ยว สายไฟฟ้าเดี่ยว เสาสำหรับทางตรง แบบ SS-TG-8	มิติเป็น มิลลิเมตร มาตราส่วน 1 : 125
รองผู้ว่าการเทคนิคและบริการ	115 kV SINGLE CIRCUIT, SINGLE CONDUCTOR TANGENT STRUCTURE TYPE SS-TG-8	แบบเลขที่ SA1-015/42002 แผ่นที่ 1 ของจำนวน 3 แผ่น

- 3 มี.ค. 2542

การประกอบเลขที่ ASSEMBLY NO. 5229

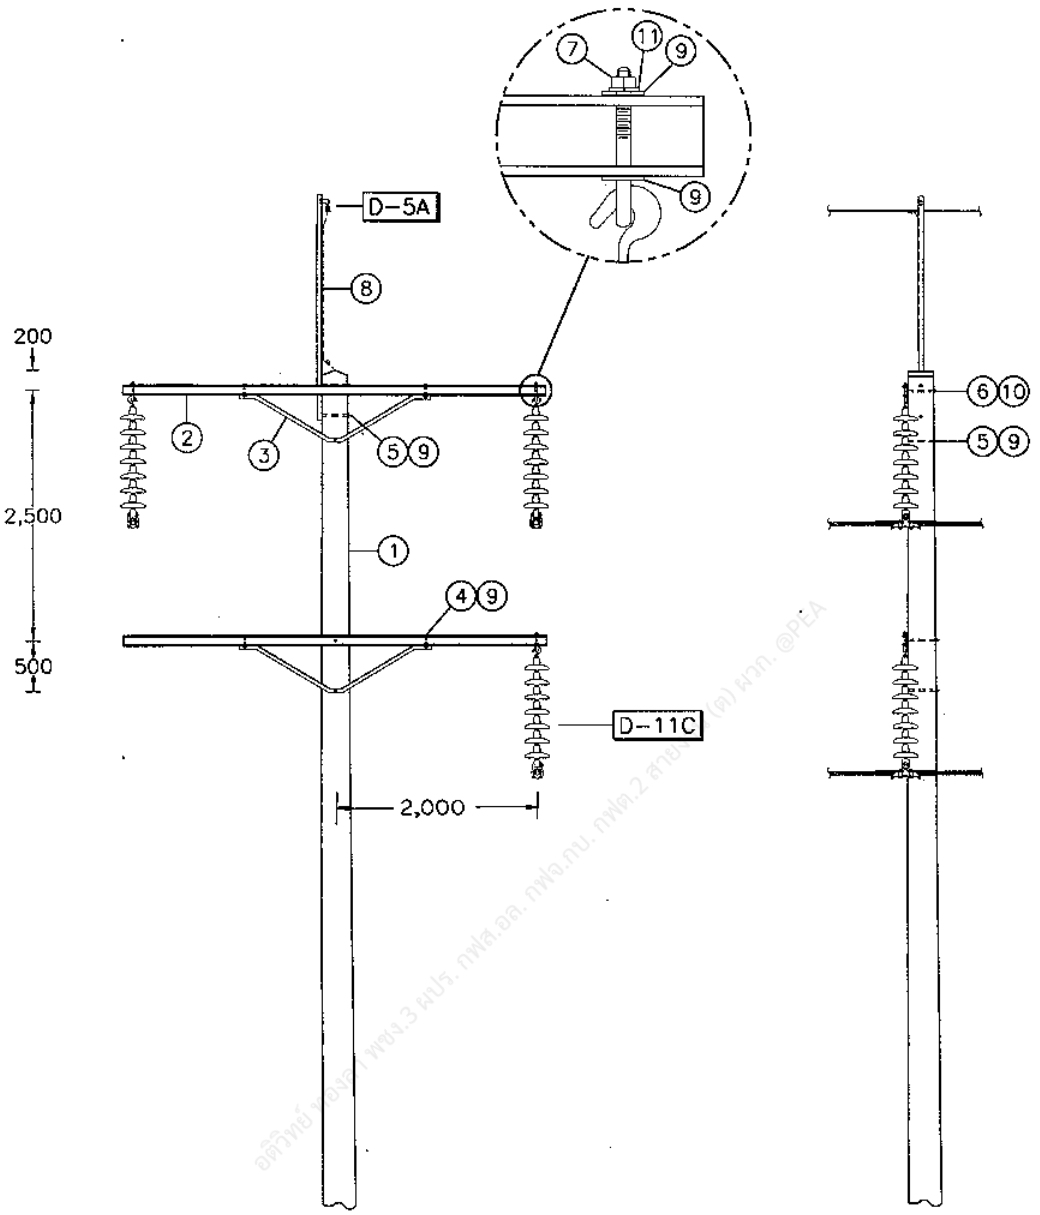

กองวิศวกรรมไฟฟ้าและเครื่องกล ฝ่ายวิศวกรรม	การไฟฟ้าส่วนภูมิภาค	ใช้แทนแบบ ..... ถูกแทนโดยแบบ .....
ผู้เขียน ..... ผู้สำรวจ ..... วิศวกร ..... หัวหน้าแผนก ..... ผู้อำนวยการกอง ..... ผู้อำนวยการฝ่าย	ผู้ว่าการ ..... - 3 ธ.ค. 2542 ..... 115 kV วงจรเดี่ยว สายไฟฟ้าเดี่ยว เสาสำหรับทางตรง แบบ SS-TG-8	เขียนเสร็จวันที่ 22 ก.พ. 2542 แก้แบบวันที่ ..... มิติเป็น มิลลิเมตร มาตราส่วน 1 : 75
รองผู้ว่าการเทคนิคและบริการ	115 kV SINGLE CIRCUIT, SINGLE CONDUCTOR TANGENT STRUCTURE TYPE SS-TG-8	แบบเลขที่ SA1-015/42002 แผ่นที่ 2 ของจำนวน 3 แผ่น

- 3 ธ.ค. 2542

การประกอบเลขที่ ASSEMBLY NO. 5229

บัญชีวัสดุ
BILL OF MATERIAL

ลำดับที่ ITEM	รายละเอียด DESCRIPTION	จำนวน REQ'D	วัสดุเลขที่ MAT. NO.
1	เสาคอนกรีต 22 ม. POLE, CONCRETE 22 m LONG	1	00010011
2	คอนสายแบบเหล็กรูปรางน้ำ 100x50x5 มม. ยาว 4.20 ม. มอก. 116 CROSSARM, STEEL, CHANNEL 100x50x5 mm, 4.20 m LONG, TIS 116	2	01000103
3	เหล็กฉากรับคอนสายขนาด 50x50x6 มม. ช่วงกว้าง 1,800 มม. ดรอพ 450 มม. BRACE, ANGLE STEEL, 50X50X6 mm, 1,800 mm WIDE 450 mm DROP	2	00120007
4	สลักเกลียว M 16x130 มม. BOLT, MACHINE M 16x130 mm	4	01110200
5	สลักเกลียว M 16x350 มม. BOLT, MACHINE M 16x350 mm	5	01110206
6	สลักเกลียว M 20x400 มม. BOLT, MACHINE M 20x400 mm	2	01110301
7	สลักหวงโอ่แวล M 16x150 มม. BOLT, OVAL EYE M 16x150 mm	3	01150000
8	เหล็กฉากรับสายลอฟ้าทางตรง ยาว 2.50 ม. OVERHEAD GROUND WIRE BAYONET 2.50 m LONG	1	01010004
9	แหวนสี่เหลี่ยมแบน 52x52x4.5 มม. รู ø18 มม. มอก. 258 WASHER, SQUARE FLAT 52x52x4.5 mm HOLE ø18 mm TIS 258	14	01180100
10	แหวนสี่เหลี่ยมแบน 62x62x6 มม. รู ø22 มม. มอก. 258 WASHER, SQUARE FLAT 62x62x6 mm HOLE ø22 mm TIS 258	2	01180101
11	แหวนสปริง M 16 มอก. 259 WASHER, LOCK M 16 TIS 259	3	01180301

รายละเอียด
DETAIL

D-11C	การประกอบลูกถ้วยแขวน SUSPENSION INSULATOR ASSEMBLY	3	
D-5A	การต่อสายลอฟ้า OVERHEAD GROUND WIRE CONNECTION	1	
D-10A*	ฐานรากเสา POLE FOUNDATION	1	

* สามารถเปลี่ยนได้ตามความเหมาะสม
* CAN BE CHANGEDTO BE SUITABLE

กองวิศวกรรมไฟฟ้าและเครื่องกล
ฝ่ายวิศวกรรม

ผู้เขียน ...
ผู้สำรวจ ...
วิศวกร ...
หัวหน้าแผนก ...
ผู้อำนวยการกอง ...
ผู้อำนวยการฝ่าย ...

รองผู้ว่าการเทคนิคและบริการ
...

การไฟฟ้าส่วนภูมิภาค

ผู้ว่าการ ...
- 3 มิ.ย. 2542

115 kV วงจรเดี่ยว สายไฟฟ้าเดี่ยว
เสาสำหรับทางตรง
แบบ SS-TG-8

115 kV SINGLE CIRCUIT, SINGLE CONDUCTOR
TANGENT STRUCTURE
TYPE SS-TG-8

ใช้แทนแบบ .....
ถูกแทนโดยแบบ .....
เขียนเสร็จวันที่ 22 ก.พ. 2542
แก้แบบวันที่ .....
มิติเป็น .....
มาตราส่วน .....

แบบเลขที่ SA1-015/42002
แผ่นที่ 3 ของจำนวน 3 แผ่น

- 3 มิ.ย. 2542