การประกอบเลขที่
ASSEMBLY NO. 3203

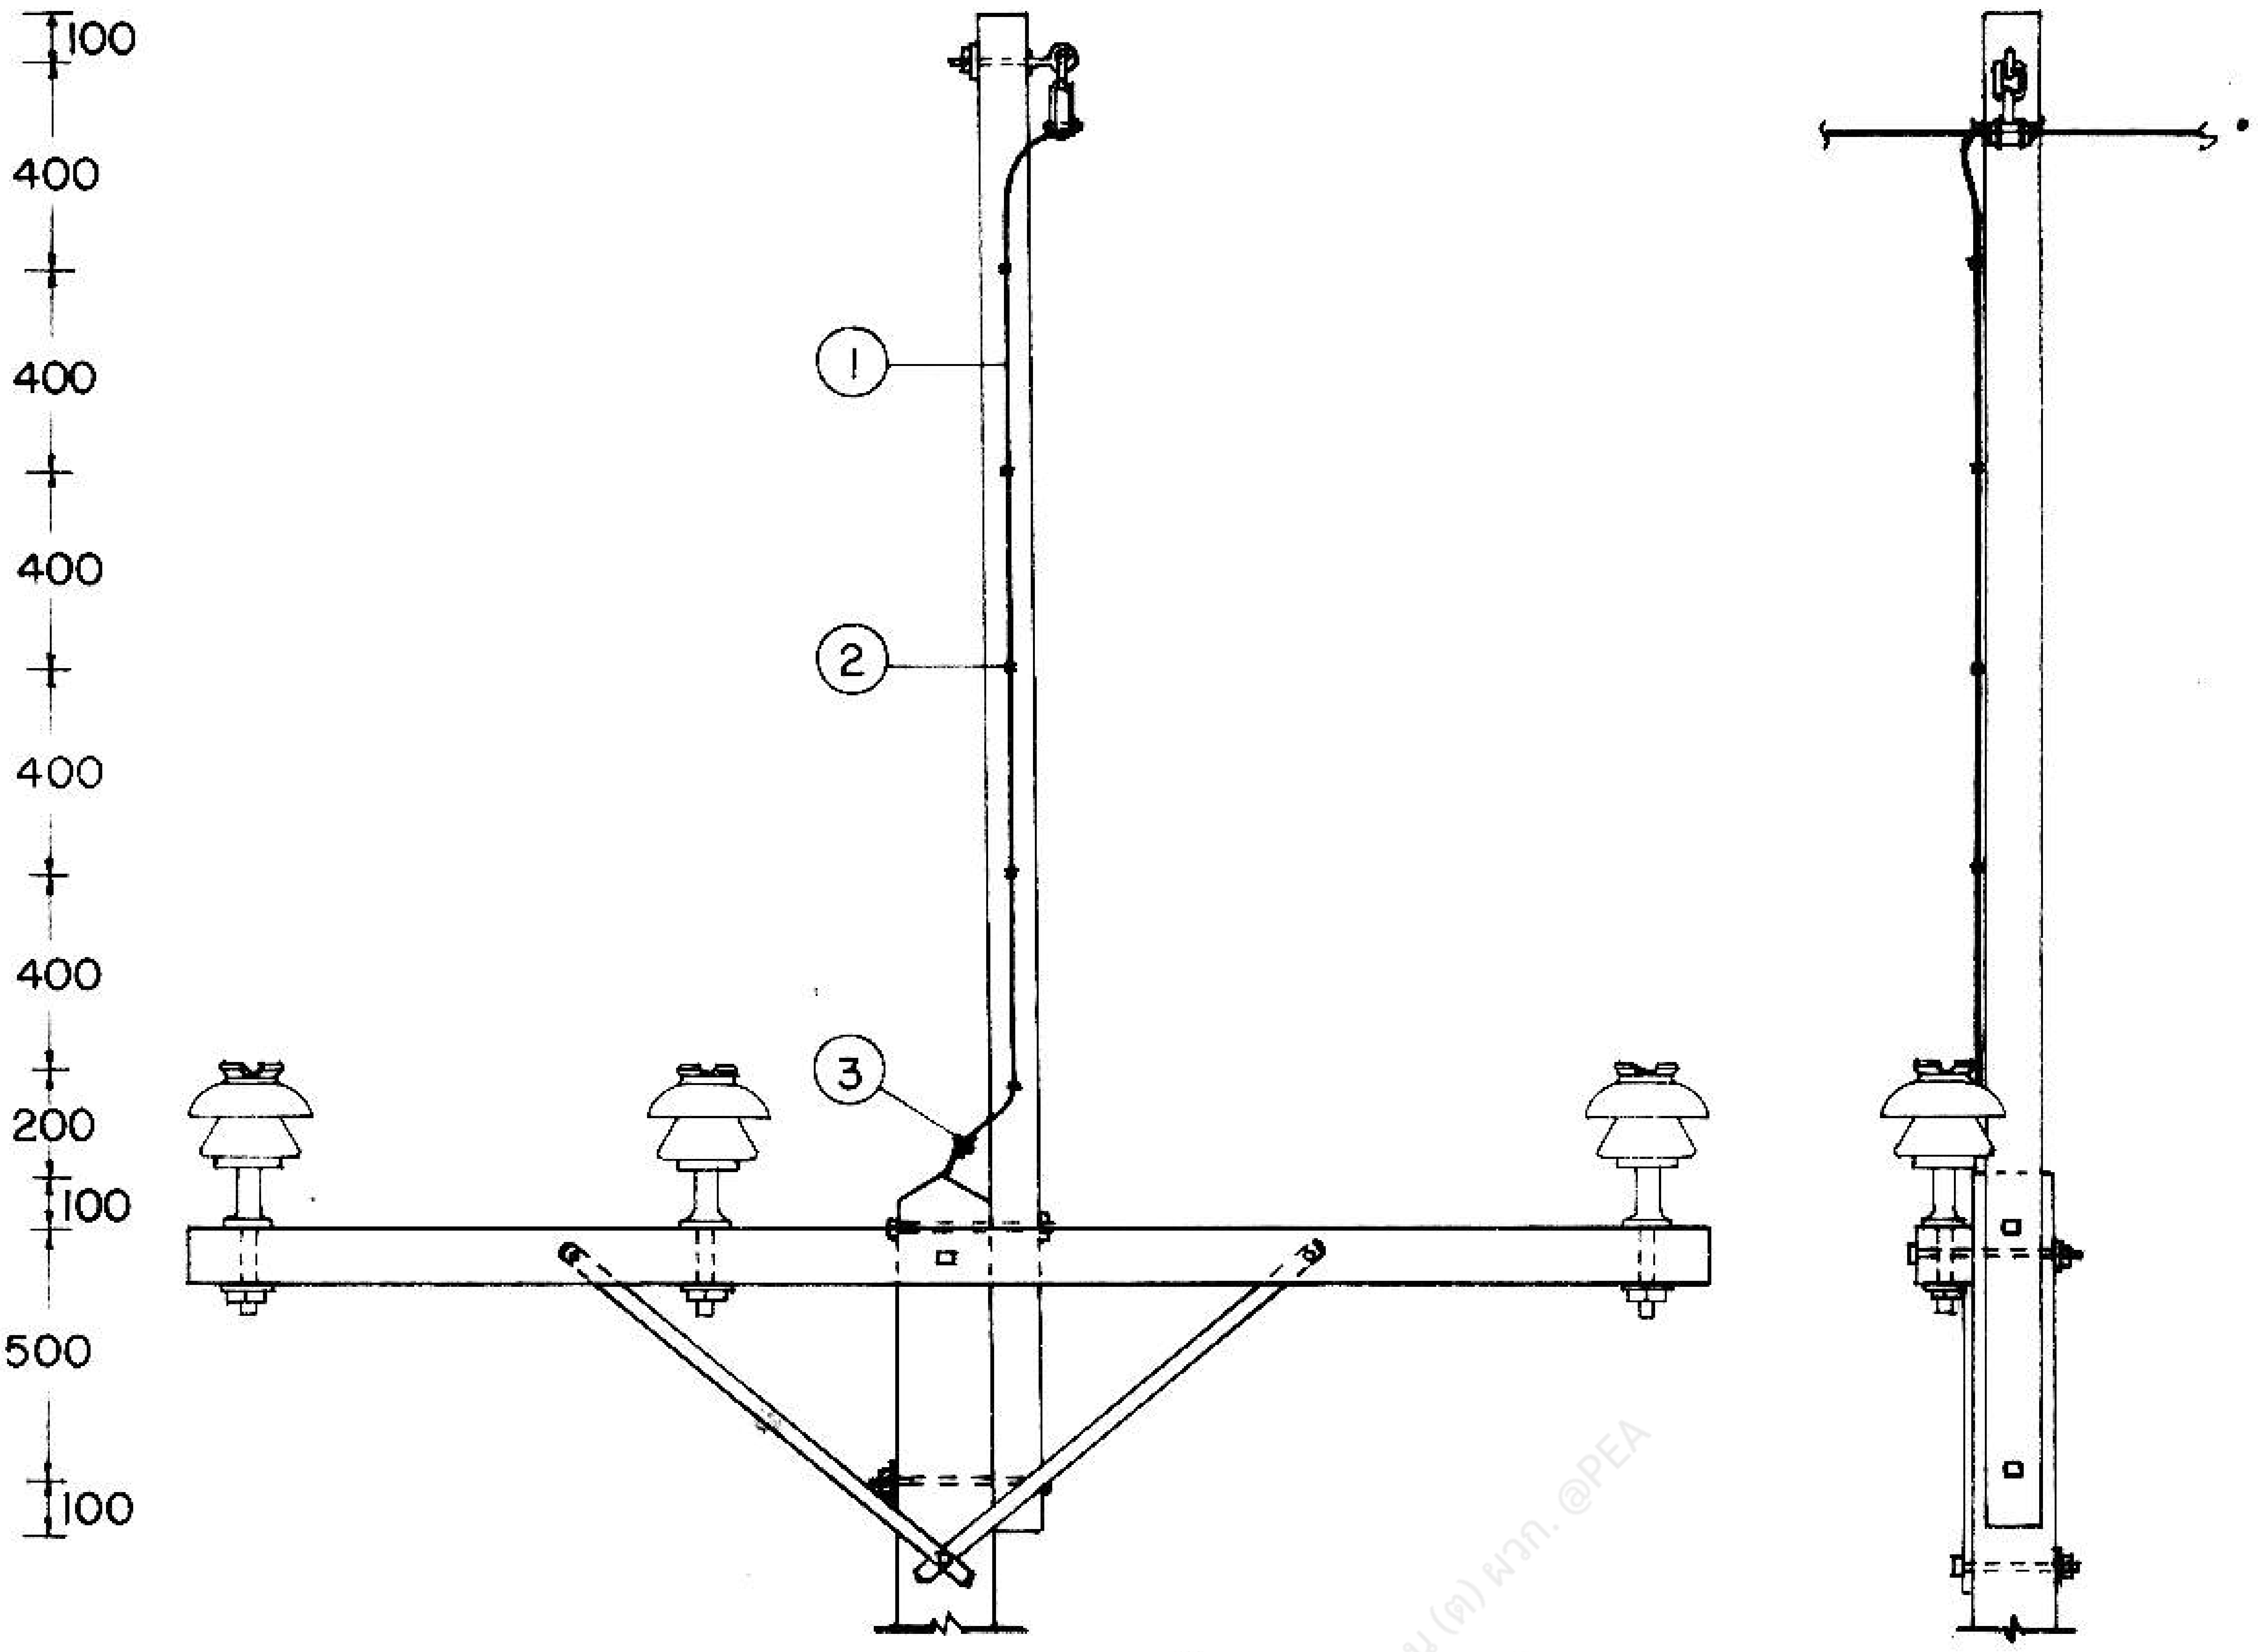

ก สำหรับไม้คอนรับล่อฟ้า
A FOR CROSSARM WOOD BAYONET

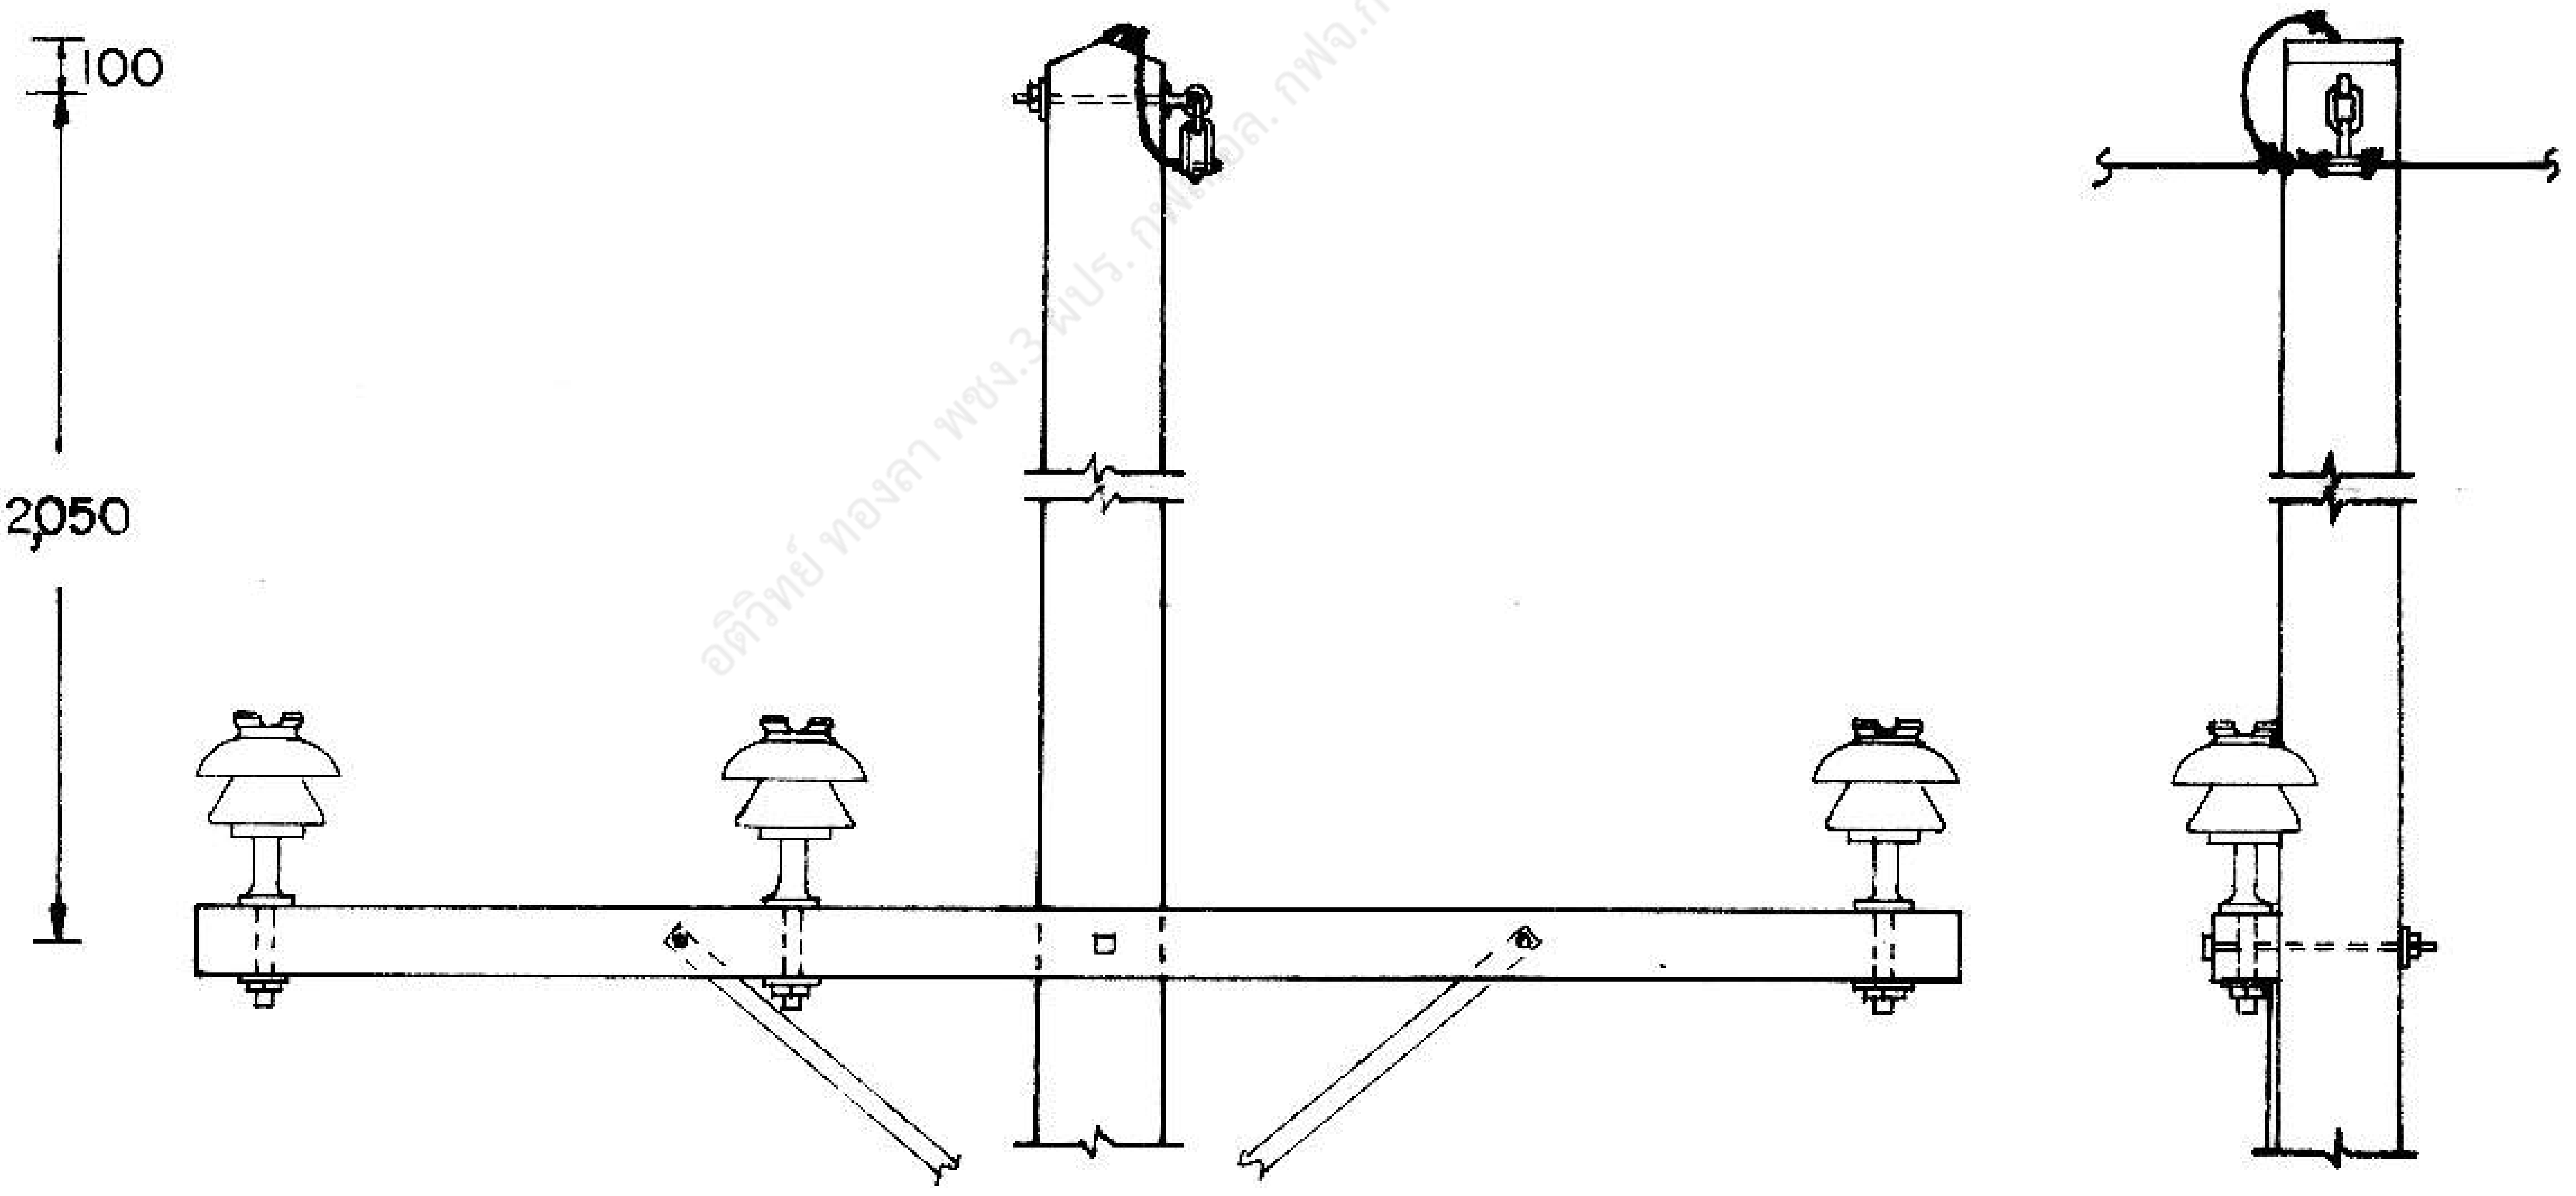

ข สำหรับเสาคอนกรีต 14 เมตร
B FOR 14 m CONCRETE POLE

กองวิศวกรรม

ผู้เขียน อนันต์ [illegible]
สถาปนิก
วิศวกร
หัวหน้าแผนก
ผู้อำนวยการกอง
รองผู้ว่าการสายเทคนิค

การไฟฟ้าส่วนภูมิภาค

ผู้ว่าการ

การต่อสายล่อฟ้า และสายดิน
ระบบ 33 kV

CONNECTION BETWEEN OVERHEAD GROUND WIRE
AND GROUND LEAD, 33 kV SYSTEM

ใช้แทนแบบ
ถูกแทนโดยแบบ
เขียนเสร็จวันที่ 13 พ.ค. 17
แก้แบบวันที่
มิติเป็น มม.
มาตราส่วน 1 : 30
แบบเลขที่ S02-015/17026
แผ่นที่ 1 ของจำนวน 2 แผ่น

การประกอบเลขที่
ASSEMBLY NO. **3203**

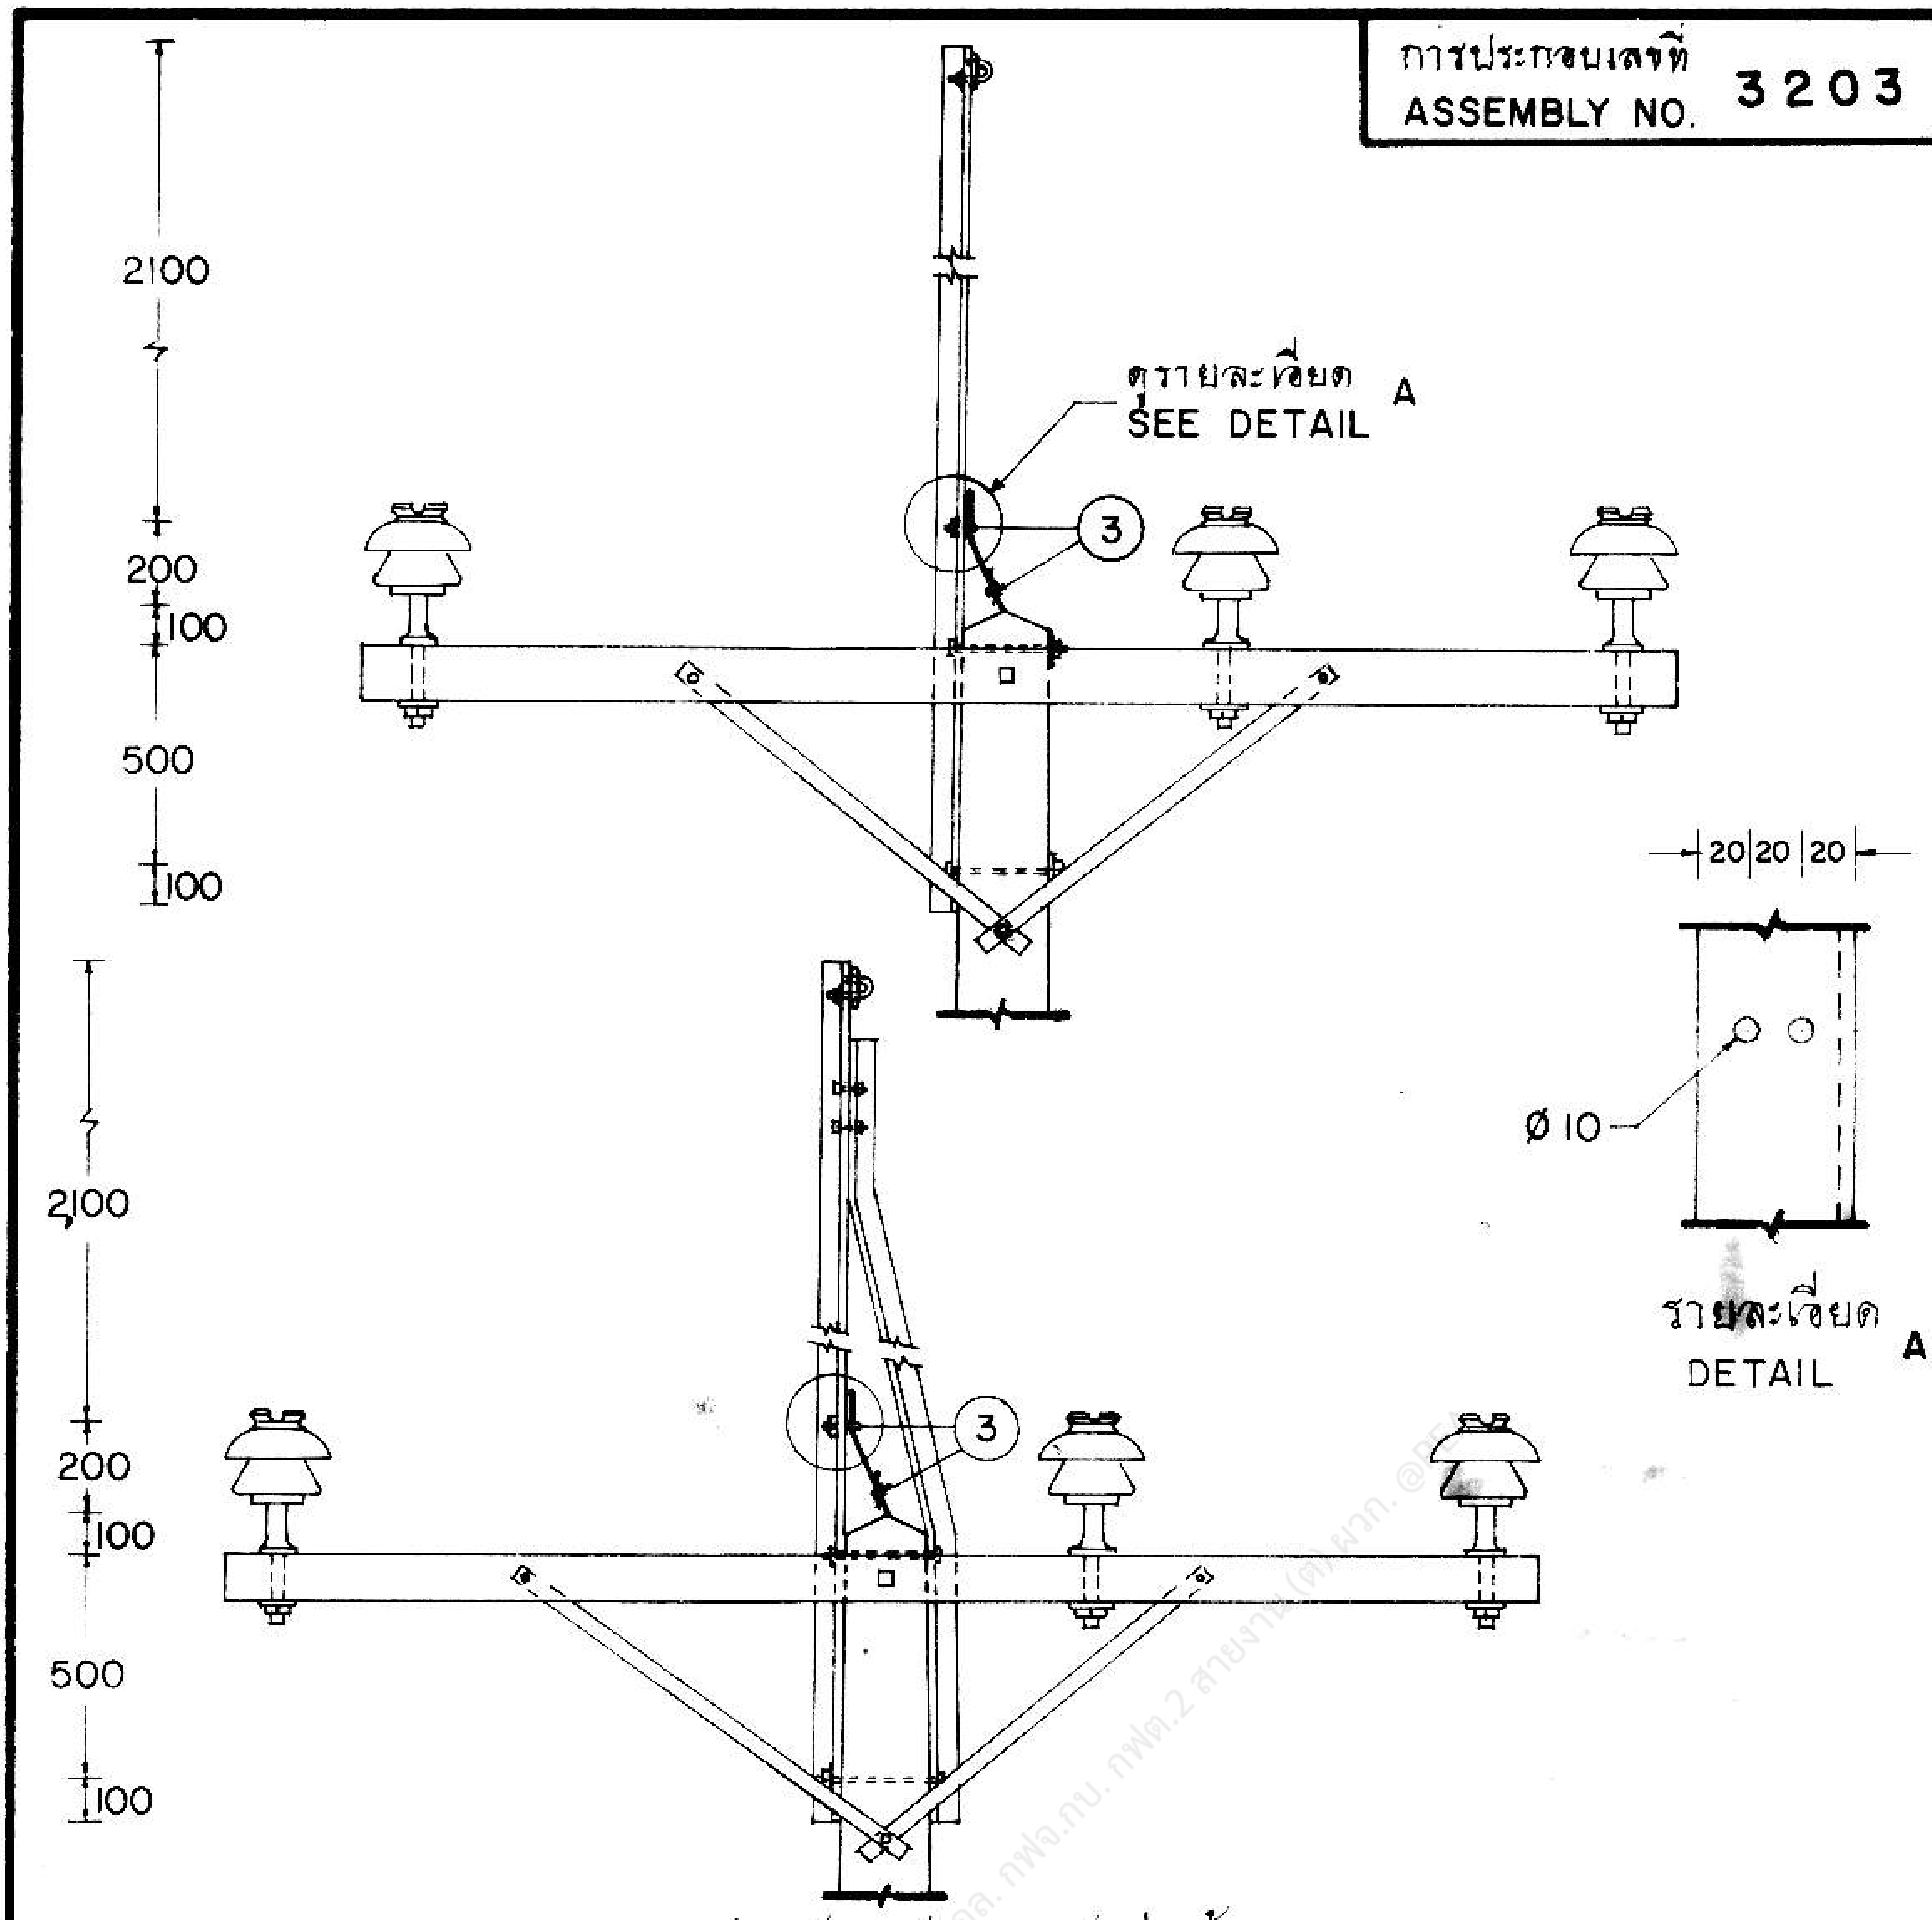

ค สำหรับเหล็กฉากรับล่อฟ้า
C FOR RIGHT ANGLE STEEL BAYONET

บัญชีวัสดุ
BILL OF MATERIAL

ลำดับที่ ITEM	รายละเอียด DESCRIPTION	จำนวน REQ'D ก/A	จำนวน REQ'D ค/C	วัสดุเลขที่ MAT. NO.
1	ลวดเหล็กกลม เส้นผ่าศูนย์กลาง 4 มม. มอก. 71–2517 WIRE, STEEL, SOLID DIAMETER 4 mm TIS 71–2517	2.5 ม. m	—	01100000 (0191)
2	ตะปู 2 ขา สำหรับสายกลม 25-50 ต.มม. STAPLE GALV, FOR ROUND CONDUCTOR 25-50 mm^2	5	—	01990003 (0393) or 01990004 (0394)
3	ยูแคล้มป์ สลัก 1 ตัว M 8 (ไวโรปคลิป) CLAMP, SINGLE U-BOLT M 8 (WIRE ROPE CLIP)	1	2	01230000 (0165)

หมายเหตุ ให้ต่อสายล่อฟ้าลงดิน ที่ทุกๆต้นเสาในกรณีเสาคอนกรีต หรือทุกๆระยะ 300 ม. ในกรณีเสาไม้
NOTE OVERHEAD GROUND WIRES SHALL BE EARTHED AT EACH POLE FOR CONCRETE POLE OR AT LEAST EVERY 300 m FOR WOOD POLE.

กองวิศวกรรม

การไฟฟ้าส่วนภูมิภาค

ผู้เขียน อนันต์ ตรุษศเวชพันธ์
สำเนาบนผ้า
วิศวกร
หัวหน้าแผนก
ผู้อำนวยการกอง
รองผู้ว่าการฝ่ายเทคนิค

ผู้ว่าการ

การต่อสายล่อฟ้า และสายดิน
ระบบ 33 kV

CONNECTION BETWEEN OVERHEAD GROUND WIRE AND GROUND LEAD, 33 kV SYSTEM

ใช้แทนแบบ
ถูกแทนโดยแบบ
เขียนเสร็จวันที่ 14 พ.ค. 17
แก้แบบวันที่
มิติเป็น มม.
มาตราส่วน 1 : 30
แบบเลขที่ S02-015/17026
แผ่นที่ 2 ของจำนวน 2 แผ่น