
การประกอบเลขที่ ASSEMBLY NO. 3204

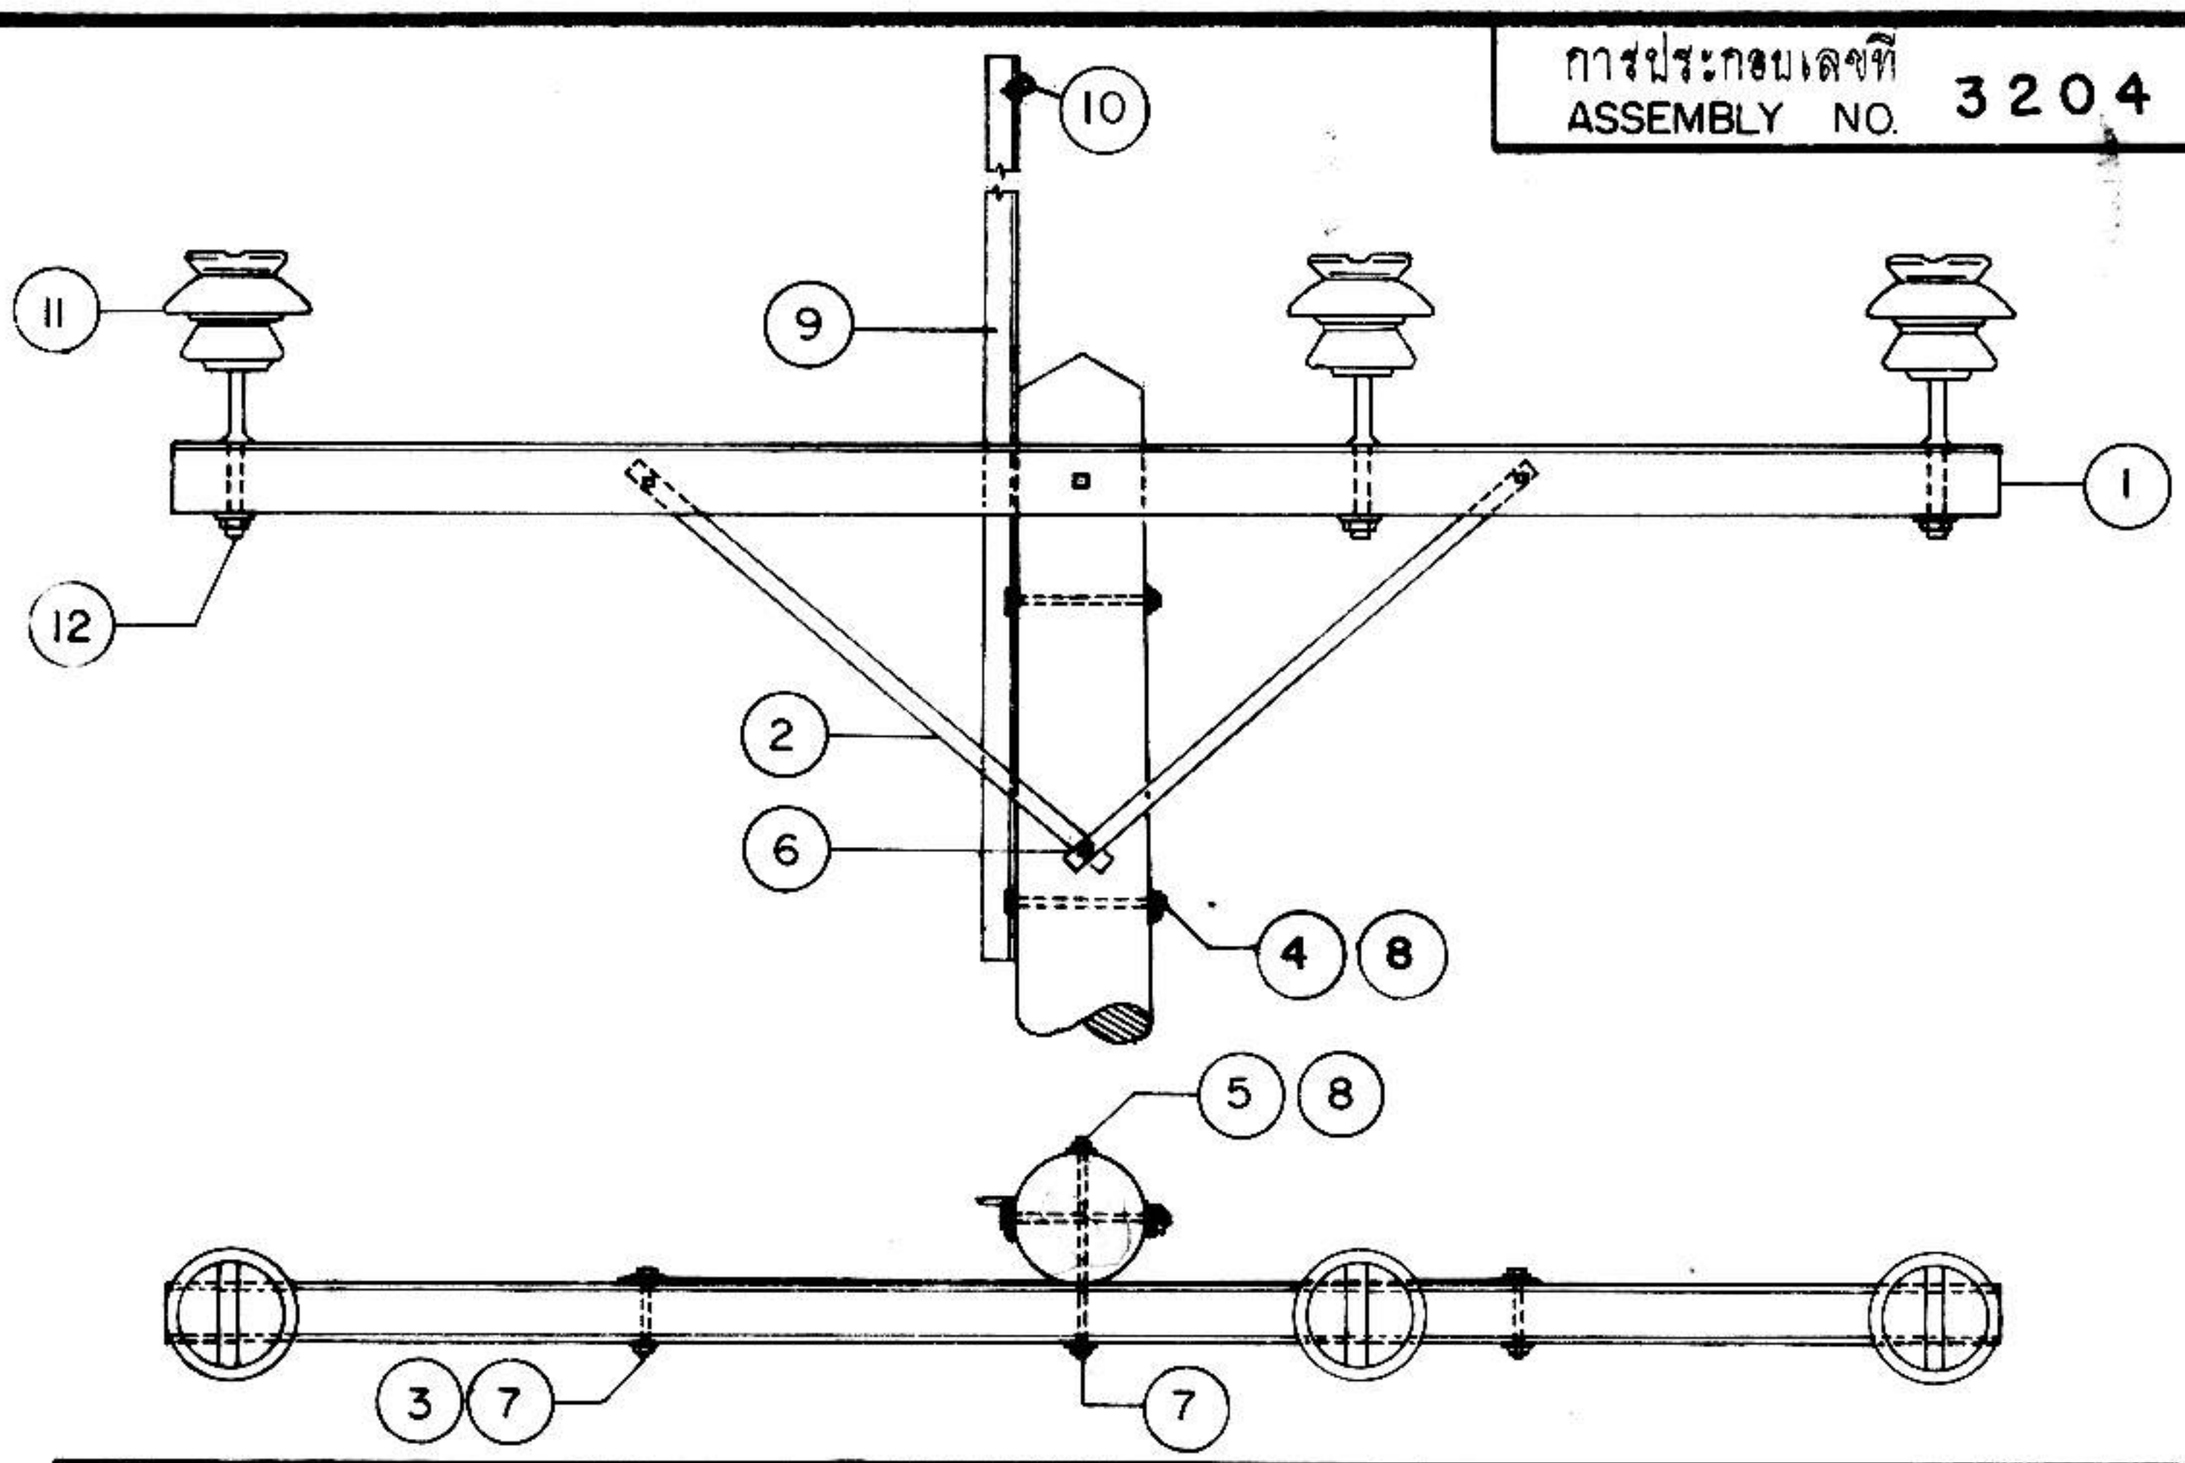

BILL OF MATERIAL

ITEM	DESCRIPTION	REQ'D	MAT. NO.
1	ไม้คอนสายขนาด 100X120 X 3,000 มม. CROSSARM (HT.) WOOD, 100 X 120 X 3,000 mm	1	00100003 (0101)
2	เหล็กประกันไม้คอน 40 X 6 X 1000 มม. BRACE, FLAT, FOR CROSSARM , 40 X 6 X 1000 mm	2	01200002 (0121)
3	สลักเกลียว M 16 X 130 มม. BOLT, MACHINE , M 16 X 130 mm	2	01110200 (0220)
4	สลักเกลียว M 16 X 300 มม. BOLT, MACHINE , M 16 X 300 mm	2	01110204 (0224)
5	สลักเกลียว M 16 X 350 มม. BOLT, MACHINE , M 16 X 350 mm.	1	01110205 (0225)
6	สลักเกลียวปล่อยขนาด 16 X 130 มม. SCREW, LAG 16 X 130 mm	1	01170001 (0325)
7	แหวนสี่เหลี่ยมแผน 52 X 52 X 4.5 มม. ขนาดรู Ø 18 มม. มอก. 258 WASHER, SQUARE , FLAT 52 X 52 X 4.5 mm HOLE Ø 18 mm TIS 258	3	01180100 (0355)
8	แหวนสี่เหลี่ยมโค้ง 50X50X5 มม. ขนาดรู Ø 18 มม. WASHER, SQUARE , CURVED, 50X50X5 mm HOLE Ø 18 mm	3	01180201 (0360)
9	เหล็กฉากรับสายล่อฟ้า OVERHEAD GROUND WIRE BAYONET	1	01010006 (0128)
10	กราวด์เวร์แคล็มป์แบบ J 1152 GROUND WIRE CLAMP J 1152	1	01230205 (0296)
11	ลูกถ้วยก้านตรง 33 kV มอก. 279 แบบ ค (แบบ 56-3) INSULATOR, PIN TYPE, 33 kV, TIS 279 TYPE C (CLASS 56-3)	3	03000002 (0409)
12	ก้านลูกถ้วยแรงสูง 33 kV PIN, INSULATOR	3	03100001 (0422)

กองวิศวกรรมและวางแผน	การไฟฟ้าส่วนภูมิภาค	ใช้แทนแบบ ถูกแทนโดยแบบ
ผู้เขียน ไพโรจน์ สถาปนิก วิศวกร หัวหน้าแผนก ผู้อำนวยการกอง	ผู้ว่าการ	เขียนเสร็จวันที่ 14 ตค 12 แก้แบบวันที่ มิติเป็น มม. มาตราส่วน 1:25
ร่องผู้ว่าการฝ่ายเทคนิค	การประกอบไม้คอนเดี่ยวกับเสาไม้ ระบบ 33 kV , 3 เฟส, มุม 0°-5° 33 kV, SINGLE CROSSARM ASSEMBLY ON WOOD POLE, 3-PHASE, 0° - 5°	แบบเลขที่ I50-015/120295 แผ่นที่ 1 ของจำนวน 1 แผ่น