

การประกอบเลขที่ ASSEMBLY NO. 5255

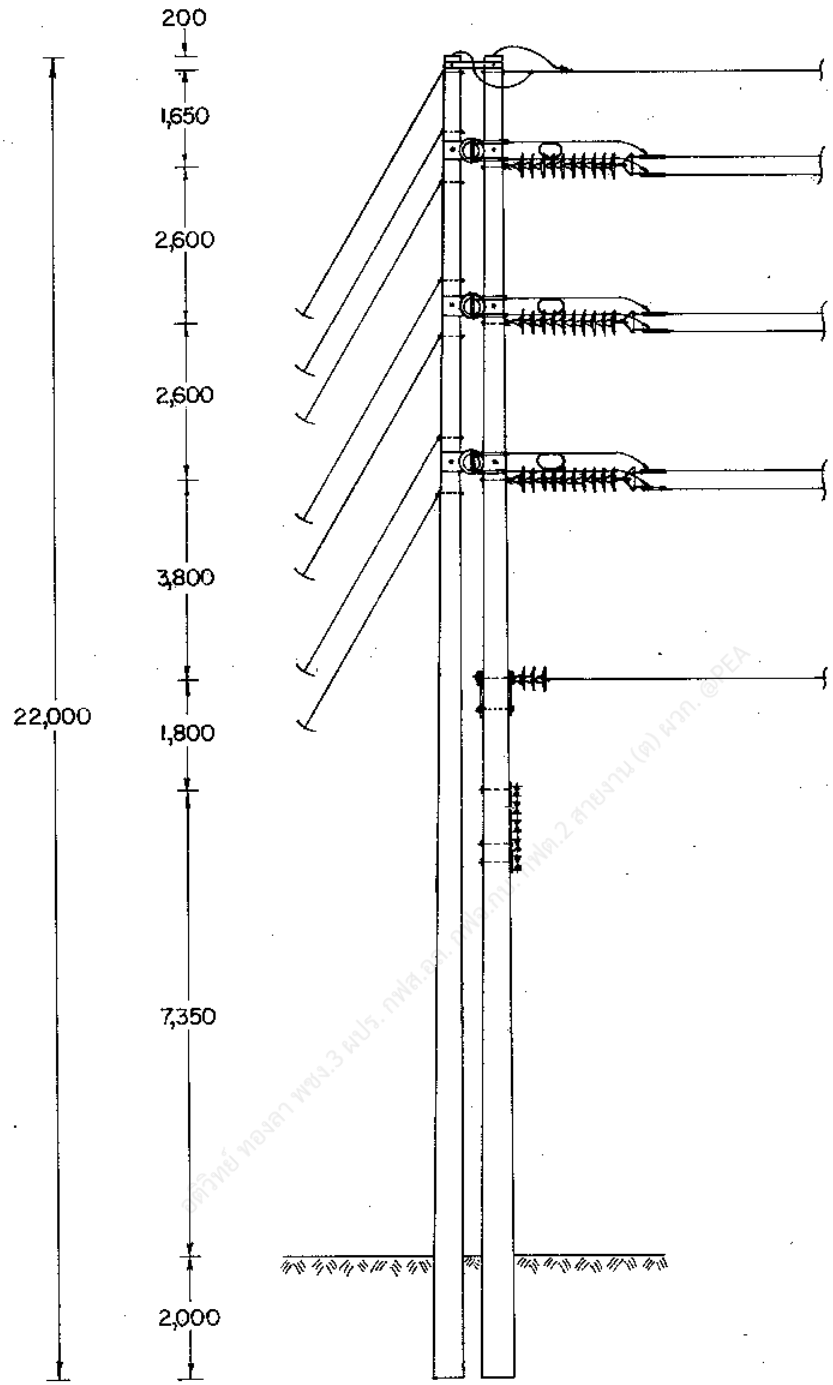

กองวิศวกรรมไฟฟ้าและเครื่องกล ฝ่ายวิศวกรรม	การไฟฟ้าส่วนภูมิภาค	ใช้แทนแบบ ถูกแทนที่โดยแบบ เขียนเสร็จวันที่ 2 มิ.ย. 23
ผู้เขียน ผู้สำรวจ วิศวกร หัวหน้าแผนก หัวหน้ากอง ผู้อำนวยการฝ่าย	ผู้ว่าการ 115 kV วงจรเดี่ยว สายไฟฟ้าคู่ เสาคู่สำหรับทางโค้ง 90° แบบ SD-LA-2	แก้แบบวันที่ มิติเป็น มม. มาตราส่วน 1 : 125
รองผู้ว่าการฝ่ายเทคนิค	115 kV SINGLE CIRCUIT DOUBLE CONDUCTOR DOUBLE POLE, 90° ANGLE STRUCTURE TYPE SD-LA-2	แบบเลขที่ SAI-015/23009 แผ่นที่ 1 รวมจำนวน 3 แผ่น

การประกอบเลขที่ ASSEMBLY NO. 5255

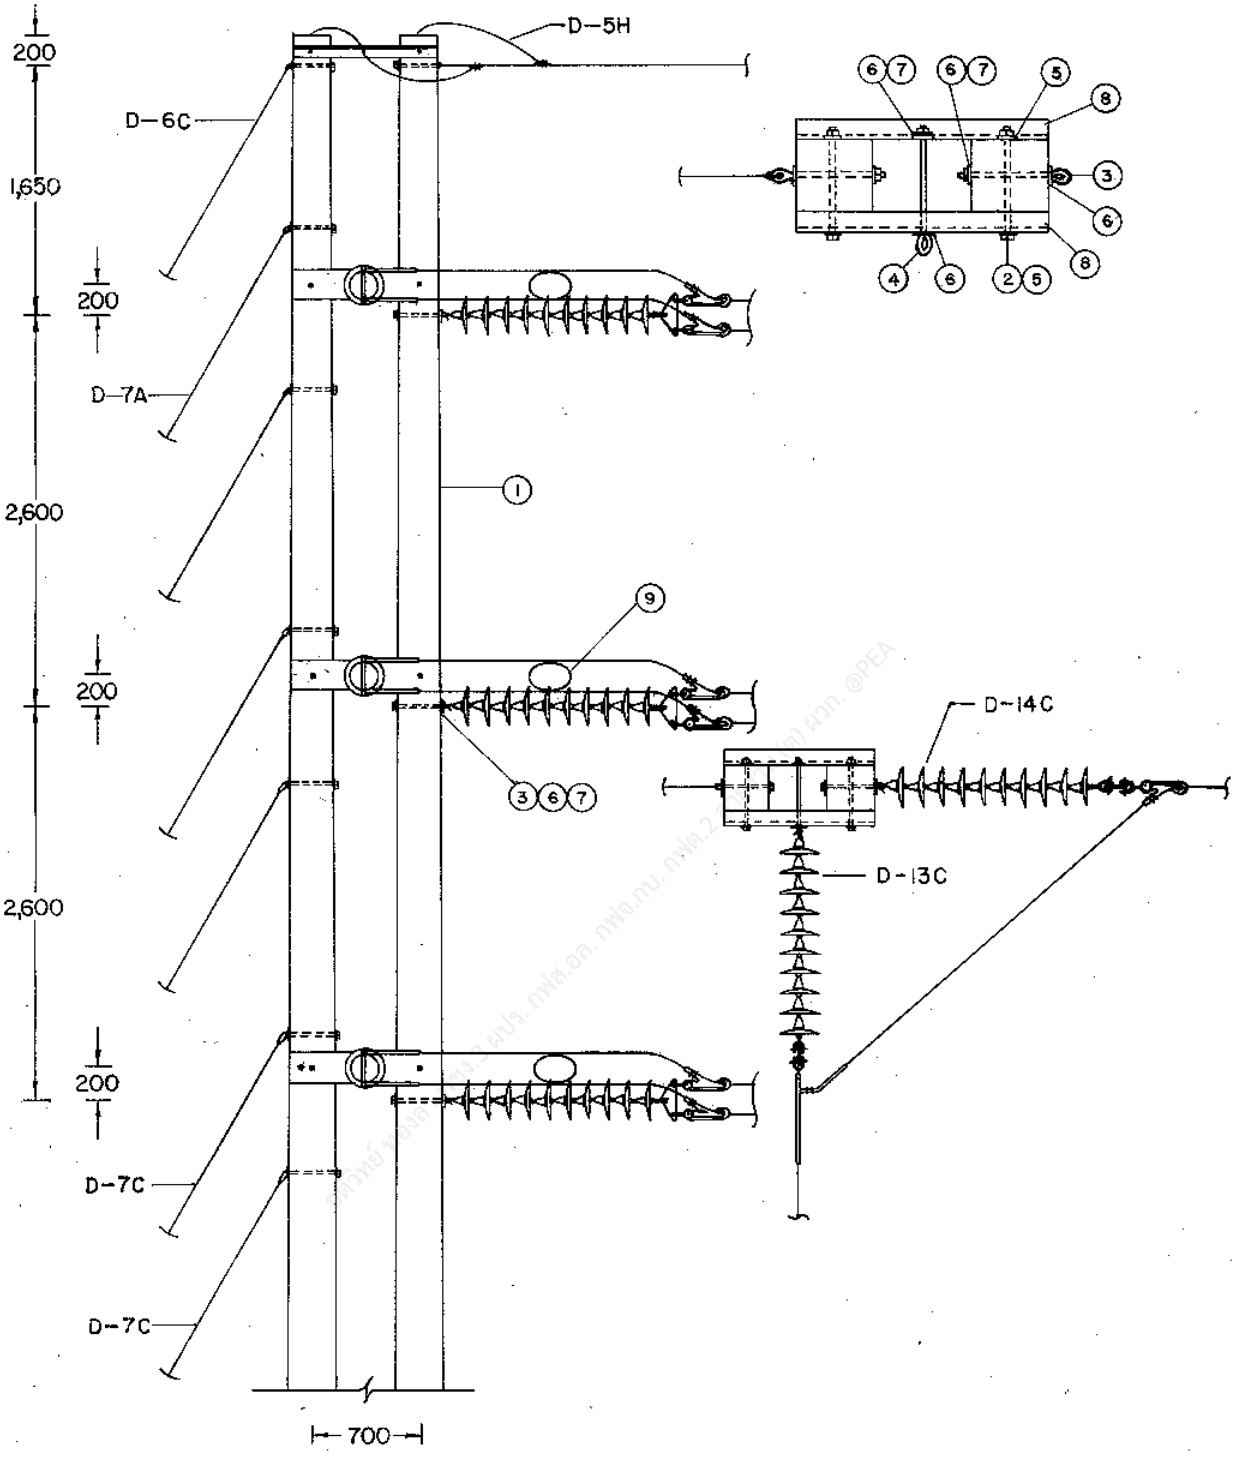

กองวิศวกรรมไฟฟ้าและเครื่องกล ฝ่ายวิศวกรรม	การไฟฟ้าส่วนภูมิภาค	ใช้แทนแบบ ถูกแทนโดยแบบ เขียนเสร็จวันที่ 2 พ.ค. 23
ผู้เขียน ผู้ตรวจ วิศวกร หัวหน้าแผนก หัวหน้ากอง ผู้อำนวยการฝ่าย	ผู้ว่าการ 115 kV วงจรเดี่ยว สายไฟฟ้าคู่ เสาคู่สำหรับทางโค้ง 90° แบบ SD-LA-2	แก้แบบวันที่ 15 กย. 40 มิติเป็น มม. มาตราส่วน 1 : 50
รองผู้ว่าการสายเทคนิค	115 kV SINGLE CIRCUIT DOUBLE CONDUCTOR DOUBLE POLE, 90° ANGLE STRUCTURE TYPE SD-LA-2	แบบเลขที่ SAI-015/23009 แผ่นที่ 2 ของจำนวน 3 แผ่น

19 ธ.ค. 2523

การประกอบเลขที่ ASSEMBLY NO. 5255

บัญชีวัสดุ
BILL OF MATERIAL

ลำดับที่ ITEM	รายละเอียด DESCRIPTION	จำนวน REQ'D	วัสดุเลขที่ MAT. NO.
1	เสาคอนกรีต 22 ม. POLE, CONCRETE 22 m LONG	2	00010011 (0041)
2	สลักเกลียว M 16 X 450 มม. BOLT, MACHINE, M 16 X 450 mm	6	01110207 (0227)
3	สลักห่วงโอเวล M 20 X 350 มม. BOLT, OVAL EYE M 20 X 350 mm	3	01150100 (0260)
4	สลักห่วงโอเวล M 20 X 450 มม. BOLT, OVAL EYE M 20 X 450 mm	3	01150101 (0261)
5	แหวนสี่เหลี่ยมแบน 52X52X4.5 มม. รู Ø 18 มม. มอก. 258 WASHER, SQUARE, FLAT 52X52X4.5 mm, HOLE Ø 18 mm, TIS 258	12	01180100 (0355)
6	แหวนสี่เหลี่ยมแบน 62X62X6 มม. รู Ø 22 มม. มอก. 258 WASHER, SQUARE, FLAT 62 X 62 X 6 mm, HOLE Ø 22 mm, TIS 258	12	01180101 (0356)
7	แหวนสปริง M 20 มอก. 259 WASHER, LOCK, M 20, TIS 259	6	01180302 (0366)
8	เหล็กรูปรางน้ำ 200 X80X7.5มม. ยาว 1,000 มม. STEEL CHANNEL 200 X 80 X7.5 mm, 1,000 mm LONG	6	01000400 (2675)
9	ปรีฟอร์มแยกสาย SPACER, HELICAL ROD, PREFORMED	3	02240000 (0918)

รายละเอียด
DETAIL

D-13C	การประกอบลูกถ้วยแขวน SUSPENSION INSULATOR ASSEMBLY	3	
D-14C	การประกอบลูกถ้วยแขวน SUSPENSION INSULATOR ASSEMBLY	3	
D-5H	การต่อสายล่อฟ้า OVERHEAD GROUND WIRE CONNECTION	1	
D-6C	การประกอบสายยึดโยงตรงเหล็กตีเกลียว 50 ต.มม. STEEL STRANDED WIRE 50 mm^2 GUY ASSEMBLY	1	
D-7A	การประกอบสายยึดโยงตรงเหล็กตีเกลียว 95 ต.มม. STEEL STRANDED WIRE 95 mm^2 GUY ASSEMBLY	4	
D-7C	การประกอบสายยึดโยงตรงเหล็กตีเกลียว 95 ต.มม. STEEL STRANDED WIRE 95 mm^2 GUY ASSEMBLY	2	
D-9A	สมอบกคอนกรีต CONCRETE ANCHOR	1	
D-10A	ฐานรากเสา POLE FOUNDATION	1	

กองวิศวกรรมไฟฟ้าและเครื่องกล
ฝ่ายวิศวกรรม

ผู้เรียน
ผู้ตรวจ
วิศวกร
หัวหน้าแผนก
หัวหน้ากอง
ผู้อำนวยการฝ่าย
ของเจ้าการไฟฟ้า

การไฟฟ้าส่วนภูมิภาค

ผู้ว่าการ

115 kV วงจรเดี่ยว สายไฟฟ้าคู่
เสาคู่สำหรับทางโค้ง 90°
แบบ SD-LA-2

115 kV SINGLE CIRCUIT DOUBLE CONDUCTOR
DOUBLE POLE, 90° ANGLE STRUCTURE
TYPE SD-LA-2

ใช้แทนแบบ
ถูกแทนโดยแบบ
เรียนฟร์จรวันที่ 2 พ.ค. 23
แก้แบบจำนวนที่ 15 ก.ย. 40
มิติเป็น
มาตราส่วน

แบบเลขที่ SAI-015/23009
แผ่นที่ 3 ของจำนวน 3 แผ่น

19 มี.ค. 25