การประกอบเลขที่ ASSEMBLY NO. 0408

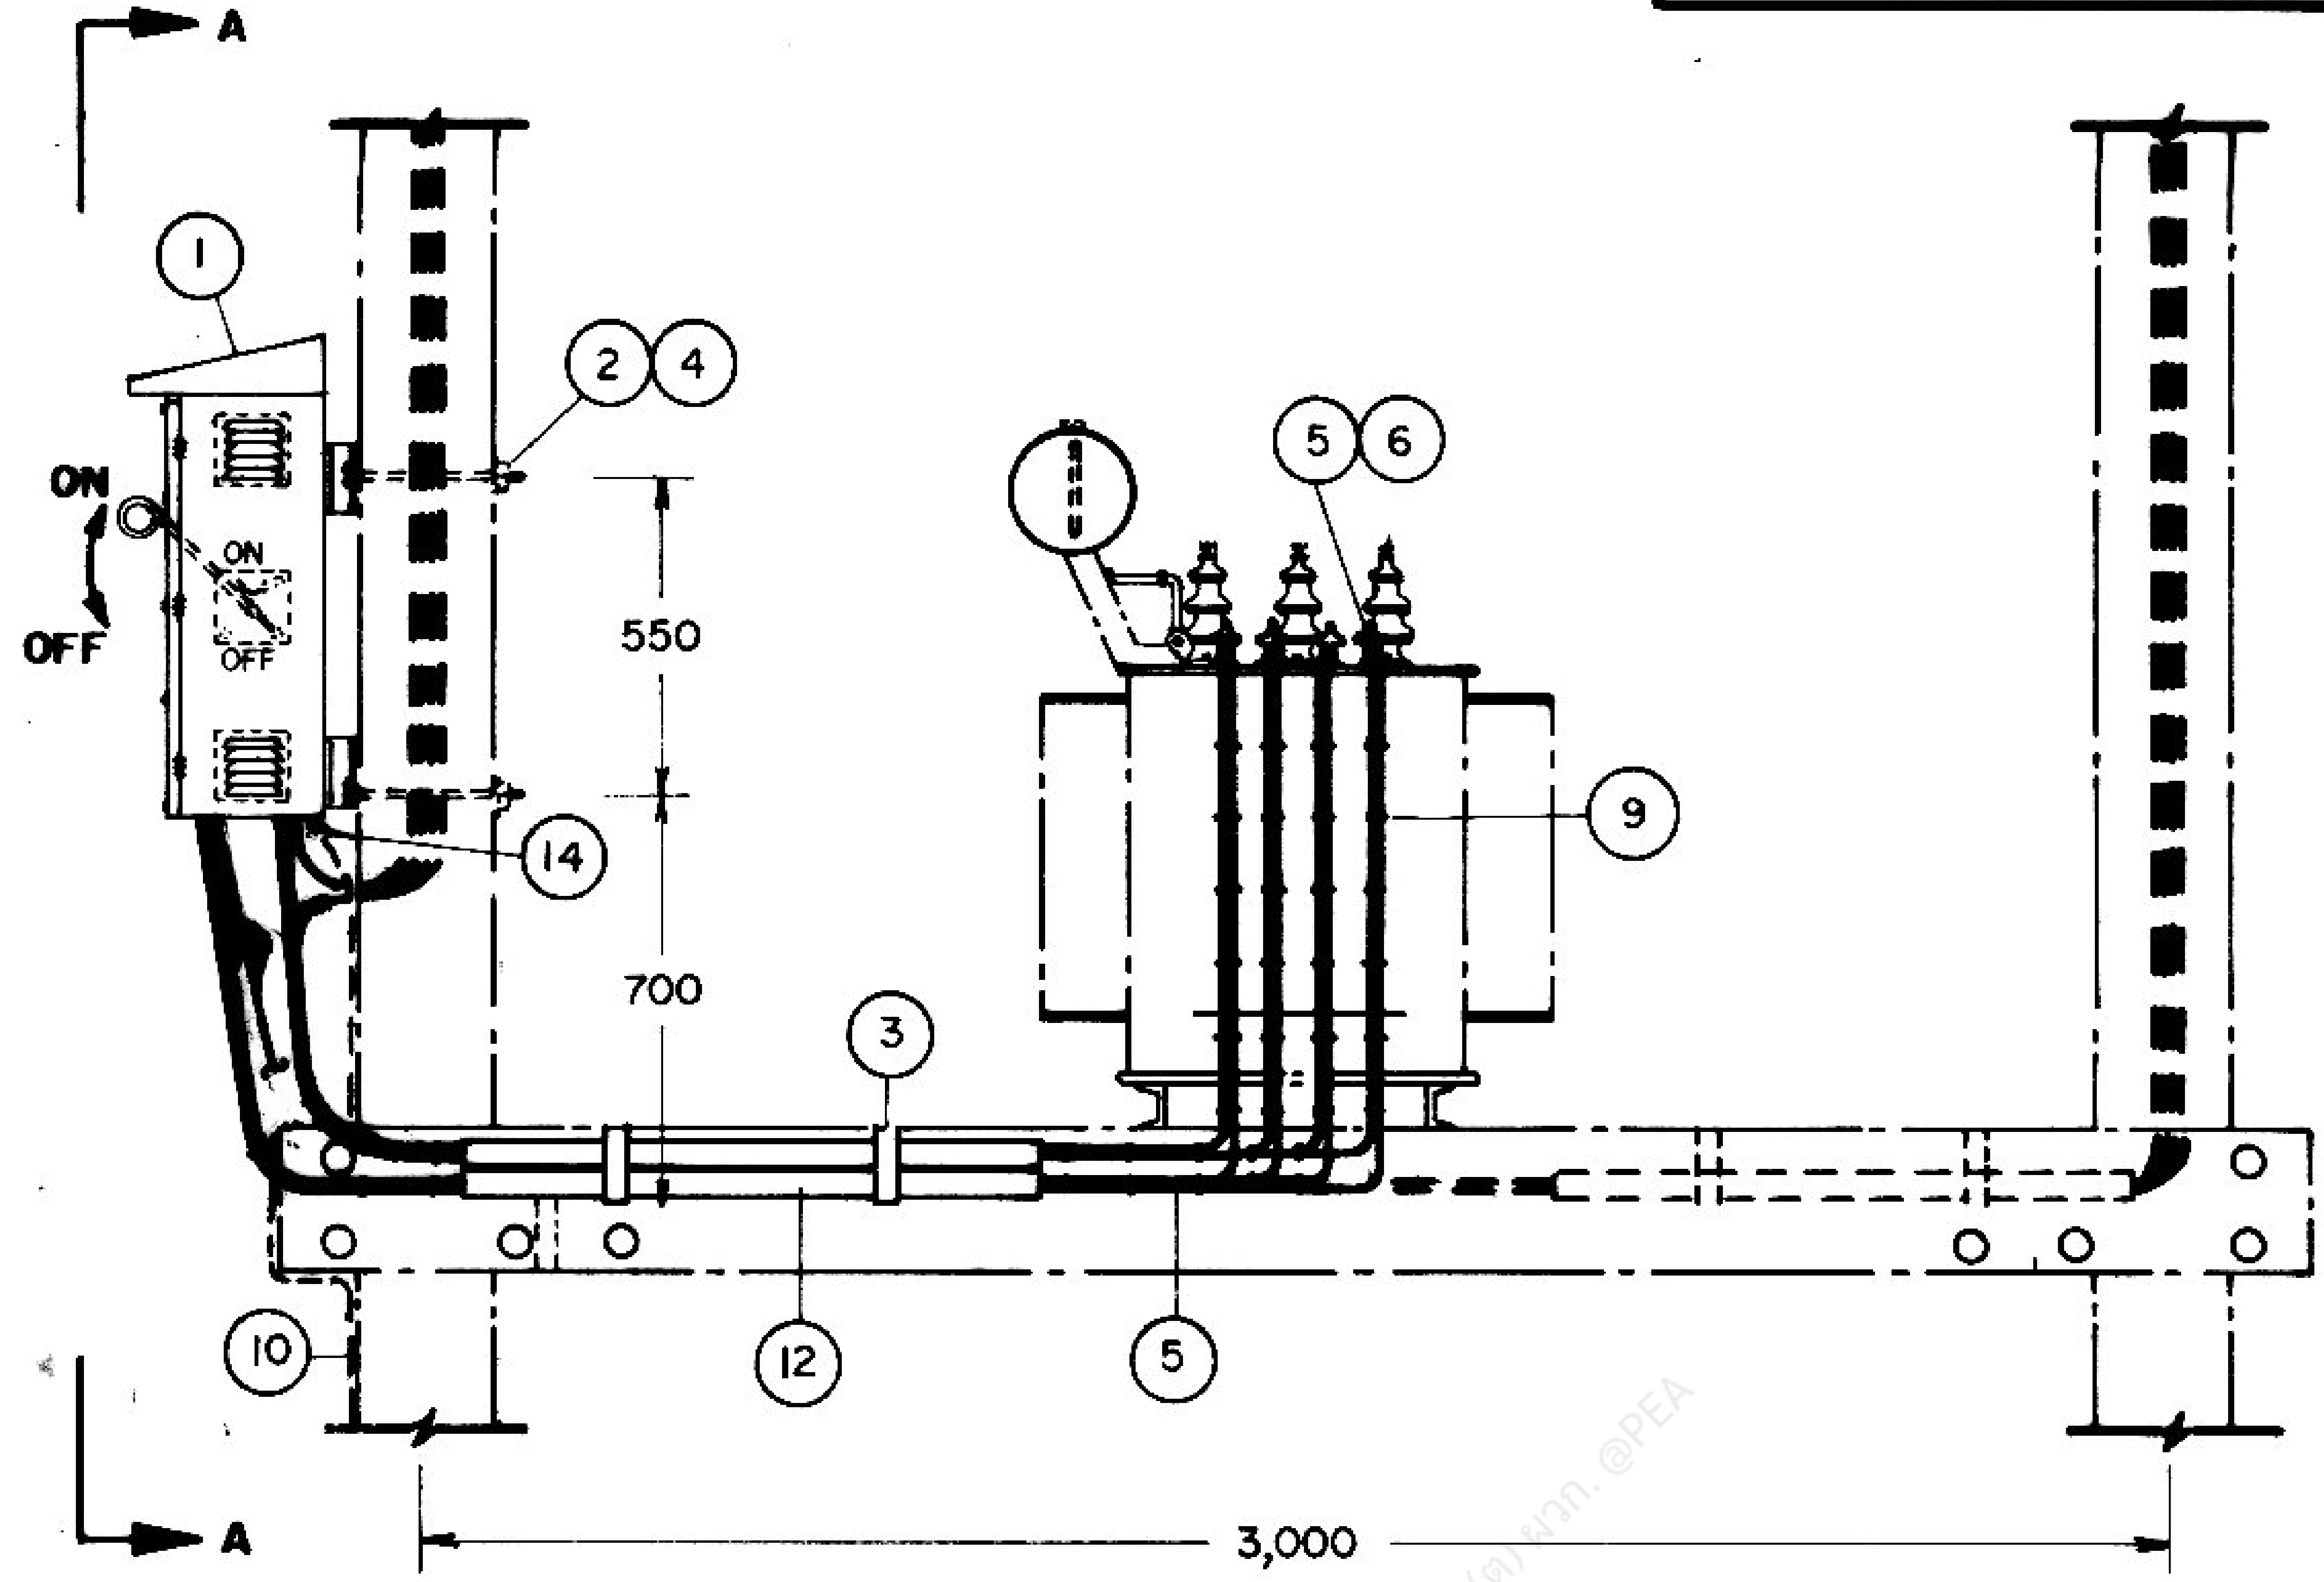

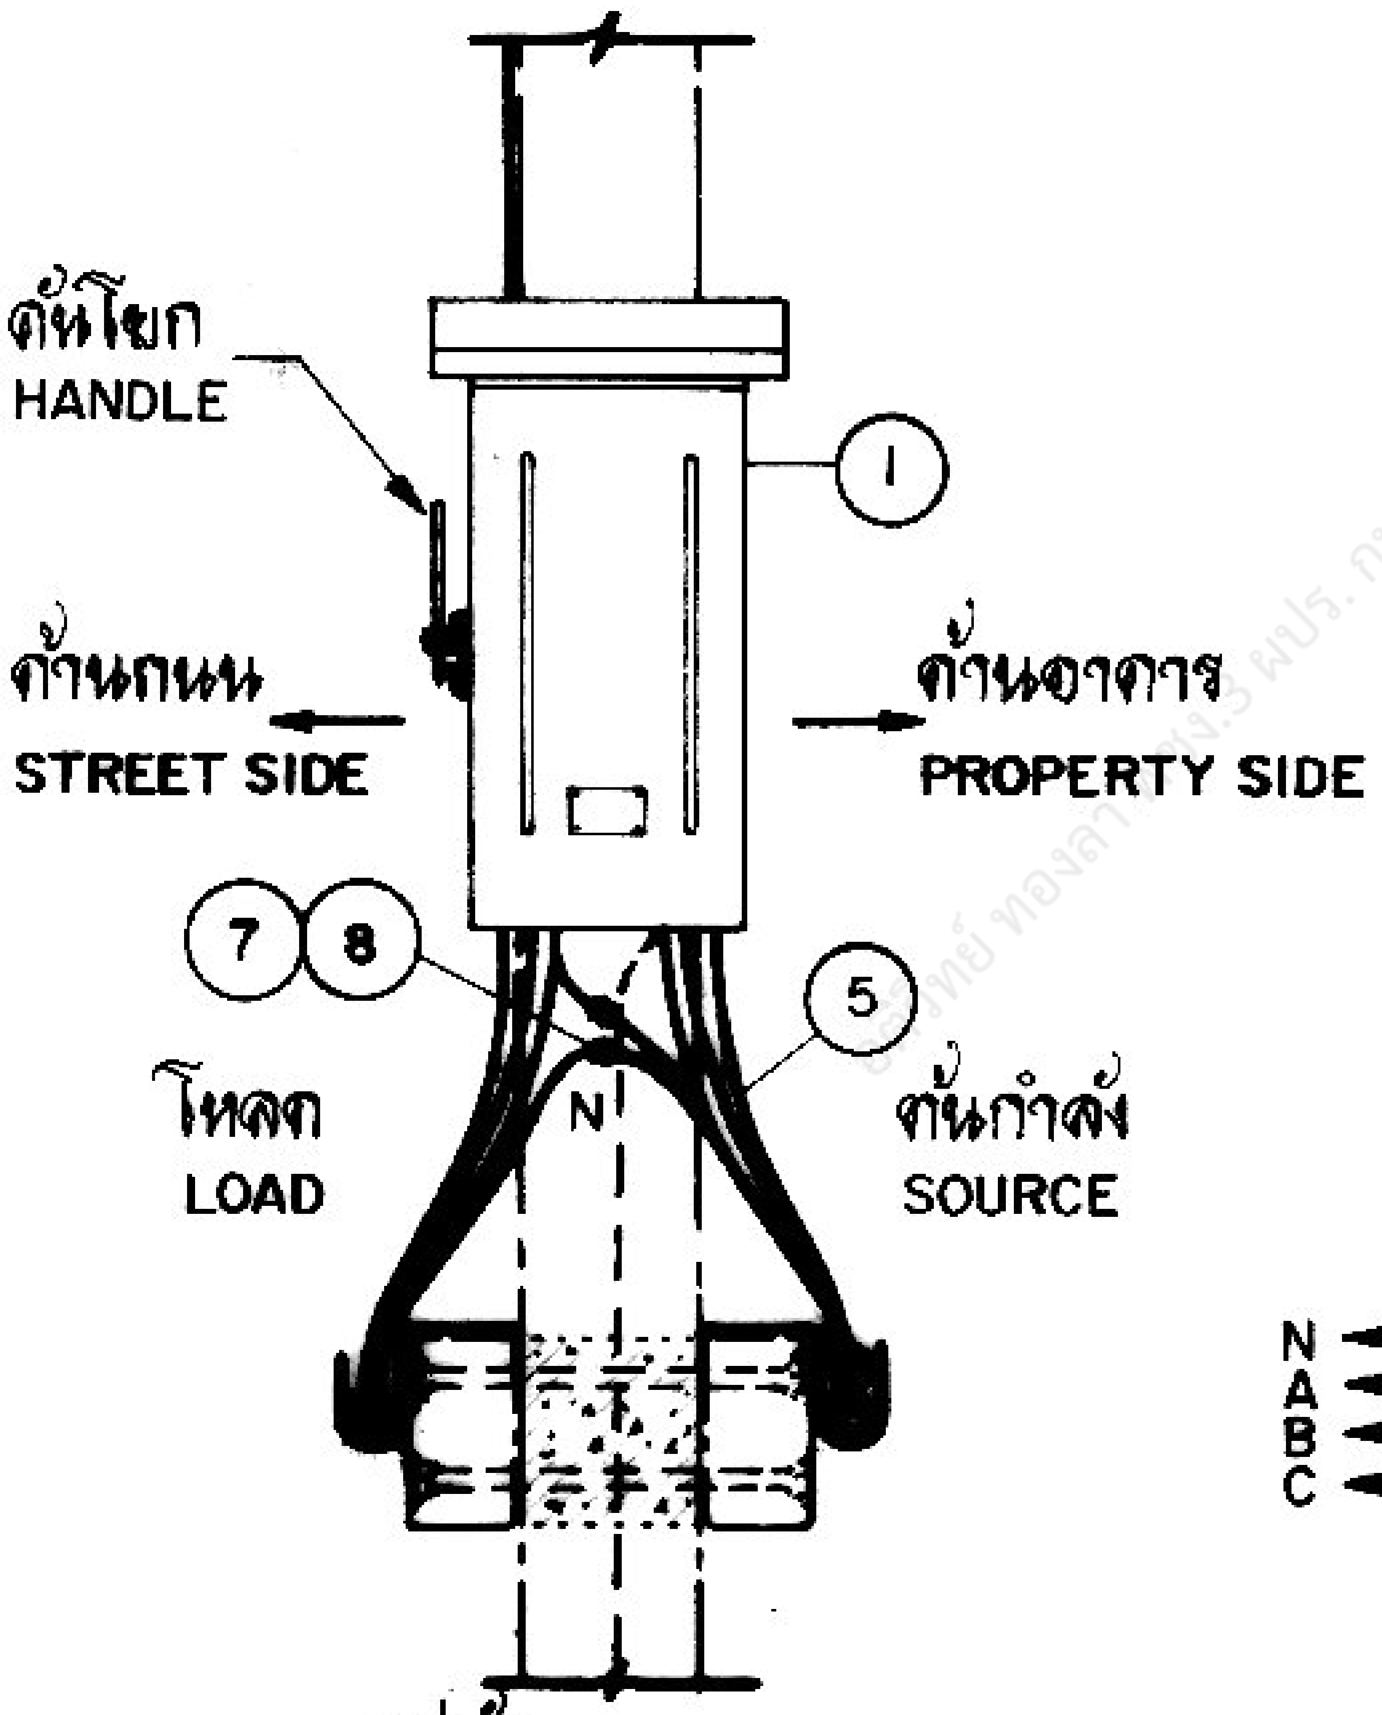

รูปตัด A—A
SECTION A—A

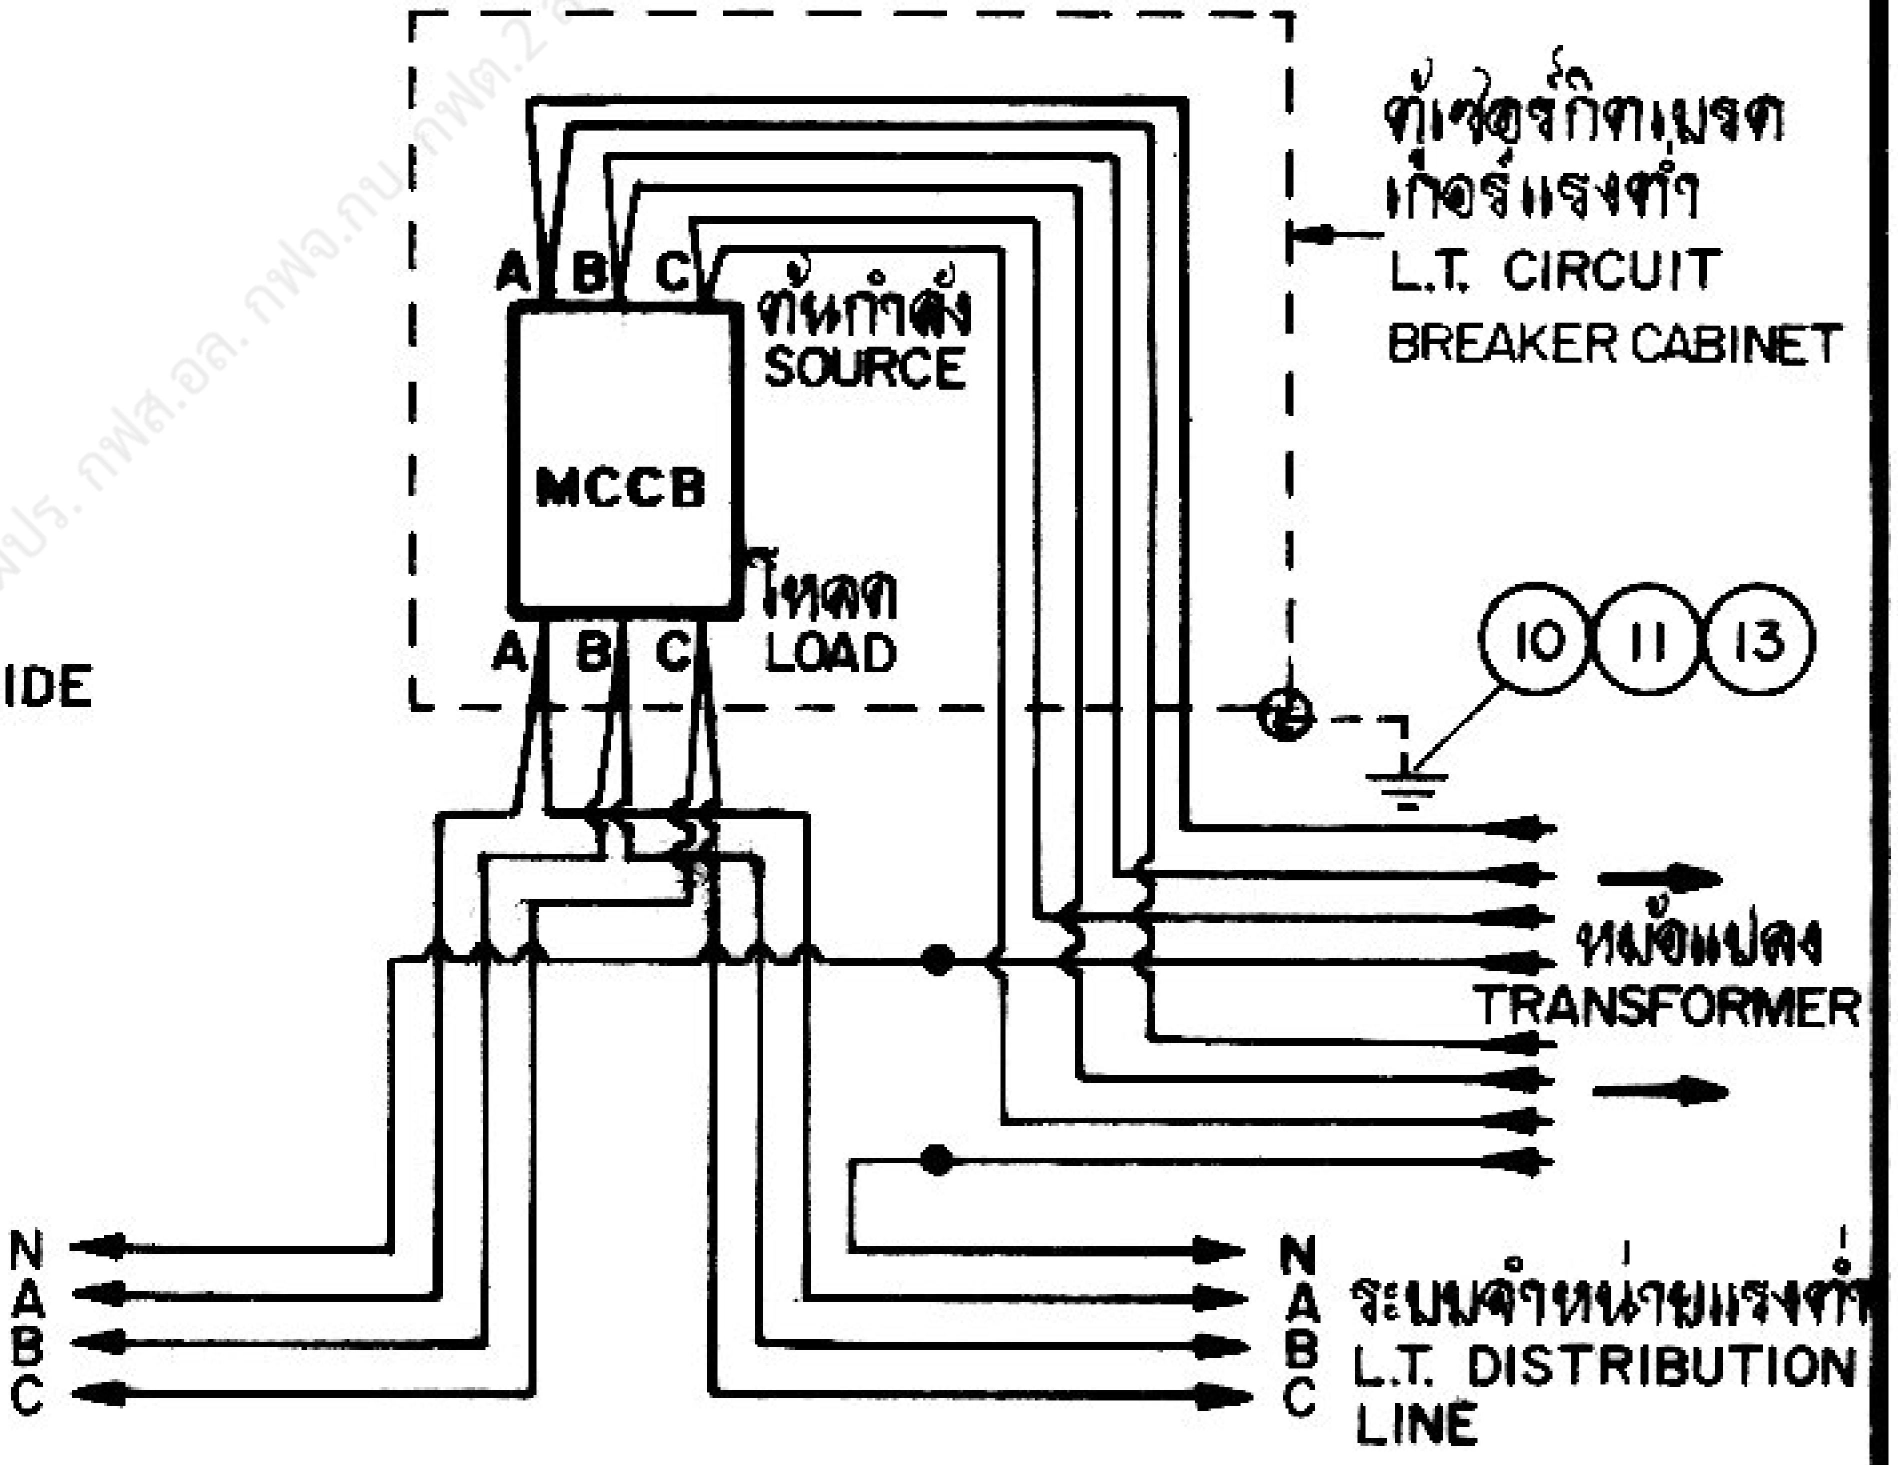

ไดอะแกรมแสดงการต่อสาย
WIRING DIAGRAM

กองวิศวกรรมไฟฟ้าและเครื่องกล ฝ่ายวิศวกรรม	การไฟฟ้าส่วนภูมิภาค	ใช้แทนแบบ ถูกแทนโดยแบบ
ผู้เขียน [redacted] ผู้สำรวจ วิศวกร หัวหน้าแผนก ผู้อำนวยการกอง ผู้อำนวยการฝ่าย	ผู้ว่าการ 10 ก.พ. 30	เขียนเสร็จวันที่ 8 ม.ค. 30 แก้แบบวันที่ มิติเป็น มิลลิเมตร มาตราส่วน 1 : 25
	การติดตั้งเซอร์กิตเบรกเกอร์แรงต่ำ ที่เสาต้นนั่งร้านหม้อแปลง	
รองผู้ว่าการฝ่ายเทคนิค [illegible] 2530	L.T. CIRCUIT BREAKER INSTALLATION ON THREE PHASE TRANSFORMER POLE	แบบเลขที่ SAI-015/30001 แผ่นที่ 1 จากจำนวน 3 แผ่น

การประกอบเลขที่ ASSEMBLY NO. 0408

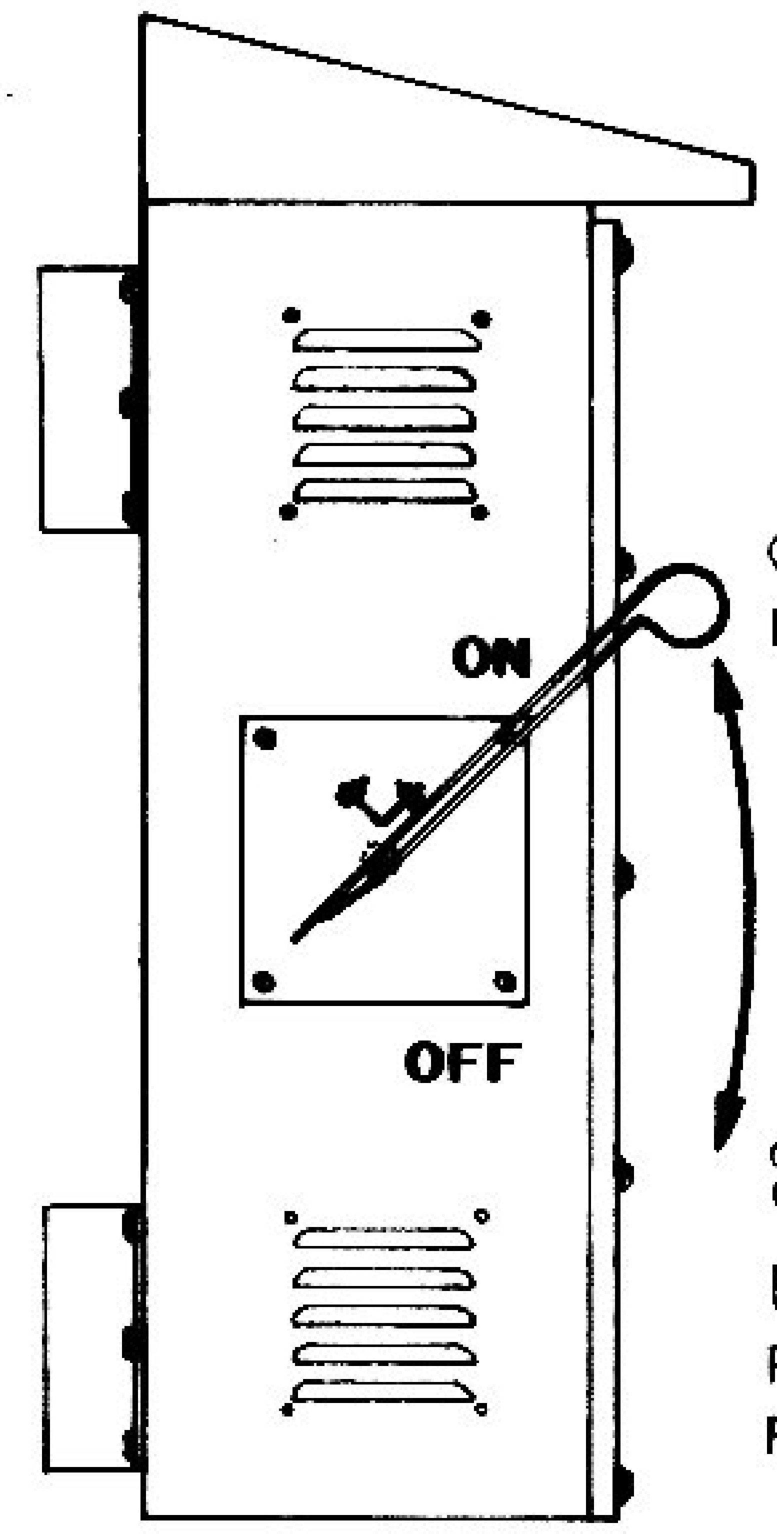
ON
OFF
ดันขึ้นเมื่อต้องการปิดวงจร
PUSH UP:TO CLOSE CIRCUIT
ดึงลงเมื่อต้องการเปิดวงจรหรือรีเซท
เซอร์กิตเบรคเกอร์ หลังจากการทริป
PULL DOWN:TO OPEN CIRCUIT OR
RESET MCCB. AFTER TRIPPING

รูปด้านข้าง
SIDE VIEW

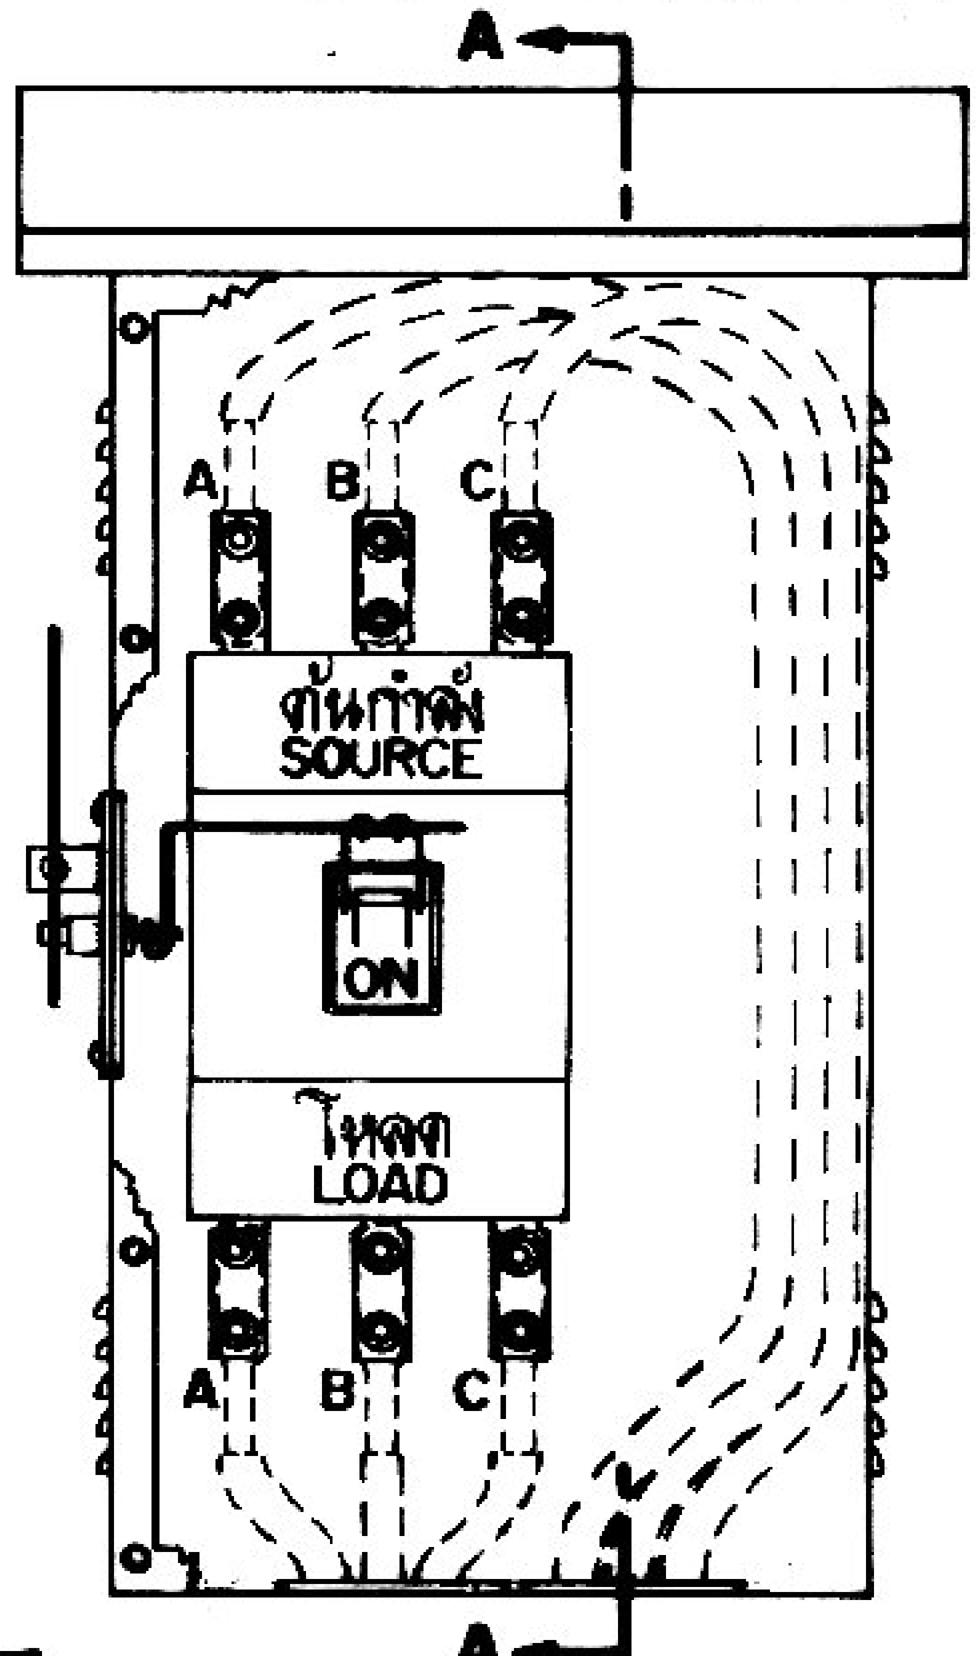

รูปแสดงการติดตั้งอุปกรณ์ภายใน
INTERNAL EQUIPMENTS ARRANGEMENT

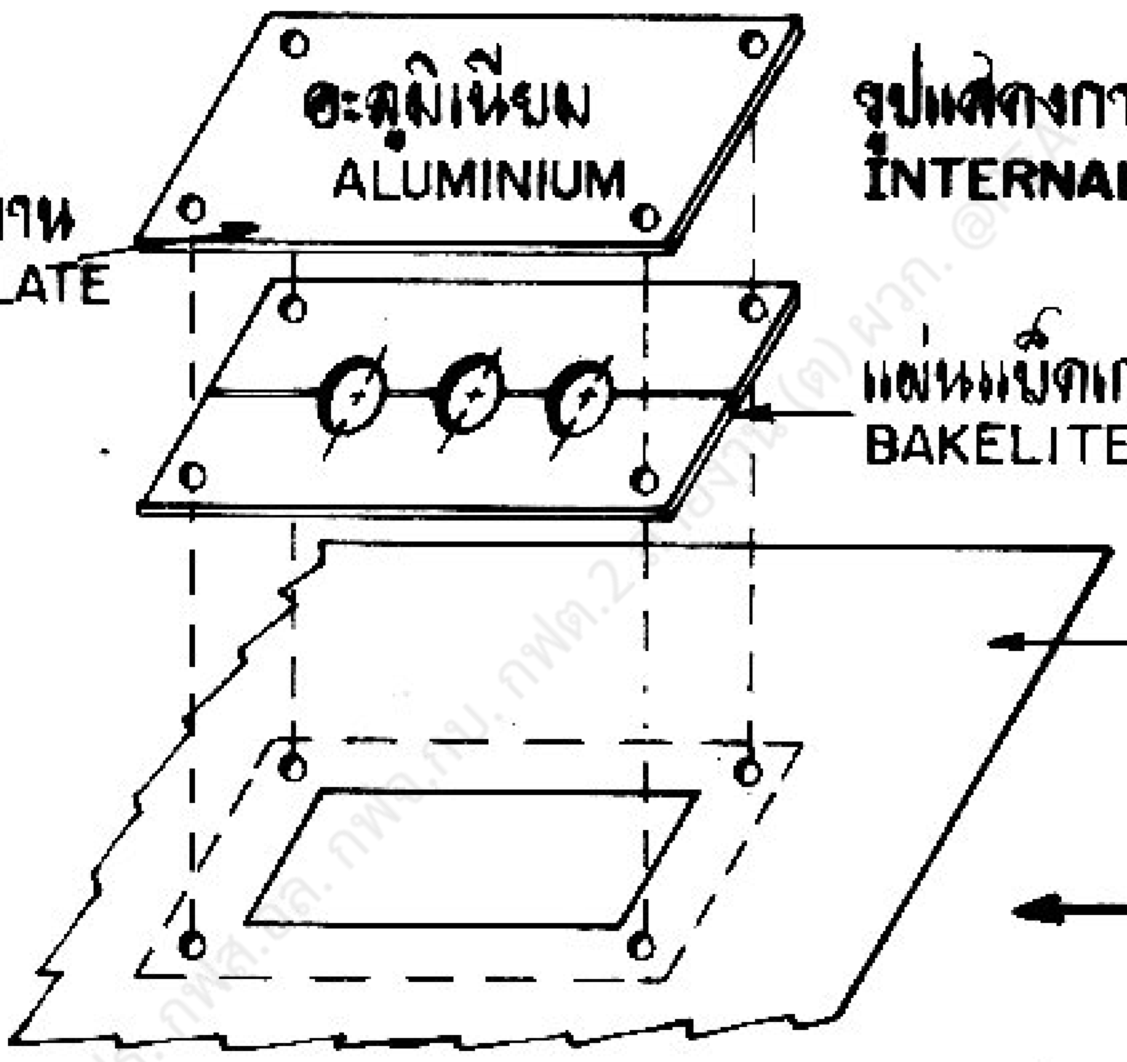

รายละเอียด B
DETAIL

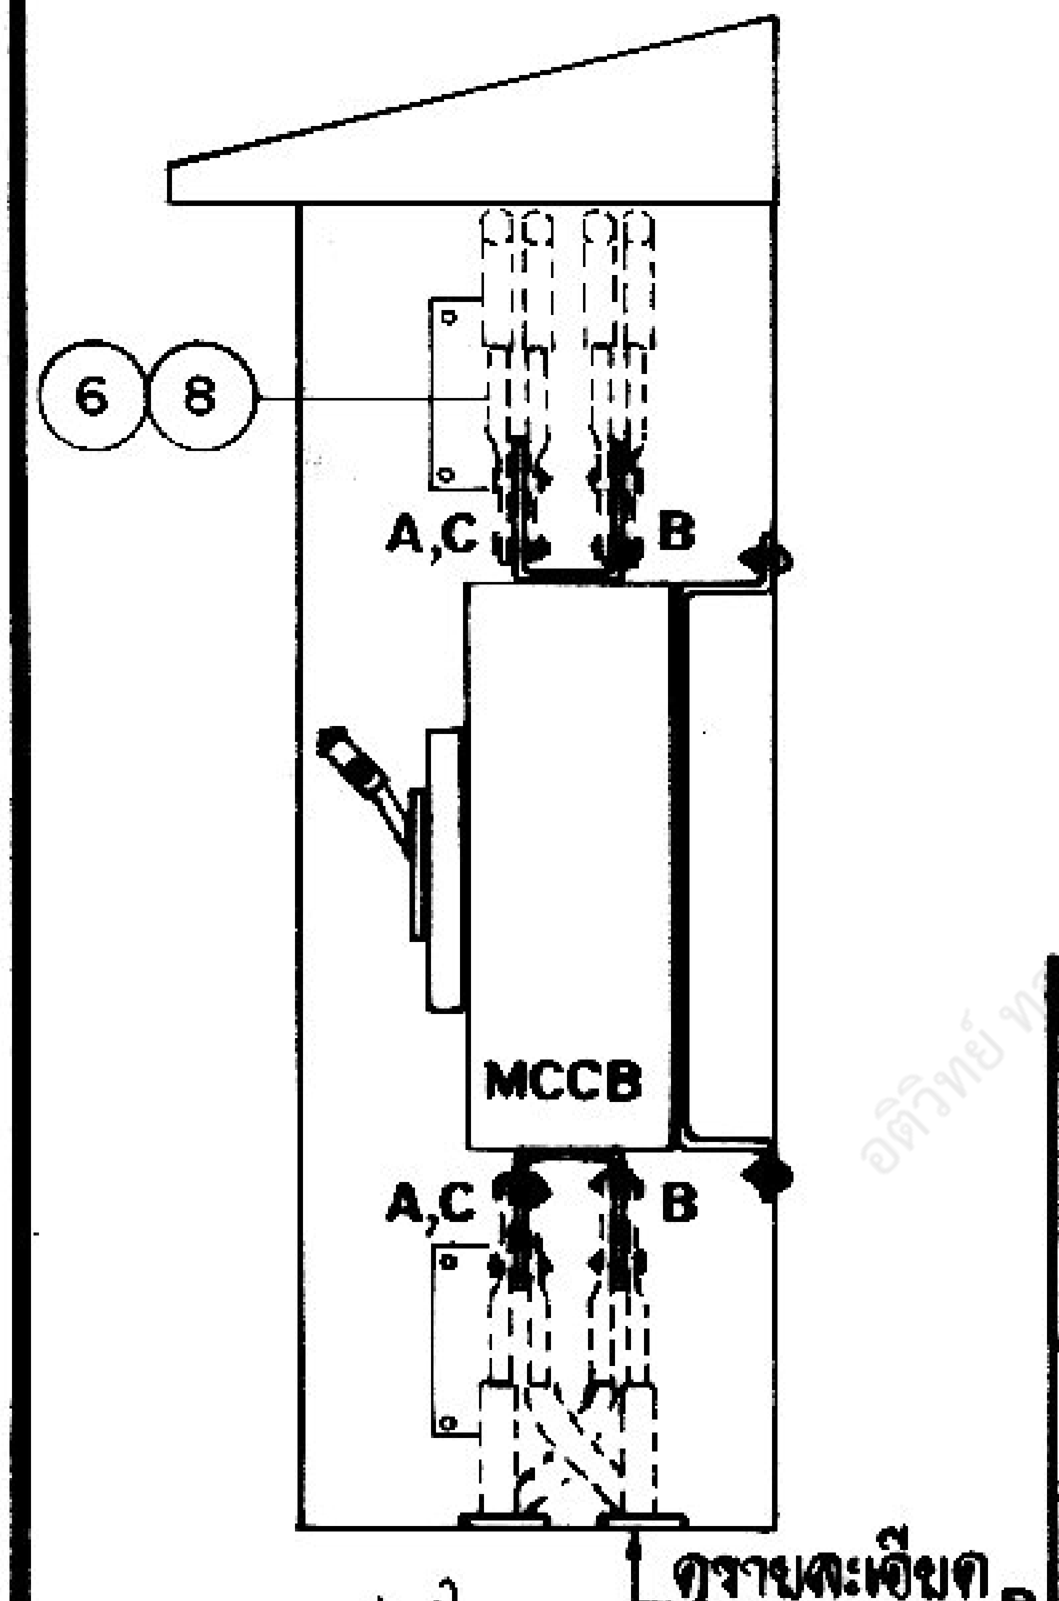

รูปตัด A-A
SECTION

ขนาดเซอร์กิตเบรคเกอร์แรงต่ำที่ใช้ป้องกันหม้อแปลง
RATED OF MCCB. FOR TRANSFORMER PROTECTION

ขนาดหม้อแปลง 3 เฟส (kVA) 3-Ø TRANSFORMER RATING (KVA)	ขนาดเซอร์กิตเบรคเกอร์ 3 ขั้ว 400 โวลต์ (แอมป์) RATED CURRENT OF MCCB, 3 P, 400 V (AMP)	
	ค่ากระแสตัดวงจร "AT" OVERCURRENT RELEASE	ขนาดเฟรม "AF" FRAME SIZE
50	60	⩾ 100
100	125	⩾ 160
160	200	⩾ 225
250	300 – 320	⩾ 400

กองวิศวกรรมไฟฟ้าและเครื่องกล ฝ่ายวิศวกรรม	การไฟฟ้าส่วนภูมิภาค	ใช้แทนแบบ ถูกแทนโดยแบบ
ผู้เขียน ผู้สำรวจ วิศวกร หัวหน้าแผนก ผู้อำนวยการกอง ผู้อำนวยการฝ่าย	ผู้ว่าการ 10 ก.พ.30.	เขียนเสร็จวันที่ 8 ม.ค. 30 แก้แบบวันที่ มิติเป็น มิลลิเมตร มาตราส่วน 1:5, 1:10
	การติดตั้งเซอร์กิตเบรคเกอร์แรงต่ำ ที่เสาต้นนั่งร้านหม้อแปลง	
รองผู้ว่าการฝ่ายเทคนิค	L.T. CIRCUIT BREAKER INSTALLATION ON THREE PHASE TRANSFORMER POLE	แบบเลขที่ SAI-015/30001 แผ่นที่ 2 ของจำนวน 3 แผ่น

การประกอบเลขที่ ASSEMBLY NO.	0408

บัญชีวัสดุ
BILL OF MATERIAL

ลำดับที่ ITEM	รายละเอียด DESCRIPTION	จำนวน REQ'D	วัสดุเลขที่ MAT.NO.
1	เซอร์กิตเบรกเกอร์ 3 ขั้ว 400 โวลท์ ขนาดพิกัดกระแสตามต้องการ พร้อมตู้ CIRCUIT BREAKER, 3 P, 400 V RATED CURRENT AS REQ'D, COMP. WITH CABINET	1	04120000-1
2	สลักเกลียว M 16X250 มม. BOLT, MACHINE, M 16X250 mm	2	01110203
3	เหล็กแขวนท่อ PVC (เหล็กแบน 30X4 มม. มอก. 55) STEEL BRACKET (FLAT IRON 30X4 mm TIS 55)	6	05100002
4	แหวนสี่เหลี่ยมแบน 52X52X4.5 มม. รู ø 18 มม. มอก. 285 WASHER, SQUARE, FLAT 52X52X4.5 mm HOLE ø 18 mm TIS 285	2	01180100
5	สายอะลูมิเนียมหุ้มฉนวน PVC 750 โวลท์ 75°C มอก. 293 ขนาดตามต้องการ CABLE, Al PVC INSULATED, 750 V, 75°C, TIS 293 SIZE AS REQUIRED	40 ม. m	02070002-5
6	หางปลาชนิดบีบเจาะรูตามมาตรฐาน NEMA สำหรับสายอะลูมิเนียม ขนาดตามต้องการ CABLE LUG, NEMA HOLE, COMPRESSION TYPE, Al CABLE SIZE AS REQ'D	20	02420102-5
7	คอนเนคเตอร์ชนิดบีบ แบบ H สำหรับสายอะลูมิเนียม 50–95 ต.มม. CONNECTOR, COMPRESSION, H-TYPE, FOR Al CONDUCTOR 50–95 mm^2	2	02320003
8	PVC เทป กว้าง 19 มม. (ใช้ความยาว 2 ม. ต่อ 1 จุด) มอก. 386 PVC TAPE, 19 mm WIDE (2 m LONG PER POINT) TIS 386	2 ม้วน rolls	02180001 or 02180002
9	ลวดอะลูมิเนียมแบน 1X10 มม. ความยาวตามต้องการ (ทำเป็นเข็มขัดรัดสาย) ARMOUR TAPE 1X10 mm LENGTH AS REQUIRED (AS CABLE STRAP)		02200000
10	ลวดเหล็กตีเกลียว 50/7 ต.มม. มอก. 404 WIRE, STEEL STRANDED 50/7 mm^2 TIS 404	9 ม. m	01100004
11	ท่อ PVC แข็ง ขนาด ø 20 X 2,500–4,000 มม. พร้อมอุปกรณ์ยึด CONDUIT, PVC RIGID ø 20 X 2,500–4,000 mm, COMP. WITH FIXING ACCESS.	1	08040002 or 08040001
12	ท่อ PVC แข็ง ขนาด 65X1,000 มม. มอก. 216 CONDUIT, PVC. RIGID, SIZE ø 65X1,000 mm TIS 216	4	08040003
13	หลักดิน 60X60X5 มม. ยาว 2 ม. ROD GROUND 60X60X5 mm 2 m LONG	1	01220002
14	ยูแคลมป์ สลักเดี่ยว M 8 CLAMP, SINGLE U-BOLT, M 8	1	01230000

	แบบอ้างอิง REFERENCE DRAWING	แบบเลขที่ DWG. NO.	การประกอบเลขที่ ASSEMBLY NO.
1*	ขนาดสายไฟฟ้าแรงต่ำออกจากหม้อแปลง THE SIZE OF L.T. CABLE FORM TRANSFORMER	SAI-015/22034	**0601**
2	การต่อสายลงดินของอุปกรณ์ (เช่นเดียวกับไดอะแกรม แผ่นที่ 2) GROUNDING EQUIPMENT (AS DIAGRAM SHEET NO. 2)	S02-015/20034	**9701**

* ทั้งนี้สายไฟฟ้าเข้าและออกจากเซอร์กิตเบรกเกอร์แรงต่ำ ต้องไม่เกิน 2 วงจร
IN AND OUT LINES, FROM L.T. CIRCUIT BREAKER, NOT MORE THAN 2 CIRCUITS

กองวิศวกรรมไฟฟ้าและเครื่องก
ฝ่ายวิศวกรรม

ผู้เขียน
ผู้สำรวจ
วิศวกร
หัวหน้าแผนก
ผู้อำนวยการกอง
ผู้อำนวยการฝ่าย
รองผู้ว่าการฝ่ายเทคนิค

การไฟฟ้าส่วนภูมิภาค

ผู้ว่าการ 10 ก.พ. 30.

การติดตั้งเซอร์กิตเบรกเกอร์แรงต่ำ
ที่เสาต้นนั่งร้านหม้อแปลง

L.T. CIRCUIT BREAKER INSTALLATION
ON THREE PHASE TRANSFORMER POLE

ใช้แทนแบบ
ถูกแทนโดยแบบ
เขียนเสร็จวันที่ 8 พ.ค. 30
แก้แบบวันที่
มิติเป็น
มาตราส่วน

แบบเลขที่ SAI-015/30001
แผ่นที่ 3 ของจำนวน 3 แผ่น