การประกอบเลขที่
ASSEMBLY NO. **5224**

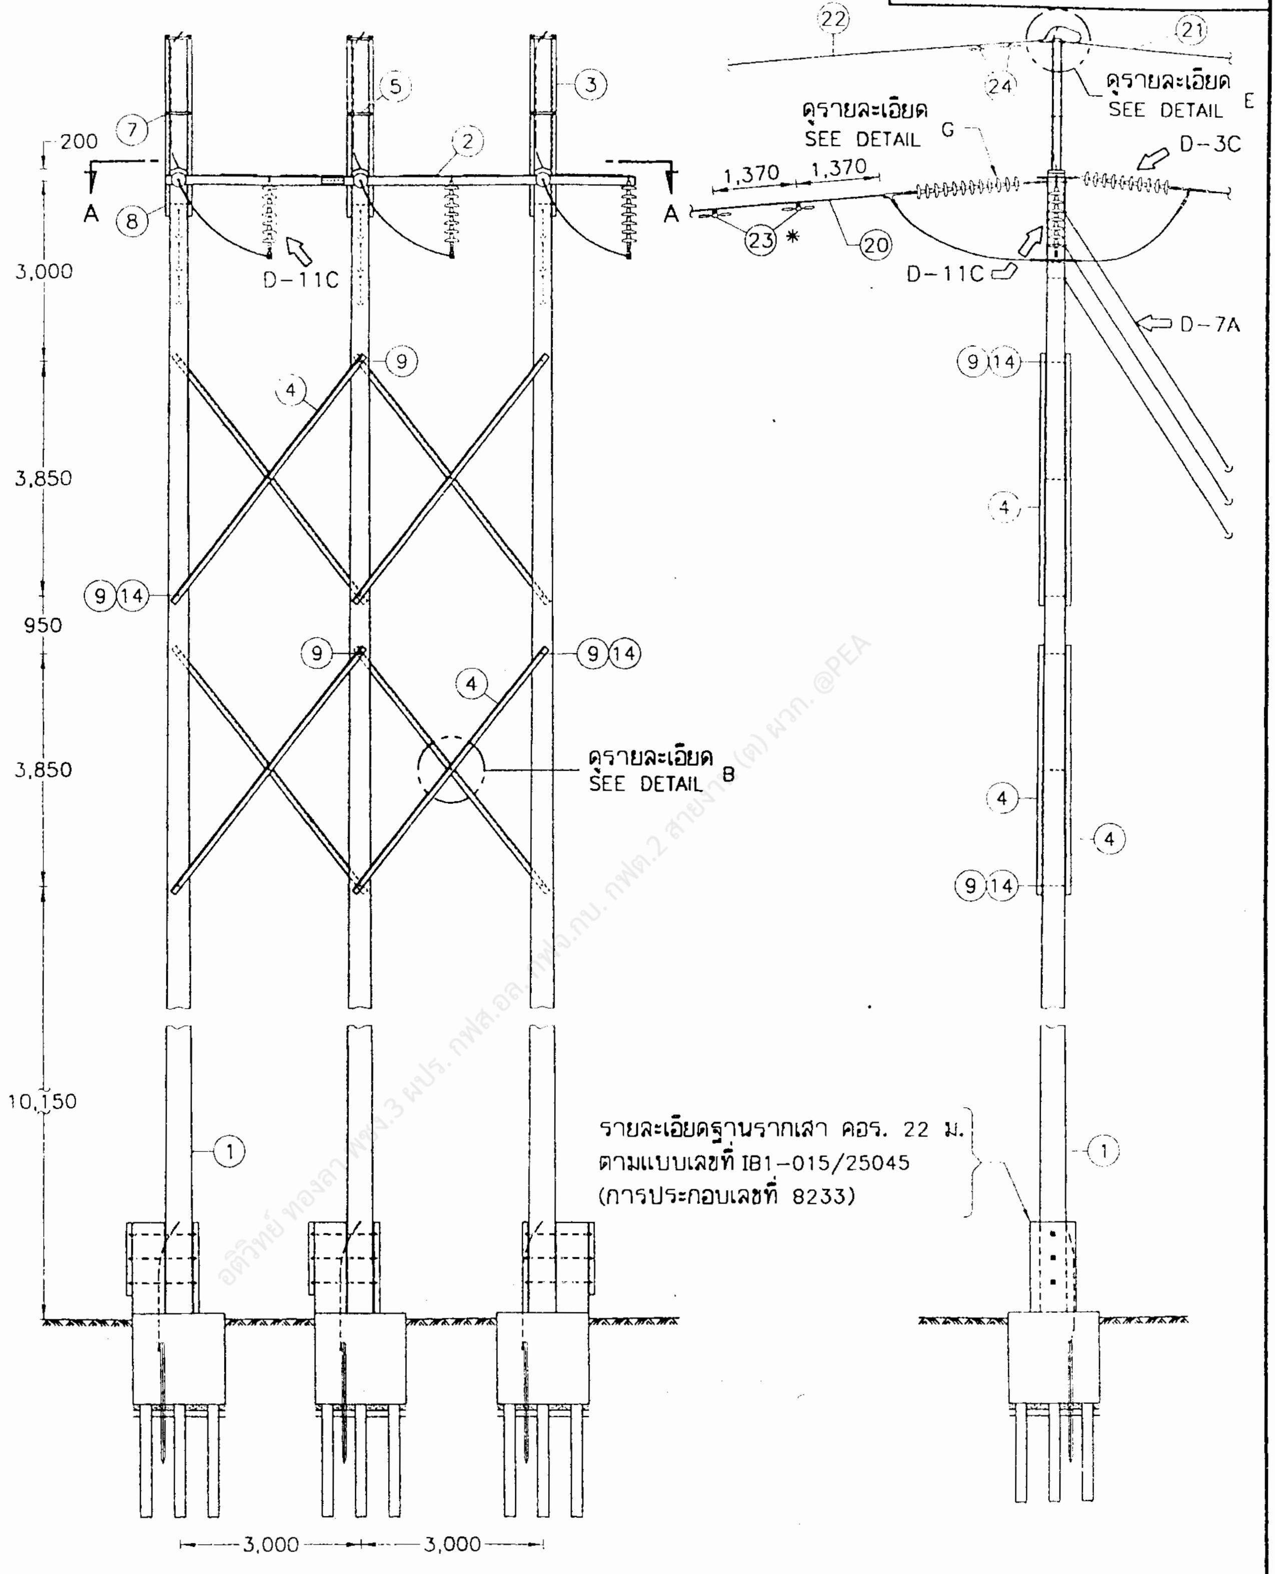

22
21
24
ดูรายละเอียด
SEE DETAIL E
ดูรายละเอียด
SEE DETAIL G
D-3C
5
3
7
2
200
1,370
1,370
A
A
8
23
*
20
D-11C
D-11C
D-7A
3,000
9
14
4
3,850
4
9
14
950
9
9
14
4
3,850
ดูรายละเอียด
SEE DETAIL B
4
4
9
14
10,150
1
1
รายละเอียดฐานรากเสา คอร. 22 ม.
ตามแบบเลขที่ IB1-015/25045
(การประกอบเลขที่ 8233)
3,000
3,000

อดิวิทย์ ทองลา พชง.3 ผปร. กฟส.อล. กฟจ.กบ. กฟต.2 สายงาน (ต) ผวก. @PEA

กองวิศวกรรมไฟฟ้าและเครื่องกล
ฝ่ายวิศวกรรม

การไฟฟ้าส่วนภูมิภาค

ใช้แทนแบบ ....
ถูกแทนโดยแบบ ....

ผู้เขียน S.
ผู้สำรวจ ....
วิศวกร ....
หัวหน้าแผนก ....
ผู้อำนวยการกอง ....
ผู้อำนวยการฝ่าย ....

ผู้ว่าการ ....

2 1 ธ.ค. 2541

115 kV วงจรเดียว สายไฟฟ้าเดียว
โครงสร้างเสา ช่วง 200-350 ม.
แบบ SS-LS-1

เขียนเสร็จวันที่ 13 ต.ค. 2541
แก้แบบวันที่ 12 มิ.ย. 2550
มิติเป็น มิลลิเมตร
มาตราส่วน 1 : 125

รองผู้ว่าการเทคนิคและบริการ
....

115 kV SINGLE CIRCUIT SINGLE CONDUCTOR
SPANS 200-350 m STRUCTURE
TYPE SS-LS-1

แบบเลขที่ SA1-015/41015
แผ่นที่ 1 ของจำนวน 8 แผ่น

2 1 ธ.ค. 2541

การประกอบเลขที่
ASSEMBLY NO. **5224**

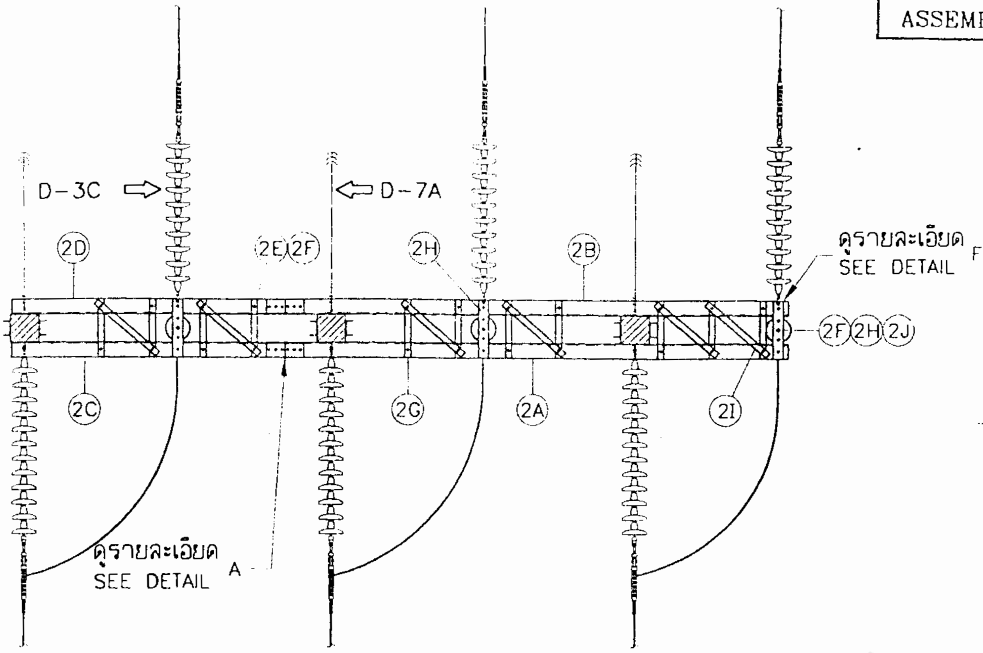
D-3C
D-7A
2D
2E 2F
2H
2B
ดูรายละเอียด F
SEE DETAIL F
2F 2H 2J
2C
2G
2A
2I
ดูรายละเอียด A
SEE DETAIL A

รูปตัด A–A
SECTION A–A

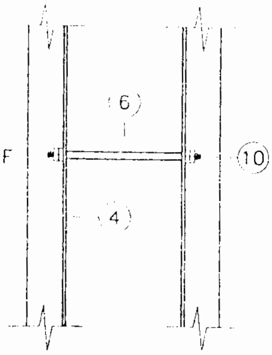

รายละเอียด B
DETAIL B

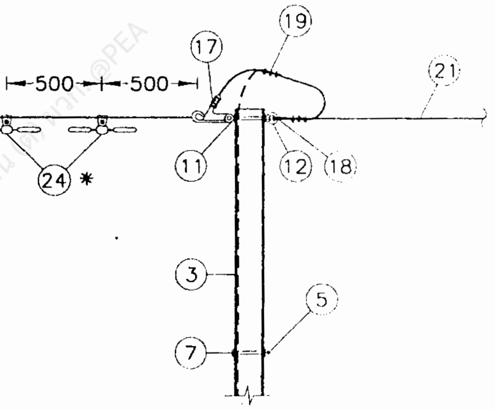
19
17
22
500
500
21
24 *
11
12
18
3
5
7

รายละเอียด E
DETAIL E

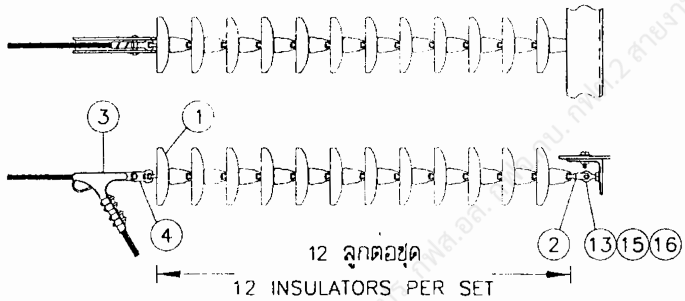
3
1
4
2
13 15 16
12 ลูกต่อชุด
12 INSULATORS PER SET

รายละเอียด G
DETAIL G

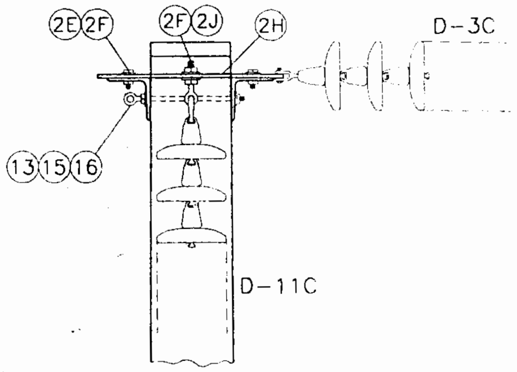
2E 2F
2F 2J
2H
D-3C
13 15 16
D-11C

รายละเอียด F
DETAIL F

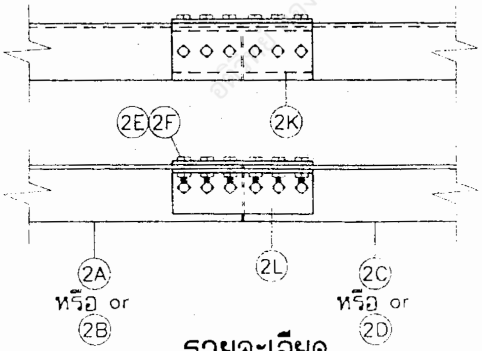
2E 2F
2K
2A
หรือ or
2B
2L
2C
หรือ or
2D

รายละเอียด A
DETAIL A

กองวิศวกรรมไฟฟ้าและเครื่องกล
ฝ่ายวิศวกรรม

การไฟฟ้าส่วนภูมิภาค

ใช้แทนแบบ ....
ถูกแทนโดยแบบ ....

ผู้เขียน Sayphabit
ผู้สำรวจ ....
วิศวกร ....
หัวหน้าแผนก ....
ผู้อำนวยการกอง ....
ผู้อำนวยการฝ่าย ....

ผู้ว่าการ ....
21 ธ.ค. 2541

115 kV วงจรเดียว สายไฟฟ้าเดี่ยว
โครงสร้างเสา ช่วง 200-350 ม.
แบบ SS-LS-1

เขียนเสร็จวันที่ 13 ต.ค. 2541
แก้แบบวันที่ 12เม.ย.2550
มิติเป็น มิลลิเมตร
มาตราส่วน ....

รองผู้ว่าการเทคนิคและบริการ
....

115 kV SINGLE CIRCUIT SINGLE CONDUCTOR
SPANS 200-350 m STRUCTURE
TYPE SS-LS-1

แบบเลขที่ SA1-015/41015
แผ่นที่ 2 ของจำนวน 8 แผ่น

21 ธ.ค. 2541

การประกอบเลขที่
ASSEMBLY NO. 5224

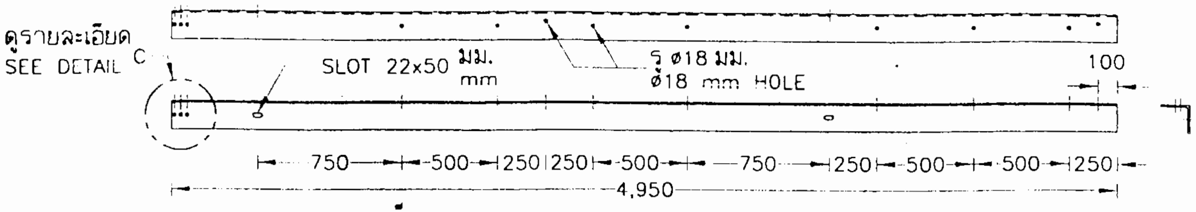
ดูรายละเอียด
SEE DETAIL C
SLOT 22x50 มม. mm
รู ø18 มม.
ø18 mm HOLE
100
750 500 250 250 500 750 250 500 500 250
4,950

(2A) เหล็กฉาก ขนาด L 150x150x12 มม. ยาว 4,950 มม.
STEEL ANGLE 150x150x12 mm, 4,950 mm LONG

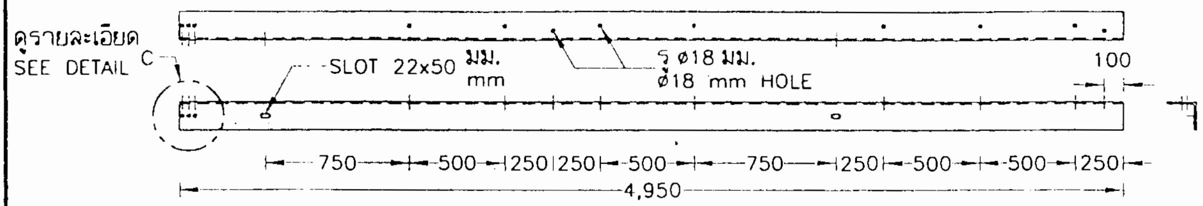
ดูรายละเอียด
SEE DETAIL C
SLOT 22x50 มม. mm
รู ø18 มม.
ø18 mm HOLE
100
750 500 250 250 500 750 250 500 500 250
4,950

(2B) เหล็กฉาก ขนาด L 150x150x12 มม. ยาว 4,950 มม.
STEEL ANGLE 150x150x12 mm, 4,950 mm LONG

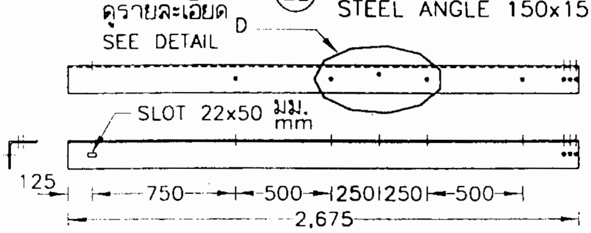
ดูรายละเอียด
SEE DETAIL D
SLOT 22x50 มม. mm
125
750 500 250 250 500
2,675

(2C) เหล็กฉาก ขนาด L 150x150x12 มม. ยาว 2,675 มม.
STEEL ANGLE 150x150x12 mm, 2,675 mm LONG

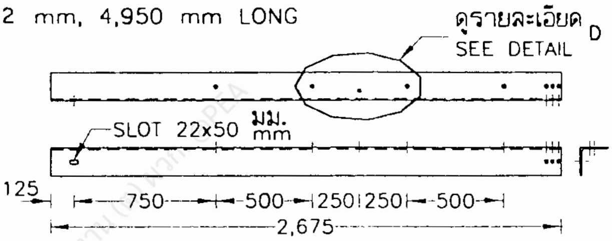
ดูรายละเอียด
SEE DETAIL D
SLOT 22x50 มม. mm
125
750 500 250 250 500
2,675

(2D) เหล็กฉาก ขนาด L 150x150x12 มม. ยาว 2,675 มม.
STEEL ANGLE 150x150x12 mm, 2,675 mm LONG

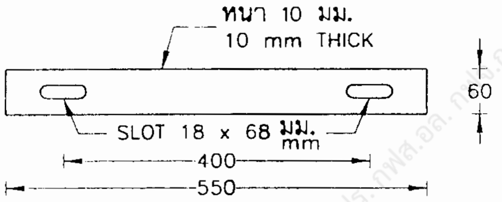
หนา 10 มม.
10 mm THICK
60
SLOT 18 x 68 มม. mm
400
550

(2G) แผ่นเหล็ก ขนาด 60x10 มม. ยาว 550 มม.
PLATE STEEL 60x10 mm, 550 mm LONG

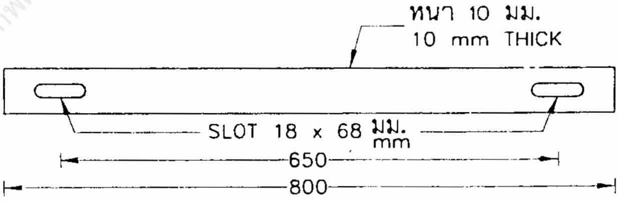
หนา 10 มม.
10 mm THICK
SLOT 18 x 68 มม. mm
650
800

(2I) แผ่นเหล็ก ขนาด 60x10 มม. ยาว 800 มม.
PLATE STEEL 60x10 mm, 800 mm LONG

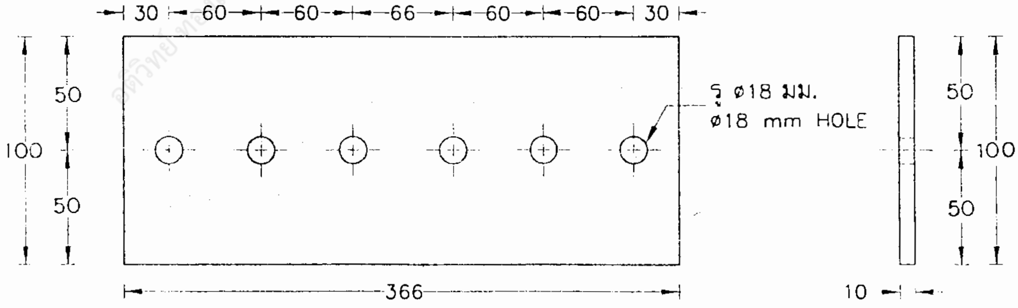
30 60 60 66 60 60 30
50
100
50
รู ø18 มม.
ø18 mm HOLE
366
50
100
50
10

(2K) แผ่นเหล็ก ขนาด 100x10 มม. ยาว 366 มม.
PLATE STEEL 100x10 mm, 366 mm LONG

กองวิศวกรรมไฟฟ้าและเครื่องกล
ฝ่ายวิศวกรรม

ผู้เขียน
ผู้สำรวจ ....
วิศวกร ....
หัวหน้าแผนก ....
ผู้อำนวยการกอง ....
ผู้อำนวยการฝ่าย ....

รองผู้ว่าการเทคนิคและบริการ
....

การไฟฟ้าส่วนภูมิภาค

ผู้ว่าการ 21 ธ.ค. 2541 ....

115 kV วงจรเดี่ยว สายไฟฟ้าเดี่ยว
โครงสร้างเสา ช่วง 200-350 ม.
แบบ SS-LS-1

115 kV SINGLE CIRCUIT SINGLE CONDUCTOR
SPANS 200-350 m STRUCTURE
TYPE SS-LS-1

ใช้แทนแบบ ....
ถูกแทนโดยแบบ ....
เขียนเสร็จวันที่ 13 ต.ค. 2541
แก้แบบวันที่ 12 เม.ย. 2550
มิติเป็น มิลลิเมตร
มาตราส่วน ....
แบบเลขที่ SA1-015/41015
แผ่นที่ 3 ของจำนวน 8 แผ่น

21 ธ.ค. 2541

การประกอบเลขที่
ASSEMBLY NO. 5224

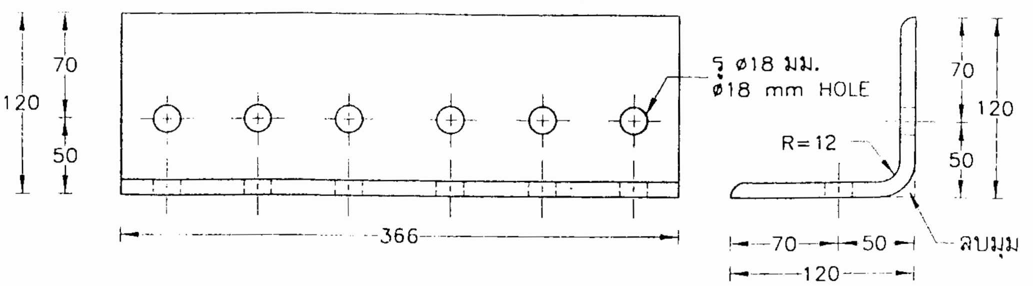
30
60
60
66
60
60
30
120
70
50
รู ø18 มม.
ø18 mm HOLE
366
R=12
70
120
50
70
50
120
ลบมุม

(2L) เหล็กฉาก ขนาด L 120x120x8 มม. ยาว 366 มม.
STEEL ANGLE 120x120x8 mm, 366 mm LONG

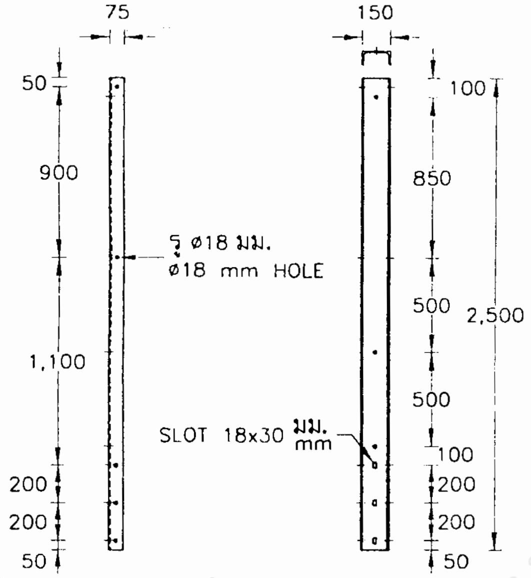
75
150
50
900
1,100
200
200
50
รู ø18 มม.
ø18 mm HOLE
SLOT 18x30 มม. mm
100
850
500
500
100
200
200
50
2,500

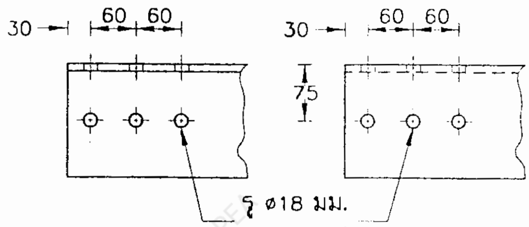
30
60
60
30
60
60
75
รู ø18 มม.
ø18 mm HOLE

รายละเอียด
DETAIL C

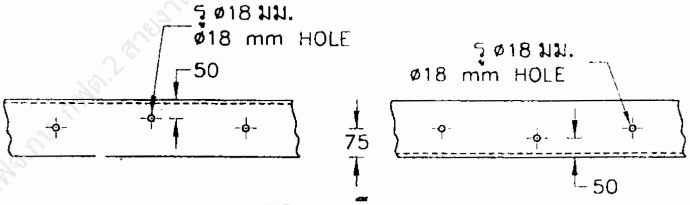
รู ø18 มม.
ø18 mm HOLE
50
รู ø18 มม.
ø18 mm HOLE
75
50

③ เหล็กรูปรางน้ำ ขนาด 150x75x6.5 มม. ยาว 2,500 มม.
STEEL CHANNEL 150x75x6.5 mm, 2,500 mm LONG

รายละเอียด
DETAIL D

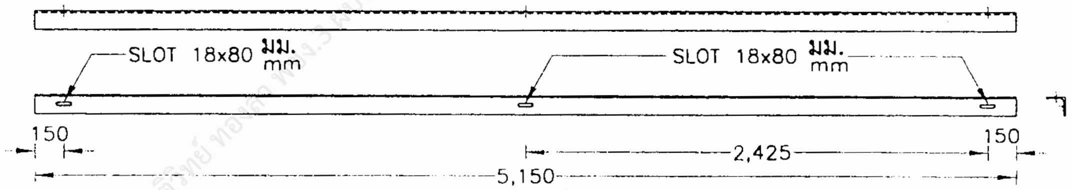
SLOT 18x80 มม. mm
SLOT 18x80 มม. mm
150
2,425
150
5,150

④ เหล็กฉาก ขนาด L 100x100x7 มม. ยาว 5,150 มม.
STEEL ANGLE 100x100x7 mm, 5,150 mm LONG

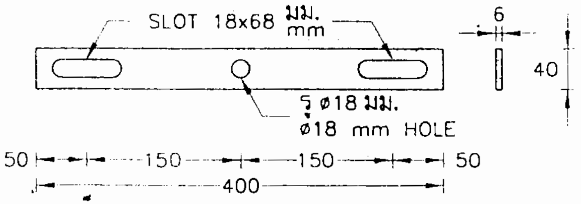
SLOT 18x68 มม. mm
6
40
รู ø18 มม.
ø18 mm HOLE
50
150
150
50
400

⑤ แผ่นเหล็ก ขนาด 6x40 มม. ยาว 400 มม.
PLATE, STEEL 6x40 mm, 400 mm LONG

กองวิศวกรรมไฟฟ้าและเครื่องกล
ฝ่ายวิศวกรรม

ผู้เขียน
ผู้สำรวจ
วิศวกร
หัวหน้าแผนก
ผู้อำนวยการกอง
ผู้อำนวยการฝ่าย
รองผู้ว่าการเทคนิคและบริการ

การไฟฟ้าส่วนภูมิภาค

ผู้ว่าการ 21 ธ.ค. 2541

115 kV วงจรเดียว สายไฟฟ้าเดี่ยว
โครงสร้างเสา ช่วง 200-350 ม.
แบบ SS-LS-1

115 kV SINGLE CIRCUIT SINGLE CONDUCTOR
SPANS 200-350 m STRUCTURE
TYPE SS-LS-1

ใช้แทนแบบ ....
ถูกแทนโดยแบบ ....
เขียนเสร็จวันที่ 13 ต.ค. 2541
แก้แบบวันที่ 12เมษ.2550
มิติเป็น มิลลิเมตร
มาตราส่วน ....
แบบเลขที่ SA1-015/41015
แผ่นที่ 4 ของจำนวน 8 แผ่น

21 ธ.ค. 2541

การประกอบเลขที่
ASSEMBLY NO. 5224

บัญชีวัสดุ
BILL OF MATERIAL

ลำดับที่ ITEM	รายละเอียด DESCRIPTION	จำนวน REQ'D	วัสดุเลขที่ MAT. NO.
1	เสาคอนกรีต 22 เมตร POLE, CONCRETE, 22 m LONG	3	1000010011
2A	คอนสาย แบบเหล็กฉาก ขนาด 150x150x12 มม. ยาว 4,950 มม.แบบ 2A CROSSARM, STEEL ANGLE 150x150x12 mm, 4,950 mm LONG, TYPE 2A	1	1000120007
2B	คอนสาย แบบเหล็กฉาก ขนาด 150x150x12 มม. ยาว 4,950 มม.แบบ 2B CROSSARM, STEEL ANGLE 150x150x12 mm, 4,950 mm LONG, TYPE 2B	1	1000120008
2C	คอนสาย แบบเหล็กฉาก ขนาด 150x150x12 มม. ยาว 2,675 มม.แบบ 2C CROSSARM, STEEL ANGLE 150x150x12 mm, 2,675 mm LONG, TYPE 2C	1	1000120009
2D	คอนสาย แบบเหล็กฉาก ขนาด 150x150x12 มม. ยาว 2,675 มม.แบบ 2D CROSSARM, STEEL ANGLE 150x150x12 mm, 2,675 mm LONG, TYPE 2D	1	1000120010
2E	สลักเกลียว M 16x75 มม. พร้อมแหวนกลม 2 อัน BOLT, MACHINE M 16x75 mm ; COMPLETE WITH 2 ROUND WASHERS	52	1010110400
2F	แหวนรองแบบสปริง ขนาดระบุ 16 มม. ประเภทใช้งานทั่วไป มอก. 259 WASHER, LOCK, SPRING, SIZE 16 mm, GENERAL PURPOSE, TIS 259	52	1010180301
2G	แผ่นเหล็ก ขนาด 10x60 มม. ยาว 550 มม. PLATE, STEEL 10x60 mm, 550 mm LONG	11	1010030009
2H	แผ่นเหล็ก ขนาด 12x100 มม. ยาว 650 มม. PLATE, STEEL 12x100 mm, 650 mm LONG	3	1010030100
2I	แผ่นเหล็ก ขนาด 10x60 มม. ยาว 800 มม. PLATE, STEEL 10x60 mm, 800 mm LONG	6	1010030010
2J	สลักห่วงโอเวล M 16x150 มม. (เพิ่มนัทอีกหนึ่งอัน) BOLT, OVAL EYE M 16x150 mm (ADD. ONE SQUARE NUT)	3	1010150000
2K	แผ่นเหล็ก ขนาด 100x10 มม. ยาว 366 มม. PLATE, STEEL 100x10 mm, 366 mm LONG	4	1010030012
2L	เหล็กฉาก ขนาด 120x120x8 มม. ยาว 366 มม. STEEL ANGLE 120x120x8 mm, 366 mm LONG	2	1010010300
3	เหล็กรูปรางน้ำ ขนาด 150x75x6.5 มม. ยาว 2,500 มม. STEEL CHANNEL 150x75x6.5 mm, 2,500 mm LONG	6	1010000304
4	เหล็กฉาก ขนาด 100x100x7 มม. ยาว 5,150 มม. STEEL ANGLE 100x100x7 mm, 5,150 mm LONG	8	1010010201
5	แผ่นเหล็ก ขนาด 6x40 มม. ยาว 400 มม. PLATE, STEEL 6x40 mm, 400 mm LONG	12	1010030011
6	ท่อเหล็ก ขนาด ø 20 มม. ความยาวตามต้องการ (310-360 มม.) PIPE, STEEL ø 20 mm ; LENGTH AS REQUIRED (310-360 mm LONG)	4	1010050007
7	สลักเกลียว M 16x200 มม. BOLT, MACHINE M 16x200 mm	18	1010110202
8	สลักเกลียว M 16x350 มม. BOLT, MACHINE M 16x350 mm	9	1010100205
9	สลักเกลียว M 16x400 มม. BOLT, MACHINE M 16x400 mm	12	1010120000

กองวิศวกรรมไฟฟ้าและเครื่องกล
ฝ่ายวิศวกรรม

ผู้เขียน
ผู้สำรวจ
วิศวกร
หัวหน้าแผนก
ผู้อำนวยการกอง
ผู้อำนวยการฝ่าย

รองผู้ว่าการเทคนิคและบริการ

การไฟฟ้าส่วนภูมิภาค

ผู้ว่าการ
21 ธ.ค. 2541

115 kV วงจรเดียว สายไฟฟ้าเดี่ยว
โครงสร้างเสา ช่วง 200-350 ม.
แบบ SS-LS-1

115 kV SINGLE CIRCUIT SINGLE CONDUCTOR
SPANS 200-350 m STRUCTURE
TYPE SS-LS-1

ใช้แทนแบบ
ถูกแทนโดยแบบ
เขียนเสร็จวันที่ 13 ต.ค. 2541
แก้แบบวันที่ 12 เม.ย. 2550
มิติเป็น
มาตราส่วน

แบบเลขที่ SA1-015/41015
แผ่นที่ 5 ของจำนวน 8 แผ่น

21 ธ.ค. 2541

การประกอบเลขที่ ASSEMBLY NO.	5224

บัญชีวัสดุ
BILL OF MATERIAL

ลำดับที่ ITEM	รายละเอียด DESCRIPTION	จำนวน REQ'D	วัสดุเลขที่ MAT. NO.
10	สลักเกลียวตลอด M 16x450 มม. BOLT, DOUBLE, ARMING, M 16x450 mm	4	1010110207
11	สลักห่วงกลม M 16x300 มม. BOLT, ROUND EYE M 16x300 mm	3	1010140003
12	นัทรูปห่วง M 16 NUT, EYE M 16	3	1010180001
13	สลักห่วงโอเวล M 20x350 มม. BOLT, OVAL EYE M 20x350 mm	3	1010150100
14	แหวนสี่เหลี่ยมแบน 52x52x4.5 มม. รู ø18 มม. WASHER, SQUARE, FLAT, 52x52x4.5 mm, HOLE ø18 mm	8	1010180100
15	แหวนสี่เหลี่ยมแบน 60x60x5 มม. รู ø22 มม. WASHER, SQUARE, FLAT, 60x60x5 mm, HOLE ø22 mm	6	1010180101
16	แหวนรองแบบสปริง ขนาดระบุ 20 มม. ประเภทใช้งานทั่วไป มอก. 259 WASHER, LOCK, SPRING, SIZE 20 mm, GENERAL PURPOSE, TIS 259	3	1010180302
17	สเตรนแคล้มป์ สำหรับสายลวดเหล็กตีเกลียว ขนาด 50 ต.มม. CLAMP, STRAIN, FOR STEEL STRANDED WIRE 50 mm^2	3	1030110300
18	กายทิมเบิ้ล สำหรับสายยึดโยง 50-95 ต.มม. THIMBLE, GUY, FOR STEEL WIRE 50-95 mm^2	3	1010210304
19	ยูแคล้มป์ สลัก 1 ตัว เอ็ม 8 CLAMP, SINGLE U-BOLT, M 8	18	1010230000
20	สายอลูมิเนียมแกนเหล็ก ขนาด 380/50 ต.มม. ความยาวตามต้องการ CONDUCTOR, ACSR 380/50 mm^2 ; LENGTH AS REQUIRED	ม. m	1020020008
21	ลวดเหล็กตีเกลียว ขนาด 35 ต.มม. ความยาวตามต้องการ WIRE, STEEL STRANDED 35 mm^2 ; LENGTH AS REQUIRED	ม. m	1010100003
22	ลวดเหล็กตีเกลียว ขนาด 50 ต.มม. ความยาวตามต้องการ WIRE, STEEL STRANDED 50 mm^2; LENGTH AS REQUIRED	ม. m	1010100004
23*	ไวเบรชั่น แดมเปอร์ แบบ ดัมเบล นน. 7.3 กก. (16 ปอนด์) VIBRATION DAMPER, TYPE DUMBBELL, 7.3 kg (16 POUNDS) WEIGHT	6	1020200107
24*	ไวเบรชั่น แดมเปอร์ แบบ ดัมเบล นน. 1.6 กก. (3.5 ปอนด์) VIBRATION DAMPER, TYPE DUMBBELL, 1.6 kg (3.5 POUNDS) WEIGHT	6	1020200106

กองวิศวกรรมไฟฟ้าและเครื่องกล ฝ่ายวิศวกรรม	การไฟฟ้าส่วนภูมิภาค	ใช้แทนแบบ .... ถูกแทนโดยแบบ ....
ผู้เขียน Supphakit Boonng ผู้สำรวจ .... วิศวกร .... หัวหน้าแผนก .... ผู้อำนวยการกอง .... ผู้อำนวยการฝ่าย	ผู้ว่าการ 21 ธ.ค. 2541 115 kV วงจรเดี่ยว สายไฟฟ้าเดี่ยว โครงสร้างเสา ช่วง 200-350 ม. แบบ SS-LS-1	เขียนเสร็จวันที่ 13 ต.ค. 2541 แก้แบบวันที่ 12 เม.ย. 2550 มิติเป็น .... มาตราส่วน ....
รองผู้ว่าการเทคนิคและบริการ	115 kV SINGLE CIRCUIT SINGLE CONDUCTOR SPANS 200-350 m STRUCTURE TYPE SS-LS-1	แบบเลขที่ SA1-015/41015 แผ่นที่ 6 ของจำนวน 8 แผ่น

21 ธ.ค. 2541

การประกอบเลขที่ ASSEMBLY NO. **5224**

	บัญชีวัสดุ BILL OF MATERIAL		
ลำดับที่ ITEM	รายละเอียด G DETAIL	จำนวน REQ'D	วัสดุเลขที่ MAT. NO.
1	ลูกถ้วยแขวน แบบ จ. (แบบ 52-8) มอก. 354 INSULATOR, SUSPENSION TYPE, TYPE E (CLASS 52-8), TIS 354	36	1030020002
2	ข้อต่อแบบ บอล-เคลวิส ANSI แบบ K BALL-CLEVIS, ANSI, TYPE K	3	1030140001
3	สเตรนแคล้มป์พร้อมแคล้มป์ปิ้งคีปเปอร์ สำหรับสายอะลูมิเนียมแกนเหล็ก CLAMP, STRAIN, WITH CLAMPING KEEPER, FOR ACSR CONDUCTOR	3	1030110105
4	ข้อต่อแบบซ็อคเก็ต-อาย ANSI แบบ B SOCKET-EYE, ANSI, TYPE B	3	1030140003

	รายละเอียด DESCRIPTION	จำนวน REQ'D
D-11C	การประกอบลูกถ้วยแขวน SUSPENSION INSULATOR ASSEMBLY	3
D-3C	การประกอบลูกถ้วยแขวน SUSPENSION INSULATOR ASSEMBLY	3
D-7A	การประกอบสายยึดโยง (แบบที่ 2) GUY ASSEMBLY (TYPE 2)	9
	ฐานรากเสา 22 ม. แบบเลขที่ IB1-015/25045 CONCRETE FOUNDATION FOR 22 m POLE, DWG NO. IB1-015/25045	3
	สมอบก คอนกรีต แบบเลขที่ IB1-015/35009 หรือ SA1-015/40008 CONCRETE ANCHOR, DWG NO. IB1-015/35009 or SA1-015/40008	3

อติวิทย์ ทองลา พชง.3 ผปร. [illegible] กบ. กฟฉ.2 สายงาน (ต) ผวก. @PEA

กองวิศวกรรมไฟฟ้าและเครื่องกล
ฝ่ายวิศวกรรม

การไฟฟ้าส่วนภูมิภาค

ใช้แทนแบบ ....
ถูกแทนโดยแบบ ....

ผู้เขียน
ผู้สำรวจ....................
วิศวกร
หัวหน้าแผนก
ผู้อำนวยการกอง
ผู้อำนวยการฝ่าย

ผู้ว่าการ .... 21 ธ.ค. 2541

เขียนเสร็จวันที่ 13 ต.ค. 2541
แก้แบบวันที่ 12 เม.ย. 2550
มิติเป็น..................
มาตราส่วน...............

115 kV วงจรเดี่ยว สายไฟฟ้าเดี่ยว
โครงสร้างเสา ช่วง 200-350 ม.
แบบ SS-LS-1

รองผู้ว่าการเทคนิคและบริการ
....

115 kV SINGLE CIRCUIT SINGLE CONDUCTOR
SPANS 200-350 m STRUCTURE
TYPE SS-LS-1

แบบเลขที่ SA1-015/41015
แผ่นที่ 7 ของจำนวน 8 แผ่น

21 ธ.ค. 2541

การประกอบเลขที่ ASSEMBLY NO.	5224

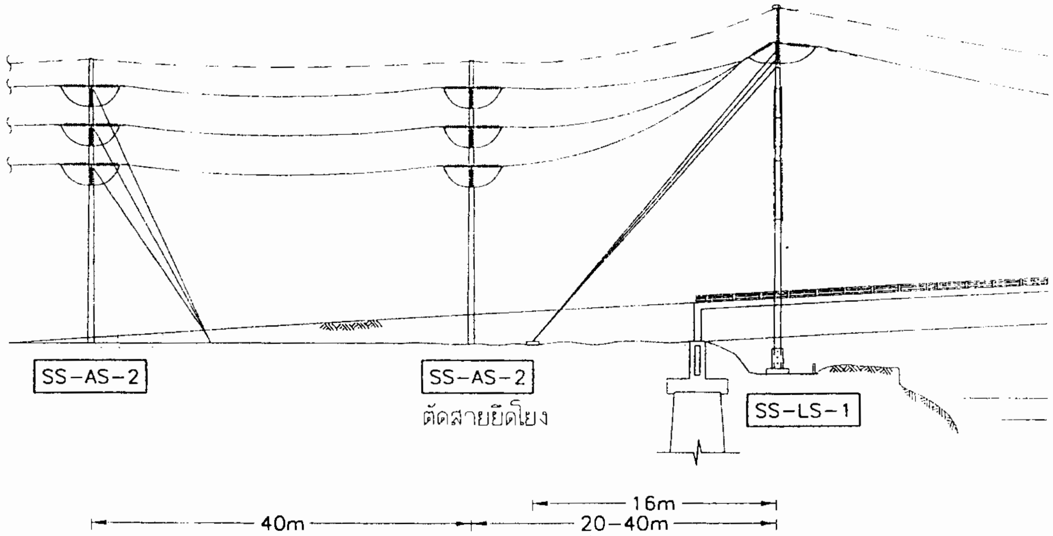

หมายเหตุ

1. มีระยะห่างช่วงเสาสูงสุด 350 ม.
2. สายไฟฟ้า สูงจากระดับน้ำสูงสุดไม่น้อยกว่า 15 ม.

* สามารถเลือกขนาด, ระยะและจำนวนของไวเบรชั่น แดมเปอร์ ได้ตามความเหมาะสม

NOTES

1. MAXIMUM SPAN LENGTH 350 m .
2. CONDUCTOR SHALL HAVE HEIGHT NOT LESS THAN 15 m , ABOVE MAXIMUM WATER LEVEL.

* SIZE, DISTANCE, AND NUMBER OF VIBRATION DAMPERS CAN BE CHOOSE TO BE SUITABLE.

อติวิทย์ ทองลา พชง.3 ผปร. กฟส.อล. [illegible] กบ. กฟต.2 สายงาน (ต) ผวก. @PEA

กองวิศวกรรมไฟฟ้าและเครื่องกล ฝ่ายวิศวกรรม	การไฟฟ้าส่วนภูมิภาค	ใช้แทนแบบ .... ถูกแทนโดยแบบ ....
ผู้เขียน .... ผู้สำรวจ .... วิศวกร.................. หัวหน้าแผนก.................. ผู้อำนวยการกอง.................. ผู้อำนวยการฝ่าย..................	ผู้ว่าการ.................... 21 ธ.ค. 2541	เขียนเสร็จวันที่ 13 ต.ค. 2541 แก้แบบวันที่ 12 เม.ย. 2550
	115 kV วงจรเดี่ยว สายไฟฟ้าเดี่ยว โครงสร้างเสา ช่วง 200-350 ม. แบบ SS-LS-1	มิติเป็น ......เมตร......... มาตราส่วน................
รองผู้ว่าการเทคนิคและบริการ	115 kV SINGLE CIRCUIT SINGLE CONDUCTOR SPANS 200-350 m STRUCTURE TYPE SS-LS-1	แบบเลขที่ SA1-015/41015 แผ่นที่ 8 ของจำนวน 8 แผ่น

21 ธ.ค. 2541