การประกอบเลขที่ 0309
ASSEMBLY NO.

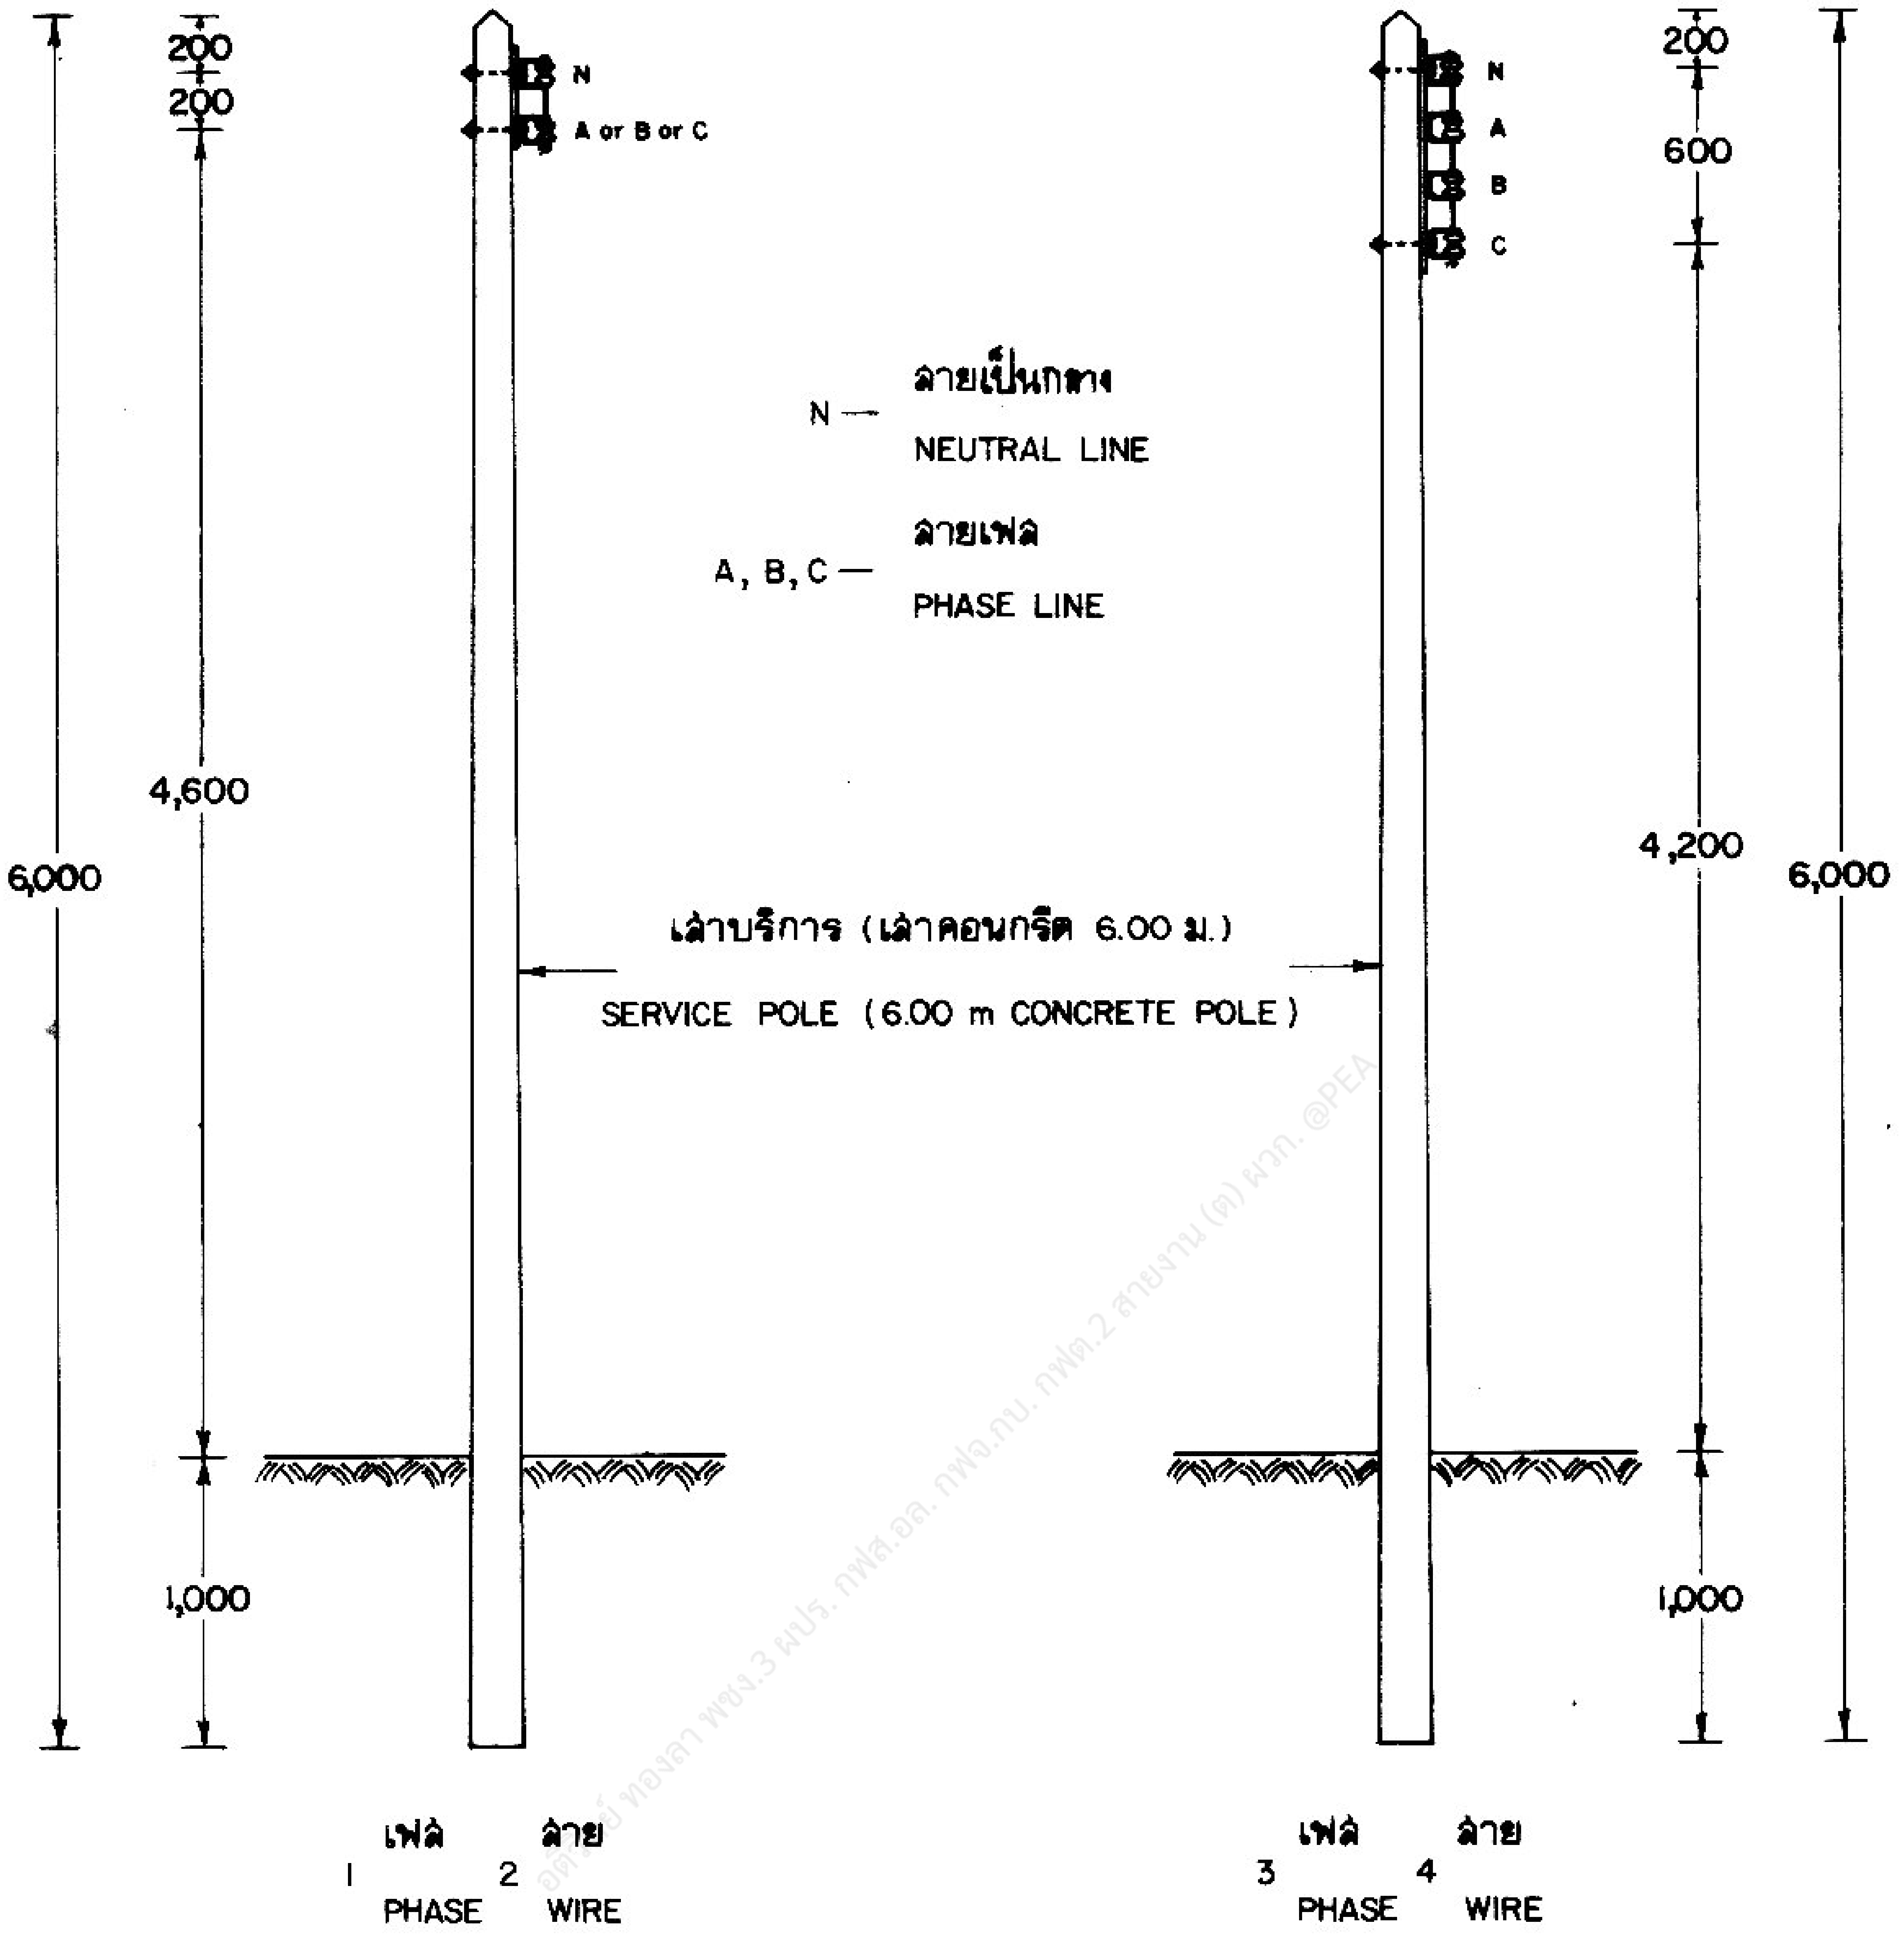
200
200
N
A or B or C
4,600
6,000
1,000
200
600
N
A
B
C
4,200
6,000
1,000
N — สายเป็นกลาง NEUTRAL LINE
A, B, C — สายเฟส PHASE LINE
เสาบริการ (เสาคอนกรีต 6.00 ม.)
SERVICE POLE (6.00 m CONCRETE POLE)
1 เฟส PHASE 2 สาย WIRE
3 เฟส PHASE 4 สาย WIRE

หมายเหตุ ระยะต่ำสุดของสายระบบจำหน่ายแรงต่ำ เหนือพื้นดินภายในบริเวณของผู้ใช้ไฟ 3.70 เมตร.

NOTE MINIMUM GROUND CLEARANCE OF L.T. LINE IN CUSTOMER AREA 3.70 METERS.

อดิศักดิ์ ทองลา พชง.3 ผปร. กฟส.อล. กฟจ.กบ. กฟต.2 สายงาน (ต) ผวก. @PEA

กองวิศวกรรมไฟฟ้าและเครื่องกล ฝ่ายวิศวกรรม	การไฟฟ้าส่วนภูมิภาค	ใช้แทนแบบ ถูกแทนโดยแบบ
ผู้เขียน ผู้ตรวจ วิศวกร กิตติพงษ์ หัวหน้าแผนก หัวหน้ากอง ผู้อำนวยการฝ่าย	ผู้ว่าการ 24 มิ.ย. 23	เขียนเสร็จวันที่ 10 มิ.ย. 23 แก้แบบวันที่ 21 มี.ค. 27
	ลักษณะการติดตั้งอุปกรณ์บนเสาบริการ ขนาด 6.00 ม. 1 สำหรับพาดสายแรงต่ำภายในบริเวณของผู้ใช้ไฟ	คิดเป็น มม. มาตราส่วน 1:50
รองผู้ว่าการฝ่ายเทคนิค	TYPICAL INSTALLATIONS ON 6.00 m SERVICE POLE 1 FOR L.T. LINE CONSTRUCTION IN CUSTOMER AREA	แบบเลขที่ SAI-015/23070 แผ่นที่ 1 ของจำนวน 2 แผ่น

17 มิ.ย. 2523

การประกอบเลขที่ ASSEMBLY NO. 0309

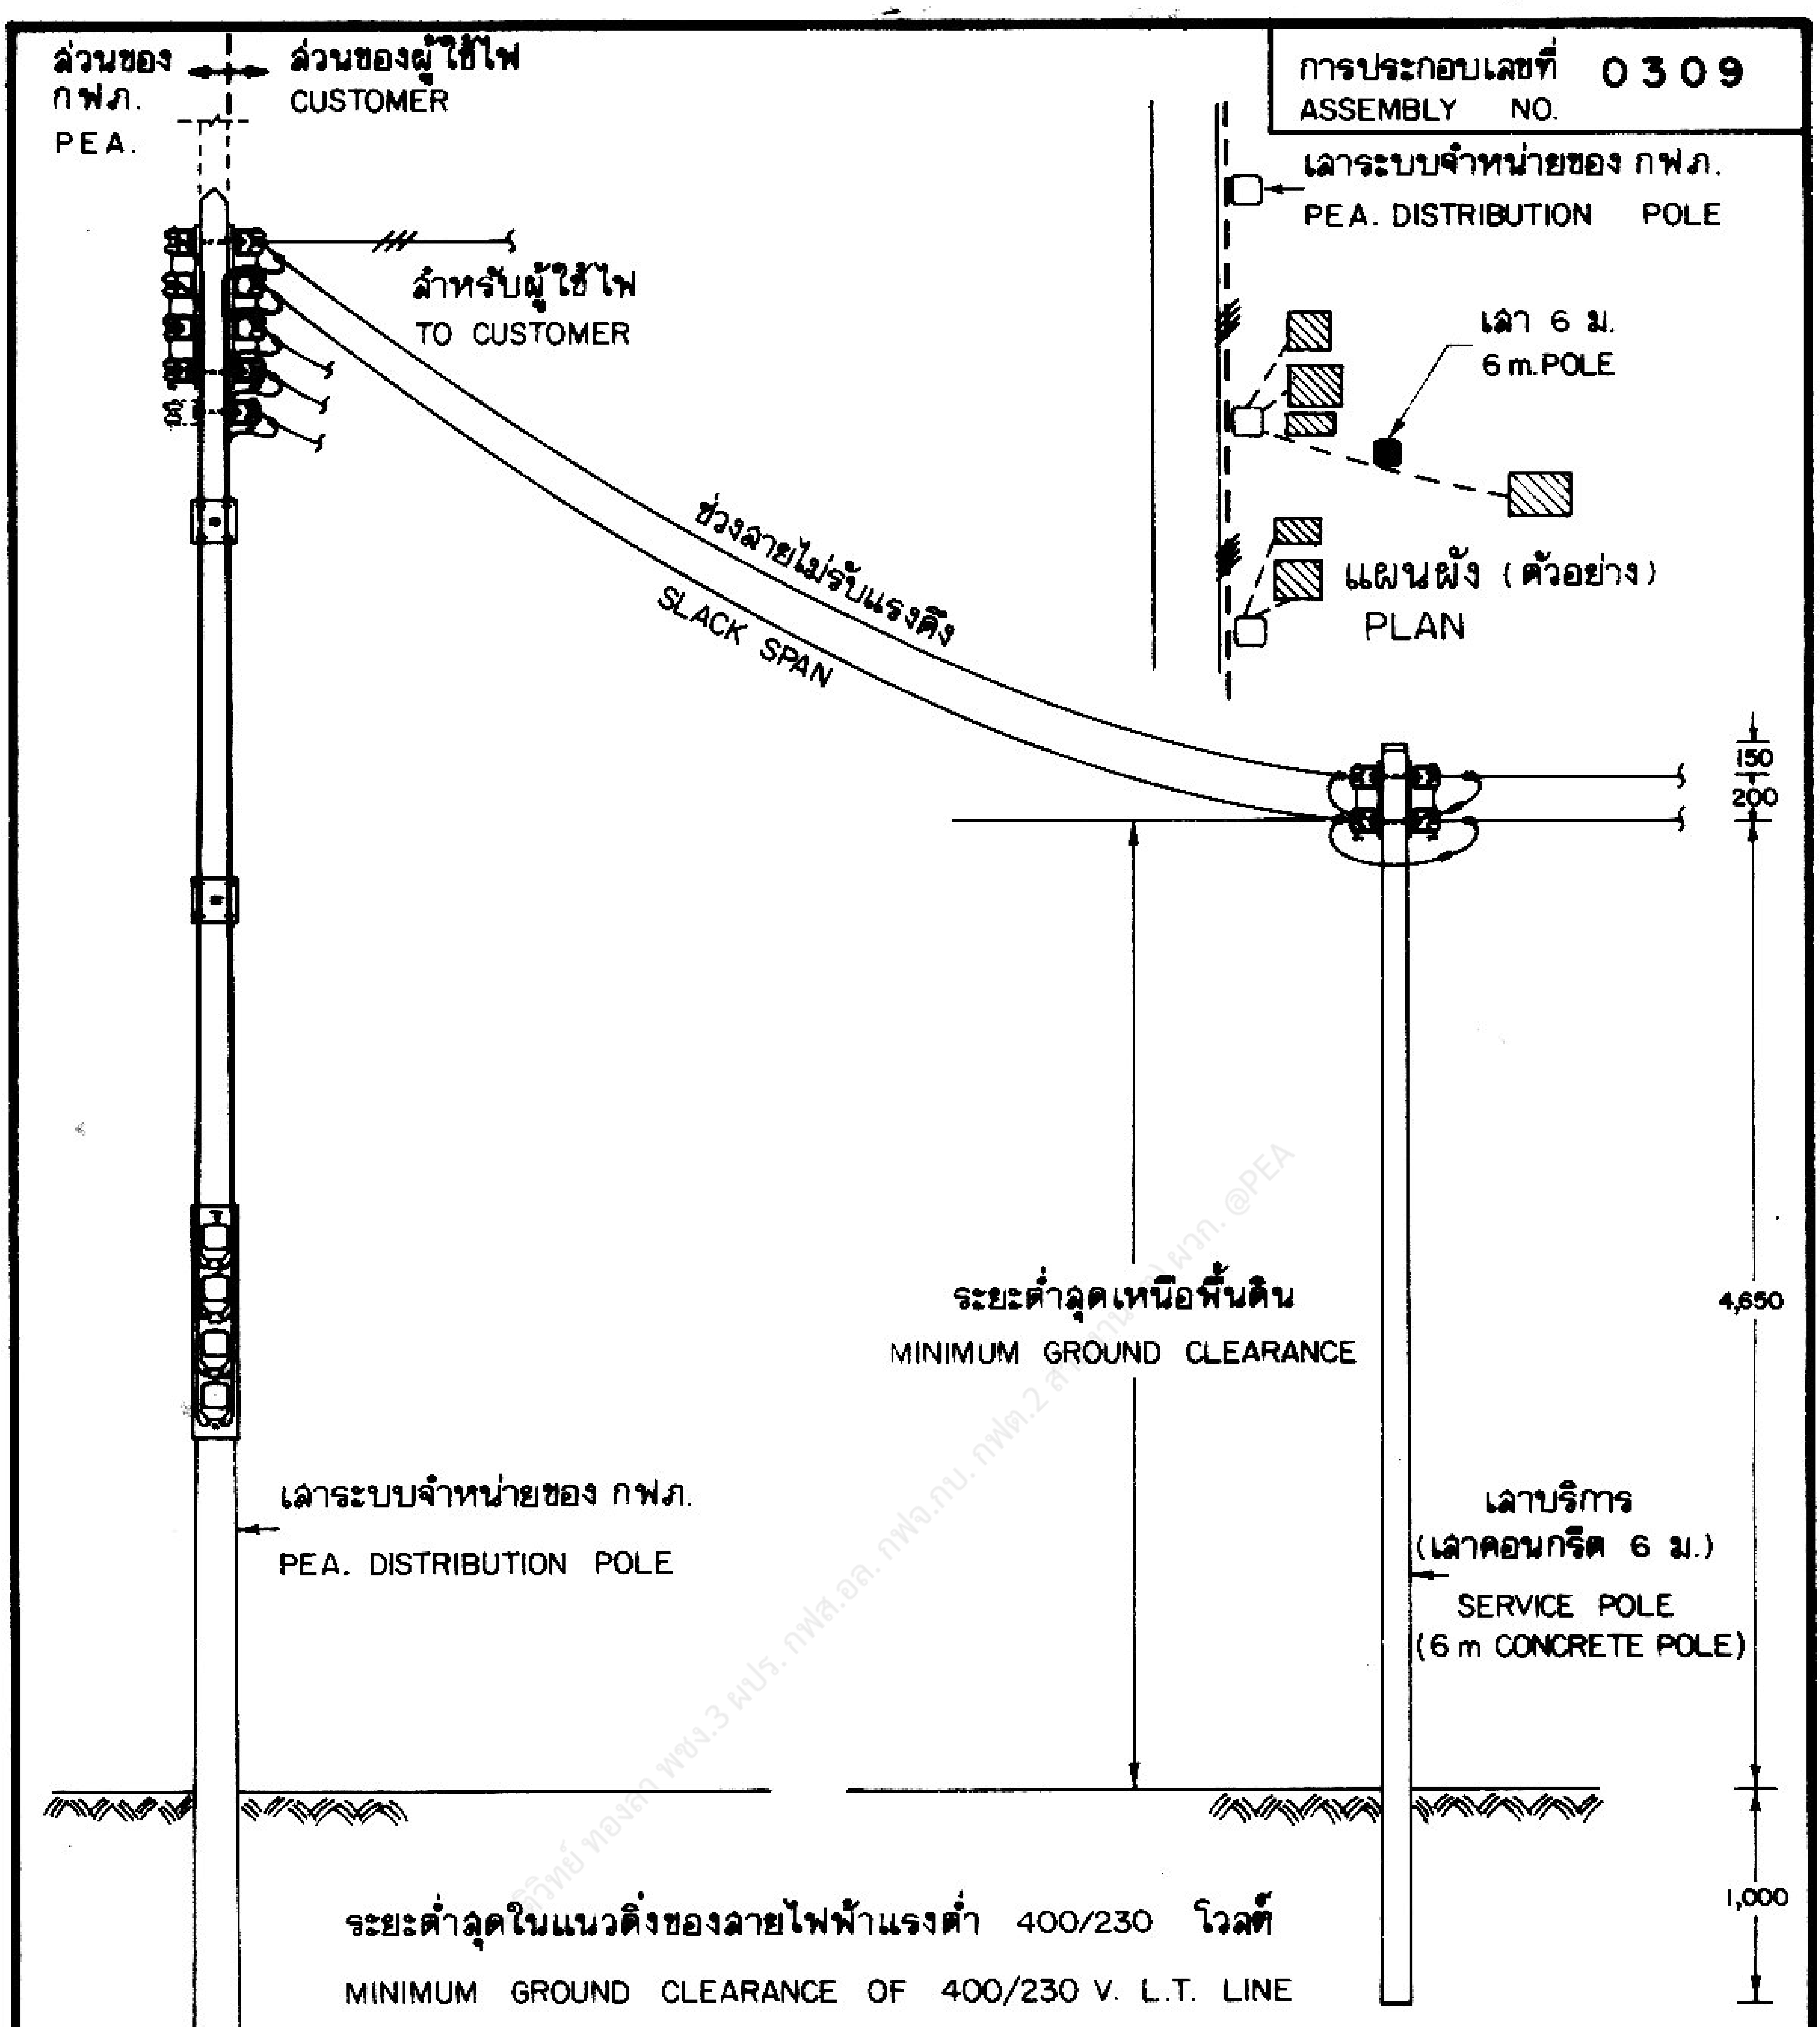

เมตร 4.60 METERS	1	เหนือทางส่วนบุคคล และไม่เป็นทางผ่านของรถบรรทุก OVER RESIDENTIAL DRIVEWAYS NOT SUBJECT TO TRUCK TR
เมตร 3.70 METERS	2	เหนือทางที่ใช้สำหรับคนเดินเท้าเท่านั้น OVER WAYS ACCESSIBLE TO PEDESTRIANS ONLY

…AFFIC

E

ใช้แทนแบบ.....
ถูกแทนโดยแบบ.....
เขียนเสร็จวันที่ 10 มิ.ย. 23
แก้แบบวันที่ 21 มี.ค. 27
มิติเป็น มม.
มาตราส่วน 1 : 50
แบบเลขที่ SAI–015/23070
แผ่นที่ 2 ของจำนวน 2 แผ่น

กองวิศวกรรมไฟฟ้าและเครื่องกล
ฝ่ายวิศวกรรม

ผู้เขียน
ผู้สำรวจ
วิศวกร กิตติพงษ์
หัวหน้าแผนก ธีรชัย
หัวหน้ากอง
ผู้อำนวยการฝ่าย

รองผู้ว่าการฝ่ายเทคนิค

17 มิ.ย. 2523

การไฟฟ้าส่วนภูมิภาค

ผู้ว่าการ ..... 24 มิ.ย. 23

ลักษณะการติดตั้งอุปกรณ์บนเสาบริการ ขนาด 6.00 ม.
2. สำหรับรับสายหลังมิเตอร์แรงต่ำ 1 เฟส

TYPICAL INSTALLATIONS ON 6.00 m SERVICE POL
2. FOR SUPPORTING 1 Ø SERVICE ENTRANCE