การประกอบเลขที่
ASSEMBLY NO. 5260

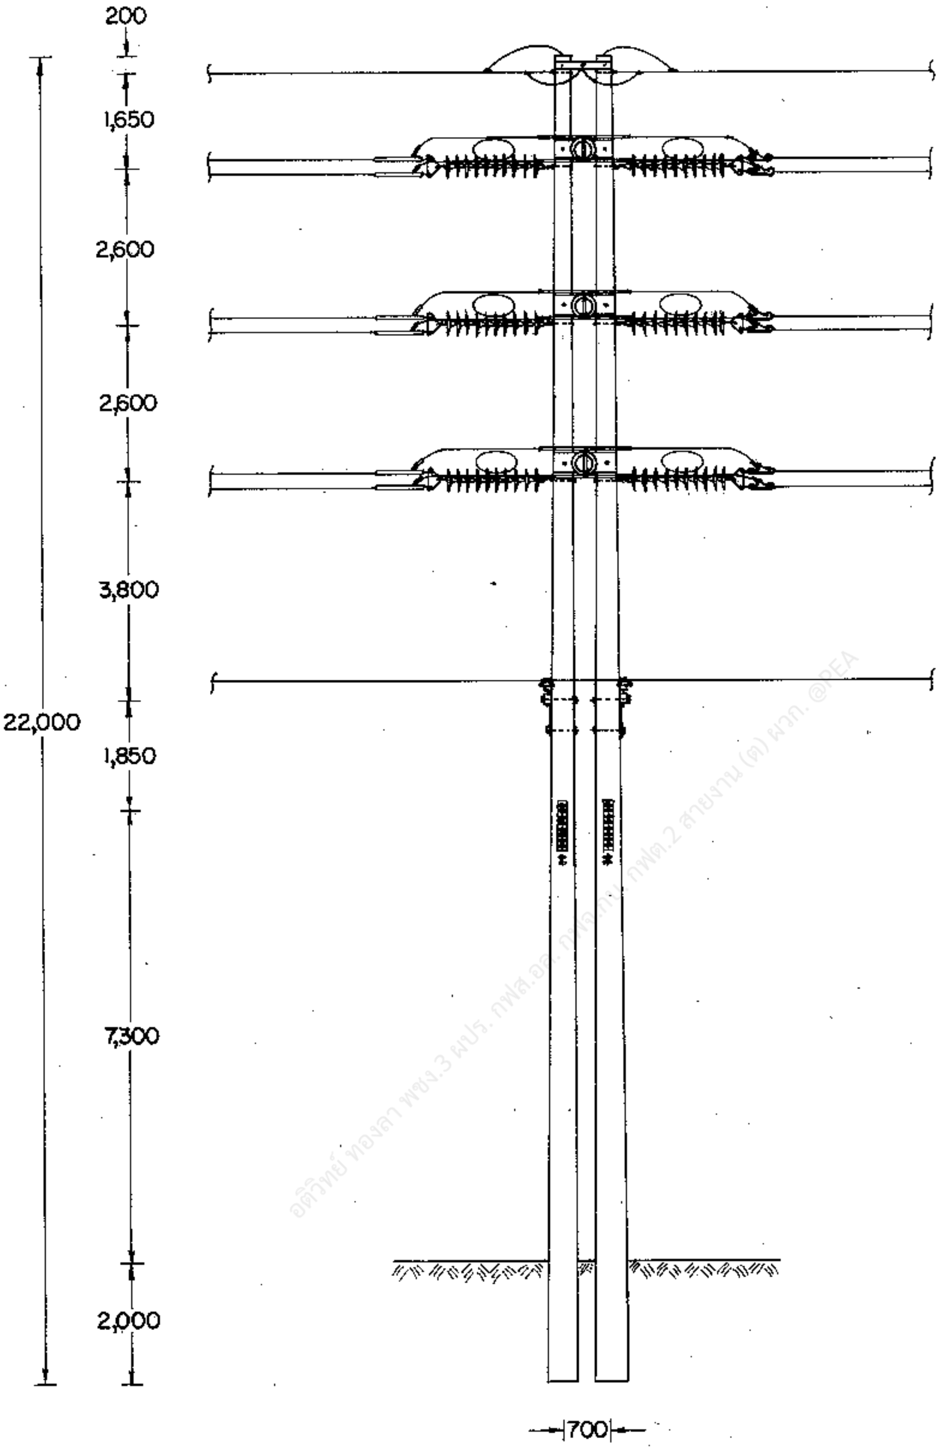

อดิวิทย์ ทองลา พชง.3 ผปร. กฟส.อล. กฟจ.กน. กฟต.2 สายงาน (ต) ผวก. @PEA

กองวิศวกรรมไฟฟ้าและเครื่องกล ฝ่ายวิศวกรรม	การไฟฟ้าส่วนภูมิภาค	ใช้แทนแบบ.......... ถูกแทนโดยแบบ..........
ผู้เขียน.......... ผู้สำรวจ.......... วิศวกร.......... หัวหน้าแผนก.......... หัวหน้ากอง.......... ผู้อำนวยการฝ่าย..........	ผู้ว่าการ..... 24 มี.ค. 23	เขียนเสร็จวันที่ 2 ม.ค. 23 แก้แบบวันที่ 29 ธ.ค. 32 มิติเป็น มม. มาตราส่วน 1 : 125
	115 kV วงจรเดี่ยว สายไฟฟ้าคู่ เสาคู่สำหรับแยกสาย แบบ SD-TL-2	
รองผู้ว่าการฝ่ายเทคนิค	115 kV SINGLE CIRCUIT DOUBLE CONDUCTOR DOUBLE POLE, TAP LINE STRUCTURE TYPE **SD-TL-2**	แบบเลขที่ SAI-015/23014 แผ่นที่ 1 ของจำนวน 3 แผ่น

19 ส.ค. 2523

การประกอบเลขที่ ASSEMBLY NO.	5260

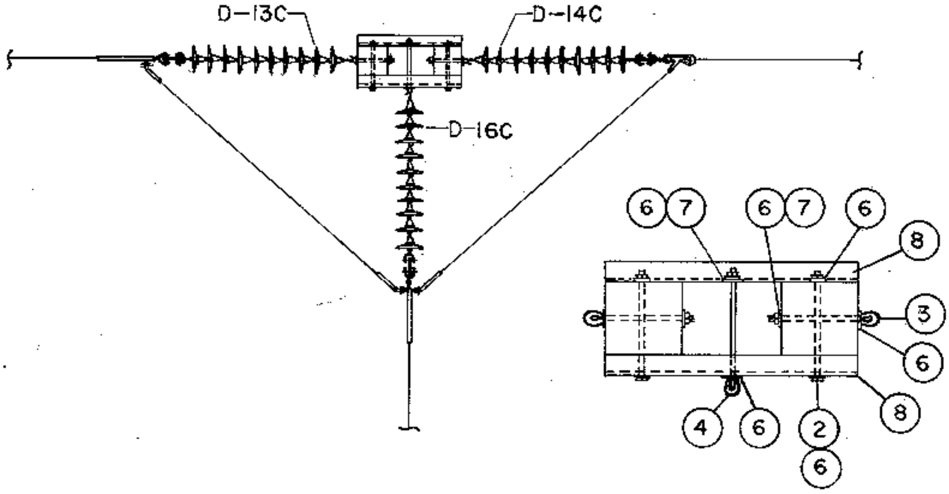
D-13C
D-14C
D-16C
6
7
6
7
6
8
3
6
8
4
6
2
6

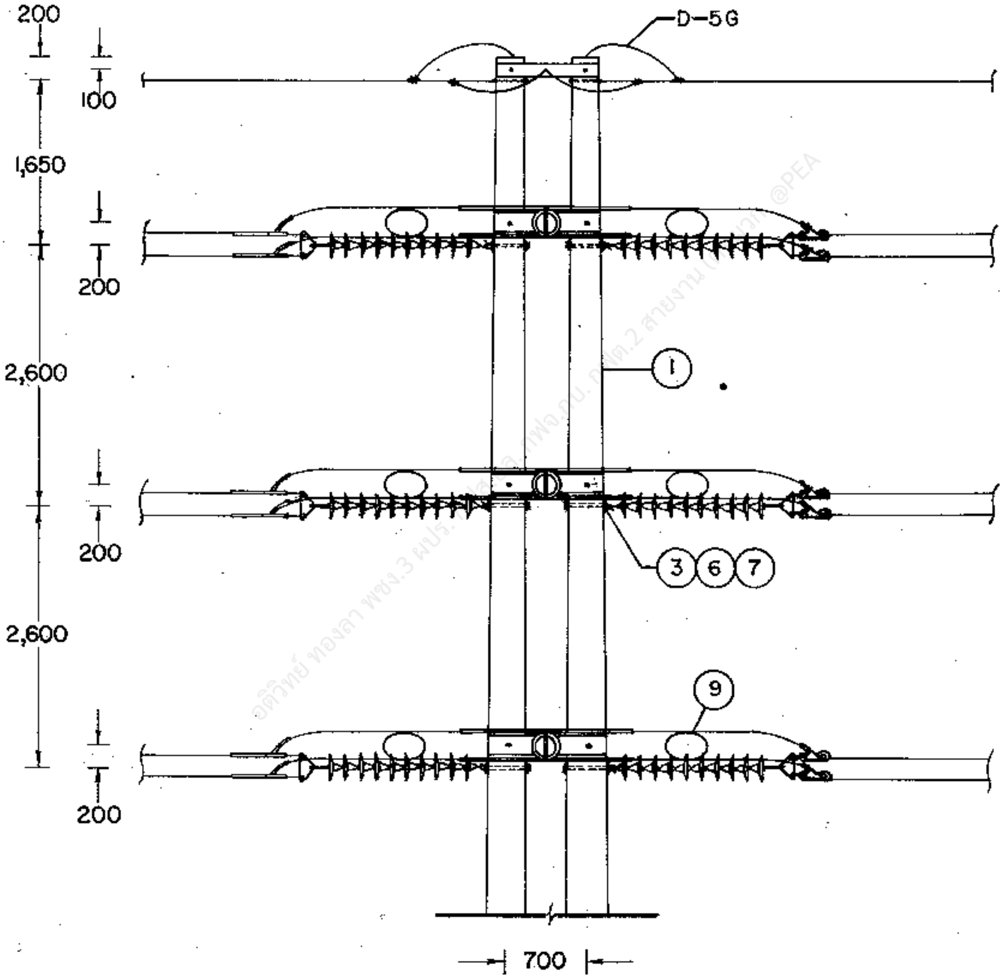
D-5G
200
100
1,650
200
2,600
200
2,600
200
1
3
6
7
9
700

อติวิทย์ ทองลา พชง.3 ผปร. [illegible] กฟจ.กบ. กฟต.2 สายงาน [illegible] @PEA

กองวิศวกรรมไฟฟ้าและเครื่องกล ฝ่ายวิศวกรรม	การไฟฟ้าส่วนภูมิภาค	ใช้แทนแบบ
ผู้เขียน ผู้ตรวจ วิศวกร หัวหน้าแผนก หัวหน้ากอง ผู้อำนวยการฝ่าย	ผู้ว่าการ 24 มี.ค. 23	ถูกแทนโดยแบบ เขียนเสร็จวันที่ 2 ม.ค. 23 แก้แบบวันที่ 29 ธ.ค. 32 มิติเป็น มม. มาตราส่วน 1 : 25 , 1 : 75
	115 kV วงจรเดี่ยว สายไฟฟ้าคู่ เสาคู่สำหรับแยกสาย แบบ SD-TL-2	
รองผู้ว่าการฝ่ายเทคนิค	115 kV SINGLE CIRCUIT DOUBLE CONDUCTOR DOUBLE POLE, TAP LINE STRUCTURE TYPE SD-TL-2	แบบเลขที่ SAI-015/23014 แผ่นที่ 2 ของจำนวน 3 แผ่น

[illegible] 2523

การประกอบเลขที่
ASSEMBLY NO. **5260**

บัญชีวัสดุ
BILL OF MATERIAL

ลำดับที่ ITEM	รายละเอียด DESCRIPTION	จำนวน REQ'D	วัสดุเลขที่ MAT. NO.
1	เสาคอนกรีต 22 ม. PLOE, CONCRETE 22 m LONG	2	00010011 (0041)
2	สลักเกลียว M 20 X 450 มม. BOLT, MACHINE, M 20 X 450 mm	6	01110302 (0234)
3	สลักห่วงโอแวล M 20 X 350 มม. BOLT, OVAL EYE M 20 X 350 mm	6	01150100 (0260)
4	สลักห่วงโอแวล M 20 X 450 มม. BOLT, OVAL EYE M 20 X 450 mm	3	01150101 (0261)
5	แหวนสี่เหลี่ยมแบน 52X52X4.5 มม. รู Ø 18 มม. มอก. 258 WASHER, SQUARE, FLAT 52X52X4.5 mm, HOLE Ø 18 mm, TIS. 258	—	01180100 (0355)
6	แหวนสี่เหลี่ยมแบน 62 X 62 X 6 มม. รู Ø 22 มม. มอก. 258 WASHER, SQUARE, FLAT 62 X 62 X 6 mm, HOLE Ø 22 mm, TIS. 258	30	01180101 (0356)
7	แหวนสปริง M 20 มอก. 259 WASHER, LOCK, M 20, TIS 259	9	01180302 (0366)
8	เหล็กรูปรางน้ำ 200 X 80 X 7.5 มม. ยาว 1,000 มม. STEEL CHANNEL 200 X 80 X 7.5 mm, 1,000 mm LONG	6	01000400 (2675)
9	ปรีฟอร์มแยกสาย SPACER, HELICAL ROD, PREFORMED	6	02240000 (0918)

รายละเอียด
DETAIL

D-13C	การประกอบลูกถ้วยแขวน SUSPENSION INSULATOR ASSEMBLY	3	
D-14C	การประกอบลูกถ้วยแขวน SUSPENSION INSULATOR ASSEMBLY	3	
D-16C	การประกอบลูกถ้วยแขวน SUSPENSION INSULATOR ASSEMBLY	3	
D-18C	การประกอบลูกถ้วยแขวน SUSPENSION INSULATOR ASSEMBLY	—	
D-5G	การต่อสายล่อฟ้า OVERHEAD GROUND WIRE CONNECTION	1	
D-10B	ฐานรากเสา POLE FOUNDATION	1	

หมายเหตุ รายละเอียดการประกอบลูกถ้วย D-16C ใช้สำหรับวงจรแยกสายที่เป็นสายไฟฟ้าคู่

NOTE SUSPENSION INSULATOR ASSEMBLY DETAIL NO. D-16C, FOR DOUBLE CONDUCTOR TAP LINE.

กองวิศวกรรมไฟฟ้าและเครื่องกล ฝ่ายวิศวกรรม	การไฟฟ้าส่วนภูมิภาค	ใช้แทนแบบ........
ผู้เขียน.... ผู้สำรวจ........ วิศวกร.... หัวหน้าแผนก.... หัวหน้ากอง.... ผู้อำนวยการฝ่าย....	ผู้ว่าการ.... 24 ธ.ค. 23	ถูกแทนโดยแบบ........ เขียนเสร็จวันที่ 2 พ.ค. 23 แก้แบบวันที่ 29 ธ.ค. 32 มิติเป็น........ มาตราส่วน........
	115 kV วงจรเดี่ยว สายไฟฟ้าคู่ เสาคู่สำหรับแยกสาย แบบ SD-TL-2	
รองผู้ว่าการฝ่ายเทคนิค	115 kV SINGLE CIRCUIT DOUBLE CONDUCTOR DOUBLE POLE, TAP LINE STRUCTURE TYPE SD-TL-2	แบบเลขที่ SAI-015/23014 แผ่นที่ 3 ของจำนวน 3 แผ่น

ธ.ค. 2523