การประกอบเลขที่ 0310
ASSEMBLY NO.

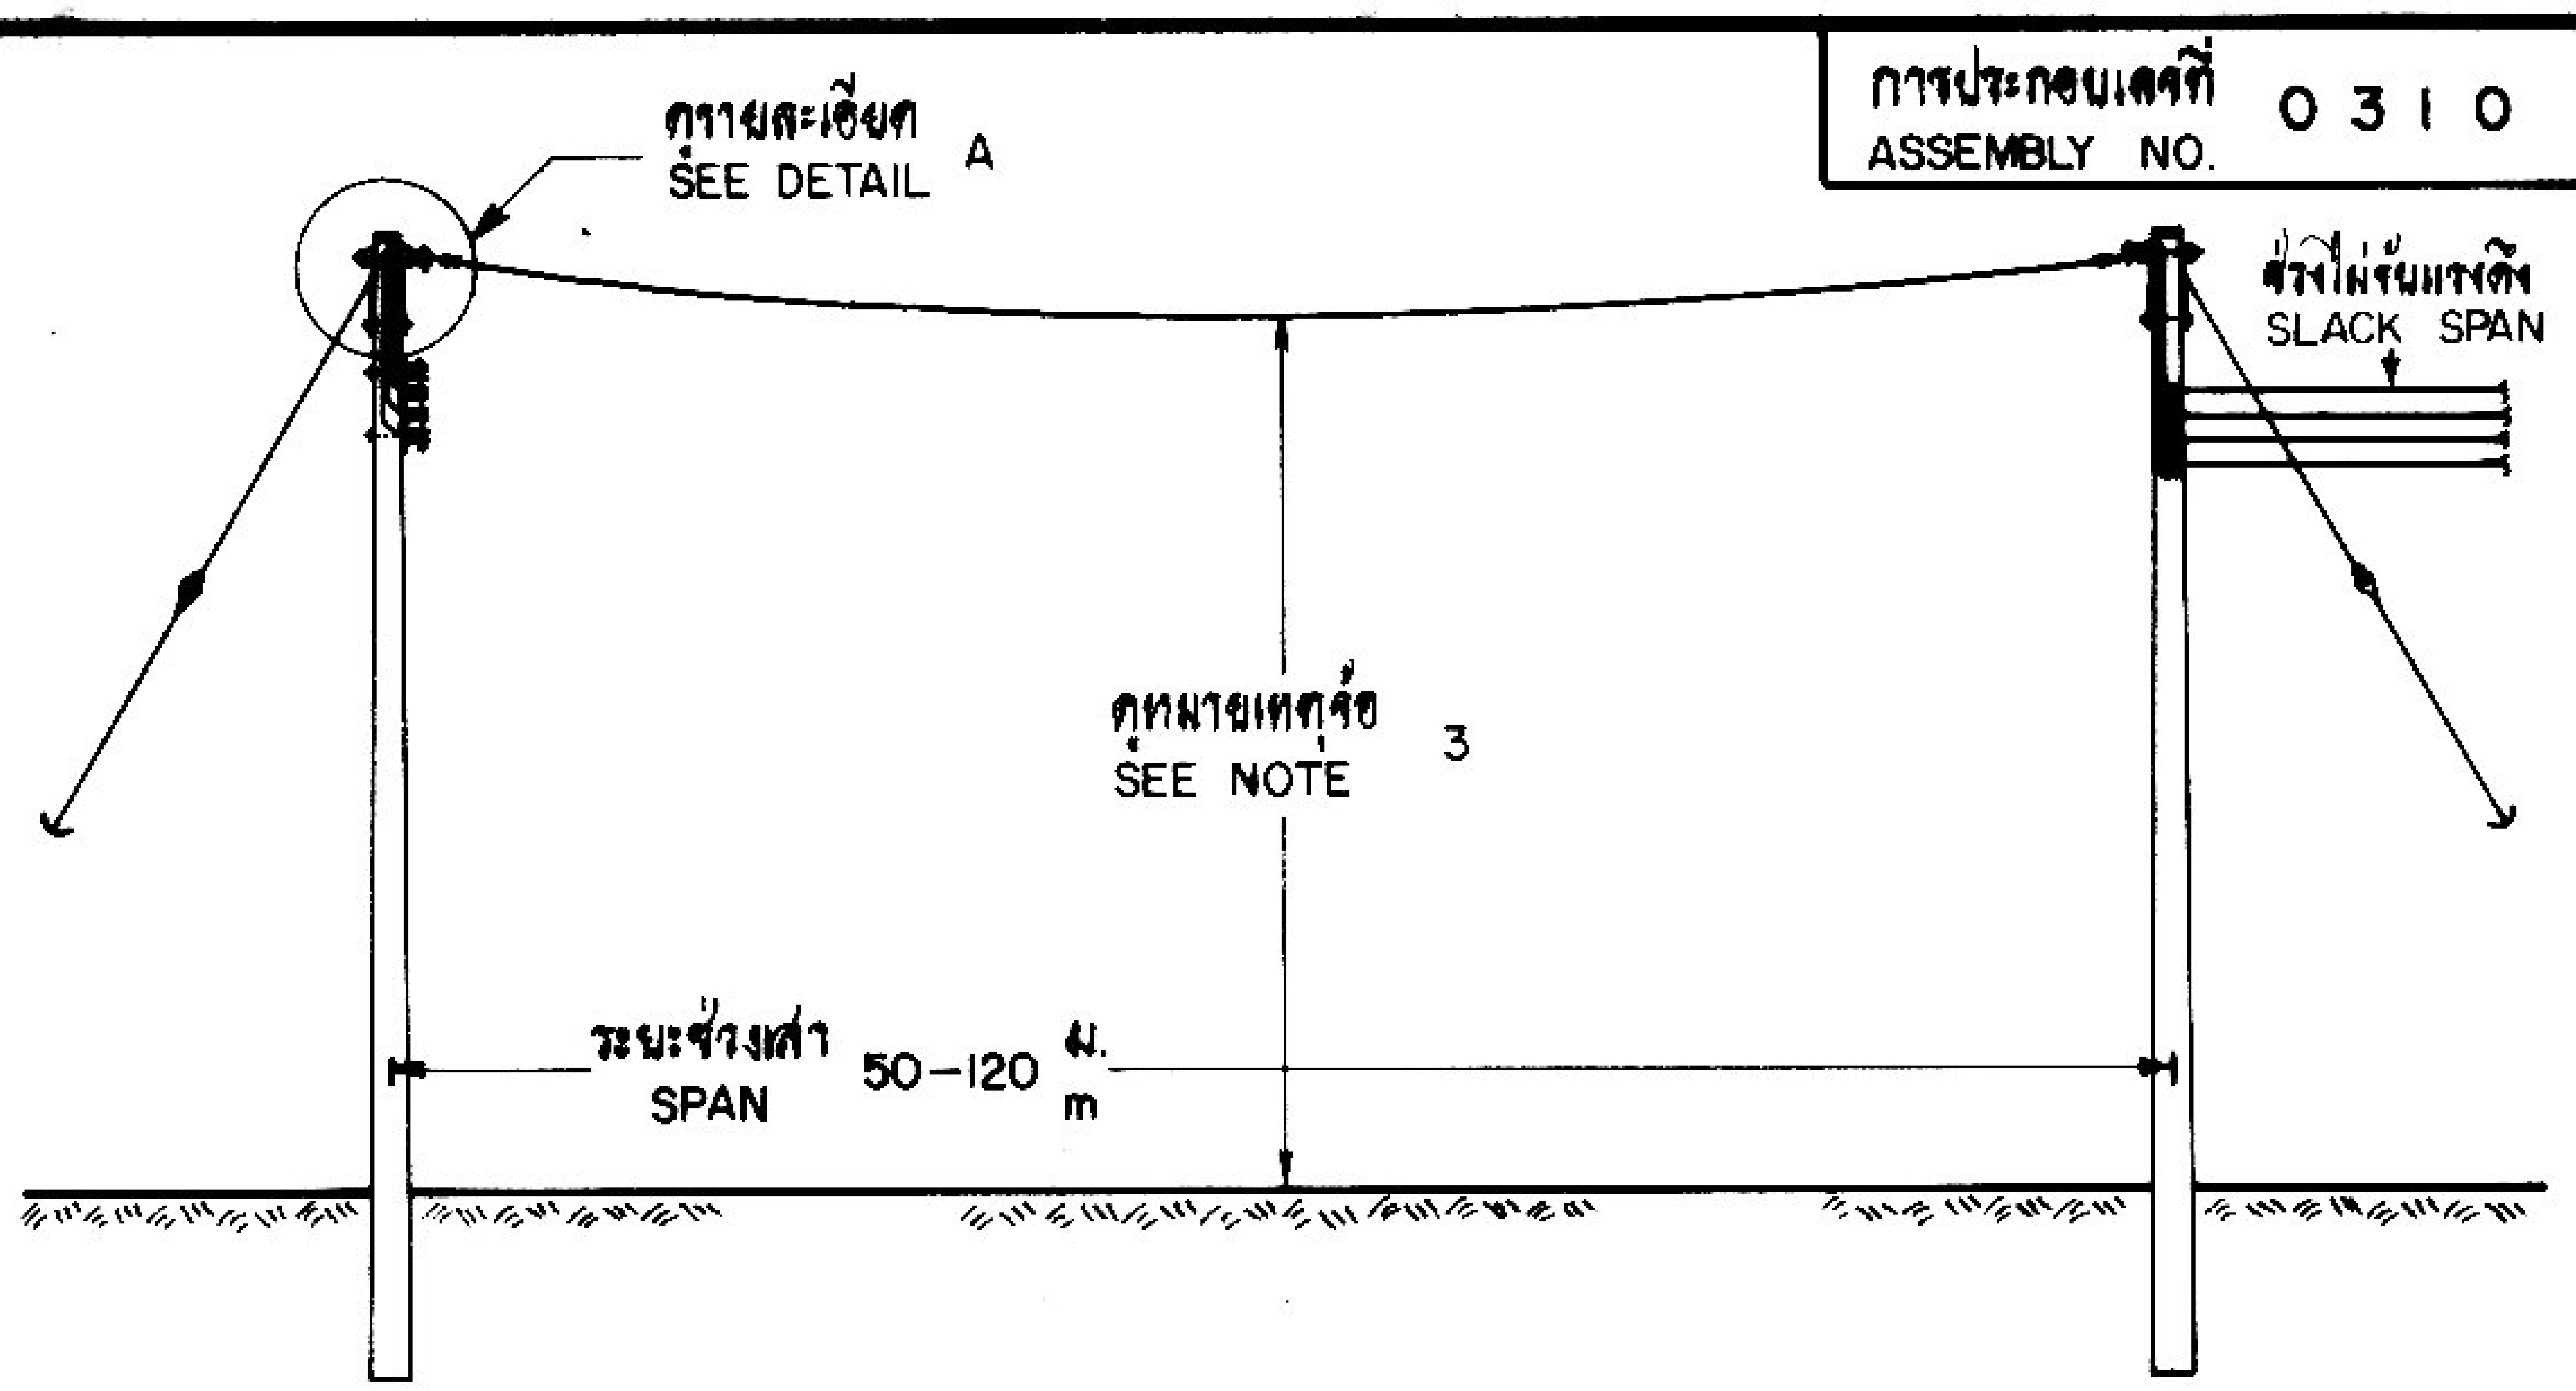

I กรณีติดตั้งบนเสา 9 ม.
ON 9 m CONCRETE POLE

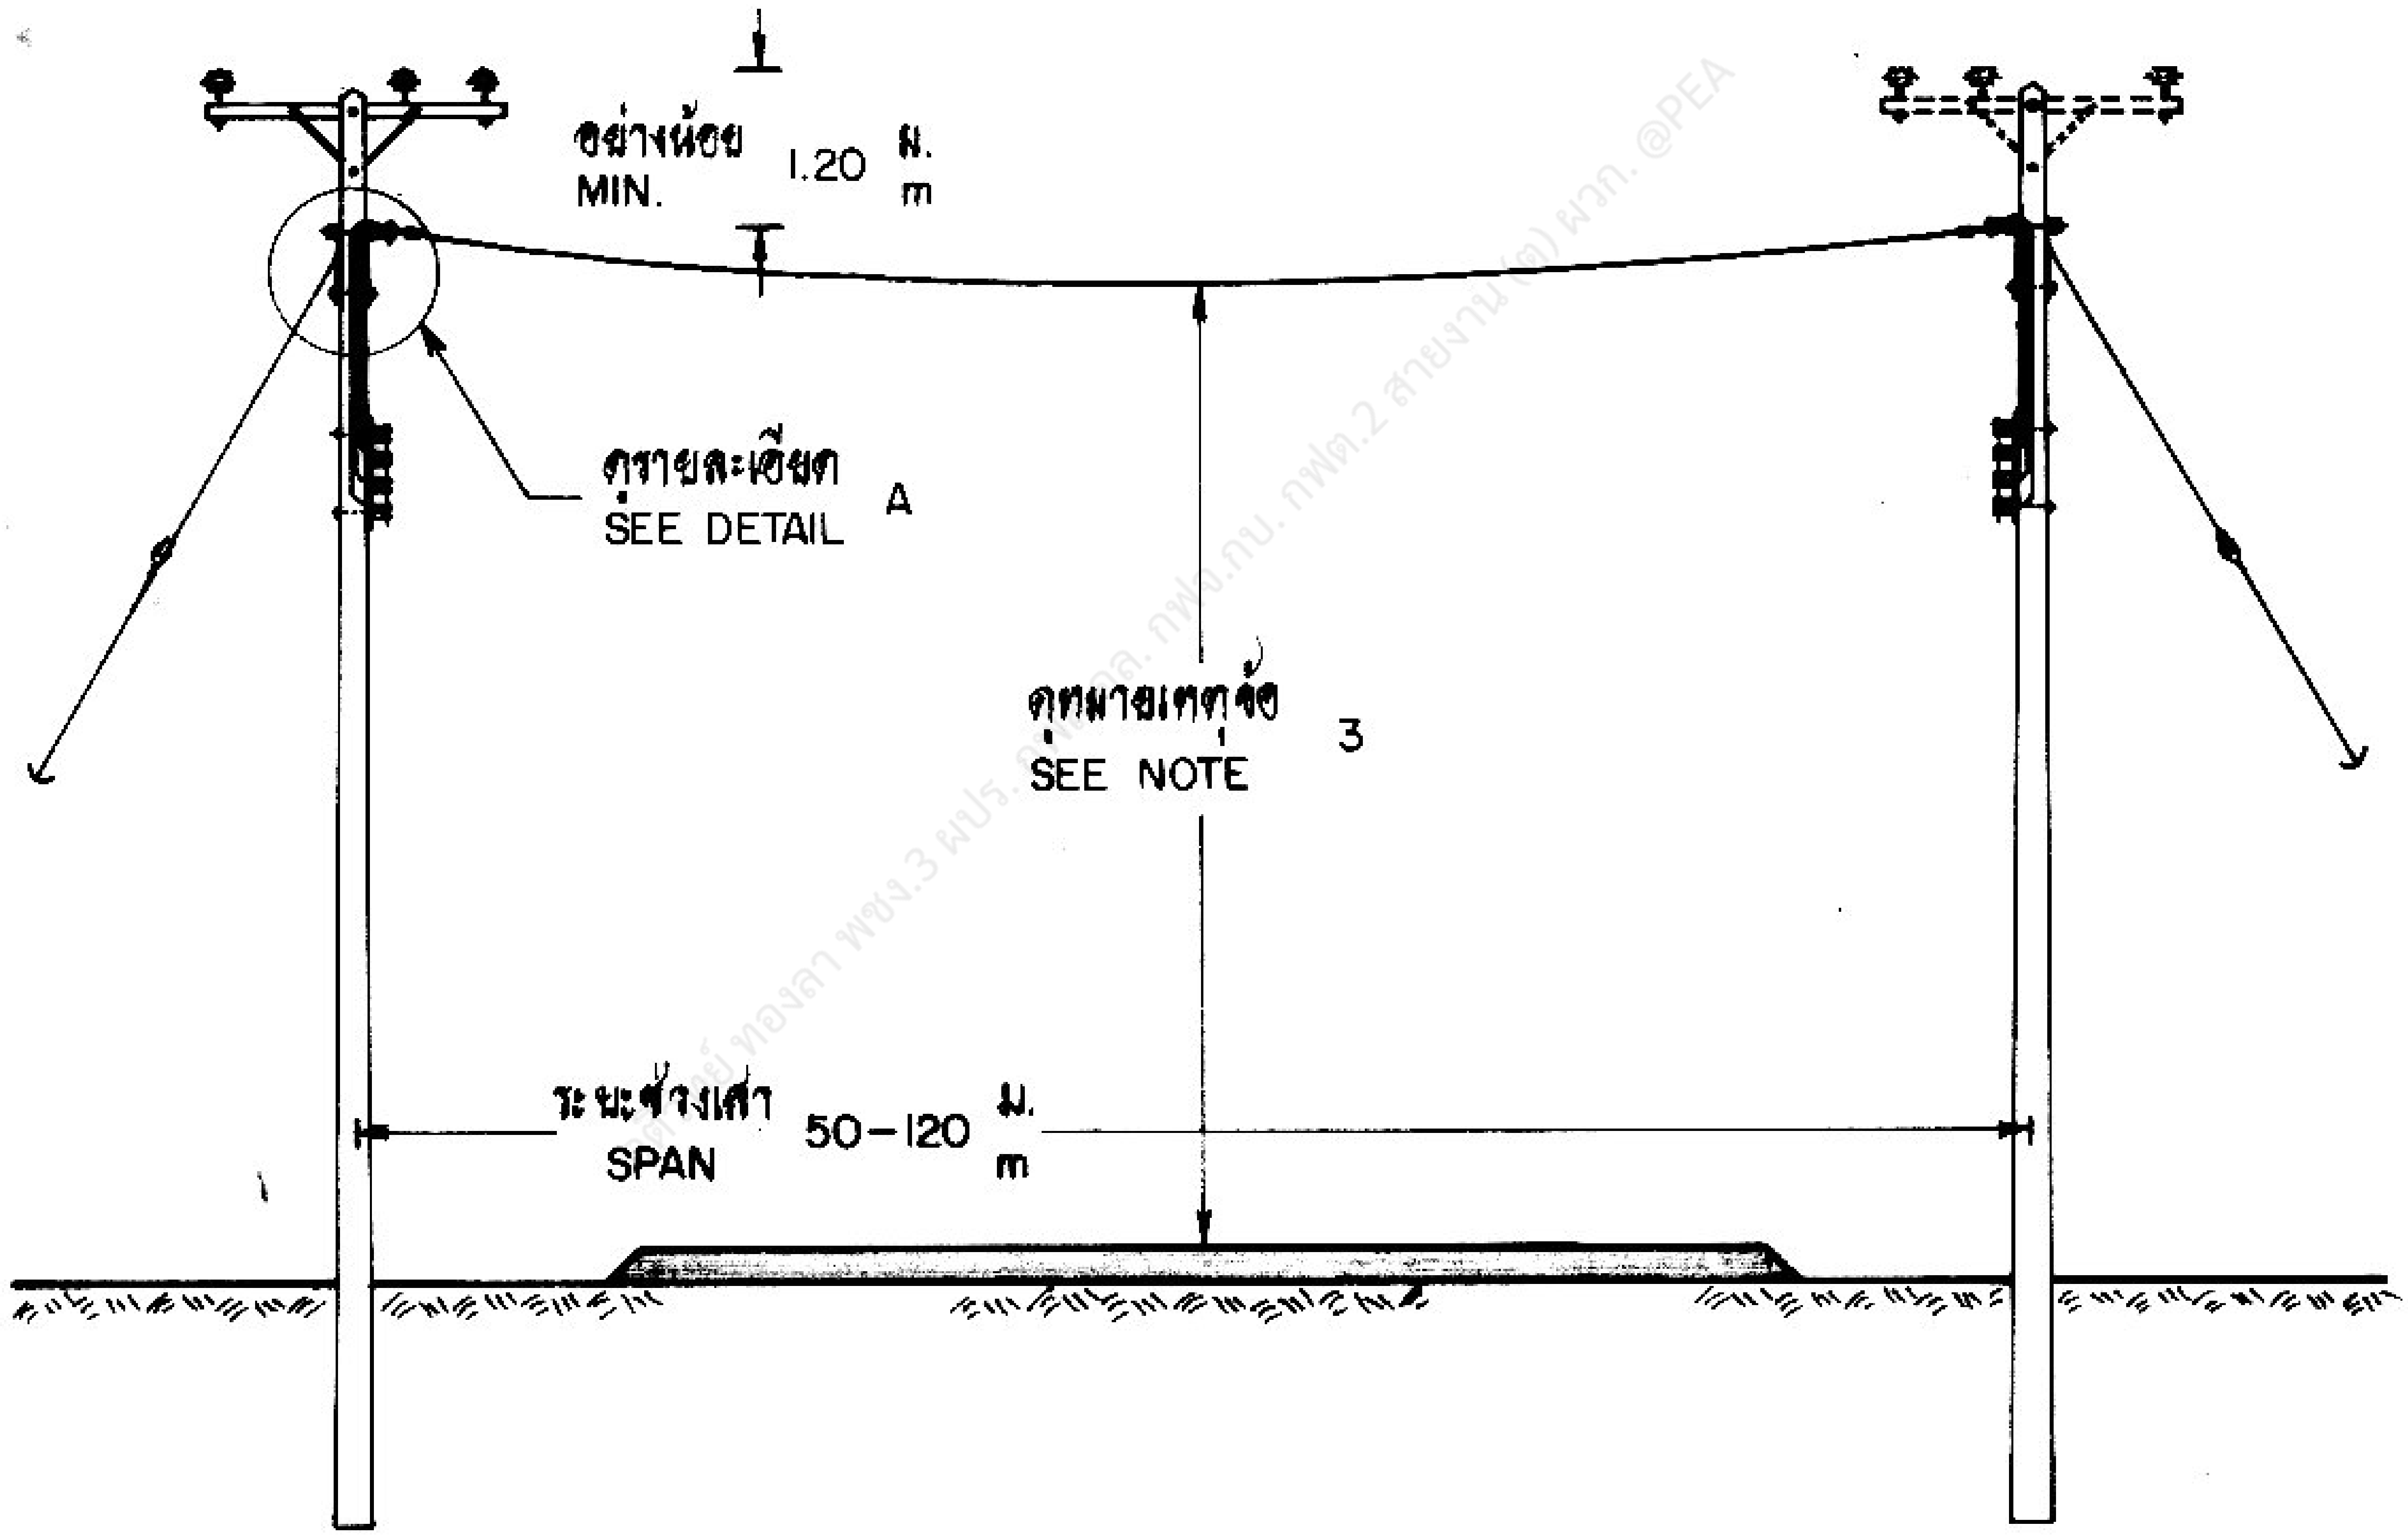

II กรณีติดตั้งบนเสา 12 ม.
ON 12 m CONCRETE POLE

กองวิศวกรรมไฟฟ้าและเครื่องกล
ฝ่ายวิศวกรรม

ผู้เขียน
ผู้สำรวจ
วิศวกร
หัวหน้าแผนก
ผู้อำนวยการกอง
ผู้อำนวยการฝ่าย

รองผู้ว่าการฝ่ายเทคนิค

การไฟฟ้าส่วนภูมิภาค

ผู้ว่าการ ๓๐ มิ.ย. ๒๖

มาตรฐานการก่อสร้างระบบจำหน่ายแรงต่ำ
ช่วง 50-120 ม.

L.T. STANDARD CONSTRUCTION
SPAN 50-120 m

ใช้แทนแบบ
ถูกแทนโดยแบบ
เขียนเสร็จวันที่ 7 มิ.ย. 26
แก้แบบวันที่
มิติเป็น
มาตราส่วน

แบบเลขที่ SAI-015/26015
แผ่นที่ 1 จากจำนวน 4 แผ่น

การประกอบเลขที่
ASSEMBLY NO. 0310

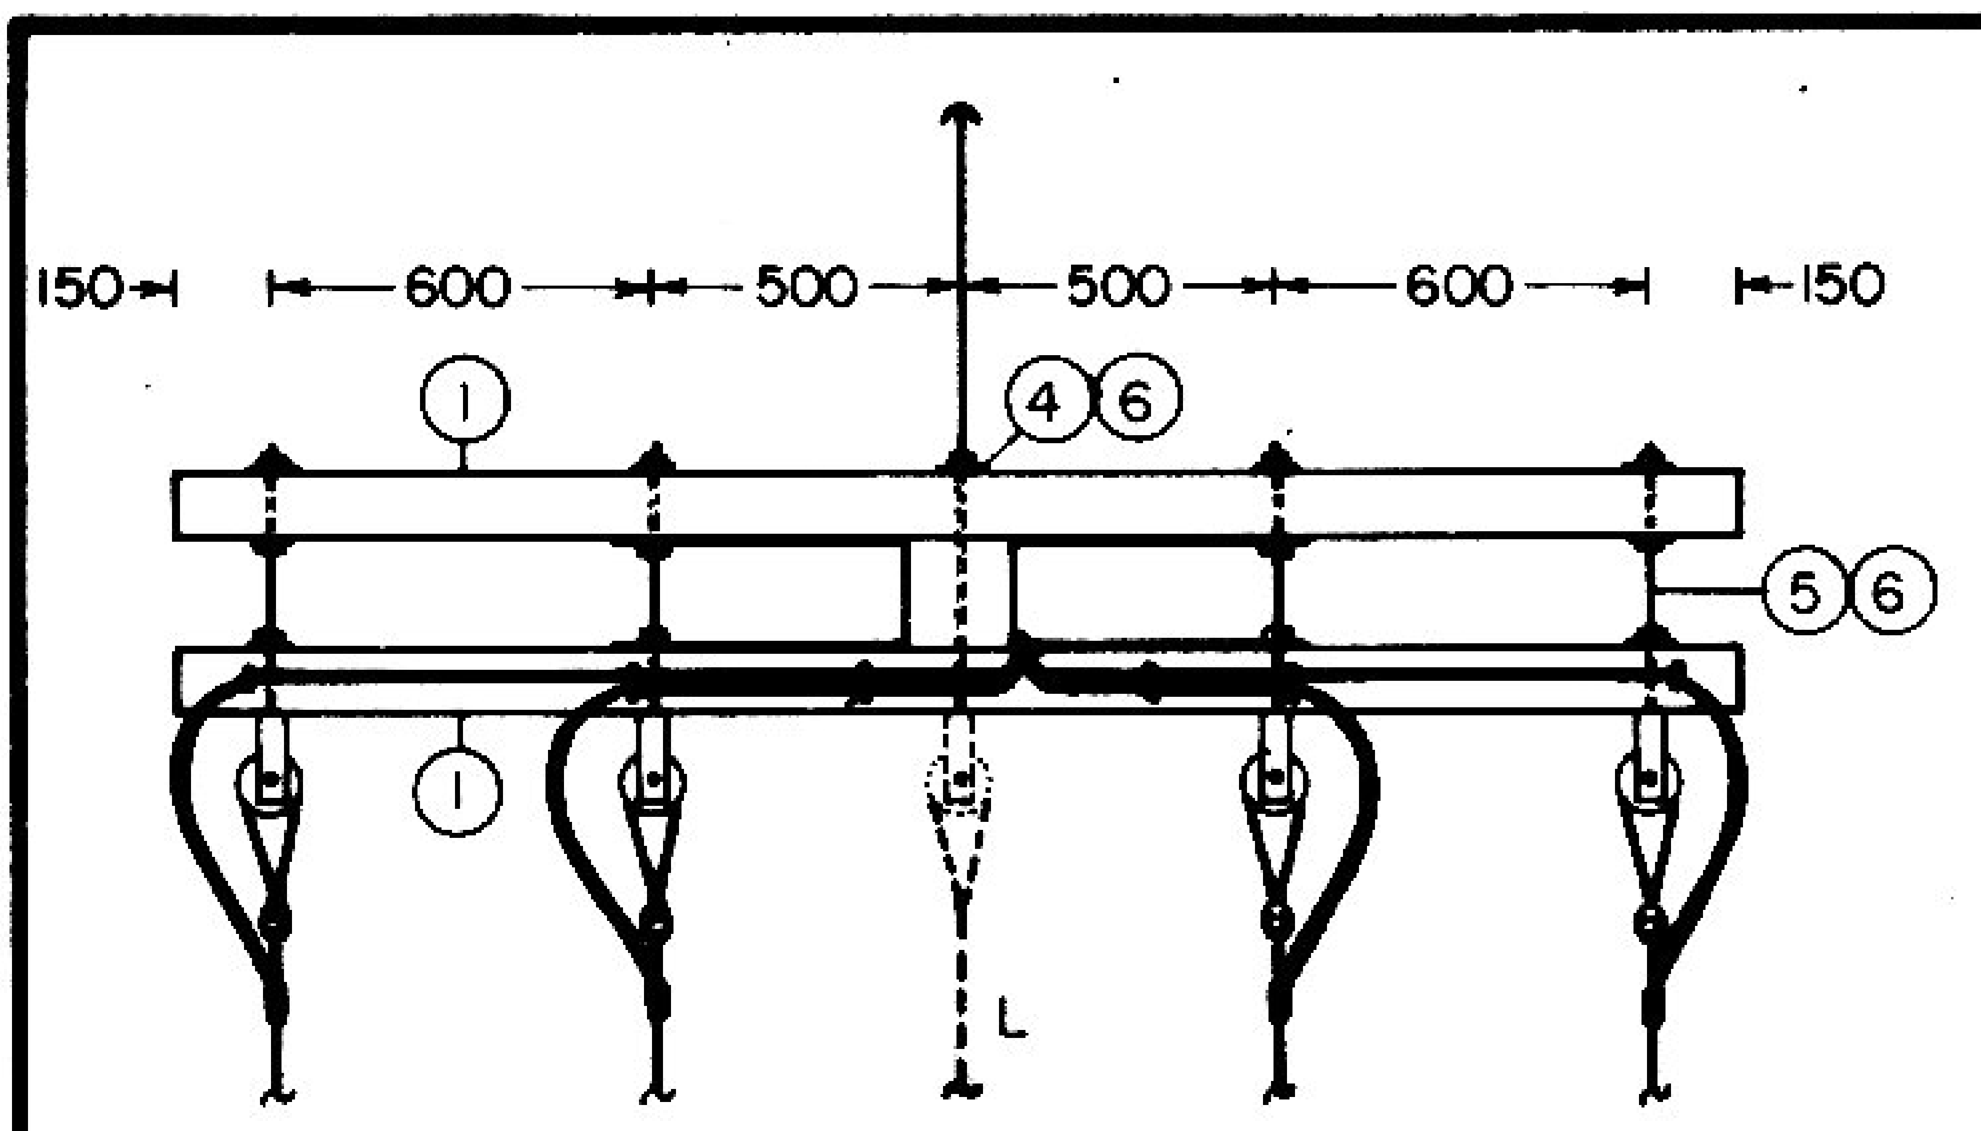

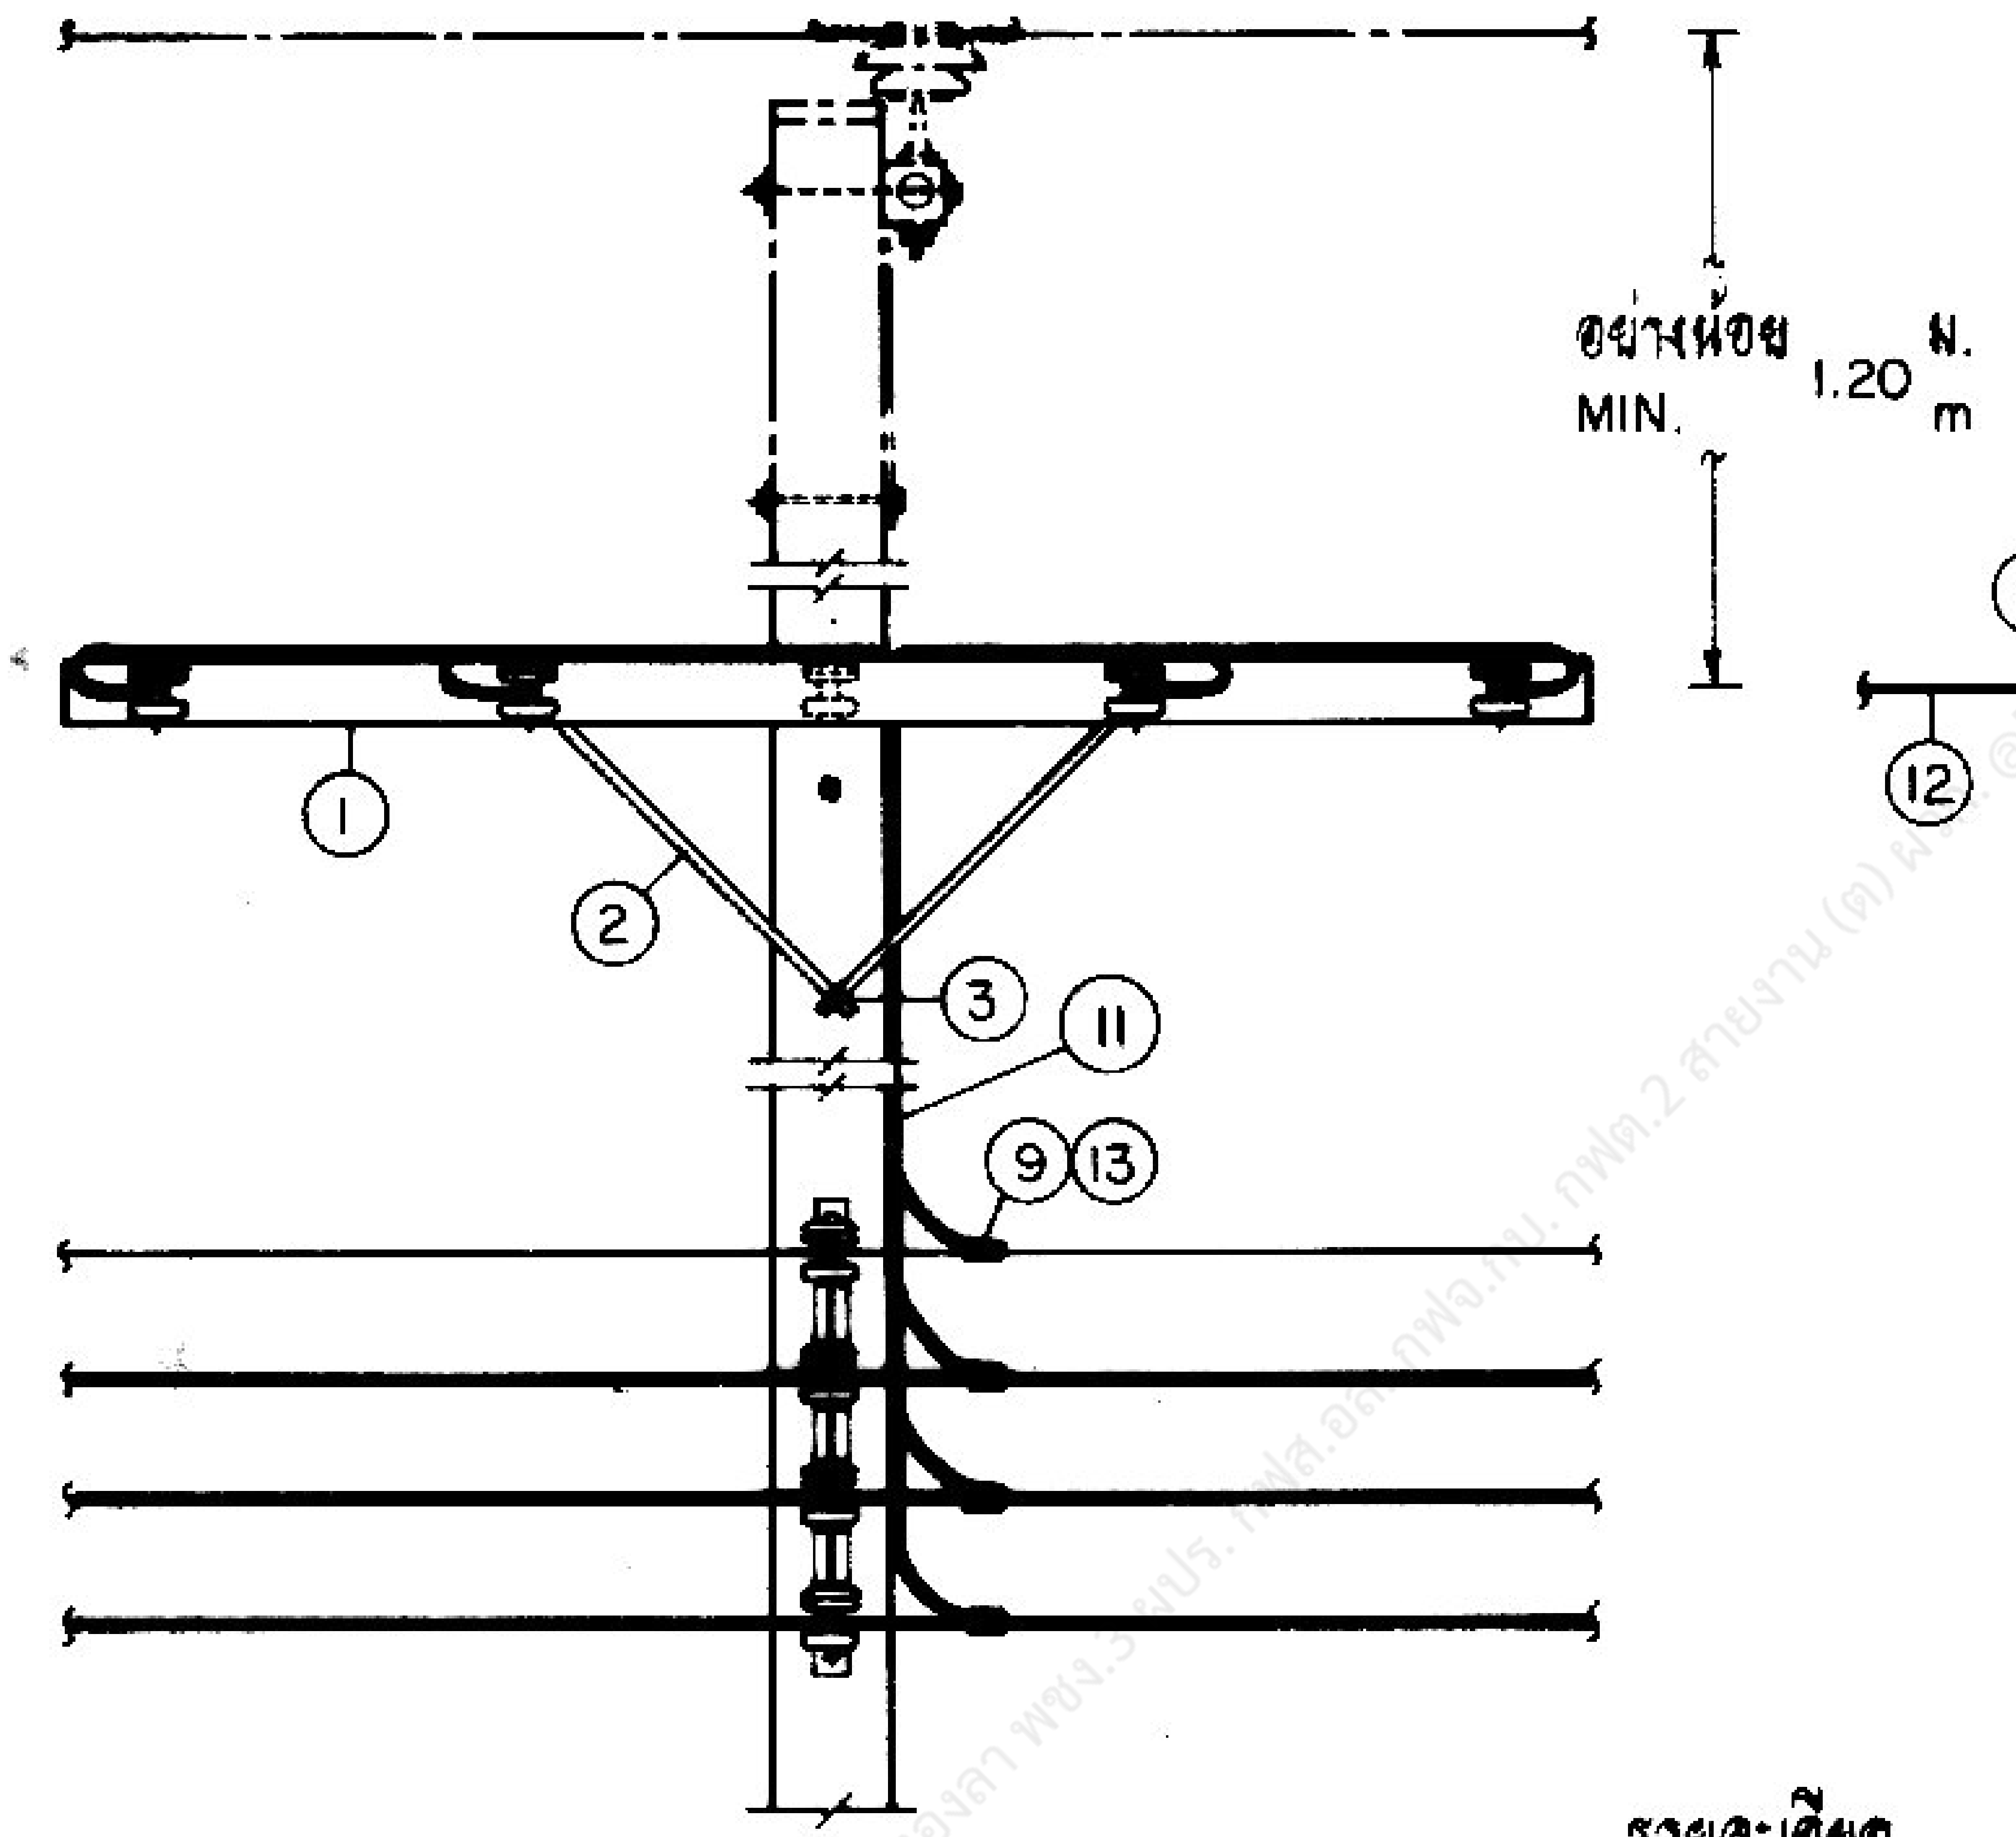

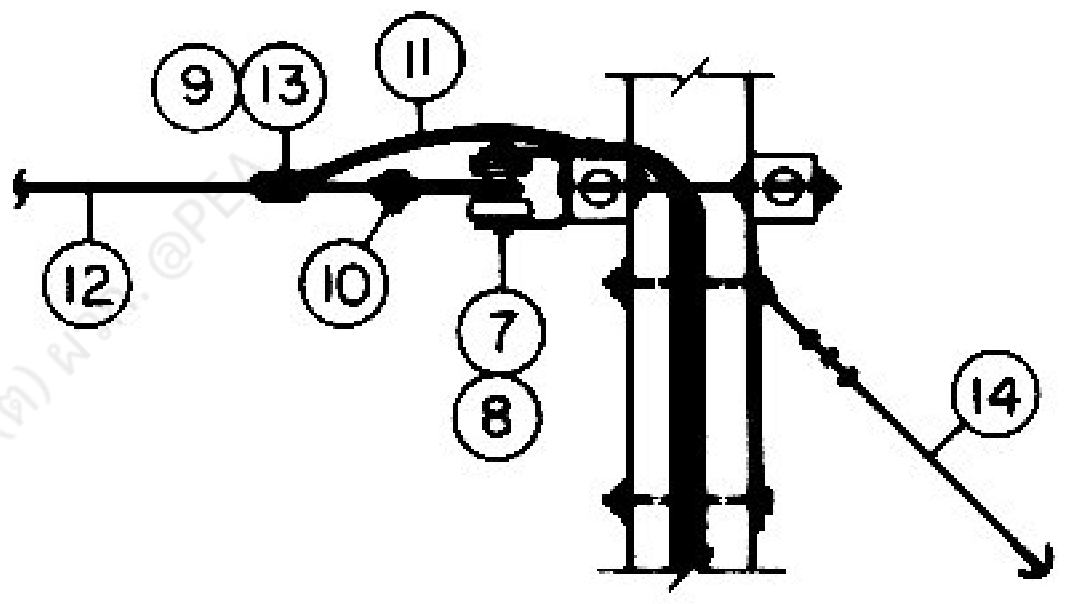

รายละเอียด A
DETAIL A

ข้อกำหนดการใช้งาน

1 สำหรับเข้าปลายสายแรงต่ำ ชนิดสายเปลือย ไม่เกิน 5 เส้น

2 สายเปลือยที่ใช้พาด เป็นสายอะลูมิเนียมแกนเหล็ก (ขนาด 35/6, 50/8 ต.มม.) หรือสายอะลูมิเนียมอัลลอย (ขนาด 35, 50 ต.มม.)

RECOMMENDATION

1 FOR DEADENDING OF L.T. BARE CONDUCTORS WHICH ARE NOT MORE THAN 5 WIRES.

2. BARE CONDUCTORS ARE ACSR (35/6, 50/8 mm^2) OR Al-ALLOY (35, 50 mm^2)

กองวิศวกรรมไฟฟ้าและเครื่องกล
ฝ่ายวิศวกรรม

ผู้เขียน
ผู้สำรวจ
วิศวกร
หัวหน้าแผนก
ผู้อำนวยการกอง
ผู้อำนวยการฝ่าย
รองผู้ว่าการฝ่ายเทคนิค

การไฟฟ้าส่วนภูมิภาค

ผู้ว่าการ 30 มิ.ย. 26

มาตรฐานการก่อสร้างระบบจำหน่ายแรงต่ำ
ช่วง 50-120 ม.

L.T. STANDARD CONSTRUCTION
SPAN 50-120 m

ใช้แทนแบบ
ถูกแทนโดยแบบ
เขียนเสร็จวันที่ 7 มิ.ย. 26
แก้แบบวันที่
มิติเป็น มม.
มาตราส่วน 1 : 30

แบบเลขที่ SAI-015/26015
แผ่นที่ 2 จากจำนวน 4 แผ่น

การประกอบเลขที่ ASSEMBLY NO.	0310

3. ระยะหย่อนยานในการขึงสายไฟ มีค่าตามตาราง

(แรงดึงสูงสุดในการขึงสายไฟฟ้า 250 กก.)

3. STRINGING SAG OF CONDUCTORS ARE ACCORDING TO TABLE BELOW.

(MAXIMUM STRINGING TENSION 250 kg)

ระยะหย่อนยานขณะขึงสายไฟ STRINGING SAG (ม.) (m)									
ระยะช่วงเสาไฟ (ม.) SPAN (m) สายเปลือย (ต.มม.) BARE CONDUCTOR (mm^2)	40	50	60	70	80	90	100	110	120
อะลูมิเนียมแกนเหล็ก ACSR 35/6 , 50/8	0.20	0.30	0.40	0.50	0.65	0.80	1.00	—	—
อะลูมิเนียมอัลลอย Al - ALLOY 35 , 50	0.15	0.18	0.25	0.35	0.50	0.60	0.70	0.85	1.00

บัญชีวัสดุ
BILL OF MATERIAL

ลำดับที่ ITEM	รายละเอียด DESCRIPTION	จำนวน REQ'D I	 II	วัสดุเลขที่ MAT. NO.
1	คอน คอนกรีตอัดแรงแบบปั่น 100 X 100 X 2,500 มม. CROSSARM, SPUN, PRESTRESSED CONCRETE 100 X 100 X 2,500 mm	2	2	00110001
2	เหล็กประกับไม้คอน 30 X 6 X 760 มม. BRACE, FLAT FOR CROSSARM 30 X 6 X 760 mm	4	4	01200001
3	สลักเกลียว M 16 X 200 มม. BOLT, MACHINE, M 16 X 200 mm	1	—	01110202
3a	สลักเกลียว M 16 X 250 มม. สำหรับเสาคอนกรีต 12 ม. BOLT, MACHINE, M 16 X 250 mm, FOR 12 m CONCRETE POLE	—	1	01110203
4	สลักเกลียว M 16 X 400 มม. BOLT, MACHINE, M 16 X 400 mm	1	—	01110206
4a	สลักเกลียว M 16 X 450 มม. สำหรับเสาคอนกรีต 12 ม. BOLT, MACHINE, M 16 X 450 mm, FOR 12 m CONCRETE POLE	—	1	01110207
5	สลักเกลียวตลอด M 16 X 450 มม. BOLT, DOUBLE ARMING, M 16 X 450 mm	4	4	01120001
6	แหวนสี่เหลี่ยมแบน 52 X 52 X 4.5 มม. รู Ø 18 มม. มอก. 258 WASHER, SQUARE, FLAT, 52 X 52 X 4.5 mm, HOLE Ø 18 mm, TIS 258	10	10	01180100
7	ลูกรอกแรงต่ำ มอก. 227 แบบ ข (แบบ 53-2) INSULATOR, SPOOL TYPE, L.T. TIS 227, TYPE B (CLASS 53-2)	4	4	03030000
8	ที่จับลูกรอกสำหรับลูกรอก มอก. 227 แบบ ข (แบบ 53-2) CLEVIS, FLAT STEEL, FOR INSULATOR TIS 227 TYPE B (CLASS 53-2)	4	4	03130100
9	พี.จี. คอนเนคเตอร์สลักคู่ หรือคอนเนคเตอร์ชนิดบีบ ขนาดตามต้องการ CONNECTOR, PARALLEL GROOVE, DOUBLE BOLT, OR COMPRESSION TYPE, SIZE AS REQ'D	8	8	02300101 or 02320003-4
10	คอนเนคเตอร์เข้าปลายสาย ขนาดตามต้องการ CONNECTOR, DEADEND, SIZE AS REQUIRED	4	4	02310000-1

กองวิศวกรรมไฟฟ้า และเครื่องกล
ฝ่ายวิศวกรรม

ผู้เขียน
ผู้ตรวจ
วิศวกร
หัวหน้าแผนก
ผู้อำนวยการกอง
ผู้อำนวยการฝ่าย

รองผู้ว่าการฝ่ายเทคนิค

การไฟฟ้าส่วนภูมิภาค

ผู้ว่าการ 30 มิ.ย. 26

มาตรฐานการก่อสร้างระบบจำหน่ายแรงต่ำ
ช่วง 50 - 120 ม.

L.T. STANDARD CONSTRUCTION
SPAN 50 - 120 m

ใช้แทนแบบ
ถูกแทนโดยแบบ
เขียนเสร็จวันที่ 7 มิ.ย. 26
แก้แบบวันที่
มิติเป็น
มาตราส่วน

แบบเลขที่ SAI-015/26015
แผ่นที่ 3 ของจำนวน 4 แผ่น

การประกอบเลขที่ 0310
ASSEMBLY NO.

บัญชีวัสดุ
BILL OF MATERIAL

ลำดับที่ ITEM	รายละเอียด DESCRIPTION	จำนวน REQ'D I	 II	วัสดุเลขที่ MAT. NO.
11	สายอะลูมิเนียมหุ้มฉนวน PVC มอก. 293 ขนาดและความยาวตามต้องการ CABLE, Al, PVC INSULATION, TIS 293, SIZE AND LENGTH AS REQUIRED	ม. m	ม. m	02070001-4
12	สายอะลูมิเนียมแกนเหล็ก หรืออะลูมิเนียมอัลลอย ขนาด 35 หรือ 50 ต.มม. ความยาวตามต้องการ CONDUCTOR, ACSR OR Al-ALLOY, 35 OR 50 mm^2, LENGTH AS REQUIRED	ม. m	ม. m	02020001-2 or 02030001-2
13	PVC เทป กว้าง 19 มม. (ใช้ความยาว 2 ม. ต่อ 1 จุด) มอก. 386 PVC TAPE, 19 mm WIDE (2 m LONG PER POINT) TIS 386	1 ม้วน rolls	1 ม้วน rolls	02180001 or 02180002
14	การประกอบสายยึดโยง GY-03 GUY ASSEMBLY GY-03	1 ชุด set	1 ชุด set	

หมายเหตุ

1 I สำหรับติดตั้งบนเสา 9 ม. และ II สำหรับติดตั้งบนเสา 12 ม.
2 หากต้องการติดตั้งบนเสาขนาดอื่น หรือจำนวนสายไฟแรงต่ำที่ใช้พาดเป็นอย่างอื่น รายการบัญชีวัสดุนี้สามารถเปลี่ยนแปลงให้เหมาะสมกับการติดตั้งได้
3 ระยะห่างความปลอดภัยในการก่อสร้างทางไฟฟ้า ดูแบบเลขที่ S02-015/17068

NOTES

1 I FOR INSTALLATION ON 9 m POLE AND II FOR INSTALLATION ON 12 m POLE.
2 THE ITEMS IN THIS BILL OF MATERIAL MAY BE CHANGED IF THIS INSTALLATION IS ON OTHER SIZE POLE OR IT HAS OTHER NUMBER OF L.T. BARE CONDUCTORS.
3 SAFETY CLEARANCES FOR ELECTRICAL CONSTRUCTION SEE DWG. NO. S02-015/17068.

อธิทัย ทองลา พชง.3 ผปร. กฟส.อล. กฟจ.กบ. ผฟต.2 สายงาน (ต) ผวก. @PEA

กองวิศวกรรมไฟฟ้าและเครื่องกล
ฝ่ายวิศวกรรม
ผู้เขียน
ผู้สำรวจ
วิศวกร
หัวหน้าแผนก
ผู้อำนวยการกอง
ผู้อำนวยการฝ่าย
รองผู้ว่าการฝ่ายเทคนิค

การไฟฟ้าส่วนภูมิภาค
ผู้ว่าการ 20 มิ.ย. 26

มาตรฐานการก่อสร้างระบบจำหน่ายแรงต่ำ
ช่วง 50-120 ม.

L.T. STANDARD CONSTRUCTION
SPAN 50-120 m

ใช้แทนแบบ
ถูกแทนโดยแบบ
เขียนเสร็จวันที่ 7 มิ.ย. 26
แก้แบบวันที่
มิติเป็น
มาตราส่วน
แบบเลขที่ SAI-015/26015
แผ่นที่ 4 ของจำนวน 4 แผ่น