


การประกอบเลขที่ ASSEMBLY NO.	5211

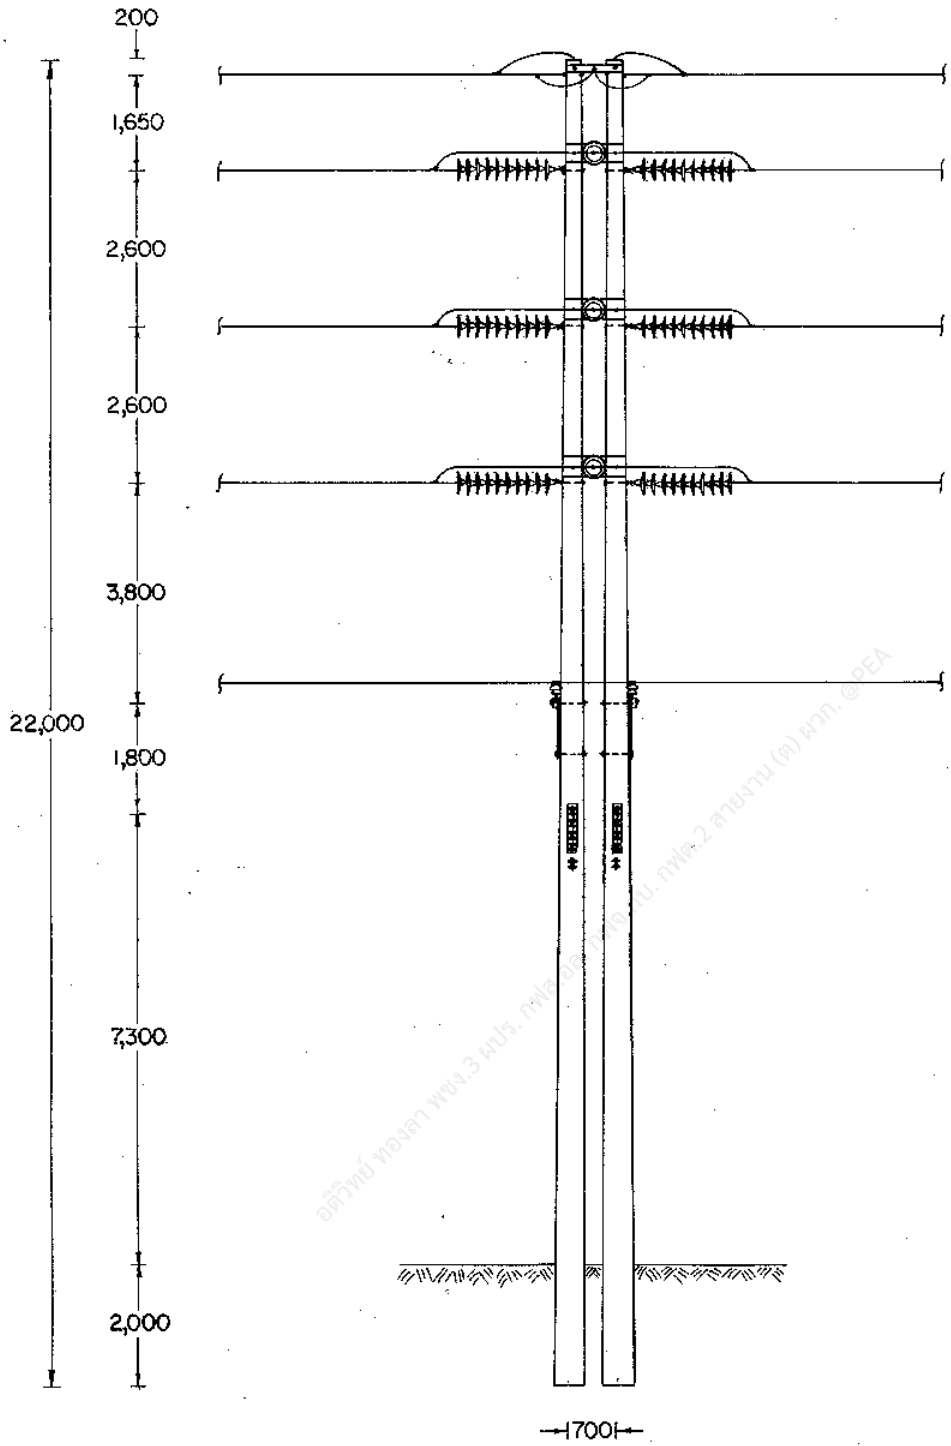

กองวิศวกรรมไฟฟ้าและเครื่องกล ฝ่ายวิศวกรรม	**การไฟฟ้าส่วนภูมิภาค**	ใช้ทดแทนแบบ
ผู้เขียน ผู้ตรวจ วิศวกร หัวหน้าแผนก หัวหน้ากอง ผู้อำนวยการฝ่าย	ผู้ว่าการ 115 kV วงจรเดี่ยว สายไฟฟ้าเดี่ยว เสาคู่สำหรับแยกสาย แบบ SS-TL-2	ถูกแทนโดยแบบ เขียนเสร็จวันที่ 2 พ.ค. 23 แก้แบบวันที่ มิติเป็น มม. มาตราส่วน 1 : 125
รองผู้ว่าการฝ่ายเทคนิค 19 มี.ค. 2523	115 kV SINGLE CIRCUIT SINGLE CONDUCTOR DOUBLE POLE, TAP LINE STRUCTURE TYPE SS—TL—2	แบบเลขที่ SAI-015/23004 แผ่นที่ 1 ของจำนวน 3 แผ่น

การประกอบเลขที่ ASSEMBLY NO.	5211

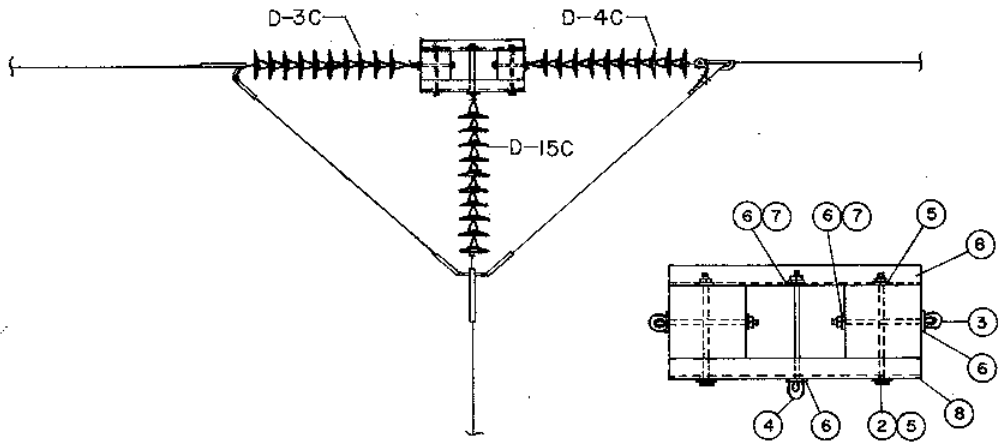

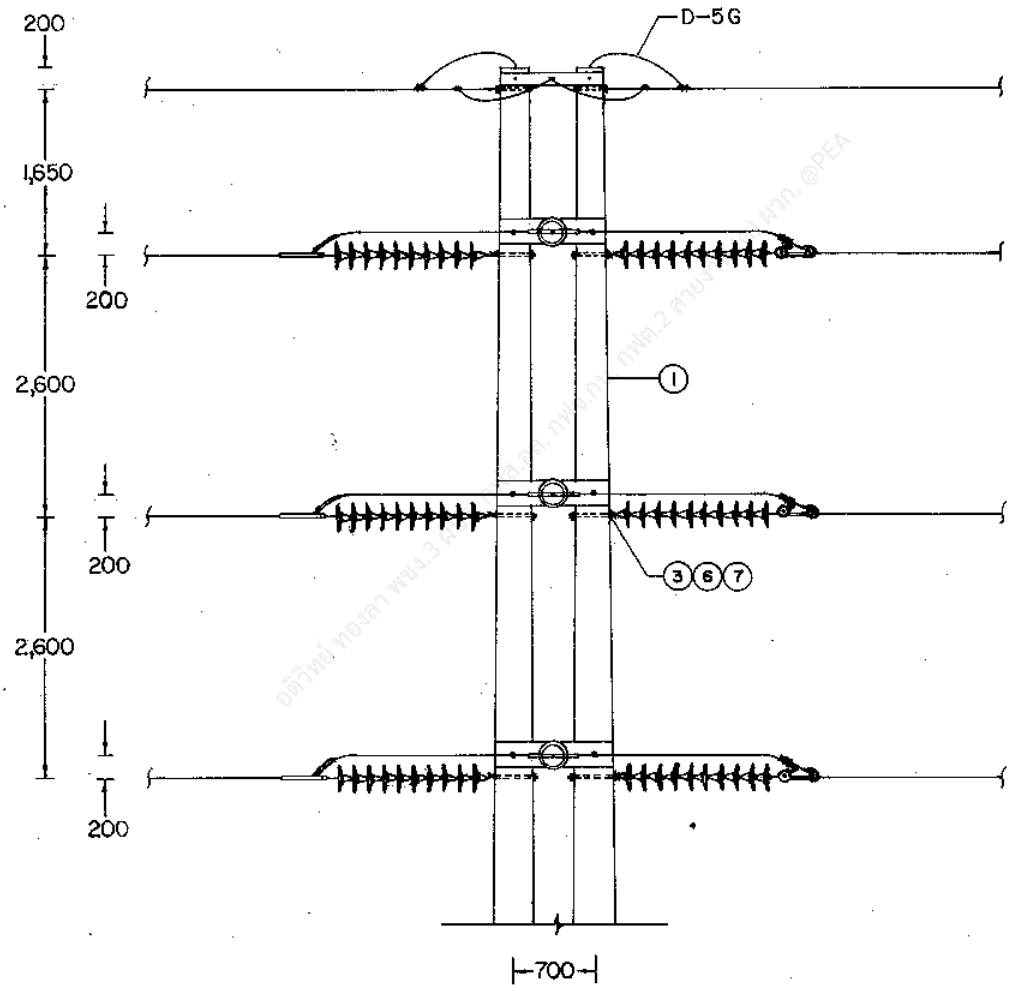

กองวิศวกรรมไฟฟ้าและเครื่องกล ฝ่ายวิศวกรรม	การไฟฟ้าส่วนภูมิภาค	ใช้แทนแบบ ถูกแทนโดยแบบ
ผู้เรียน ผู้สำรวจ วิศวกร หัวหน้าแผนก หัวหน้ากอง ผู้อำนวยการฝ่าย	ผู้ว่าการ 115 kV วงจรเดี่ยว สายไฟฟ้าเดี่ยว เสาคู่สำหรับแยกสาย แบบ SS-TL-2	เขียนเสร็จวันที่ 2 ม.ค. 23 แก้แบบวันที่ มิลลิเมตร มม. มาตราส่วน 1 : 75
ของผู้ว่าการฝ่ายเทคนิค	115 kV SINGLE CIRCUIT SINGLE CONDUCTOR DOUBLE POLE, TAP LINE STRUCTURE TYPE SS-TL-2	แบบเลขที่ SAI-015/23004 แผ่นที่ 2 ของจำนวน 3 แผ่น

19 มี.ค. 2523

การประกอบเลขที่ ASSEMBLY NO. 5211

บัญชีวัสดุ BILL OF MATERIAL

ลำดับที่ ITEM	รายละเอียด DESCRIPTION	จำนวน REQ'D	วัสดุเลขที่ MAT. NO.
1	เสาคอนกรีต 22 ม. POLE, CONCRETE 22 m. LONG	2	0001001I (0041)
2	สลักเกลียว M 16 X 450 มม. BOLT, MACHINE, M 16 X 450 mm.	6	0111020I (0227)
3	สลักห่วงโอแวล M 20 X 350 มม. BOLT, OVAL EYE M 20 X 350 mm.	6	0115010O (0260)
4	สลักห่วงโอแวล M 20 X 450 มม. BOLT, OVAL EYE M 20 X 450 mm.	3	0115010I (0261)
5	แหวนสี่เหลี่ยมแบน 52X52X4.5 มม. รู Ø 18 มม. มอก. 258 WASHER, SQUARE, FLAT 52X52X4.5 mm. HOLE Ø 18 mm TIS 258	12	0118010O (0355)
6	แหวนสี่เหลี่ยมแบน 62X62X6 มม. รู Ø 22 มม. มอก. 258 WASHER, SQUARE, FLAT 62X62X6 mm. HOLE Ø 22 mm TIS 258	18	0118010I (0356)
7	แหวนสปริง M 20 มอก. 259 WASHER, LOCK, M 20, TIS 259	9	0118030I (0366)
8	เหล็กรูปรางน้ำ 200X80X7.5 มม. ยาว 1,000 มม. STEEL CHANNEL 200X80X7.5 mm, 1,000 mm LONG	6	0100040O (2675)

รายละเอียด DETAIL

D-3C	การประกอบลูกถ้วยแขวน SUSPENSION INSULATOR ASSEMBLY	3	
D-4C	การประกอบลูกถ้วยแขวน SUSPENSION INSULATOR ASSEMBLY	3	
D-15C	การประกอบลูกถ้วยแขวน SUSPENSION INSULATOR ASSEMBLY	3	
D-5G	การต่อสายล่อฟ้า OVERHEAD GROUND WIRE CONNECTION	1	
D-10B	ฐานรากเสา POLE FOUNDATION	1	

กองวิศวกรรมไฟฟ้าและเครื่องกล ฝ่ายวิศวกรรม ผู้เขียน ผู้สำรวจ วิศวกร หัวหน้าแผนก หัวหน้ากอง ผู้อำนวยการฝ่าย รองผู้ว่าการฝ่ายเทคนิค	การไฟฟ้าส่วนภูมิภาค ผู้ว่าการ 115 kV วงจรเดี่ยว สายไฟฟ้าเดี่ยว เสาคู่สำหรับแยกสาย แบบ SS-TL-2 23 115 kV SINGLE CIRCUIT SINGLE CONDUCTOR DOUBLE POLE, TAP LINE STRUCTURE TYPE SS—TL—2	ใช้แทนแบบ ถูกแทนโดยแบบ เขียนเสร็จวันที่ 2 ม.ค. 23 แก้แบบวันที่ มิติเป็น มาตราส่วน แบบเลขที่ SAI-015/23004 แผ่นที่ 3 ของจำนวน 3 แผ่น

ฉบับ พ.ศ. 2523