การประกอบเลขที่
ASSEMBLY NO. 5 2 8 2

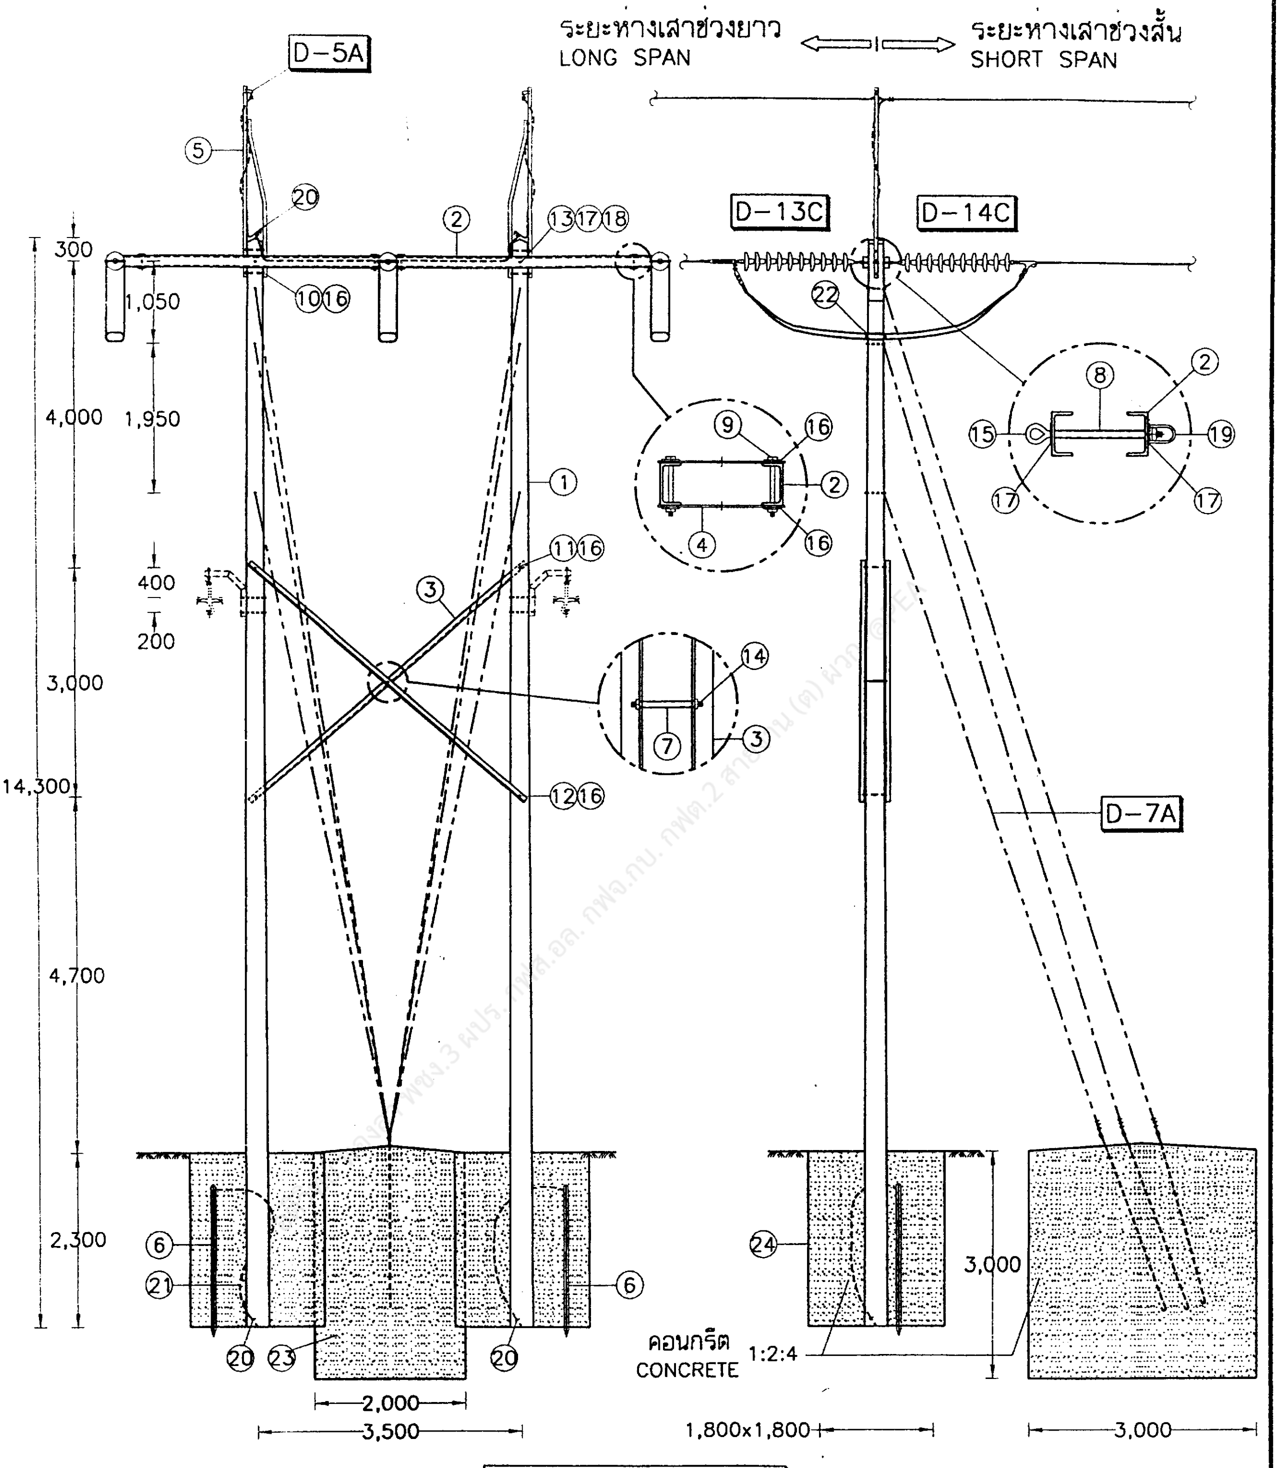
ระยะห่างเสาช่วงยาว
LONG SPAN
ระยะห่างเสาช่วงสั้น
SHORT SPAN
D-5A
D-13C
D-14C
D-7A
5
20
2
13 17 18
10 16
1
11 16
3
12 16
9
16
2
4
16
14
7
3
22
8
2
15
19
17
17
6
21
20
23
20
6
24
300
1,050
4,000
1,950
400
200
3,000
14,300
4,700
2,300
3,000
คอนกรีต
CONCRETE
1:2:4
2,000
3,500
1,800x1,800
3,000

SD-HFDD-1B

กองวิศวกรรมไฟฟ้าและเครื่องกล ฝ่ายวิศวกรรม	การไฟฟ้าส่วนภูมิภาค	ใช้แทนแบบ .... ถูกแทนโดยแบบ ....
ผู้เขียน Suppakit Boonrung ผู้สำรวจ.................. วิศวกร.......... หัวหน้าแผนก.......... ผู้อำนวยการกอง.......... ผู้อำนวยการฝ่าย..........	ผู้ว่าการ.................. 23 ธ.ค. 2541 แบบโครงสร้างสายส่ง 115 kV วงจรเดี่ยว สายไฟฟ้าคู่ เสาคู่สำหรับเข้าปลายสายสองข้างแบบ H-FRAME กรณีข้ามเหวช่วงไม่เกิน 150 ม. แบบ SD-HFDD-1B	เขียนเสร็จวันที่ 14 ต.ค. 2541 แก้แบบวันที่ .... มิติเป็น มิลลิเมตร มาตราส่วน 1 : 100
รองผู้ว่าการเทคนิคและบริการ	115 kV LINE STRUCTURE CONSTRUCTION, SINGLE CIRCUIT DOUBLE CONDUCTOR, H-FRAME DOUBLE DEADEND STRUCTURE, IN CASE OF CROSSING THE VALLEY ≤150 m TYPE SD-HFDD-1B	แบบเลขที่ SA1-015/41027 แผ่นที่ 1 ของจำนวน 3 แผ่น

23 ธ.ค. 2541

การประกอบเลขที่ ASSEMBLY NO.	5282

บัญชีวัสดุ
BILL OF MATERIAL

ลำดับที่ ITEM	รายละเอียด DESCRIPTION	จำนวน REQ'D	วัสดุเลขที่ MAT. NO.
1	เสาคอนกรีต 14.30 เมตร POLE, CONCRETE, 14.30 m LONG	2	–
2	เหล็กรูปรางน้ำ ขนาด 150x75x6.5 มม. ยาว 7.40 ม. (ดูรายละเอียด A) STEEL CHANNEL 150x75x6.5 mm, 7.40 m LONG (SEE DETAIL A)	2	–
3	เหล็กฉาก ขนาด 75x75x6 มม. ยาว 4.83 ม. (ดูรายละเอียด B) STEEL ANGLE 75x75x6 mm, 4.83 m LONG (SEE DETAIL B)	2	–
4	แผ่นเหล็กขนาด 6x100x450 มม. (เจาะรูกึ่งกลางให้เป็นขนาด ø 22 มม.) PLATE, STEEL 6x100x450 mm (DRILLING THE CENTER HOLE ø 22 mm)	8	01030002
5	เหล็กฉากรับสายล่อฟ้าทางโค้ง ขนาด 65x65x6 มม. ยาว 2.50 ม. มอก. 116 OVERHEAD GROUND WIRE CORNER BAYONET, 65x65x6 mm, 2.50 m LONG TIS 116	2	01010005
6	หลักดิน ขนาด 60x60x5 มม. ยาว 2 ม. ROD, GROUND, 60x60x5 mm, 2 m LONG	2	01220002
7	ท่อเหล็ก ขนาด 20 มม. หนา 2.65 มม. ยาว 285 มม. PIPE, IRON DIA. 20 mm ID, 2.65 mm THICKNESS, 285 mm LONG	1	–
8	ท่อเหล็ก ขนาด 25 มม. หนา 3.25 มม. ยาว 365 มม. PIPE, IRON DIA. 25 mm ID, 3.25 mm THICKNESS, 365 mm LONG	3	–
9	สลักเกลียว M 16x200 มม. BOLT, MACHINE, M 16x200 mm	8	01110202
10	สลักเกลียว M 16x250 มม. BOLT, MACHINE, M 16x250 mm	4	01110203
11	สลักเกลียว M 16x300 มม. BOLT, MACHINE, M 16x300 mm	2	01110204
12	สลักเกลียว M 16x350 มม. BOLT, MACHINE, M 16x350 mm	2	01110205
13	สลักเกลียว M 20x450 มม. BOLT, MACHINE, M 20x450 mm	2	01110302
14	สลักเกลียวตลอด M 16x400 มม. BOLT, DOUBLE ARMING, M 16x400 mm	1	01120000
15	สลักห่วงโอแวล M 20x450 มม. BOLT, OVAL EYE, M 20x450 mm	3	01150101
16	แหวนสี่เหลี่ยมแบน 52x52x4.5 มม. รู ø18 มม. มอก. 258 WASHER, SQUARE, FLAT 52x52x4.5 mm, HOLE ø18 mm TIS 258	32	01180100
17	แหวนสี่เหลี่ยมแบน 62x62x6 มม. รู ø22 มม. มอก. 258 WASHER, SQUARE, FLAT 62x62x6 mm, HOLE ø22 mm TIS 258	10	01180101
18	แหวนสปริง M 20 มอก. 259 WASHER, LOCK, M 20 TIS 259	2	01180302
19	อายเล็ท สำหรับสลักเกลียว EYELET FOR BOLT M 20	3	01180002
20	ยูแคล้มป์สลัก 1 ตัว M 8 CLAMP, SINGLE U-BOLT, M 8	12	01230000

กองวิศวกรรมไฟฟ้าและเครื่องกล ฝ่ายวิศวกรรม	การไฟฟ้าส่วนภูมิภาค	ใช้แทนแบบ .... ถูกแทนโดยแบบ ....
ผู้เขียน Supplakit Boonreung ผู้สำรวจ .... วิศวกร .... หัวหน้าแผนก .... ผู้อำนวยการกอง .... ผู้อำนวยการฝ่าย	ผู้ว่าการ .... 23 ธ.ค. 2541 แบบโครงสร้างสายส่ง 115 kV วงจรเดี่ยว สายไฟฟ้าคู่ เสาคู่สำหรับเข้าปลายสายสองข้างแบบ H-FRAME กรณีข้ามเหวช่วงไม่เกิน 150 ม. แบบ SD-HFDD-1B	เขียนเสร็จวันที่ 14 ต.ค. 2541 แก้แบบวันที่ .... มิติเป็น .... มาตราส่วน ....
รองผู้ว่าการเทคนิคและบริการ	115 kV LINE STRUCTURE CONSTRUCTION, SINGLE CIRCUIT DOUBLE CONDUCTOR, H-FRAME DOUBLE DEADEND STRUCTURE, IN CASE OF CROSSING THE VALLEY ≤150 m TYPE SD-HFDD-1B	แบบเลขที่ SA1-015/41027 แผ่นที่ 2 ของจำนวน 3 แผ่น

23 ธ.ค. 2541

การประกอบเลขที่ ASSEMBLY NO.	5282

บัญชีวัสดุ
BILL OF MATERIAL

ลำดับที่ ITEM	รายละเอียด DESCRIPTION	จำนวน REQ'D	วัสดุเลขที่ MAT. NO.
21	ลวดเหล็กตีเกลียว 50 ต.มม. WIRE, STEEL STRANDED 50 mm^2	15 ม. m	01100004
22	ปรีฟอร์มแยกสาย SPACER, HELICAL ROD, PREFORMED	3	–
23	สมอบกคอนกรีต 3x2x3 ม. พร้อมก้านสมอบกแบบห่วงสองร่อง M 24x2,500 มม. 3 ก้าน CONCRETE ANCHOR 3x2x3 m ; COMP. WITH 3 SETS OF m 24x2,500 mm, ANCHOR ROD, DOUBLE STRAND EYE	1	– 01210004
24	คอนกรีต 1 : 2 : 4 CONCRETE 1 : 2 : 4	14 ม.^{3} m^3	–

รายละเอียด
DETAIL

D-5A	การต่อสายล่อฟ้า OVERHEAD GROUND WIRE CONNECTION	2	
D-13C	การประกอบลูกถ้วยแขวน SUSPENSION INSULATOR ASSEMBLY	3	
D-14C	การประกอบลูกถ้วยแขวน SUSPENSION INSULATOR ASSEMBLY	3	
D-7A	การประกอบสายยึดโยงลวดเหล็กตีเกลียว 95 ต.มม. STEEL STRANDED WIRE 95 mm^2 GUY ASSEMBLY	6	

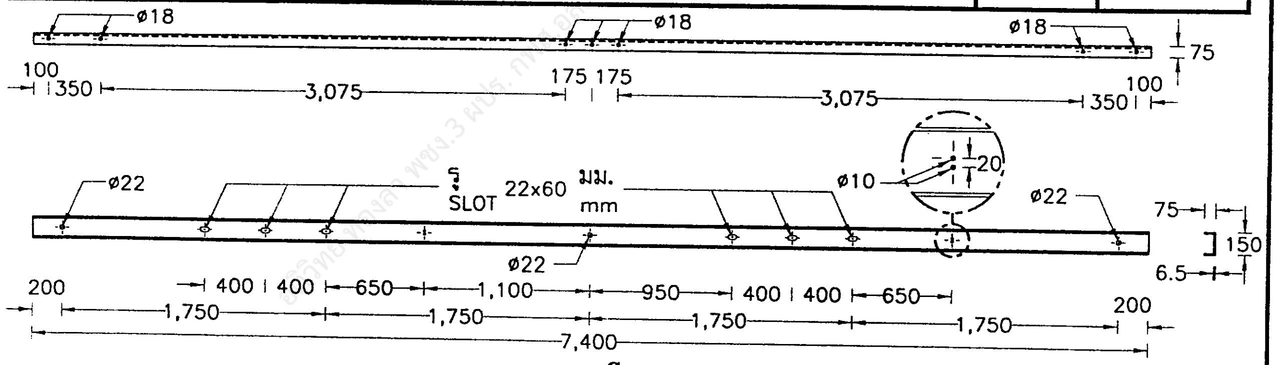
ø18
ø18
ø18
75
100
350
3,075
175 175
3,075
100
350
ø22
รู
SLOT
22x60
มม.
mm
ø10
20
ø22
75
150
6.5
ø22
200
400 400
650
1,100
950
400 400
650
1,750
1,750
1,750
1,750
200
7,400

รายละเอียด
DETAIL A

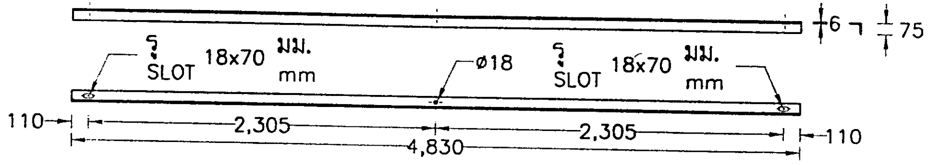
75
6
75
รู
SLOT
18x70
มม.
mm
ø18
รู
SLOT
18x70
มม.
mm
110
2,305
2,305
110
4,830

รายละเอียด
DETAIL B

กองวิศวกรรมไฟฟ้าและเครื่องกล ฝ่ายวิศวกรรม	การไฟฟ้าส่วนภูมิภาค	ใช้แทนแบบ .... ถูกแทนโดยแบบ ....
ผู้เขียน Supphchit Boonreung ผู้สำรวจ .... วิศวกร .... หัวหน้าแผนก .... ผู้อำนวยการกอง .... ผู้อำนวยการฝ่าย	ผู้ว่าการ .... 23 ธ.ค. 2541 แบบโครงสร้างสายส่ง 115 kV วงจรเดี่ยว สายไฟฟ้าคู่ เสาคู่สำหรับเข้าปลายสายสองข้างแบบ H-FRAME กรณีข้ามเหวช่วงไม่เกิน 150 ม. แบบ SD-HFDD-1B	เขียนเสร็จวันที่ 14 ต.ค. 2541 แก้แบบวันที่ .... มิติเป็น มิลลิเมตร มาตราส่วน 1 : 50
รองผู้ว่าการเทคนิคและบริการ	115 kV LINE STRUCTURE CONSTRUCTION, SINGLE CIRCUIT DOUBLE CONDUCTOR, H-FRAME DOUBLE DEADEND STRUCTURE, IN CASE OF CROSSING THE VALLEY ≤150 m TYPE SD-HFDD-1B	แบบเลขที่ SA1-015/41027 แผ่นที่ 3 ของจำนวน 3 แผ่น

23 ธ.ค. 2541