การประกอบเลขที่ ASSEMBLY NO.	3309

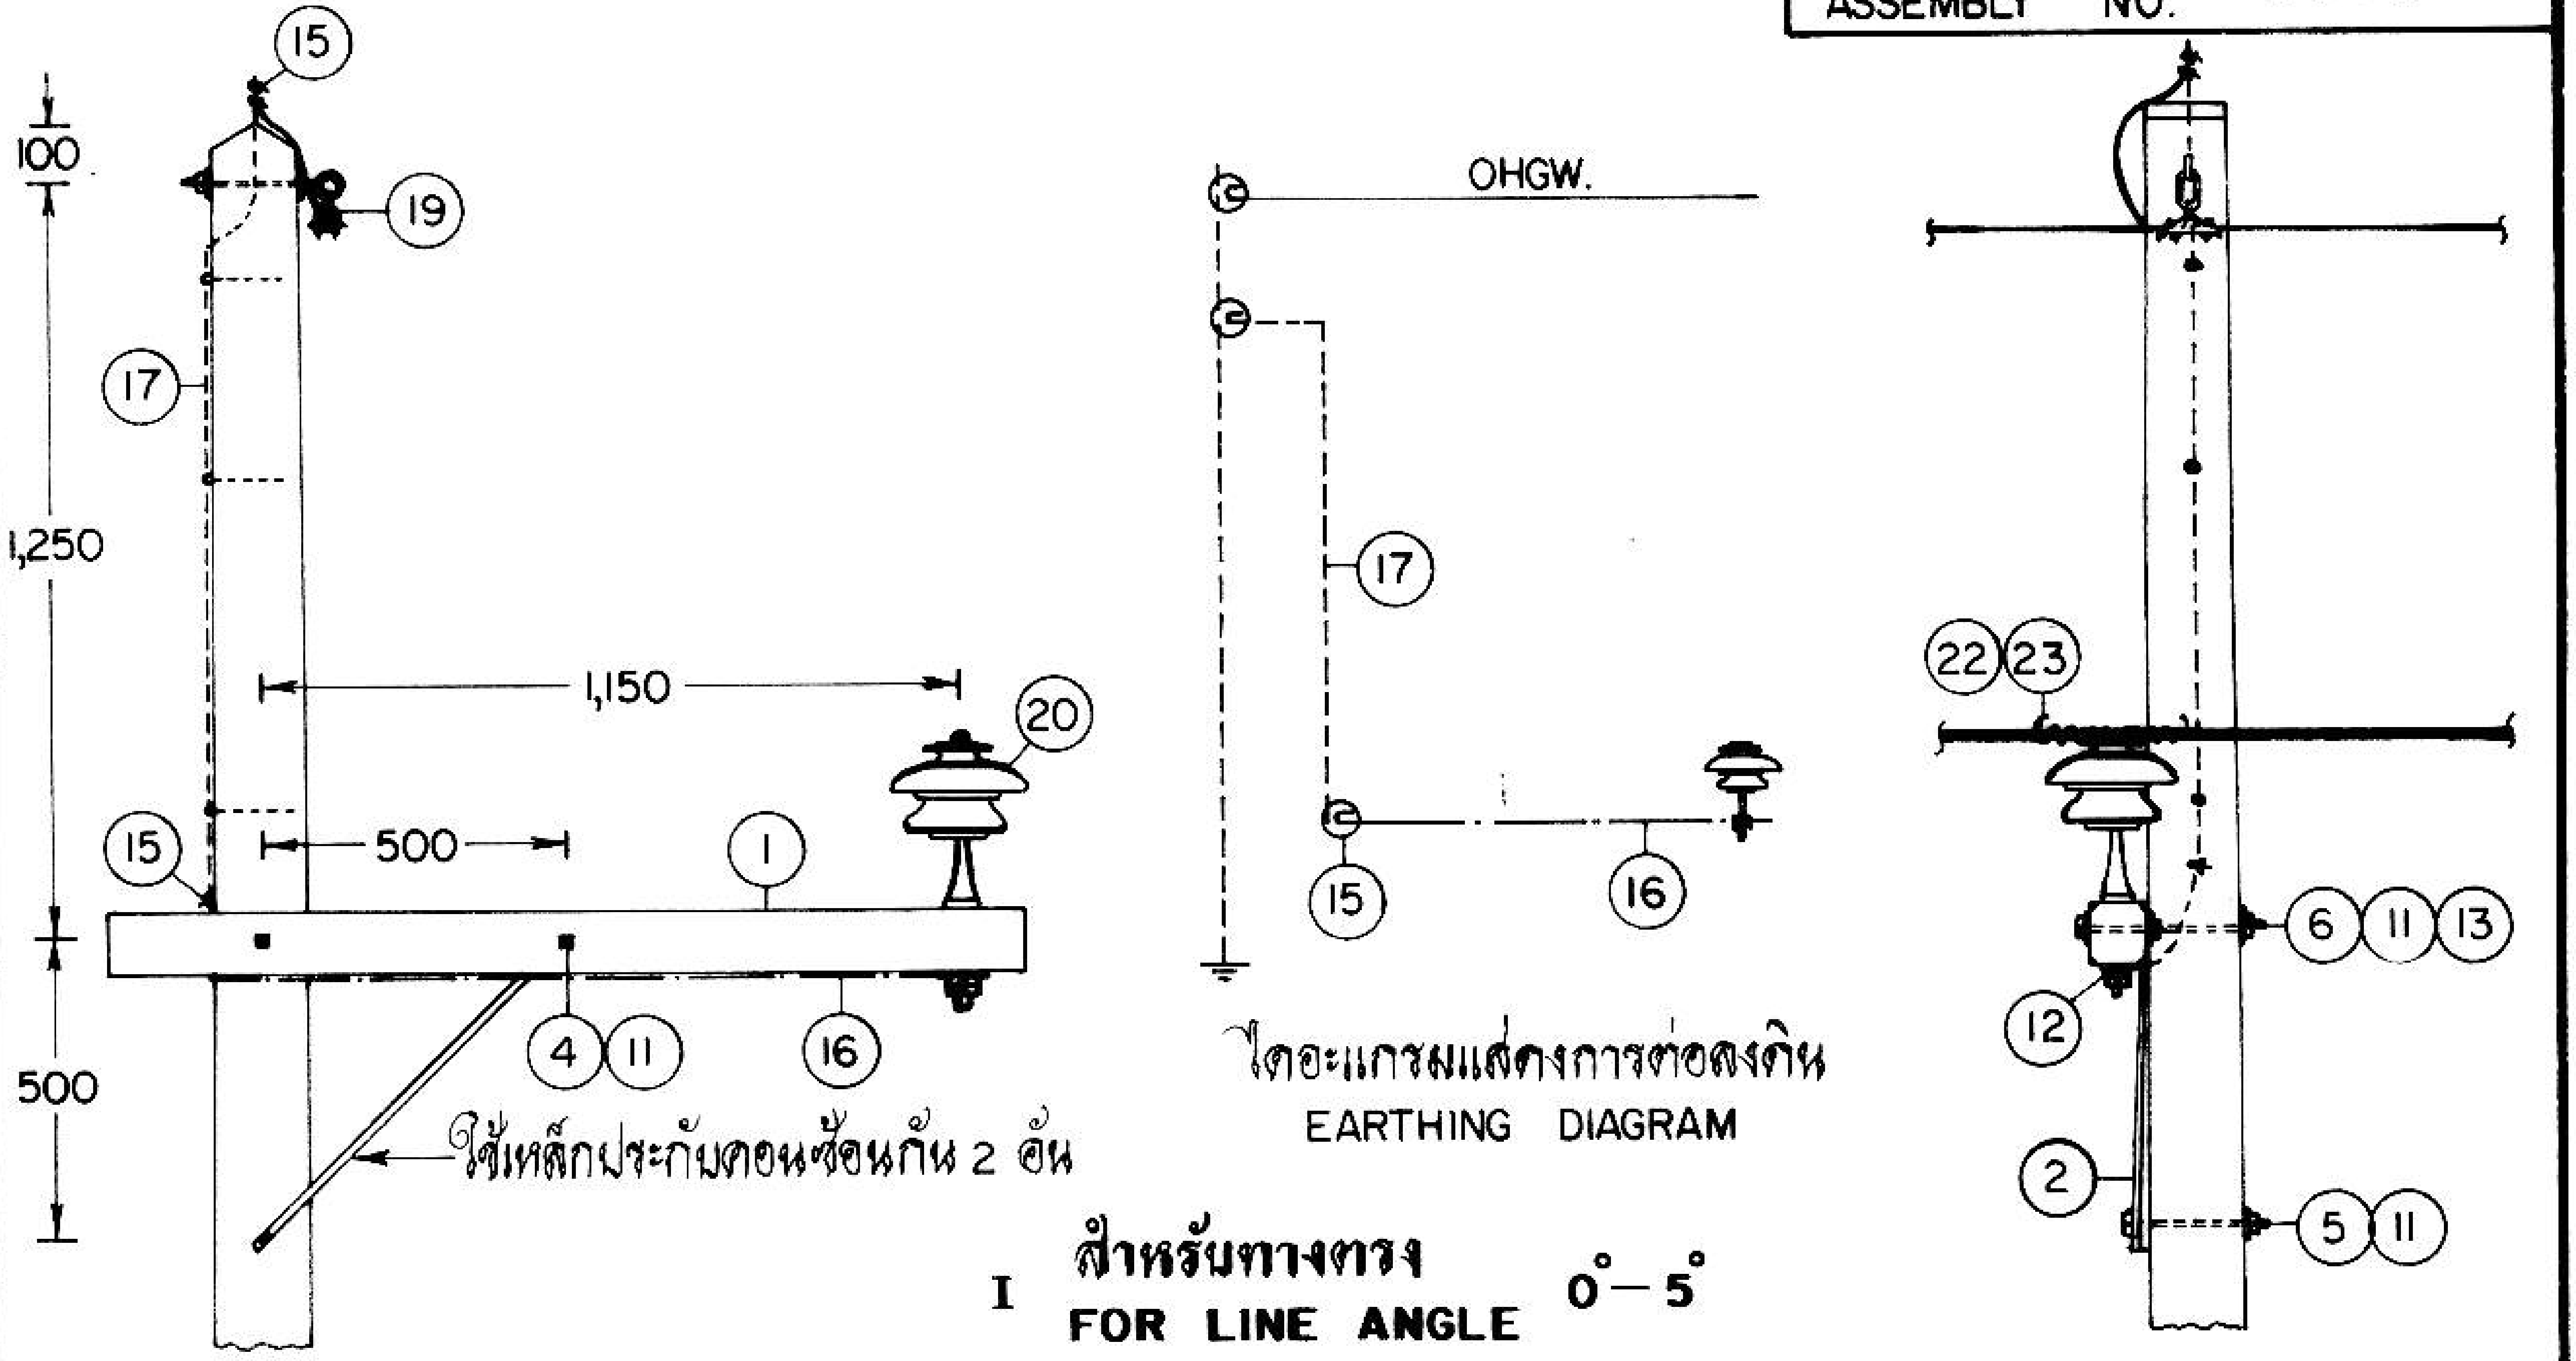

ไดอะแกรมแสดงการต่อลงดิน
EARTHING DIAGRAM

I สำหรับทางตรง
FOR LINE ANGLE 0°–5°

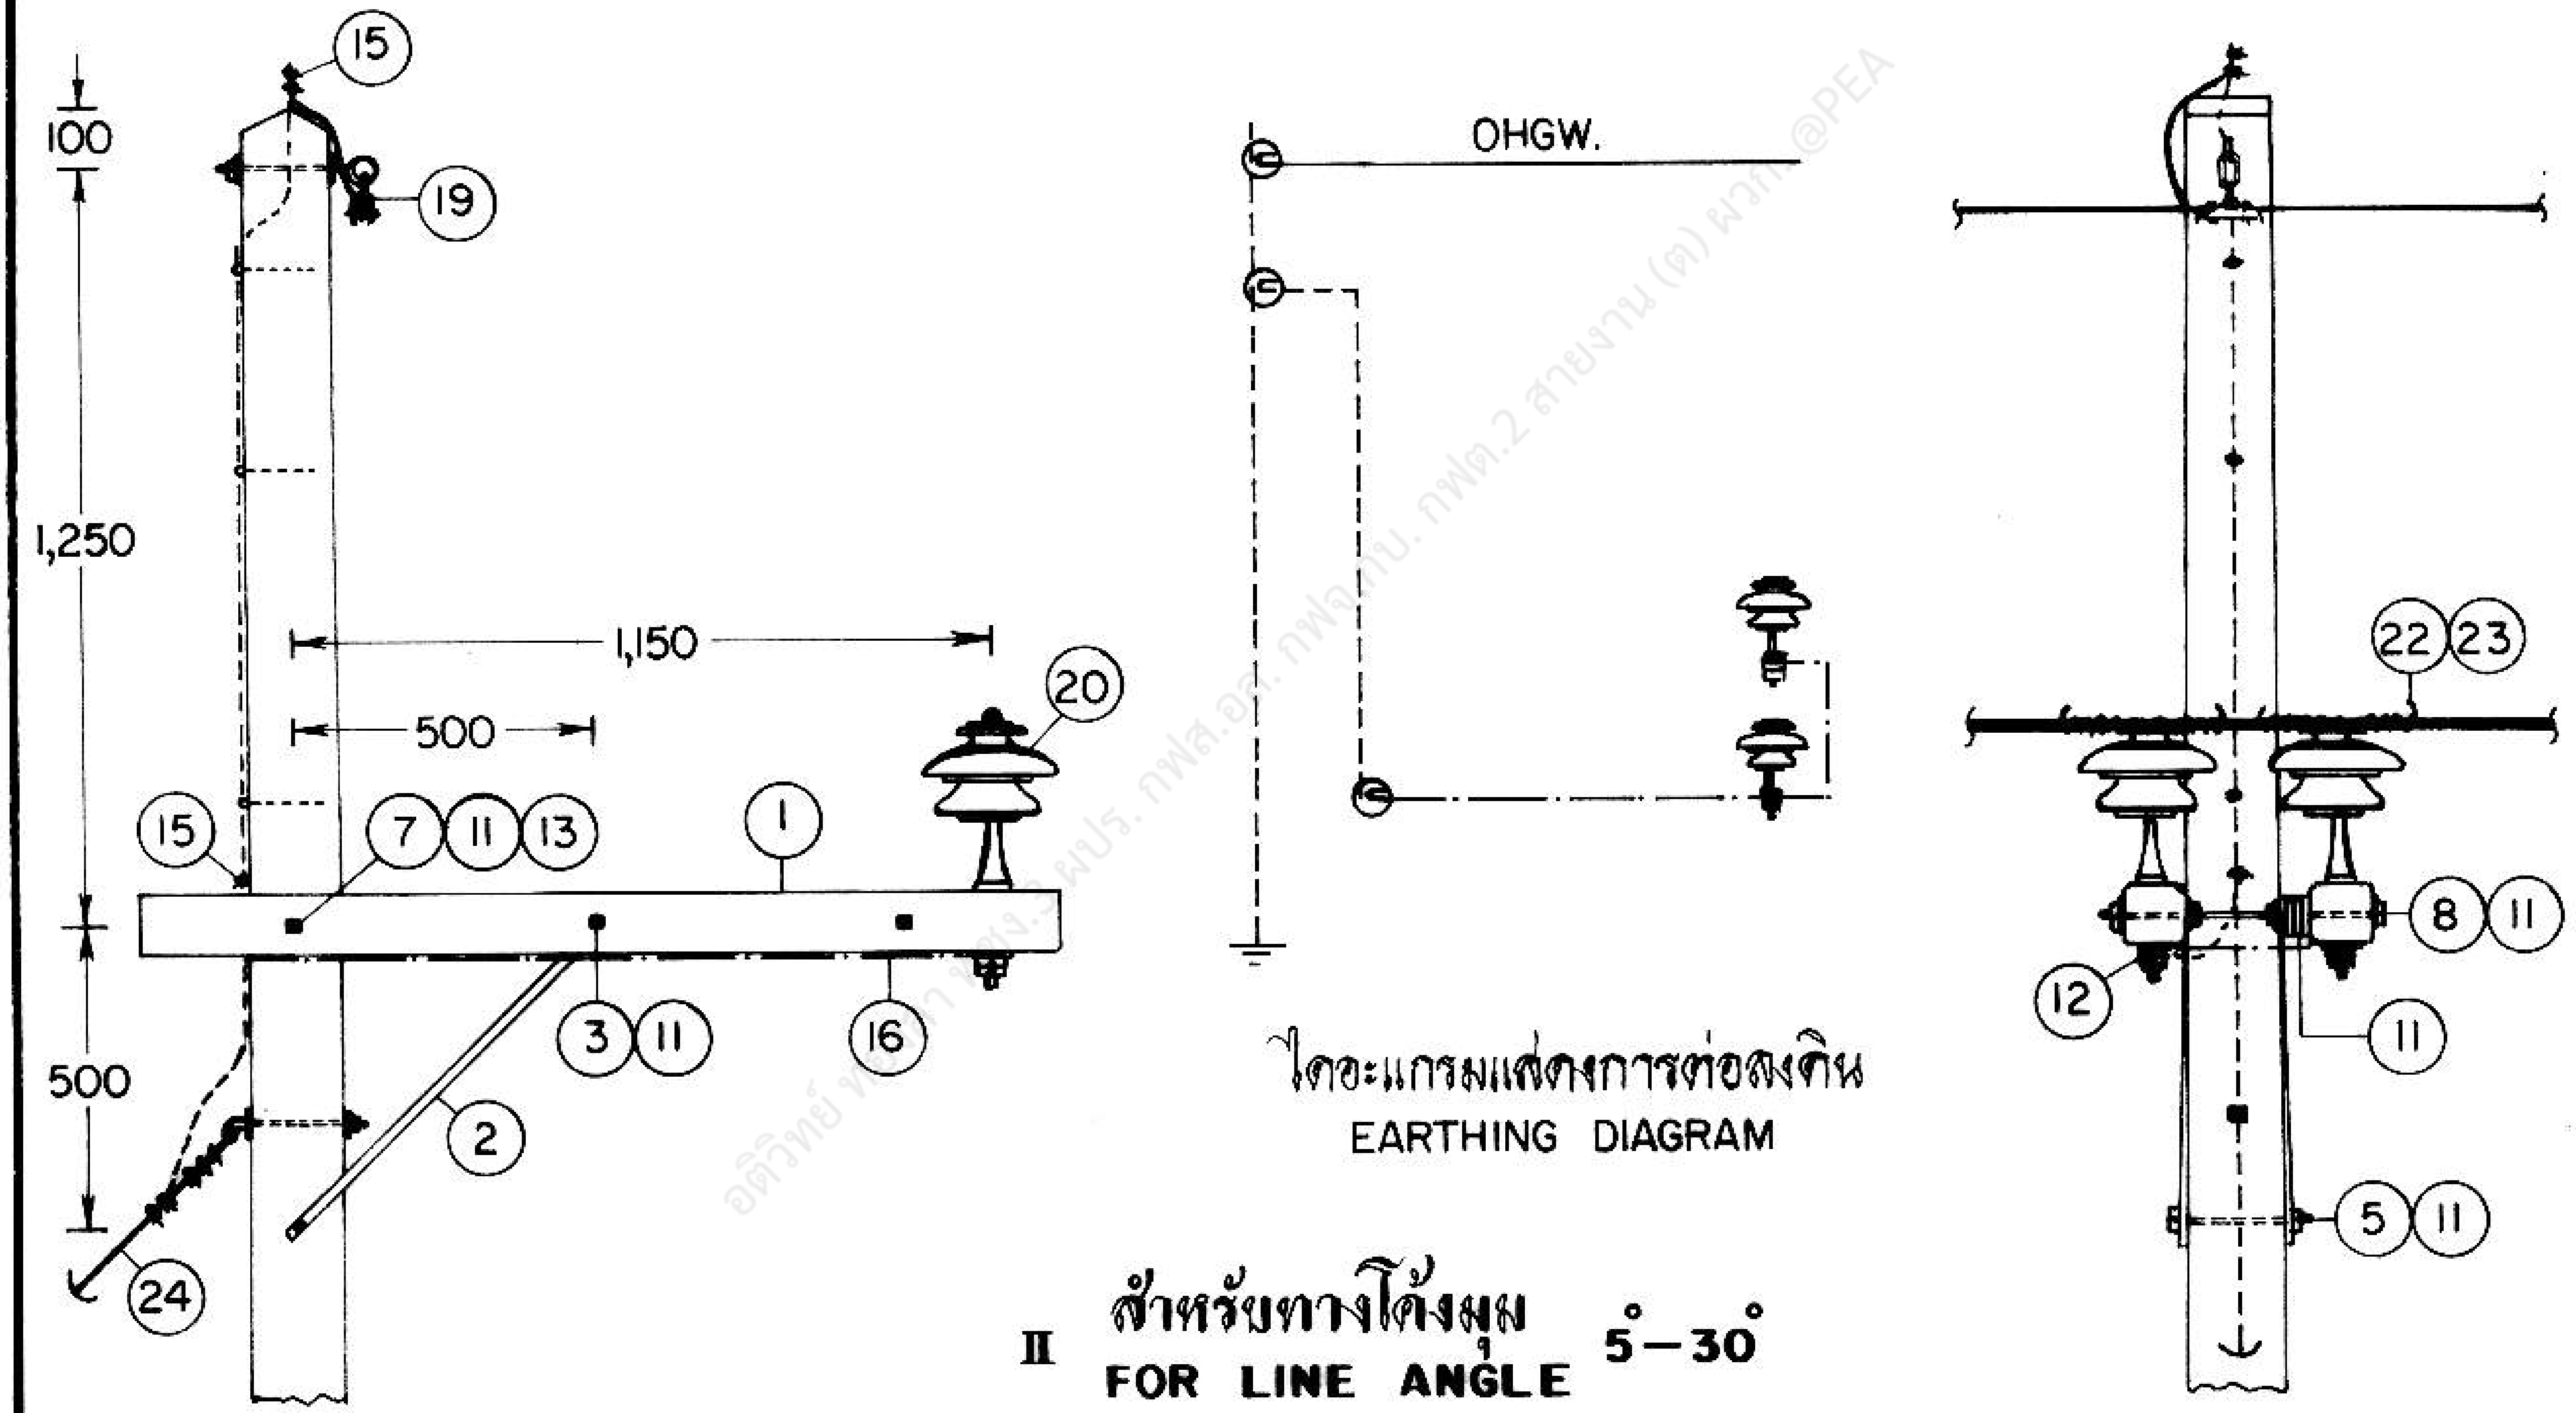

ไดอะแกรมแสดงการต่อลงดิน
EARTHING DIAGRAM

II สำหรับทางโค้งมุม
FOR LINE ANGLE 5°–30°

ผปร. กฟส.อล. กฟจ.ฉบ. กฟต.2 สายงาน (ต) ผวก.@PEA

สำหรับใช้ก่อสร้างในบริเวณที่มีโหลดน้อย และไม่มีการปรับปรุงเป็น ระบบ 3 เฟส 33 กิโลโวลต์ ในอนาคตอันใกล้
FOR CONSTRUCTION IN LIGHT LOAD SITE WHERE SHALL NOT BE REVAMPED TO 3-PHASE, 33 kV SYSTEM IN THE NEAR FUTURE.

กองวิศวกรรมไฟฟ้าและเครื่องกล ฝ่ายวิศวกรรม	การไฟฟ้าส่วนภูมิภาค	ใช้แทนแบบ ถูกแทนโดยแบบ
ผู้เขียน ผู้สำรวจ วิศวกร หัวหน้าแผนก ผู้อำนวยการกอง (แทน) ผู้อำนวยการฝ่าย	ผู้ว่าการ 2 พ.ย. 2531 การประกอบคอนแขนท้าวแขน กับเสาคอนกรีต 12 ม. (กรณีใช้คอนคอนกรีต) ระบบ 1 เฟส 19 kV	เขียนเสร็จวันที่ 16 พ.ค. 31 แก้แบบวันที่ มิติเป็น มม. มาตราส่วน 1 : 25
รองผู้ว่าการฝ่ายเทคนิค	ALLEY ARM ASSEMBLY ON 12 m CONCRETE POLE (CONCRETE CROSSARM) 1-PHASE, 19 kV SYSTEM	แบบเลขที่ SA1-015/31045 แผ่นที่ 1 ของจำนวน 4 แผ่น

การประกอบเลขที่
ASSEMBLY NO. **3309**

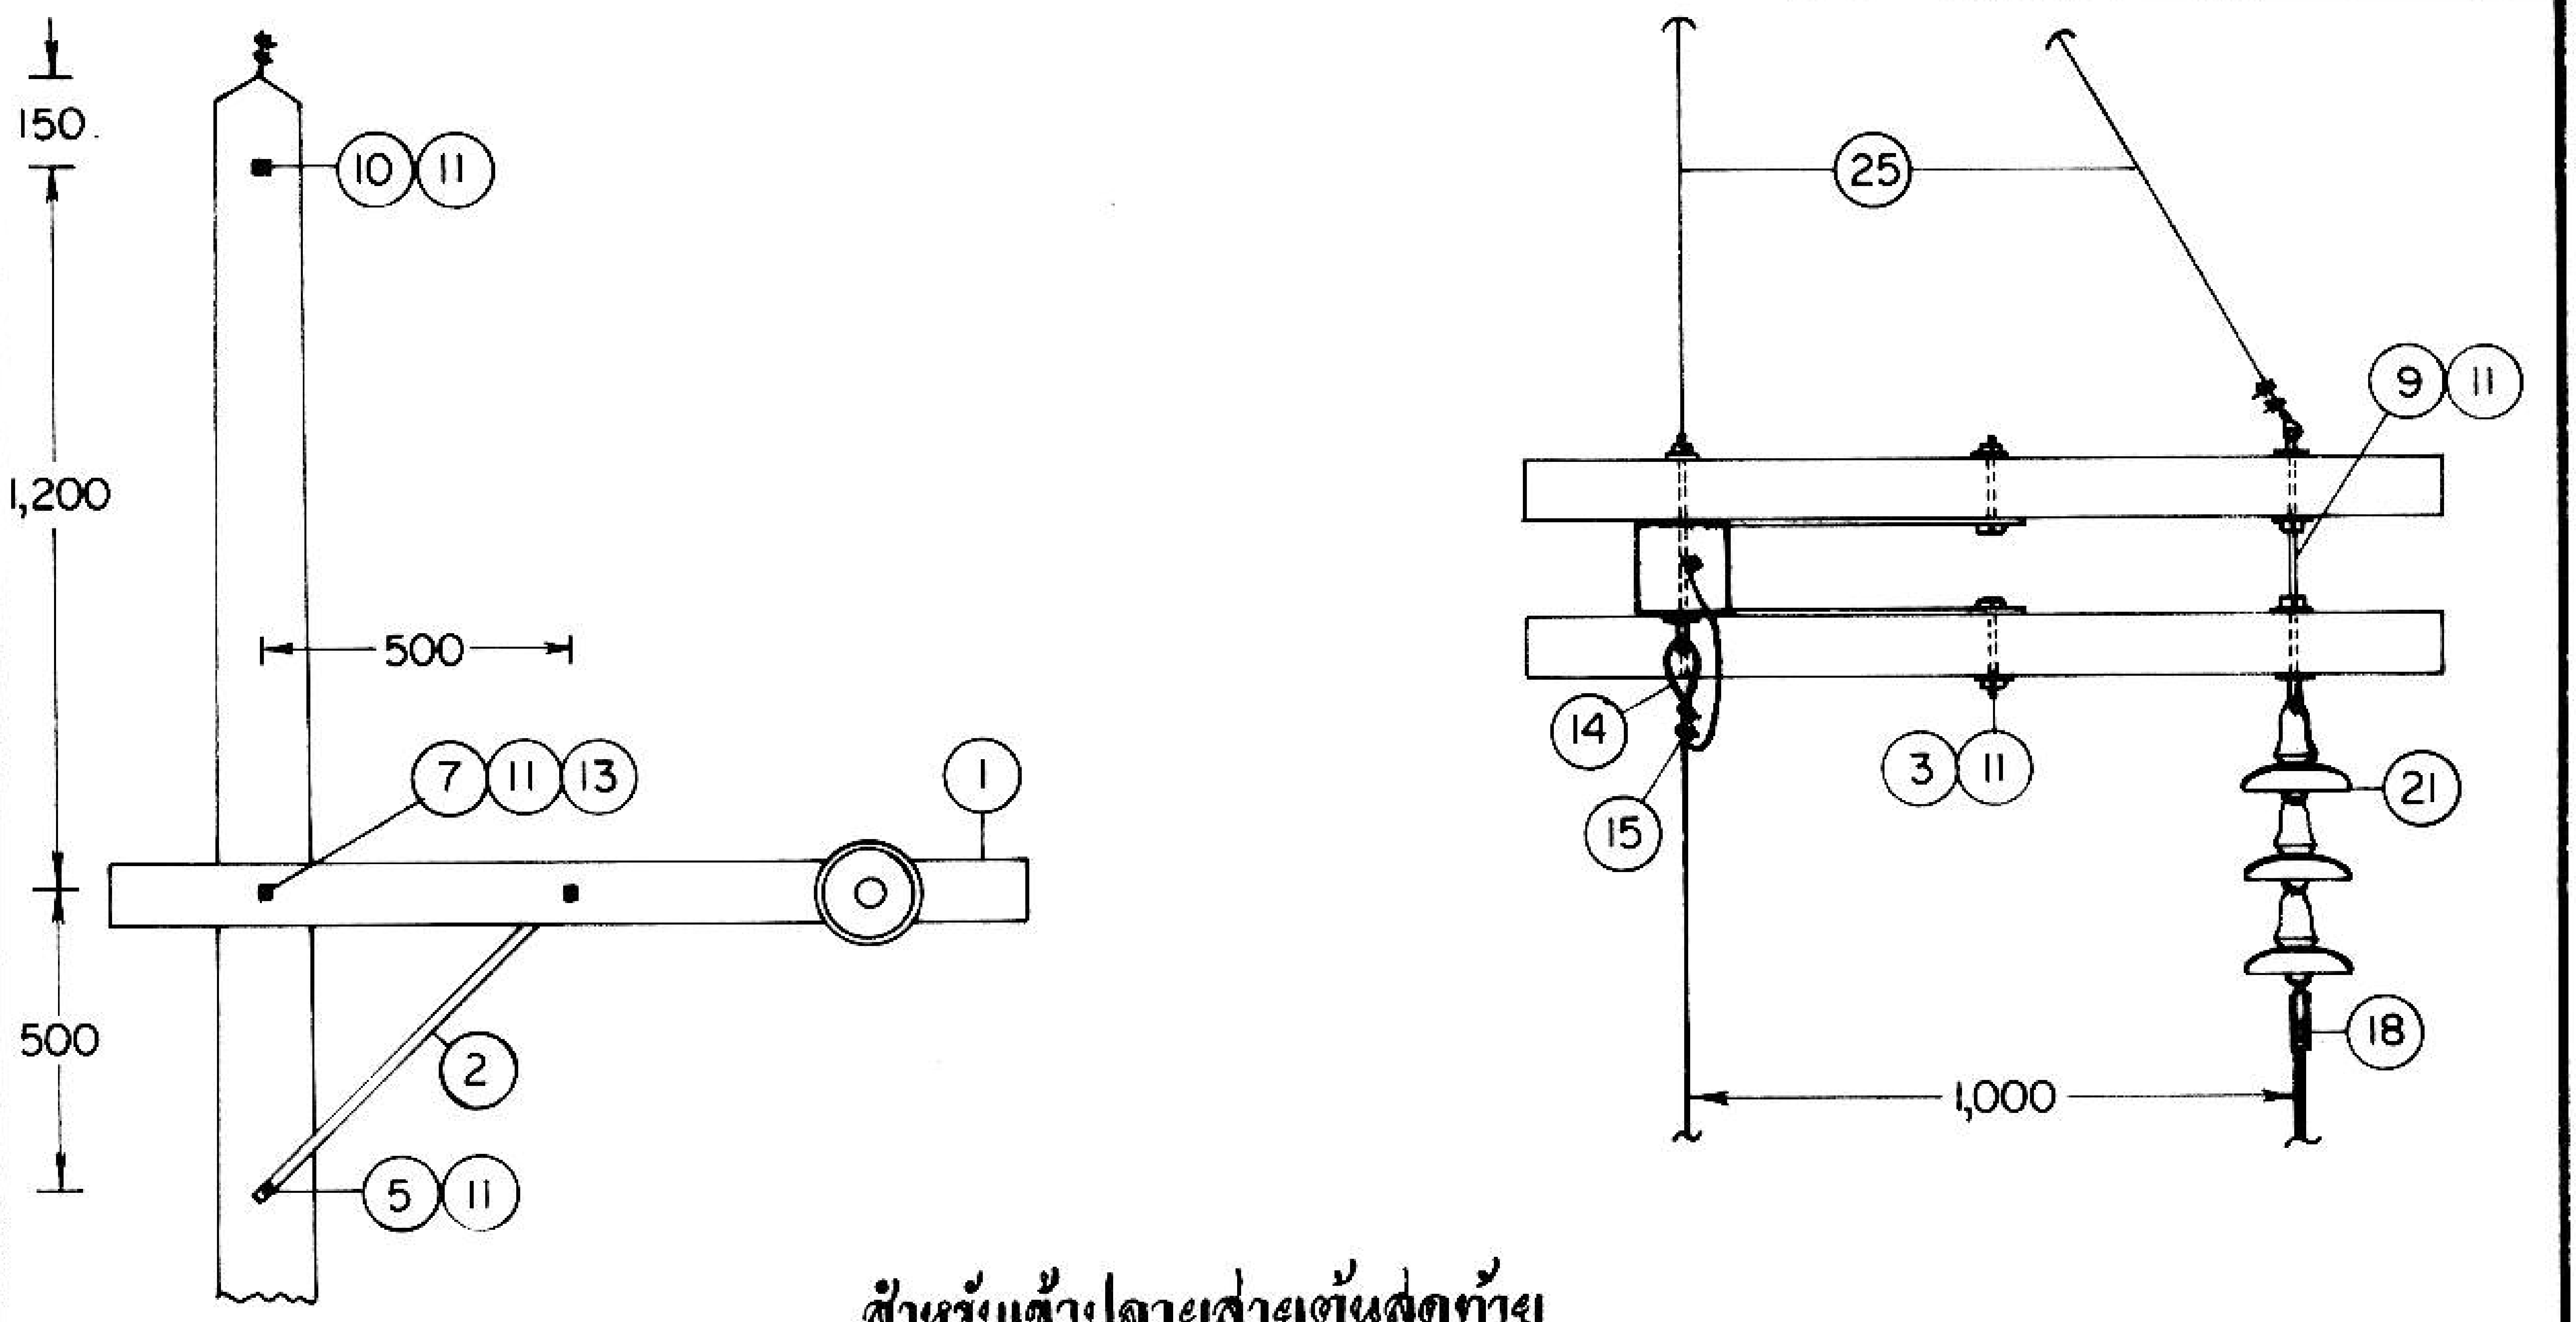

III สำหรับเข้าปลายสายต้นสุดท้าย
FOR DEADEND

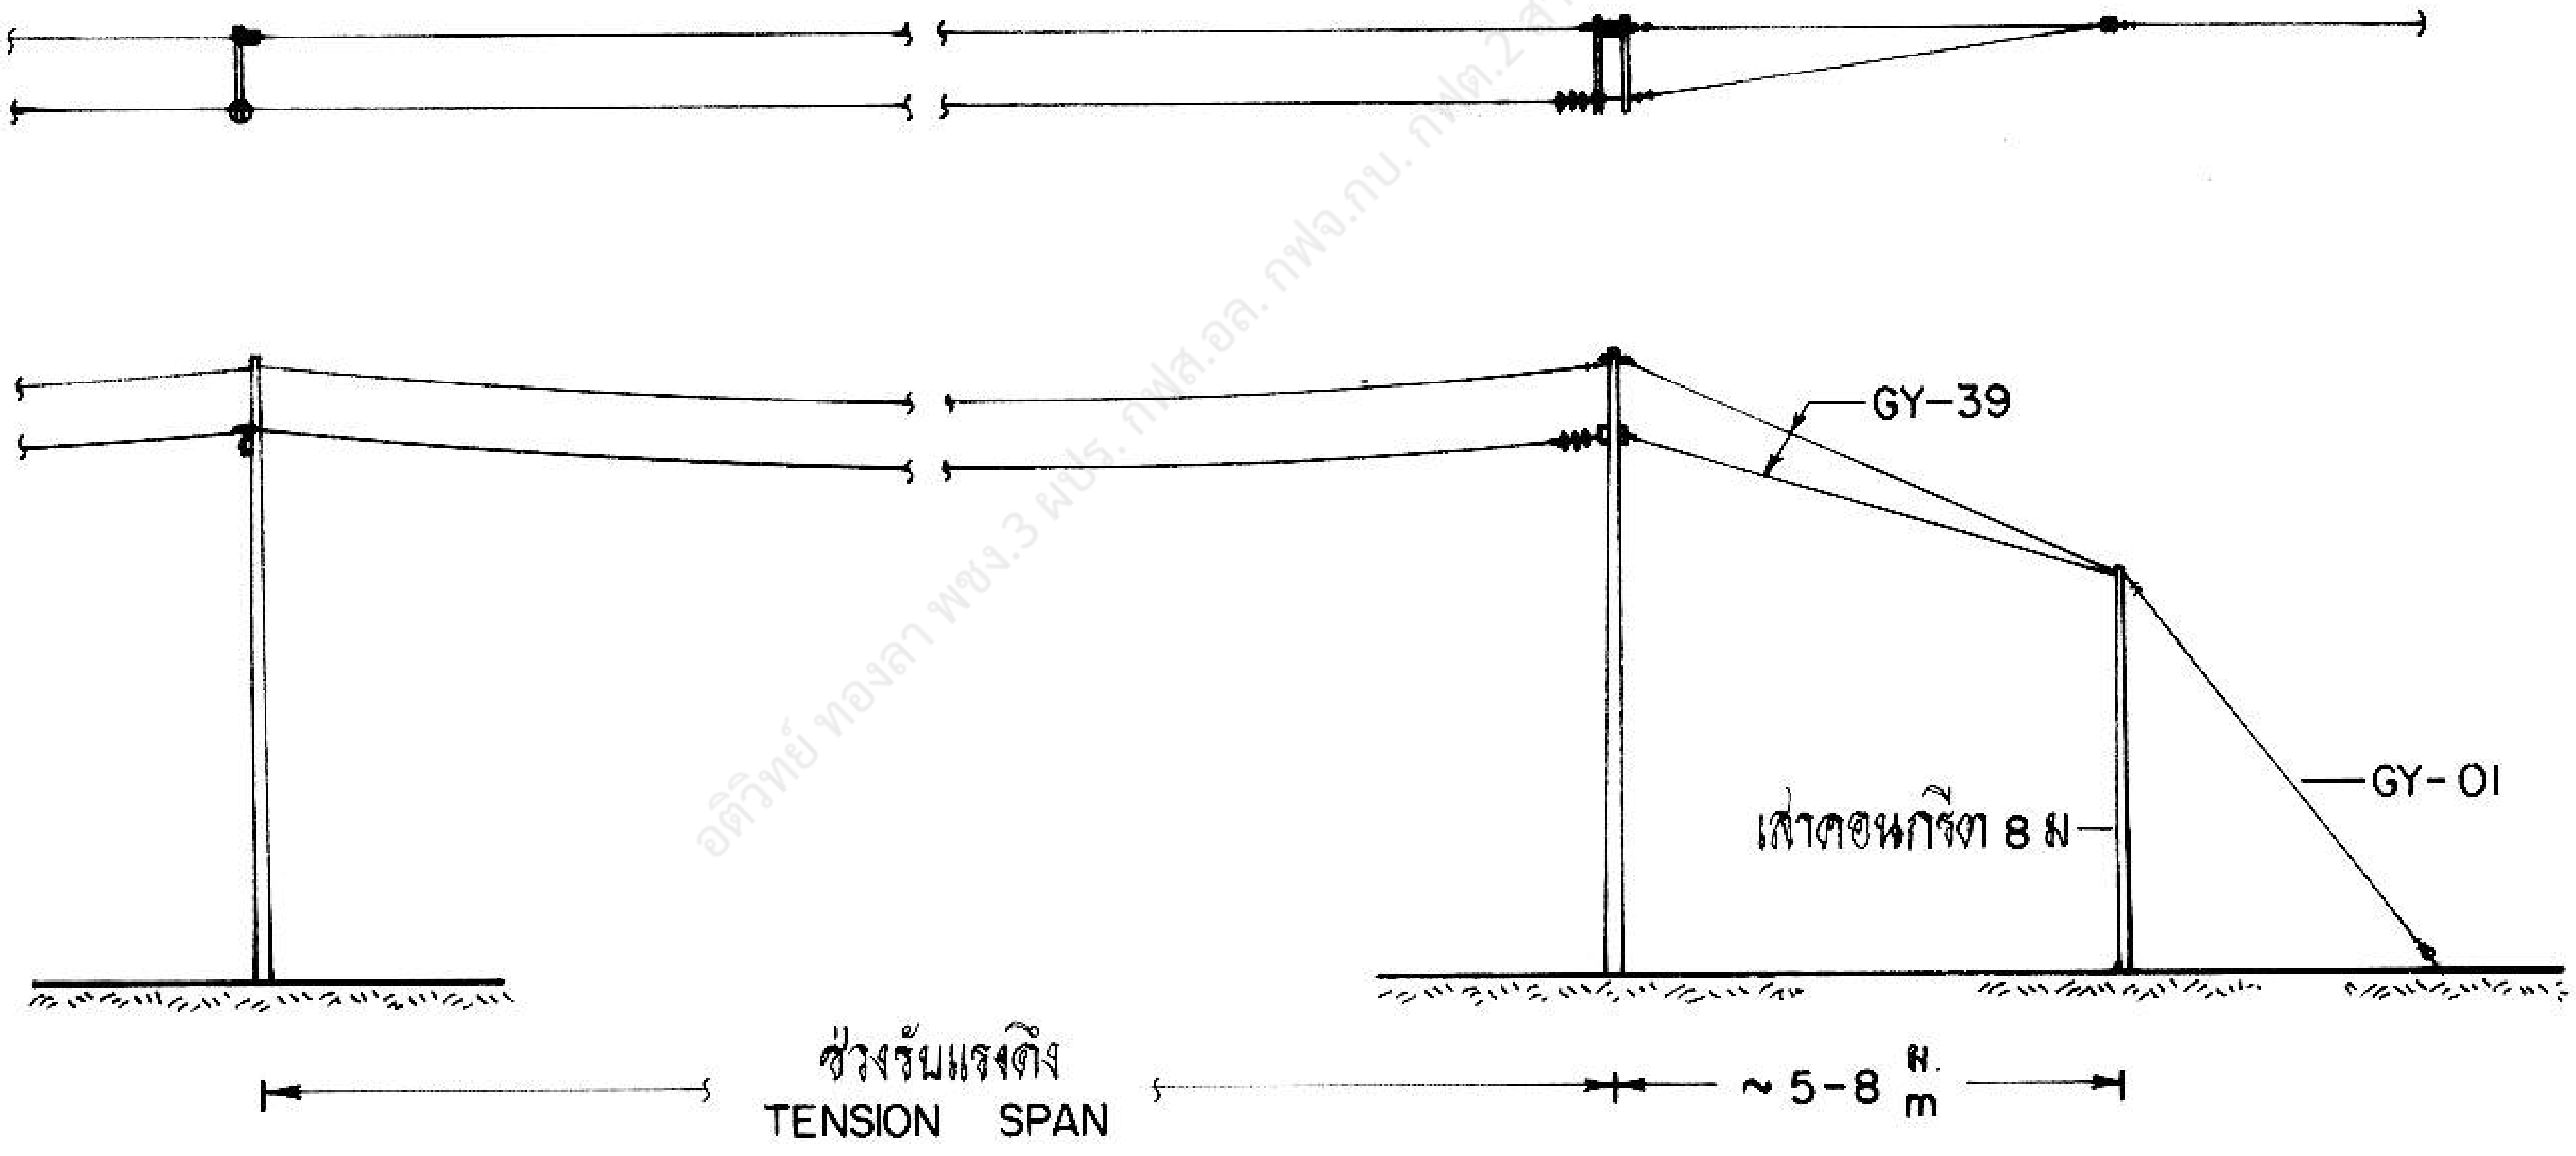

อดิวิทย์ ทองลา พชง.3 ฝปร. กฟส.อล. กฟจ.กบ. กฟต.2 สายงาน (ต) ผวก. @PEA

กองวิศวกรรมไฟฟ้าและเครื่องกล
ฝ่ายวิศวกรรม

ผู้เขียน
ผู้สำรวจ
วิศวกร
หัวหน้าแผนก
ผู้อำนวยการกอง
ผู้อำนวยการฝ่าย

รองผู้ว่าการฝ่ายเทคนิค

การไฟฟ้าส่วนภูมิภาค

ผู้ว่าการ

2 ส.ค. 2531

การประกอบคอนแขนท้าวแขน กับเสาคอนกรีต 12 ม.
(กรณีใช้คอนคอนกรีต)
ระบบ 1 เฟส 19 kV

ALLEY ARM ASSEMBLY ON 12 m CONCRETE POLE
(CONCRETE CROSSARM)
1-PHASE, 19 kV SYSTEM

ใช้แทนแบบ
ถูกแทนโดยแบบ
เขียนเสร็จวันที่ 16 พ.ค. 31
แก้แบบวันที่
มิติเป็น มม.
มาตราส่วน 1 : 25

แบบเลขที่ SA1-015/31045
แผ่นที่ 2 ของจำนวน 4 แผ่น

การประกอบเลขที่
ASSEMBLY NO. **3309**

บัญชีวัสดุ
BILL OF MATERIAL

ลำดับที่ ITEM	รายละเอียด DESCRIPTION	จำนวน REQ'D			วัสดุเลขที่ MAT. NO.
		I	II	III	
1	คอน คอร. ขนาด 100 X 100 X 1,500 มม. CROSSARM, PRESTRESSED CONCRETE 100 X 100 X 1,500 mm	1	2	2	00110000
2	เหล็กประกับคอน 30 X 6 X 760 มม. BRACE, FLAT, FOR CROSSARM, 30 X 6 X 760 mm	2	2	2	01200001
3	สลักเกลียว M 16 X 130 มม. BOLT, MACHINE M 16 X 130 mm	–	2	2	01110200
4	สลักเกลียว M 16 X 170 มม. BOLT, MACHINE M 16 X 170 mm	1	–	–	01110201
5	สลักเกลียว M 16 X 200 มม. BOLT, MACHINE M 16 X 200 mm	1	1	1	01110202
6	สลักเกลียว M 16 X 300 มม. BOLT, MACHINE M 16 X 300 mm	1	–	–	01110204
7	สลักเกลียว M 16 X 450 มม. BOLT, MACHINE M 16 X 450 mm	–	1	1	01110207
8	สลักเกลียวตลอด M 16 X 450 มม. BOLT, DOUBLE ARMING, M 16 X 450 mm	–	1	–	01120001
9	สลักเกลียวห่วงกลม M 16 X 450 มม. BOLT, DOUBLE ARMING, ROUND EYE, M 16 X 450 mm	–	–	1	01130001
10	สลักห่วงกลม M 16 X 200 มม. BOLT, ROUND EYE, M 16 X 200 mm	–	–	1	01140001
11	แหวนสี่เหลี่ยมแบน 52 X 52 X 4.5 มม. รู Ø 18 มม. มอก. 258 WASHER, SQUARE, FLAT, 52 X 52 X 4.5 mm, HOLE Ø 18 mm, TIS 258	4	12	10	01180100
12	แหวนสี่เหลี่ยมโค้ง 60 X 60 X 5 มม. รู Ø 22 มม. WASHER, SQUARE, CURVED, 60 X 60 X 5 mm, HOLE Ø 22 mm	1	2	–	01180201
13	แหวนสปริง M 16 มอก. 259 WASHER, LOCK, M 16, TIS 259	1	1	1	01180301
14	กายทิมเบิ้ล สำหรับสายยึดโยง 50-95 ต.มม. THIMBLE, GUY, FOR STEEL WIRE 50-95 mm^2	–	–	1	01210302
15	ยูแคล้มป์ สลัก 1 ตัว M8 (ไวร์ โร้ป คลิ๊ฟ) CLAMP, SINGLE U-BOLT, M 8 (WIRE ROPE CLIP)	3	1	2	01230000
16	ลวดเหล็กกลมเส้นผ่าศูนย์กลาง 4 มม. เส้นเดียว มอก. 71 น.น. ประมาณ 0.1 กก./ม. WIRE, STEEL, SOLID, DIAMETER 4 mm TIS 71 WEIGHT APPROX. 0.1 kg / m	1.3 ม. m	1.5 ม. m	–	01100000
17	ลวดเหล็กตีเกลียว 25 ต.มม. มอก. 404 WIRE, STEEL STRANDED, 25 mm^2, TIS 404	1.5 ม. m	–	–	01100002
18	สเตรนแคล้มป์สำหรับสายอะลูมิเนียม 35-95 ต.มม. อะลูมิเนียมแกนเหล็ก 35-50 ต.มม. CLAMP, STRAIN FOR Al 35-95 mm^2, ACSR. 35-50 mm^2	–	–	1	03110000 03110001
19	กราวด์วายแคล้มป์ สำหรับเสาคอนกรีต GROUND WIRE SUPPORT AND CLAMP, FOR CONCRETE POLE	1	1	–	01230201
20	ลูกถ้วยก้านตรง 33 kV มอก. 279 แบบ ค (แบบ 56-3) พร้อมก้าน INSULATOR, PIN TYPE, 33 kV, TIS 279 TYPE C (CLASS 56-3), COMP. WITH PIN	1	2	–	03000002 03100001

กองวิศวกรรมไฟฟ้าและเครื่องกล
ฝ่ายวิศวกรรม

ผู้เขียน
ผู้สำรวจ
วิศวกร
หัวหน้าแผนก
ผู้อำนวยการกอง (แทน)
ผู้อำนวยการฝ่าย

รองผู้ว่าการฝ่ายเทคนิค

การไฟฟ้าส่วนภูมิภาค

ผู้ว่าการ

การประกอบคอนแบบท้าวแขน กับเสาคอนกรีต 12 ม.
(กรณีใช้คอนคอนกรีต)
ระบบ 1 เฟส 19 kV

ALLEY ARM ASSEMBLY ON 12 m CONCRETE POLE
(CONCRETE CROSSARM)
1-PHASE, 19 kV SYSTEM

ใช้แทนแบบ
ถูกแทนโดยแบบ
เขียนเสร็จวันที่ 16 พ.ค. 31
แก้แบบวันที่
มิติเป็น
มาตราส่วน

แบบเลขที่ SAI-015/31045

แผ่นที่ 3 ของจำนวน 4 แผ่น

การประกอบเลขที่ ASSEMBLY NO.	3309

บัญชีวัสดุ
BILL OF MATERIAL

ลำดับที่ ITEM	รายละเอียด DESCRIPTION	จำนวน REQ'D I	 II	 III	วัสดุเลขที่ MAT. NO.
21	ลูกถ้วยแขวน มอก. 354 แบบ ง (แบบ 52-4) INSULATOR, SUSPENSION TYPE, TIS 354 TYPE D (CLASS 52-4)	–	–	3	03020002
22	ลวดอะลูมิเนียมแบน 1X10 มม. ความยาวตามต้องการ ARMOUR TAPE, Al 1X10 mm, LENGTH AS REQUIRED			–	02200000
23	ลวดอะลูมิเนียมกลม Ø 4 มม. ความยาวตามต้องการ TIE WIRE, Al Ø 4 mm, LENGTH AS REQUIRED			–	02200002
24	การประกอบสายยึดโยง GY-32 GUY ASSEMBLY GY-32	–	1	–	
25	การประกอบสายยึดโยง GY-39 และ GY-01 GUY ASSEMBLY GY-39 AND GY-01	–	–	1	

	แบบอ้างอิง REFERENCE DRAWING	แบบเลขที่ DWG. NO.	การประกอบเลขที่ ASSEMBLY NO.
1	ข้อแนะนำในการก่อสร้างระบบจำหน่าย 1 เฟส 19 kV CONSTRUCTION SUGGESTION OF 1-PHASE 19 kV SYSTEM	S02-015/20016	3305
2	รายละเอียดการประกอบสายยึดโยง ชุด GY-32 DETAIL OF GUY ASSEMBLY GY-32	SA1-015/20040	8453
3	รายละเอียดการประกอบสายยึดโยง ชุด GY-39 DETAIL OF GUY ASSEMBLY GY-39	SA1-015/21071	8455
4	รายละเอียดการประกอบสายยึดโยง ชุด GY-01 DETAIL OF GUY ASSEMBLY GY-01	SA1-015/20037	8451
5	การประกอบสายลงดินด้วยวิธียึดลวดเหล็ก GROUND LEAD ASSEMBLY STEEL WIRE FITTING	S02-015/19166	9703

กองวิศวกรรมไฟฟ้าและเครื่องกล
ฝ่ายวิศวกรรม
ผู้เขียน
ผู้สำรวจ
วิศวกร
หัวหน้าแผนก
ผู้อำนวยการกอง
ผู้อำนวยการฝ่าย
รองผู้ว่าการฝ่ายเทคนิค

การไฟฟ้าส่วนภูมิภาค

ผู้ว่าการ
2 มิ.ย. 2531

การประกอบคอนแบบท้าวแขน กับเสาคอนกรีต 12 ม.
(กรณีใช้คอนคอนกรีต)
ระบบ 1 เฟส 19 kV

ALLEY ARM ASSEMBLY ON 12 m CONCRETE POLE
(CONCRETE CROSSARM)
1-PHASE, 19 kV SYSTEM

ใช้แทนแบบ
ถูกแทนโดยแบบ
เขียนเสร็จวันที่ 16 พ.ค. 31
แก้แบบวันที่
มิติเป็น
มาตราส่วน
แบบเลขที่ SA1-015/31045
แผ่นที่ 4 ของจำนวน 4 แผ่น

2531