การประกอบเลขที่
ASSEMBLY NO. 5208

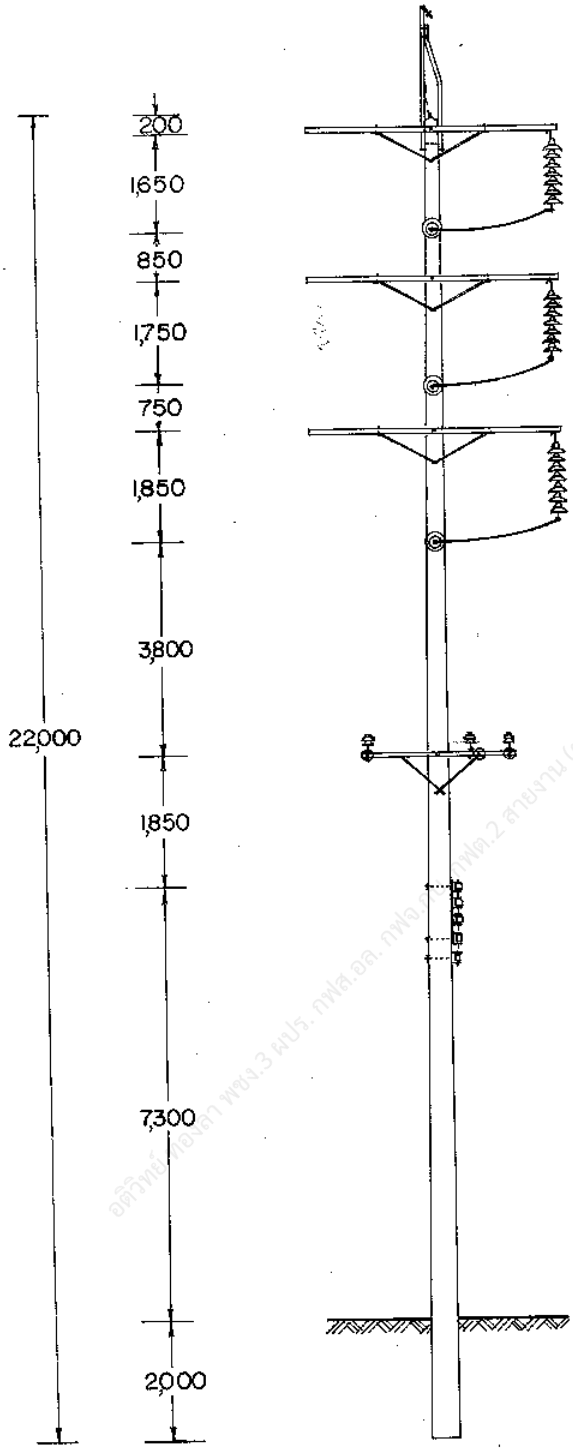

แบบ
TYPE SS-DD-1

อดิวิทย์ ทองลา พชง.3 ผปร. กฟส.อล. กฟจ.กบ กฟต.2 สายงาน (ต) ผวก. @PEA

JAPANESE EXPERT TO PEA

กองวิศวกรรม
ผู้เขียน
สถาปนิก
วิศวกร
หัวหน้าแผนก
ผู้อำนวยการกอง
รองผู้ว่าการฝ่ายเทคนิค

การไฟฟ้าส่วนภูมิภาค
ผู้ว่าการ 26 มิ.ย. 19

แบบโครงสร้างเสาส่งระบบ 115 kV
วงจรเดี่ยว
แบบเสาสำหรับเข้าปลายสายสองข้าง

115 kV LINE STRUCTURE CONSTRUCTION
SINGLE CIRCUIT
DOUBLE DEAD END STRUCTURE

ใช้แทนแบบ
ถูกแทนโดยแบบ
เขียนเสร็จวันที่ 18 มี.ค. 19
แก้แบบวันที่ 24 มี.ค. 23
มิติเป็น มม.
มาตราส่วน 1:125
แบบเลขที่ S02-015/19025
แผ่นที่ 1 ของจำนวน 3 แผ่น

การประกอบเลขที่
ASSEMBLY NO. 5208

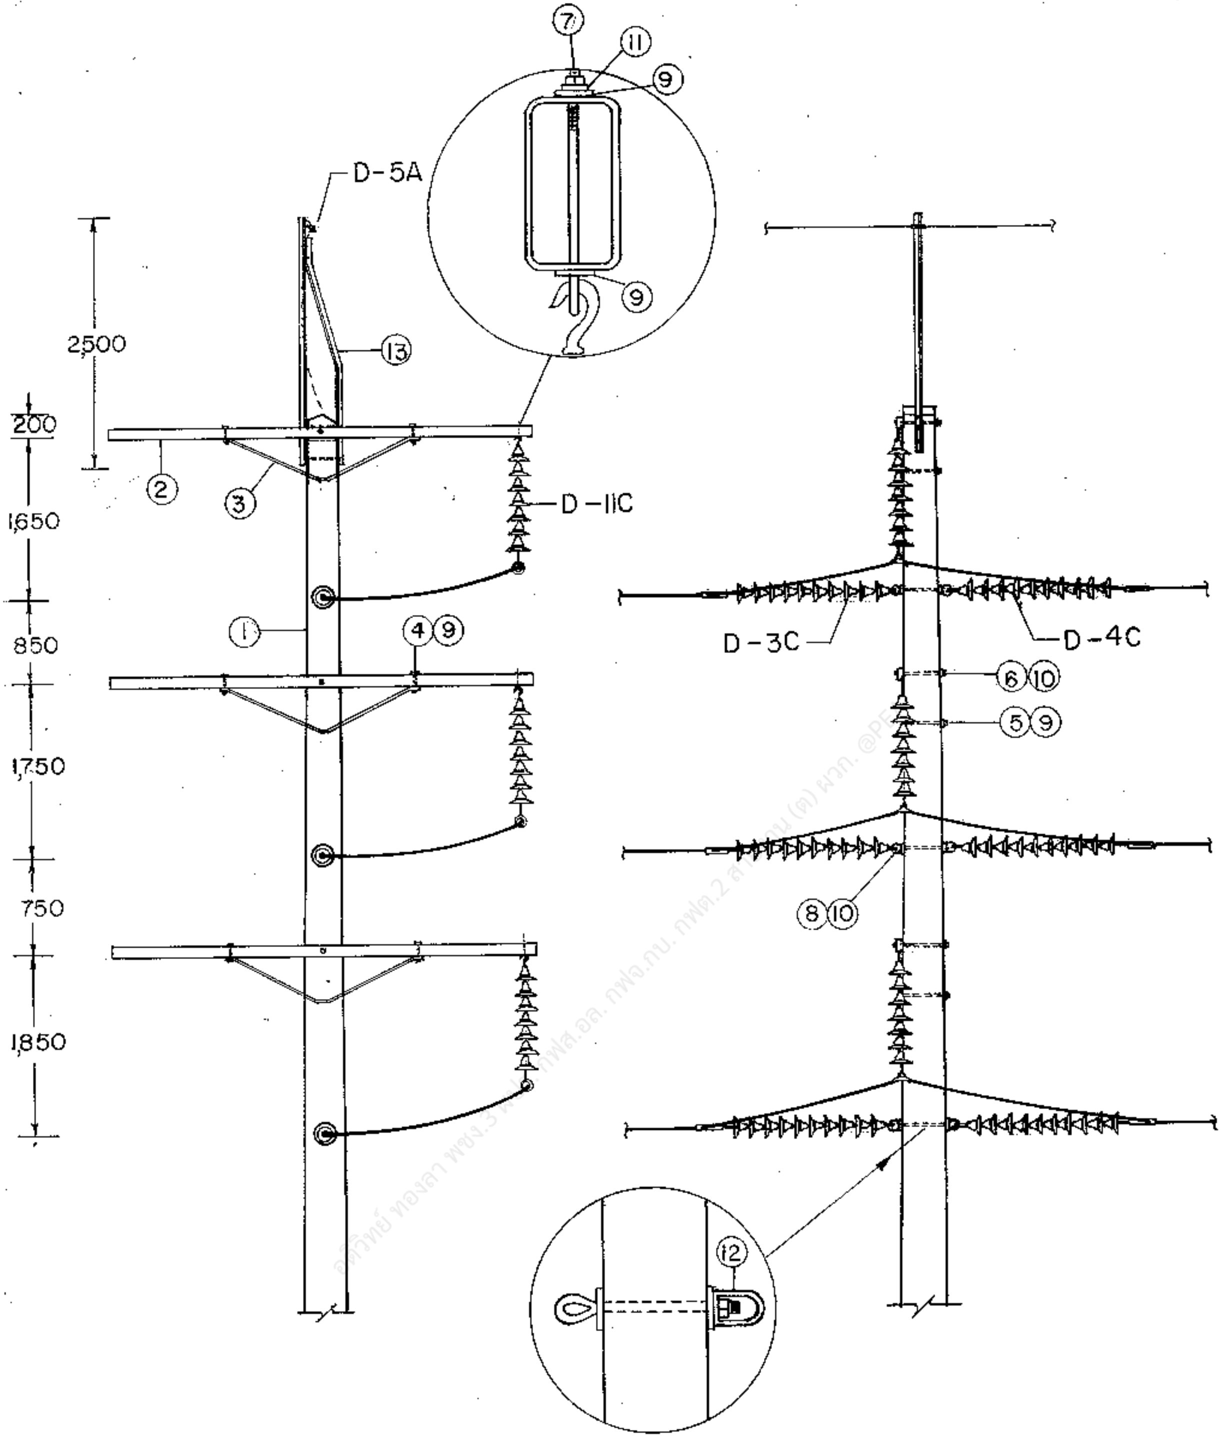

อติวิทย์ ทองลา พชง.3 [illegible] กฟส.อล. กฟจ.กบ. กฟต.2 สาย[illegible] (ต) ผวก. @PEA

JAPANESE EXPERT TO PEA. T. Yamada

กองวิศวกรรม	การไฟฟ้าส่วนภูมิภาค	ใช้แทนแบบ.......... ถูกแทนโดยแบบ.......... เขียนเสร็จวันที่ 18 มี.ค. 19 แก้แบบวันที่ 24 มี.ค. 23 มิติเป็น ม.ม. มาตราส่วน 1 : 75 แบบเลขที่ S02-015/19025 แผ่นที่ 2 ของจำนวน 3 แผ่น
ผู้เขียน.......... สถาปนิก.......... วิศวกร.......... หัวหน้าแผนก.......... ผู้อำนวยการกอง..........	ผู้ว่าการ.......... 26 มี.ค. 19 แผนโครงสร้างเสาส่งระบบ 115 kV วงจรเดี่ยว แบบเสาสำหรับเข้าปลายสายสองข้าง	
รองผู้ว่าการฝ่ายเทคนิค..........	115 kV LINE STRUCTURE CONSTRUCTION SINGLE CIRCUIT DOUBLE DEAD END STRUCTURE	

การประกอบเลขที่
ASSEMBLY NO. **5208**

บัญชีวัสดุ
BILL OF MATERIAL

ลำดับที่ ITEM	รายละเอียด DESCRIPTION	จำนวน REQ'D	วัสดุเลขที่ MAT. NO.
1	เสาคอนกรีต 22 ม. POLE, CONCRETE 22 m. LONG	1	00010011 (0041)
2	คอนสายแบบเหล็กขนาด 100x50x3.2 มม ยาว 4.20 ม. CROSSARM, STEEL, 100x50x3.2 mm 4.20 m LONG	3	00120001 (0116)
3	เหล็กฉากรับคอนสายขนาด 50x50x6 มม. ช่วงกว้าง 1800 มม. ดรอพ 450 มม. BRACE, ANGLE STEEL 50 x 50 x 6 mm., 1800 mm. WIDE 450 mm. DROP	3	00120007 (1119)
4	สลักเกลียว M 16 x 130 มม. BOLT, MACHINE M 16 x 130 mm.	6	01110200 (0220) *
5	สลักเกลียว M 16 x 350 มม. BOLT, MACHINE M 16 x 350 mm.	6	01110205 (0225)
6	สลักเกลียว M 20 x 400 มม. BOLT, MACHINE M 20 x 400 mm.	3	01110301 (0233)
7	สลักห่วงโอแวล M 16 x 150 มม. BOLT, OVAL EYE, M 16 x 150 mm.	3	01150000 (0257)
8	สลักห่วงโอแวล M 20 x 350 มม. BOLT, OVAL EYE M 20 x 350 mm.	3	01150100 (0260)
9	แหวนสี่เหลี่ยมแบน 52X52X4.5 มม. รู Ø18 มม. มอก. 258 WASHER, SQUARE, FLAT 52X52X4.5 mm HOLE Ø 18 mm TIS. 258	15	01180100 (0355)
10	แหวนสี่เหลี่ยมโค้ง 62X62X6 มม. รู Ø22 มม. WASHER, SQUARE, FLAT, 62X62X6 mm HOLE Ø 22 mm	9	01180101 (0356)
11	แหวนสปริง M 16 มอก. 259 WASHER, LOCK, M 16, TIS 259	3	01180301 (0365)
12	อายเล็ท สำหรับสลักเกลียว M 20 EYELET FOR BOLT, M 20	3	01180002 (0346)
13	เหล็กฉากรับสายล่อฟ้า ทางโค้ง OVERHEAD GROUND WIRE CORNER BAYONET	1	01010005 (0136)
	รายละเอียด DETAIL		
D-3C	การประกอบลูกถ้วยแขวน SUSPENSION INSULATOR ASSEMBLY	3	
D-4C	การประกอบลูกถ้วยแขวน SUSPENSION INSULATOR ASSEMBLY	3	
D-11C	การประกอบลูกถ้วยแขวน SUSPENSION INSULATOR ASSEMBLY	3	
D-5A	การต่อสายล่อฟ้า OVERHEAD GROUND WIRE CONNECTION	1	
D-10A	ฐานรากเสา POLE FOUNDATION	1	

JAPANESE EXPERT TO PEA.

กองวิศวกรรม

การไฟฟ้าส่วนภูมิภาค

ผู้เขียน.....
สถาปนิก.....
วิศวกร.....
หัวหน้าแผนก.....
ผู้อำนวยการกอง.....
รองผู้ว่าการฝ่ายเทคนิค
.....

ผู้ว่าการ..... 26 มี.ค. 19

แบบโครงสร้างเสาส่งระบบ 115 kV
วงจรเดี่ยว
แบบเสาสำหรับเข้าปลายสายสองข้าง

115 kV LINE STRUCTURE CONSTRUCTION
SINGLE CIRCUIT
DOUBLE DEAD END STRUCTURE

ใช้แทนแบบ.....
ถูกแทนโดยแบบ.....
เขียนเสร็จวันที่ 18 มี.ค. 19
แก้แบบวันที่ 24 มี.ค. 23
มิติเป็น.....
มาตราส่วน.....
แบบเลขที่ S02-015/19025
แผ่นที่ 3 ของจำนวน 3 แผ่น