

การประกอบเลขที่ ASSEMBLY NO.	5 7 0 3

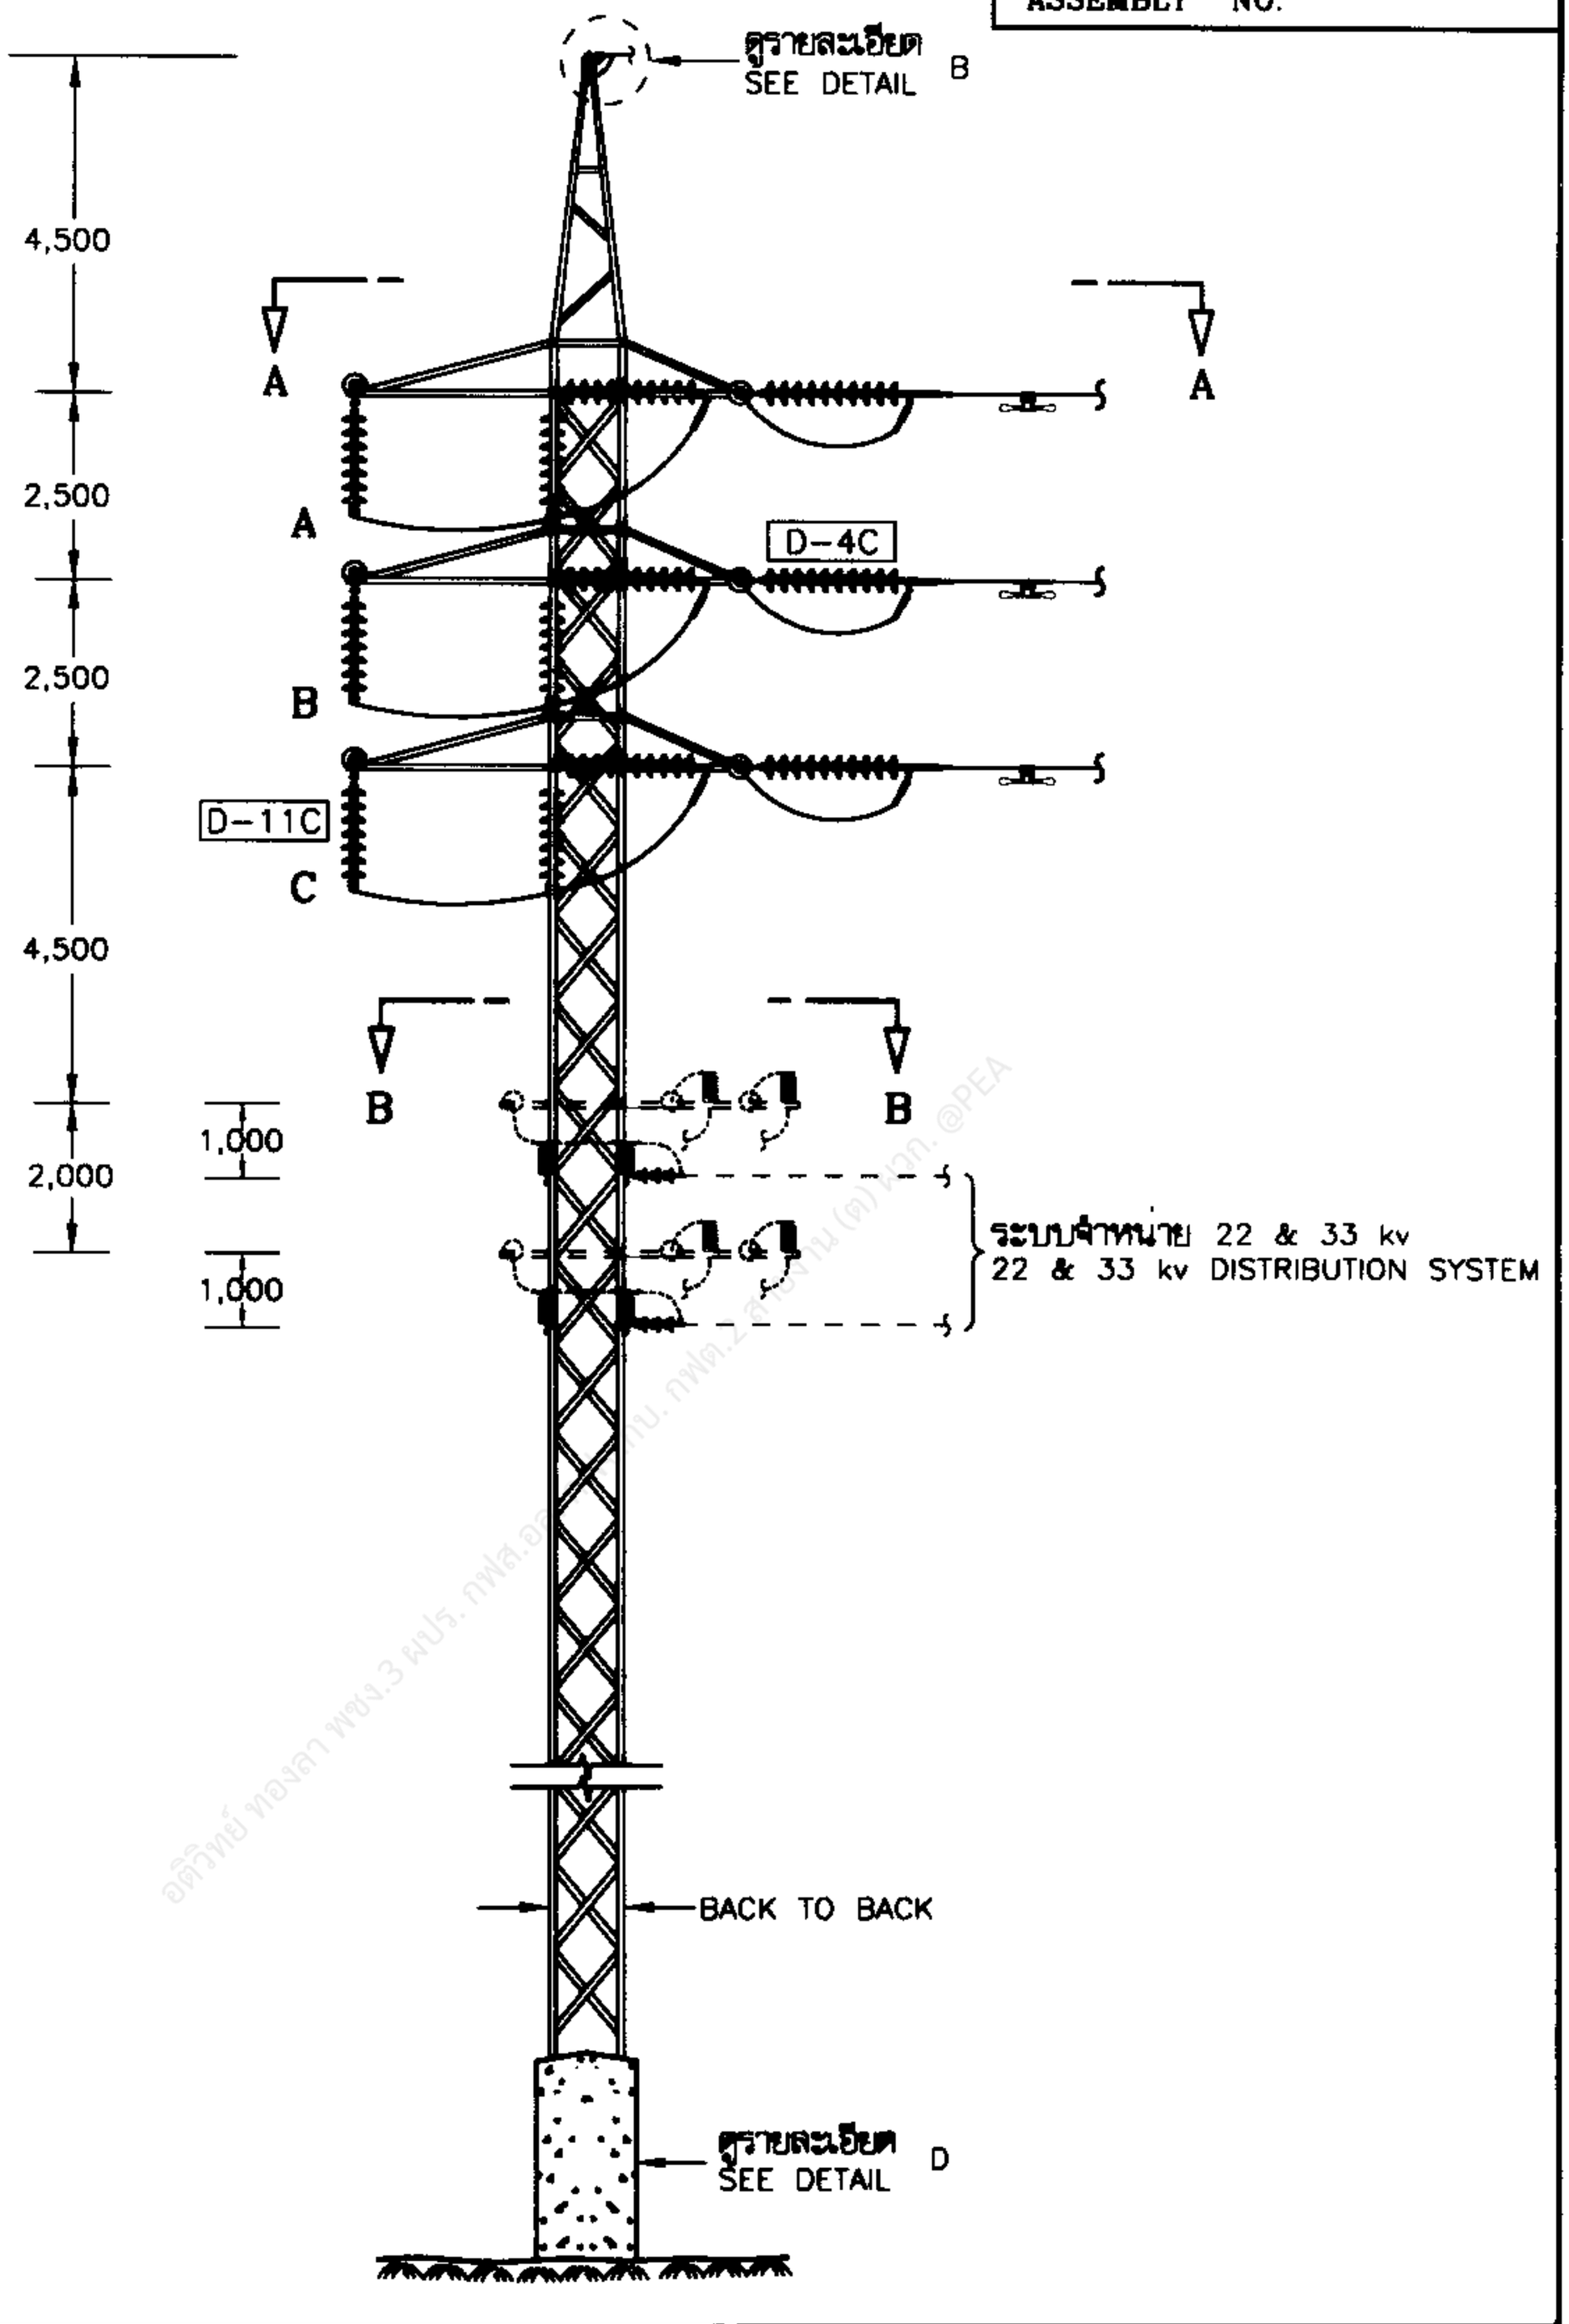


กองมาตรฐานระบบไฟฟ้า ฝ่ายมาตรฐานและความปลอดภัย	การไฟฟ้าส่วนภูมิภาค	ใช้แทนแบบ..... ถูกแทนโดยแบบ.....
ผู้เขียน สมชาย..... ผู้สำรวจ..... วิศวกร..... หัวหน้าแผนก..... ผู้อำนวยการกอง..... ผู้อำนวยการฝ่าย.....	ผู้ว่าการ.....	เขียนเสร็จวันที่ 25 เมษ. 45 แก้แบบวันที่..... มิติเป็น มิลลิเมตร มาตราส่วน 1 : 150
รองผู้ว่าการวางแผนและพัฒนาระบบไฟฟ้า.....	โครงเหล็กสำหรับทางโค้ง 90° 13 มิ.ย. 2545 STEEL TOWER, FOR LARGE ANGLE STRUCTURE 90°	แบบเลขที่ SA1-015/45007 แผ่นที่ 1 ของจำนวน 5 แผ่น

13 มิ.ย. 2545


การประกอบเลขที่ ASSEMBLY NO. 5703

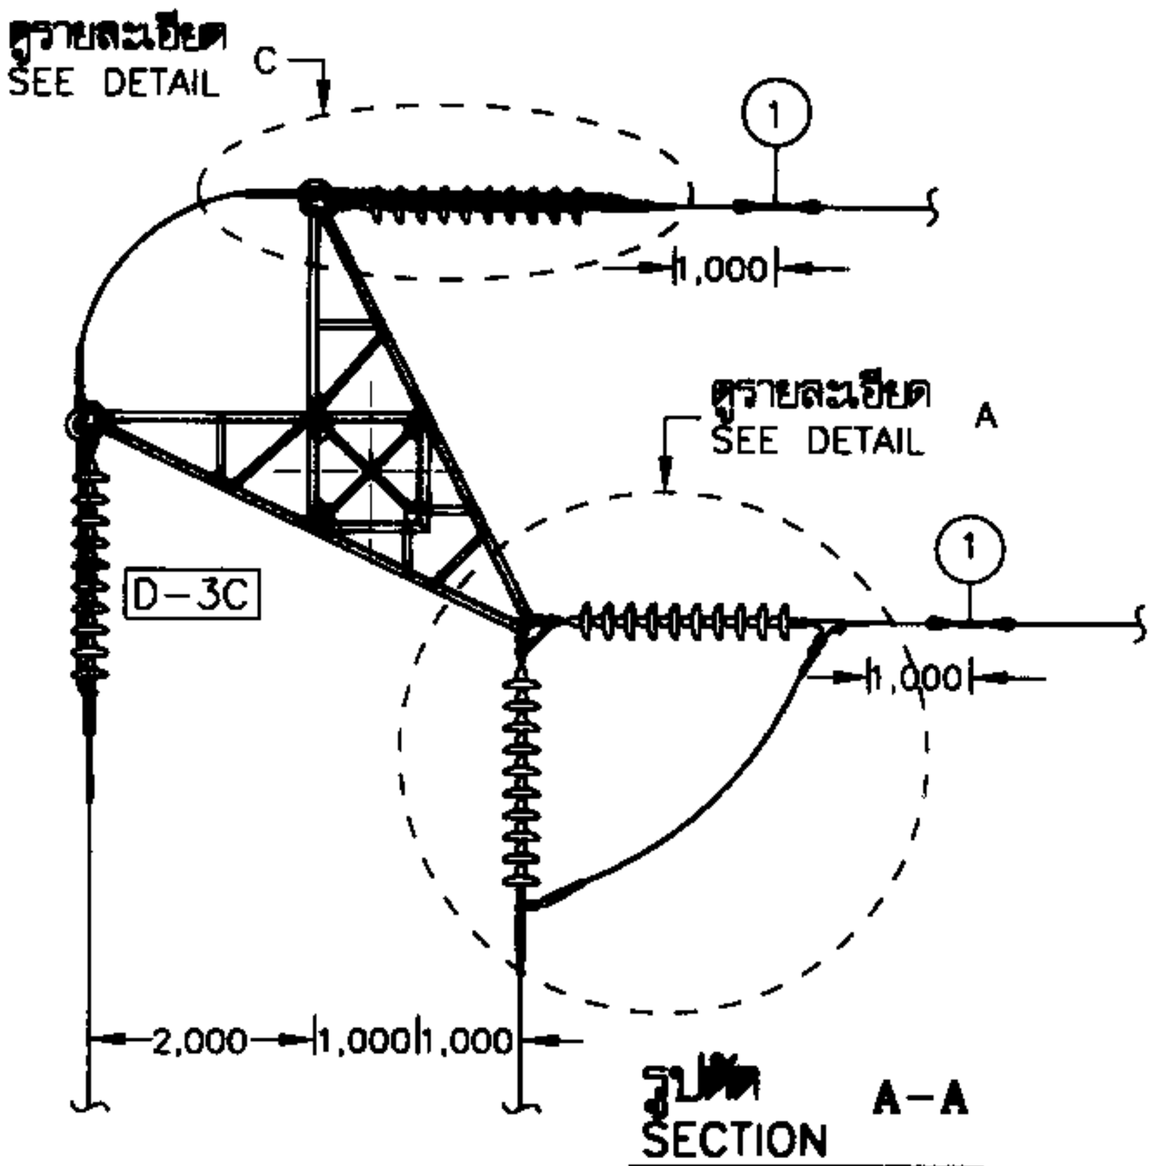

รูปตัด SECTION A-A

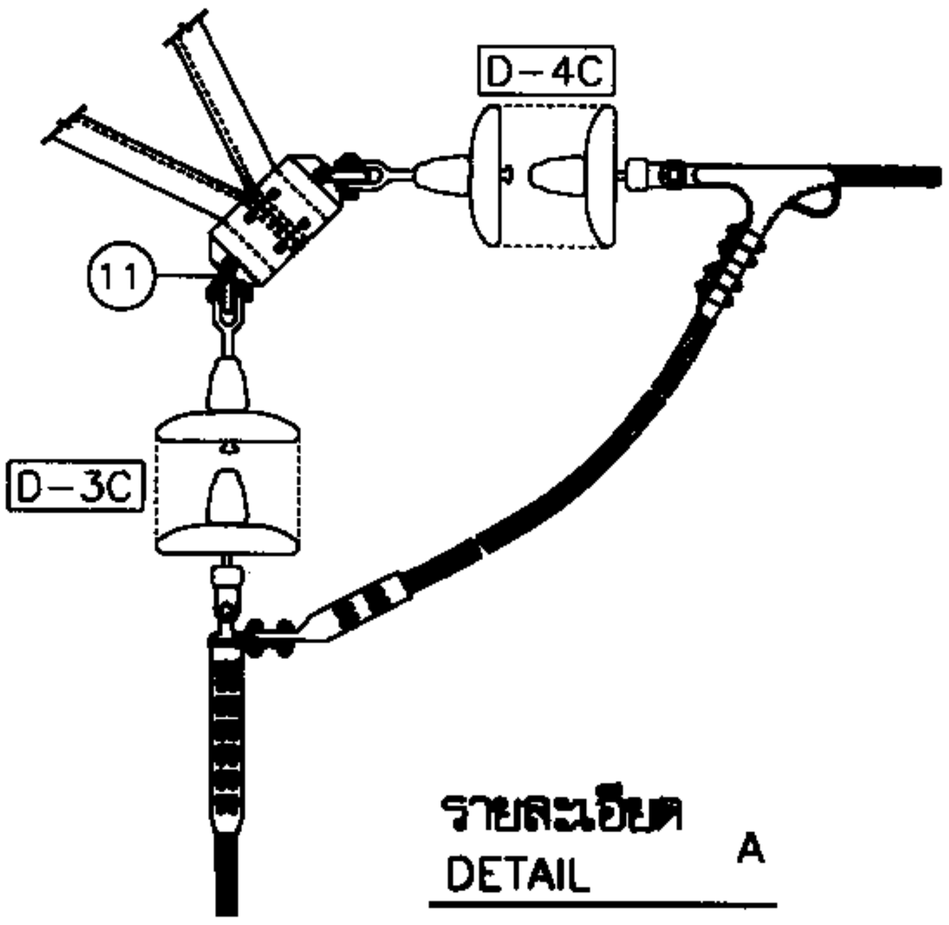


รายละเอียด DETAIL A

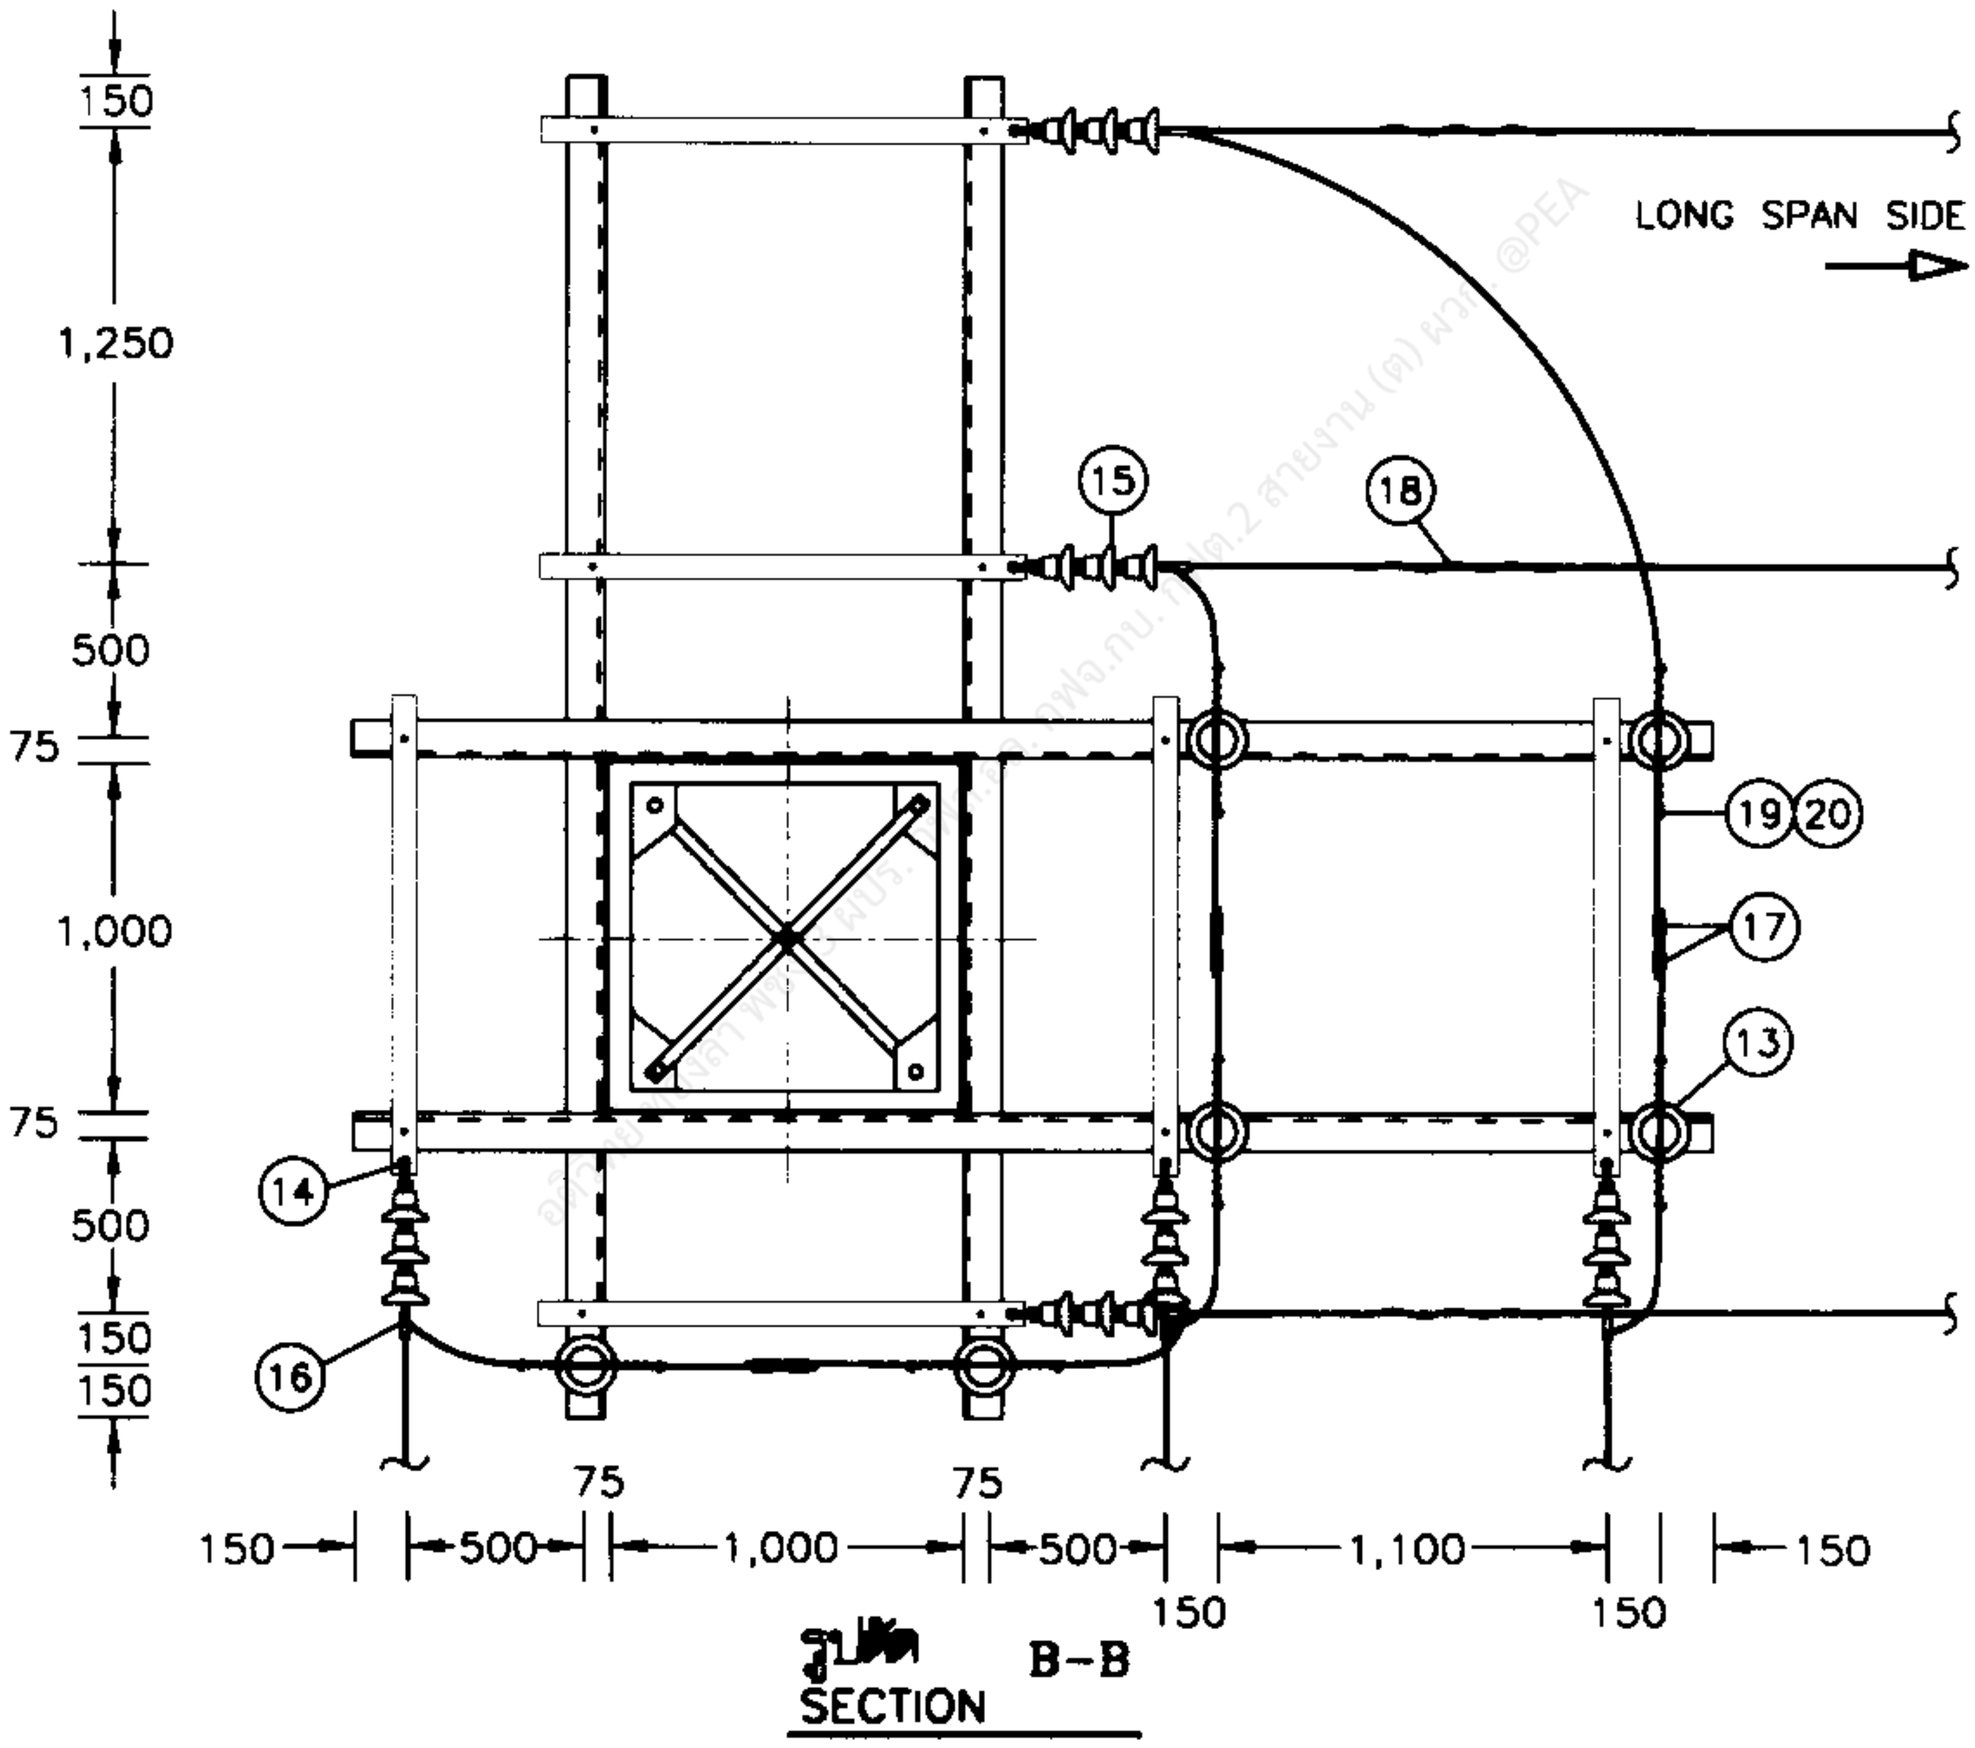


รูปตัด SECTION B-B

กองมาตรฐานระบบไฟฟ้า ฝ่ายมาตรฐานและความปลอดภัย	การไฟฟ้าส่วนภูมิภาค	ใช้แทนแบบ ..... ถูกแทนโดยแบบ .....
ผู้เขียน สมชาย ..... ผู้สำรวจ ..... วิศวกร ..... หัวหน้าแผนก ..... ผู้อำนวยการกอง ..... ผู้อำนวยการฝ่าย	ผู้ว่าการ ..... โครงเหล็กสำหรับทางโค้ง 90° 13 ก.ค. 2545	เขียนเสร็จวันที่ 25 เม.ย. 45 แก้แบบวันที่ ..... มิติเป็น มิลลิเมตร มาตราส่วน —
รองผู้ว่าการวางแผนและพัฒนาระบบไฟฟ้า	STEEL TOWER, FOR LARGE ANGLE STRUCTURE 90°	แบบเลขที่ SA1-015/45007 แผ่นที่ 2 ของจำนวน 5 แผ่น


การประกอบเลขที่ ASSEMBLY NO. 5703

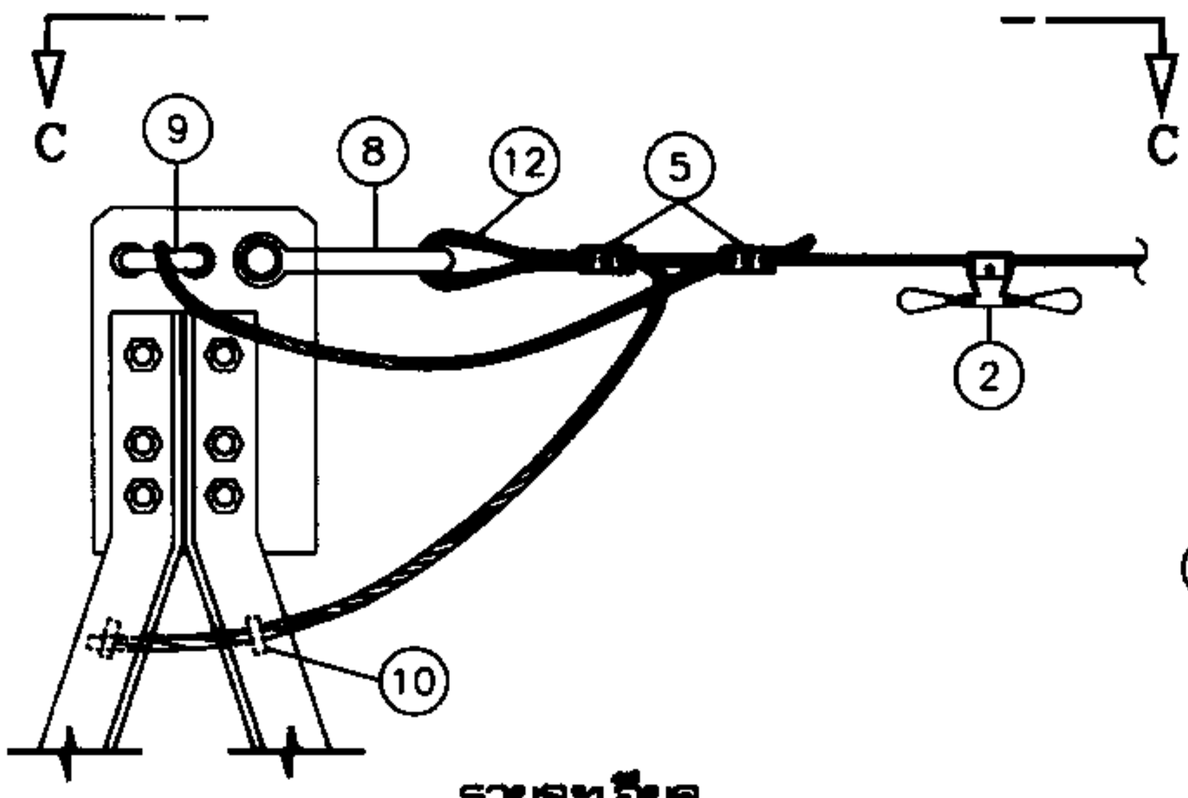


รายละเอียด B
DETAIL

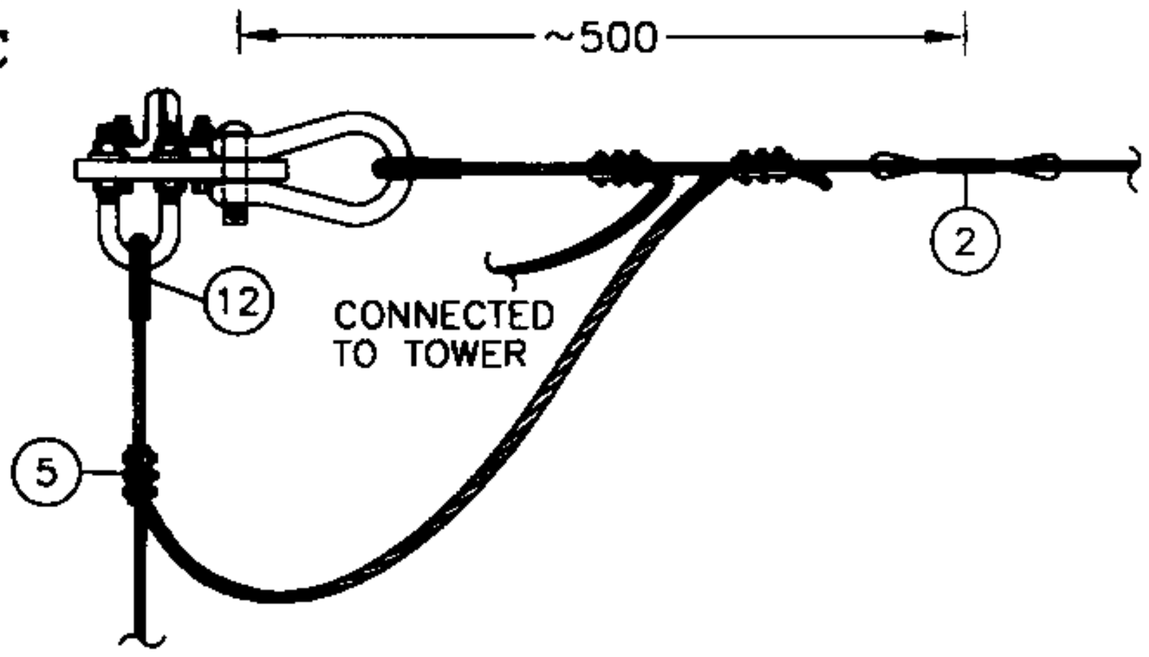


รูปตัด C–C
SECTION

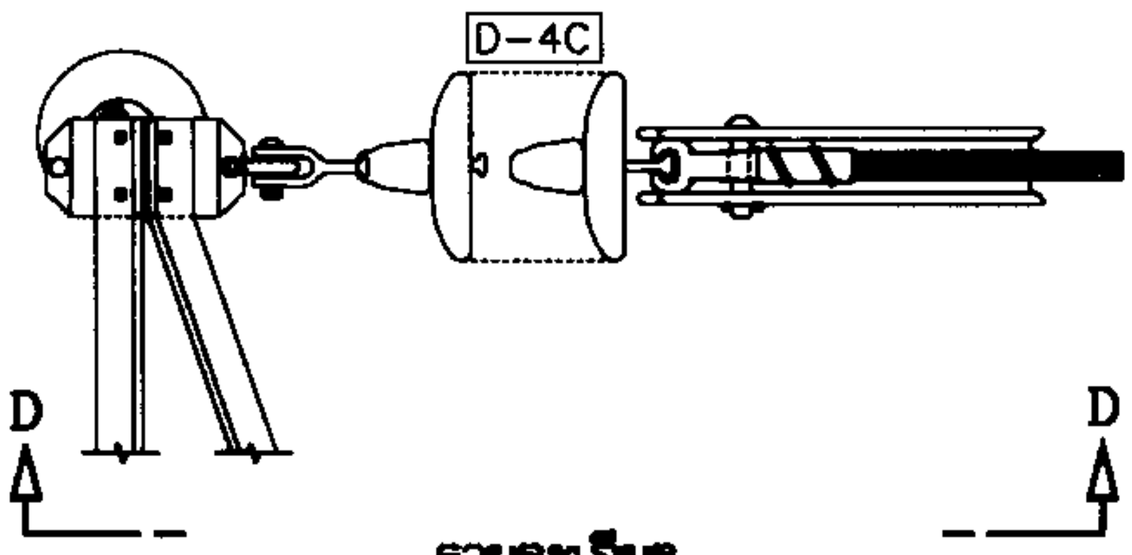


รายละเอียด C
DETAIL

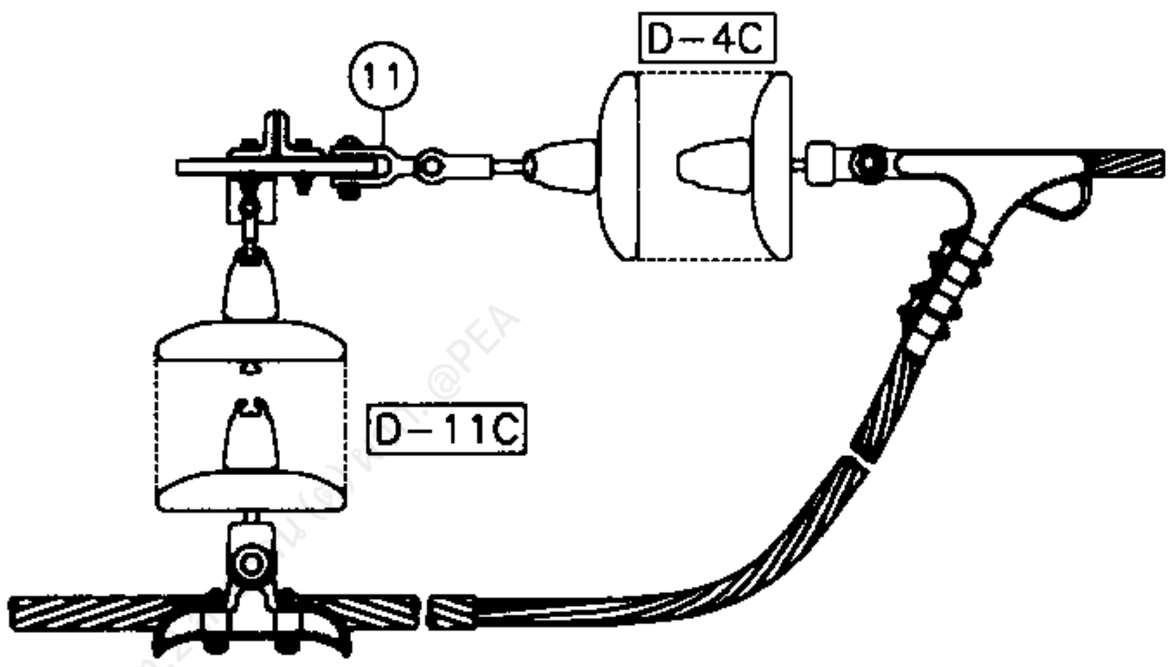

รูปตัด D–D
SECTION

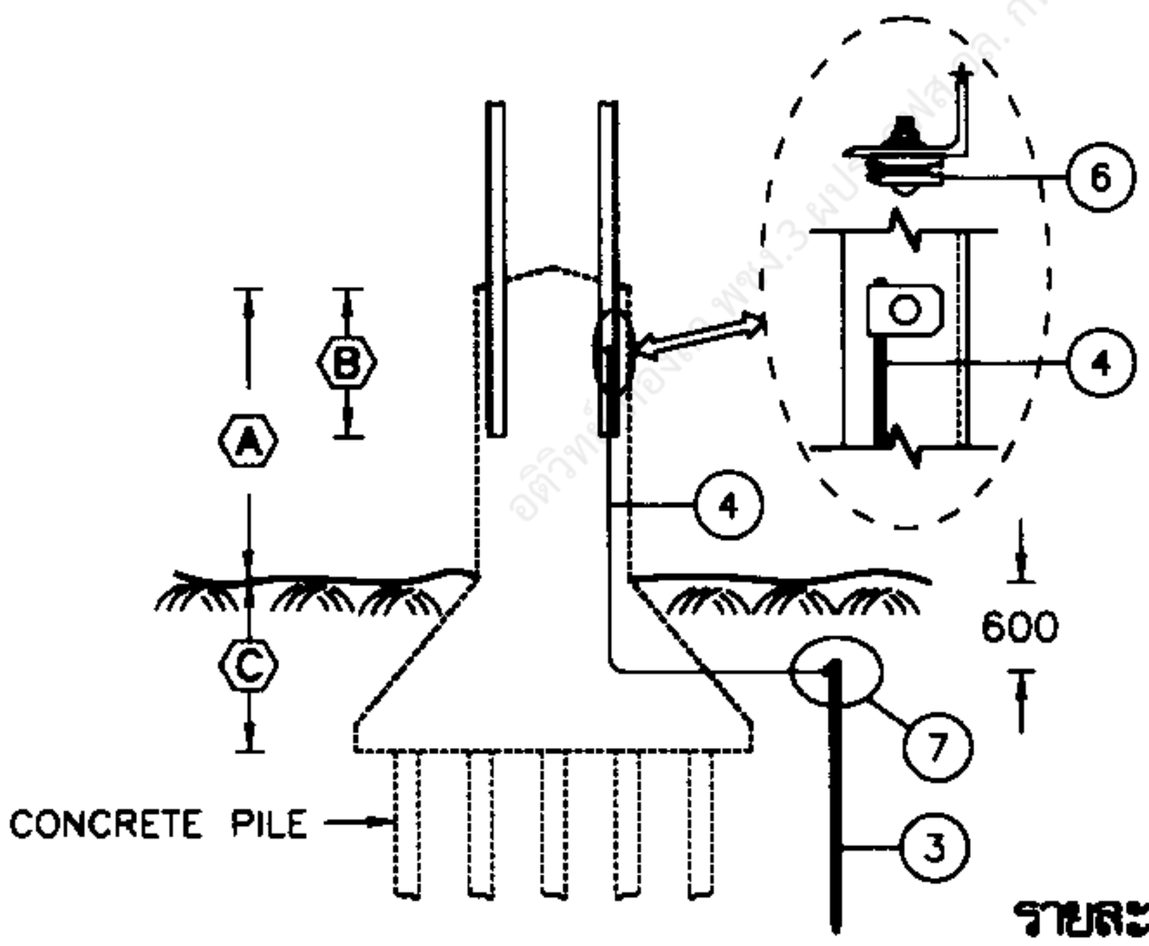

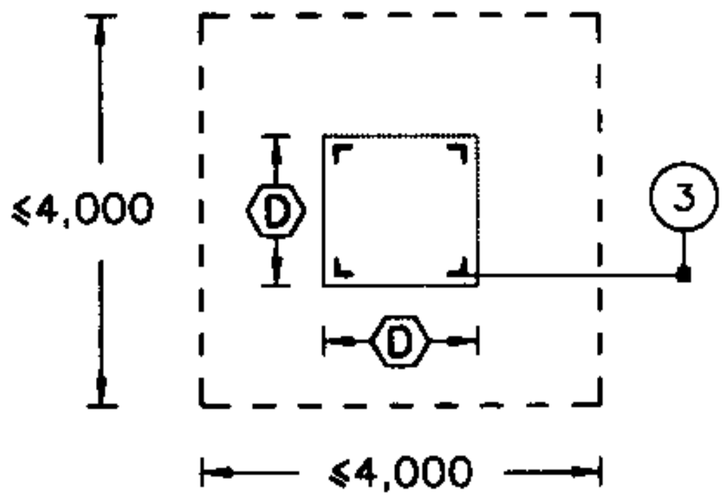

รายละเอียด D
DETAIL

กองมาตรฐานระบบไฟฟ้า ฝ่ายมาตรฐานและความปลอดภัย	การไฟฟ้าส่วนภูมิภาค	ใช้แทนแบบ ..... ถูกแทนโดยแบบ .....
ผู้เขียน สมชาย ..... ผู้สำรวจ ..... วิศวกร ..... หัวหน้าแผนก ..... ผู้อำนวยการกอง ..... ผู้อำนวยการฝ่าย	ผู้ว่าการ	เขียนเสร็จวันที่ 25 เม.ย. 45 แก้แบบวันที่ ..... มิติเป็น มิลลิเมตร มาตราส่วน —
รองผู้ว่าการวางแผนและพัฒนาระบบไฟฟ้า	13 มิ.ย. 2545 โครงเหล็กสำหรับทางโค้ง 90 STEEL TOWER, FOR LARGE ANGLE STRUCTURE 90°	แบบเลขที่ SA1–015/45007 แผ่นที่ 3 ของจำนวน 5 แผ่น

45

การประกอบเลขที่ ASSEMBLY NO. 5703

ลำดับที่ ITEM	รายละเอียด DESCRIPTION	จำนวน REQ'D	วัสดุเลขที่ MAT. NO.
	บัญชีวัสดุ สำหรับระบบ 115 kV BILL OF MATERIAL FOR 115 kV SYSTEM		
1	ไวเบรชั่นแดมเปอร์ แบบดัมเบล สำหรับสายอะลูมิเนียมแกนเหล็ก ขนาด 380/50 ตร.มม. VIBRATION DAMPER, DUMBBELL; FOR 380/50 mm^2 ACSR	6	02200107
2	ไวเบรชั่นแดมเปอร์ แบบดัมเบล สำหรับสายลวดเหล็กตีเกลียว ขนาด 50 ตร.มม. VIBRATION DAMPER, DUMBBELL; FOR 50 mm^2 STEEL STRANDED WIRE	1	02200100
3	หลักดินทำด้วยเหล็กเคลือบทองแดง ø 16 มม. ยาว 3 ม. จำนวนตามต้องการ ROD, GROUND, COPPER COVERED STEEL, 16 mm DIA., 3 m LONG; QUANTITIES AS REQUIRED		01220007
4	สายทองแดงเปลือย 95 ตร.มม. มอก. 64 ความยาวตามต้องการ CONDUCTOR, CU, BARE, 95 mm^2, TIS 64; QUANTITIES AS REQUIRED	ม. m	02000007
5	แคล้มป์สลัก 3 ตัว สำหรับลวดเหล็กตีเกลียว 50 ตร.มม. CLAMP, TRIPLE BOLT; FOR 50 mm^2 STEEL STRANDED WIRE	3	01230004
6	แคล้มป์สายดินแบบร่องเดี่ยว สำหรับสายทองแดง 95 ตร.มม. CLAMP, GROUND, SINGLE GROOVE; FOR 95 mm^2 Cu CONDUCTOR	1	01230009
7	การต่อหลักดินแบบเชื่อมด้วยความร้อน จำนวนตามต้องการ GROUNDING, THERMO WELDING; QUANTITIES AS REQUIRED		–
8	เหล็กพวงสำหรับสายยึดโยง SHACKLE ANCHOR	1	–
9	ยูโบลท์ M 16 U-BOLT, M 16	1	–
10	ยูแคล้มป์ สลักเดี่ยว M 8 CLAMP, SINGLE U- BOLT, M 8	2	01230000
11	ข้อต่อแบบ เคลวิสอาย CLEVIS-EYE	12	03140000
12	กายทิมบิลสำหรับลวดเหล็กตีเกลียว 50 ตร.มม. THIMBLE, GUY; FOR 50 mm^2 STEEL STRANDED WIRE	2	01210304
	บัญชีวัสดุ สำหรับระบบ BILL OF MATERIAL FOR 22 & 33 kV SYSTEM		
13	ลูกถ้วยไลน์โพสท์ไทพ์แบบ 57-2 หรือแบบ 57-3 มอก. 1077 INSULATOR, LINE POST TYPE, CLASS 57-2 OR 57-3, TIS 1077	12	03010001 or 03010103
14	ข้อต่อแบบ เคลวิส-อาย CLEVIS, EYE	12	03140000
15	ลูกถ้วยแขวน มอก. 354 แบบ ง (แบบ 52-4) INSULATOR, SUSPENSION TYPE, TIS 354, TYPE D (CLASS 52-4)	36	03020002
16	สเตรนแคล้มป์สำหรับสายอะลูมิเนียมแกนเหล็ก ขนาด 185/30 ตร.มม. CLAMP, STRAIN; FOR 185/30 mm^2 ACSR	12	03110004
17	พีจี คอนเนคเตอร์ 3 สลัก สำหรับสายอะลูมิเนียมแกนเหล็ก ขนาด 185/30 ตร.มม. CONNECTOR, PARALLEL GROOVE, TRIPLE BOLT; FOR 185/30 mm^2 ACSR	12	02300103
18	ไวเบรชั่น แดมเปอร์ แบบสไปแรล สำหรับสายอะลูมิเนียมแกนเหล็กขนาด 185/30 ตร.มม. VIBRATION DAMPER, SPIRAL; FOR 185/30 mm^2 ACSR	6	02200103
19	ลวดอะลูมิเนียมกลม ø 4.0 มม. ความยาวตามต้องการ TIE, WIRE, AL, ø 4.0 mm; LENGTH AS REQUIRED	ม. m	02200002
20	ลวดอะลูมิเนียมแบน 1x10 มม. ความยาวตามต้องการ TAPE, ARMOUR, AL, 1x10 mm; LENGTH AS REQUIRED	ม. m	02200000

กองมาตรฐานระบบไฟฟ้า ฝ่ายมาตรฐานและความปลอดภัย	การไฟฟ้าส่วนภูมิภาค	ใช้แทนแบบ ..... ถูกแทนโดยแบบ ..... เขียนเสร็จวันที่ 25 เมษ. 45
ผู้เขียน สมชาย ..... ผู้สำรวจ ..... วิศวกร ..... หัวหน้าแผนก ..... ผู้อำนวยการกอง ..... ผู้อำนวยการฝ่าย	ผู้ว่าการ ..... 13 มิ.ย. 2545 โครงเหล็กสำหรับทางโค้ง 90°	แก้แบบวันที่ ..... มิติเป็น — ..... มาตราส่วน —
ของผู้ว่าการวางแผนและพัฒนาระบบไฟฟ้า	STEEL TOWER, FOR LARGE ANGLE STRUCTURE 90°	แบบเลขที่ SA1-015/45007 แผ่นที่ 4 ของจำนวน 5 แผ่น

การประกอบเลขที่ ASSEMBLY NO.	5 7 0 3

รายละเอียด DESCRIPTION			
	การประกอบลูกถ้วยแขวน D-11C SUSPENSION, INSULATOR ASSEMBLY, D-11C	6	
	การประกอบลูกถ้วยแขวน D-3C SUSPENSION, INSULATOR ASSEMBLY, D-3C	6	
	การประกอบลูกถ้วยแขวน D-4C SUSPENSION, INSULATOR ASSEMBLY, D-4C	6	

หมายเหตุ

1. โครงสร้างของโครงเหล็ก (Ⓐ,Ⓑ,Ⓒ,Ⓓ, และขนาด BACK TO BACK) ผู้รับจ้างเป็นผู้ออกแบบและต้องส่งรายการคำนวณให้ กฟภ. พิจารณาอนุมัติก่อนดำเนินการก่อสร้าง
2. แนะนำให้ใช้โครงเหล็ก แบบนี้ที่ระยะห่างเสา ไม่เกิน 150 เมตร
3. จำนวนวงจรของระบบจำหน่าย 22 & 33 kV ใต้ไลน์ 115 kV ไม่เกิน 2 วงจร
4. การประกอบไวเบรชั่นแดมเปอร์ แบบสไปแรล ดูแบบเลขที่ SA1-015/22019 (การประกอบเลขที่ 9557)
5. รายละเอียดเพิ่มเติม ดูแบบเลขที่ SA1-015/45005 (การประกอบเลขที่ 5701)

NOTES

1. THE STRUCTURE OF STEEL TOWER (Ⓐ,Ⓑ,Ⓒ,Ⓓ AND BACK TO BACK) SHALL BE DESIGNED BY THE CONTRACTOR AND SUBMITED CALCULATION SHEET TO PEA FOR APPROVAL BEFORE CONSTRUCTION .
2. SPAN OF STEEL TOWER IS RECOMMENDED TO BE NO MORE THAN 150 METERS .
3. THE NUMBER OF 22 & 33 kV DISTRIBUTION LINE UNDER 115 kV SYSTEM NO MORE THAN TWO(2) CIRCUITS.
4. SPIRAL VIBRATION DAMPER ASSEMBLY, SEE DWG. NO. SA1-015/22019 (ASSEMBLY NO. 9557)
5. FOR MORE DETAILS SEE DWG. NO. SA1-015/45005 (ASSEMBLY NO. 5701) .

กองมาตรฐานระบบไฟฟ้า ฝ่ายมาตรฐานและความปลอดภัย	การไฟฟ้าส่วนภูมิภาค	ใช้แทนแบบ..... ถูกแทนโดยแบบ.....
ผู้เขียน สมชาย..... ผู้สำรวจ..... วิศวกร..... หัวหน้าแผนก..... ผู้อำนวยการกอง..... ผู้อำนวยการฝ่าย.....	ผู้ว่าการ.....	เขียนเสร็จวันที่ 25 เมย. 45 แก้แบบวันที่..... มิติเป็น — มาตราส่วน —
ของผู้วางแผนและพัฒนาระบบไฟฟ้า.....	13 มิ.ย. 2545 โครงเหล็กสำหรับทางโค้ง 90°	แบบเลขที่ SA1-015/45007 แผ่นที่ 5 ของจำนวน 5 แผ่น
	STEEL TOWER, FOR LARGE ANGLE STRUCTURE 90°	

13 มิ.ย. 2545