การประกอบเลขที่
ASSEMBLY NO. 0806

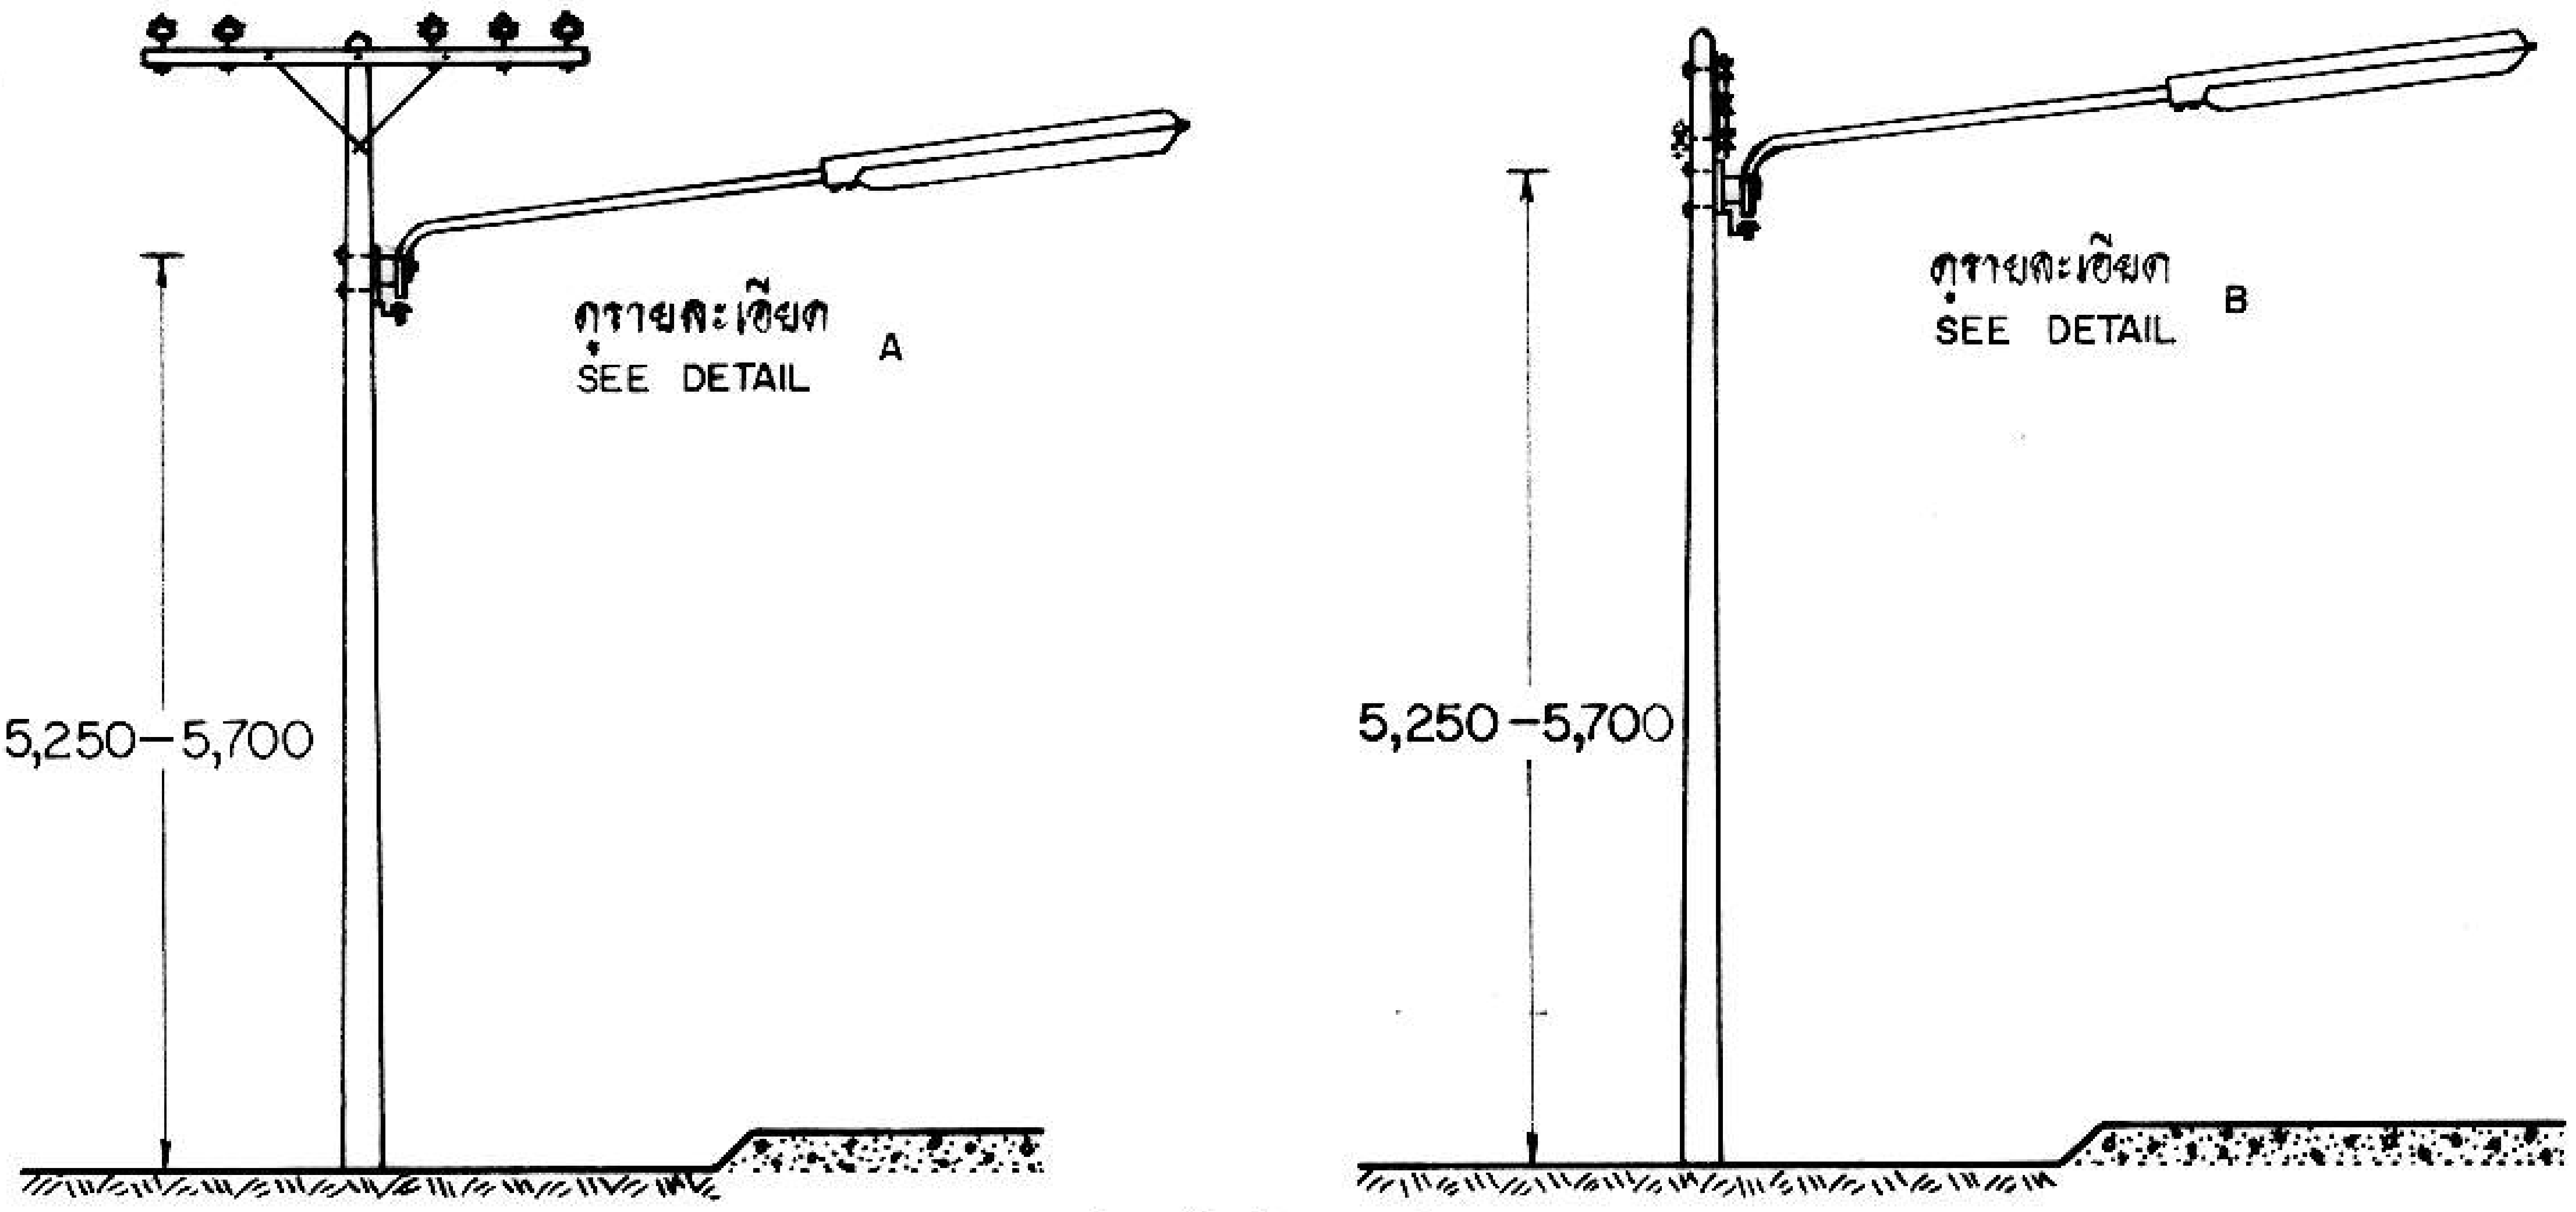

สำหรับเสาคอนกรีต 8 ม.
FOR 8 m CONCRETE POLE

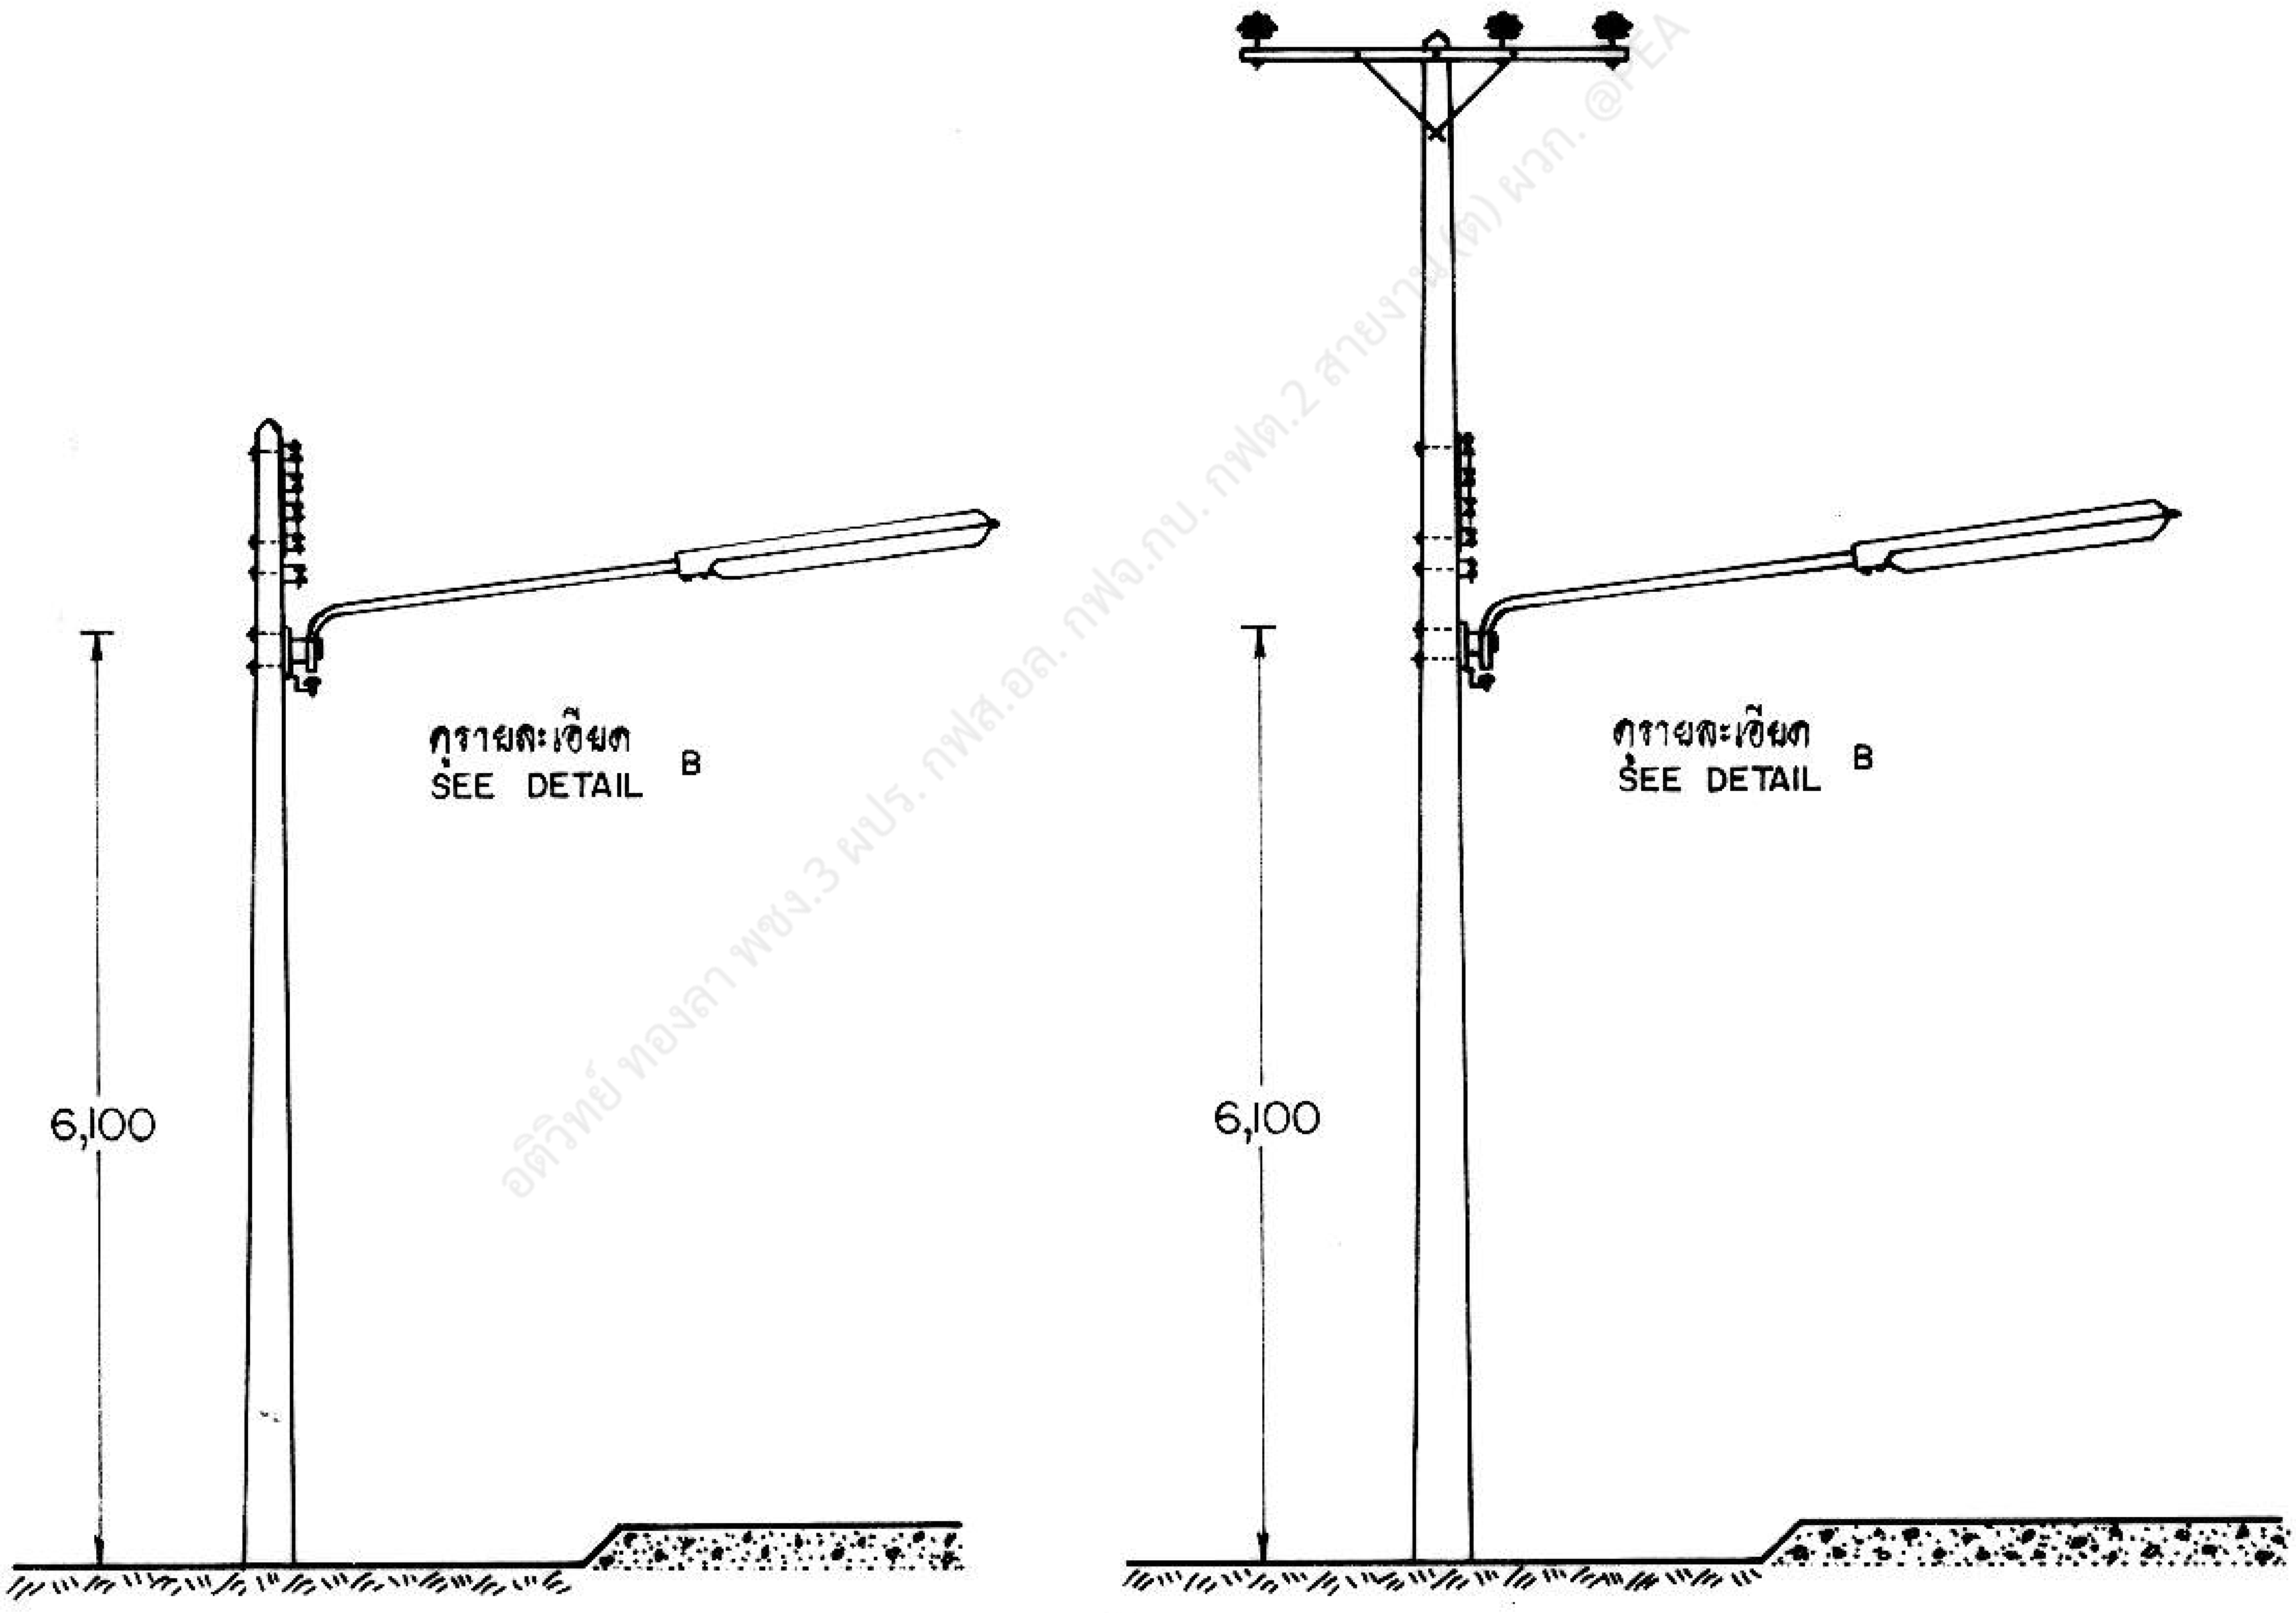

สำหรับเสาคอนกรีต 9, 12, 14 ม.
FOR 9, 12, 14 m CONCRETE POLE

อดิวิทย์ ทองลา พชง.3 ผปร. กฟส.อล. กฟจ.กบ. กฟต.2 สายงาน(ต) ผวก. @PEA

กองวิศวกรรมไฟฟ้าและเครื่องกล ฝ่ายวิศวกรรม	การไฟฟ้าส่วนภูมิภาค	ใช้แทนแบบ ถูกแทนโดยแบบ
ผู้เขียน ผู้สำรวจ วิศวกร หัวหน้าแผนก หัวหน้ากอง ผู้อำนวยการฝ่าย	ผู้ว่าการ 28 เม.ย. 21	เขียนเสร็จวันที่ 31 มี.ค. 21 แก้แบบวันที่
	การติดตั้งไฟถนน การติดตั้งดวงโคม (แบบที่ 1)	มิติเป็น มม. มาตราส่วน 1 : 100
รองผู้ว่าการฝ่ายเทคนิค	STREET LIGHT INSTALLATION LUMINAIRE FITTING (TYPE 1)	แบบเลขที่ SAI-015/21025 แผ่นที่ 1 ของจำนวน 7 แผ่น

การประกอบเลขที่
ASSEMBLY NO. 0806

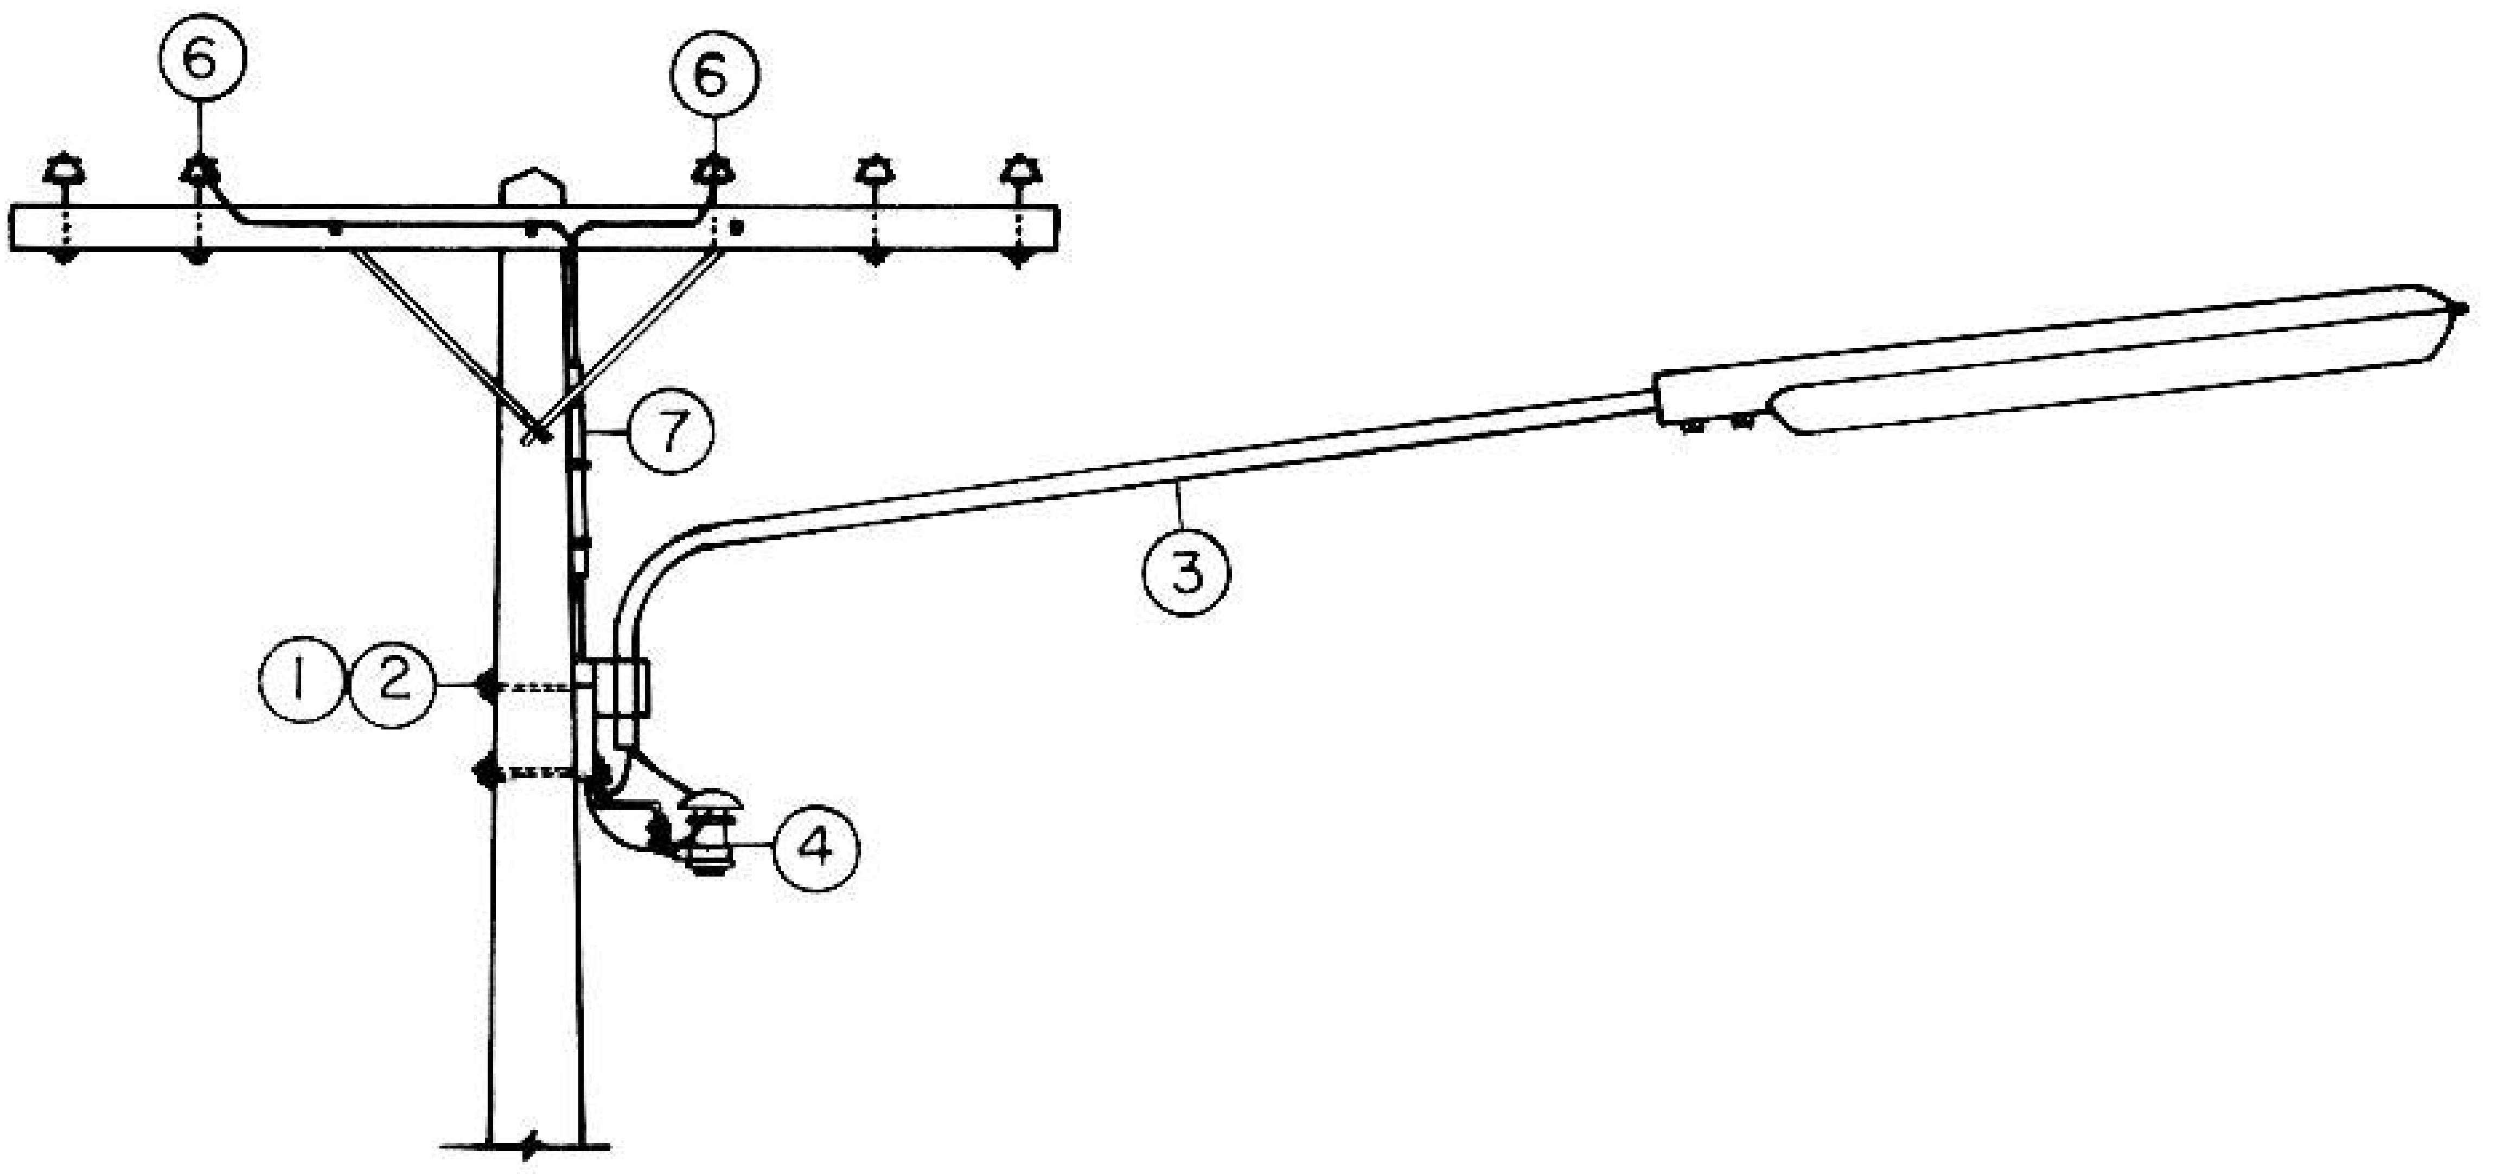

รายละเอียด
DETAIL A

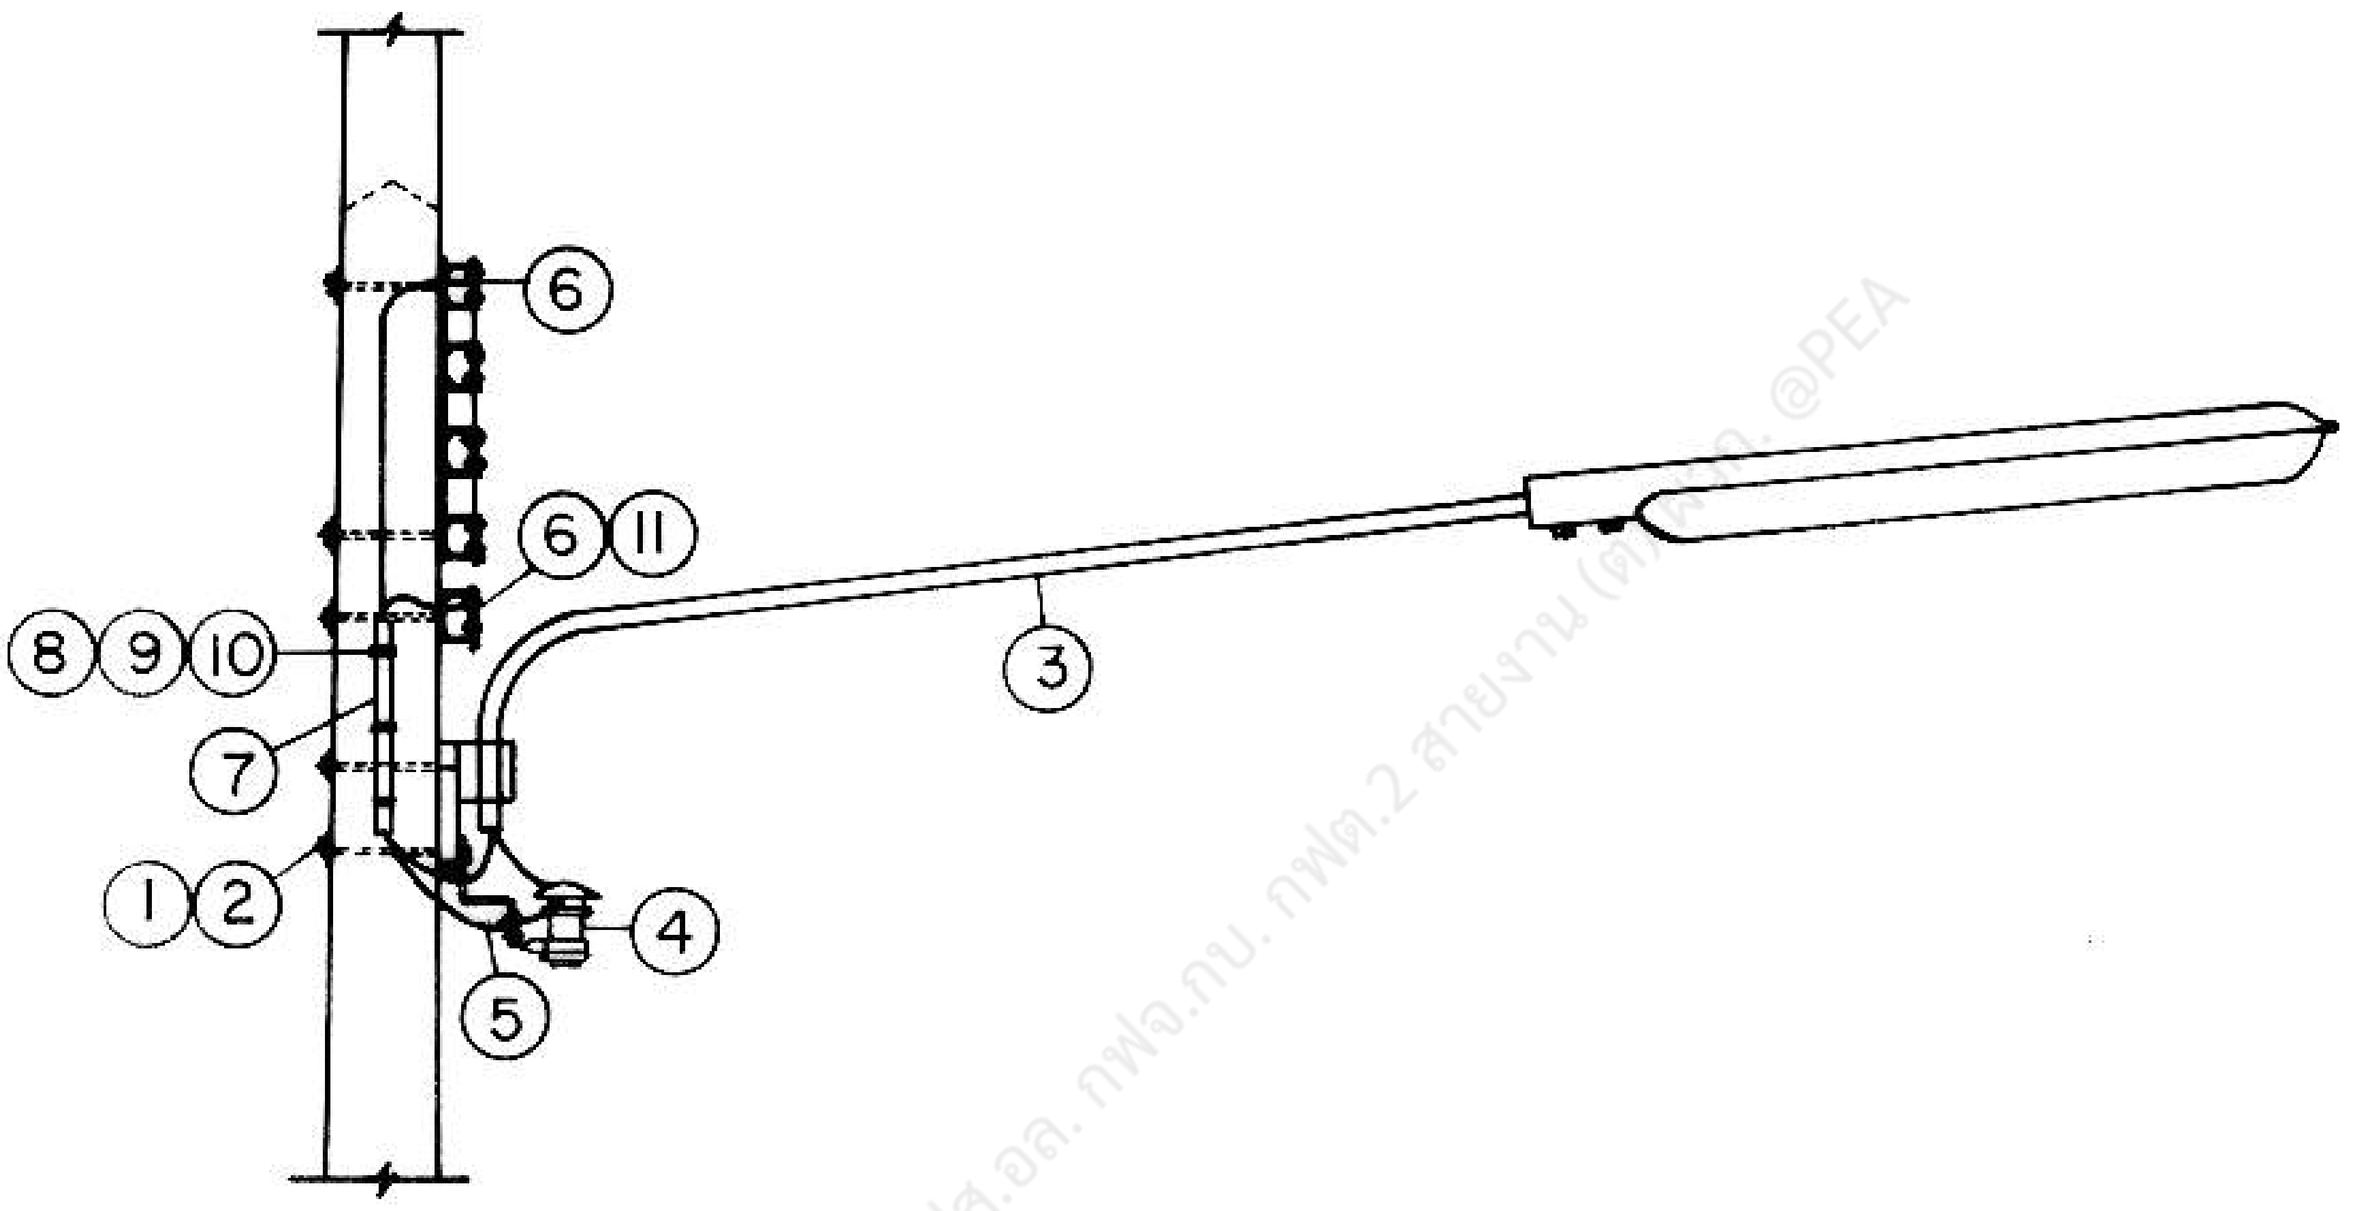

รายละเอียด
DETAIL B

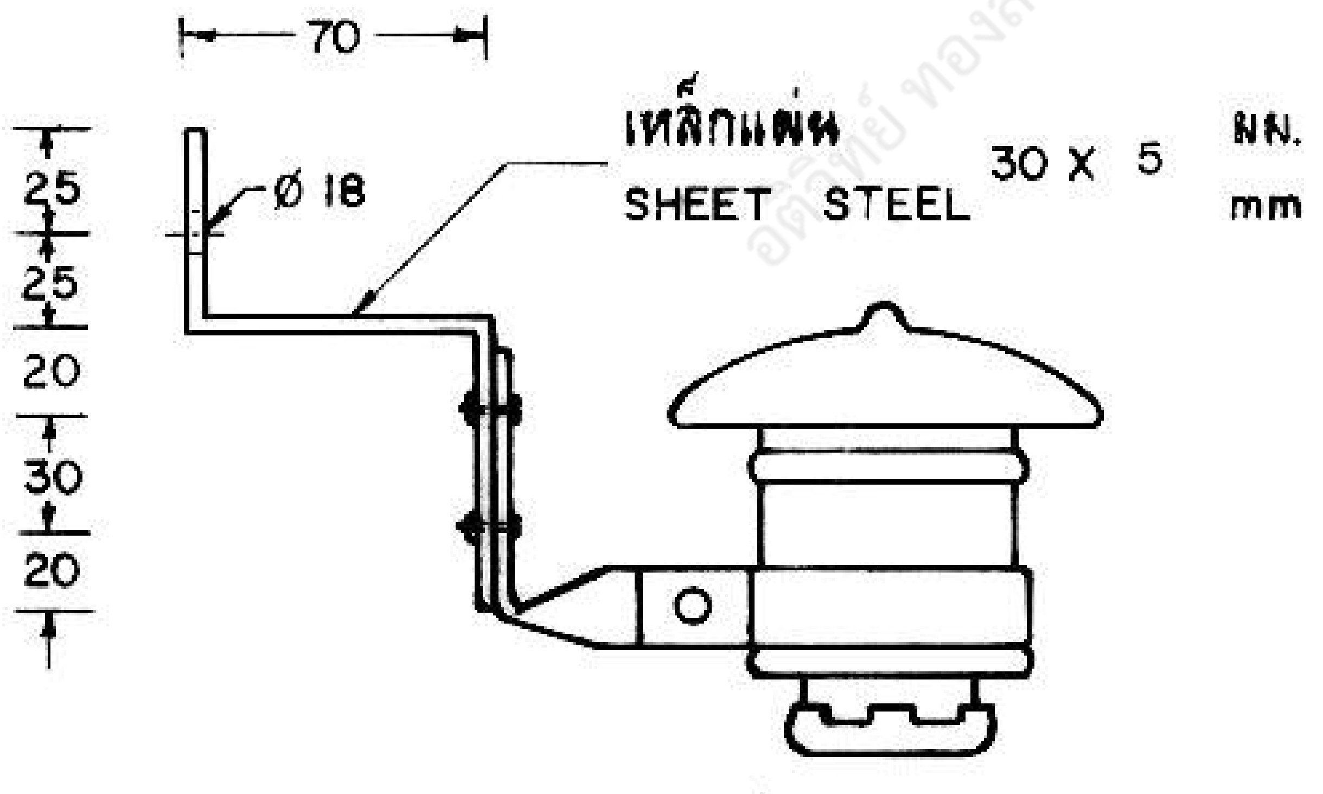

ฐานฟิวส์สำหรับติดตั้งในระบบจำหน่าย
FUSE FITTING FOR OVERHEAD LINE

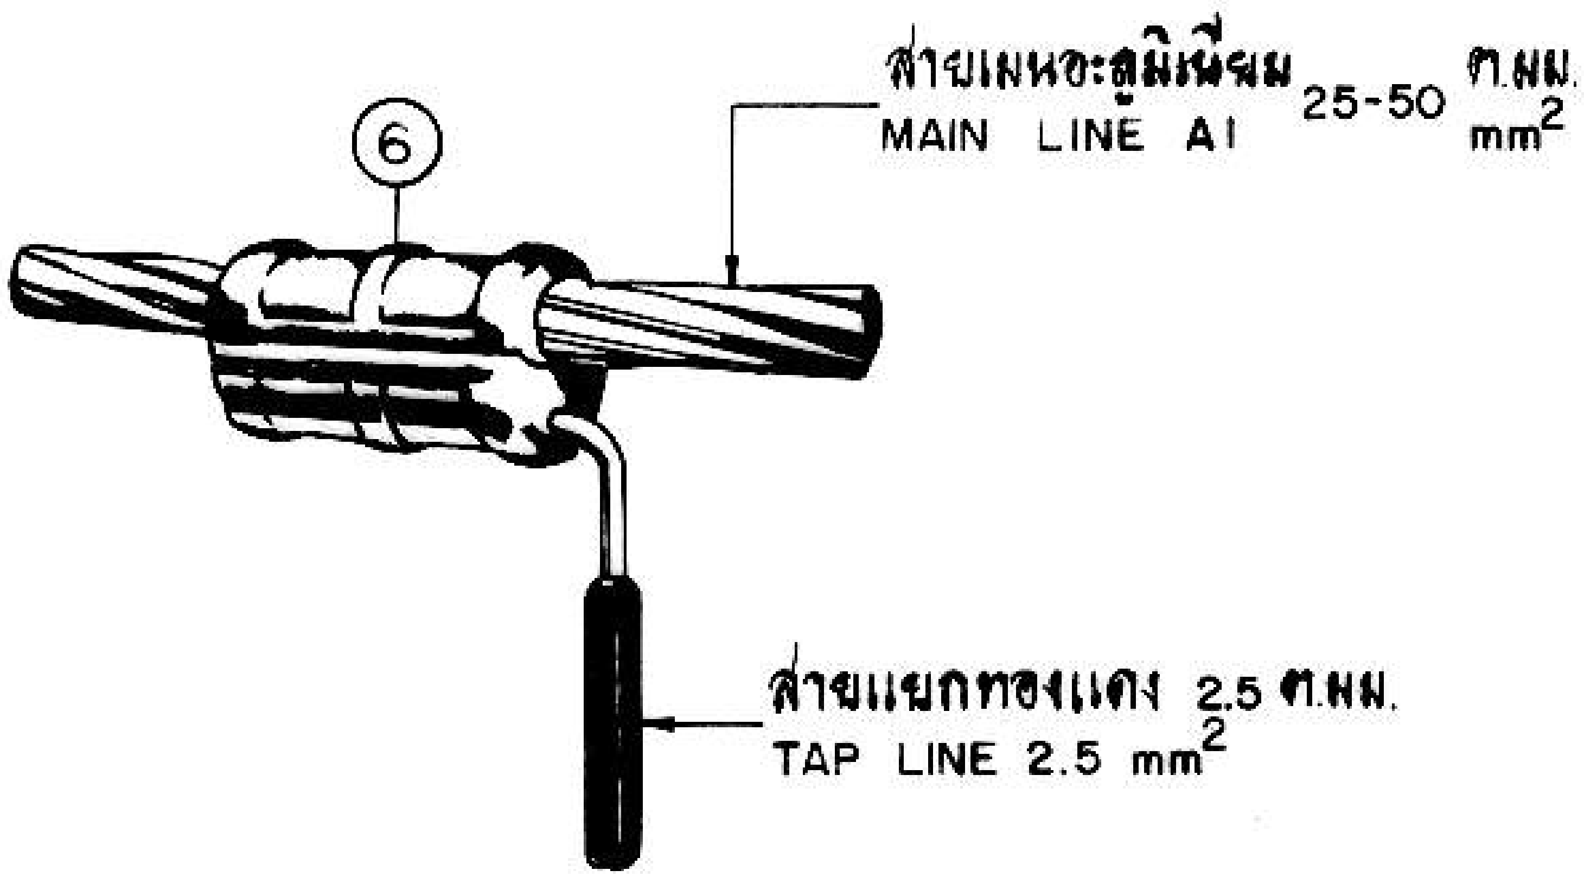

[illegible] ทองลา พชง.3 ผปร. กฟส.อล. กฟจ.กบ. กฟต.2 สายงาน (ต[illegible]) @PEA

กองวิศวกรรมไฟฟ้าและเครื่องกล
ฝ่ายวิศวกรรม

ผู้เขียน
ผู้สำรวจ
วิศวกร
หัวหน้าแผนก
หัวหน้ากอง
ผู้อำนวยการฝ่าย
21

รองผู้ว่าการฝ่ายเทคนิค

การไฟฟ้าส่วนภูมิภาค

ผู้ว่าการ 28 เม.ย. 21

การติดตั้งไฟถนน
การติดตั้งดวงโคม (แบบที่ 1)

STREET LIGHT INSTALLATION
LUMINAIRE FITTING (TYPE 1)

ใช้แทนแบบ
ถูกแทนโดยแบบ
เขียนเสร็จวันที่ 31 มี.ค. 21
แก้แบบวันที่
มิติเป็น มม.
มาตราส่วน 1:5, 1:50
แบบเลขที่ SAI-015/21025
แผ่นที่ 2 ของจำนวน 7 แผ่น

การประกอบเลขที่
ASSEMBLY NO. 0806

บัญชีวัสดุ
BILL OF MATERIAL

ลำดับที่ ITEM	รายละเอียด DESCRIPTION	จำนวน REQ'D	วัสดุเลขที่ MAT. NO.
1	สลักเกลียว M 16 X 250 - 350 มม. BOLT, MACHINE, M 16 X 250 - 350 mm	2	01110203-5
2	แหวนสี่เหลี่ยมแบน 52 X 52 X 4.5 มม. รู Ø 18 มม. มอก. 258 WASHER, SQUARE, FLAT, 52 X 52 X 4.5 mm, HOLE Ø 18 mm, TIS 258	2	01180100
3	โคมไฟถนน พร้อม กิ่งโคม แป้น และหลอด STREET LIGHTING LUMINAIRES, COMPLETE WITH ROD BRACKET & BULB	1	07010000 07010102
4	ฐานฟิวส์สำหรับติดในระบบจำหน่าย 500 โวลต์ พร้อม ดี-คาทริดจ์ฟิวส์ 2 แอมป์ FUSE FITTING FOR OVERHEAD LINE 500 V COMP. WITH D-CARTRIDGE FUSE 2 A	1	07030000 07030100
5	สายทองแดงหุ้มฉนวน ใช้ภายนอก 600 โวลต์ 70°C 2.5 ต.มม. มอก. 11 CONDUCTOR, INSULATED WEATHER PROOF, 600 V, 70°C, 2.5 mm^2, TIS 11		02089954
6	คอนเนคเตอร์ ชนิดบีบ สำหรับสายเมนอะลูมิเนียม 25-50 ต.มม. สายแยกทองแดง 2.5-6 ต.มม. CONNECTOR, COMPRESSION TYPE, MAIN Al 25-50 mm^2, TAP OFF Cu 2.5-6 mm^2	2	02320001
7	ท่อ PVC แข็ง ชื่อขนาด 20 ยาว 500 มม. (ทำจากวัสดุเลขที่ 08040002 หรือ 08040001) CONDUIT, PVC RIGID, Ø 20, 500 mm LONG (MADE OF MAT. NO. 08040002 OR 08040001)	1	
8	เข็มขัดรัดท่อเอสล่อน (ทำด้วยลวดอะลูมิเนียมแบน 1 X 10 มม. ยาว 150 มม.) STRAP TO FIX S'LON PIPE (MADE OF ARMOUR TAPE 1 X 10 mm, 150 mm LONG)	3	02200000
9	หมุดไม้สำหรับอุดรูเสาคอนกรีต ขนาด Ø 19-21 มม. ยาว 60 มม. (ทำด้วยไม้เนื้อแข็ง) WOOD PLUG, SIZE Ø 19-21 mm, 60 mm LONG (MADE OF HARD WOOD)	3	
10	ตะปูเหล็กหัวกลมแบน Ø 2.00 X 5.00 มม. ยาว 35 มม. NAIL, MILD STEEL, ROUND- FLAT HEAD, Ø 2.00 X 5.00 mm, 35 mm LONG	3	01990000
11	PVC เทป กว้าง 19 มม. (ใช้ความยาว 2 ม. ต่อ จุด) PVC TAPE 19 mm WIDE (2 m LONG PER POINT)		02180001 or 02180002

หมายเหตุ สลักเกลียวที่ใช้ยึดแป้นติดกิ่งโคม กับเสาคอนกรีต

เสา 8,9 ม. ใช้สลักเกลียว M 16 X 250 มม.
เสา 12 ม. ใช้สลักเกลียว M 16 X 300 มม.
เสา 14 ม. ใช้สลักเกลียว M 16 X 350 มม.

NOTE MACHINE BOLTS FOR FIXING STREET LIGHTING BRACKET TO CONCRETE POLE.

8,9 m POLE USE MACHINE BOLT M 16 X 250 mm
12 m POLE USE MACHINE BOLT M 16 X 300 mm
14 m POLE USE MACHINE BOLT M 16 X 350 mm

กองวิศวกรรมไฟฟ้าและเครื่องกล
ฝ่ายวิศวกรรม
ผู้เขียน
ผู้สำรวจ
วิศวกร
หัวหน้าแผนก
หัวหน้ากอง
ผู้อำนวยการฝ่าย
รองผู้ว่าการฝ่ายเทคนิค

การไฟฟ้าส่วนภูมิภาค
ผู้ว่าการ 28 เมย. 21

การติดตั้งไฟถนน
การติดตั้งดวงโคม (แบบที่ 1)

STREET LIGHT INSTALLATION
LUMINAIRE FITTING (TYPE 1)

ใช้แทนแบบ
ถูกแทนโดยแบบ
เขียนเสร็จวันที่ 31 มี.ค. 21
แก้แบบวันที่ 21 ม.ค. 36
มิติเป็น
มาตราส่วน
แบบเลขที่ SA1-015/21025
แผ่นที่ 3 ของจำนวน 7 แผ่น

การประกอบเลขที่
ASSEMBLY NO. 0806

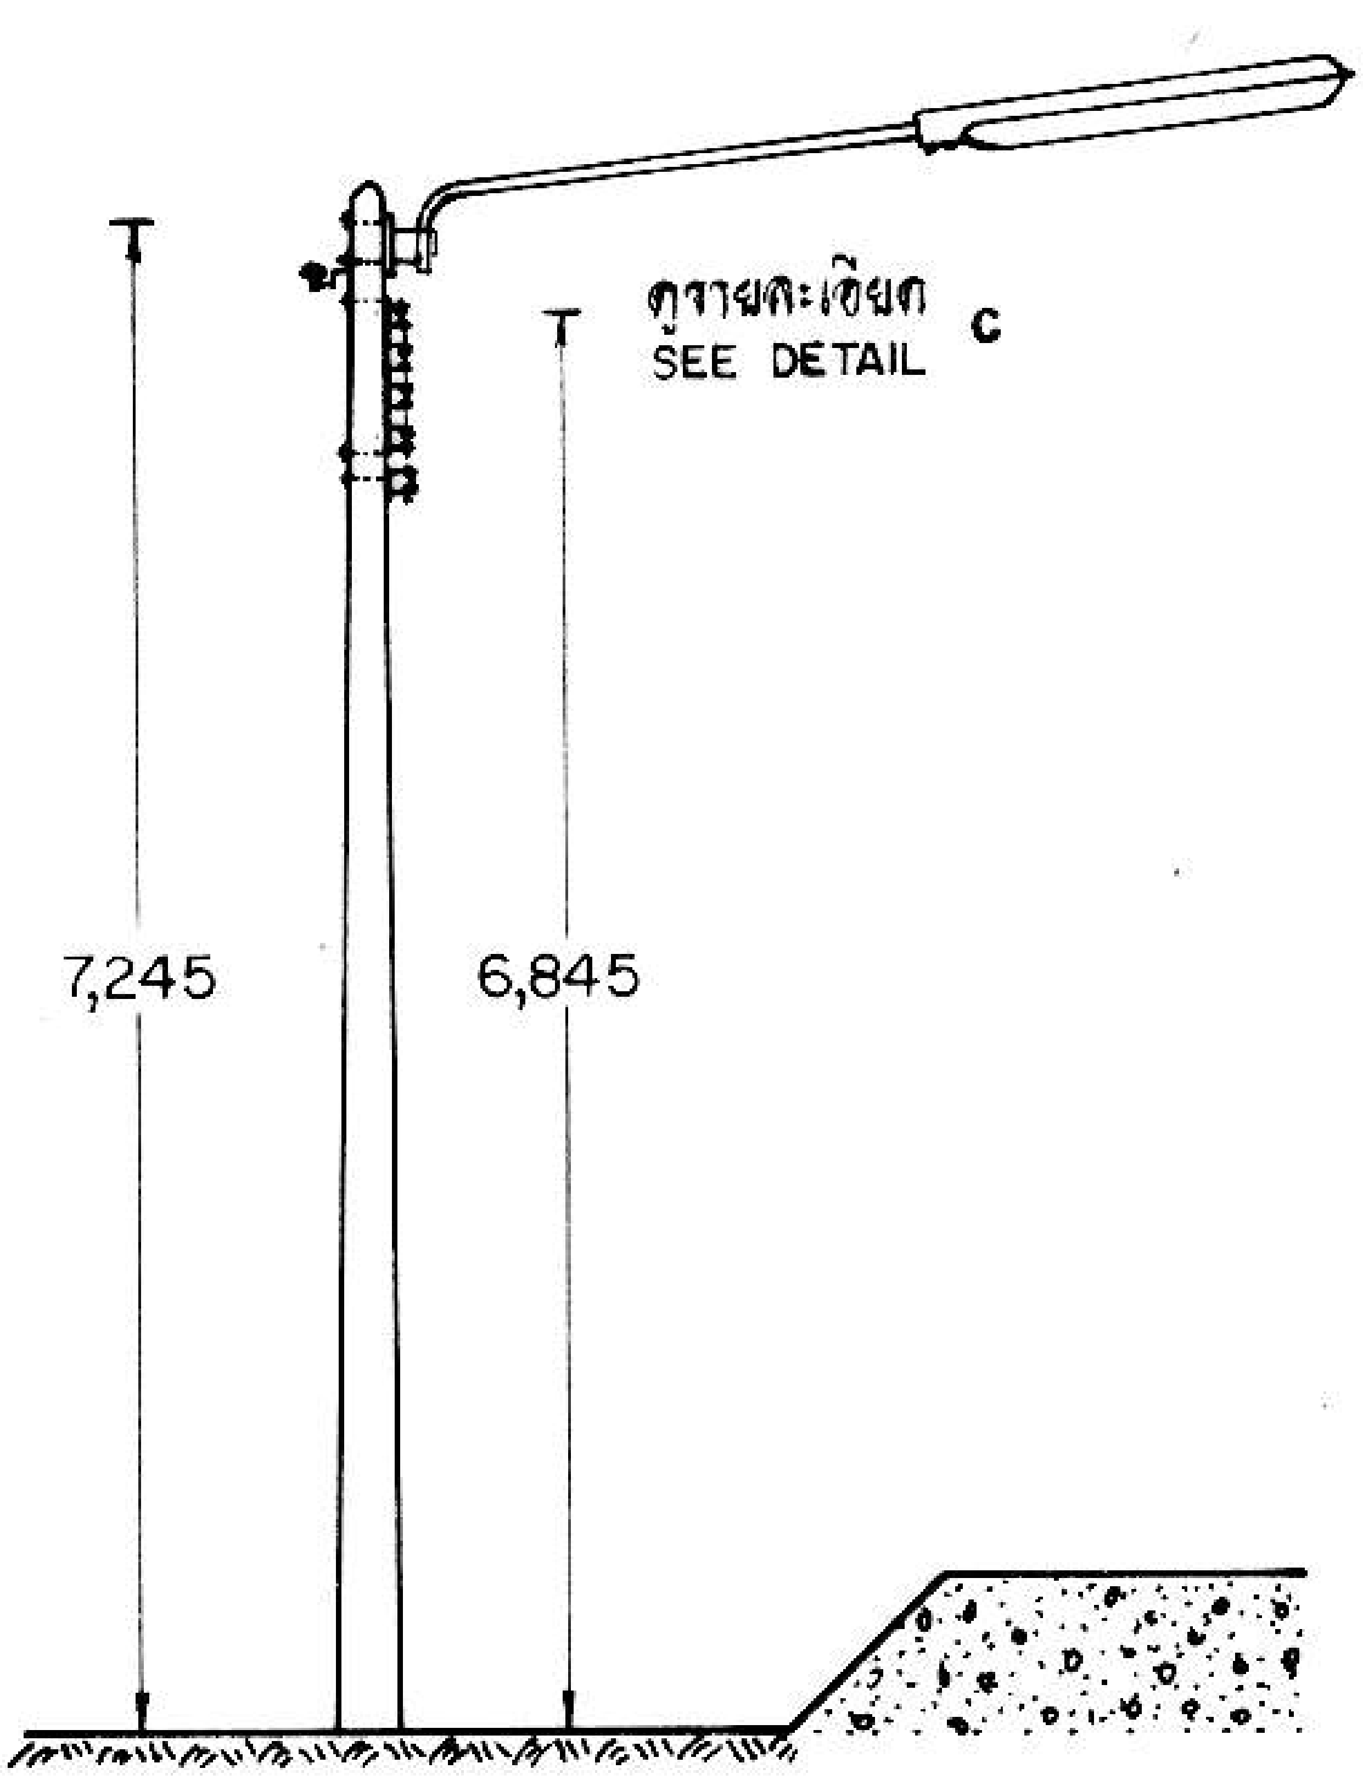

สำหรับเสาคอนกรีต 9 ม.
FOR 9 m CONCRETE POLE

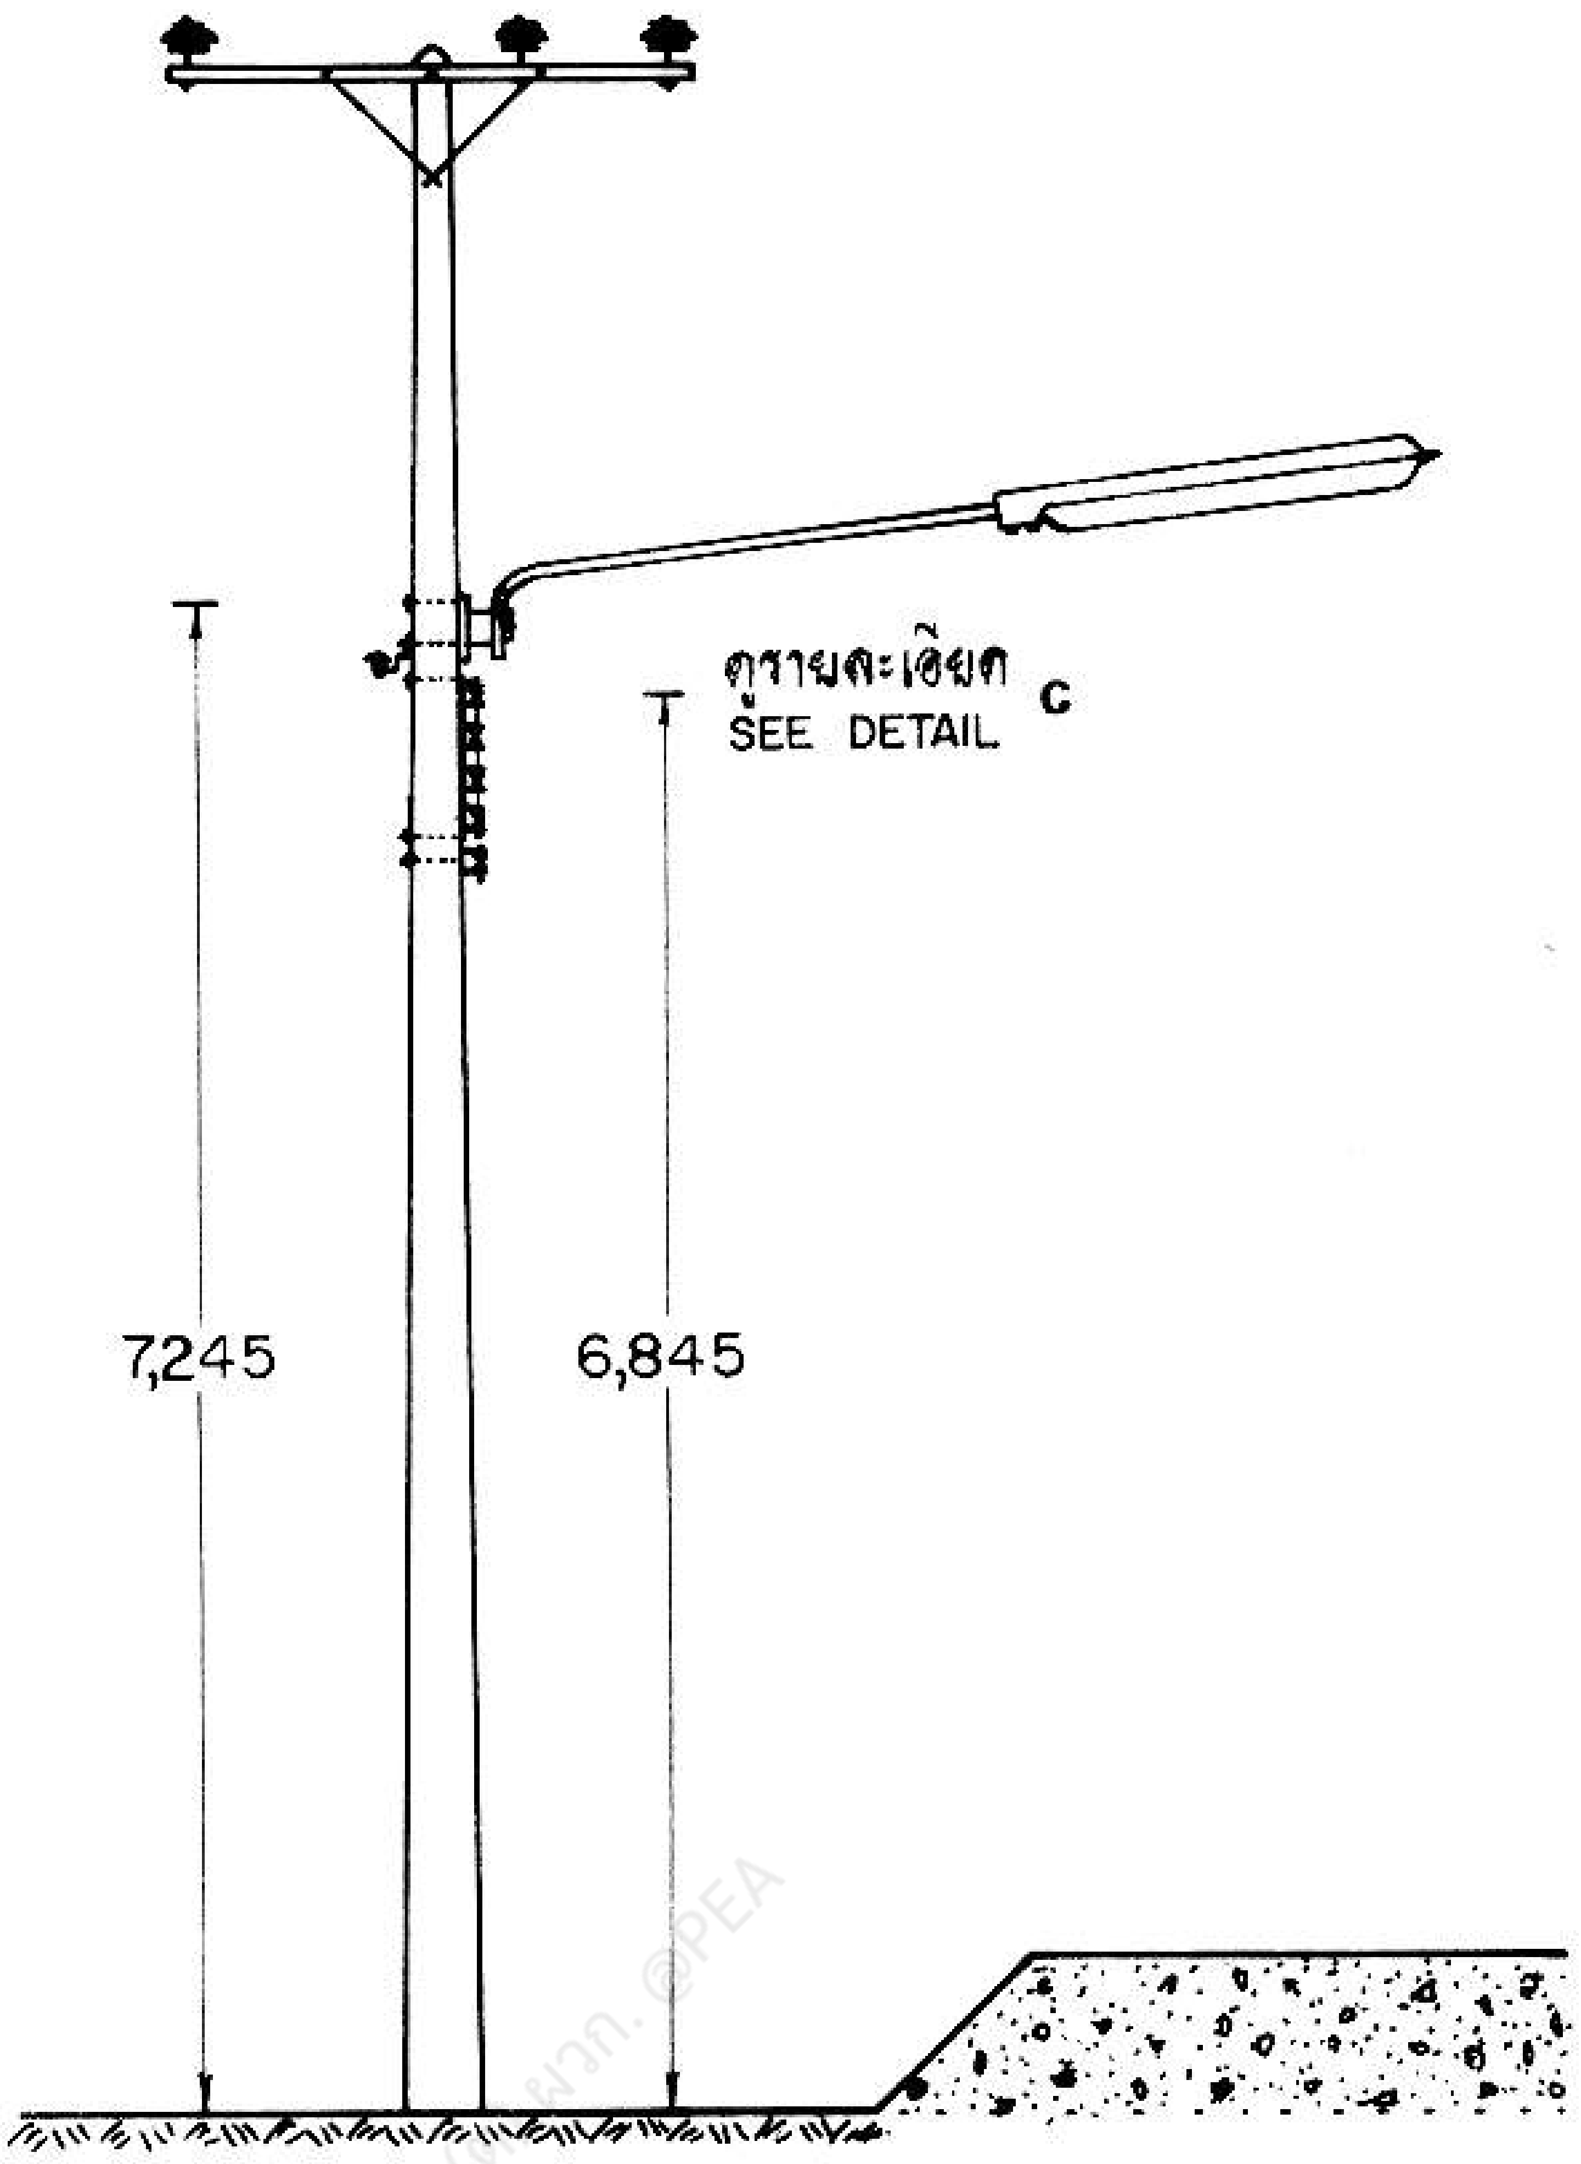

สำหรับเสาคอนกรีต 12, 14 ม.
FOR 12, 14 m CONCRETE POLE

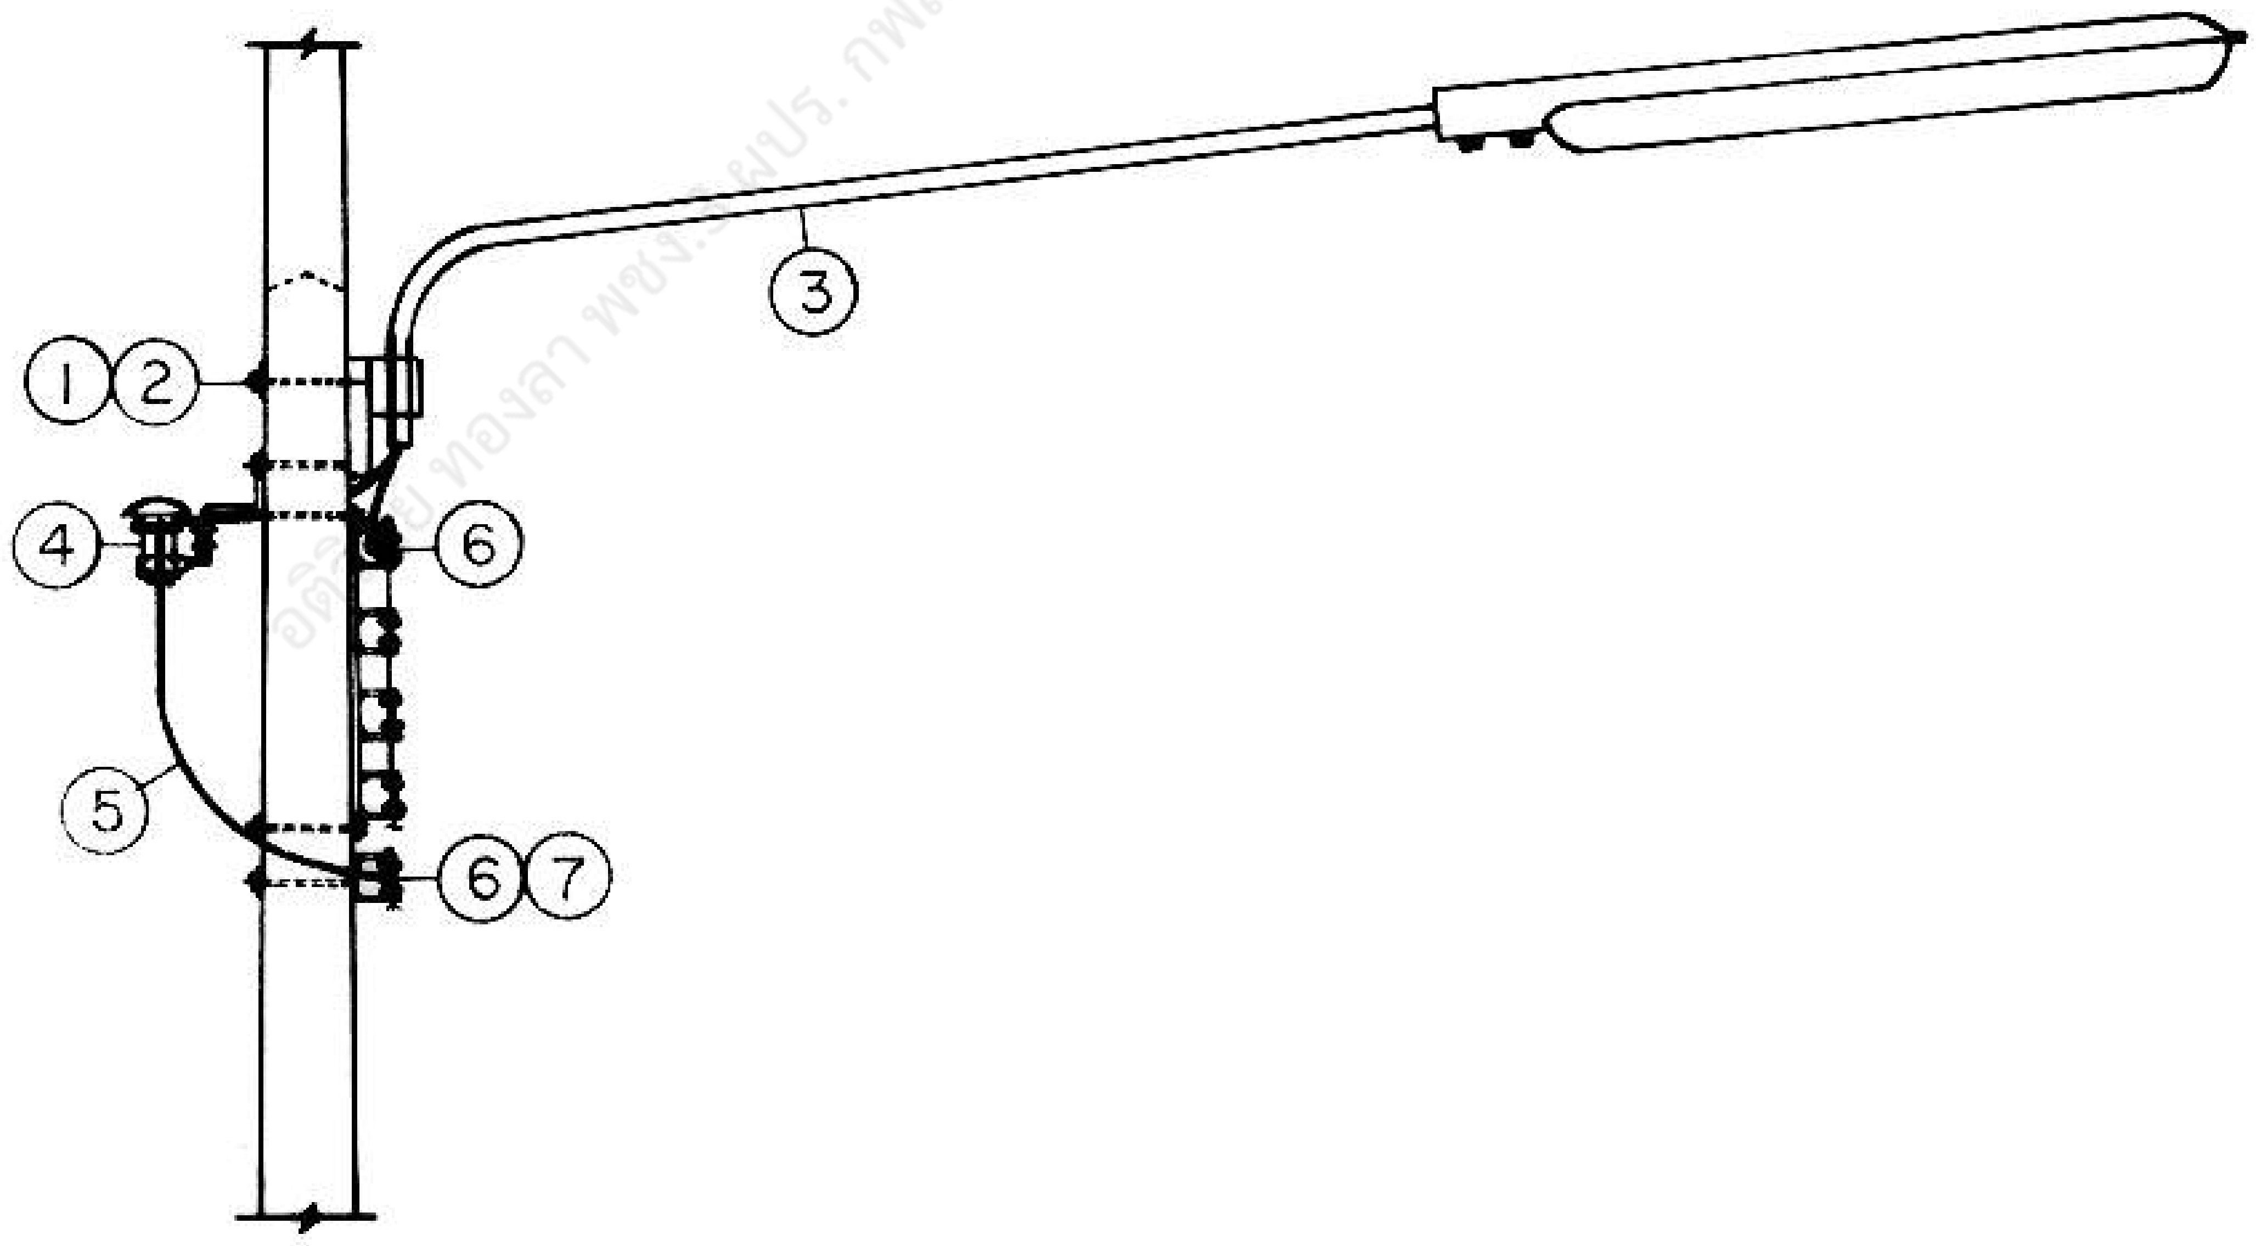

รายละเอียด C
DETAIL C

อดิ[illegible] ทองลา พชง.[illegible]ปร. กฟส.อล. กฟจ.กบ. กฟต.2 สายงาน ([illegible]) ผวก. @PEA

กองวิศวกรรมไฟฟ้าและเครื่องกล
ฝ่ายวิศวกรรม

ผู้เขียน
ผู้สำรวจ
วิศวกร
หัวหน้าแผนก
หัวหน้ากอง
ผู้อำนวยการฝ่าย

รองผู้ว่าการฝ่ายเทคนิค

การไฟฟ้าส่วนภูมิภาค

ผู้ว่าการ 28 เมย. 21

การติดตั้งไฟถนน
การติดตั้งดวงโคม (แบบที่ 2)

STREET LIGHT INSTALLATION
LUMINAIRE FITTING (TYPE 2)

ใช้แทนแบบ
ถูกแทนโดยแบบ
เขียนเสร็จวันที่ 31 มี.ค. 21
แก้แบบวันที่
มิติเป็น มม.
มาตราส่วน 1:50, 1:100

แบบเลขที่ SAI-015/21025
แผ่นที่ 4 ของจำนวน 7 แผ่น

การประกอบเลขที่
ASSEMBLY NO. 0806

บัญชีวัสดุ
BILL OF MATERIAL

ลำดับที่ ITEM	รายละเอียด DESCRIPTION	จำนวน REQ'D	วัสดุเลขที่ MAT. NO.
1	สลักเกลียว M 16 X 250-350 มม. BOLT, MACHINE, M 16 X 250-350 mm	2	01110203-5
2	แหวนสี่เหลี่ยมแบน 52 X 52 X 4.5 มม. รู Ø 18 มม. มอก. 258 WASHER, SQUARE FLAT 52 X 52 X 4.5 mm, HOLE Ø 18 mm, TIS 258	2	01180100
3	โคมไฟถนน พร้อมกิ่งโคม แป้น และหลอด STREET LIGHTING LUMINAIRES, COMPLETE WITH ROD BRACKET & BULB	1	07010000 07010102
4	ฐานฟิวส์สำหรับติดในระบบจำหน่าย 500 โวลต์ พร้อม ดี-คาทริดฟิวส์ 2 แอมป์ FUSE FITTING FOR OVERHEAD LINE 500 V COMP. WITH D-CARTRIDGE FUSE 2 A	1	07030000 07030100
5	สายทองแดงหุ้มฉนวนใช้ภายนอก 0.6/1 kV 2.5 ต.มม. CONDUCTOR, INSULATED WEATHER PROOF 0.6/1 kV 2.5 mm^2, Cu		02089954
6	คอนเนคเตอร์ ชนิดบีบ สำหรับสายเมนอะลูมิเนียม 25-50 ต.มม. สายแยกทองแดง 2.5-6 ต.มม. CONNECTOR, COMPRESSION TYPE, MAIN Al 25-50 mm^2, TAP OFF Cu 2.5-6 mm^2	2	02320001
7	PVC เทป กว้าง 19 มม. (ใช้ความยาว 2 ม. ต่อ จุด) มอก. 386 PVC TAPE 19 mm WIDE (2 m LONG PER POINT) TIS 386		02180001 or 02180002

หมายเหตุ 1. สลักเกลียวที่ใช้ยึดแป้นติดกิ่งโคม กับเสาคอนกรีต

เสา 9 ม. ใช้สลักเกลียว M 16 X 250 มม.
เสา 12 ม. ใช้สลักเกลียว M 16 X 300 มม.
เสา 14 ม. ใช้สลักเกลียว M 16 X 350 มม.

2. ใช้ก่อสร้างสำหรับกรณีแนวระบบจำหน่ายอยู่ห่างจากถนน หรือ ระดับถนนยกสูงจากระดับพื้นดินมาก ให้พิจารณาความเหมาะสมเป็นแห่ง ๆ ไป

[illegible] ผชง.3 ผปร. กฟส.อล. [illegible] 2 สายงาน (ต) ผวก. @PEA

NOTES 1. MACHINE BOLTS FOR FIXING STREET LIGHTING BRACKET TO CONCRETE POLE.

9 m POLE USE MACHINE BOLT M 16 X 250 mm
12 m POLE USE MACHINE BOLT M 16 X 300 mm
14 m POLE USE MACHINE BOLT M 16 X 350 mm

2. THIS INSTALLATION SHOULD BE APPLIED IN CASE OF DISTRIBUTION LINES ARE FAR FROM STREET SIDE OR STREET LEVEL IS SO HIGH.

กองวิศวกรรมไฟฟ้าและเครื่องกล ฝ่ายวิศวกรรม	การไฟฟ้าส่วนภูมิภาค	ใช้แทนแบบ ถูกแทนโดยแบบ
ผู้เขียน ผู้สำรวจ วิศวกร หัวหน้าแผนก หัวหน้ากอง ผู้อำนวยการฝ่าย	ผู้ว่าการ 28 เมย.21	เขียนเสร็จวันที่ 31 มี.ค. 21 แก้แบบวันที่
	การติดตั้งไฟถนน การติดตั้งดวงโคม (แบบที่ 2)	มิติเป็น มาตราส่วน
~~รองผู้ว่าการฝ่ายเทคนิค~~	STREET LIGHT INSTALLATION LUMINAIRE FITTING (TYPE 2)	แบบเลขที่ SAI-015/21025 แผ่นที่ 5 ของจำนวน 7 แผ่น

การประกอบเลขที่ ASSEMBLY NO.	0806

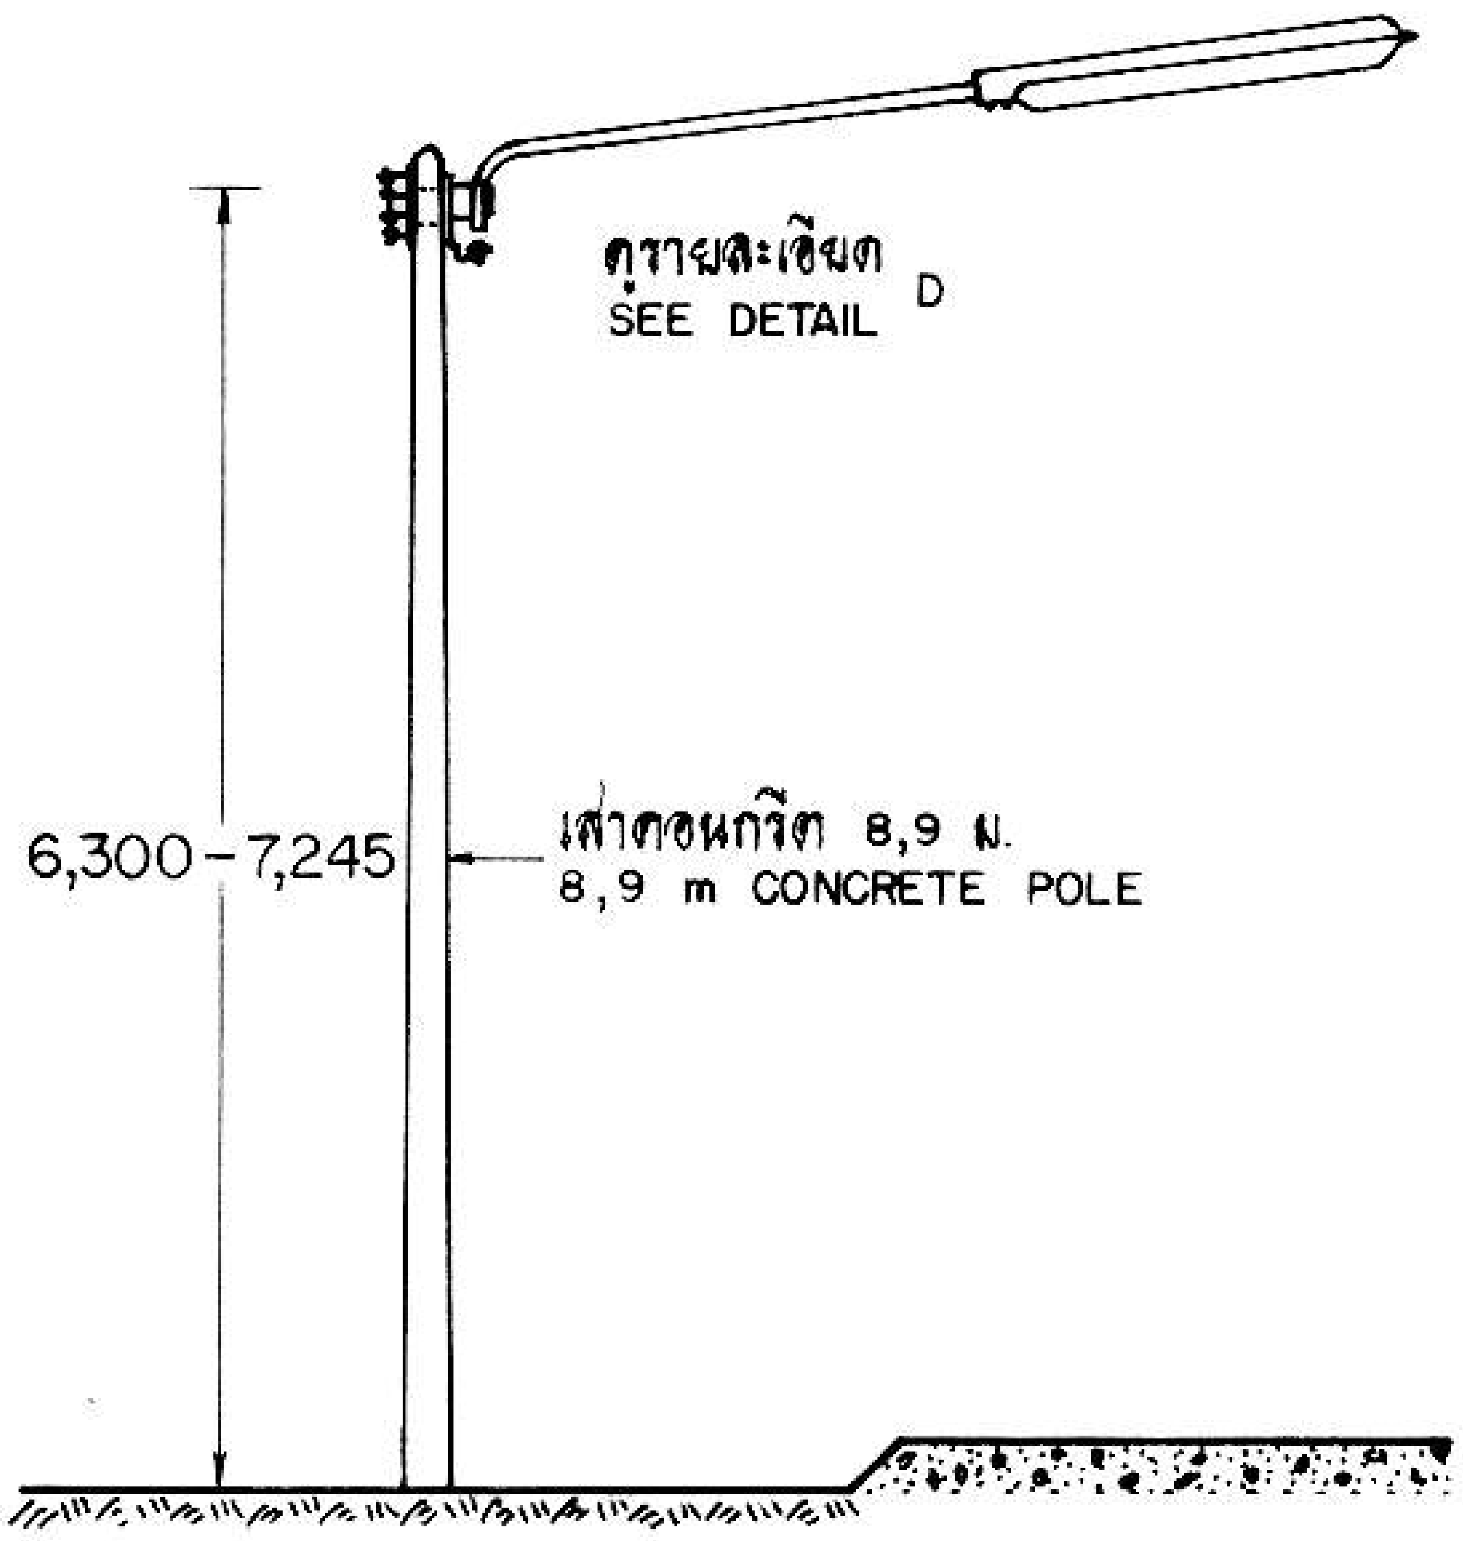

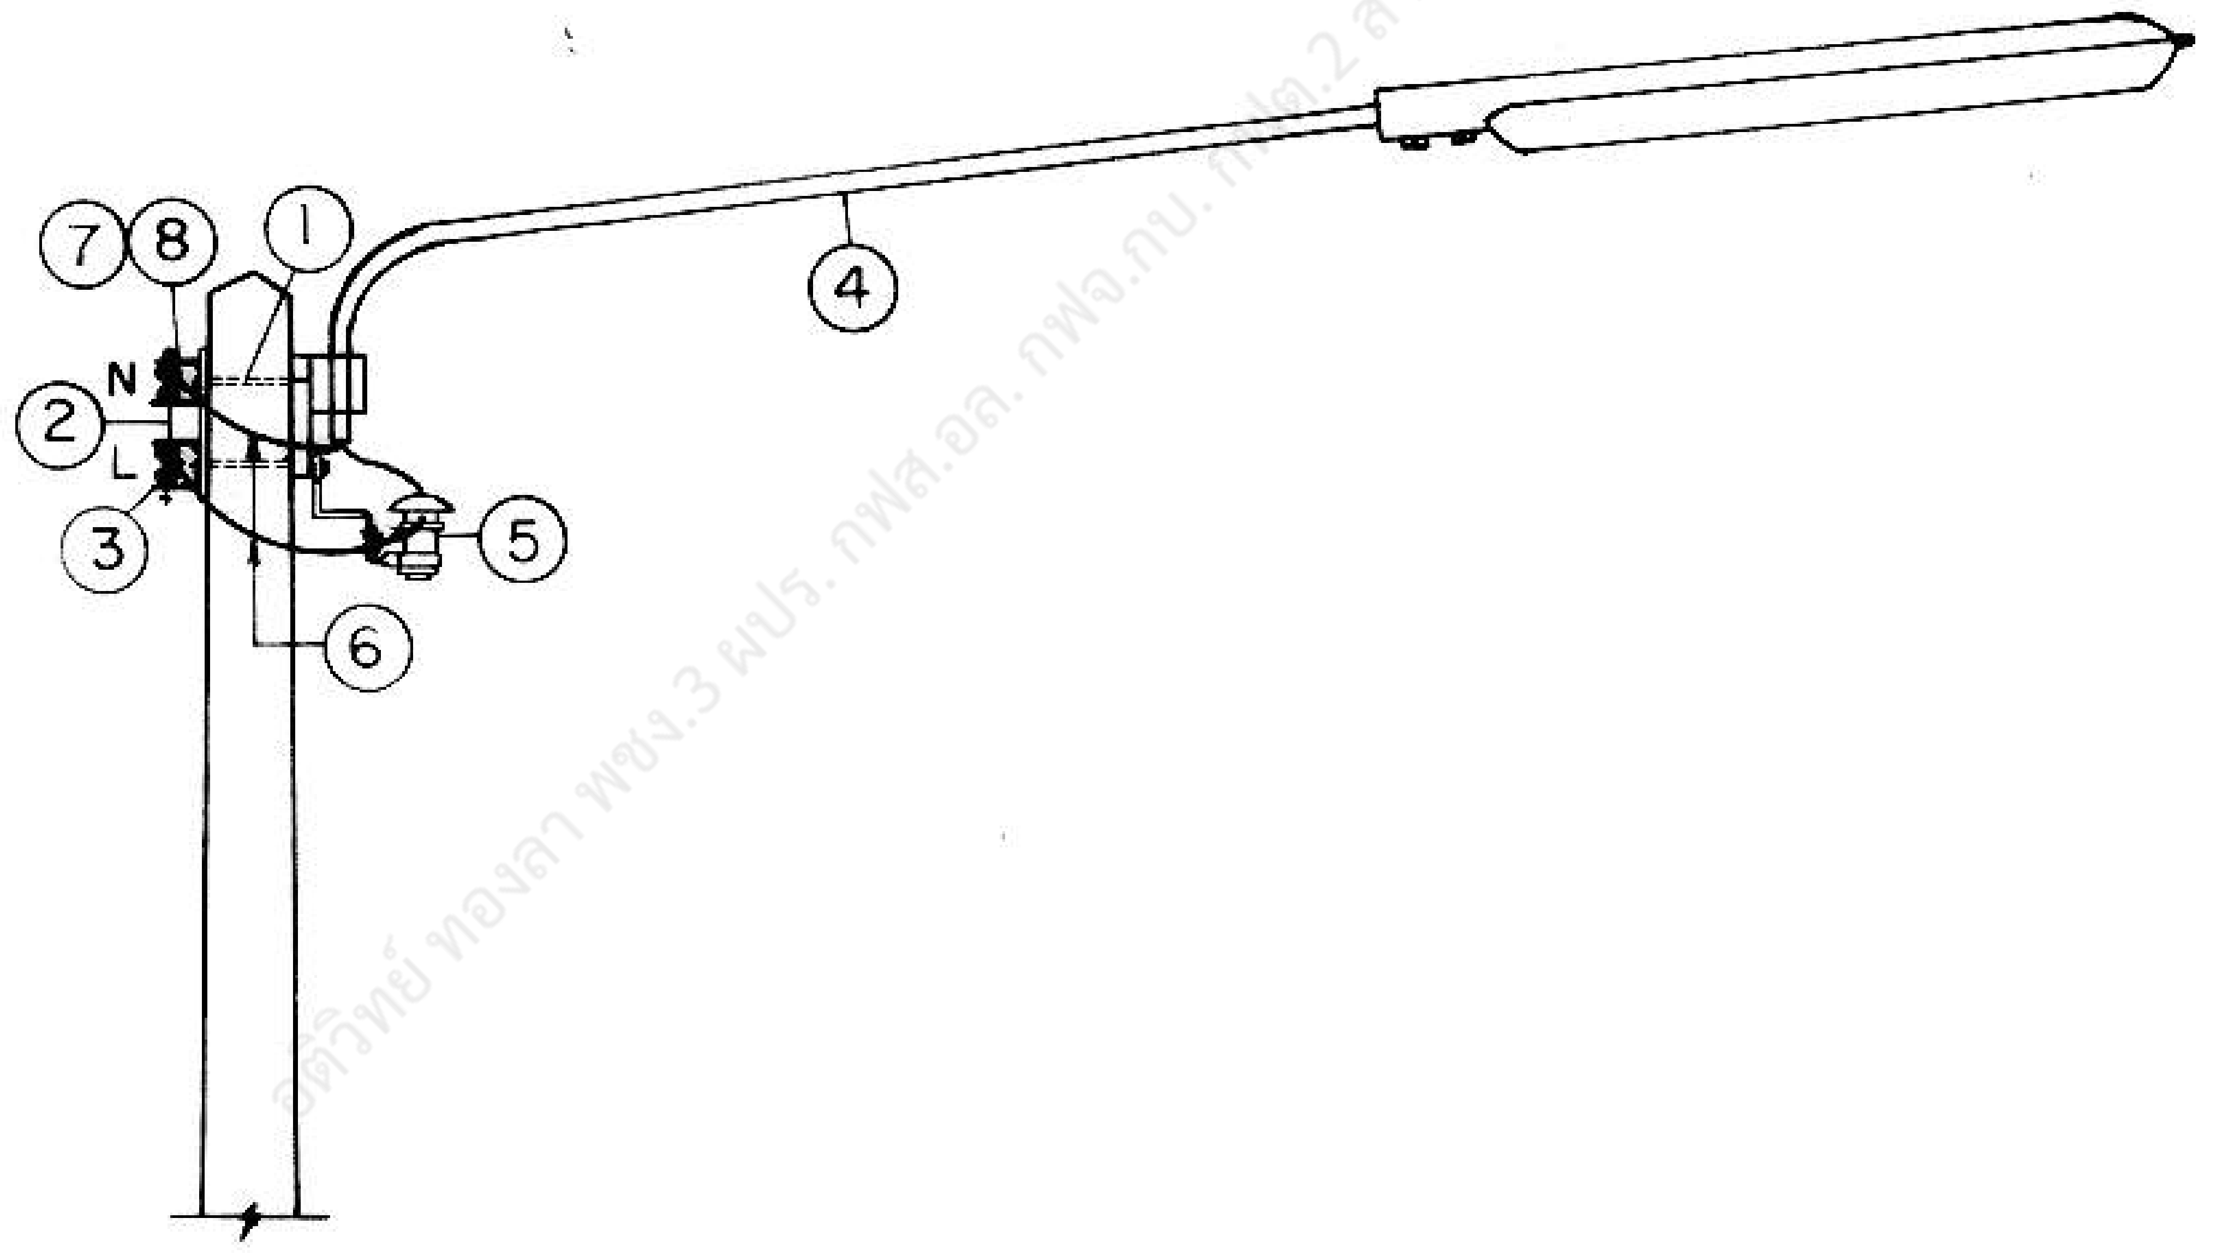

รายละเอียด D
DETAIL

สิติวิทย์ ทองลา พชง.3 ผปร. กฟส.อล. กฟจ.กบ. กฟต.2 สายงาน (ต) ผวก. @PEA

กองวิศวกรรมไฟฟ้าและเครื่องกล
ฝ่ายวิศวกรรม

ผู้เขียน
ผู้สำรวจ
วิศวกร
หัวหน้าแผนก
หัวหน้ากอง
ผู้อำนวยการฝ่าย

รองผู้ว่าการฝ่ายเทคนิค

การไฟฟ้าส่วนภูมิภาค

ผู้ว่าการ

การติดตั้งไฟถนน
การติดตั้งดวงโคม (แบบที่ 3)

STREET LIGHT INSTALLATION
LUMINAIRE FITTING (TYPE 3)

ใช้แทนแบบ
ถูกแทนโดยแบบ
เขียนเสร็จวันที่ 31 มี.ค. 21
แก้แบบวันที่
มิติเป็น มม.
มาตราส่วน 1:50, 1:100

แบบเลขที่ SAI-015/21025
แผ่นที่ 6 ของจำนวน 7 แผ่น

การประกอบเลขที่ ASSEMBLY NO.	0 8 0 6

บัญชีวัสดุ
BILL OF MATERIAL

ลำดับที่ ITEM	รายละเอียด DESCRIPTION	จำนวน REQ'D	วัสดุเลขที่ MAT. NO
1	สลักเกลียว M 16 X 250 มม. BOLT, MACHINE, M 16 X 250 mm	2	01110203
2	แร็ค 2 X 200 มม. (2 X 8") แบบหลังยื่น RACK, SECONDARY, MEDIUM PRESSED STEEL 2 X 200 mm (2 X 8") EXT. BACK	1	03130000
3	ลูกรอกแรงต่ำ มอก. 227 แบบ ข (แบบ 53-2) INSULATOR, SPOOL TYPE, TIS 227 TYPE B (CLASS 53-2)	2	03030000
4	โคมไฟถนน พร้อมกิ่งโคม แป้น และหลอด STREET LIGHTING LUMINAIRES, COMPLETE WITH ROD BRACKET & BULB	1	07010000 - 07010102
5	ฐานฟิวส์สำหรับติดในระบบจำหน่าย 500 โวลต์ พร้อม ดี-คาทริดฟิวส์ 2 แอมป์ FUSE FITTING FOR OVERHEAD LINE 500 V COMP. WITH D-CARTRIDGE FUSE 2 A	1	07030000 07030100
6	สายทองแดงหุ้มฉนวน ใช้ภายนอก 0.6/1 kV 2.5 ต.มม. CONDUCTOR, INSULATED WEATHER PROOF 0.6/1 kV 2.5 mm^2, Cu	7	02089954
7	คอนเนคเตอร์ ชนิดบีบ สำหรับสายเมนอะลูมิเนียม 25-50 ต.มม. สายแยกทองแดง 2.5-6 ต.มม. CONNECTOR, COMPRESSION TYPE, MAIN Al 25-50 mm^2, TAP OFF Cu 2.5-6mm^2	2	02320001
8	PVC เทป กว้าง 19 มม. (ใช้ความยาว 2 ม. ต่อ จุด) มอก. 386 PVC TAPE 19 mm WIDE (2 m LONG PER POINT) TIS 386		02180001 or 02180002

อดิวิทย์ ทองลา พชง.3 ผปร. กฟส.อล. [illegible] กบ. [illegible] ต.2 สายงาน (ต) ผวก. @PEA

หมายเหตุ ระบบแรงต่ำสำหรับไฟถนนโดยเฉพาะ

NOTE L.T. LINES FOR STREET LIGHTING ONLY

กองวิศวกรรมไฟฟ้าและเครื่องกล ฝ่ายวิศวกรรม	การไฟฟ้าส่วนภูมิภาค	ใช้แทนแบบ ถูกแทนโดยแบบ
ผู้เขียน ผู้สำรวจ วิศวกร หัวหน้าแผนก หัวหน้ากอง ผู้อำนวยการฝ่าย	ผู้ว่าการ 28 เมย-21	เขียนเสร็จวันที่ 31 มี.ค. 21 แก้แบบวันที่
	การติดตั้งไฟถนน การติดตั้งดวงโคม (แบบที่ 3)	มิติเป็น มาตราส่วน
รองผู้ว่าการฝ่ายเทคนิค	21 STREET LIGHT INSTALLATION LUMINAIRE FITTING (TYPE 3)	แบบเลขที่ SAI-015/21025 แผ่นที่ 7 ของจำนวน 7 แผ่น