การประกอบเลขที่
ASSEMBLY NO. 5 2 1 1 A

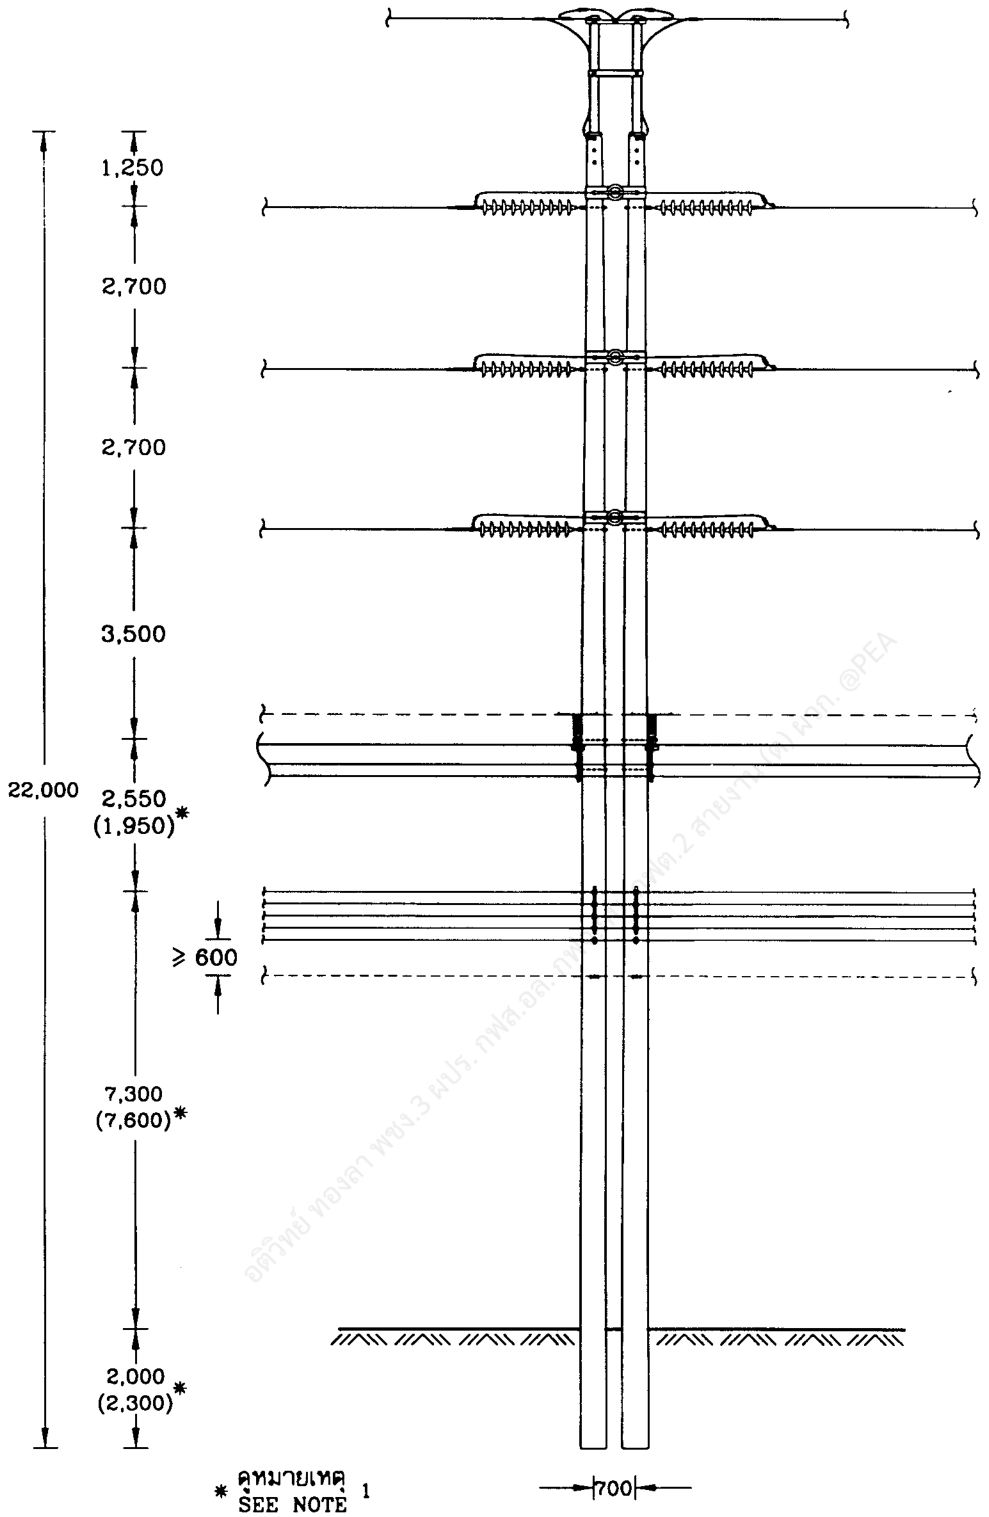

* ดูหมายเหตุ 1
SEE NOTE 1

อดิวิทย์ ทองลา พชง.3 ผปร. กฟส.อล. [illegible] ฟต.2 สายงาน (ต) ผวก. @PEA

กองมาตรฐานระบบไฟฟ้า
ฝ่ายมาตรฐานและความปลอดภัย

การไฟฟ้าส่วนภูมิภาค

ผู้เขียน สมชาย
ผู้สำรวจ
วิศวกร
หัวหน้าแผนก
ผู้อำนวยการกอง
ผู้อำนวยการฝ่าย

รองผู้ว่าการฝ่ายวางแผนและพัฒนาระบบไฟฟ้า

ผู้ว่าการ

115 kV วงจรเดี่ยว สายไฟฟ้าเดี่ยว
เสาคู่ (ชนิดมีกราวด์เพลทในเสา) สำหรับแยกสาย
แบบ SS-TL-2

26 [illegible] 2547

115 kV SINGLE CIRCUIT SINGLE CONDUCTOR
DOUBLE POLE (WITH GROUND PLATE IN POLE), TAP LINE STRUCTURE
TYPE SS-TL-2

ใช้แทนแบบ
ถูกแทนโดยแบบ
เขียนเสร็จวันที่ 2 มิ.ย. 2547
แก้แบบวันที่
มิติเป็น มิลลิเมตร
มาตราส่วน 1:125
แบบเลขที่ SA1-015/47008
แผ่นที่ 1 ของจำนวน 3 แผ่น

[illegible]

การประกอบเลขที่
ASSEMBLY NO. **5211A**

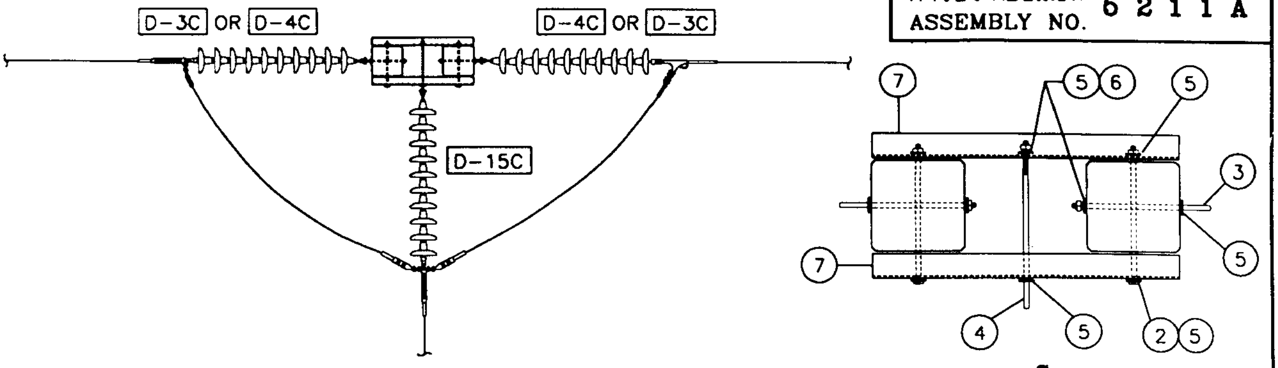

รายละเอียด
DETAIL A

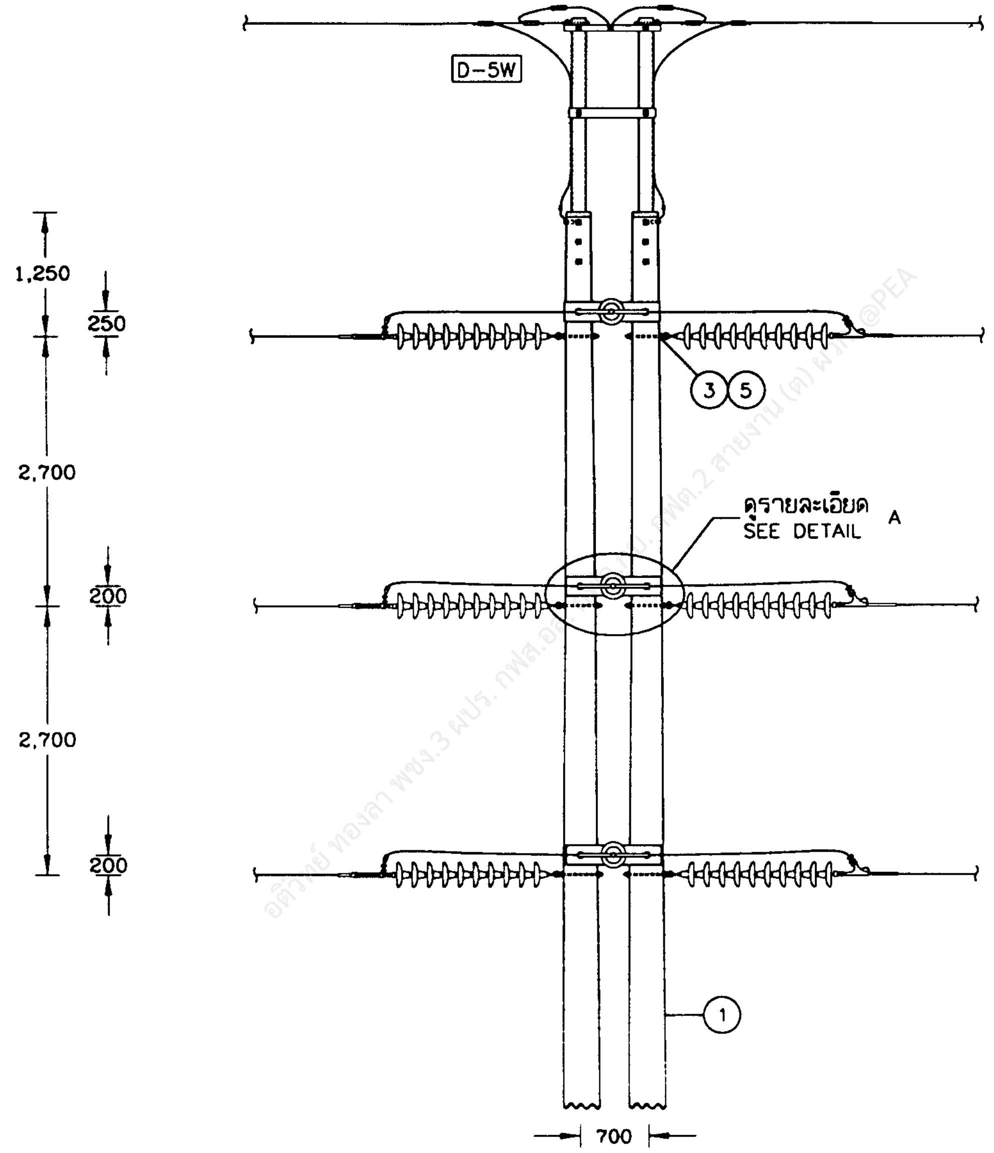

อดิศักดิ์ ทองลา พชง.3 ผปร. กฟส.อ [illegible] กฟต.2 สายงาน (ต) ผ [illegible] @PEA

กองมาตรฐานระบบไฟฟ้า ฝ่ายมาตรฐานและความปลอดภัย	การไฟฟ้าส่วนภูมิภาค	ใช้แทนแบบ .... ถูกแทนโดยแบบ ....
ผู้เขียน ..สมชาย.......... ผู้สำรวจ .... วิศวกร..................... หัวหน้าแผนก............. ผู้อำนวยการกอง.......... ผู้อำนวยการฝ่าย..........	ผู้ว่าการ..	เขียนเสร็จวันที่.2..มิ.ย..2547 แก้แบบวันที่ .... มิติเป็น...มิลลิเมตร....... มาตราส่วน..1:75........
	115 kV วงจรเดี่ยว สายไฟฟ้าเดี่ยว เสาคู่ (ชนิดมีกราวด์เพลทในเสา) สำหรับแยกสาย แบบ SS-TL-2	
รองผู้ว่าการฝ่ายวางแผนและพัฒนาระบบไฟฟ้า	115 kV SINGLE CIRCUIT SINGLE CONDUCTOR DOUBLE POLE (WITH GROUND PLATE IN POLE), TAP LINE STRUCTURE TYPE SS-TL-2	แบบเลขที่ SA1-015/47008 แผ่นที่.2.ของจำนวน.3.แผ่น

26 ก.ค. 2547

26 ก.ค. 2547

การประกอบเลขที่
ASSEMBLY NO. **5211A**

บัญชีวัสดุ
BILL OF MATERIAL

ลำดับที่ ITEM	รายละเอียด DESCRIPTION	จำนวน REQ.D	วัสดุเลขที่ MAT. NO.
1	เสา คอร. ยาว 22.00 ม. ชนิดมีกราวด์เพลทในเสา POLE, CONCRETE, 22.00 m LONG, WITH GROUND PLATE IN POLE	2	00010015
2	สลักเกลียว M 20x450 มม. BOLT, MACHINE, M 20x450 mm	6	01110302
3	สลักห่วงโอเวล M 20x350 มม. BOLT, OVAL EYE, M 20x350 mm	6	01150100
4	สลักห่วงโอเวล M 20x450 มม. BOLT, OVAL EYE, M 20x450 mm	3	01150101
5	แหวนสี่เหลี่ยมแบน 62x62x6 มม. รู ø22 มม. มอก.258 WASHER, SQUARE, FLAT, 62x62x6 mm, HOLE ø22 mm, TIS 258	30	01180101
6	แหวนสปริง M 20 มอก. 259 WASHER, LOCK, M 20, TIS 259	9	01180302
7	เหล็กรูปรางน้ำ 200x80x7.5 มม. ยาว 1,000 มม. STEEL CHANNEL, 200x80x7.5 mm, 1,000 mm LONG	6	01000400

รายละเอียด
DETAIL

D-3C	การประกอบลูกถ้วยแขวน SUSPENSION INSULATOR ASSEMBLY	3	
D-4C	การประกอบลูกถ้วยแขวน SUSPENSION INSULATOR ASSEMBLY	3	
D-15C	การประกอบลูกถ้วยแขวน SUSPENSION INSULATOR ASSEMBLY	3	
D-5W	การประกอบสายล่อฟ้า OVERHEAD GROUND WIRE ASSEMBLY	1	
D-10B	ฐานรากเสา POLE FOUNDATION	1	
D-25	การต่อลงดิน GROUNDING	1	

พชง.3 ผฟร. กฟส.อล. กฟล.กบ. กฟต.2 สายงาน (ต) ผวก. ©PEA

หมายเหตุ

1.* กรณีก่อสร้างในพื้นที่เขตทางหลวง ให้ใช้ค่าระยะห่างตามแนวดิ่งในวงเล็บ โดยดูรายละเอียดเพิ่มเติมในแบบเลขที่ SA1-015/43012 (การประกอบเลขที่ 5687)
2. ระยะห่างระหว่างช่วงเสาของโครงสร้างสายส่ง 115 kV โครงสร้างเสาสำหรับแยกสาย ให้ดูแบบเลขที่ SA1-015/47010 (การประกอบเลขที่ 5162)

NOTES

1.* IN CASE OF CONSTRUCTION IN HIGHWAY AREA, USE A VERTICAL CLEARANCE VALUE IN THE PARENTHESIS. FOR ADDITIONAL DETAIL, SEE DWG NO. SA1-015/43012 (ASSEMBLY NO. 5687) .
2. SPAN LENGTHS FOR 115 kV CONSTRUCTION STRUCTURE, TAP LINE STRUCTURE, SEE DWG. NO. SA1-015/47010 (ASSEMBLY NO. 5162) .

กองมาตรฐานระบบไฟฟ้า ฝ่ายมาตรฐานและความปลอดภัย	การไฟฟ้าส่วนภูมิภาค	ใช้แทนแบบ .... ถูกแทนโดยแบบ ....
ผู้เขียน ...สมชาย........... ผู้สำรวจ .... วิศวกร .... หัวหน้าแผนก .... ผู้อำนวยการกอง .... ผู้อำนวยการฝ่าย	ผู้ว่าการ .... 115 kV วงจรเดี่ยว สายไฟฟ้าเดี่ยว 26 ก.ค. 2547 เสาคู่ (ชนิดมีกราวด์เพลทในเสา) สำหรับแยกสาย แบบ SS-TL-2	เขียนเสร็จวันที่ 2 มิ.ย. 2547 แก้แบบวันที่ .... มิติเป็น .... มาตราส่วน ....
รองผู้ว่าการฝ่ายวางแผนและพัฒนาระบบไฟฟ้า	115 kV SINGLE CIRCUIT SINGLE CONDUCTOR DOUBLE POLE (WITH GROUND PLATE IN POLE), TAP LINE STRUCTURE TYPE SS-TL-2	แบบเลขที่ SA1-015/47008 แผ่นที่ 3 ของจำนวน 3 แผ่น

26 ก.ค. 2547