


การประกอบเลขที่ 3221
ASSEMBLY NO.

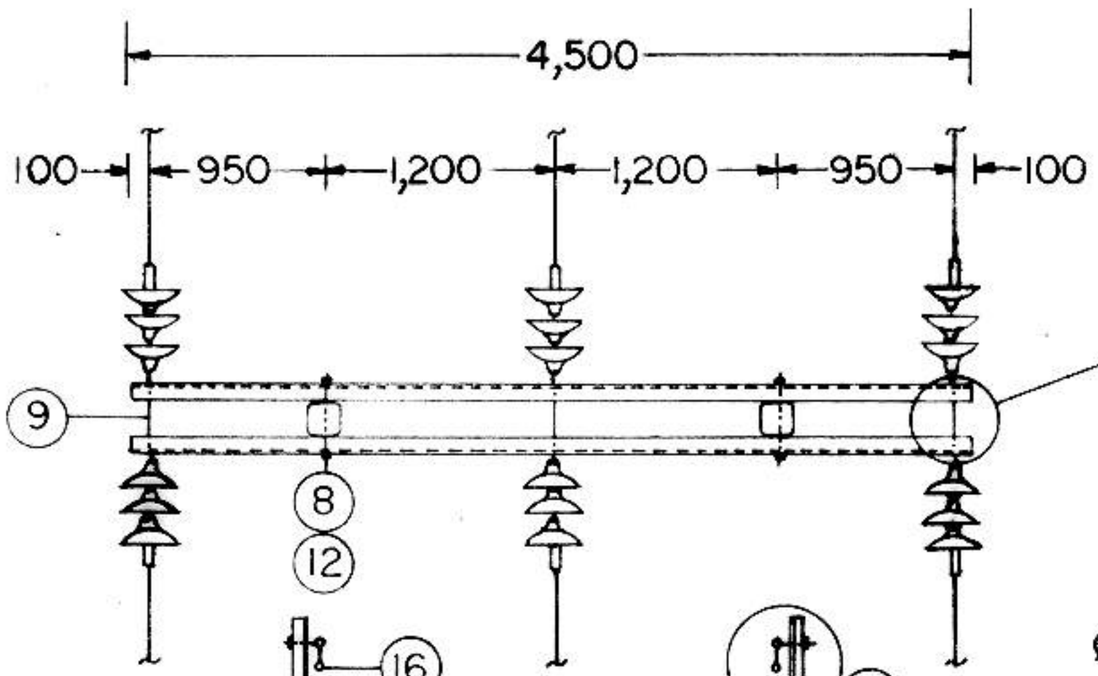


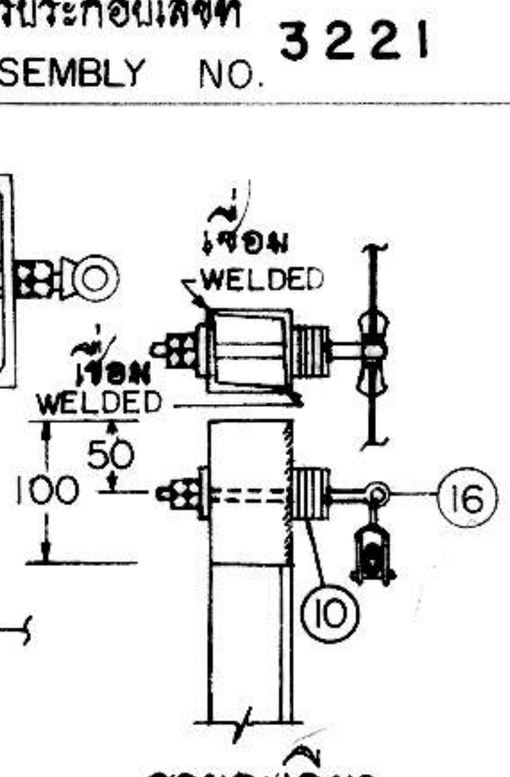

รายละเอียด A
DETAIL A

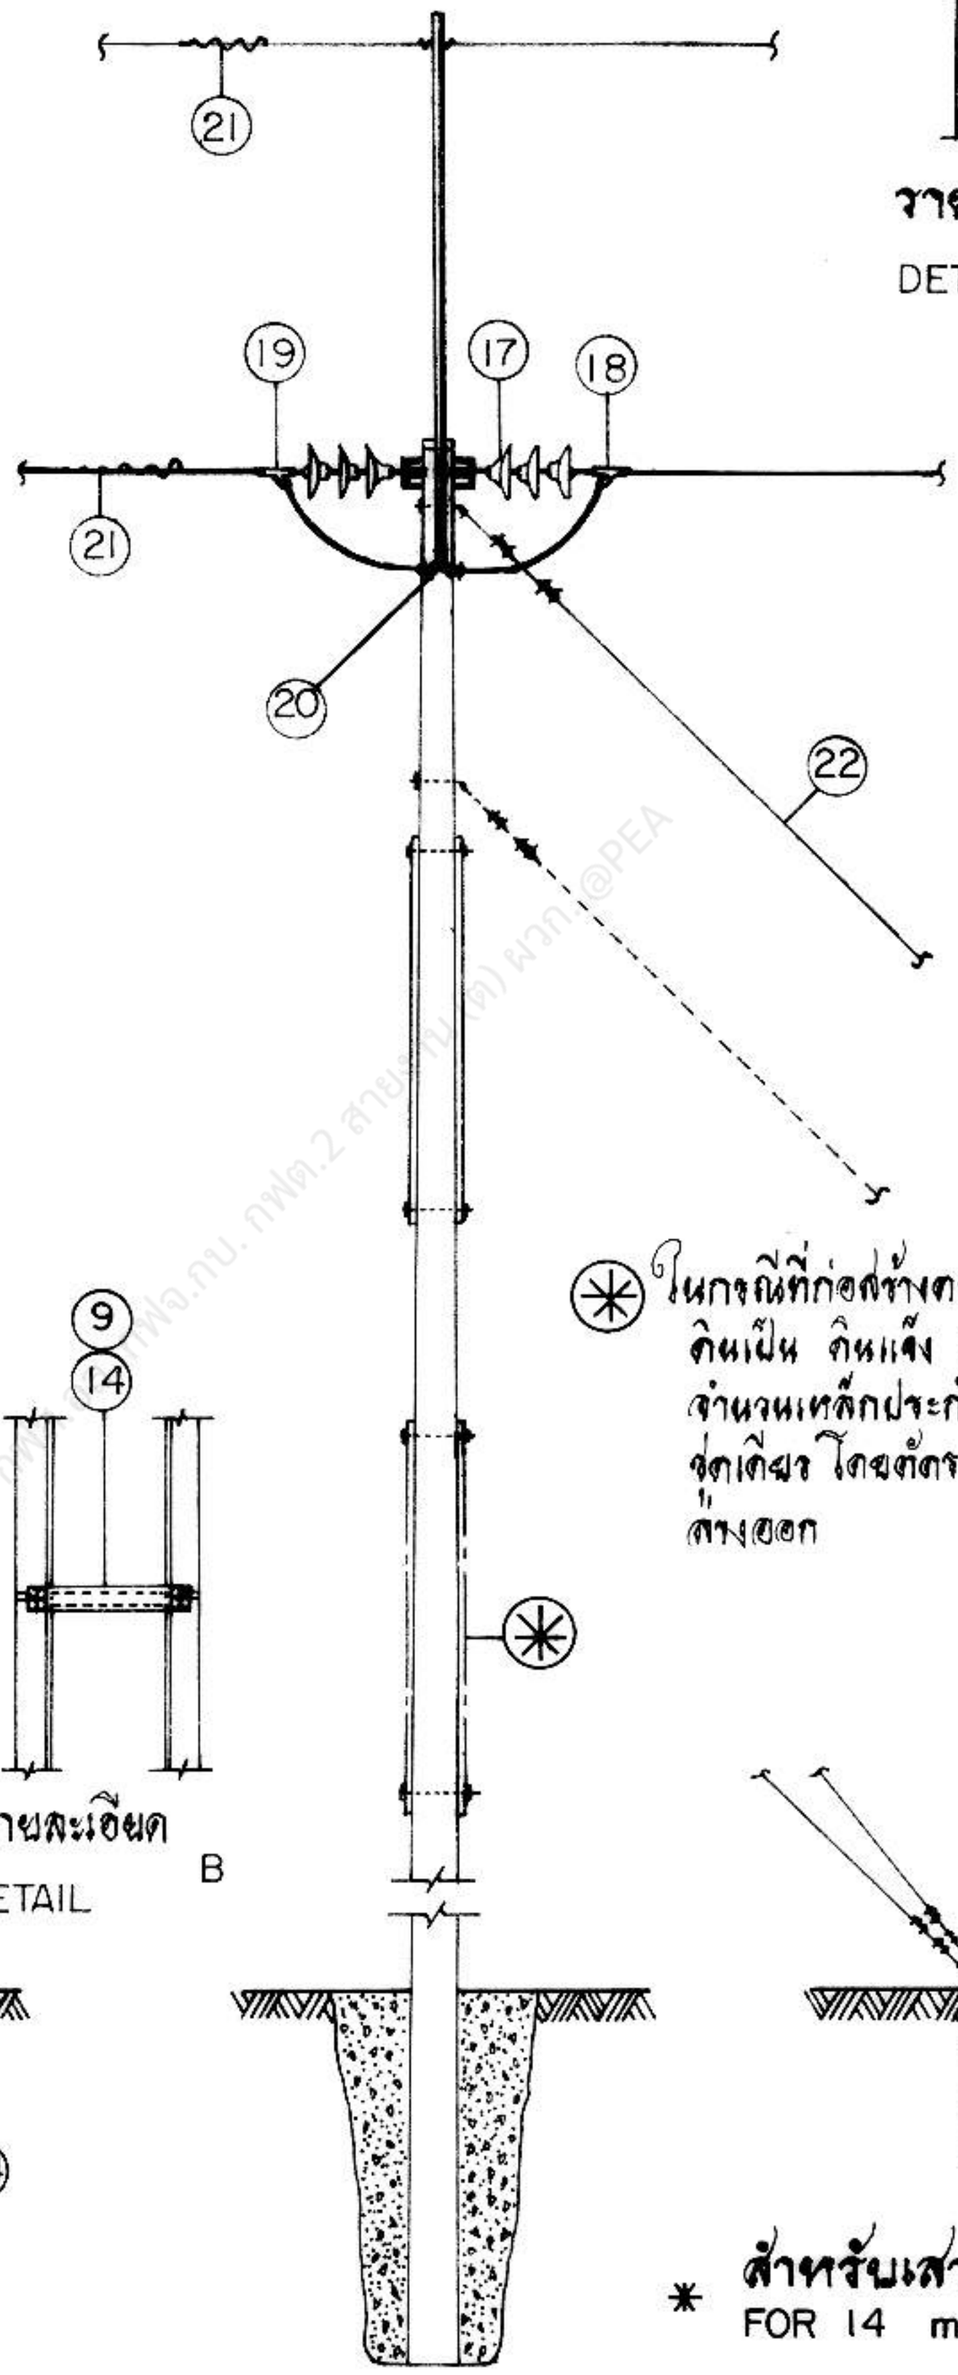

รายละเอียด B
DETAIL B

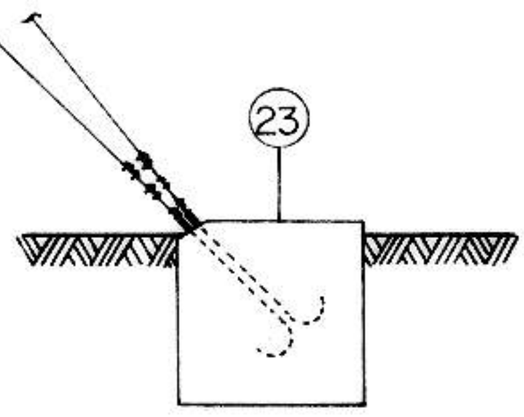

* ในกรณีที่ก่อสร้างตามบริเวณภูเขา ซึ่งสภาพดินเป็น ดินแข็ง ลูกรัง หรือหิน ให้ลดจำนวนเหล็กประกับยึดเสาคู่ เหลือเพียงชุดเดียว โดยตัดรายการเหล็กประกับชุดข้างออก

* สำหรับเสา 14 ม.
FOR 14 m POLE

กองวิศวกรรมไฟฟ้าและเครื่องกล ฝ่ายวิศวกรรม	การไฟฟ้าส่วนภูมิภาค	ใช้แทนแบบ ถูกแทนโดยแบบ
ผู้เขียน ผู้สำรวจ วิศวกร หัวหน้าแผนก หัวหน้ากอง ผู้อำนวยการฝ่าย รองผู้ว่าการฝ่ายเทคนิค	ผู้ว่าการ 30 มิ.ย. 21.	เขียนเสร็จวันที่ 22 มีค. 21 แก้แบบวันที่ 14 ก.ค. 21 มิติเป็น มม. 8 ต.ค. 24 มาตราส่วน 1:75
	มาตรฐานการก่อสร้าง ระบบ 33 kV ช่วง 120-200 ม.	
	33 kV STANDARD CONSTRUCTION SPAN 120-200 m	แบบเลขที่ SAI-015/21020 แผ่นที่ 1 ของจำนวน 3 แผ่น

บัญชีวัสดุ

ช่อง I กรณีพาดสายข้ามแม่น้ำ
ช่อง II กรณีก่อสร้างตามเงื่อนไขภูเขา ซึ่งสภาพดินเป็นดินแข็ง ลูกรัง หรือหิน

การประกอบเลขที่ ASSEMBLY NO. 3221

บัญชีวัสดุ
BILL OF MATERIAL

ลำดับที่ ITEM	รายละเอียด DESCRIPTION	จำนวน REQ'D I	จำนวน REQ'D II	วัสดุเลขที่ MAT. NO.
1	เสาคอนกรีต 12 , 14 ม. CONCRETE POLE 12 , 14 m	2	2	00010004 or 00010006
2	เหล็กรูปรางน้ำ ขนาด 150 X 75 X6.5 มม. ยาว 4.50 ม. (น้ำหนัก 18.6 กก./ม.) STEEL CHANNEL 150X75X6.5 mm 4.50 m LONG (WEIGHT 18.6 kg/m)	2	2	01000302 (0114)
3	เหล็กฉาก ขนาด 75 X 75 X 6 มม. ยาว 3.50 ม. (น้ำหนัก 6.87 กก./ม.) STEEL ANGLE 75X 75X 6 mm 3.50 m LONG (WEIGHT 6.87 kg/m)	4	2	01010100 (0123)
4	เหล็กฉากรับสายล่อฟ้าทางโค้ง 60 X 60 X 6 มม. OVERHEAD GROUND WIRE CORNER BAYONET 60 X 60 X 6 mm	2	2	01010007 (0129)
5	สลักเกลียว M 12 X 35 มม. BOLT, MACHINE, M 12 X 35 mm	4	4	01110100 (0212)
6	สลักเกลียว M 16 X 250 มม. BOLT, MACHINE, M 16 X 250 mm	6	6	01110203 (0223)
7	สลักเกลียว M 16 X 300 มม. BOLT, MACHINE, M 16 X 300 mm	6	2	01110204 (0224)
8	สลักเกลียว M 16 X 350 มม. BOLT, MACHINE, M 16 X 350 mm	2	2	01110205 (0225)
9	สลักเกลียวตลอด M 16 X 400 มม. BOLT, DOUBLE ARMING, M 16 X 400 mm	5	4	01120000 (0243)
10	แหวนสี่เหลี่ยมแบน 52X52X4.5 มม. รู Ø 18 มม. มอก. 258 WASHER , SQUARE , FLAT 52X52X4.5 mm HOLE Ø 18 mm TIS 258	16	12	011 80100 (0355)
11	แหวนสปริง M 12 มอก. 259 WASHER, LOCK , M 12 TIS 259	4	4	01180300 (0364)
12	แหวนสปริง M 16 มอก. 259 WASHER, LOCK , M 16 TIS 259	2	2	01180301 (0365)
13	นัทรูปห่วง M 16 DIN 582 NUT, EYE M 16 DIN 582	6	6	01180001 (0345)
14	ท่อเหล็ก ขนาด Ø 20 มม. ความยาวตามต้องการ PIPE, STEEL Ø 20 mm LENGTH AS REQ'D	5	4	01050005 01050008
15	ยูแคล้มป์สลัก 1 ตัว M 8 (ไวร์ โร้ป คลิ๊ป) CLAMP, SINGLE U—BOLT M 8 (WIRE ROPE CLIP)	4	4	01230000 (0165)
16	กราวด์วายแคล้มป์สำหรับไม้คอนสาย GROUND WIRE SUPPORT AND CLAMP, FOR WOOD BAYONET	2	2	01230200 (0297)
17	ลูกถ้วยแขวน มอก. 354 แบบ ง (แบบ 52-4) INSULATOR, SUSPENSION TYPE, TIS 354 TYPE D (CLASS 52-4)	18	18	03020002 (0415)
18	สเตรนแคล้มป์สำหรับสายอะลูมิเนียม CLAMP, STRAIN, FOR Al CONDUCTOR	3	3	03110000 - 03110101
19	สเตรนแคล้มป์สำหรับสายอะลูมิเนียมแกนเหล็ก CLAMP, STRAIN, FOR ACSR	3	3	03110000 - 03110101
20	พี จี คอนเนคเตอร์ สำหรับ สายอะลูมิเนียม อะลูมิเนียมอัลลอย และ อะลูมิเนียมแกนเหล็ก CONNECTOR, PARALLEL GROOVE FOR Al, Al-ALLOY AND ACSR	6	6	02300103 - 02300104

กองวิศวกรรมไฟฟ้าและเครื่องกล ฝ่ายวิศวกรรม	**การไฟฟ้าส่วนภูมิภาค**	ใช้แทนแบบ ถูกแทนโดยแบบ เขียนเสร็จวันที่ 22 มีค. 21 แก้แบบวันที่ 14 ก.ค. 21 8 ต.ค. 24 มิติเป็น มาตราส่วน
ผู้เขียน ผู้สำรวจ วิศวกร หัวหน้าแผนก หัวหน้ากอง ผู้อำนวยการฝ่าย	ผู้ว่าการ 30 มี.ค. 21	
	มาตรฐานการก่อสร้าง ระบบ 33 kV ช่วง 120-200 ม.	
รองผู้ว่าการฝ่ายเทคนิค	33 kV STANDARD CONSTRUCTION SPAN 120-200 m	แบบเลขที่ SAI-015/21020 แผ่นที่ 2 ของจำนวน 3 แผ่น

การประกอบเลขที่ ASSEMBLY NO. 3221

บัญชีวัสดุ
BILL OF MATERIAL

ลำดับที่ ITEM	รายละเอียด DESCRIPTION	จำนวน REQ'D I	จำนวน REQ'D II	วัสดุเลขที่ MAT. NO.
21	สไปแรลไวเบรชั่นแดมเปอร์ SPIRIAL VIBRATION DAMPER	5	5	02200100 02200102-3
22	สายยึดโยง GY— 32 (ลวดเหล็กตีเกลียว 95 ต.มม. ไม่รวมท่อนไม้) GUY GY — 32 (STEEL STRANDED WIRE 95 mm^2, LOG ANCHOR NOT INCLUDED)	4	4	—
23	สมอบกคอนกรีต IXIXI ม. (คอนกรีต 1:2:4) CONCRETE ANCHOR IXIXI m (CONCRETE 1:2:4)	2	2	—
24	คอนกรีต 1 : 3 : 5 CONCRETE 1 : 3 : 5	3 ม.^{3} m^3	3 ม.^{3} m^3	—

หมายเหตุ

1. ระยะช่วงเสาสำหรับสายไฟฟ้า :
   อะลูมิเนียมเปลือย 185 ต.มม. ระยะช่วงเสาไม่เกิน 150 ม. (สำหรับสายขนาดอื่นไม่สมควรใช้)
   อะลูมิเนียมแกนเหล็ก อะลูมิเนียมอัลลอย ระยะช่วงเสาเกิน 100 ม.
2. อุปกรณ์ที่เป็นเหล็ก เจาะรูขนาด Ø 18X50 มม. อาบสังกะสี หรือทาด้วยสีกันสนิม
3. ในกรณีสภาพดินอ่อนให้ใช้เสาตอม่อ หรือฐานคอนกรีตสำหรับเสาไฟฟ้า
4. ระยะระหว่างสมอบกกับโครงสร้างเสา ประมาณ 7.50 ม.
5. ในกรณีพาดสายอะลูมิเนียมอัลลอย 50 ต.มม.หรืออะลูมิเนียมแกนเหล็ก 50/8 ต.มม. สามารถใช้สายยึดโยงเพียง 2 ชุดได้
6. สายล่อฟ้าใช้ลวดเหล็กตีเกลียว 25 ต.มม.

NOTES

1. LIMITING SPAN FOR CONDUCTOR:
   BARE ALUMINIUM CONDUCTOR 185 mm^2 SPAN NOT EXCEED 150 m (OTHER SIZE DO NOT ALLOW)
   ACSR, ALUMINIUM ALLOY, SPAN EXCEED 100 m
2. DRILL Ø 18 X 50 mm FOR STEEL PARTS AND SHALL BE GALVANIZED OR COATED WITH RUST—RESISTING PAINT.
3. FOR BAD SOIL CONDITION STUB POLE OR CONCRETE FOUNDATION FOR CONCRETE POLE SHALL BE USED.
4. DISTANCE BETWEEN ANCHOR AND POLE STRUCTURE IS APPROX 7.50 m.
5. TWO SETS OF GUY WIRE MAY BE USED IF CONDUCTOR SIZE ARE Al-ALLOY 50 mm^2 OR ACSR 50/8 mm^2.
6. USE STEEL STRANDED WIRE 25 mm^2 AS OVERHEAD GROUND WIRE.

กองวิศวกรรมไฟฟ้าและเครื่องกล ฝ่ายวิศวกรรม	การไฟฟ้าส่วนภูมิภาค	ใช้แทนแบบ ถูกแทนโดยแบบ เขียนเสร็จวันที่ 22 มีค. 21 แก้แบบวันที่ 14 ก.ค. 21 มิติเป็น 8 ต.ค. 24 / 5 มิ.ย. 28 มาตราส่วน
ผู้เขียน ผู้สำรวจ วิศวกร หัวหน้าแผนก หัวหน้ากอง ผู้อำนวยการฝ่าย	ผู้ว่าการ 30 มี.ค. 21	มาตรฐานการก่อสร้าง ระบบ 33 kV ช่วง 120–200 ม.
รองผู้ว่าการฝ่ายเทคนิค	33 kV STANDARD CONSTRUCTION SPAN 120–200 m	แบบเลขที่ SAI-015/21020 แผ่นที่ 3 ของจำนวน 3 แผ่น