การประกอบเลขที่
ASSEMBLY NO. **3701**

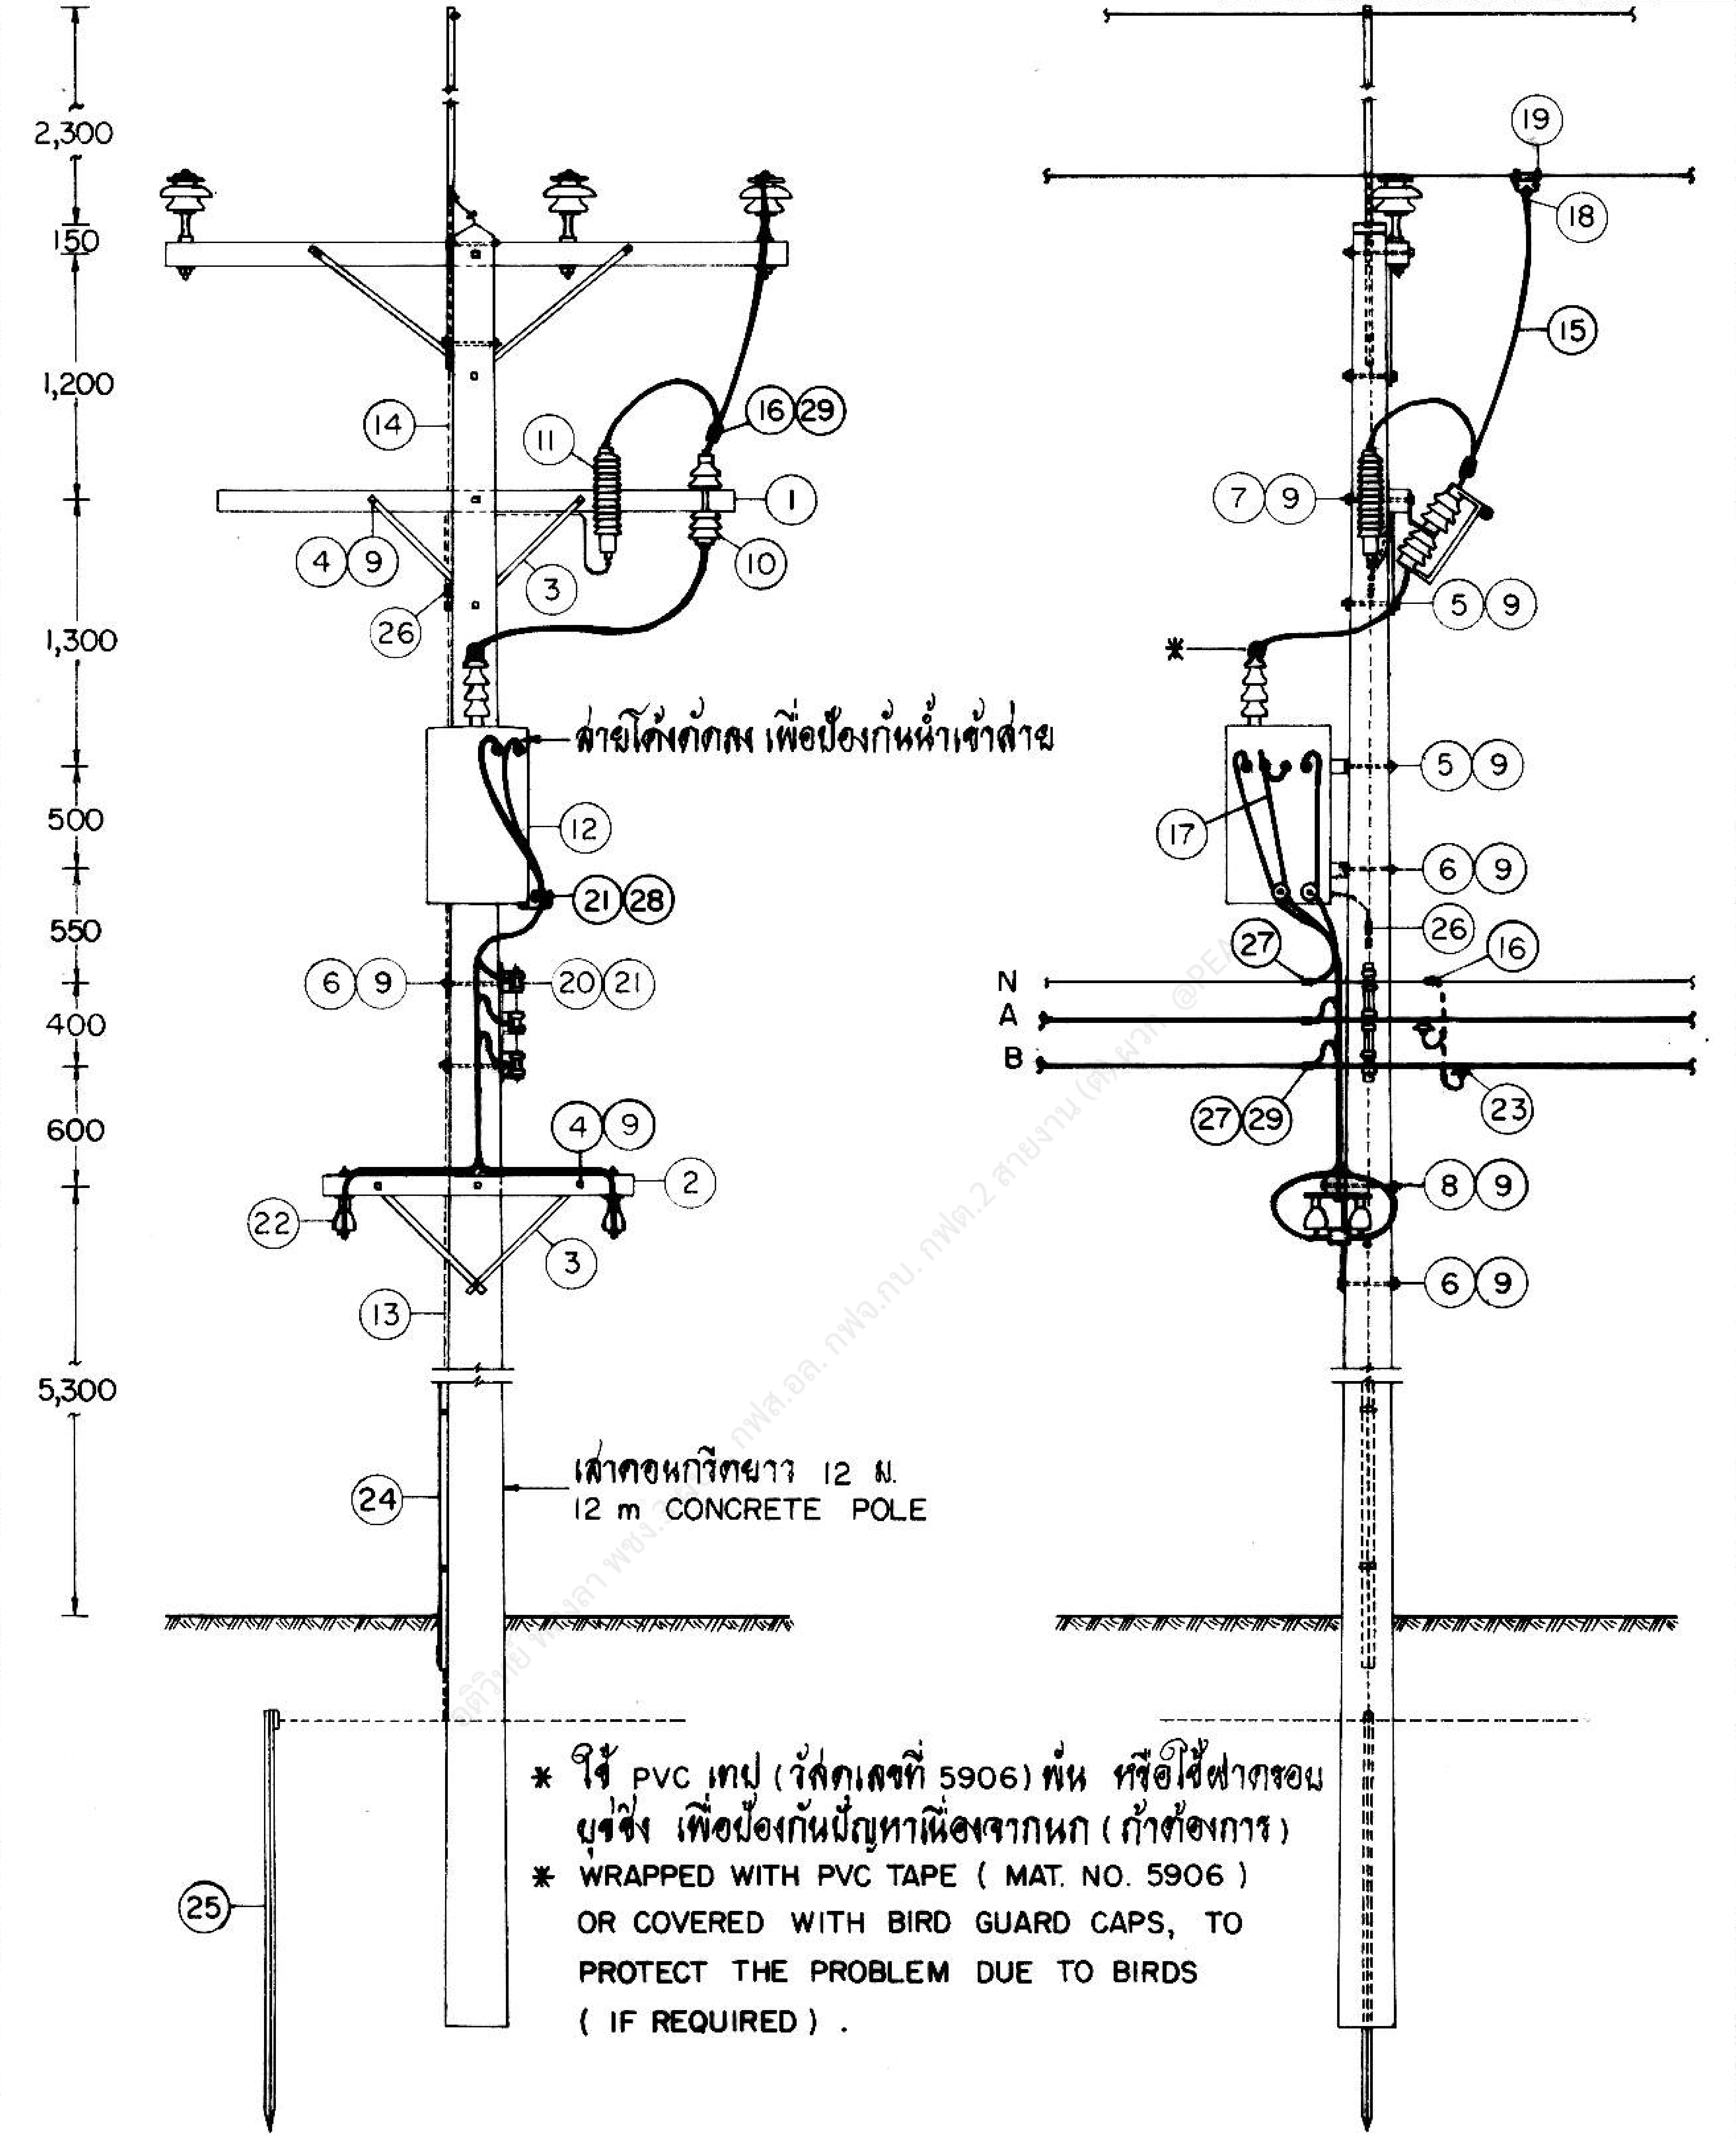

* ใช้ PVC เทป (วัสดุเลขที่ 5906) พัน หรือใช้ฝาครอบบุชชิ่ง เพื่อป้องกันปัญหาเนื่องจากนก (ถ้าต้องการ)

* WRAPPED WITH PVC TAPE (MAT. NO. 5906) OR COVERED WITH BIRD GUARD CAPS, TO PROTECT THE PROBLEM DUE TO BIRDS (IF REQUIRED) .

กองวิศวกรรมไฟฟ้าและเครื่องกล ฝ่ายวิศวกรรม	**การไฟฟ้าส่วนภูมิภาค**	ใช้แทนแบบ I 50-015/120420 ถูกแทนโดยแบบ
ผู้เขียน ผู้สำรวจ วิศวกร หัวหน้าแผนก หัวหน้ากอง ผู้อำนวยการฝ่าย	ผู้ว่าการ ๖ ก.ค. ๒๐	เขียนเสร็จวันที่ 21 มิ.ย. 20 แก้แบบวันที่ 4 ก.ย. 35
	การติดตั้งหม้อแปลงซิงเกิลบุชชิ่ง 19 kV (ก ในสายระบบจำหน่าย 3 เฟส 33 kV)	มิติเป็น มม. มาตราส่วน 1 : 50
รองผู้ว่าการฝ่ายเทคนิค	19 kV SINGLE BUSHING TRANSFORMER INSTALLATION (A ON 3-PHASE 33 kV DISTRIBUTION LINE)	แบบเลขที่ S02-015/20075 แผ่นที่ 1 ของจำนวน 4 แผ่น

การประกอบเลขที่
ASSEMBLY NO. **3701**

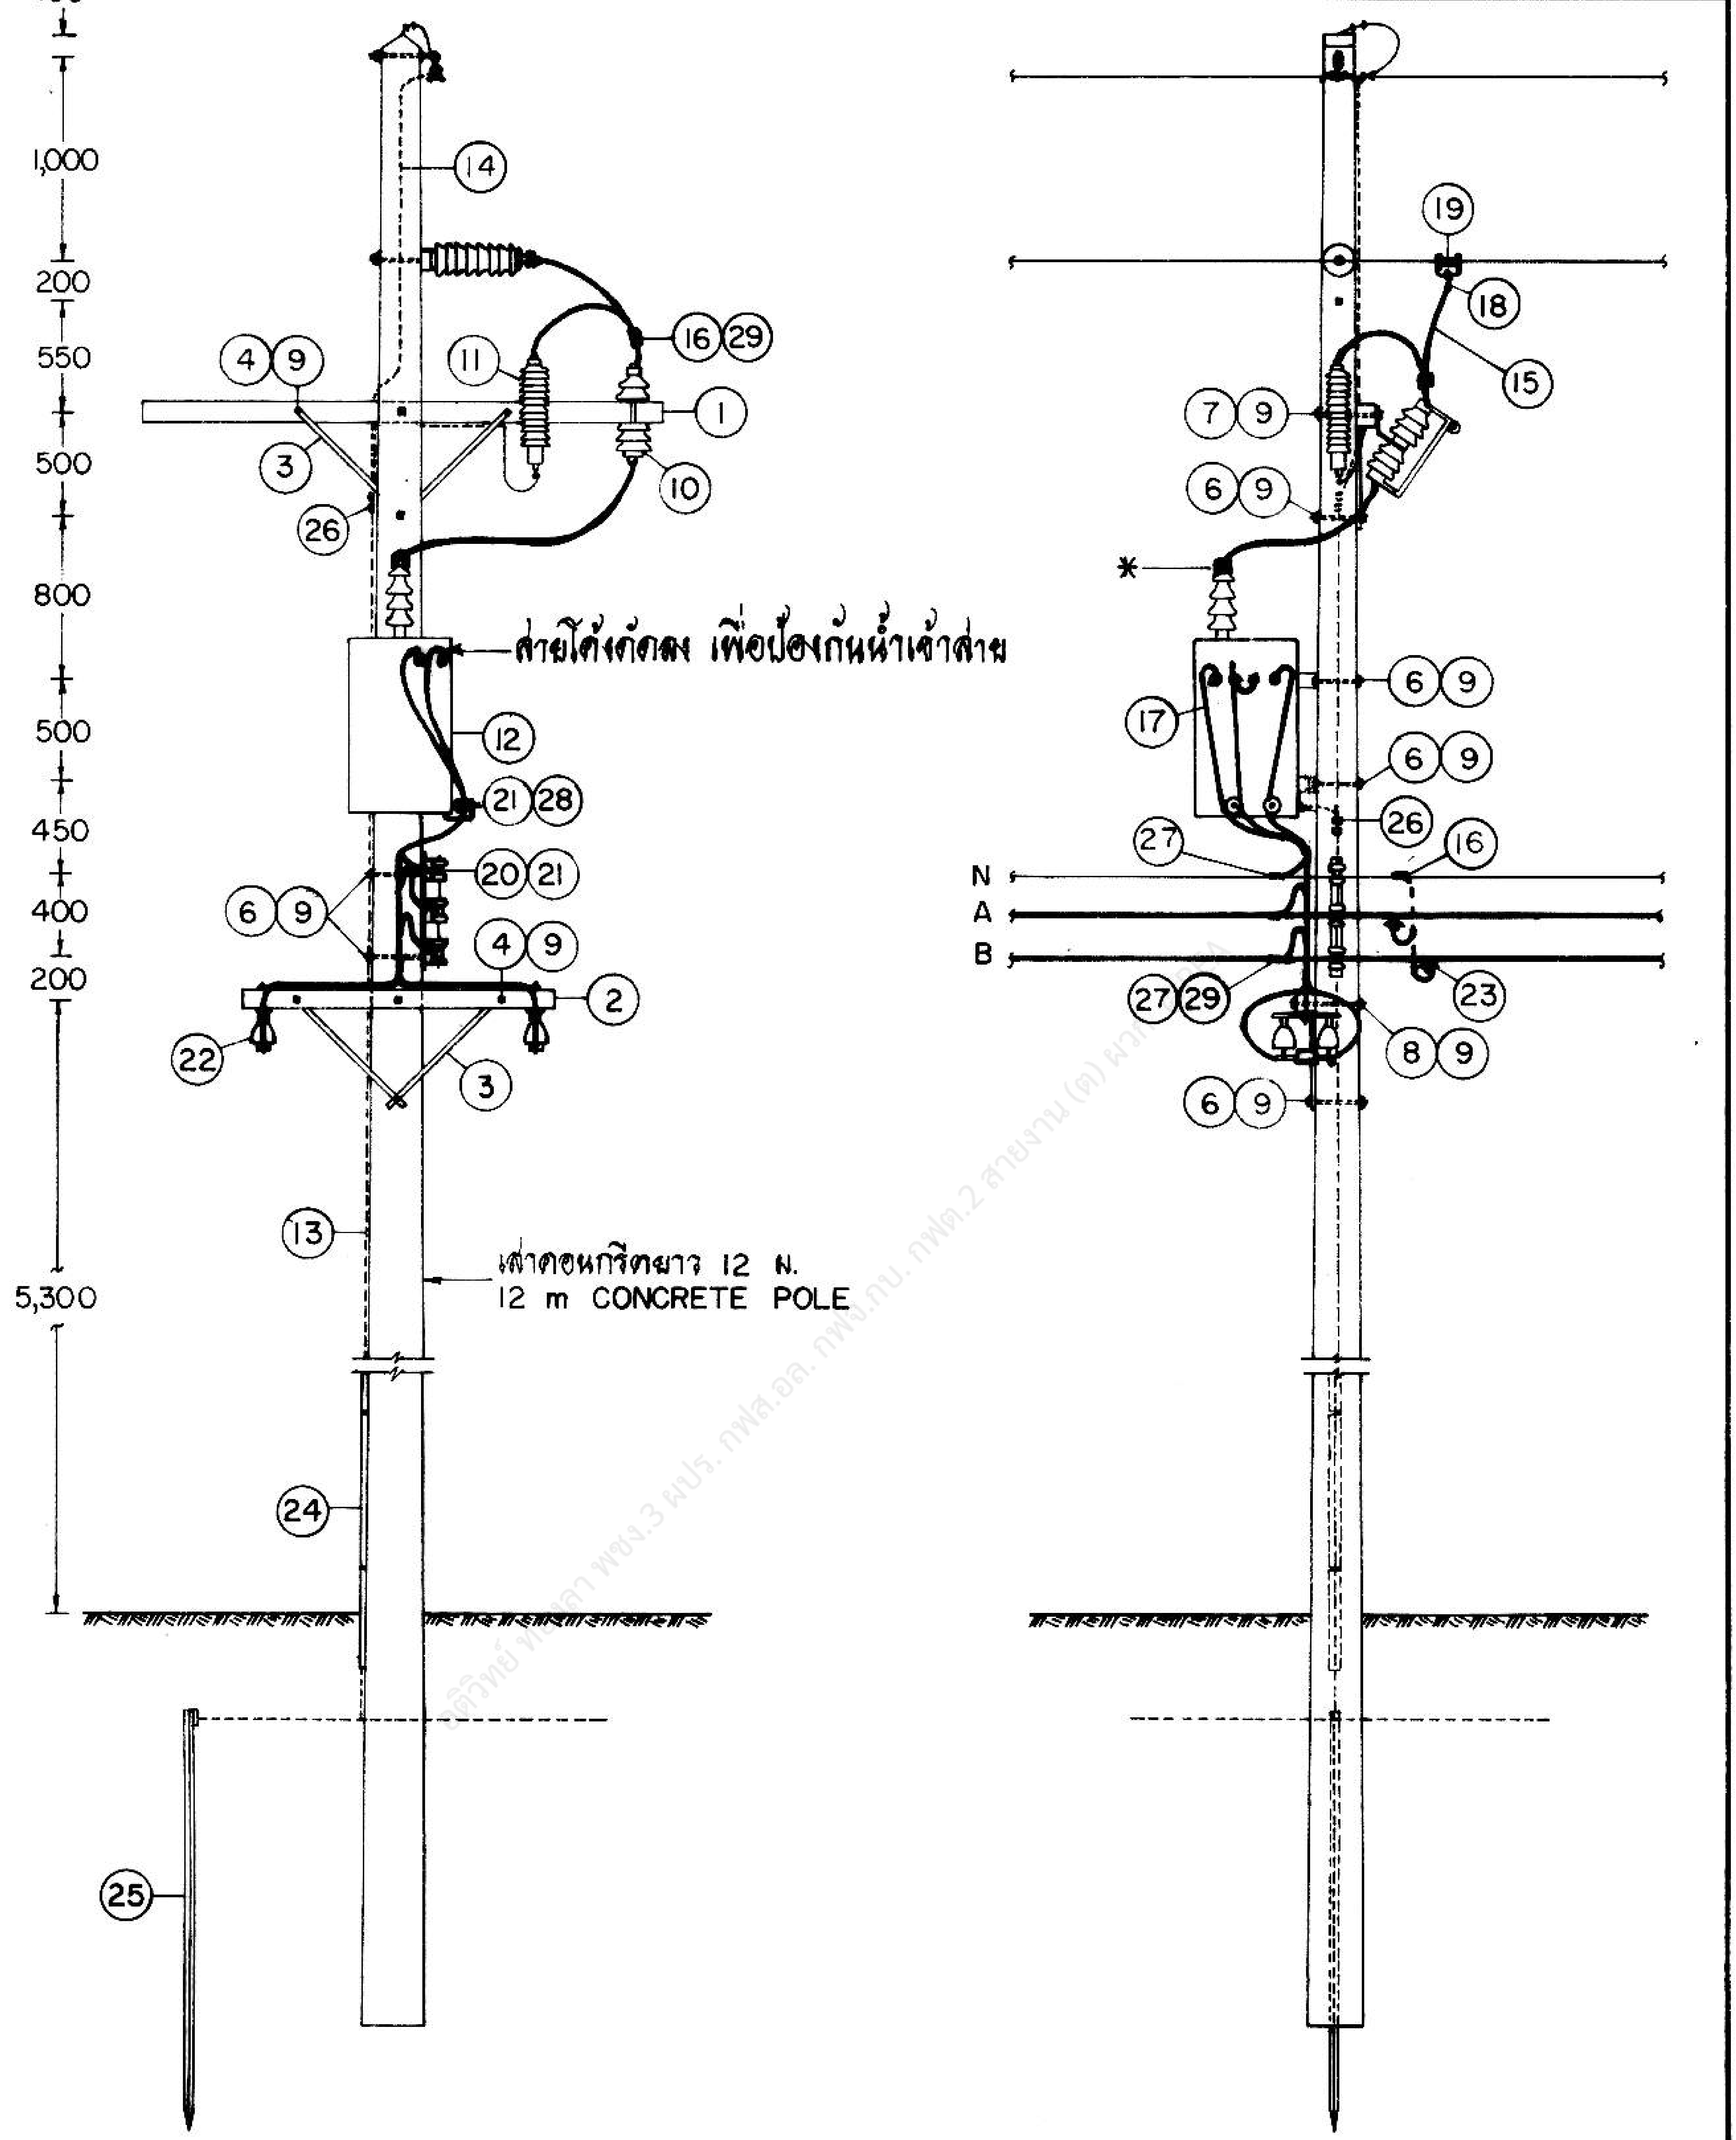

กองวิศวกรรมไฟฟ้าและเครื่องกล ฝ่ายวิศวกรรม	**การไฟฟ้าส่วนภูมิภาค**	ใช้แทนแบบ I50-015/120420 ถูกแทนโดยแบบ
ผู้เขียน ผู้สำรวจ วิศวกร หัวหน้าแผนก หัวหน้ากอง ผู้อำนวยการฝ่าย	ผู้ว่าการ 6 ก.ค. 20. การติดตั้งหม้อแปลงซิงเกิลบุชชิ่ง 19 kV (ข ในสายระบบจำหน่าย 1 เฟส 19 kV)	เขียนเสร็จวันที่ 21 มิ.ย. 20 แก้แบบวันที่ 4 ก.ย. 35 มิติเป็น มม. มาตราส่วน 1 : 50
รองผู้ว่าการฝ่ายเทคนิค	19 kV SINGLE BUSHING TRANSFORMER INSTALLATION (B ON 1-PHASE 19 kV DISTRIBUTION LINE)	แบบเลขที่ S 02-015/20075 แผ่นที่ 2 ของจำนวน 4 แผ่น

การประกอบเลขที่
ASSEMBLY NO. 3701

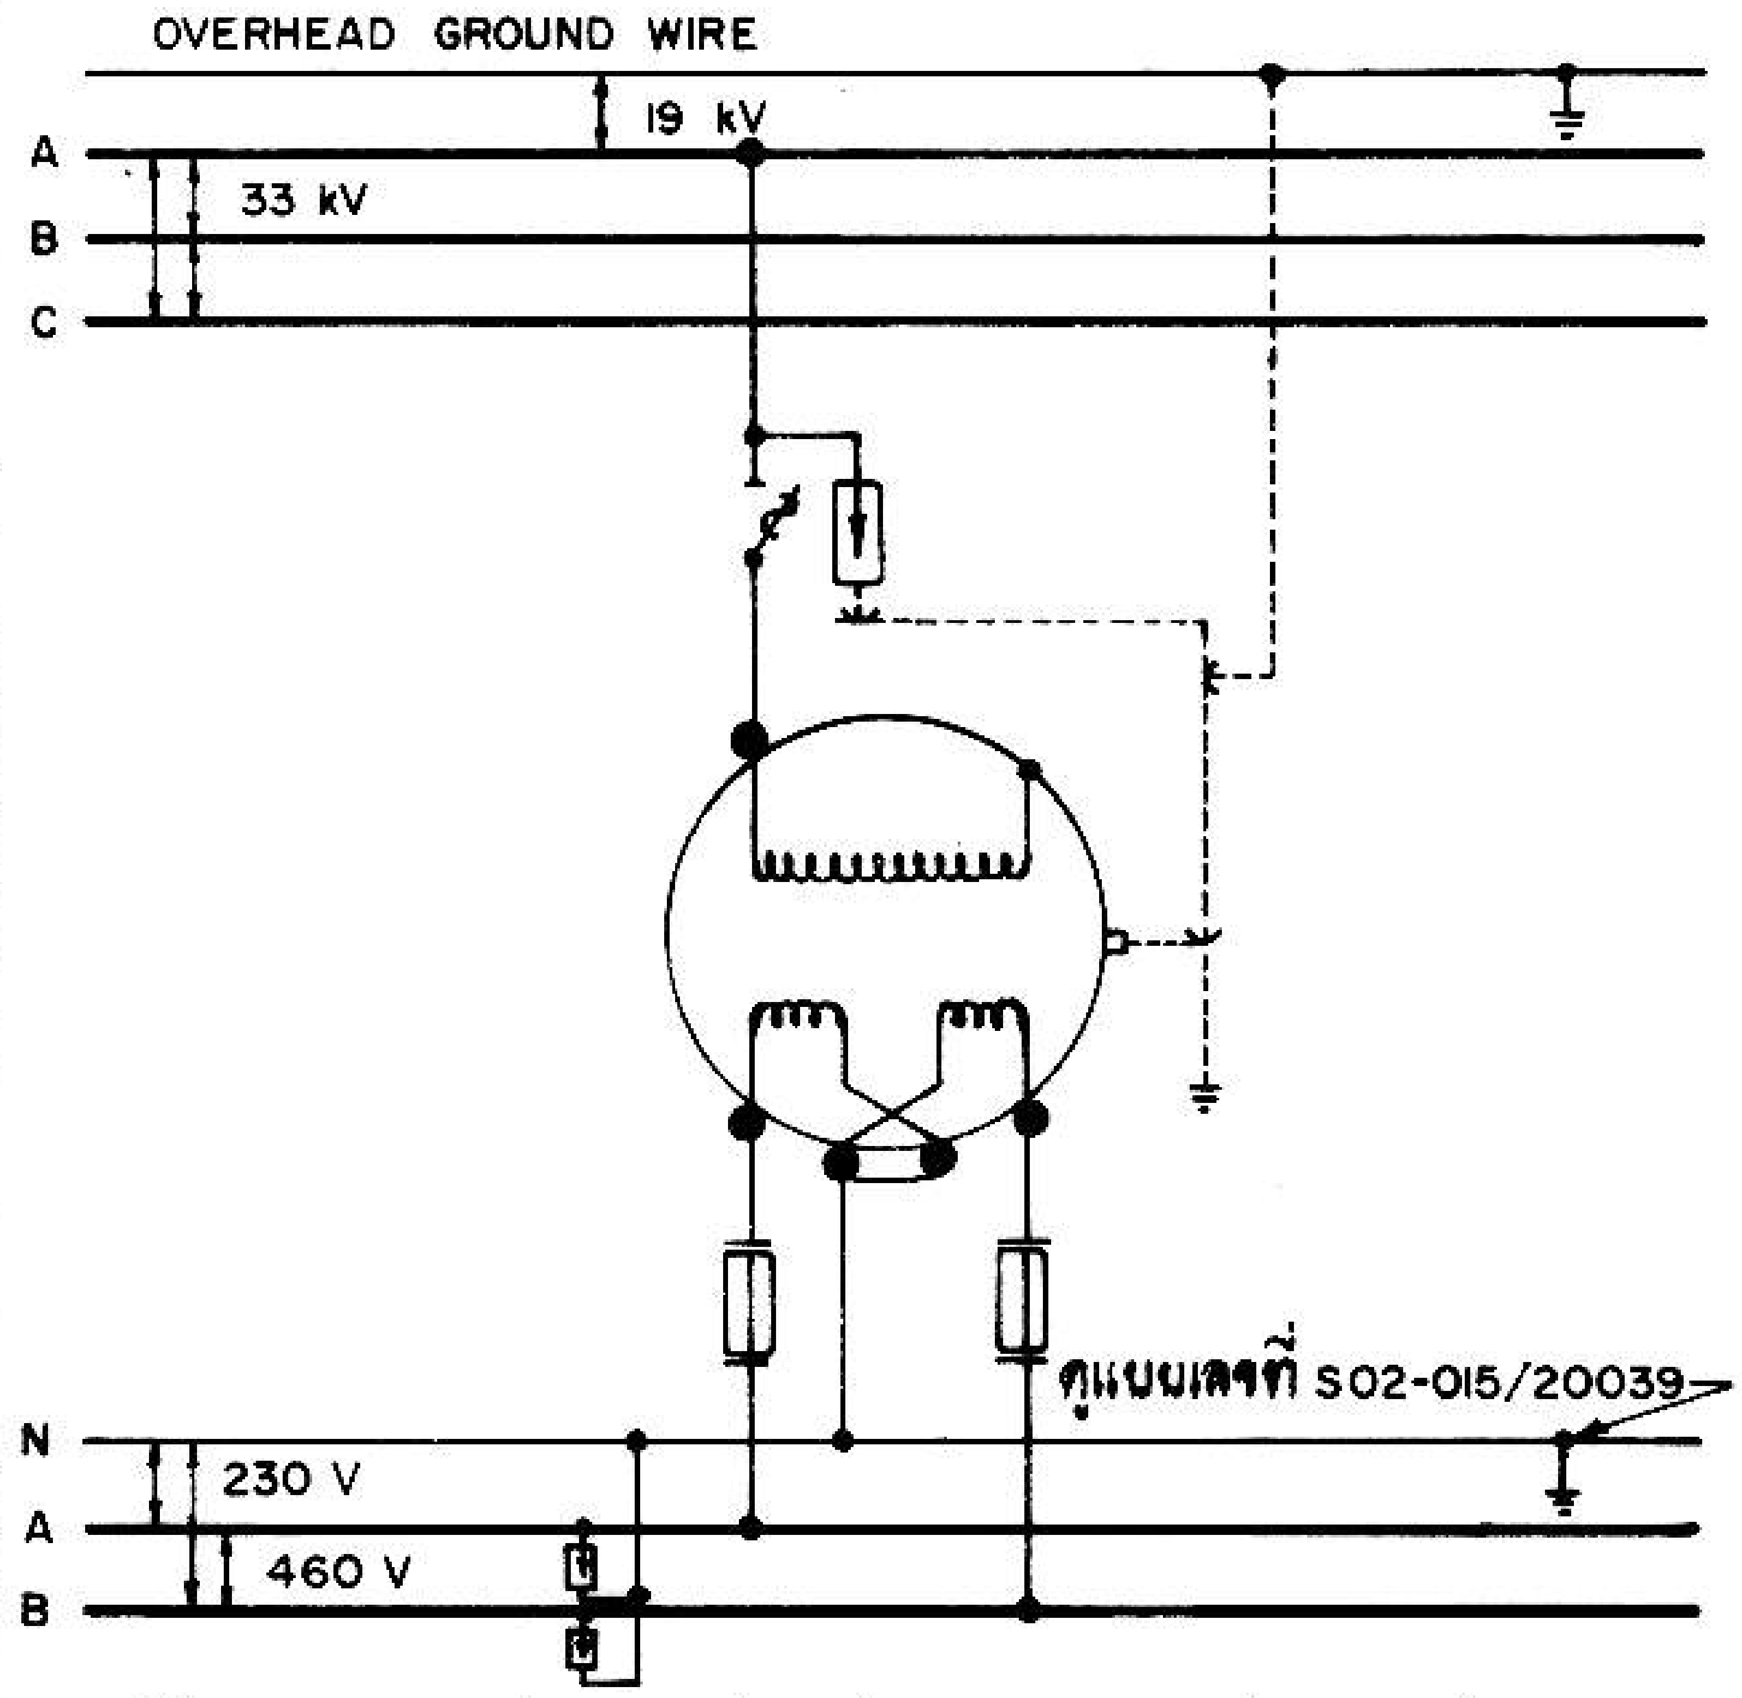

ไดอะแกรมแสดงการต่อหม้อแปลง 1 เฟส 3 สาย
1-PHASE 3-WIRE TRANSFORMER WIRING DIAGRAM

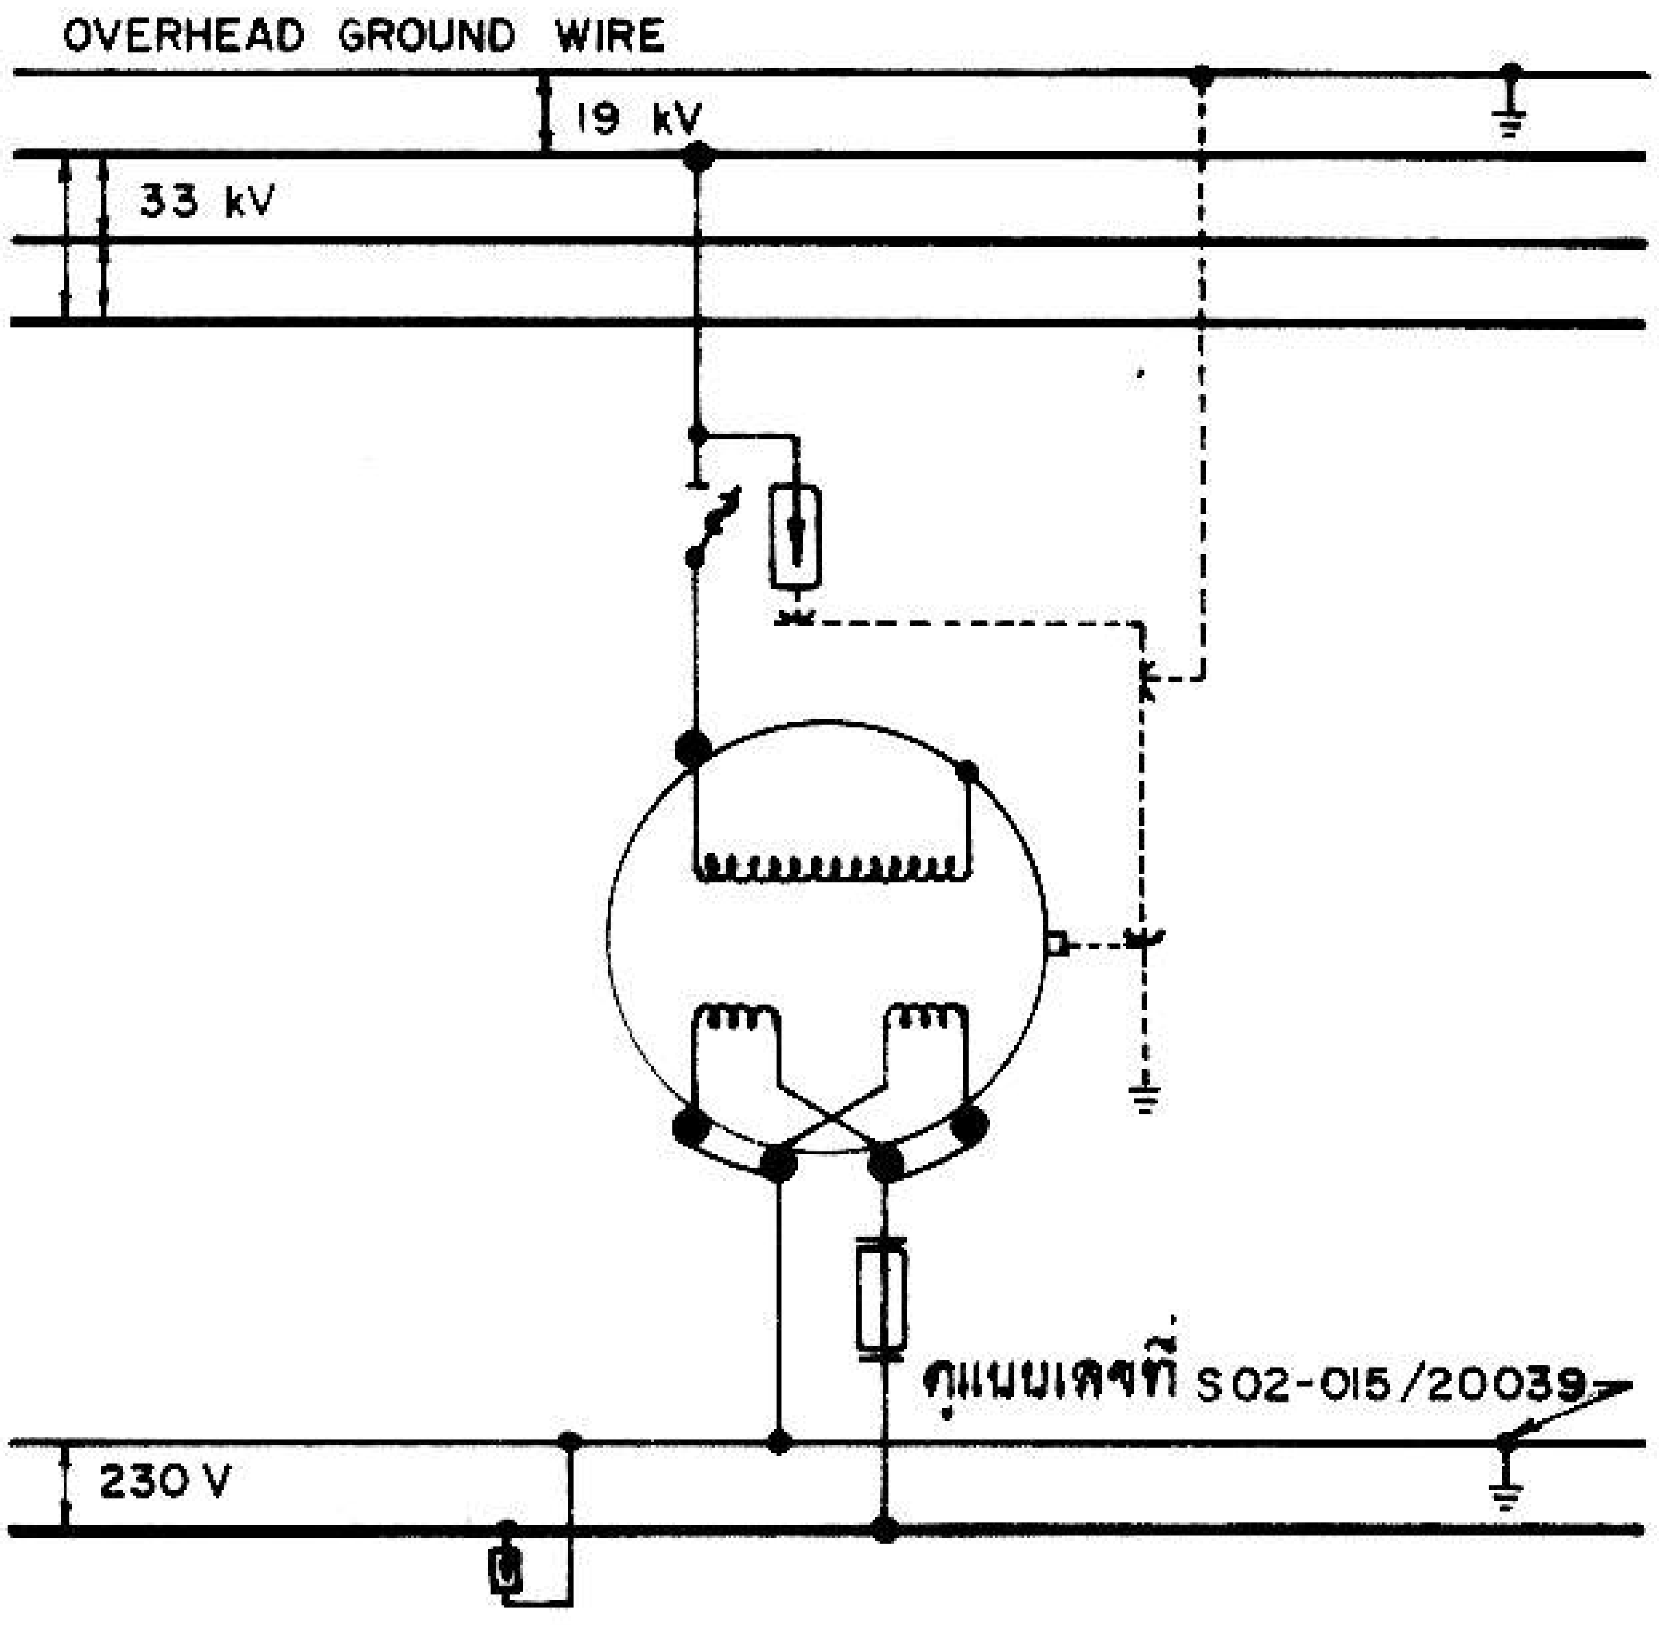

ไดอะแกรมแสดงการต่อหม้อแปลง 1 เฟส 2 สาย
1-PHASE 2-WIRE TRANSFORMER WIRING DIAGRAM

บัญชีวัสดุ
BILL OF MATERIAL

ลำดับที่ ITEM	รายละเอียด DESCRIPTION	จำนวน REQ'D		วัสดุเลขที่ MAT. NO.
		ก/A	ข/B	
1	คอน คอร.สปัน ขนาด 100 X 100 X 2,500 มม. CROSSARM, SPUN, PRESTRESSED CONCRETE, 100 X 100 X 2,500 mm	1	1	00110001
2	คอน คอร. ขนาด 100 X 100 X 1,500 มม. CROSSARM, PRESTRESSED CONCRETE, 100 X 100 X 1,500 mm	1	1	00110000
3	เหล็กประกับคอน 30 X 6 X 760 มม. BRACE, FLAT, FOR CROSSARM, 30 X 6 X 760 mm	4	4	01200001
4	สลักเกลียว M 16 X 130 มม. BOLT, MACHINE, M 16 X 130 mm	4	4	01110200
5	สลักเกลียว M 16 X 200 มม. BOLT, MACHINE, M 16 X 200 mm	2	–	01110202
6	สลักเกลียว M 16 X 250 มม. BOLT, MACHINE, M 16 X 250 mm	4	6	01110203
7	สลักเกลียว M 16 X 300 มม. BOLT, MACHINE, M 16 X 300 mm	1	1	01110204
8	สลักเกลียว M 16 X 350 มม. BOLT, MACHINE, M 16 X 350 mm	1	1	01110205
9	แหวนสี่เหลี่ยมแบน 52 X 52 X 4.5 มม. รู Ø 18 มม. มอก. 258 WASHER, SQUARE, FLAT, 52 X 52 X 4.5 mm, HOLE Ø 18 mm, TIS 258	14	14	01180100
10	ดรอพเอาต์ ฟิวส์คัตเอาต์ หนึ่งอินซูเลเตอร์ 33 kV, 100 แอมป์ CUT-OUT, FUSE, OPEN TYPE, SINGLE INSULATOR, DROPOUT, 33 kV, 100 A	1	1	04010100

กองวิศวกรรมไฟฟ้าและเครื่องกล
ฝ่ายวิศวกรรม

ผู้เขียน
ผู้สำรวจ
วิศวกร
หัวหน้าแผนก
หัวหน้ากอง
ผู้อำนวยการฝ่าย
รองผู้ว่าการฝ่ายเทคนิค

การไฟฟ้าส่วนภูมิภาค

ผู้ว่าการ ๒ ก.ค.๒๐.

การติดตั้งหม้อแปลงซิงเกิลบุชชิ่ง 19 kV

19 kV SINGLE BUSHING TRANSFORMER INSTALLATION

ใช้แทนแบบ I 50-015/120420
ถูกแทนโดยแบบ
เขียนเสร็จวันที่ 21 มิ.ย. 20
แก้แบบวันที่ 4 ก.ย. 35
ผิดเป็น
มาตราส่วน

แบบเลขที่ S 02-015/20075
แผ่นที่ 3 ของจำนวน 4 แผ่น

การประกอบเลขที่
ASSEMBLY NO. 3701

บัญชีวัสดุ
BILL OF MATERIAL

ลำดับที่ ITEM	รายละเอียด DESCRIPTION	จำนวน REQ'D ก/A	จำนวน REQ'D ข/B	วัสดุเลขที่ MAT. NO.
11	ล่อฟ้าแรงสูง 30 kV, 5 kA LIGHTNING ARRESTER, 30 kV, 5 kA	1	1	04000100
12	หม้อแปลงซิงเกิลบุชชิ่ง 33 GRDY/19/0.46-0.23 kV, 10-50 kVA TRANSFORMER, SINGLE BUSHING, 33 GRDY/19/0.46-0.23 kV, 10- 0 kVA	1	1	05000200 05000203
13	ลวดเหล็กตีเกลียว 50/7 ต.มม. พร้อมอุปกรณ์ยึด มอก. 404 WIRE, STEEL, STRANDED 50/7 mm² COMP. WITH FIXING ACCESS. TIS 404	20 ม. m	20 ม. m	01100004
14	ลวดเหล็กกลมเส้นผ่าศูนย์กลาง 4 มม. มอก. 71 WIRE, STEEL, SOLID DIAMETER 4 mm TIS 71	2 ม. m	2.5 ม. m	01100000
15	สายอะลูมิเนียมหุ้มฉนวน PVC 750V, 75°C มอก. 293 หรือหุ้มฉนวนแบบไม่เต็มพิกัด 33 kV ขนาด 35 ต.มม. CABLE, Al, PVC INSULATED, 750 V, 75°C, TIS 293 OR PARTIALLY INSULATED, 33 kV, 35 mm²	5 ม. m	5 ม. m	02070001 or 02070007
16	พี.จี. คอนเนคเตอร์ สลักคู่ สำหรับสายอะลูมิเนียม 25-95 ต.มม. CONNECTOR, PARALLEL GROOVE, DOUBLE BOLT, Al, 25-95 mm²	1	1	02300102
17	สายอะลูมิเนียมหุ้มฉนวน PVC, 750 V, 75°C มอก. 293 ขนาดตามต้องการ CABLE, Al, PVC INSULATED, 750 V, 75°C, TIS 293 ; SIZE AS REQUIRED	20 ม. m	17 ม. m	02070001 02070004
18	ฮอทไลน์แคล้มป์ สำหรับสายเมนอะลูมิเนียม ขนาดตามต้องการ CLAMP, HOT LINE, MAIN LINE, Al, SIZE AS REQUIRED	1	1	02330100 02330101
19	สเตอร์รัพแคล้มป์ หรือเบลแคล้มป์ สำหรับสายเมนอะลูมิเนียม ขนาดตามต้องการ CLAMP, STIRRUP OR BAIL, MAIN LINE, Al, SIZE AS REQUIRED	1	1	02330000 02330001
20	แร็ค 3 X 200 มม. (3X8") แบบหลังยื่น RACK, SECONDARY, MEDIUM PRESSED STEEL, 3X200 mm (3X8") EXT. BACK	1	1	03130001
21	ลูกรอกแรงต่ำ มอก. 227 แบบ ข (แบบ 53-2) INSULATOR, SPOOL TYPE, L.T., TIS 227, TYPE B (CLASS 53-2)	5	5	03030000
22	ฟิวส์สวิตช์แรงต่ำ 1 X 400 แอมป์ 500 โวลต์ L.T. – FUSE SWITCHES, 1X400 A, 500 V	2	2	04020100
23	ล่อฟ้า 250-500 โวลต์ 2.5-5.0 กิโลแอมป์ LIGHTNING ARRESTER, 250–500V, 2.5–5.0 kA	2	2	04000300
24	ท่อ PVC แข็ง ขนาด Ø 20 มม. พร้อมอุปกรณ์ยึดแบบเลขที่ S02-015/19128 PIPE, PVC, RIGID, Ø 20 mm ; COMP. WITH FIXING ACCESS. DWG. NO. S02–015/19128	1	1	08040001
25	หลักดิน 60 X 60 X 5 มม. ยาว 2 ม. ROD, GROUND, 60X60X5 mm, 2 m LONG	1	1	01220002
26	ยูแคล้มป์ สลัก 1 ตัว M 8 (ไวร์โรป คลิฟ) CLAMP, SINGLE U–BOLT, M 8 (WIRE ROPE CLIP)	4	4	01230000
27	คอนเนคเตอร์ ชนิดบีบ แบบ H สำหรับสายอะลูมิเนียม ขนาดตามต้องการ CONNECTOR, COMPRESSION, H TYPE, Al, SIZE AS REQUIRED	3	3	02320003 or 02320002
28	เหล็กจับขอบถังหม้อแปลง สำหรับยึดสายแรงต่ำ BRACKET STEEL, FOR TRANSFORMER SECONDARY LEAD	2	2	05100003
29	PVC เทป กว้าง 19 มม. (ใช้ความยาว 2 ม. ต่อ 1 จุด) PVC TAPE, 19 mm WIDE (2 m LONG FOR POINT)	ม้วน rolls	ม้วน rolls	02180002

หมายเหตุ ไดอะแกรมแสดงการต่อลงดิน และการติดตั้งสายดิน ดูแบบเลขที่ S02-015/20039 (การประกอบเลขที่ 9701)

NOTE EARTHING DIAGRAM AND EARTHING INSTALLATION, SEE DWG NO. S02-015/20039 (ASSEMBLY NO. 9701).

กองวิศวกรรมไฟฟ้าและเครื่องกล
ฝ่ายวิศวกรรม
ผู้เขียน
ผู้ตรวจ
วิศวกร
หัวหน้าแผนก
หัวหน้ากอง
ผู้อำนวยการฝ่าย
รองผู้ว่าการฝ่ายเทคนิค

การไฟฟ้าส่วนภูมิภาค

ผู้ว่าการ ๖ ก.ค. ๒๐

การติดตั้งหม้อแปลงซิงเกิลบุชชิ่ง 19 kV

19 kV SINGLE BUSHING TRANSFORMER INSTALLATION

ใช้แทนแบบ I 50-015/120420
ถูกแทนโดยแบบ
เขียนเสร็จวันที่ 21 มิ.ย. 20
แก้แบบวันที่ 4 ก.ย. 35
มิติเป็น
มาตราส่วน
แบบเลขที่ S02-015/20075
แผ่นที่ 4 ของจำนวน 4 แผ่น